


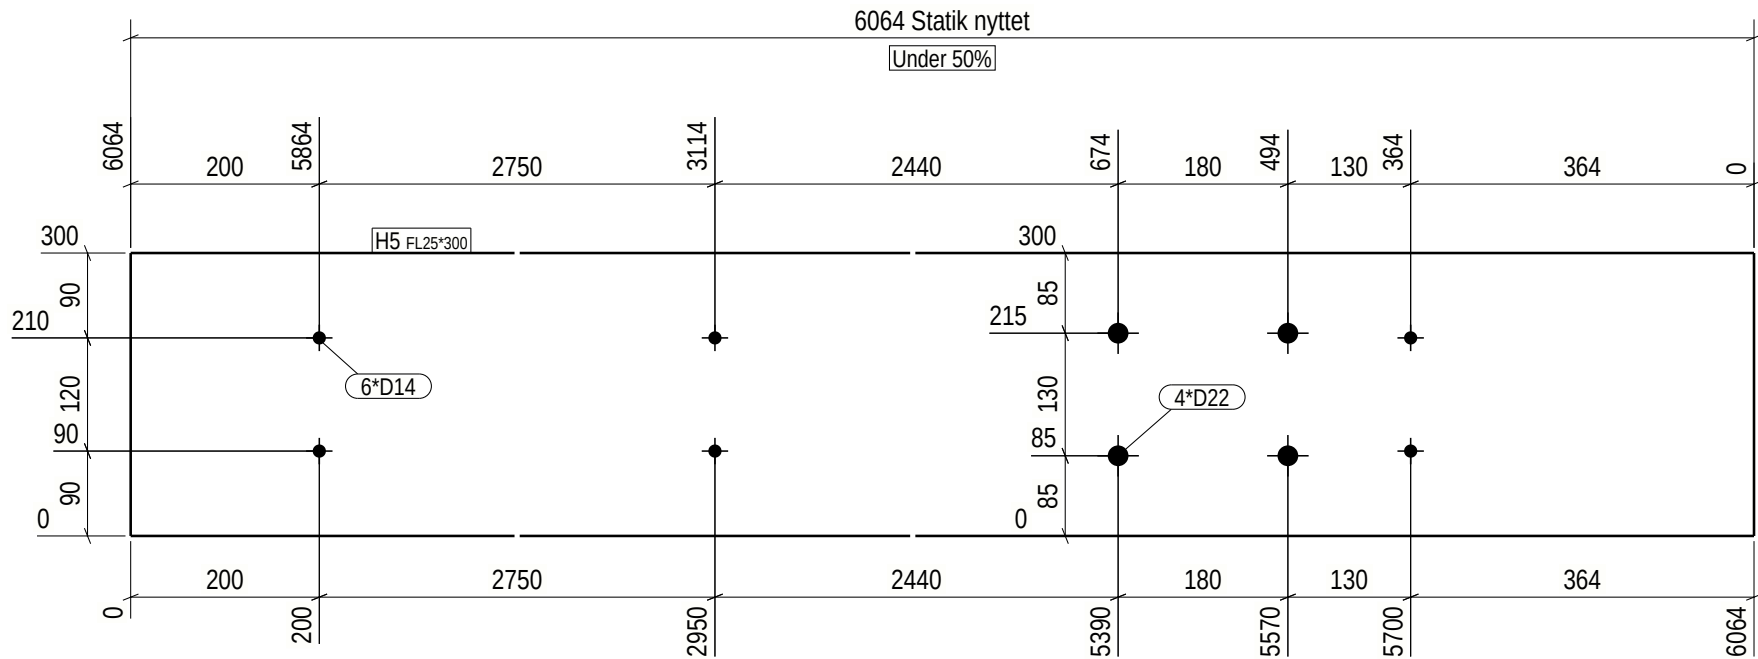

|                                                |          |     |        |        |                        |             |
|------------------------------------------------|----------|-----|--------|--------|------------------------|-------------|
| GENERAL NOTES:                                 |          |     |        |        |                        |             |
| For your safety, check weight before handling: |          |     |        |        |                        |             |
| 0-5kg Light    5-15kg Normal    15+kg Heavy    |          |     |        |        |                        |             |
| MATERIAL LIST FOR PART - H5                    |          |     |        |        |                        |             |
| 4 PARTS REQUIRED                               |          |     |        |        |                        |             |
| POS. No.                                       | PROFILE  | No. | GRADE  | L (mm) | AREA (m <sup>2</sup> ) | WEIGHT (kg) |
| H5                                             | FL25*300 | 1   | S355J2 | 6064   | 4.0                    | 357.0 !!    |
| TOTAL WEIGHT FOR                               |          |     |        |        | 4 PARTS                | 1428.1      |

|           |      |
|-----------|------|
| Part list | Qty. |
| FT        | 4    |

|   |  |   |                                      |              |             |
|---|--|---|--------------------------------------|--------------|-------------|
| Execution class: EXC 2   |  | * o 3 0 4 8 0 - 2 *  DS <i>Skalkonstruktion</i> * WH 5 * |                                      |              |             |
| No utilization on drawings = over 50%   |  |   |                                      |              |             |
| V-SEAM<br>Utilization under 50%<br>EXC 2=> Acc. to process control<br>EXC 3=> 20% UT<br>Utilization over 50%<br>EXC 2=> 10% UT<br>EXC 3=> 20% UT |  | PROJECT   | Akkasæter Lager- og vedlikeholdshall | PHASE        | 2 / Phase 2 |
|   |  | MEMBER   | Flange                               | QUANTITY:    | 4           |
|   |  | REVISION   |                                      | ISSUED:      | 07.11.2025  |
|   |  |   |                                      | DRAFTER:     | ZLL         |
|   |  |   |                                      | BIM control: | SST         |
|   |  | PROJECT No   |                                      |              | 30480-2     |
|   |  | DRAWING No.   |                                      |              | H.5         |