


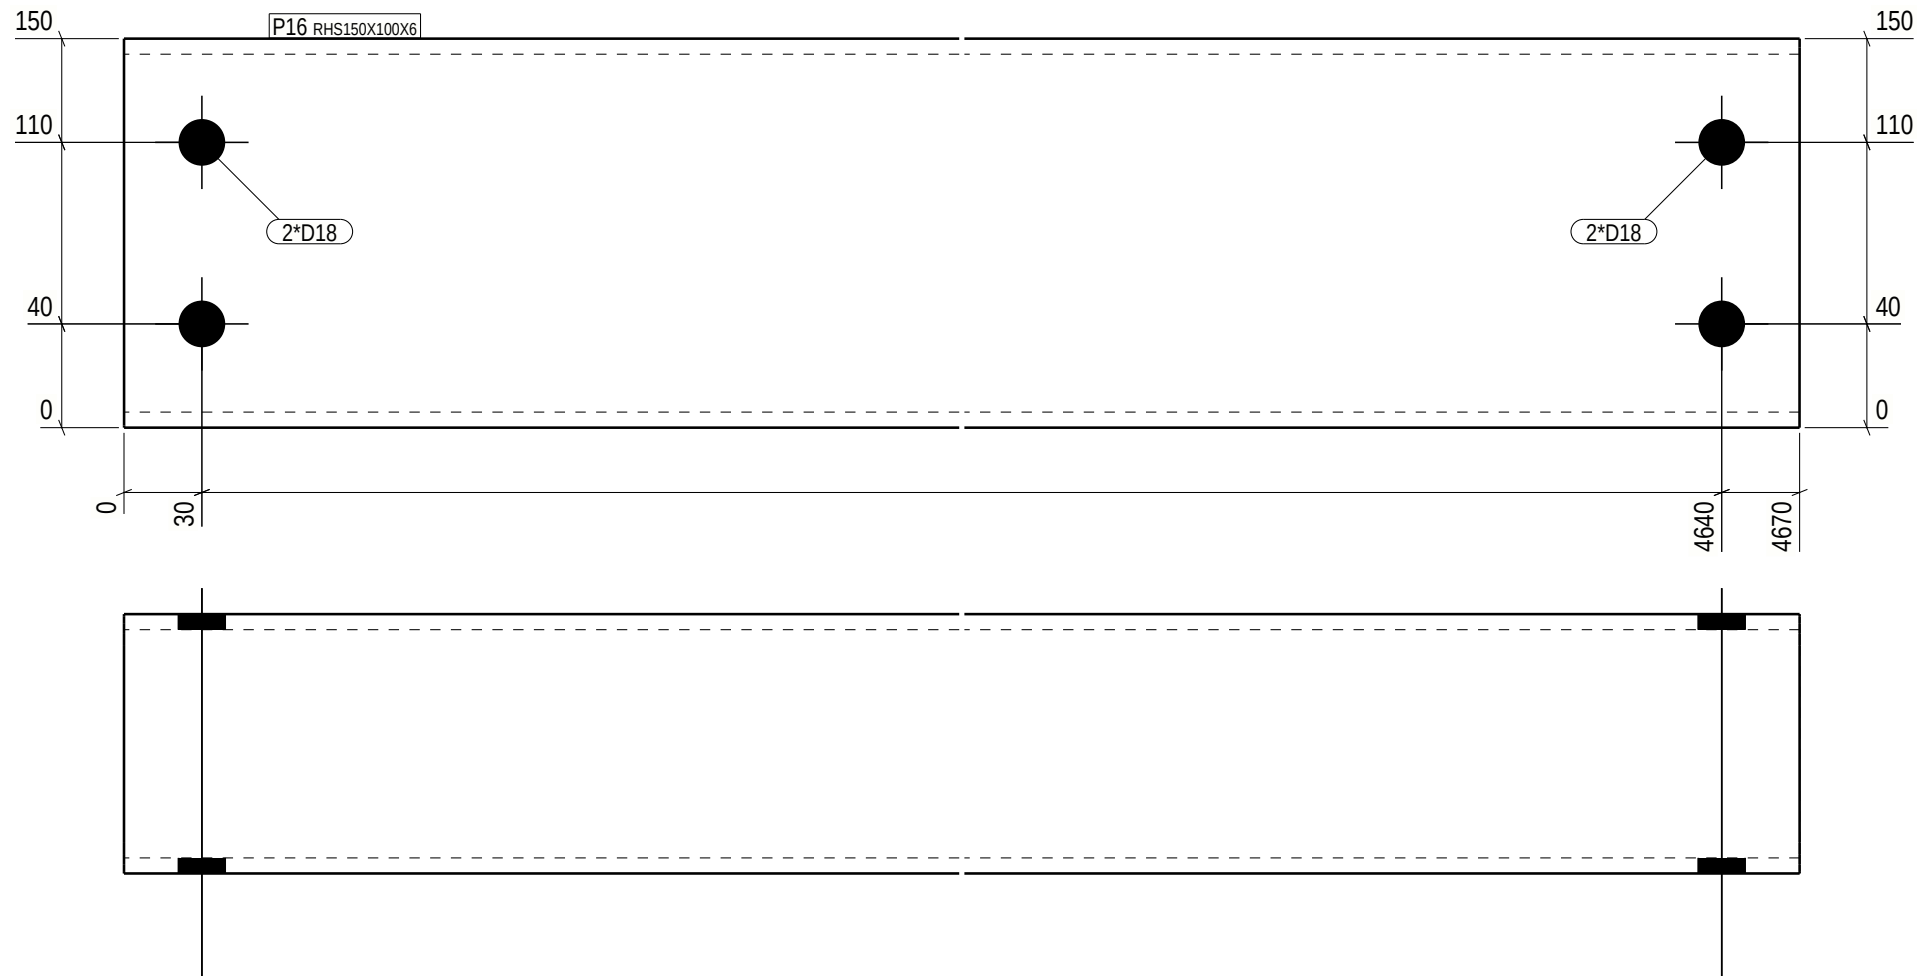

GENERAL NOTES:						
For your safety, check weight before handling:						
0-5kg Light 5-15kg Normal 15+kg Heavy						
MATERIAL LIST FOR PART - P16						
4 PARTS REQUIRED						
POS. No.	PROFILE	No.	GRADE	L (mm)	AREA (m ²)	WEIGHT (kg)
P16	RHS150X100X6	1	S355J2H	4670	2.2	101.0 !!
TOTAL WEIGHT FOR				4	PARTS	403.9

Part list	Qty.
OP	4

Execution class: EXC 2		* o 3 0 4 8 0 - 2 *  DS <i>Skalkonstruktion</i> * WP 1 6 *			
No utilization on drawings = over 50%					
V-SEAM Utilization under 50% EXC 2=> Acc. to process control EXC 3=> 20% UT Utilization over 50% EXC 2=> 10% UT EXC 3=> 20% UT		PROJECT	Akkasæter Lager- og vedlikeholdshall	PHASE	2 / Phase 2
		MEMBER	Portomfatning	QUANTITY:	4
		REVISION		ISSUED:	07.11.2025
				DRAFTER:	ZLL
				BIM control:	SST
				PROJECT No	30480-2
				DRAWING No.	P.16