


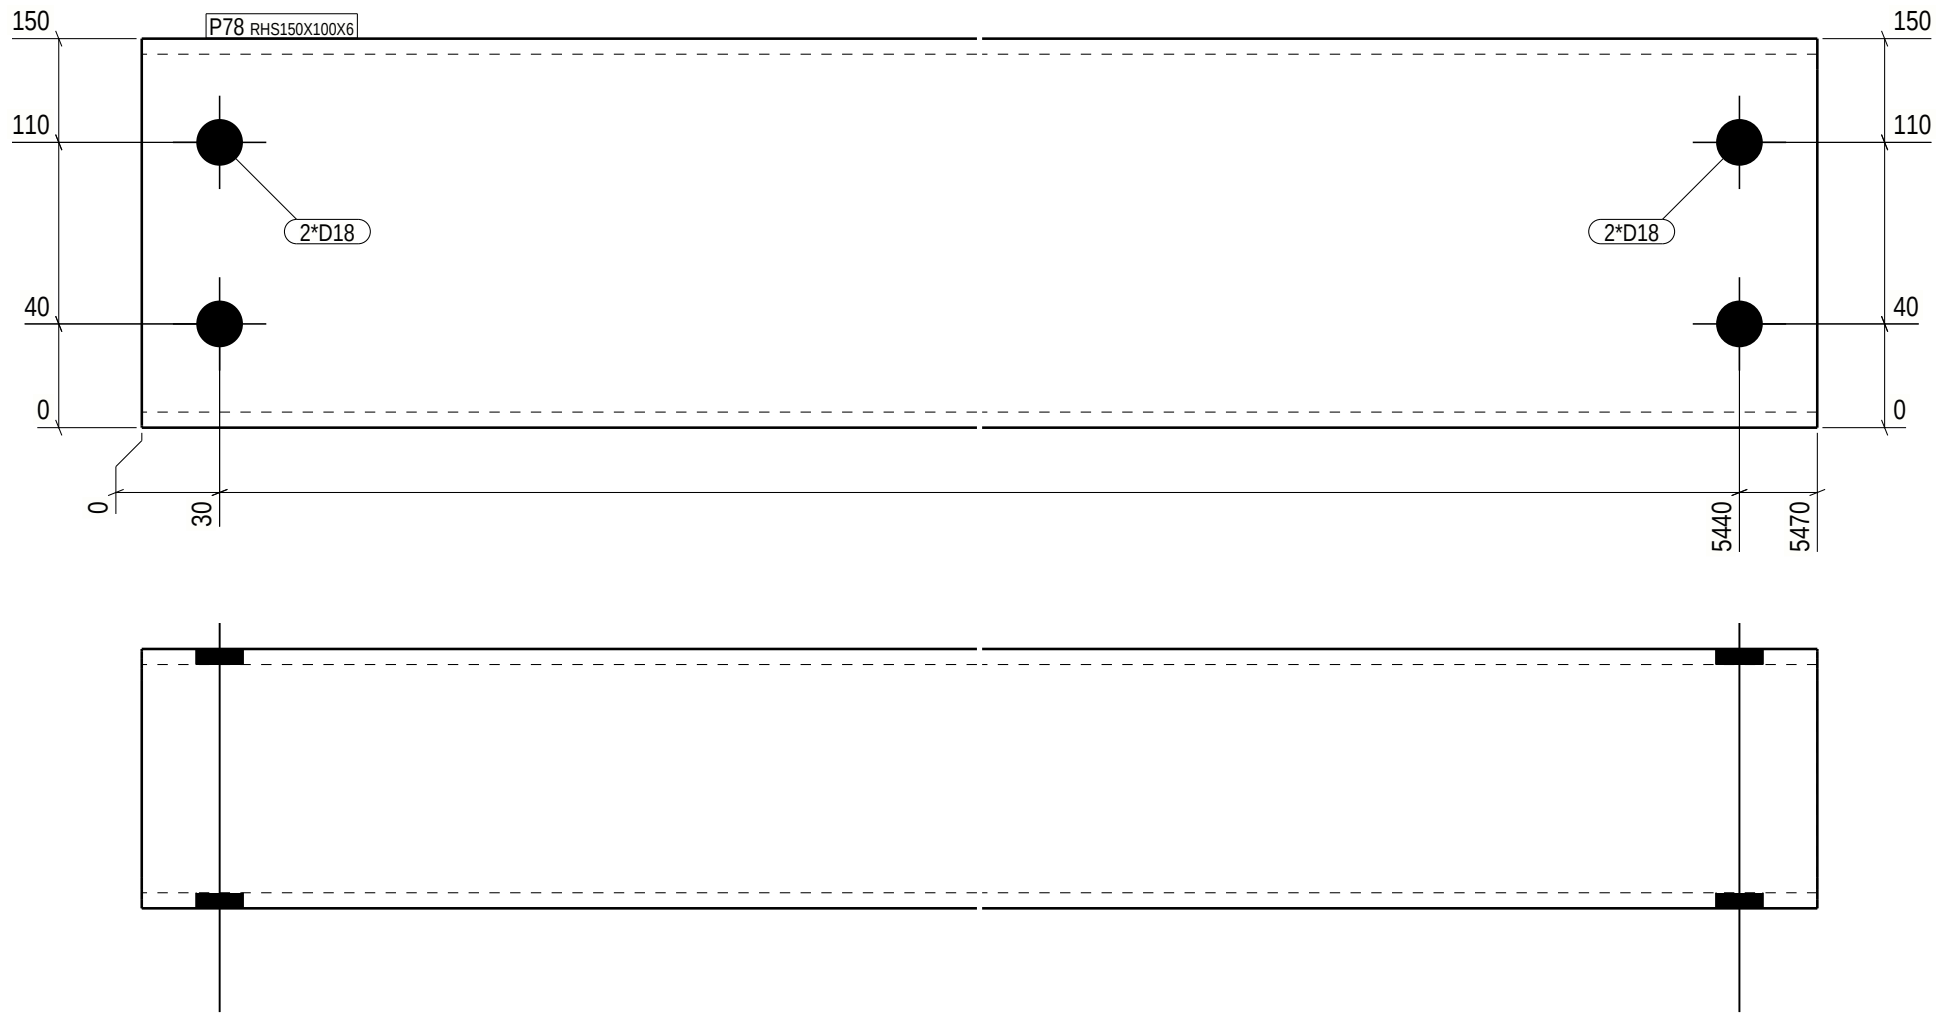

|                              |              |                                                |         |        |                        |             |
|------------------------------|--------------|------------------------------------------------|---------|--------|------------------------|-------------|
| GENERAL NOTES:               |              | For your safety, check weight before handling: |         |        |                        |             |
|                              |              | 0-5kg Light    5-15kg Normal    15+kg Heavy    |         |        |                        |             |
| MATERIAL LIST FOR PART - P78 |              | 2 PARTS REQUIRED                               |         |        |                        |             |
| POS. No.                     | PROFILE      | No.                                            | GRADE   | L (mm) | AREA (m <sup>2</sup> ) | WEIGHT (kg) |
| P78                          | RHS150X100X6 | 1                                              | S355J2H | 5470   | 2.6                    | 118.3 !!    |
| TOTAL WEIGHT FOR             |              | 2                                              | PARTS   | 236.6  |                        |             |

|           |      |
|-----------|------|
| Part list | Qty. |
| OP        | 2    |

|                                       |  |
|---------------------------------------|--|
| Execution class: EXC 2                |  |
| No utilization on drawings = over 50% |  |
| V-SEAM                                |  |
| Utilization under 50%                 |  |
| EXC 2=> Acc. to process control       |  |
| EXC 3=> 20% UT                        |  |
| Utilization over 50%                  |  |
| EXC 2=> 10% UT                        |  |
| EXC 3=> 20% UT                        |  |

|                     |                                      |                     |           |             |                    |
|---------------------|--------------------------------------|---------------------|-----------|-------------|--------------------|
| * o 3 0 4 8 0 - 2 * |                                      | DS Skalkonstruktion |           | * WP 7 8 *  |                    |
| PROJECT             | Akkasæter Lager- og vedlikeholdshall |                     | PHASE     | 2 / Phase 2 |                    |
| MEMBER              | Portomfatning                        |                     | QUANTITY: | 2           | PROJECT No 30480-2 |
| REVISION            | ISSUED: 07.11.2025                   |                     | DRAFTER:  | ZLL         | DRAWING No. P.78   |
|                     |                                      | BIM control:        |           | SST         |                    |