


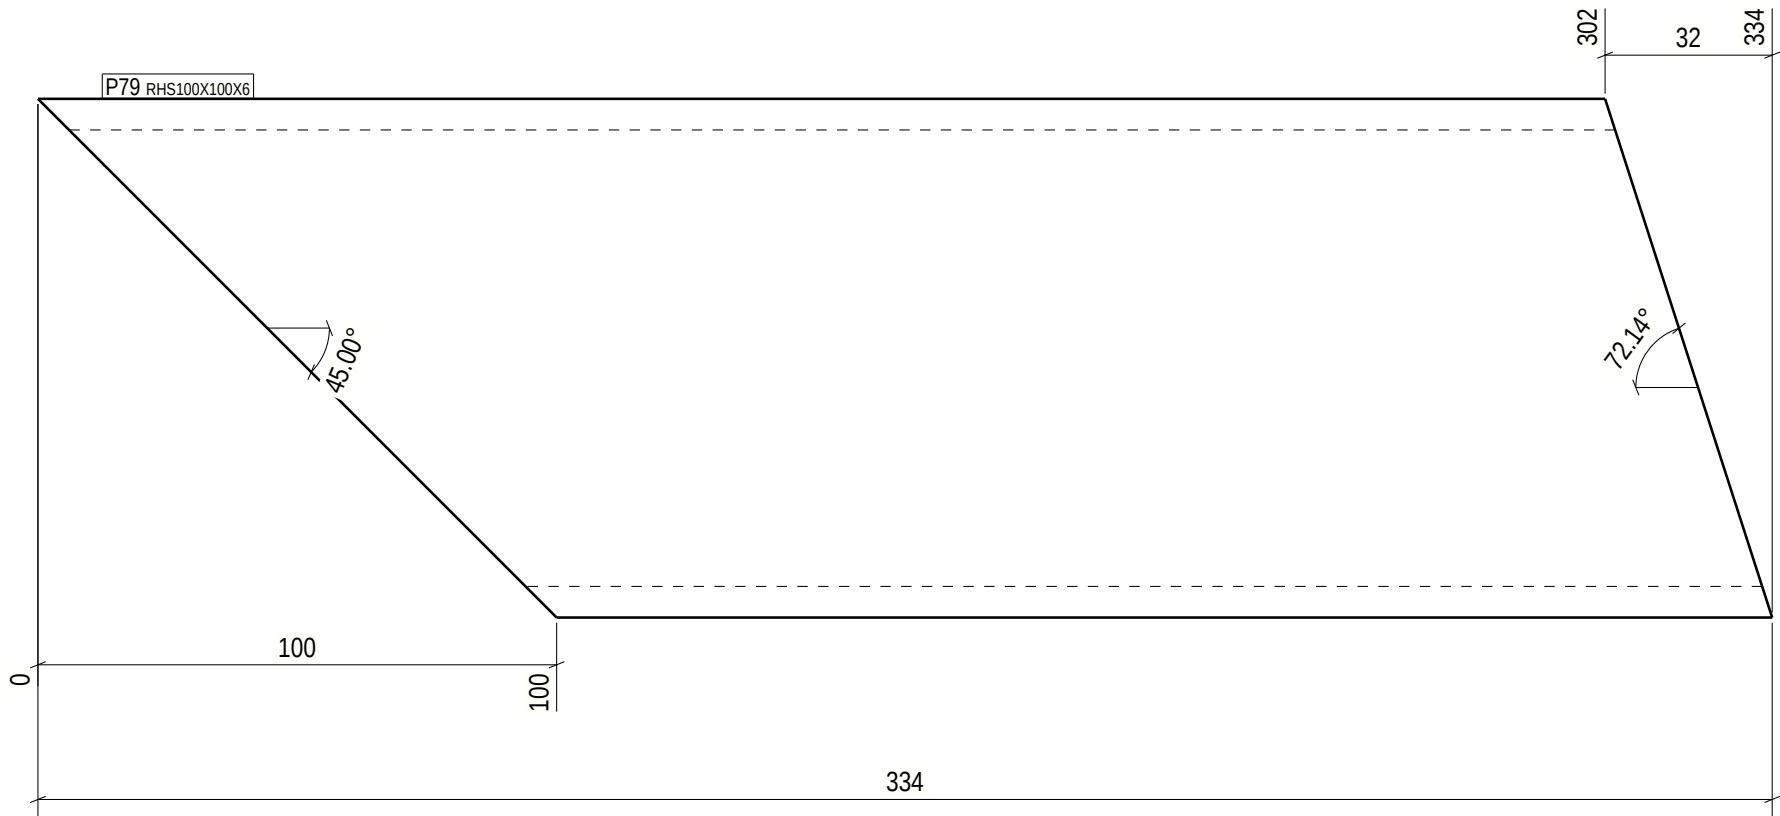

GENERAL NOTES:						
For your safety, check weight before handling:						
0-5kg Light 5-15kg Normal 15+kg Heavy						
MATERIAL LIST FOR PART - P79						
2 PARTS REQUIRED						
POS. No.	PROFILE	No.	GRADE	L (mm)	AREA (m ²)	WEIGHT (kg)
P79	RHS100X100X6	1	S355J2H	334	0.1	4.5
TOTAL WEIGHT FOR				2	PARTS	9.1

Part list	Qty.
OP	2

Execution class: EXC 2	
No utilization on drawings = over 50%	
V-SEAM	
Utilization under 50%	
EXC 2=> Acc. to process control	
EXC 3=> 20% UT	
Utilization over 50%	
EXC 2=> 10% UT	
EXC 3=> 20% UT	

* o 3 0 4 8 0 - 2 *  DS <i>Skalkonstruktion</i> * WP 7 9 *			
PROJECT	Akkasæter Lager- og vedlikeholdshall		PHASE 2 / Phase 2
MEMBER	Portomfatning		QUANTITY: 2 PROJECT No 30480-2
REVISION	ISSUED: 07.11.2025		DRAFTER: ZLL BIM control: SST DRAWING No. P.79