


Tekla Structures

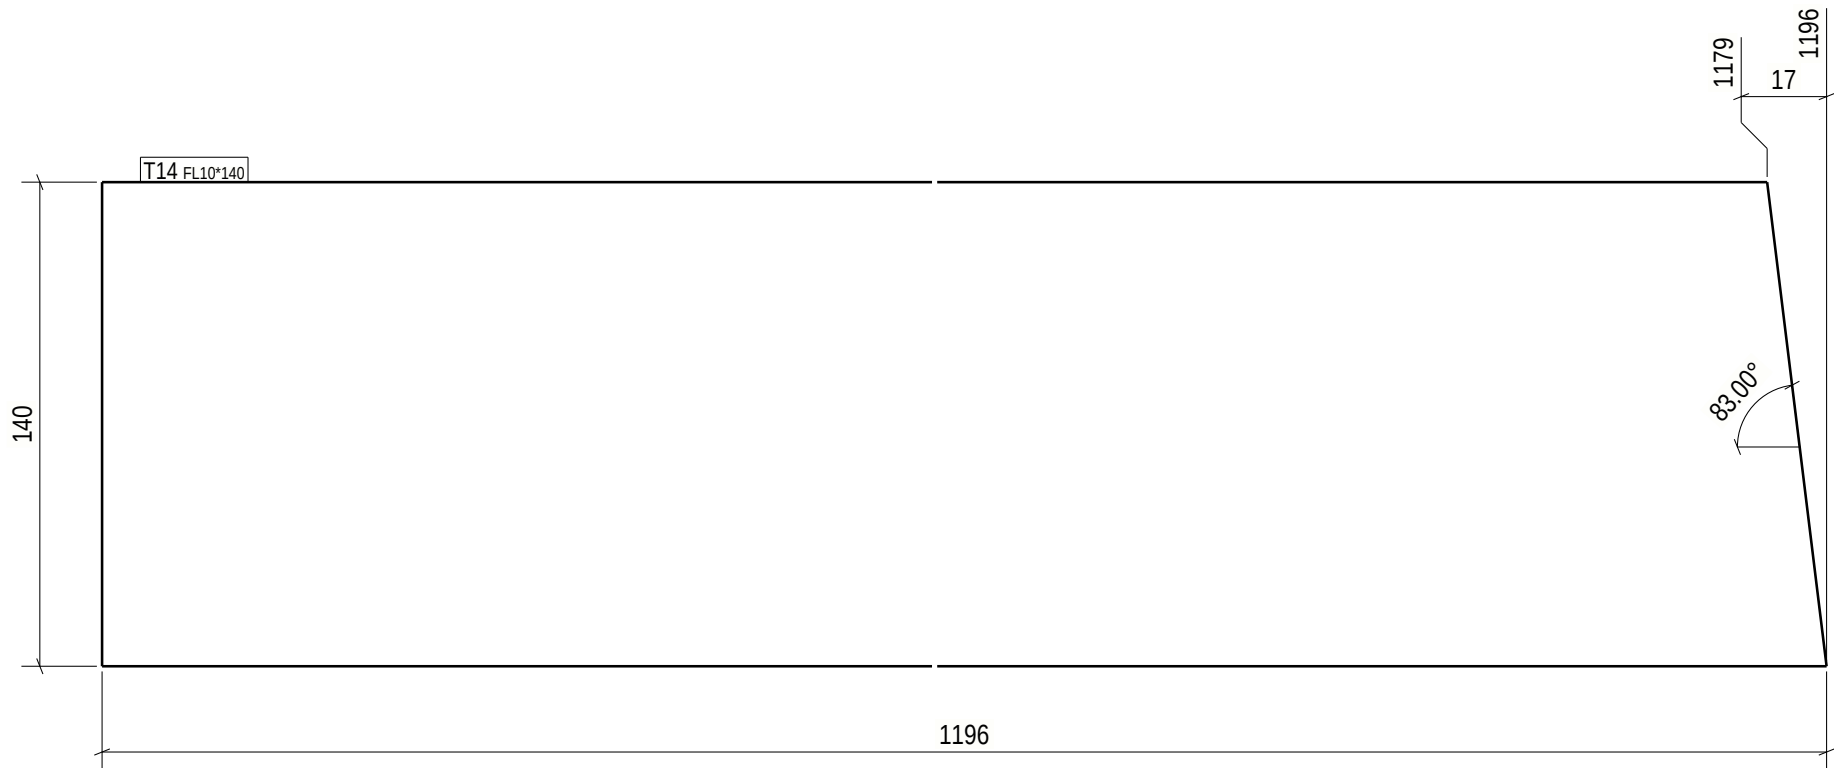

GENERAL NOTES:

For your safety, check weight before handling:
0-5kg Light 5-15kg Normal 15+kg Heavy

MATERIAL LIST FOR PART - T14

2 PARTS REQUIRED

POS. No.	PROFILE	No.	GRADE	L (mm)	AREA (m ²)	WEIGHT (kg)
T14	FL10*140	1	S355J2	1196	0.4	13.0

TOTAL WEIGHT FOR 2 PARTS 26.1

Part list	Qty.
GS	2

Execution class: EXC 2

No utilization on drawings = over 50%

V-SEAM
Utilization under 50%
EXC 2=> Acc. to process control
EXC 3=> 20% UT
Utilization over 50%
EXC 2=> 10% UT
EXC 3=> 20% UT

* o 3 0 4 8 0 - 2 *



DS Steelkonstruktion

* W T 1 4 *

PROJECT	Akkasæter Lager- og vedlikeholdshall		PHASE	2 / Phase 2	
MEMBER	Opstik		QUANTITY:	2	PROJECT No 30480-2
REVISION		ISSUED: 07.11.2025	DRAFTER: ZLL BIM control: SST		DRAWING No. T.14