


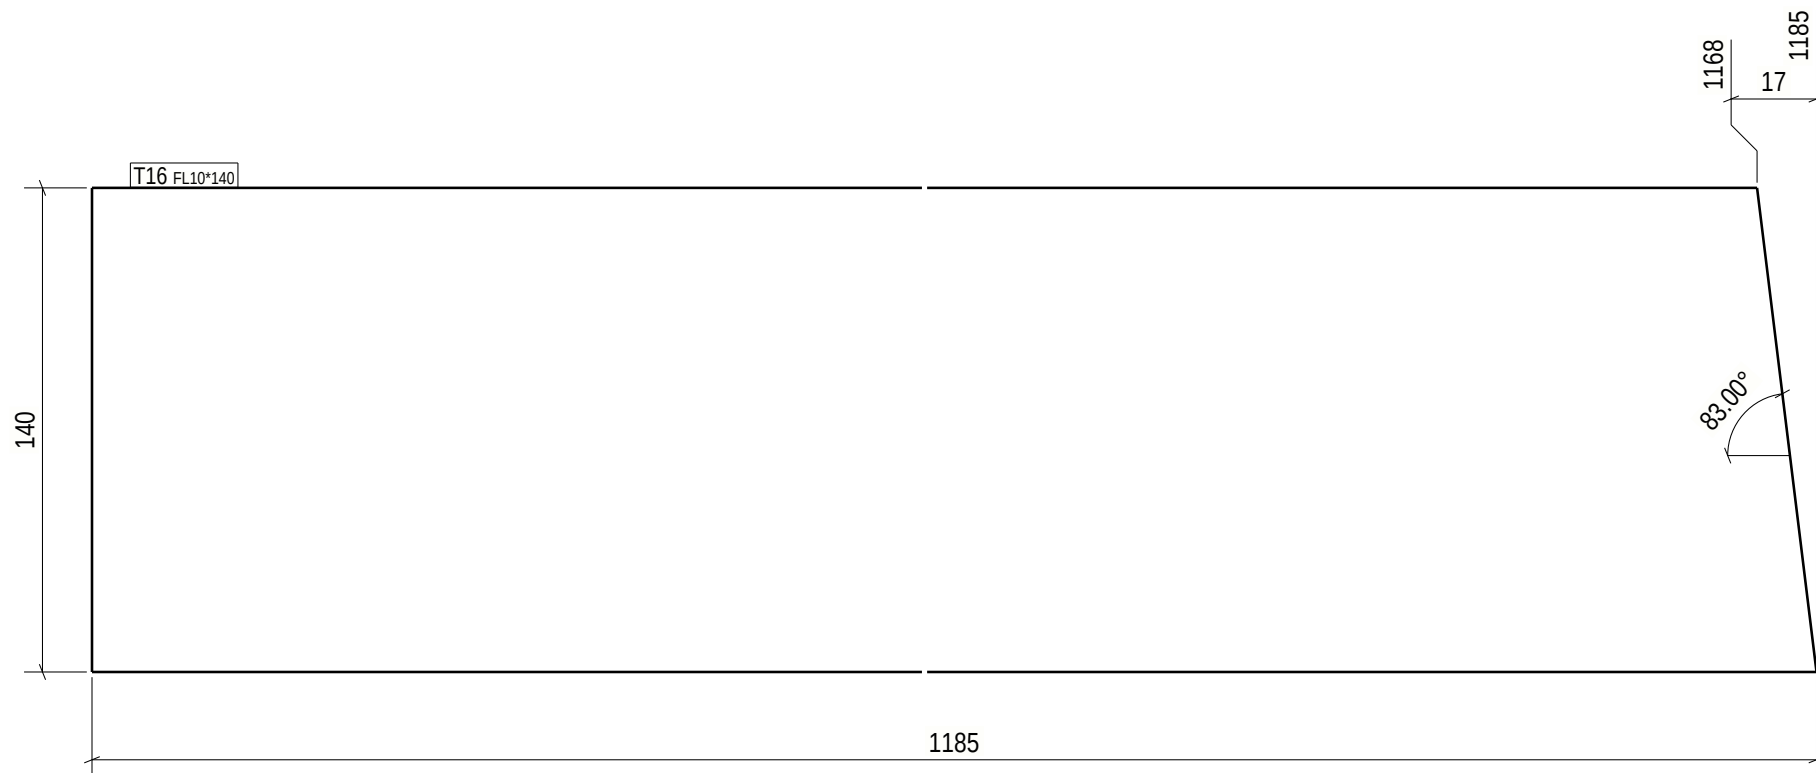

GENERAL NOTES:

MATERIAL LIST FOR PART - T16

POS. No.	PROFILE	No.	GRADE	L (mm)	AREA (m ²)	WEIGHT (kg)
T16	FL10*140	1	S355J2	1185	0.4	12.9

Execution class: EXC 2

* 0 3 0 4 8 0 - 2 *

PROJECT	Akksæter Lager- og vedlikeholdshall				PHASE	2 / Phase 2	
MEMBER	Opstik		QUANTITY:		2	PROJECT No	30480-2
REVISION		ISSUED: 07.11.2025	DRAFTER: BIM Control:	ZLL SSI	DRAWING No.		T.16