


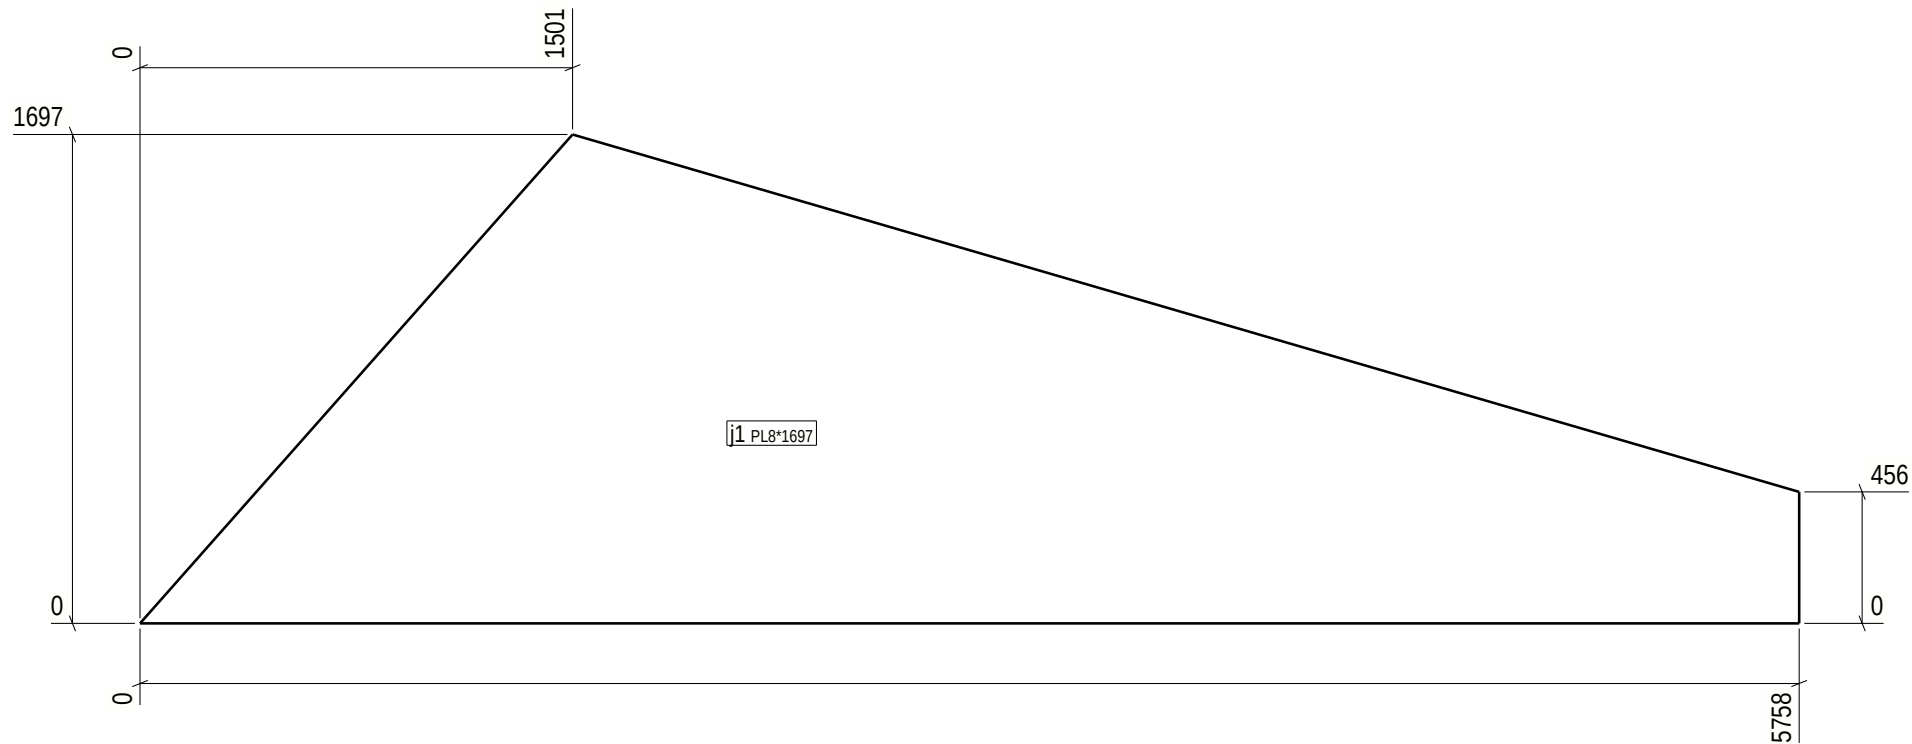

## GENERAL NOTES:

For your safety, check weight before handling:  
0-5kg Light 5-15kg Normal 15+kg Heavy

## MATERIAL LIST FOR PART - j1

## 1 PARTS REQUIRED

| POS. No.         | PROFILE  | No. | GRADE  | L (mm) | AREA (m <sup>2</sup> ) | WEIGHT (kg) |
|------------------|----------|-----|--------|--------|------------------------|-------------|
| j1               | PL8*1697 | 1   | S355J2 | 5758   | 11.8                   | 367.7 !!    |
| TOTAL WEIGHT FOR |          |     |        | 1      | PARTS                  | 367.7       |

| Part list | Qty. |
|-----------|------|
| BN        | 1    |

## Execution class: EXC 2

No utilization on drawings = over 50%

V-SEAM  
Utilization under 50%  
EXC 2=> Acc. to process control  
EXC 3=> 20% UT  
Utilization over 50%  
EXC 2=> 10% UT  
EXC 3=> 20% UT

\* o 3 0 4 8 0 - 2 \*



DS Skalkonstruktion

\* W j 1 \*

|          |                                      |                    |                                  |             |                    |
|----------|--------------------------------------|--------------------|----------------------------------|-------------|--------------------|
| PROJECT  | Akkasæter Lager- og vedlikeholdshall |                    | PHASE                            | 2 / Phase 2 |                    |
| MEMBER   | Benkile                              |                    | QUANTITY:                        | 1           | PROJECT No 30480-2 |
| REVISION |                                      | ISSUED: 07.11.2025 | DRAFTER: ZLL<br>BIM control: SST |             | DRAWING No. j.1    |