


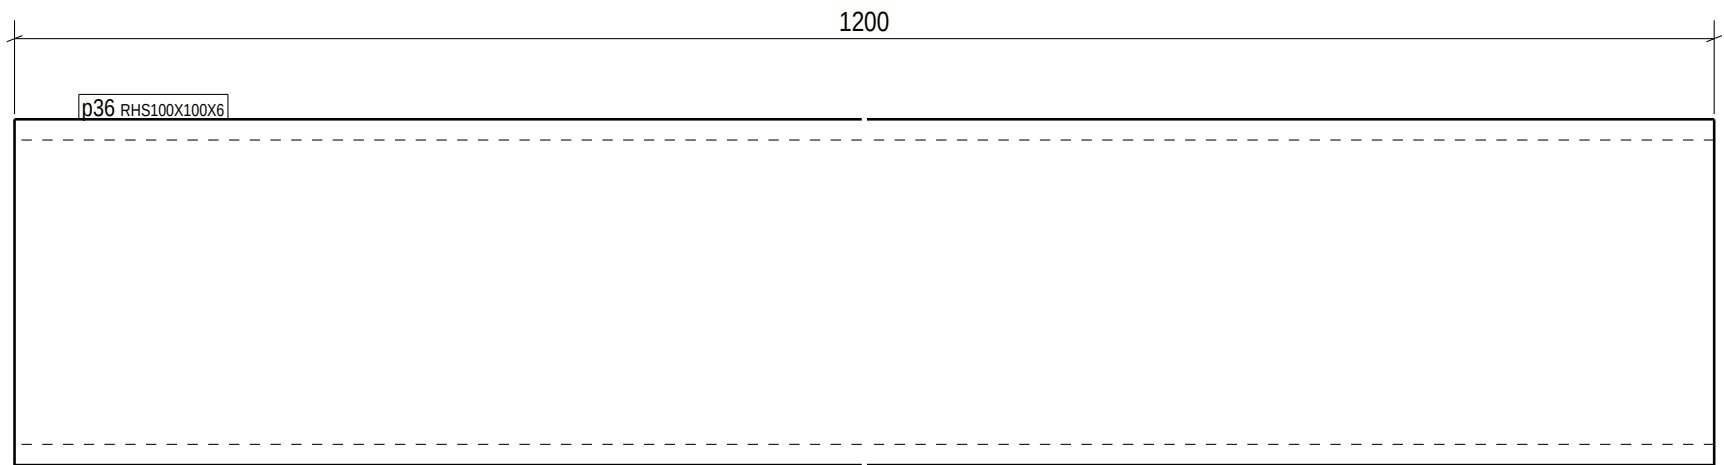

GENERAL NOTES:		For your safety, check weight before handling: 0-5kg Light 5-15kg Normal 15+kg Heavy				
MATERIAL LIST FOR PART - p36		18 PARTS REQUIRED				
POS. No.	PROFILE	No.	GRADE	L (mm)	AREA (m ²)	WEIGHT (kg)
p36	RHS100X100X6	1	S355J2H	1200	0.5	20.3 !!
TOTAL WEIGHT FOR		18	PARTS	365.3		

Execution class: EXC 2		* o 3 0 4 8 0 - 2 *  DS <i>Skalkonstruktion</i> * W p 3 6 *			
No utilization on drawings = over 50%		PROJECT	Akkasæter Lager- og vedlikeholdshall	PHASE	2 / Phase 2
V-SEAM Utilization under 50% EXC 2=> Acc. to process control EXC 3=> 20% UT		MEMBER	Portomfatning	QUANTITY:	18
Utilization over 50% EXC 2=> 10% UT EXC 3=> 20% UT		REVISION		ISSUED:	07.11.2025
				DRAFTER:	ZLL
				BIM control:	SST
		DRAWING No.		30480-2	
				p.36	