


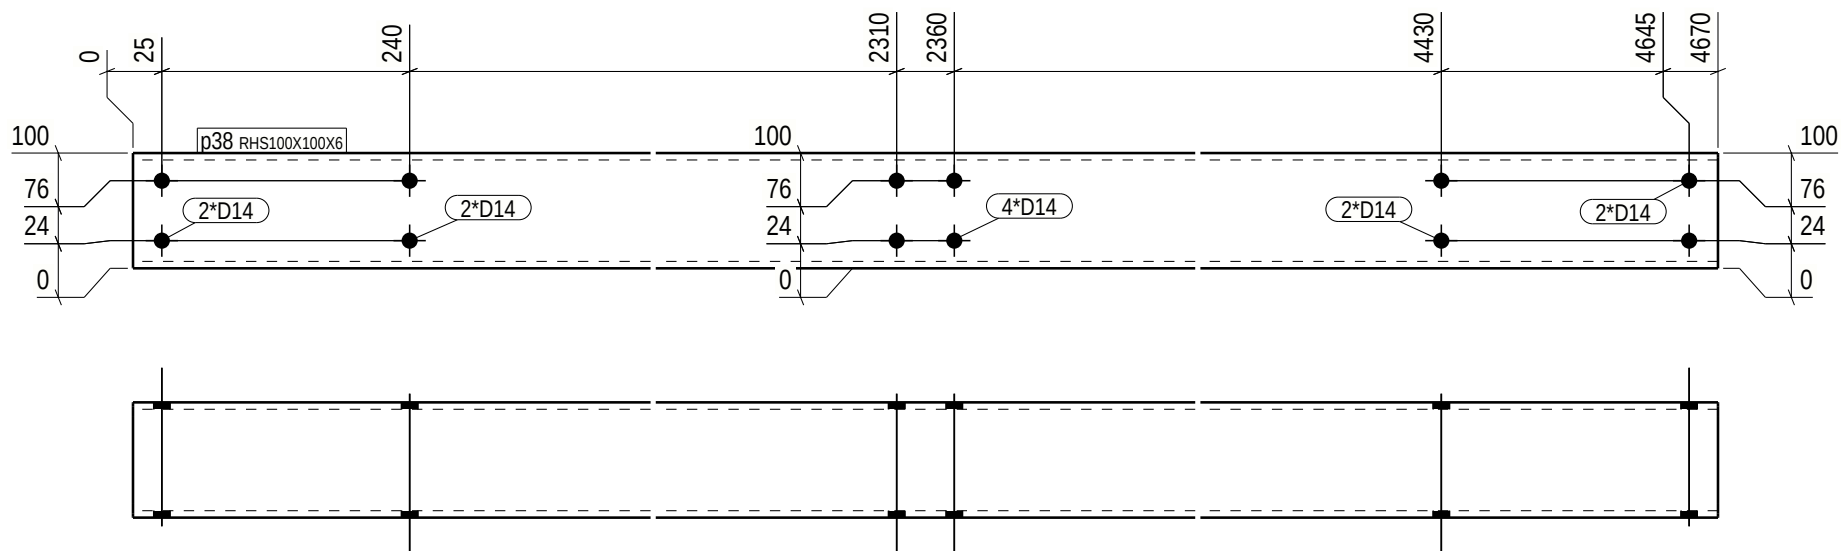

|   |              |     |         |                  |                        |             |
|---|--------------|-----|---------|------------------|------------------------|-------------|
| GENERAL NOTES: For your safety, check weight before handling:<br>0-5kg Light 5-15kg Normal 15+kg Heavy |              |     |         |                  |                        |             |
| MATERIAL LIST FOR PART - p38                                                                           |              |     |         | 2 PARTS REQUIRED |                        |             |
| POS. No.                                                                                               | PROFILE      | No. | GRADE   | L (mm)           | AREA (m <sup>2</sup> ) | WEIGHT (kg) |
| p38   | RHS100X100X6 | 1   | S355J2H | 4670             | 1.8                    | 79.0 !!     |
| TOTAL WEIGHT FOR                                                                                       |              |     |         | 2                | PARTS                  | 158.0       |

|           |      |
|-----------|------|
| Part list | Qty. |
| OP        | 2    |

|   |  |   |                                      |  |                                                   |
|---|--|---|--------------------------------------|--|---------------------------------------------------|
| Execution class: EXC 2   |  | * o 3 0 4 8 0 - 2 *  DS <i>Skalkonstruktion</i> * W p 3 8 * |                                      |  |                                                   |
| No utilization on drawings = over 50%   |  | PROJECT   | Akkasæter Lager- og vedlikeholdshall |  | PHASE 2 / Phase 2                                 |
| V-SEAM<br>Utilization under 50%<br>EXC 2=> Acc. to process control<br>EXC 3=> 20% UT<br>Utilization over 50%<br>EXC 2=> 10% UT<br>EXC 3=> 20% UT |  | MEMBER   | Portomfatning                        |  | QUANTITY: 2 PROJECT No 30480-2                    |
|   |  | REVISION   | ISSUED: 07.11.2025                   |  | DRAFTER: ZLL<br>BIM control: SST DRAWING No. p.38 |