


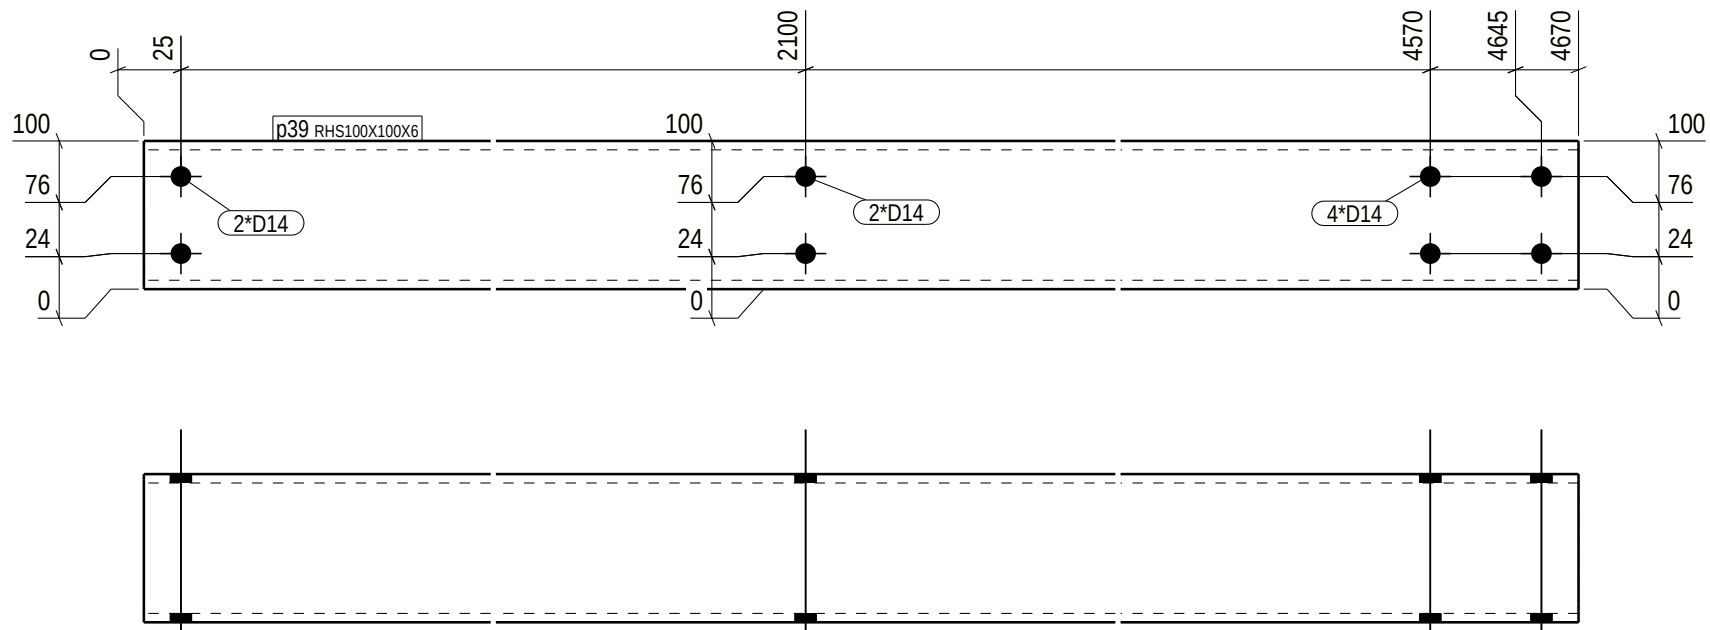

GENERAL NOTES: For your safety, check weight before handling: 0-5kg Light 5-15kg Normal 15+kg Heavy						
MATERIAL LIST FOR PART - p39				1 PARTS REQUIRED		
POS. No.	PROFILE	No.	GRADE	L (mm)	AREA (m ²)	WEIGHT (kg)
p39	RHS100X100X6	1	S355J2H	4670	1.8	79.0 !!
TOTAL WEIGHT FOR				1	PARTS	79.0

Part list	Qty.
OP	1

Execution class: EXC 2	
No utilization on drawings = over 50%	
V-SEAM Utilization under 50% EXC 2=> Acc. to process control EXC 3=> 20% UT Utilization over 50% EXC 2=> 10% UT EXC 3=> 20% UT	

* o 3 0 4 8 0 - 2 *  DS <i>Skalkonstruktion</i> * W p 3 9 *			
PROJECT	Akkasæter Lager- og vedlikeholdshall	PHASE	2 / Phase 2
MEMBER	Portomfatning	QUANTITY:	1
REVISION		DRAFTER:	ZLL
	ISSUED: 07.11.2025	BIM control:	SST
		PROJECT No	30480-2
		DRAWING No.	p.39