


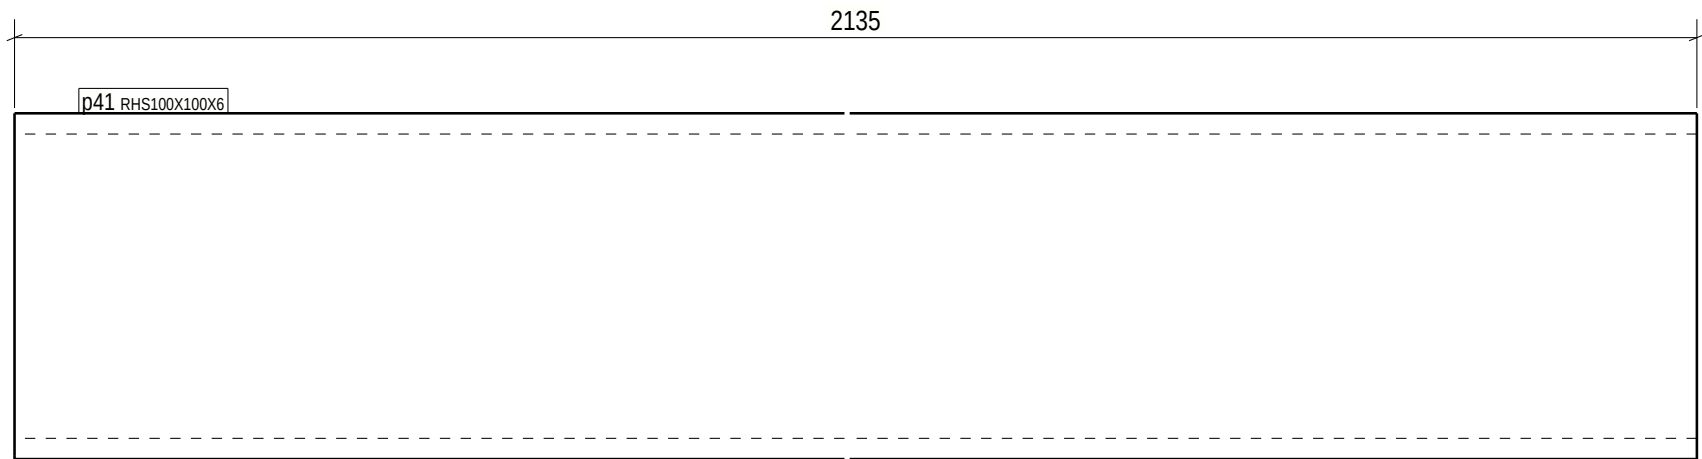

GENERAL NOTES:		For your safety, check weight before handling:				
		0-5kg Light 5-15kg Normal 15+kg Heavy				
MATERIAL LIST FOR PART - p41		1 PARTS REQUIRED				
POS. No.	PROFILE	No.	GRADE	L (mm)	AREA (m ²)	WEIGHT (kg)
p41	RHS100X100X6	1	S355J2H	2135	0.8	36.1 !!
TOTAL WEIGHT FOR		1	PARTS	36.1		

Execution class: EXC 2	
No utilization on drawings = over 50%	
V-SEAM Utilization under 50% EXC 2=> Acc. to process control EXC 3=> 20% UT Utilization over 50% EXC 2=> 10% UT EXC 3=> 20% UT	
Part list	Qty.
OP	1

* o 3 0 4 8 0 - 2 *  DS <i>Skalkonstruktion</i> * W p 4 1 *			
PROJECT	Akkasæter Lager- og vedlikeholdshall		PHASE 2 / Phase 2
MEMBER	Portomfatning	QUANTITY: 1	PROJECT No 30480-2
REVISION	ISSUED: 07.11.2025	DRAFTER: ZLL BIM control: SST	DRAWING No. p.41