


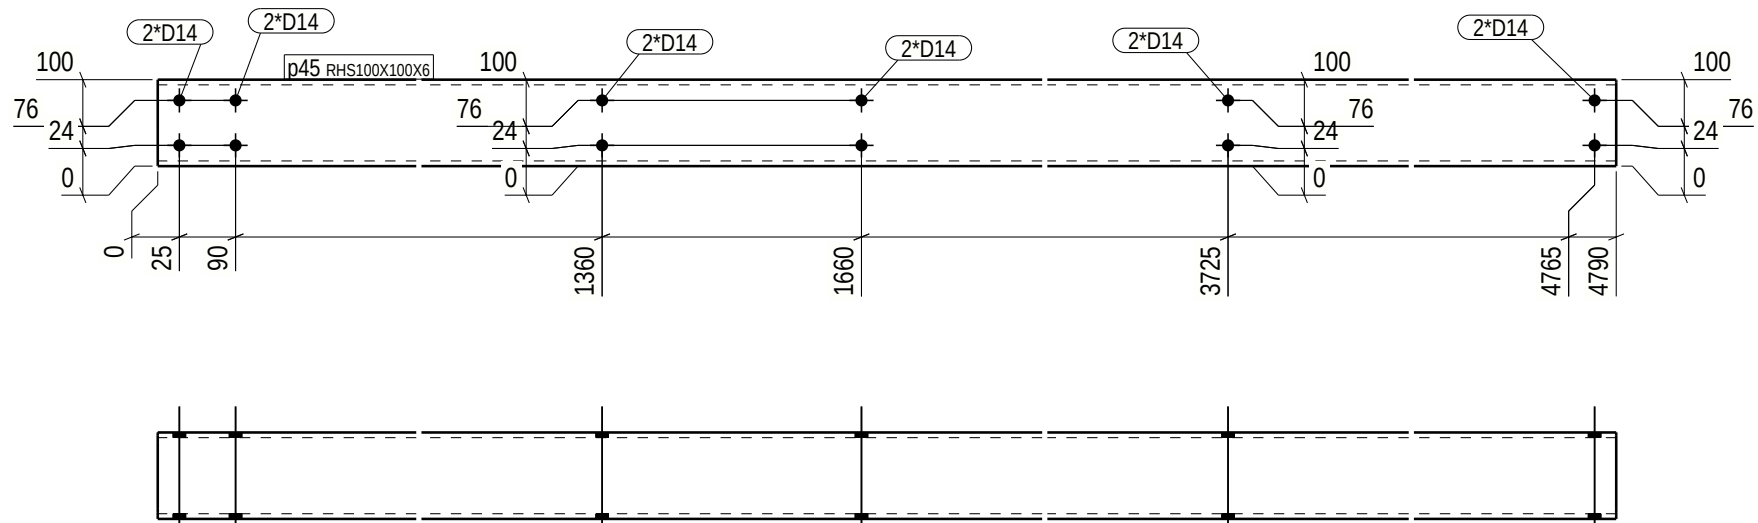

GENERAL NOTES:

For your safety, check weight before handling:
0-5kg Light 5-15kg Normal 15+kg Heavy

MATERIAL LIST FOR PART - p45 1 PARTS REQUIRED

POS. No.	PROFILE	No.	GRADE	L (mm)	AREA (m ²)	WEIGHT (kg)
p45	RHS100X100X6	1	S355J2H	4790	1.8	81.0 !!
TOTAL WEIGHT FOR				1	PARTS	81.0

Part list	Qty.
OP	1

Execution class: EXC 2

No utilization on drawings = over 50%

V-SEAM
Utilization under 50%
EXC 2=> Acc. to process control
EXC 3=> 20% UT
Utilization over 50%
EXC 2=> 10% UT
EXC 3=> 20% UT

* o 3 0 4 8 0 - 2 *  **DS** *Skalkonstruktion* * W p 4 5 *

PROJECT	Akkasæter Lager- og vedlikeholdshall		PHASE	2 / Phase 2	
MEMBER	Portomfatning		QUANTITY:	1	PROJECT No 30480-2
REVISION		ISSUED: 07.11.2025	DRAFTER: ZLL	BIM control: SST	DRAWING No. p.45