


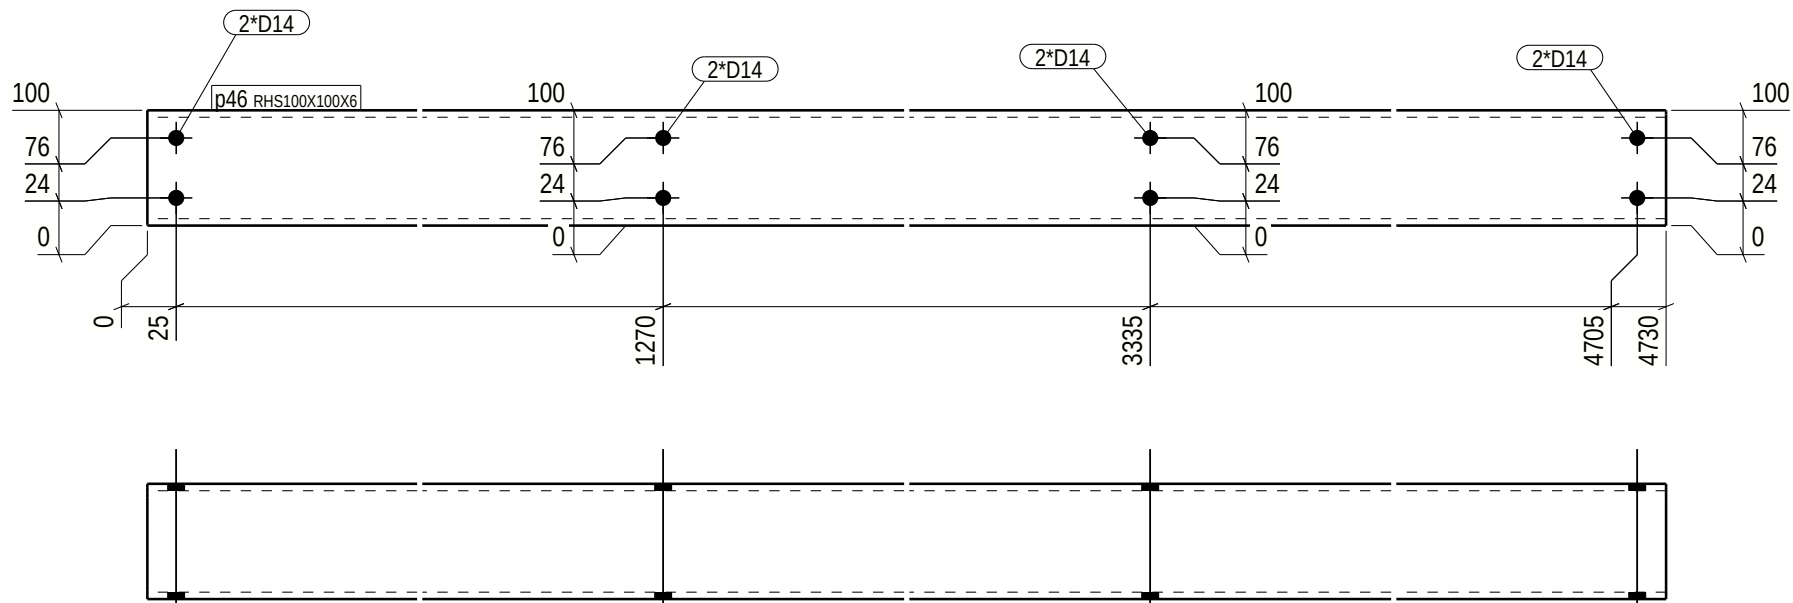

GENERAL NOTES:

For your safety, check weight before handling:
0-5kg Light 5-15kg Normal 15+kg Heavy

MATERIAL LIST FOR PART - p46

2 PARTS REQUIRED

POS. No.	PROFILE	No.	GRADE	L (mm)	AREA (m ²)	WEIGHT (kg)
p46	RHS100X100X6	1	S355J2H	4730	1.8	80.0 !!

TOTAL WEIGHT FOR 2 PARTS 160.0

Part list	Qty.
OP	2

Execution class: EXC 2

No utilization on drawings = over 50%

V-SEAM
Utilization under 50%
EXC 2=> Acc. to process control
EXC 3=> 20% UT
Utilization over 50%
EXC 2=> 10% UT
EXC 3=> 20% UT

* o 3 0 4 8 0 - 2 *



DS Skalkonstruktion

* W p 4 6 *

PROJECT	Akkasæter Lager- og vedlikeholdshall	PHASE	2 / Phase 2
MEMBER	Portomfatning	QUANTITY:	2
REVISION		ISSUED:	07.11.2025
		DRAFTER:	ZLL
		BIM control:	SST
		PROJECT No	30480-2
		DRAWING No.	p.46