


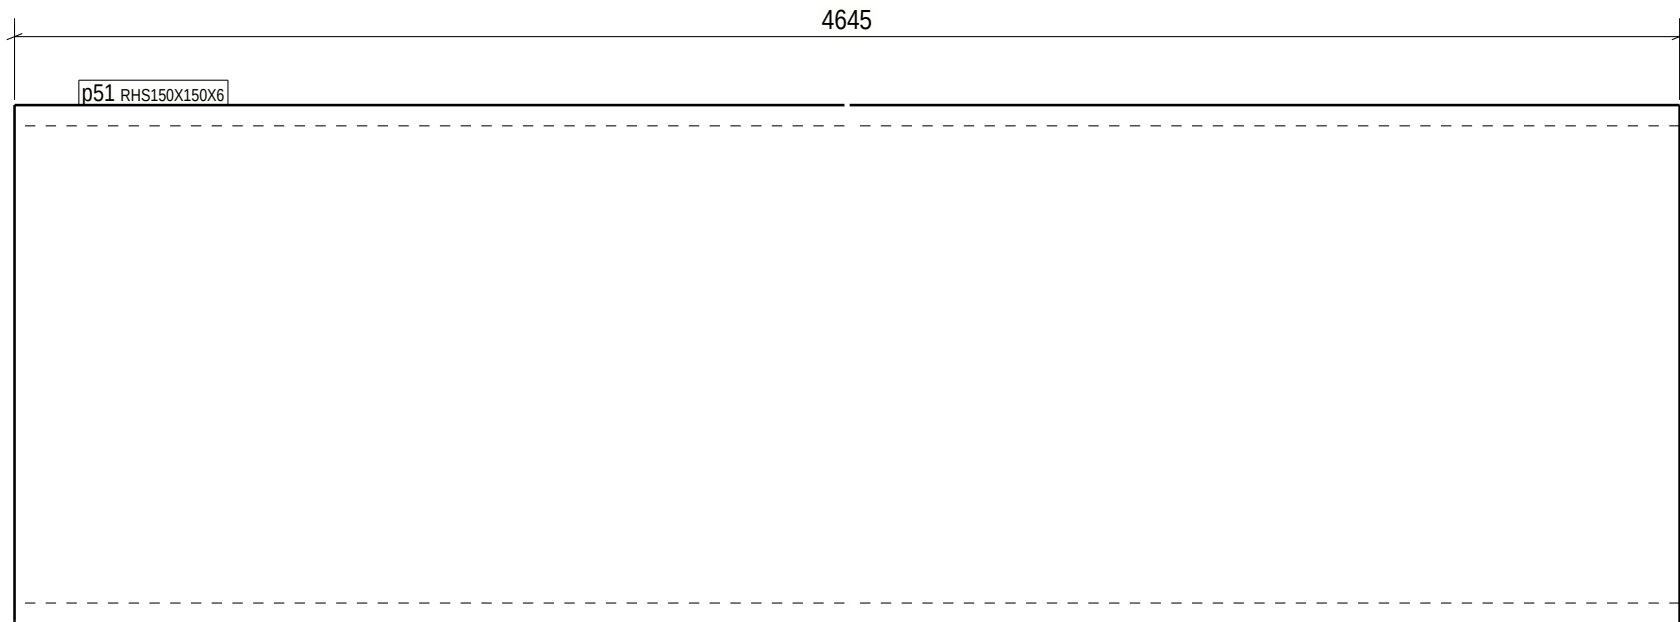

GENERAL NOTES:						
For your safety, check weight before handling:						
0-5kg Light 5-15kg Normal 15+kg Heavy						
MATERIAL LIST FOR PART - p51						
4 PARTS REQUIRED						
POS. No.	PROFILE	No.	GRADE	L (mm)	AREA (m ²)	WEIGHT (kg)
p51	RHS150X150X6	1	S355J2H	4645	2.7	122.3 !!
TOTAL WEIGHT FOR				4	PARTS	489.3

		Execution class: EXC 2		* o 3 0 4 8 0 - 2 *  DS <i>Skalkonstruktion</i> * W p 5 1 *							
		No utilization on drawings = over 50%									
		V-SEAM Utilization under 50% EXC 2=> Acc. to process control EXC 3=> 20% UT Utilization over 50% EXC 2=> 10% UT EXC 3=> 20% UT		PROJECT		Akkasæter Lager- og vedlikeholdshall		PHASE 2 / Phase 2			
Part list		Qty.		MEMBER		Portomfatning		QUANTITY: 4		PROJECT No 30480-2	
OP		4		REVISION		ISSUED: 07.11.2025		DRAFTER: ZLL BIM control: SST		DRAWING No. p.51	