


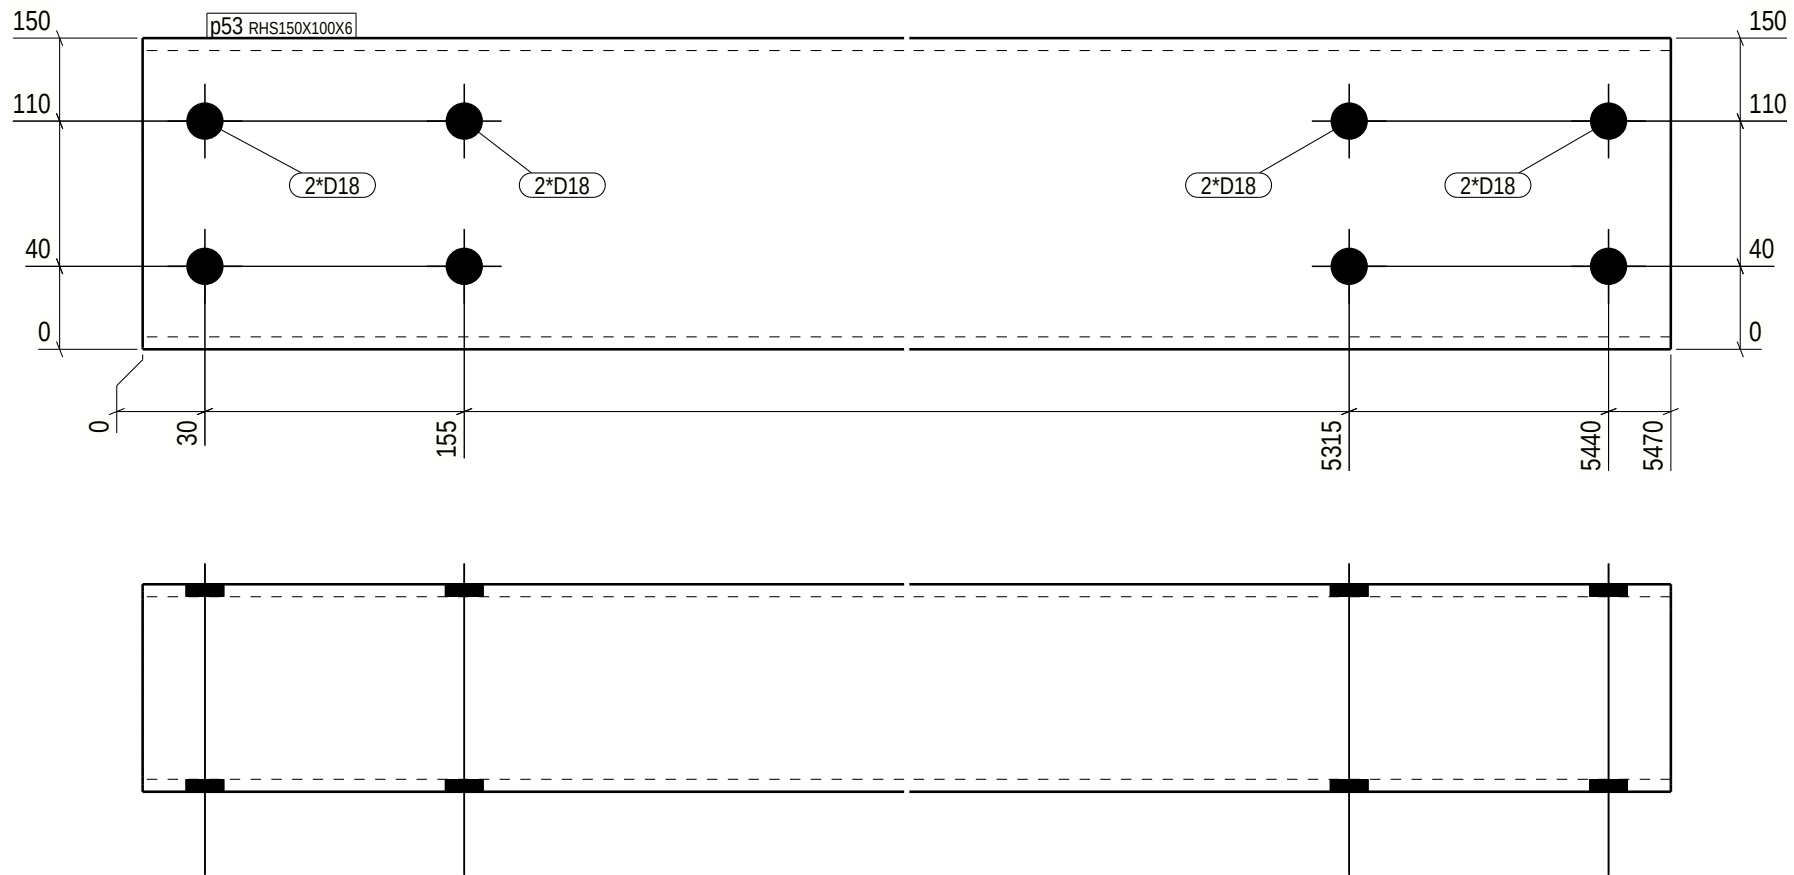

GENERAL NOTES: For your safety, check weight before handling: 0-5kg Light 5-15kg Normal 15+kg Heavy						
MATERIAL LIST FOR PART - p53				2 PARTS REQUIRED		
POS. No.	PROFILE	No.	GRADE	L (mm)	AREA (m ²)	WEIGHT (kg)
p53	RHS150X100X6	1	S355J2H	5470	2.6	118.3 !!
TOTAL WEIGHT FOR				2	PARTS	236.6

Part list	Qty.
OP	2

Execution class: EXC 2	
No utilization on drawings = over 50%	
V-SEAM Utilization under 50% EXC 2=> Acc. to process control EXC 3=> 20% UT Utilization over 50% EXC 2=> 10% UT EXC 3=> 20% UT	

* o 3 0 4 8 0 - 2 *  DS <i>Skalkonstruktion</i> * W p 5 3 *			
PROJECT	Akkasæter Lager- og vedlikeholdshall		PHASE 2 / Phase 2
MEMBER	Portomfatning	QUANTITY: 2	PROJECT No 30480-2
REVISION	ISSUED: 07.11.2025	DRAFTER: ZLL BIM control: SST	DRAWING No. p.53