
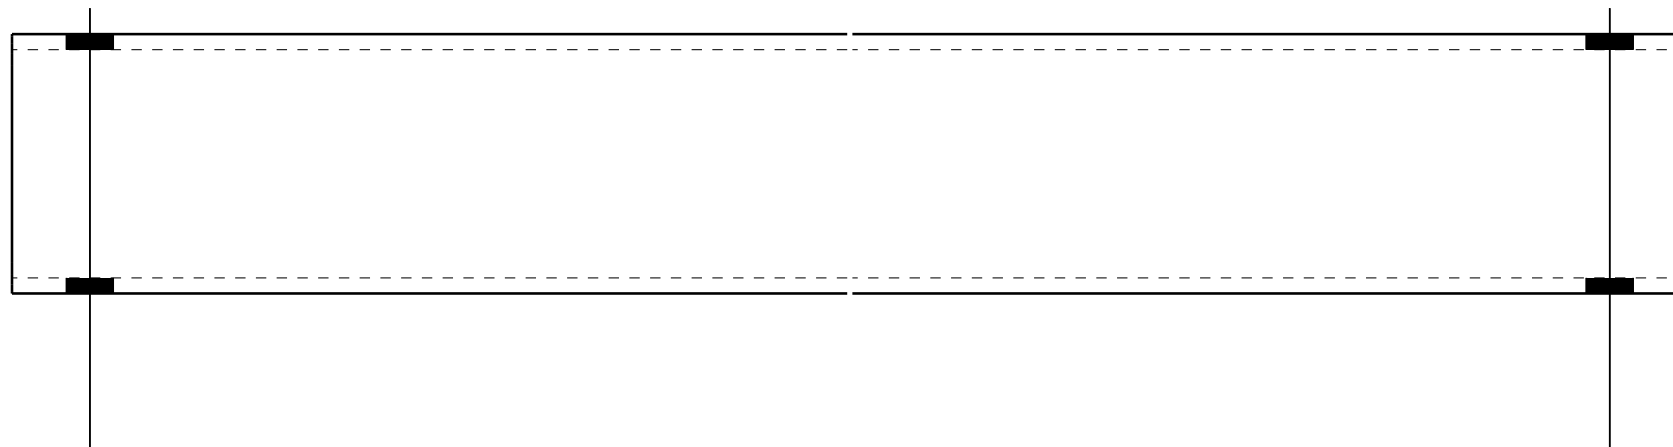


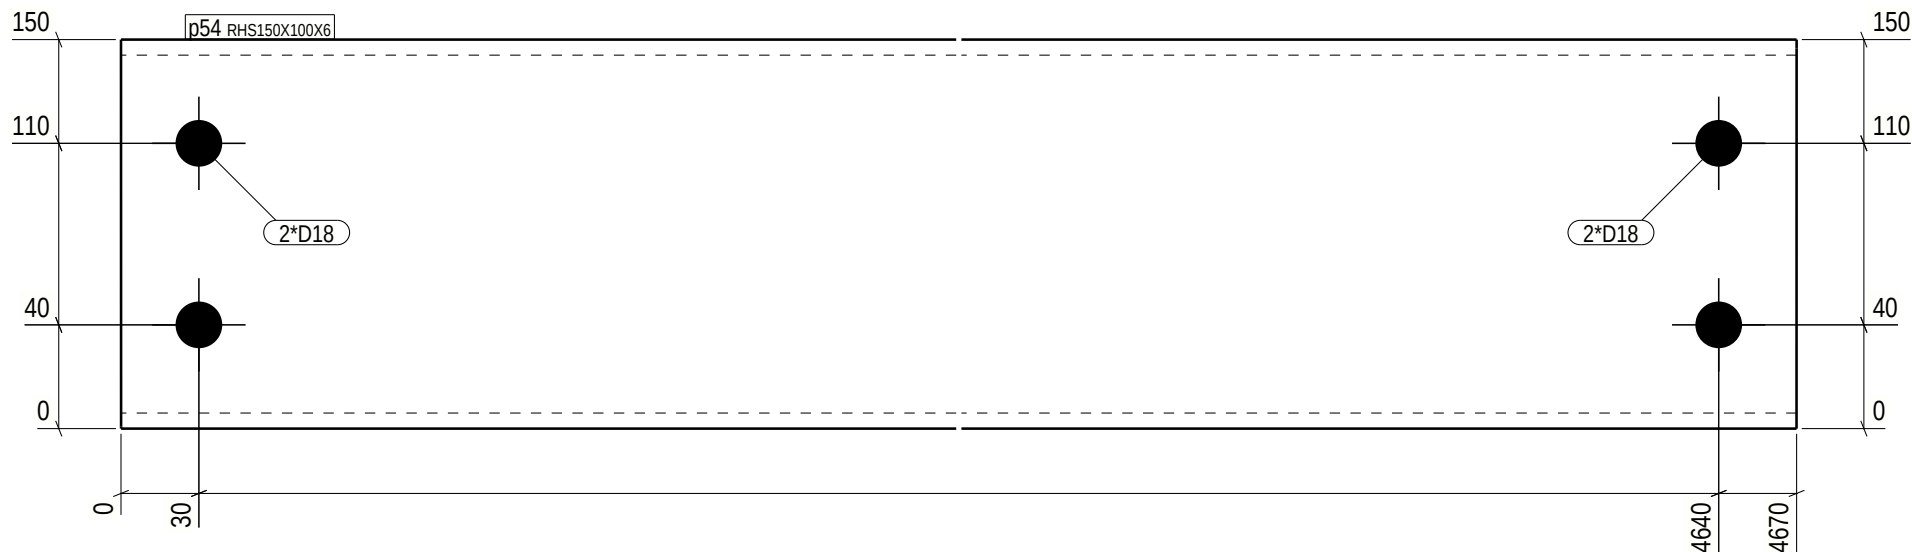

GENERAL NOTES:

For your safety, check weight before handling:
0-5kg Light 5-15kg Normal 15+kg Heavy

MATERIAL LIST FOR PART - p54

4 PARTS REQUIRED

POS. No.	PROFILE	No.	GRADE	L (mm)	AREA (m ²)	WEIGHT (kg)
p54	RHS150X100X6	1	S355J2H	4670	2.2	101.0 !!

TOTAL WEIGHT FOR 4 PARTS 403.9

Part list	Qty.
OP	4

Execution class: EXC 2

No utilization on drawings = over 50%

V-SEAM
Utilization under 50%
EXC 2=> Acc. to process control
EXC 3=> 20% UT
Utilization over 50%
EXC 2=> 10% UT
EXC 3=> 20% UT

* o 3 0 4 8 0 - 2 *



DS Steelkonstruktion

* W p 5 4 *

PROJECT	Akkasæter Lager- og vedlikeholdshall	PHASE	2 / Phase 2
MEMBER	Portomfatning	QUANTITY:	4
REVISION		DRAFTER:	ZLL
	ISSUED: 07.11.2025	BIM control:	SST
		PROJECT No	30480-2
		DRAWING No.	p.54