


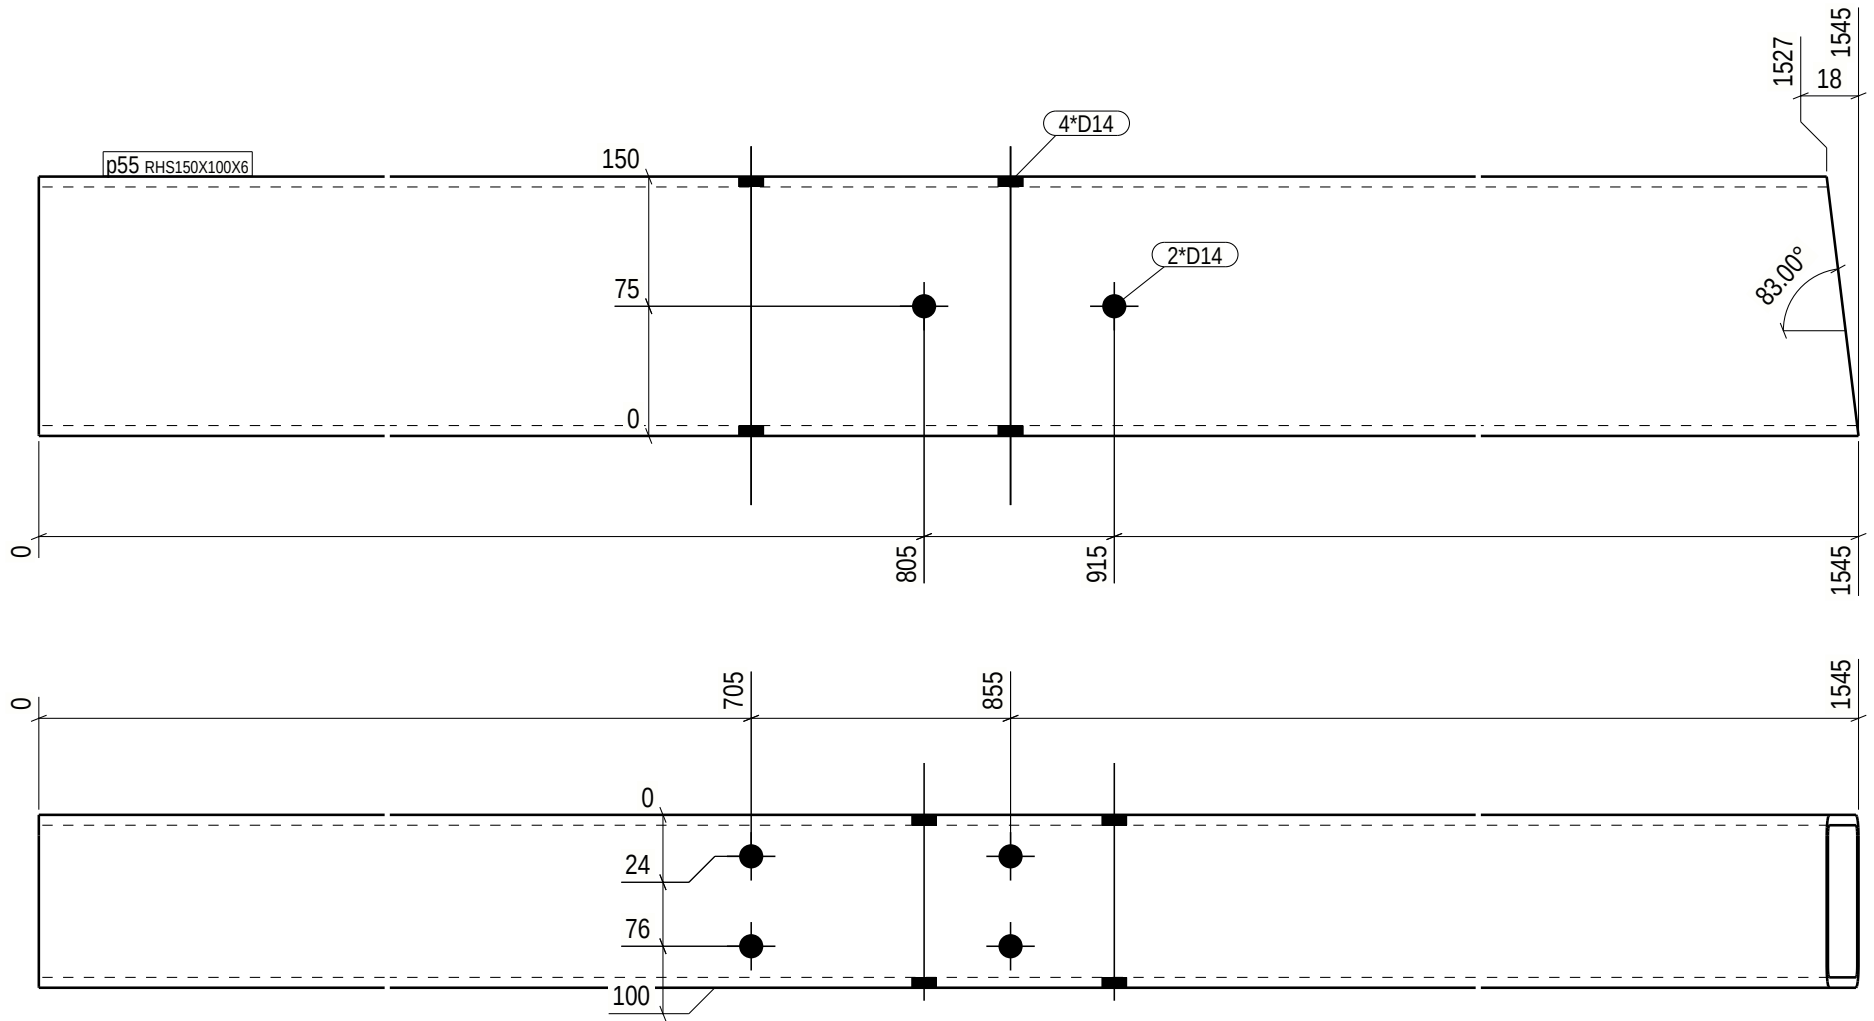

GENERAL NOTES:		For your safety, check weight before handling: 0-5kg Light 5-15kg Normal 15+kg Heavy				
MATERIAL LIST FOR PART - p55		1 PARTS REQUIRED				
POS. No.	PROFILE	No.	GRADE	L (mm)	AREA (m ²)	WEIGHT (kg)
p55	RHS150X100X6	1	S355J2H	1545	0.7	33.2 !!
TOTAL WEIGHT FOR		1	PARTS	33.2		

Execution class: EXC 2	
No utilization on drawings = over 50%	
V-SEAM Utilization under 50% EXC 2=> Acc. to process control EXC 3=> 20% UT Utilization over 50% EXC 2=> 10% UT EXC 3=> 20% UT	

* o 3 0 4 8 0 - 2 *		DS <i>Skalkonstruktion</i>		* W p 5 5 *	
PROJECT	Akkasæter Lager- og vedlikeholdshall		PHASE	2 / Phase 2	
MEMBER	Portomfatning		QUANTITY:	1	PROJECT No 30480-2
REVISION	ISSUED: 07.11.2025		DRAFTER: ZLL	BIM control: SST	DRAWING No. p.55