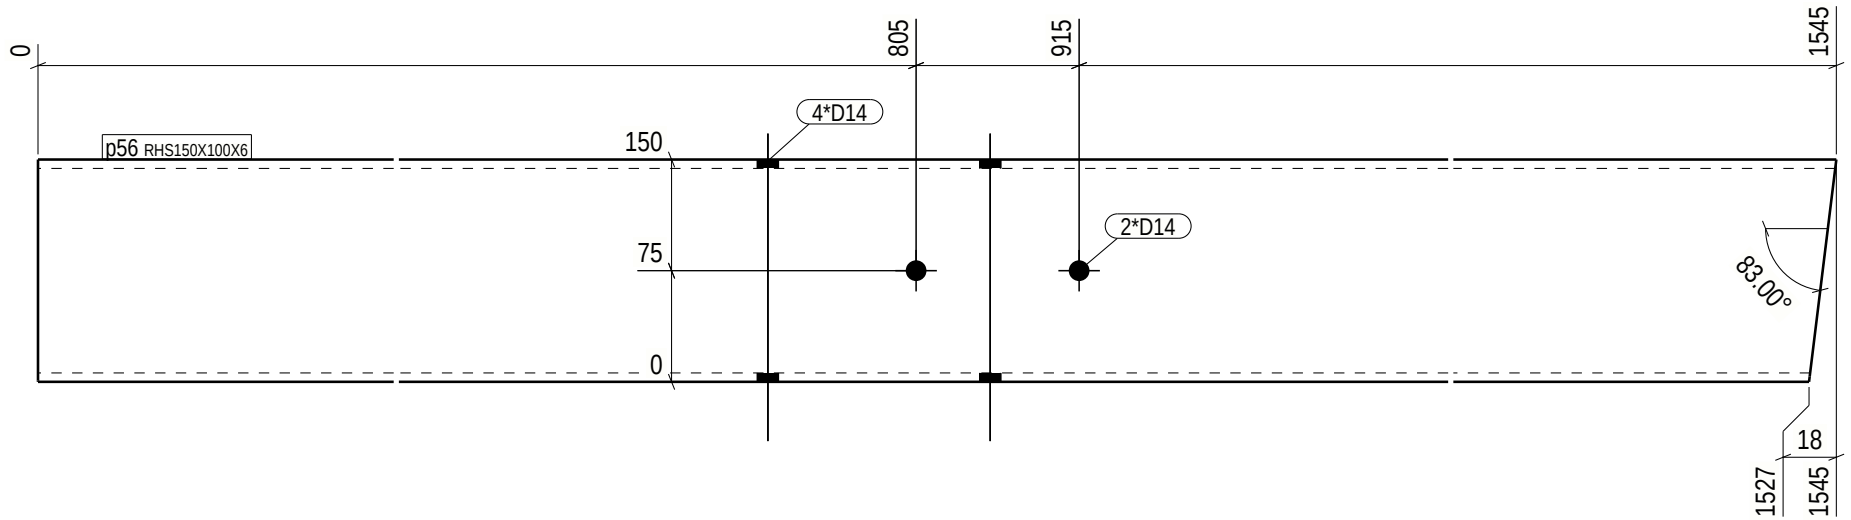


#### GENERAL NOTES:

For your safety, check weight before handling:  
0-5kg Light 5-15kg Normal 15+kg Heavy

#### MATERIAL LIST FOR PART - p56

1 PARTS REQUIRED

| POS. No. | PROFILE      | No. | GRADE   | L (mm) | AREA (m <sup>2</sup> ) | WEIGHT (kg) |
|----------|--------------|-----|---------|--------|------------------------|-------------|
| p56      | RHS150X100X6 | 1   | S355J2H | 1545   | 0.7                    | 33.2 !!     |

TOTAL WEIGHT FOR 1 PARTS 33.2

| Part list | Qty. |
|-----------|------|
| OP        | 1    |

#### Execution class: EXC 2

No utilization on drawings = over 50%

V-SEAM  
Utilization under 50%  
EXC 2=> Acc. to process control  
EXC 3=> 20% UT  
Utilization over 50%  
EXC 2=> 10% UT  
EXC 3=> 20% UT

\* o 3 0 4 8 0 - 2 \*



DS Skalkonstruktion

\* W p 5 6 \*

|          |                                      |                    |              |                  |                    |
|----------|--------------------------------------|--------------------|--------------|------------------|--------------------|
| PROJECT  | Akkasæter Lager- og vedlikeholdshall |                    | PHASE        | 2 / Phase 2      |                    |
| MEMBER   | Portomfatning                        |                    | QUANTITY:    | 1                | PROJECT No 30480-2 |
| REVISION |                                      | ISSUED: 07.11.2025 | DRAFTER: ZLL | BIM control: SST | DRAWING No. p.56   |