


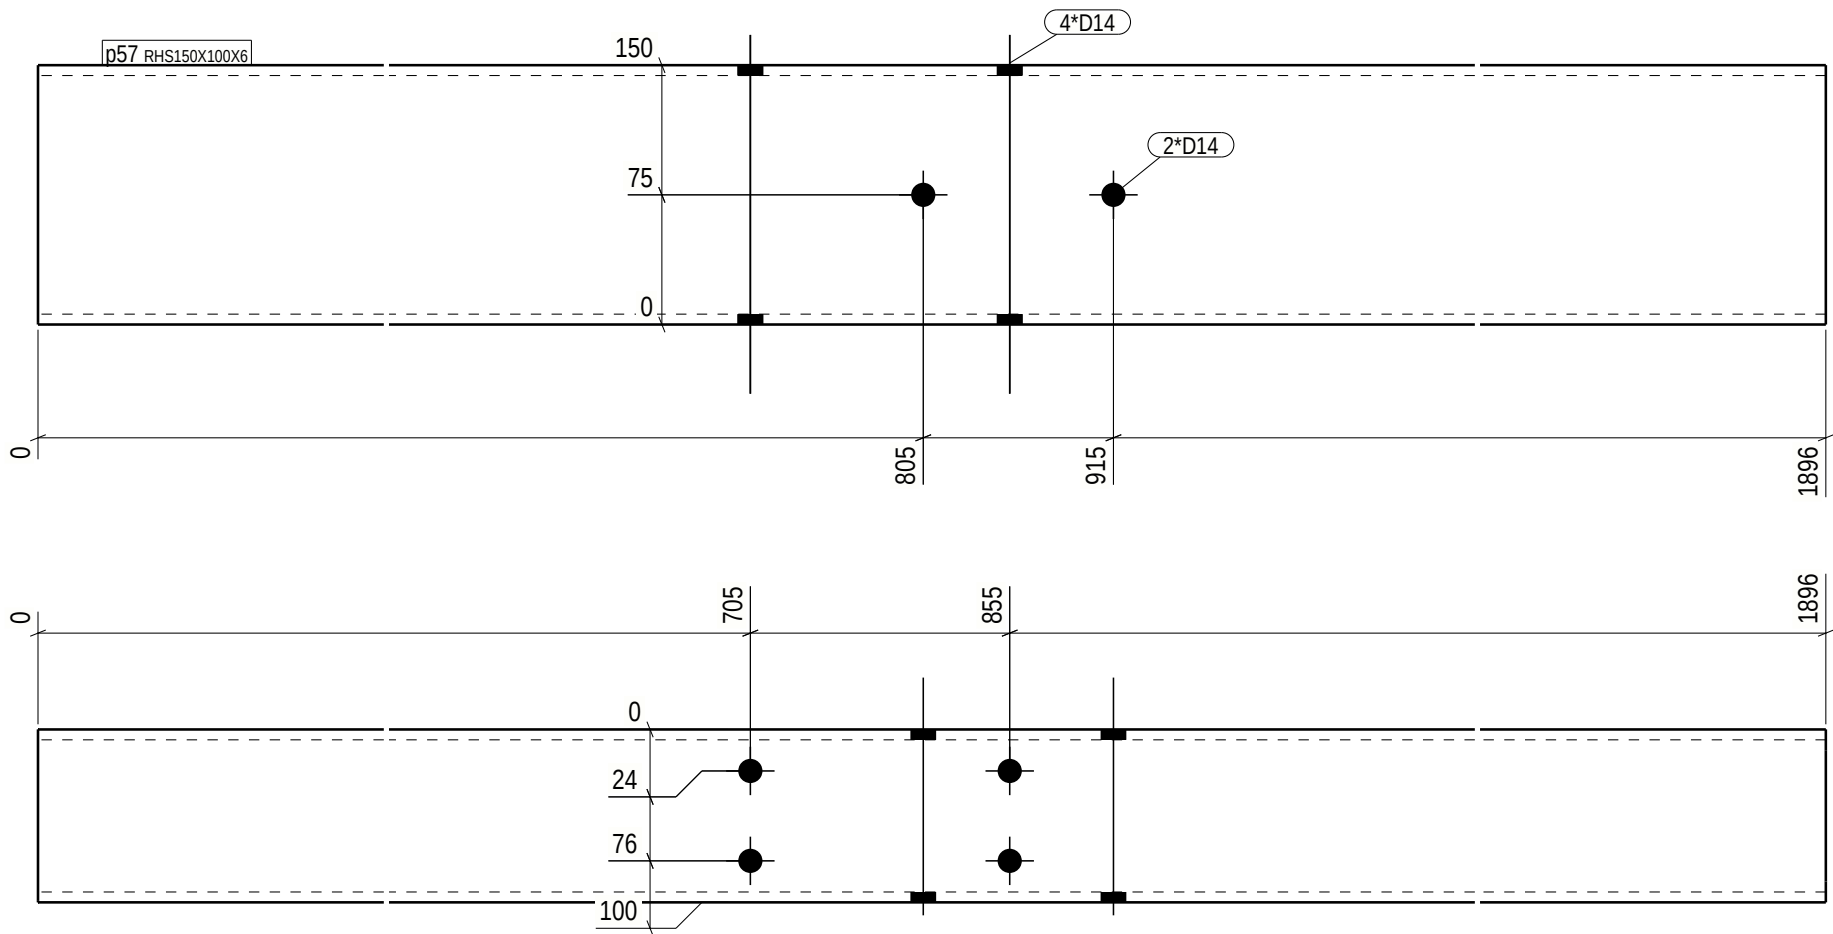

GENERAL NOTES:

For your safety, check weight before handling:
0-5kg Light 5-15kg Normal 15+kg Heavy

MATERIAL LIST FOR PART - p57

1 PARTS REQUIRED

POS. No.	PROFILE	No.	GRADE	L (mm)	AREA (m ²)	WEIGHT (kg)
p57	RHS150X100X6	1	S355J2H	1896	0.9	41.0 !!
TOTAL WEIGHT FOR				1 PARTS	41.0	

Execution class: EXC 2

No utilization on drawings = over 50%

V-SEAM
Utilization under 50%
EXC 2=> Acc. to process control
EXC 3=> 20% UT
Utilization over 50%
EXC 2=> 10% UT
EXC 3=> 20% UT

Part list	Qty.
OP	1

* o 3 0 4 8 0 - 2 *  **DS** *Skalkonstruktion* * W p 5 7 *

PROJECT	Akkasæter Lager- og vedlikeholdshall	PHASE	2 / Phase 2
MEMBER	Portomfatning	QUANTITY:	1
REVISION	ISSUED: 07.11.2025	DRAFTER:	ZLL
		BIM control:	SST
		PROJECT No	30480-2
		DRAWING No.	p.57