


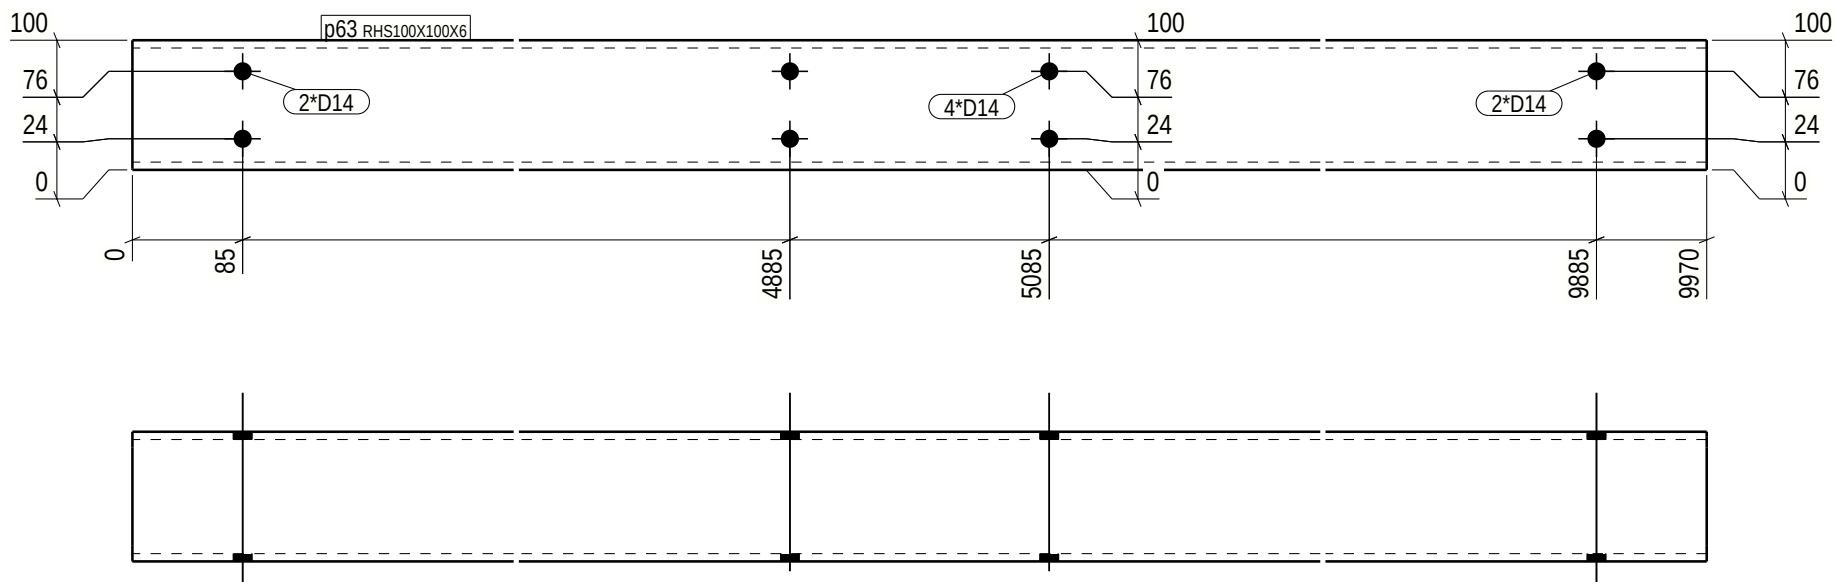

GENERAL NOTES: For your safety, check weight before handling: 0-5kg Light 5-15kg Normal 15+kg Heavy						
MATERIAL LIST FOR PART - p63				1 PARTS REQUIRED		
POS. No.	PROFILE	No.	GRADE	L (mm)	AREA (m ²)	WEIGHT (kg)
p63	RHS100X100X6	1	S355J2H	9970	3.8	168.6 !!
TOTAL WEIGHT FOR				1	PARTS	168.6

Part list	Qty.
OP	1

Execution class: EXC 2		* o 3 0 4 8 0 - 2 *  DS <i>Skalkonstruktion</i> * W p 6 3 *			
No utilization on drawings = over 50%					
V-SEAM Utilization under 50% EXC 2=> Acc. to process control EXC 3=> 20% UT Utilization over 50% EXC 2=> 10% UT EXC 3=> 20% UT		PROJECT	Akkasæter Lager- og vedlikeholdshall	PHASE	2 / Phase 2
		MEMBER	Portomfatning	QUANTITY:	1
		REVISION		DRAFTER:	ZLL
			ISSUED: 07.11.2025	BIM control:	SST
				PROJECT No	30480-2
				DRAWING No.	p.63