


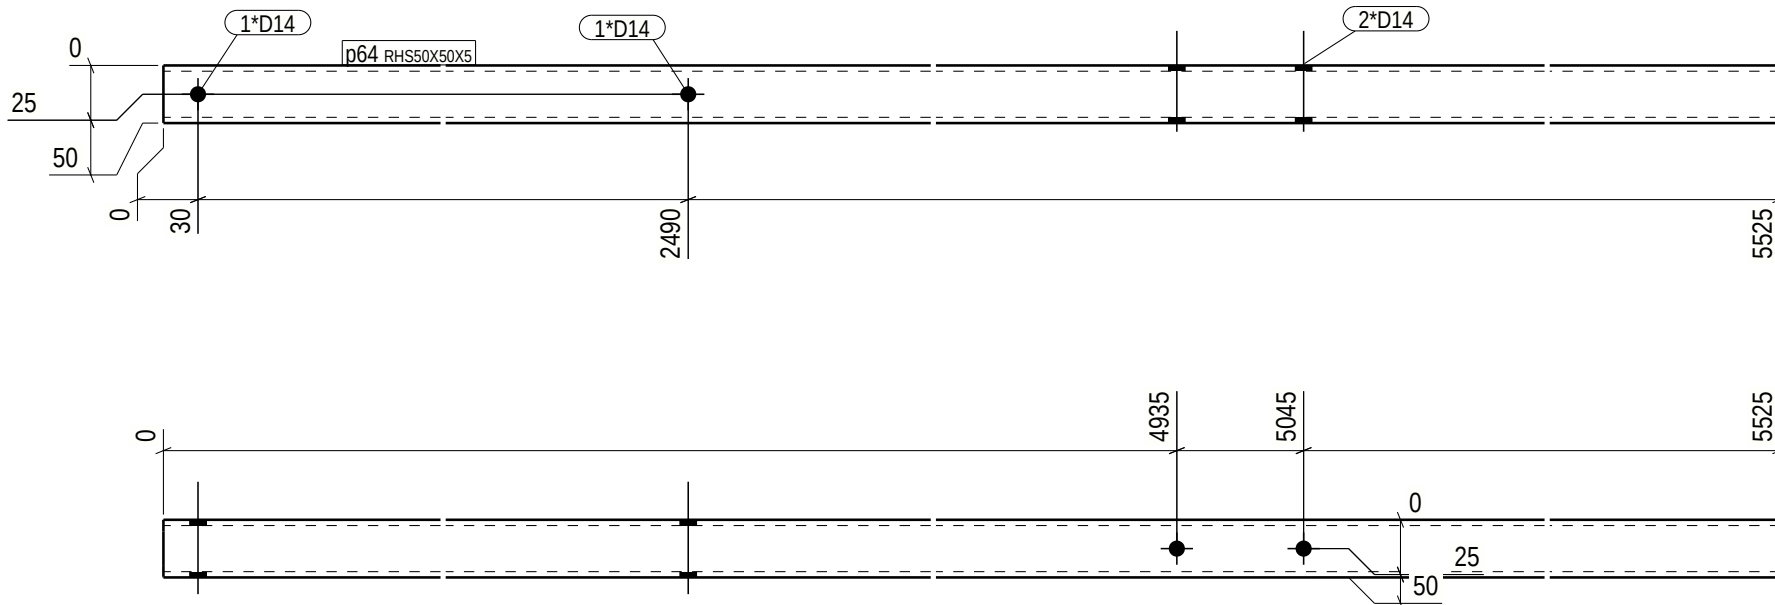

GENERAL NOTES: For your safety, check weight before handling: 0-5kg Light 5-15kg Normal 15+kg Heavy						
MATERIAL LIST FOR PART - p64				4 PARTS REQUIRED		
POS. No.	PROFILE	No.	GRADE	L (mm)	AREA (m ²)	WEIGHT (kg)
p64	RHS50X50X5	1	S355J2H	5525	1.0	36.0 !!
TOTAL WEIGHT FOR				4	PARTS	143.9

Part list	Qty.
OP	4

Execution class: EXC 2		* o 3 0 4 8 0 - 2 *  DS <i>Skalkonstruktion</i> * W p 6 4 *			
No utilization on drawings = over 50%		PROJECT	Akkasæter Lager- og vedlikeholdshall		PHASE 2 / Phase 2
V-SEAM Utilization under 50% EXC 2=> Acc. to process control EXC 3=> 20% UT		MEMBER	Portomfatning		QUANTITY: 4
Utilization over 50% EXC 2=> 10% UT EXC 3=> 20% UT		REVISION	ISSUED: 07.11.2025		PROJECT No 30480-2
			DRAFTER: ZLL BIM control: SST		DRAWING No. p.64