


Tekla Structures

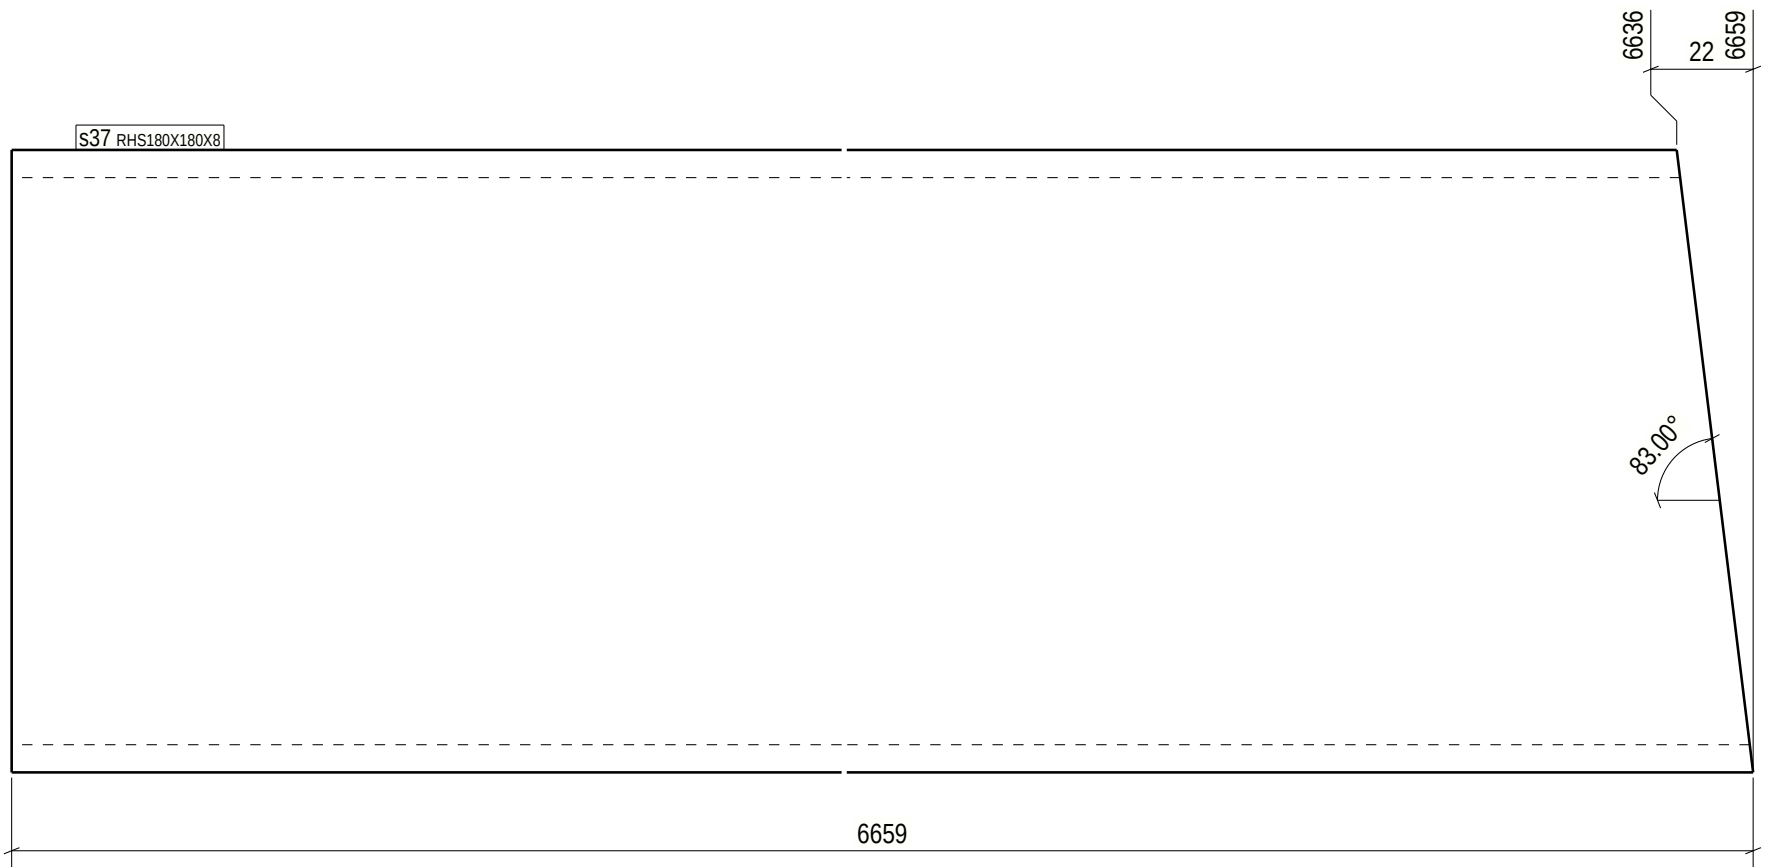

|                                                |              |     |         |                  |                        |             |
|------------------------------------------------|--------------|-----|---------|------------------|------------------------|-------------|
| GENERAL NOTES:                                 |              |     |         |                  |                        |             |
| For your safety, check weight before handling: |              |     |         |                  |                        |             |
| 0-5kg Light    5-15kg Normal    15+kg Heavy    |              |     |         |                  |                        |             |
| MATERIAL LIST FOR PART - S37                   |              |     |         | 1 PARTS REQUIRED |                        |             |
| POS. No.                                       | PROFILE      | No. | GRADE   | L (mm)           | AREA (m <sup>2</sup> ) | WEIGHT (kg) |
| s37                                            | RHS180X180X8 | 1   | S355J2H | 6659             | 4.6                    | 277.8 !!    |
| TOTAL WEIGHT FOR                               |              |     |         | 1                | PARTS                  | 277.8       |

|           |      |
|-----------|------|
| Part list | Qty. |
| GS        | 1    |

|   |  |   |                                      |              |             |
|---|--|---|--------------------------------------|--------------|-------------|
| Execution class: EXC 2   |  | * o 3 0 4 8 0 - 2 *  <b>DS</b> <i>Skalkonstruktion</i> * W s 3 7 * |                                      |              |             |
| No utilization on drawings = over 50%   |  |   |                                      |              |             |
| V-SEAM<br>Utilization under 50%<br>EXC 2=> Acc. to process control<br>EXC 3=> 20% UT<br>Utilization over 50%<br>EXC 2=> 10% UT<br>EXC 3=> 20% UT |  | PROJECT   | Akkasæter Lager- og vedlikeholdshall | PHASE        | 2 / Phase 2 |
|   |  | MEMBER   | Søyle                                | QUANTITY:    | 1           |
|   |  | REVISION   |                                      | ISSUED:      | 07.11.2025  |
|   |  |   |                                      | DRAFTER:     | ZLL         |
|   |  |   |                                      | BIM control: | SST         |
|   |  |   |                                      | PROJECT No   | 30480-2     |
|   |  |   |                                      | DRAWING No.  | S.37        |