


Tekla Structures

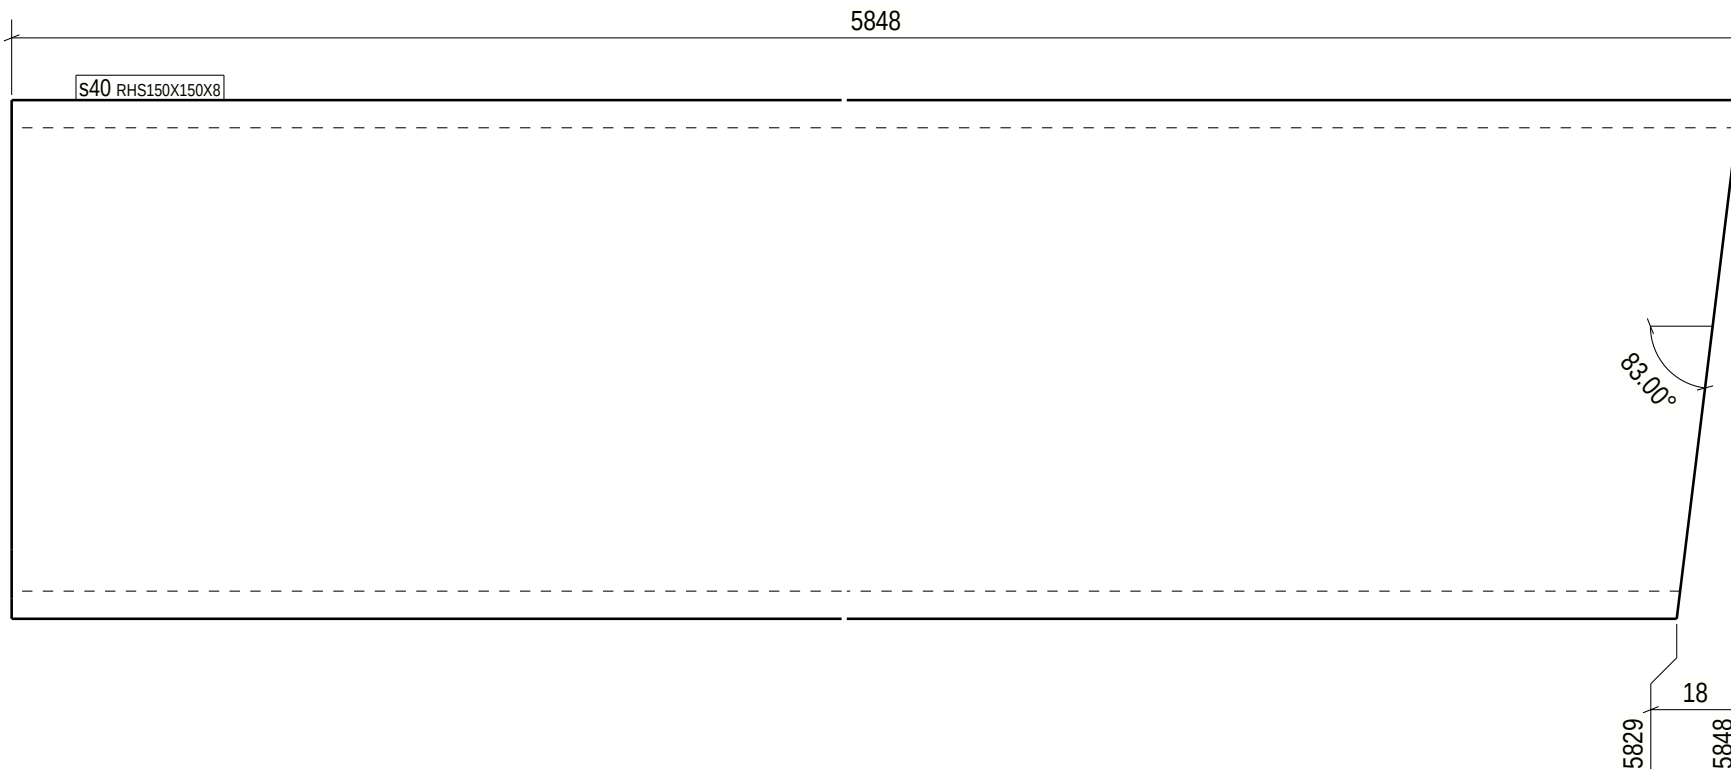

GENERAL NOTES:						
For your safety, check weight before handling:						
0-5kg Light 5-15kg Normal 15+kg Heavy						
MATERIAL LIST FOR PART - S40				1 PARTS REQUIRED		
POS. No.	PROFILE	No.	GRADE	L (mm)	AREA (m ²)	WEIGHT (kg)
s40	RHS150X150X8	1	S355J2H	5848	3.3	197.3 !!
TOTAL WEIGHT FOR				1	PARTS	197.3

Part list	Qty.
GS	1

Execution class: EXC 2		* o 3 0 4 8 0 - 2 *  DS <i>Skalkonstruktion</i> * W s 4 0 *			
No utilization on drawings = over 50%					
V-SEAM Utilization under 50% EXC 2=> Acc. to process control EXC 3=> 20% UT Utilization over 50% EXC 2=> 10% UT EXC 3=> 20% UT		PROJECT	Akkasæter Lager- og vedlikeholdshall		PHASE 2 / Phase 2
		MEMBER	Søyle		QUANTITY: 1 PROJECT No 30480-2
		REVISION		ISSUED: 07.11.2025	DRAFTER: ZLL BIM control: SST DRAWING No. s.40