

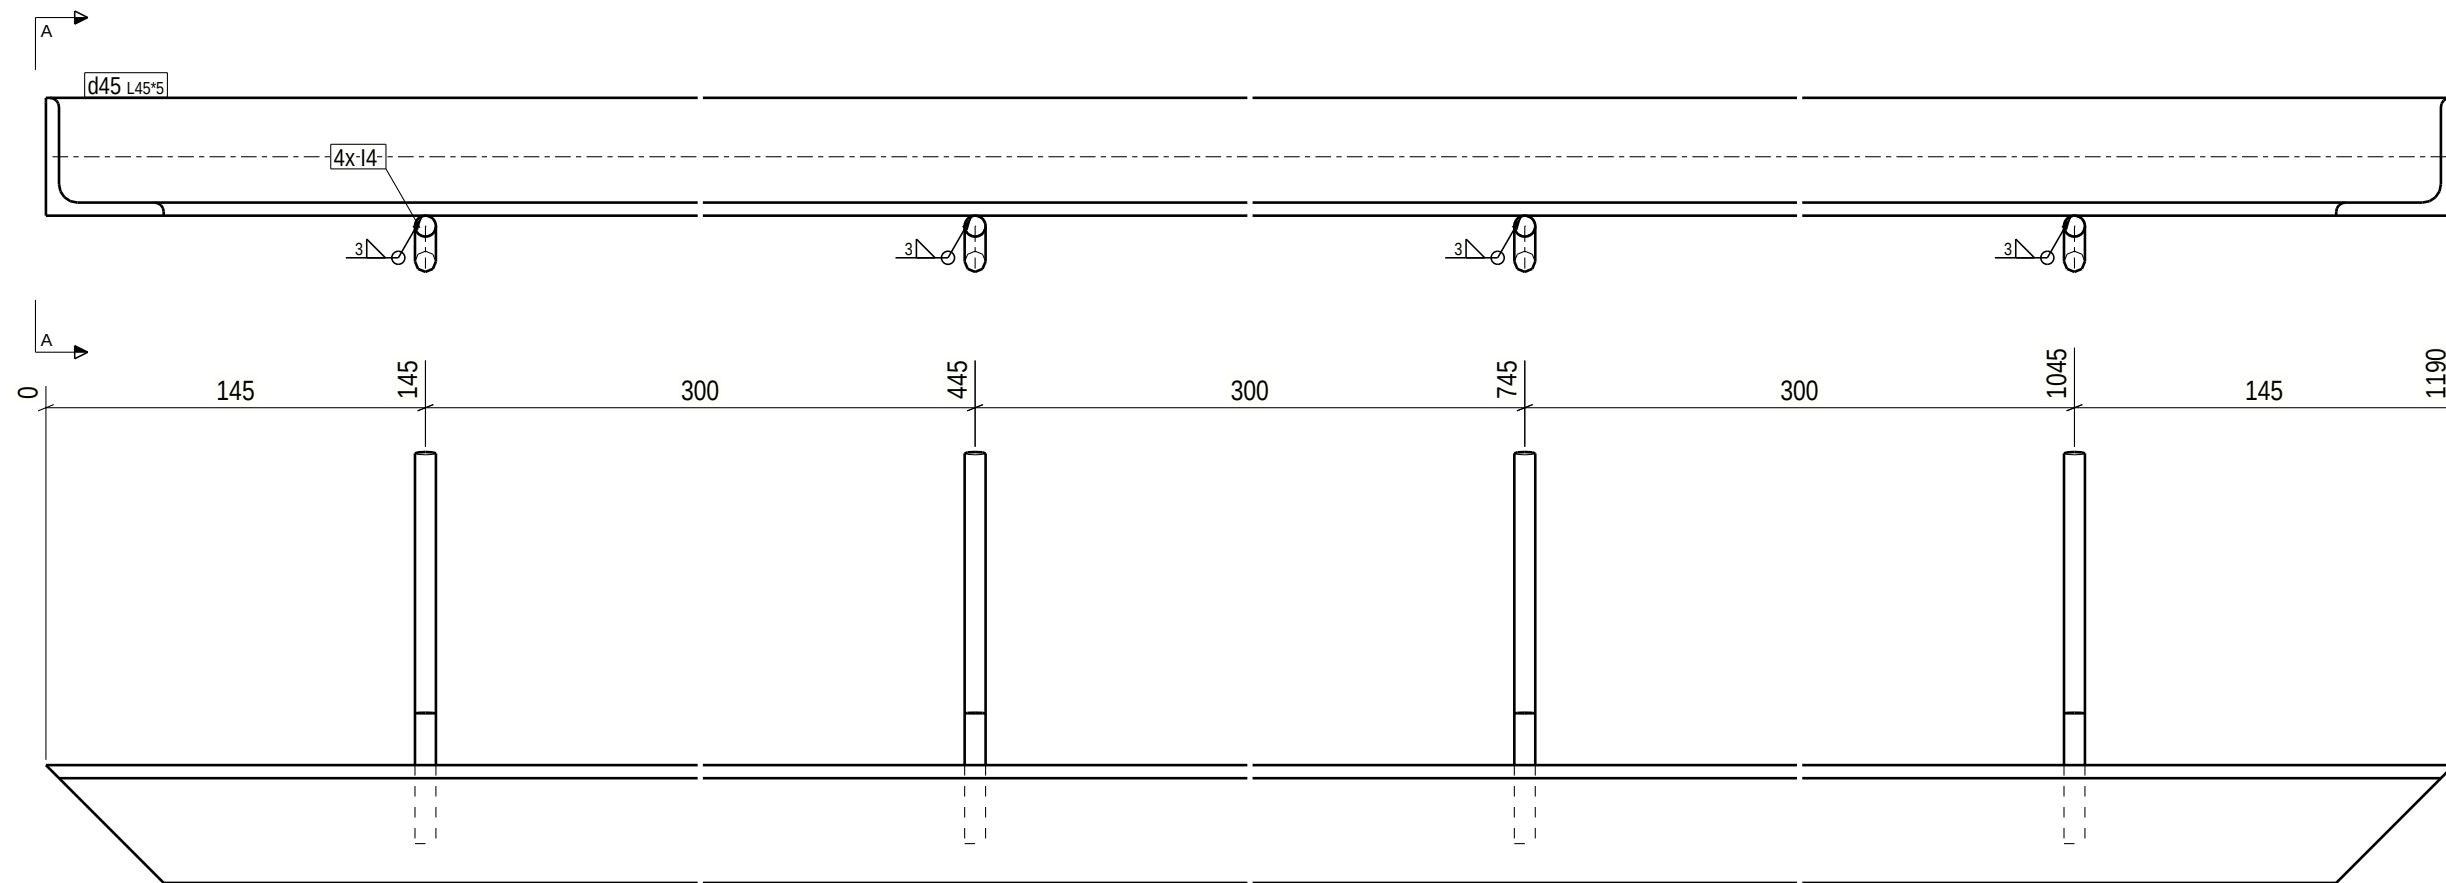


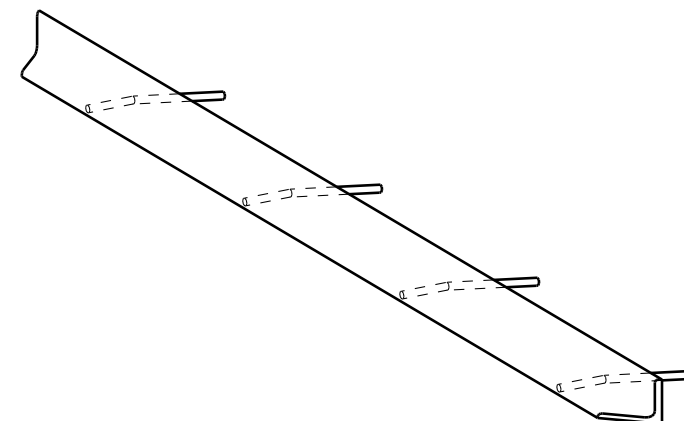

A - A
1:1

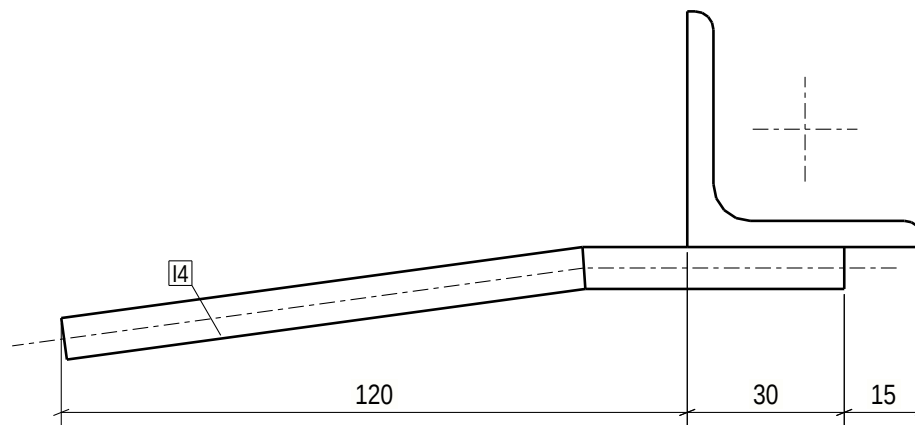

GENERAL NOTES: For your safety, check weight before handling:
0-5kg Light 5-15kg Normal 15+kg Heavy

ALL WELDS ARE 4 UNLESS NOTED ON DRAWING

MATERIAL LIST FOR ASSEMBLY MK'D d.45						4 No. Required
Mark	Profile	Material	No.	Length	Area	Weight
d45	L45*5	S355J2	1	1190	0.2	3.9
I4	REBAR8	B550B	4	150	0.0	0.1
Total					0.2	4.2

Finish Class
Standard

Surface treatment info:	Thickness/start point-> length	No.
Galvanised	/	4



Special
surface treatment



weld a = 4

PHASE	QUANTITY
4	4

* o 3 0 4 8 0 - 4 *  DS <i>Stalkonstruktion</i> * A d 4 5 *			
PROJECT	Akkasæter Lager- og vedlikeholdshall	EXEC. CLASS	EXC 2
MEMBER	Drager	QUANTITY:	4
REVISION	ISSUED: 19.11.2025	DRAFTER: ZLL	PROJECT No 30480-4
	BIM control: SST		DRAWING No. d.45