


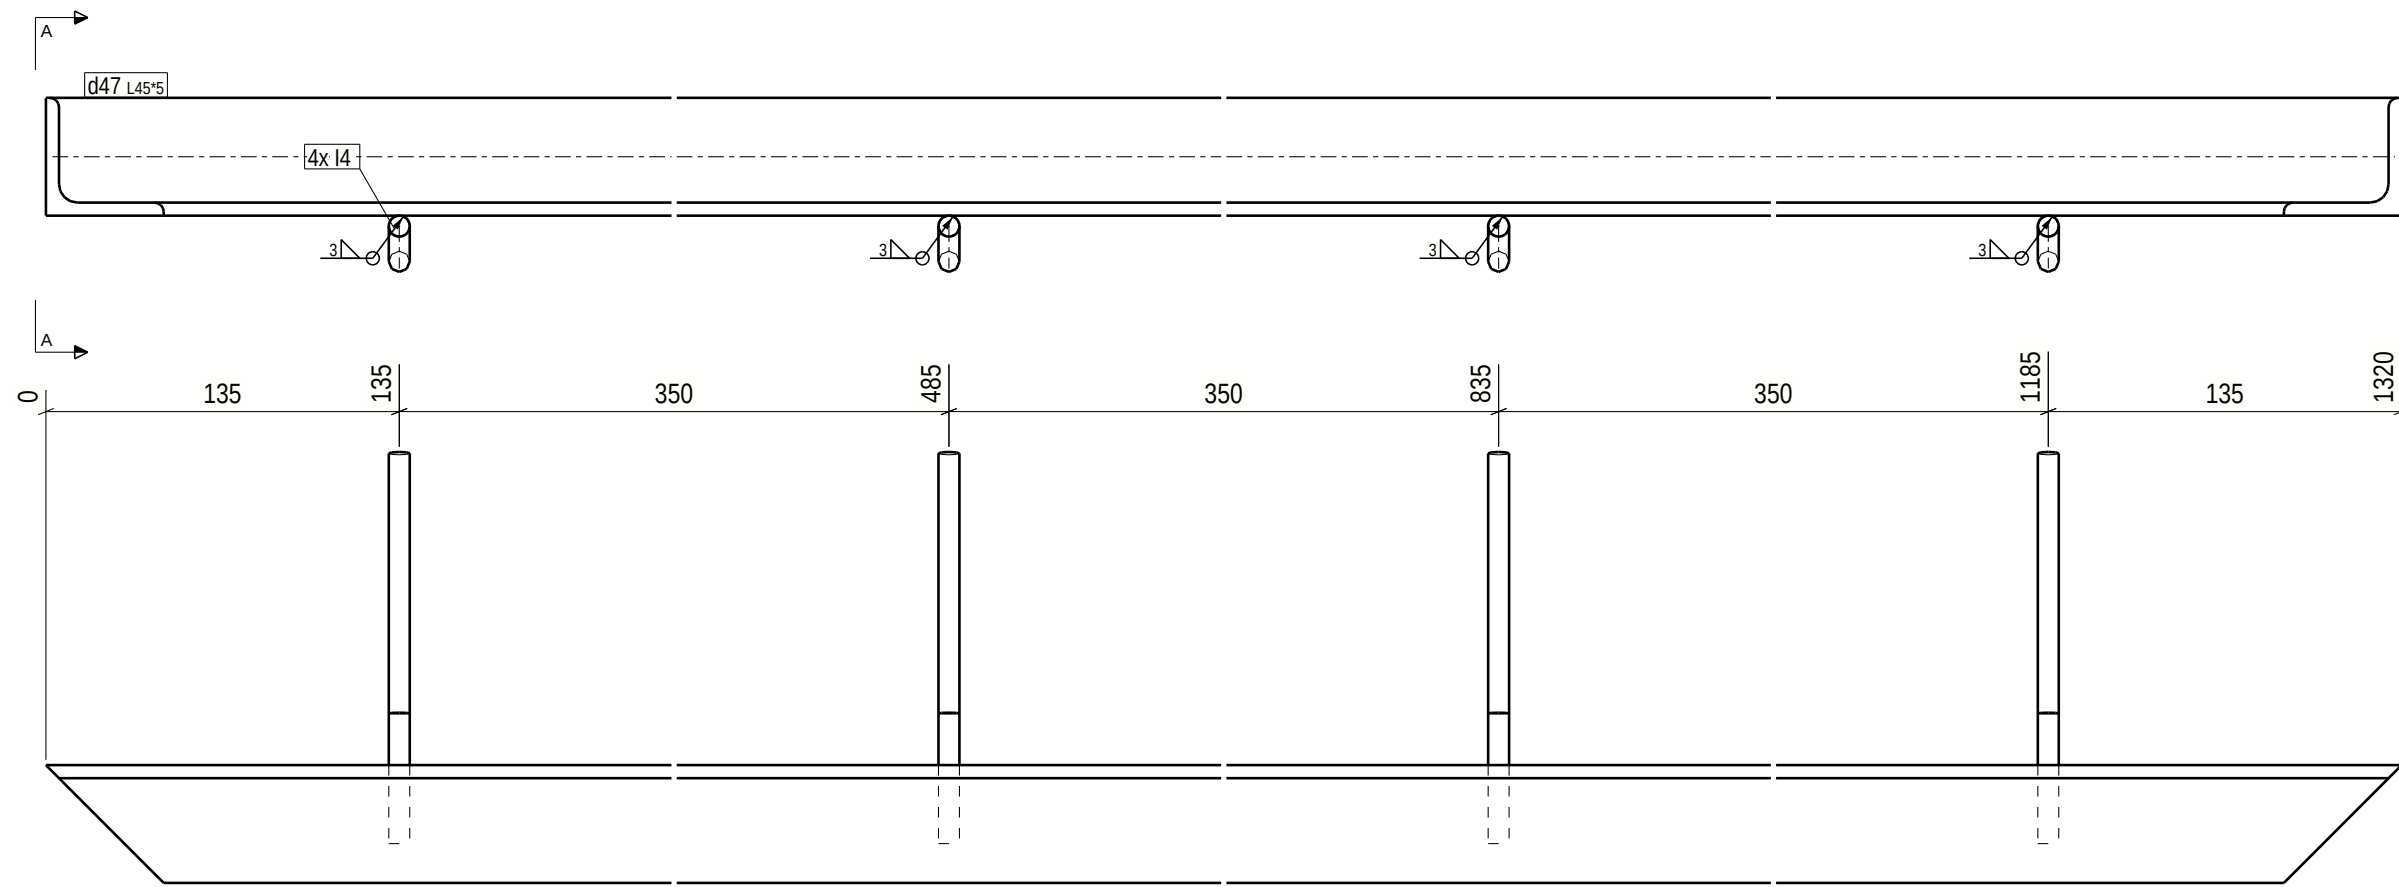

A - A
1:1

GENERAL NOTES:						
For your safety, check weight before handling:						
0-5kg Light 5-15kg Normal 15+kg Heavy						
ALL WELDS ARE 4 UNLESS NOTED ON DRAWING						
MATERIAL LIST FOR ASSEMBLY MK'D d.47						
Mark	Profile	Material	No.	Length	Area	Weight
d47	L45*5	S355J2	1	1320	0.2	4.4
I4	REBAR8	B550B	4	150	0.0	0.1
Total					0.2	4.6

Finish Class
Standard

Surface treatment info:	Thickness/start point-> length	No.
Galvanised	/	4

Special surface treatment

weld a = 4

PHASE	QUANTITY
4	4

* o 3 0 4 8 0 - 4 *							DS		Stalkonstruktion		* A d 4 7 *	
PROJECT		Akkasæter Lager- og vedlikeholdshall					EXEC. CLASS		EXC 2			
MEMBER		Drager			QUANTITY:		4		PROJECT No		30480-4	
REVISION		ISSUED: 19.11.2025			DRAFTER:		ZLL		DRAWING No.		d.47	
					BIM control:		SST					

Tekla Structures