

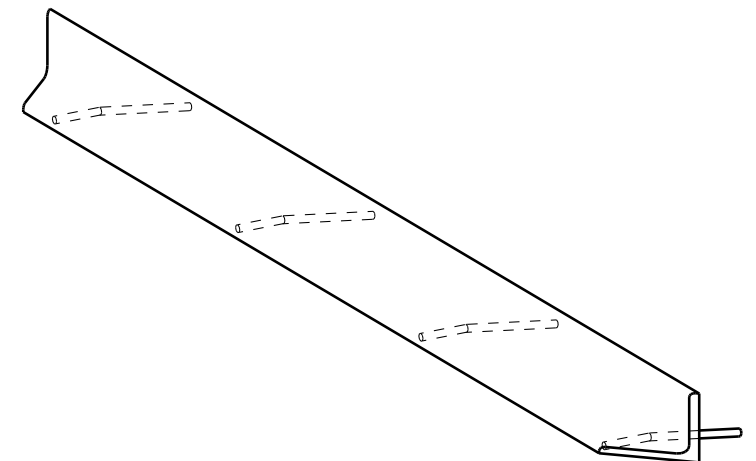


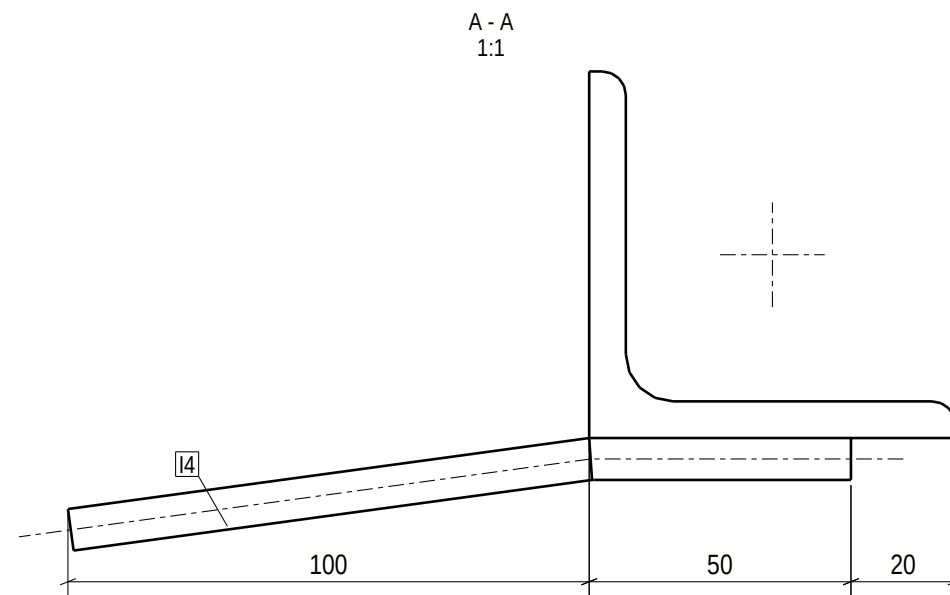

GENERAL NOTES:						
For your safety, check weight before handling:						
0-5kg Light 5-15kg Normal 15+kg Heavy						
ALL WELDS ARE 4 UNLESS NOTED ON DRAWING						
MATERIAL LIST FOR ASSEMBLY MK'D d.50						
Mark	Profile	Material	No.	Length	Area	Weight
d50	L70*7	S355J2	1	1240	0.3	8.9
I4	REBAR8	B550B	4	150	0.0	0.1
Total				0.4	9.1	

Finish Class
Standard

Surface treatment info:	Thickness/start point--> length	No.
Galvanised	/	4

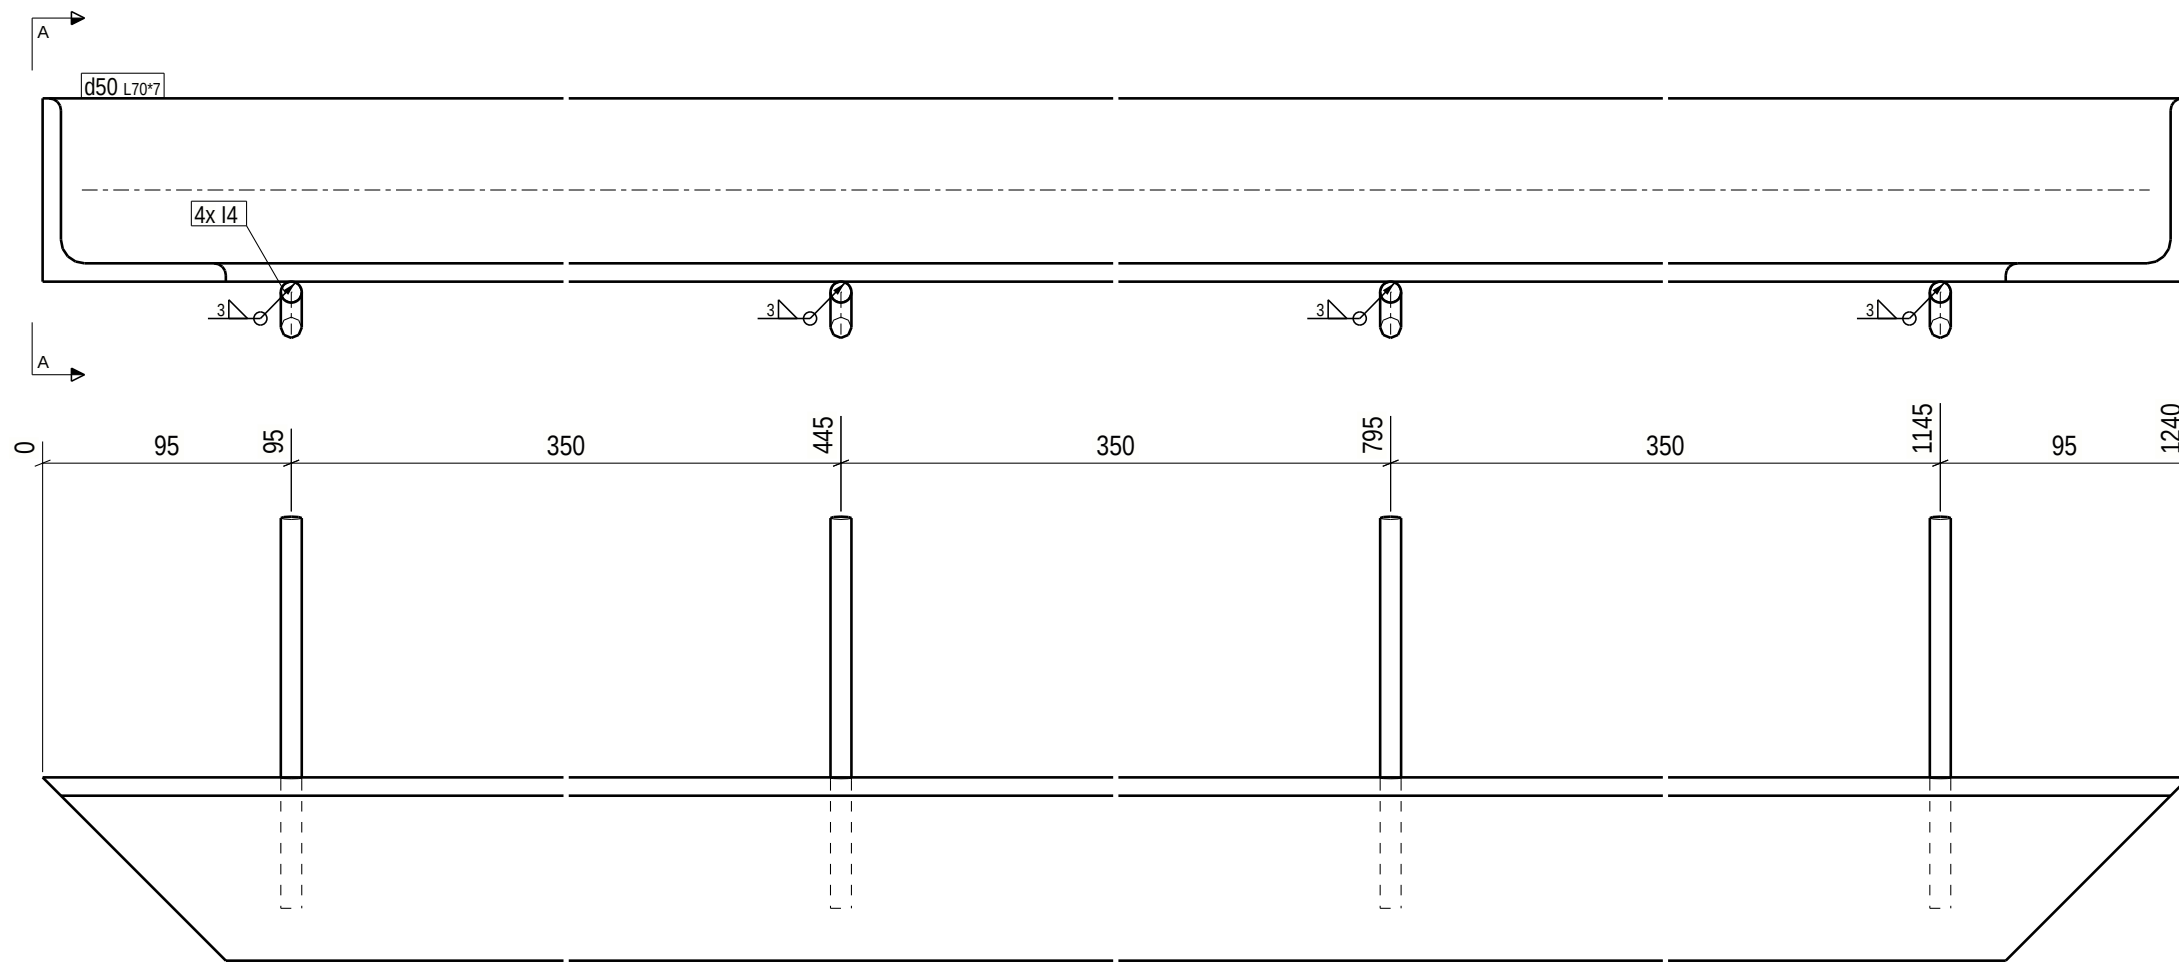

Special
surface treatment



weld a = 4

PHASE	QUANTITY
4	4

* o 3 0 4 8 0 - 4 *								DS		Stalkonstruktion		* A d 5 0 *	
PROJECT		Akkasæter Lager- og vedlikeholdshall						EXEC. CLASS		EXC 2			
MEMBER		Drager				QUANTITY:		4		PROJECT No		30480-4	
REVISION		ISSUED: 19.11.2025				DRAFTER: ZLL		BIM control: SST		DRAWING No.		d.50	