


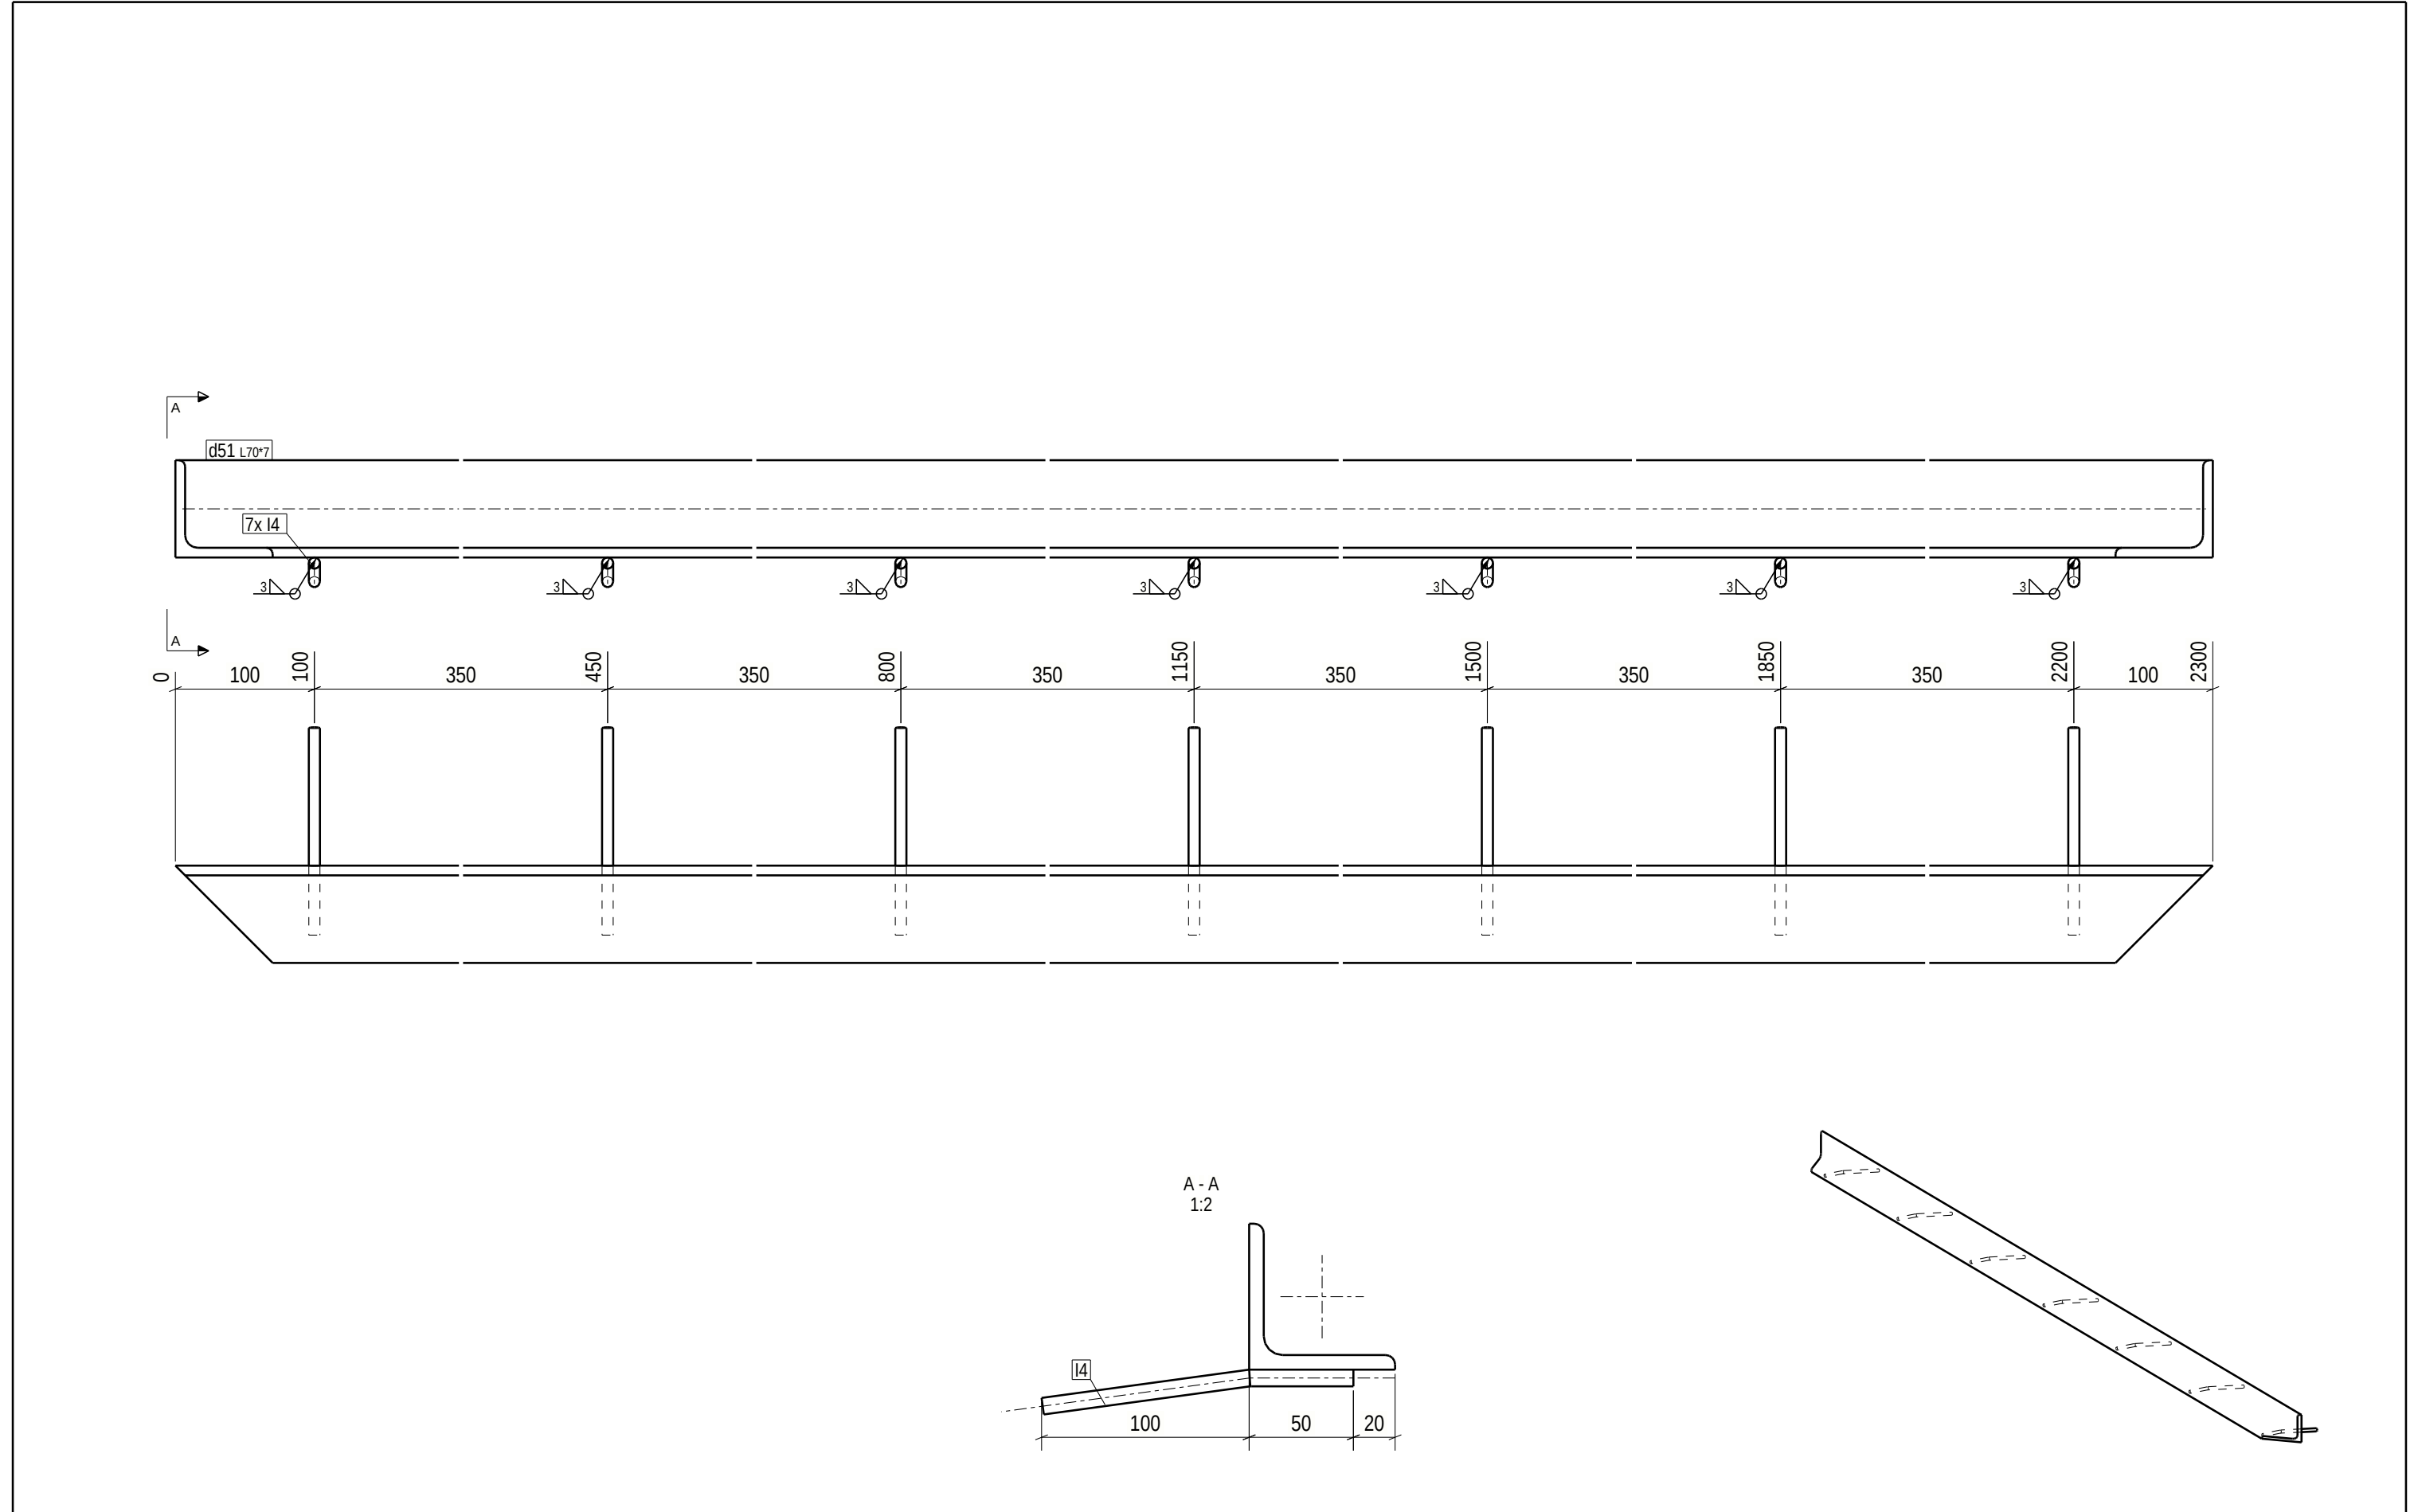

GENERAL NOTES:

For your safety, check weight before handling:
0-5kg Light 5-15kg Normal 15+kg Heavy

ALL WELDS ARE 4

UNLESS NOTED ON DRAWING

MATERIAL LIST FOR ASSEMBLY MK'D

d.51

4

No. Required

Mark	Profile	Material	No.	Length	Area	Weight
d51	L70*7	S355J2	1	2300	0.6	16.7 !!
I4	REBAR8	B550B	7	150	0.0	0.1
Total					0.7	17.1

Finish Class

Standard

Surface treatment info:

Thickness/start point-> length

No.

Galvanised

/

4



Special surface treatment



weld a = 4

PHASE	QUANTITY
4	4

* o 3 0 4 8 0 - 4 *

 **DS** Skalkonstruktion

* A d 5 1 *

PROJECT	Akkasæter Lager- og vedlikeholdshall		EXEC. CLASS		EXC 2		
MEMBER	Drager		QUANTITY:	4	PROJECT No	30480-4	
REVISION	ISSUED: 19.11.2025		DRAFTER:	ZLL	DRAWING No.		d.51
		BIM control:		SST			