


E51WF-1032 end updated
E51WF-1034 length updated

APPROVED FOR CONSTRUCTION 12.06.2026

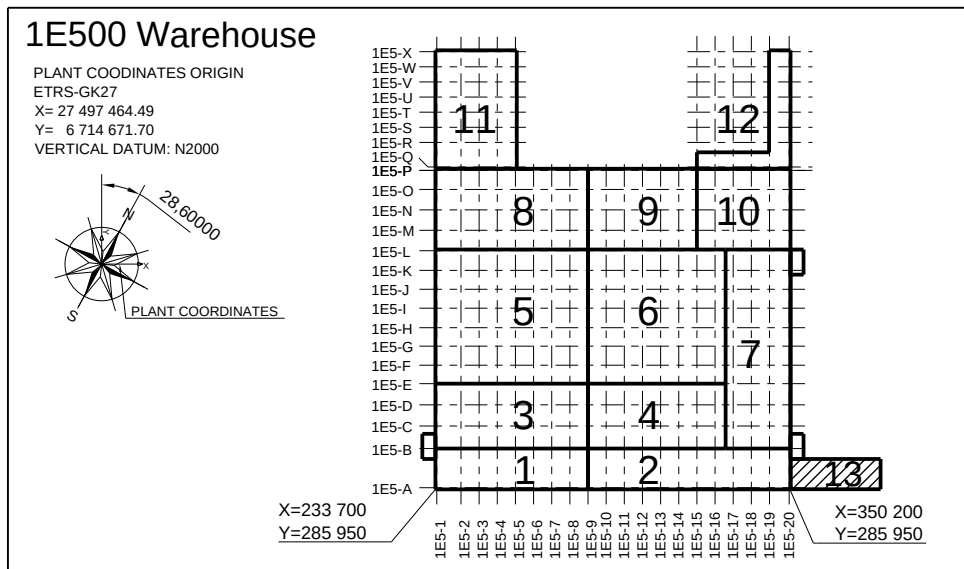

01	Panel supports shortened				FIALES	29.06.2026	FIKJER
REV.		REVISION			CHANGED BY	DATE	CHECKED BY
Date	Designed	Checked	Approved	Status			
05.06.2026	FIALES	FIKJER	FIKOPE	AFC			
Document ID		Area	Relates			Scale	Size
25019443-ICC250-0600-0660-001335		1E500					A4
Project ID		Sub area	Position ID			Discipline	
25019443						CIVIL	
		Title Easpring New Materials Oy FAIR phase 1 Warehouse, Steel Structures, Access bridge between 1A100-1E500, Frame Supports, Assembly Drawings					
Drawing number						Revision	Page/Pages
25019443-ICC250-0600-0660-001335						01	1/1

ASSEMBLY PART LIST

Project Number		25019443						Content	Access bridge between 1A100-1E500, Frame Supports						
Project Name		Easpring New Materials Oy						Document	25019443-ICC250-0600-0660-001335						
Project Address		FAIR Phase 1						Status	AFC				Revisio	01	
Author	FIALES	Inspector	FIKJER	Approver	FIPEKO			Rev. Comment:		Panel supports shortened				Date	29.06.2026
Phase	Position	Main part name	Main part profile	Exec. Class	Shade (assembly) / Material (part)	Pcs.	Length [mm]	Width [mm]	Height [mm]	Paino [kg]	Weight sum [kg]	Area [m²]	Date	Rev.	Rev. Date
9000	E51WF-1007	FRAME		EXC2	RAL 7024 (Graphite Gray)	1	2235	220	140	27.8	27.8	0.92	12.06.2026		
9000	E51WFL-1017		PL5X220		S355J2+N	1	140	220	5	1.2	1.2		12.06.2026		
9000	E51WFL-1020		PL10X100		S355J2+N	1	150	100	10	1.2	1.2		12.06.2026		
9000	E51WFL-1021		PL15X100		S355J2+N	1	100	100	15	1.2	1.2		12.06.2026		
9000	E51WFP-1003		CFRHS100X100X4		S355J2H	1	2065	0	0	24.2	24.2		12.06.2026		
9000	E51WF-1008	FRAME		EXC2	RAL 7024 (Graphite Gray)	1	4010	145	250	59.6	59.6	1.95	12.06.2026		
9000	E51WFL-1014		PL10X120		S355J2+N	1	165	120	10	1.6	1.6		12.06.2026		
9000	E51WFL-1015		PL15X130		S355J2+N	1	140	130	15	2.1	2.1		12.06.2026		
9000	E51WFL-1016		PL5X145		S355J2+N	1	250	145	5	1.4	1.4		12.06.2026		
9000	E51WFP-1001		CFRHS120X120X4		S355J2H	1	3825	0	0	54.5	54.5		12.06.2026		
9000	E51WF-1009	FRAME		EXC2	RAL 7024 (Graphite Gray)	2	4010	141	250	59.6	119.1	1.95	12.06.2026		
9000	E51WFL-1014		PL10X120		S355J2+N	2	165	120	10	1.6	3.1		12.06.2026		
9000	E51WFL-1015		PL15X130		S355J2+N	2	140	130	15	2.1	4.3		12.06.2026		
9000	E51WFL-1026		PL5X140		S355J2+N	2	250	140	5	1.4	2.7		12.06.2026		
9000	E51WFP-1001		CFRHS120X120X4		S355J2H	2	3825	0	0	54.5	109.0		12.06.2026		
9000	E51WF-1010	FRAME		EXC2	RAL 7024 (Graphite Gray)	3	4010	141	250	59.6	178.7	1.95	12.06.2026		
9000	E51WFL-1014		PL10X120		S355J2+N	3	165	120	10	1.6	4.7		12.06.2026		
9000	E51WFL-1015		PL15X130		S355J2+N	3	140	130	15	2.1	6.4		12.06.2026		
9000	E51WFL-1027		PL5X140		S355J2+N	3	250	140	5	1.4	4.1		12.06.2026		
9000	E51WFP-1001		CFRHS120X120X4		S355J2H	3	3825	0	0	54.5	163.5		12.06.2026		
9000	E51WF-1011	FRAME		EXC2	RAL 7024 (Graphite Gray)	1	4010	210	200	60.2	60.2	1.97	12.06.2026		
9000	E51WFL-1014		PL10X120		S355J2+N	1	165	120	10	1.6	1.6		12.06.2026		
9000	E51WFL-1015		PL15X130		S355J2+N	1	140	130	15	2.1	2.1		12.06.2026		
9000	E51WFL-1022		PL10X55		S355J2+N	1	120	55	10	0.5	0.5		12.06.2026		
9000	E51WFL-1028		PL5X190		S355J2+N	1	200	190	5	1.5	1.5		12.06.2026		
9000	E51WFP-1001		CFRHS120X120X4		S355J2H	1	3825	0	0	54.5	54.5		12.06.2026		
9000	E51WF-1012	FRAME		EXC2	RAL 7024 (Graphite Gray)	1	3751	412	110	48.1	51.2	1.61	12.06.2026		
9000	E51WFL-1019		PL10X100		S355J2+N	2	150	100	10	1.2	2.4		12.06.2026		
9000	E51WFL-1023		PL10X55		S355J2+N	2	100	55	10	0.4	0.9		12.06.2026		
9000	E51WFL-1024		PL15X110		S355J2+N	2	120	110	15	1.6	3.1		12.06.2026		
9000	E51WFL-1056		PL16X162		S355J2	1	150	162	16	2.6	2.6		12.06.2026		

9000	E51WFP-1004		CFRHS100X100X4		S355J2H	1	3611	0	0	42.4	42.4		12.06.2026		
9000	E51WF-1013	FRAME		EXC2	RAL 7024 (Graphite Gray)	1	3635	190	220	54.5	54.5	1.79	12.06.2026		
9000	E51WFL-1014		PL10X120		S355J2+N	1	165	120	10	1.6	1.6		12.06.2026		
9000	E51WFL-1015		PL15X130		S355J2+N	1	140	130	15	2.1	2.1		12.06.2026		
9000	E51WFL-1025		PL5X190		S355J2+N	1	220	190	5	1.6	1.6		12.06.2026		
9000	E51WFP-1002		CFRHS120X120X4		S355J2H	1	3450	0	0	49.1	49.1		12.06.2026		
9000	E51WF-1014	FRAME		EXC2	RAL 7024 (Graphite Gray)	1	3635	210	220	55.0	55.0	1.80	12.06.2026		
9000	E51WFL-1014		PL10X120		S355J2+N	1	165	120	10	1.6	1.6		12.06.2026		
9000	E51WFL-1015		PL15X130		S355J2+N	1	140	130	15	2.1	2.1		12.06.2026		
9000	E51WFL-1022		PL10X55		S355J2+N	1	120	55	10	0.5	0.5		12.06.2026		
9000	E51WFL-1025		PL5X190		S355J2+N	1	220	190	5	1.6	1.6		12.06.2026		
9000	E51WFP-1002		CFRHS120X120X4		S355J2H	1	3450	0	0	49.1	49.1		12.06.2026		
9000	E51WF-1030	FRAME		EXC2	RAL 7024 (Graphite Gray)	1	4325	90	260	165.1	165.1	3.64	12.06.2026		
9000	E51WFL-1029		PL10X76		S355J2+N	1	246	76	10	1.5	1.5		12.06.2026		
9000	E51WFP-1033		UNP260		S355J2	1	4315	0	0	163.6	163.6		12.06.2026		
9000	E51WF-1031	FRAME		EXC2	RAL 7024 (Graphite Gray)	1	4670	90	260	177.1	177.1	3.89	12.06.2026		
9000	E51WFP-1024		UNP260		S355J2	1	4670	0	0	177.1	177.1		12.06.2026		
9000	E51WF-1032	FRAME		EXC2	RAL 7024 (Graphite Gray)	1	9730	162	487	305.0	312.1	8.09	12.06.2026	01	29.06.2026
9000	E51WFL-1030		PL12X190		S355J2+N	2	400	190	12	7.2	14.3		12.06.2026		
9000	E51WFL-1032		PL5X140		S355J2+N	1	240	140	5	1.3	1.3		12.06.2026	01	29.06.2026
9000	E51WFL-1056		PL16X162		S355J2	1	150	162	16	2.6	2.6		12.06.2026		
9000	E51WFL-1058		PL10X150		S355J2+N	1	130	150	10	1.5	1.5		29.06.2026		
9000	E51WFP-1023		CFRHS250X150X5		S355J2H	1	9605	0	0	289.2	289.2		12.06.2026	01	29.06.2026
9000	E51WFP-1048		L120*12		S355J2	1	150	0	0	3.2	3.2		29.06.2026		
9000	E51WF-1033	FRAME		EXC2	RAL 7024 (Graphite Gray)	2	9620	162	487	300.4	617.8	8.05	12.06.2026		
9000	E51WFL-1030		PL12X190		S355J2+N	4	400	190	12	7.2	28.6		12.06.2026		
9000	E51WFL-1032		PL5X140		S355J2+N	4	240	140	5	1.3	5.3		12.06.2026	01	29.06.2026
9000	E51WFL-1056		PL16X162		S355J2	2	150	162	16	2.6	5.1		12.06.2026		
9000	E51WFP-1035		CFRHS250X150X5		S355J2H	2	9610	0	0	289.4	578.8		12.06.2026		
9000	E51WF-1034	FRAME		EXC2	RAL 7024 (Graphite Gray)	1	9620	162	387	222.6	228.7	5.99	12.06.2026	01	29.06.2026
9000	E51WFL-1031		PL12X190		S355J2+N	2	300	190	12	5.4	10.7		12.06.2026		
9000	E51WFL-1033		PL5X140		S355J2+N	2	140	140	5	0.8	1.5		12.06.2026		
9000	E51WFL-1056		PL16X162		S355J2	1	150	162	16	2.6	2.6		12.06.2026		
9000	E51WFP-1026		CFRHS150X150X5		S355J2H	1	9610	0	0	213.9	213.9		12.06.2026	01	29.06.2026
9000	E51WF-1035	FRAME		EXC2	RAL 7024 (Graphite Gray)	2	9620	162	387	222.6	457.5	5.99	12.06.2026		
9000	E51WFL-1031		PL12X190		S355J2+N	4	300	190	12	5.4	21.5		12.06.2026		
9000	E51WFL-1033		PL5X140		S355J2+N	4	140	140	5	0.8	3.1		12.06.2026		
9000	E51WFL-1056		PL16X162		S355J2	2	150	162	16	2.6	5.1		12.06.2026		
9000	E51WFP-1037		CFRHS150X150X5		S355J2H	2	9610	0	0	213.9	427.8		12.06.2026		

9000	E51WF-1036	BEAM		EXC2	RAL 7024 (Graphite Gray)	2	3180	100	211	74.0	148.1	2.26	12.06.2026		
9000	E51WFL-1041		PL10X100		S355J2+N	2	210	100	10	1.6	3.3		12.06.2026		
9000	E51WFP-1032		UPE200		S355J2H	2	3180	0	0	72.4	144.8		12.06.2026		
9000	E51WF-1037	BEAM		EXC2	RAL 7024 (Graphite Gray)	3	3180	80	200	72.4	217.2	2.22	12.06.2026		
9000	E51WFP-1031		UPE200		S355J2H	3	3180	0	0	72.4	217.2		12.06.2026		
9000	E51WF-1038	BEAM		EXC2	RAL 7024 (Graphite Gray)	2	3140	100	211	73.1	146.3	2.24	12.06.2026		
9000	E51WFL-1041		PL10X100		S355J2+N	2	210	100	10	1.6	3.3		12.06.2026		
9000	E51WFP-1025		UPE200		S355J2H	2	3140	0	0	71.5	143.0		12.06.2026		
9000	E51WF-1039	BEAM		EXC2	RAL 7024 (Graphite Gray)	1	3180	100	211	74.0	74.0	2.26	12.06.2026		
9000	E51WFL-1041		PL10X100		S355J2+N	1	210	100	10	1.6	1.6		12.06.2026		
9000	E51WFP-1038		UPE200		S355J2H	1	3180	0	0	72.4	72.4		12.06.2026		
9000	E51WF-1040	BEAM		EXC2	RAL 7024 (Graphite Gray)	1	3140	100	211	73.1	73.1	2.24	12.06.2026		
9000	E51WFL-1041		PL10X100		S355J2+N	1	210	100	10	1.6	1.6		12.06.2026		
9000	E51WFP-1036		UPE200		S355J2H	1	3140	0	0	71.5	71.5		12.06.2026		
9000	E51WF-1041	FRAME		EXC2	RAL 7024 (Graphite Gray)	1	3355	200	255	68.7	68.7	1.80	12.06.2026		
9000	E51WFL-1042		PL10X200		S355J2+N	1	180	200	10	2.8	2.8		12.06.2026		
9000	E51WFL-1043		PL15X150		S355J2+N	1	240	150	15	4.2	4.2		12.06.2026		
9000	E51WFL-1044		PL8X60		S355J2+N	1	120	60	8	0.4	0.4		12.06.2026		
9000	E51WFL-1045		PL5X110		S355J2+N	1	115	110	5	0.5	0.5		12.06.2026		
9000	E51WFL-1046		PL15X100		S355J2+N	1	240	100	15	2.8	2.8		12.06.2026		
9000	E51WFL-1052		PL10X75		S355J2+N	1	120	75	10	0.7	0.7		12.06.2026		
9000	E51WFP-1043		CFRHS120X120X5		S355J2H	1	3265	0	0	57.3	57.3		12.06.2026		
9000	E51WF-1042	FRAME		EXC2	RAL 7024 (Graphite Gray)	2	3065	200	255	61.4	122.9	1.60	12.06.2026		
9000	E51WFL-1042		PL10X200		S355J2+N	2	180	200	10	2.8	5.5		12.06.2026		
9000	E51WFL-1043		PL15X150		S355J2+N	2	240	150	15	4.2	8.5		12.06.2026		
9000	E51WFL-1044		PL8X60		S355J2+N	2	120	60	8	0.4	0.8		12.06.2026		
9000	E51WFL-1050		PL12X75		S355J2+N	2	120	75	12	0.8	1.7		12.06.2026		
9000	E51WFL-1051		PL15X120		S355J2+N	2	120	120	15	1.6	3.3		12.06.2026		
9000	E51WFL-1052		PL10X75		S355J2+N	2	120	75	10	0.7	1.4		12.06.2026		
9000	E51WFP-1042		CFRHS120X120X5		S355J2H	2	2895	0	0	50.8	101.6		12.06.2026		
9000	E51WF-1043	FRAME		EXC2	RAL 7024 (Graphite Gray)	1	3350	200	255	68.7	68.7	1.79	12.06.2026		
9000	E51WFL-1042		PL10X200		S355J2+N	1	180	200	10	2.8	2.8		12.06.2026		
9000	E51WFL-1043		PL15X150		S355J2+N	1	240	150	15	4.2	4.2		12.06.2026		
9000	E51WFL-1044		PL8X60		S355J2+N	1	120	60	8	0.4	0.4		12.06.2026		
9000	E51WFL-1045		PL5X110		S355J2+N	1	115	110	5	0.5	0.5		12.06.2026		
9000	E51WFL-1046		PL15X100		S355J2+N	1	240	100	15	2.8	2.8		12.06.2026		
9000	E51WFL-1052		PL10X75		S355J2+N	1	120	75	10	0.7	0.7		12.06.2026		
9000	E51WFP-1039		CFRHS120X120X5		S355J2H	1	3260	0	0	57.2	57.2		12.06.2026		


9000	E51WF-1044	FRAME		EXC2	RAL 7024 (Graphite Gray)	1	3350	200	255	68.7	68.7	1.79	12.06.2026		
9000	E51WFL-1042		PL10X200		S355J2+N	1	180	200	10	2.8	2.8		12.06.2026		
9000	E51WFL-1043		PL15X150		S355J2+N	1	240	150	15	4.2	4.2		12.06.2026		
9000	E51WFL-1044		PL8X60		S355J2+N	1	120	60	8	0.4	0.4		12.06.2026		
9000	E51WFL-1045		PL5X110		S355J2+N	1	115	110	5	0.5	0.5		12.06.2026		
9000	E51WFL-1046		PL15X100		S355J2+N	1	240	100	15	2.8	2.8		12.06.2026		
9000	E51WFL-1052		PL10X75		S355J2+N	1	120	75	10	0.7	0.7		12.06.2026		
9000	E51WFP-1039		CFRHS120X120X5		S355J2H	1	3260	0	0	57.2	57.2		12.06.2026		
9000	E51WF-1045	FRAME		EXC2	RAL 7024 (Graphite Gray)	1	2235	200	120	27.5	27.5	0.91	12.06.2026		
9000	E51WFL-1020		PL10X100		S355J2+N	1	150	100	10	1.2	1.2		12.06.2026		
9000	E51WFL-1021		PL15X100		S355J2+N	1	100	100	15	1.2	1.2		12.06.2026		
9000	E51WFL-1040		PL5X200		S355J2+N	1	120	200	5	0.9	0.9		12.06.2026		
9000	E51WFP-1003		CFRHS100X100X4		S355J2H	1	2065	0	0	24.2	24.2		12.06.2026		
9000	E51WF-1046	FRAME		EXC2	RAL 7024 (Graphite Gray)	1	4091	245	310	105.9	107.0	2.74	12.06.2026		
9000	E51WFL-1034		PL8X205		S355J2+N	1	205	205	8	2.6	2.6		12.06.2026		
9000	E51WFL-1035		PL20X200		S355J2+N	1	240	200	20	7.5	7.5		12.06.2026		
9000	E51WFL-1036		PL10X150		S355J2+N	1	150	150	10	1.8	1.8		12.06.2026		
9000	E51WFL-1049		PL12X75		S355J2+N	2	150	75	12	1.1	2.1		12.06.2026		
9000	E51WFP-1027		CFRHS150X150X5		S355J2H	1	4073	0	0	90.7	90.7		12.06.2026		
9000	E51WFP-1034		L100*10		S355J2	1	150	0	0	2.3	2.3		12.06.2026		
9000	E51WF-1047	FRAME		EXC2	RAL 7024 (Graphite Gray)	4	2390	120	120	41.1	174.0	1.14	12.06.2026		
9000	E51WFL-1051		PL15X120		S355J2+N	8	120	120	15	1.6	13.2		12.06.2026		
9000	E51WFL-1053		PL10X75		S355J2+N	8	120	75	10	0.7	5.6		12.06.2026		
9000	E51WFP-1041		CFRHS120X120X5		S355J2H	4	2210	0	0	38.8	155.1		12.06.2026		
9000	E51WF-1048	FRAME		EXC2	RAL 7024 (Graphite Gray)	1	3355	200	357	71.3	71.3	1.85	12.06.2026		
9000	E51WFL-1042		PL10X200		S355J2+N	1	180	200	10	2.8	2.8		12.06.2026		
9000	E51WFL-1043		PL15X150		S355J2+N	1	240	150	15	4.2	4.2		12.06.2026		
9000	E51WFL-1044		PL8X60		S355J2+N	1	120	60	8	0.4	0.4		12.06.2026		
9000	E51WFL-1045		PL5X110		S355J2+N	1	115	110	5	0.5	0.5		12.06.2026		
9000	E51WFL-1046		PL15X100		S355J2+N	1	240	100	15	2.8	2.8		12.06.2026		
9000	E51WFL-1052		PL10X75		S355J2+N	1	120	75	10	0.7	0.7		12.06.2026		
9000	E51WFL-1056		PL16X162		S355J2	1	150	162	16	2.6	2.6		12.06.2026		
9000	E51WFP-1043		CFRHS120X120X5		S355J2H	1	3265	0	0	57.3	57.3		12.06.2026		
9000	E51WF-1049	FRAME		EXC2	RAL 7024 (Graphite Gray)	1	3065	200	357	64.0	64.0	1.65	12.06.2026		
9000	E51WFL-1042		PL10X200		S355J2+N	1	180	200	10	2.8	2.8		12.06.2026		
9000	E51WFL-1043		PL15X150		S355J2+N	1	240	150	15	4.2	4.2		12.06.2026		
9000	E51WFL-1044		PL8X60		S355J2+N	1	120	60	8	0.4	0.4		12.06.2026		
9000	E51WFL-1050		PL12X75		S355J2+N	1	120	75	12	0.8	0.8		12.06.2026		
9000	E51WFL-1051		PL15X120		S355J2+N	1	120	120	15	1.6	1.6		12.06.2026		
9000	E51WFL-1052		PL10X75		S355J2+N	1	120	75	10	0.7	0.7		12.06.2026		
9000	E51WFL-1056		PL16X162		S355J2	1	150	162	16	2.6	2.6		12.06.2026		
9000	E51WFP-1042		CFRHS120X120X5		S355J2H	1	2895	0	0	50.8	50.8		12.06.2026		

9000	E51WF-1050	FRAME		EXC2	RAL 7024 (Graphite Gray)	1	3345	200	357	71.1	71.1	1.84	12.06.2026		
9000	E51WFL-1042		PL10X200		S355J2+N	1	180	200	10	2.8	2.8		12.06.2026		
9000	E51WFL-1043		PL15X150		S355J2+N	1	240	150	15	4.2	4.2		12.06.2026		
9000	E51WFL-1044		PL8X60		S355J2+N	1	120	60	8	0.4	0.4		12.06.2026		
9000	E51WFL-1045		PL5X110		S355J2+N	1	115	110	5	0.5	0.5		12.06.2026		
9000	E51WFL-1046		PL15X100		S355J2+N	1	240	100	15	2.8	2.8		12.06.2026		
9000	E51WFL-1052		PL10X75		S355J2+N	1	120	75	10	0.7	0.7		12.06.2026		
9000	E51WFL-1056		PL16X162		S355J2	1	150	162	16	2.6	2.6		12.06.2026		
9000	E51WFP-1040		CFRHS120X120X5		S355J2H	1	3255	0	0	57.1	57.1		12.06.2026		
9000	E51WF-1051	FRAME		EXC2	RAL 7024 (Graphite Gray)	1	3345	200	357	71.1	71.1	1.84	12.06.2026		
9000	E51WFL-1042		PL10X200		S355J2+N	1	180	200	10	2.8	2.8		12.06.2026		
9000	E51WFL-1043		PL15X150		S355J2+N	1	240	150	15	4.2	4.2		12.06.2026		
9000	E51WFL-1044		PL8X60		S355J2+N	1	120	60	8	0.4	0.4		12.06.2026		
9000	E51WFL-1045		PL5X110		S355J2+N	1	115	110	5	0.5	0.5		12.06.2026		
9000	E51WFL-1046		PL15X100		S355J2+N	1	240	100	15	2.8	2.8		12.06.2026		
9000	E51WFL-1052		PL10X75		S355J2+N	1	120	75	10	0.7	0.7		12.06.2026		
9000	E51WFL-1056		PL16X162		S355J2	1	150	162	16	2.6	2.6		12.06.2026		
9000	E51WFP-1040		CFRHS120X120X5		S355J2H	1	3255	0	0	57.1	57.1		12.06.2026		
9000	E51WF-1052	FRAME		EXC2	RAL 7024 (Graphite Gray)	1	4827	245	230	120.4	120.4	3.05	12.06.2026		
9000	E51WFL-1035		PL20X200		S355J2+N	1	240	200	20	7.5	7.5		12.06.2026		
9000	E51WFL-1036		PL10X150		S355J2+N	1	150	150	10	1.8	1.8		12.06.2026		
9000	E51WFL-1037		PL15X210		S355J2+N	1	160	210	15	4.0	4.0		12.06.2026		
9000	E51WFL-1038		PL10X150		S355J2+N	1	150	150	10	1.7	1.7		12.06.2026		
9000	E51WFP-1028		CFRHS150X150X5		S355J2H	1	4736	0	0	105.4	105.4		12.06.2026		
9000	E51WF-1053	FRAME		EXC2	RAL 7024 (Graphite Gray)	1	3505	200	255	69.5	69.5	1.84	12.06.2026		
9000	E51WFL-1042		PL10X200		S355J2+N	1	180	200	10	2.8	2.8		12.06.2026		
9000	E51WFL-1043		PL15X150		S355J2+N	1	240	150	15	4.2	4.2		12.06.2026		
9000	E51WFL-1044		PL8X60		S355J2+N	1	120	60	8	0.4	0.4		12.06.2026		
9000	E51WFL-1045		PL5X110		S355J2+N	1	115	110	5	0.5	0.5		12.06.2026		
9000	E51WFL-1047		PL10X60		S355J2+N	1	100	60	10	0.5	0.5		12.06.2026		
9000	E51WFL-1052		PL10X75		S355J2+N	1	120	75	10	0.7	0.7		12.06.2026		
9000	E51WFL-1057		PL10X60		S355J2+N	1	100	60	10	0.5	0.5		12.06.2026		
9000	E51WFP-1047		CFRHS120X120X5		S355J2H	1	3415	0	0	59.9	59.9		12.06.2026		
9000	E51WF-1054	FRAME		EXC2	RAL 7024 (Graphite Gray)	1	3500	200	255	69.4	69.4	1.83	12.06.2026		
9000	E51WFL-1042		PL10X200		S355J2+N	1	180	200	10	2.8	2.8		12.06.2026		
9000	E51WFL-1043		PL15X150		S355J2+N	1	240	150	15	4.2	4.2		12.06.2026		
9000	E51WFL-1044		PL8X60		S355J2+N	1	120	60	8	0.4	0.4		12.06.2026		
9000	E51WFL-1045		PL5X110		S355J2+N	1	115	110	5	0.5	0.5		12.06.2026		
9000	E51WFL-1048		PL10X60		S355J2+N	1	100	60	10	0.5	0.5		12.06.2026		
9000	E51WFL-1052		PL10X75		S355J2+N	1	120	75	10	0.7	0.7		12.06.2026		
9000	E51WFL-1057		PL10X60		S355J2+N	1	100	60	10	0.5	0.5		12.06.2026		
9000	E51WFP-1044		CFRHS120X120X5		S355J2H	1	3410	0	0	59.8	59.8		12.06.2026		


9000	E51WF-1055	FRAME		EXC2	RAL 7024 (Graphite Gray)	1	3500	200	255	69.4	69.4	1.83	12.06.2026		
9000	E51WFL-1042		PL10X200		S355J2+N	1	180	200	10	2.8	2.8		12.06.2026		
9000	E51WFL-1043		PL15X150		S355J2+N	1	240	150	15	4.2	4.2		12.06.2026		
9000	E51WFL-1044		PL8X60		S355J2+N	1	120	60	8	0.4	0.4		12.06.2026		
9000	E51WFL-1045		PL5X110		S355J2+N	1	115	110	5	0.5	0.5		12.06.2026		
9000	E51WFL-1047		PL10X60		S355J2+N	1	100	60	10	0.5	0.5		12.06.2026		
9000	E51WFL-1052		PL10X75		S355J2+N	1	120	75	10	0.7	0.7		12.06.2026		
9000	E51WFL-1057		PL10X60		S355J2+N	1	100	60	10	0.5	0.5		12.06.2026		
9000	E51WFP-1044		CFRHS120X120X5		S355J2H	1	3410	0	0	59.8	59.8		12.06.2026		
9000	E51WF-1056	FRAME		EXC2	RAL 7024 (Graphite Gray)	4	1190	120	120	20.1	89.7	0.58	12.06.2026		
9000	E51WFL-1051		PL15X120		S355J2+N	8	120	120	15	1.6	13.2		12.06.2026		
9000	E51WFL-1053		PL10X75		S355J2+N	8	120	75	10	0.7	5.6		12.06.2026		
9000	E51WFP-1045		CFRHS120X120X5		S355J2H	4	1010	0	0	17.7	70.9		12.06.2026		
9000	E51WF-1057	FRAME		EXC2	RAL 7024 (Graphite Gray)	1	5612	300	380	178.6	179.6	4.10	12.06.2026		
9000	E51WFL-1037		PL15X210		S355J2+N	1	160	210	15	4.0	4.0		12.06.2026		
9000	E51WFL-1038		PL10X150		S355J2+N	1	150	150	10	1.7	1.7		12.06.2026		
9000	E51WFL-1039		PL15X270		S355J2+N	1	217	270	15	6.9	6.9		12.06.2026		
9000	E51WFL-1049		PL12X75		S355J2+N	2	150	75	12	1.1	2.1		12.06.2026		
9000	E51WFL-1054		PL10X300		S355J2+N	1	150	300	10	3.2	3.2		12.06.2026		
9000	E51WFL-1055		PL10X135		S355J2+N	1	150	135	10	1.5	1.5		12.06.2026		
9000	E51WFP-1029		CFRHS150X150X5		S355J2H	1	4440	0	0	98.8	98.8		12.06.2026		
9000	E51WFP-1030		L150*15		S355J2	1	1820	0	0	61.4	61.4		12.06.2026		
9000	E51WF-1058	FRAME		EXC2	RAL 7024 (Graphite Gray)	1	3500	200	357	71.9	71.9	1.88	12.06.2026		
9000	E51WFL-1042		PL10X200		S355J2+N	1	180	200	10	2.8	2.8		12.06.2026		
9000	E51WFL-1043		PL15X150		S355J2+N	1	240	150	15	4.2	4.2		12.06.2026		
9000	E51WFL-1044		PL8X60		S355J2+N	1	120	60	8	0.4	0.4		12.06.2026		
9000	E51WFL-1045		PL5X110		S355J2+N	1	115	110	5	0.5	0.5		12.06.2026		
9000	E51WFL-1047		PL10X60		S355J2+N	1	100	60	10	0.5	0.5		12.06.2026		
9000	E51WFL-1052		PL10X75		S355J2+N	1	120	75	10	0.7	0.7		12.06.2026		
9000	E51WFL-1056		PL16X162		S355J2	1	150	162	16	2.6	2.6		12.06.2026		
9000	E51WFL-1057		PL10X60		S355J2+N	1	100	60	10	0.5	0.5		12.06.2026		
9000	E51WFP-1044		CFRHS120X120X5		S355J2H	1	3410	0	0	59.8	59.8		12.06.2026		
9000	E51WF-1059	FRAME		EXC2	RAL 7024 (Graphite Gray)	1	3060	200	357	63.9	63.9	1.64	12.06.2026		
9000	E51WFL-1042		PL10X200		S355J2+N	1	180	200	10	2.8	2.8		12.06.2026		
9000	E51WFL-1043		PL15X150		S355J2+N	1	240	150	15	4.2	4.2		12.06.2026		
9000	E51WFL-1044		PL8X60		S355J2+N	1	120	60	8	0.4	0.4		12.06.2026		
9000	E51WFL-1050		PL12X75		S355J2+N	1	120	75	12	0.8	0.8		12.06.2026		
9000	E51WFL-1051		PL15X120		S355J2+N	1	120	120	15	1.6	1.6		12.06.2026		
9000	E51WFL-1052		PL10X75		S355J2+N	1	120	75	10	0.7	0.7		12.06.2026		
9000	E51WFL-1056		PL16X162		S355J2	1	150	162	16	2.6	2.6		12.06.2026		
9000	E51WFP-1046		CFRHS120X120X5		S355J2H	1	2890	0	0	50.7	50.7		12.06.2026		

9000	E51WF-1060	FRAME		EXC2	RAL 7024 (Graphite Gray)	1	3500	200	357	71.9	71.9	1.88	12.06.2026		
9000	E51WFL-1042		PL10X200		S355J2+N	1	180	200	10	2.8	2.8		12.06.2026		
9000	E51WFL-1043		PL15X150		S355J2+N	1	240	150	15	4.2	4.2		12.06.2026		
9000	E51WFL-1044		PL8X60		S355J2+N	1	120	60	8	0.4	0.4		12.06.2026		
9000	E51WFL-1045		PL5X110		S355J2+N	1	115	110	5	0.5	0.5		12.06.2026		
9000	E51WFL-1048		PL10X60		S355J2+N	1	100	60	10	0.5	0.5		12.06.2026		
9000	E51WFL-1052		PL10X75		S355J2+N	1	120	75	10	0.7	0.7		12.06.2026		
9000	E51WFL-1056		PL16X162		S355J2	1	150	162	16	2.6	2.6		12.06.2026		
9000	E51WFL-1057		PL10X60		S355J2+N	1	100	60	10	0.5	0.5		12.06.2026		
9000	E51WFP-1044		CFRHS120X120X5		S355J2H	1	3410	0	0	59.8	59.8		12.06.2026		
9000	E51WF-1061	FRAME		EXC2	RAL 7024 (Graphite Gray)	1	3500	200	357	71.9	71.9	1.88	12.06.2026		
9000	E51WFL-1042		PL10X200		S355J2+N	1	180	200	10	2.8	2.8		12.06.2026		
9000	E51WFL-1043		PL15X150		S355J2+N	1	240	150	15	4.2	4.2		12.06.2026		
9000	E51WFL-1044		PL8X60		S355J2+N	1	120	60	8	0.4	0.4		12.06.2026		
9000	E51WFL-1045		PL5X110		S355J2+N	1	115	110	5	0.5	0.5		12.06.2026		
9000	E51WFL-1047		PL10X60		S355J2+N	1	100	60	10	0.5	0.5		12.06.2026		
9000	E51WFL-1052		PL10X75		S355J2+N	1	120	75	10	0.7	0.7		12.06.2026		
9000	E51WFL-1056		PL16X162		S355J2	1	150	162	16	2.6	2.6		12.06.2026		
9000	E51WFL-1057		PL10X60		S355J2+N	1	100	60	10	0.5	0.5		12.06.2026		
9000	E51WFP-1044		CFRHS120X120X5		S355J2H	1	3410	0	0	59.8	59.8		12.06.2026		

PART LIST FOR ASSEMBLY E51WF-1007, MANUFACTURING AMOUNT 1 PIECES						
PART	PROFILE	MATERIAL	LENGTH [mm]	AREA [m2]	WEIGHT [kg]	PCS
E51WFL-1017	PL5X220	S355J2+N	140	0.07	1.2	1
E51WFL-1020	PL10X100	S355J2+N	150	0.03	1.2	1
E51WFL-1021	PL15X100	S355J2+N	100	0.03	1.2	1
E51WFP-1003	CFRHS100X100X4	S355J2H	2065	0.80	24.2	1
TOTAL:				0.92	27.8	

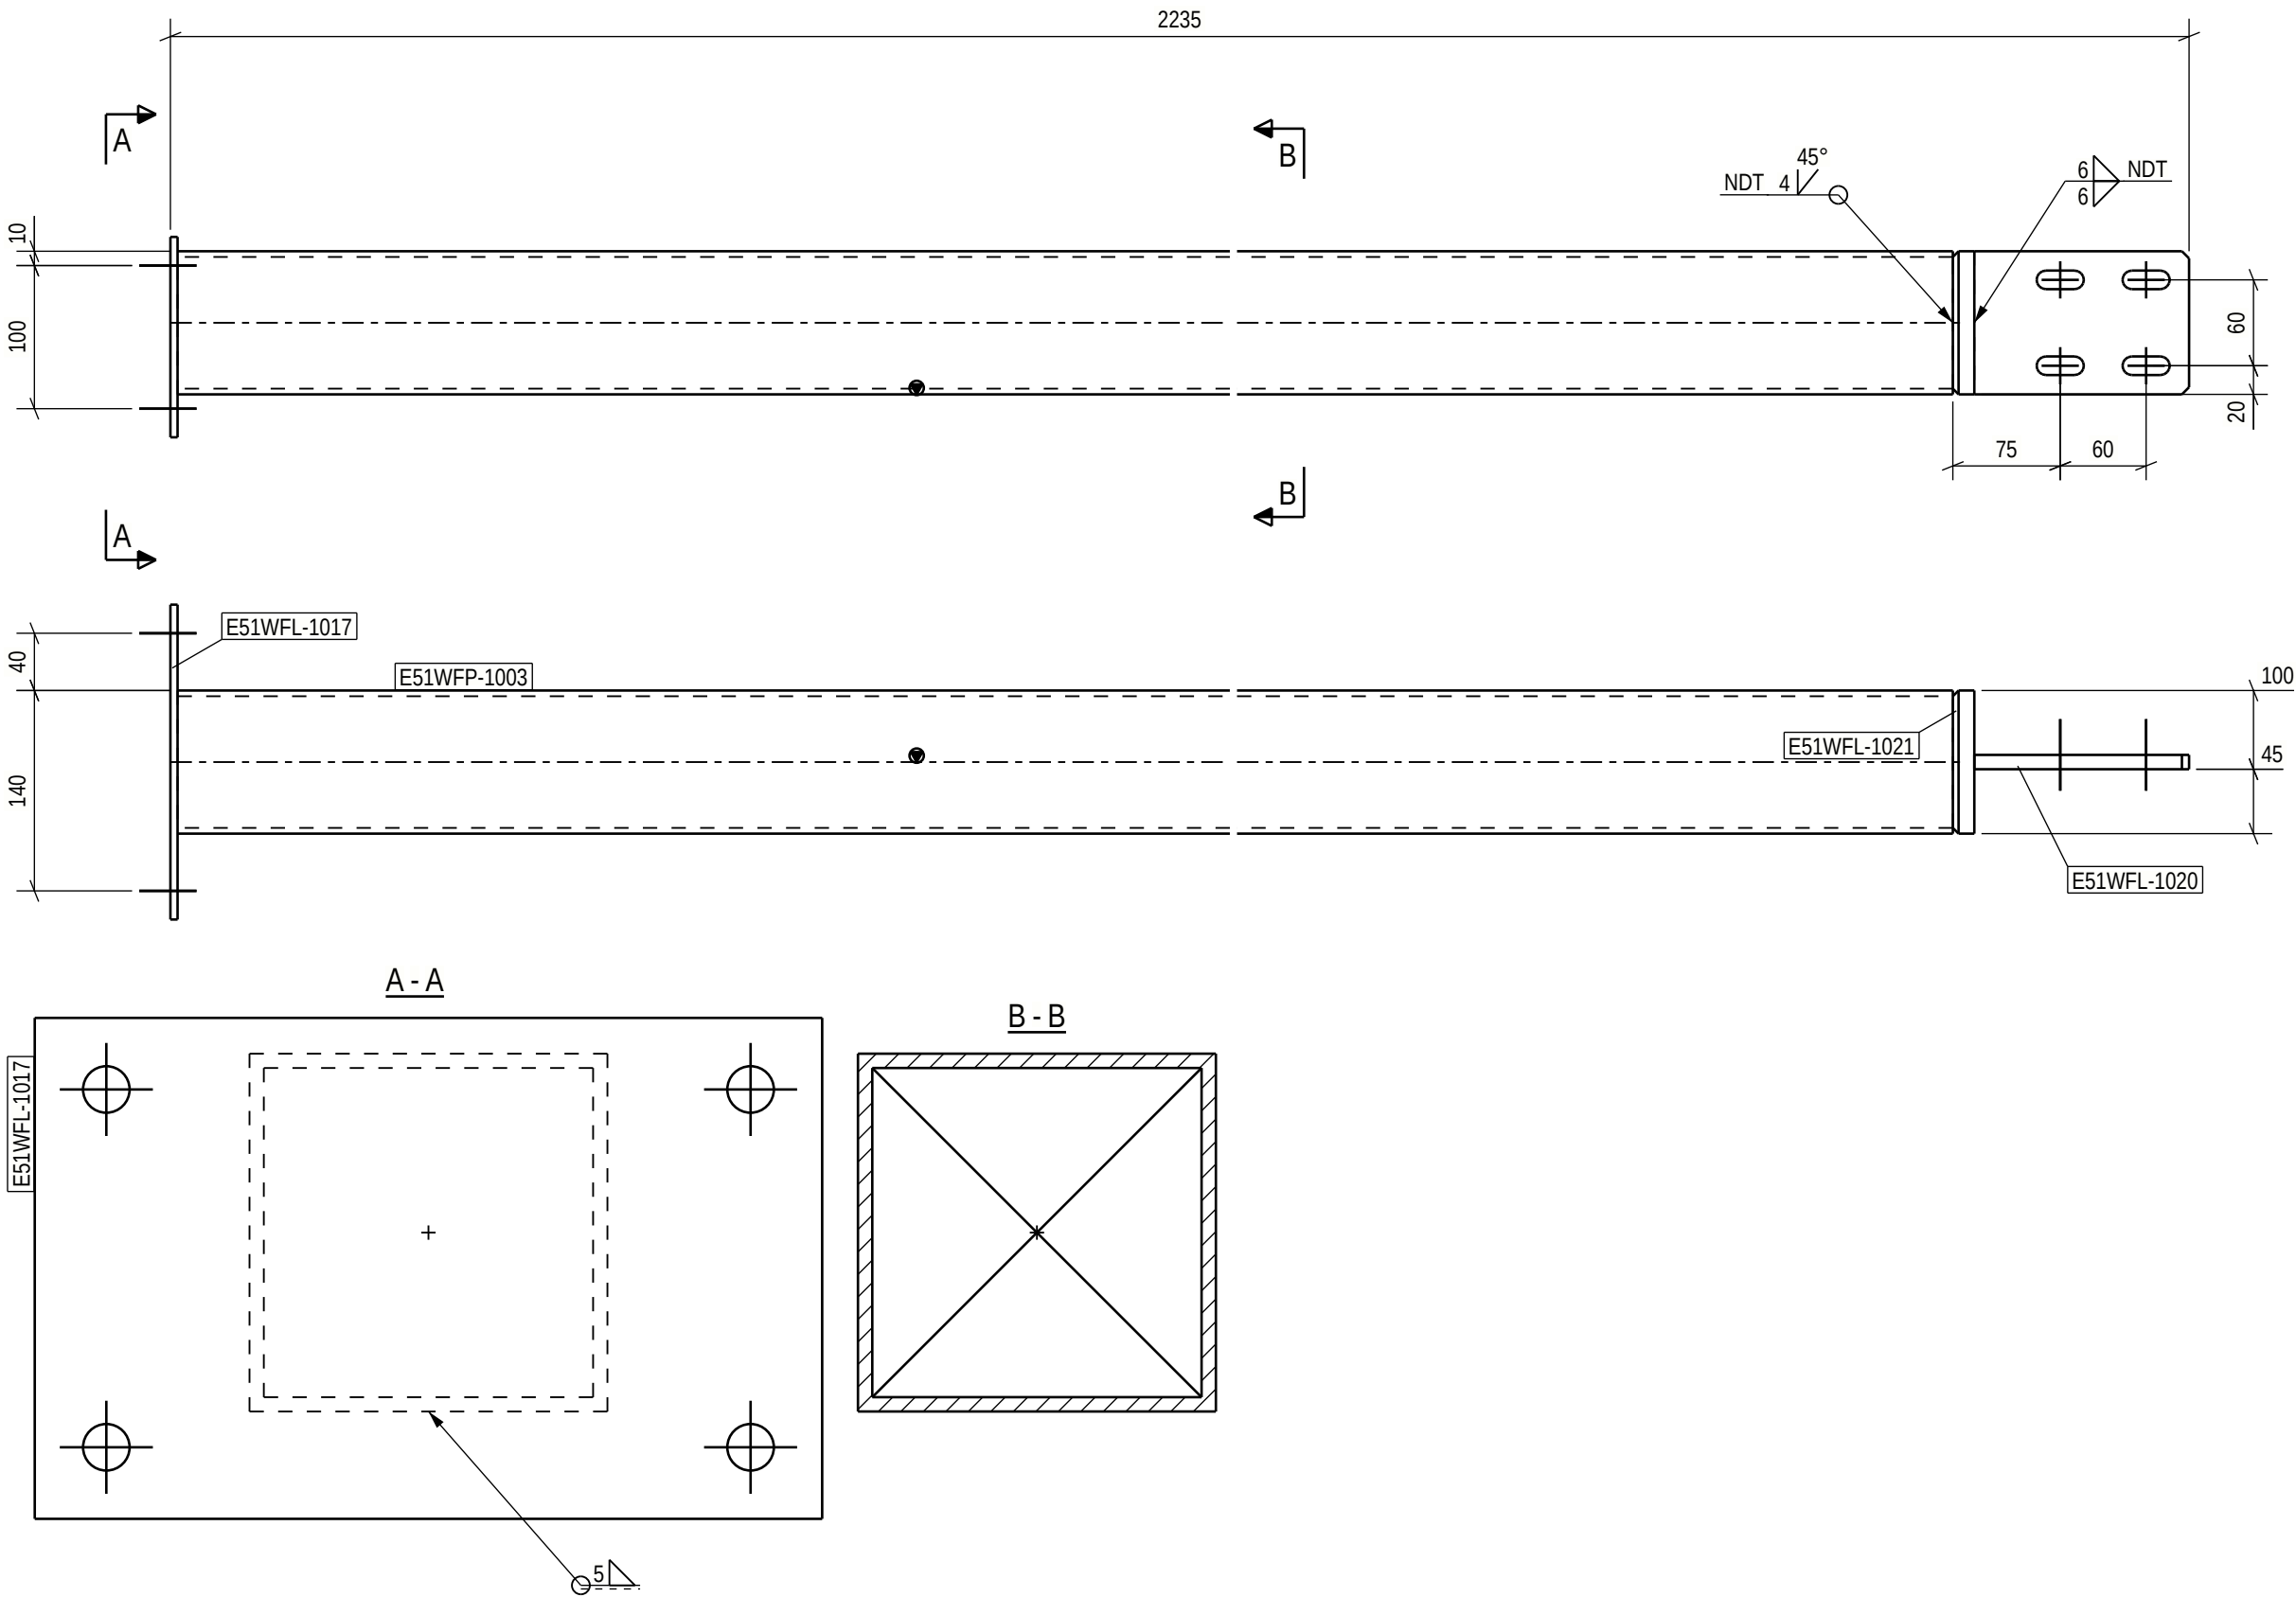

LIFTING LUG WELDING, WEIGHT < 1,5 t


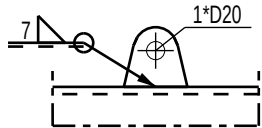


Technical fabrication requirements:		Execution class	
Requirements for fabrication, standard EN1090-2, table A.3 : EXC2		EXC2	
Execution Specification document nr 25019443-ICC250-0600-0660-000005		Fabrication tolerances EN 1090-2, Appendix B	
Surface preparation grade ISO8501-3, grade P2		Special fabrication tolerances Project specification/ shown on drwg.	
Surface treatment ISO12944-5		Weld inspection, requirements EN 1090-2, Table 24, U>0.5	
Additional requirements on surface treatment C3.07, EPPUR 240/2		Extent of NDT, fillet welds MT-EN1290, 20% of welds	
Shade RAL 7024 (Graphite Gray)		Extent of NDT, butt welds UT, EN-ISO17640, 20% of welds	
Welding of built up steel section Appendix 1 / Project spec.		Extent of NDT for splices not shown on drawing UT, EN-ISO17640, 100% of welds	
Welds, if not specified otherwise EN 9692-1, EN 9692-2		Requirements on hoisting EN1090-2 Section 6.6.3	
		Weld class C, EN ISO 5817	
		Additional material inspection Shown on drwg.	

PROJECT NAME Easpring New Materials Oy FAIR Phase 1		DRAWING CONTENT ASSEMBLY DRAWING FRAME E51WF-1007	
DATE 12.06.2026		ARCHIVING CODE	PAGE
DRAWN Alexey Serous		DESIGNER Alexey Serous	APPROVED Pertti Koivumaa
PROJECT NUMBER 25019443		DWG. NO. E51WF-1007	CHECKED Jere Kallosalmi
REVISION			


SWECO  Sustainable engineering and design		SWECO RAKENNETEKNIikka OY ILMALANPORTTI 2 00240 HELSINKI PUH. +358 207 393 000 www.sweco.fi	
---	--	---	--

For special tolerances of bolt hole location
see specification for steel structures
Approved For Construction

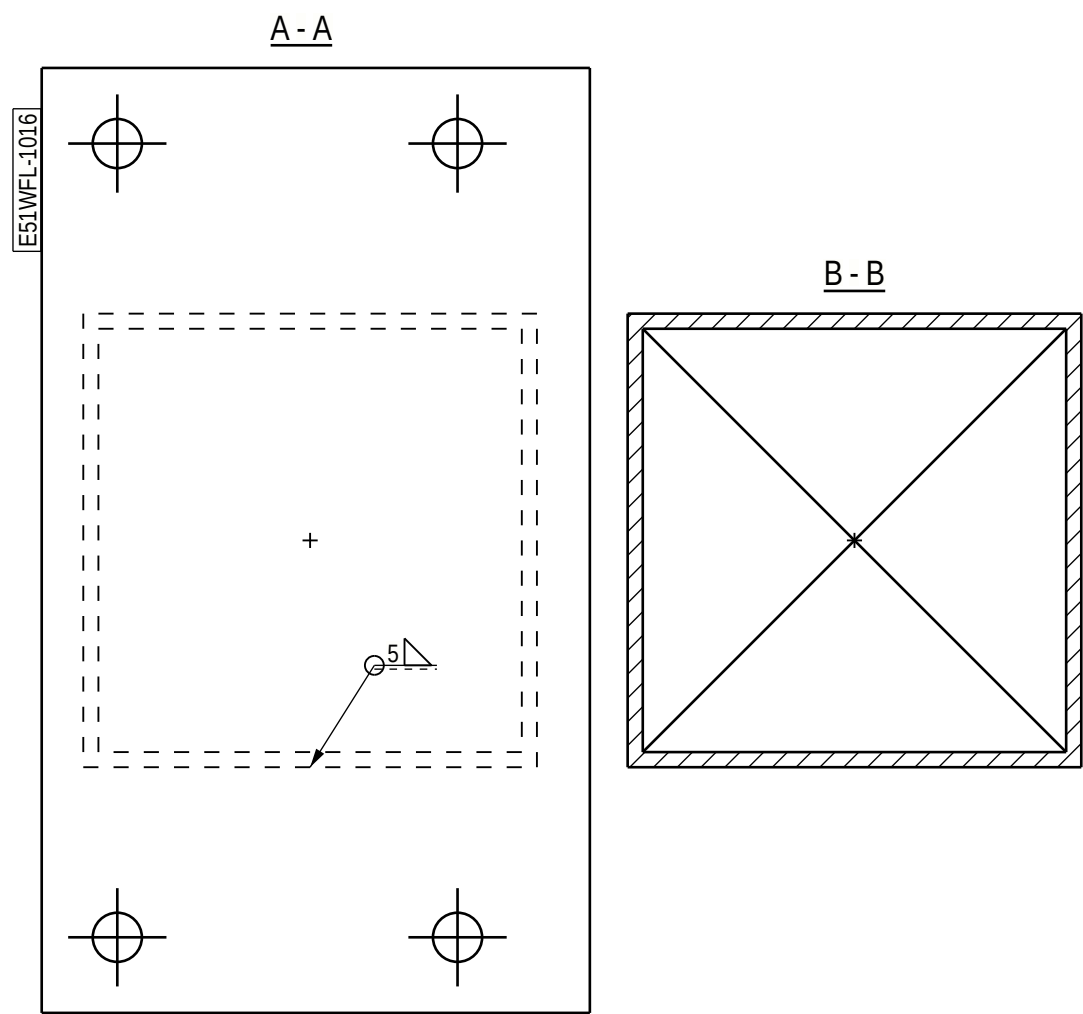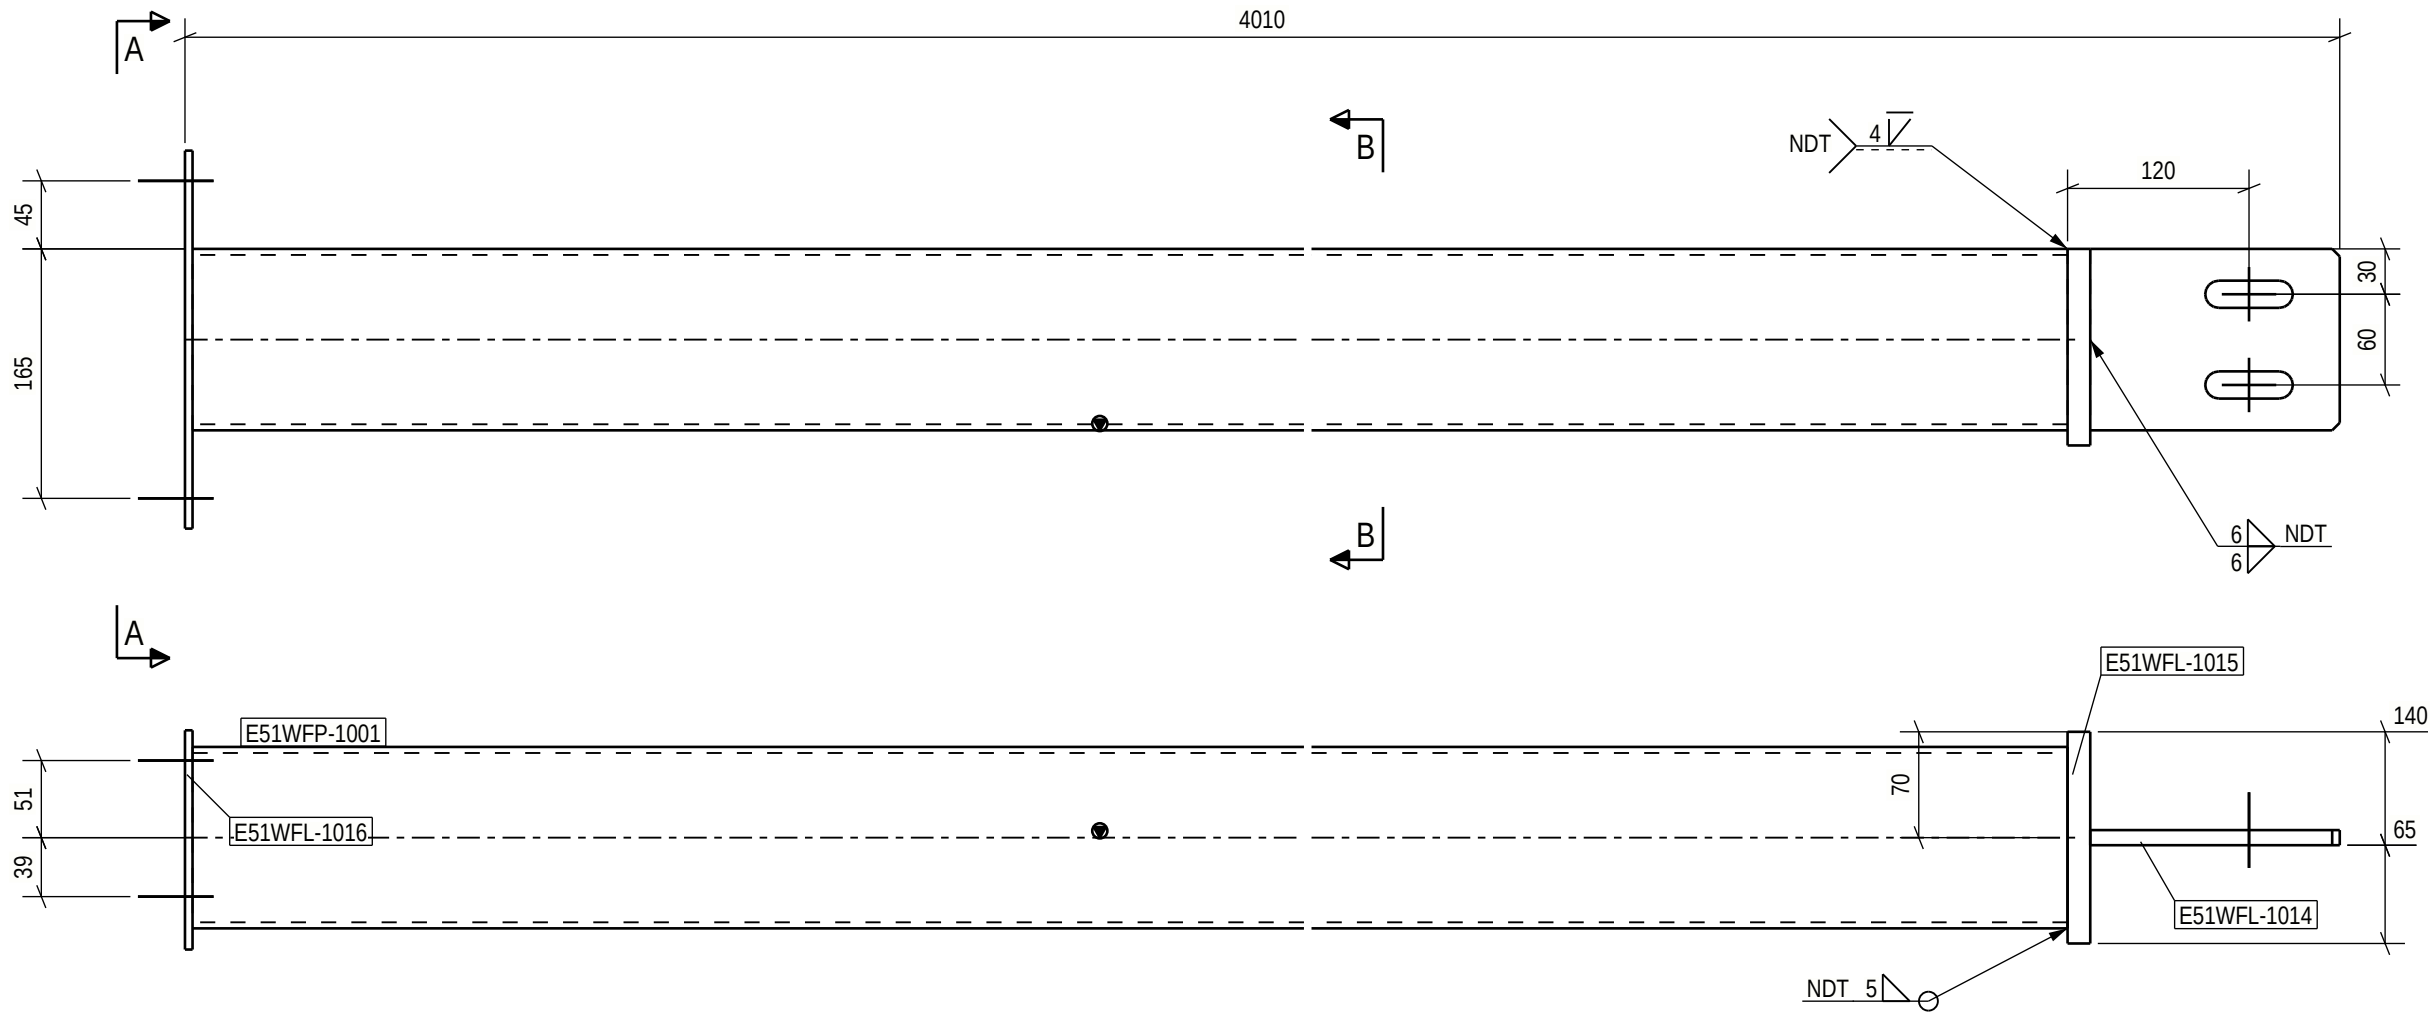

PART LIST FOR ASSEMBLY E51WF-1008, MANUFACTURING AMOUNT 1 PIECES						
PART	PROFILE	MATERIAL	LENGTH [mm]	AREA [m2]	WEIGHT [kg]	PCS
E51WFL-1014	PL10X120	S355J2+N	165	0.05	1.6	1
E51WFL-1015	PL15X130	S355J2+N	140	0.04	2.1	1
E51WFL-1016	PL5X145	S355J2+N	250	0.08	1.4	1
E51WFP-1001	CFRHS120X120X4	S355J2H	3825	1.78	54.5	1
TOTAL:				1.95	59.6	


LIFTING LUG WELDING, WEIGHT < 1,5 t

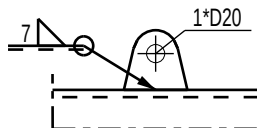

Technical fabrication requirements:		Execution class
Requirements for fabrication, standard EN1090-2, table A.3 : EXC2		EXC2
Execution Specification document nr 25019443-ICC250-0600-0660-000005	Fabrication tolerances EN 1090-2, Appendix B	
Surface preparation grade ISO8501-3, grade P2	Special fabrication tolerances Project specification/ shown on drwg.	
Surface treatment ISO12944-5	Weld inspection, requirements EN 1090-2, Table 24, U>0.5	
Additional requirements on surface treatment C3.07, EPPUR 240/2	Extent of NDT, fillet welds MT-EN1290, 20% of welds	
Shade RAL 7024 (Graphite Gray)	Extent of NDT, butt welds UT, EN-ISO17640, 20% of welds	
Welding of built up steel section Appendix 1 / Project spec.	Extent of NDT for splices not shown on drawing UT, EN-ISO17640, 100% of welds	
Welds, if not specified otherwise EN 9692-1, EN 9692-2	Requirements on holing EN1090-2 Section 6.6.3	
	Weld class C, EN ISO 5817	Additional material inspection Shown on drwg.

For special tolerances of bolt hole location
see specification for steel structures
Approved For Construction

PROJECT NAME
Easpring New Materials Oy
FAIR Phase 1

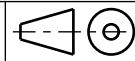


DRAWING CONTENT
ASSEMBLY DRAWING
FRAME
E51WF-1008

SWECO
Sustainable engineering and design


SWECO RAKENNETEKNIikka OY
ILMALANPORTTI 2
00240 HELSINKI
PUH. +358 207 393 000
www.sweco.fi

DATE	ARCHIVING CODE	PAGE	DESIGN GROUP
12.06.2026			STR
DRAWN	DESIGNER	APPROVED	CHECKED
Alexey Serous	Alexey Serous	Pertti Koivumaa	Jere Kallosalmi
PROJECT NUMBER	DWG. NO.	REVISION	
25019443	E51WF-1008		

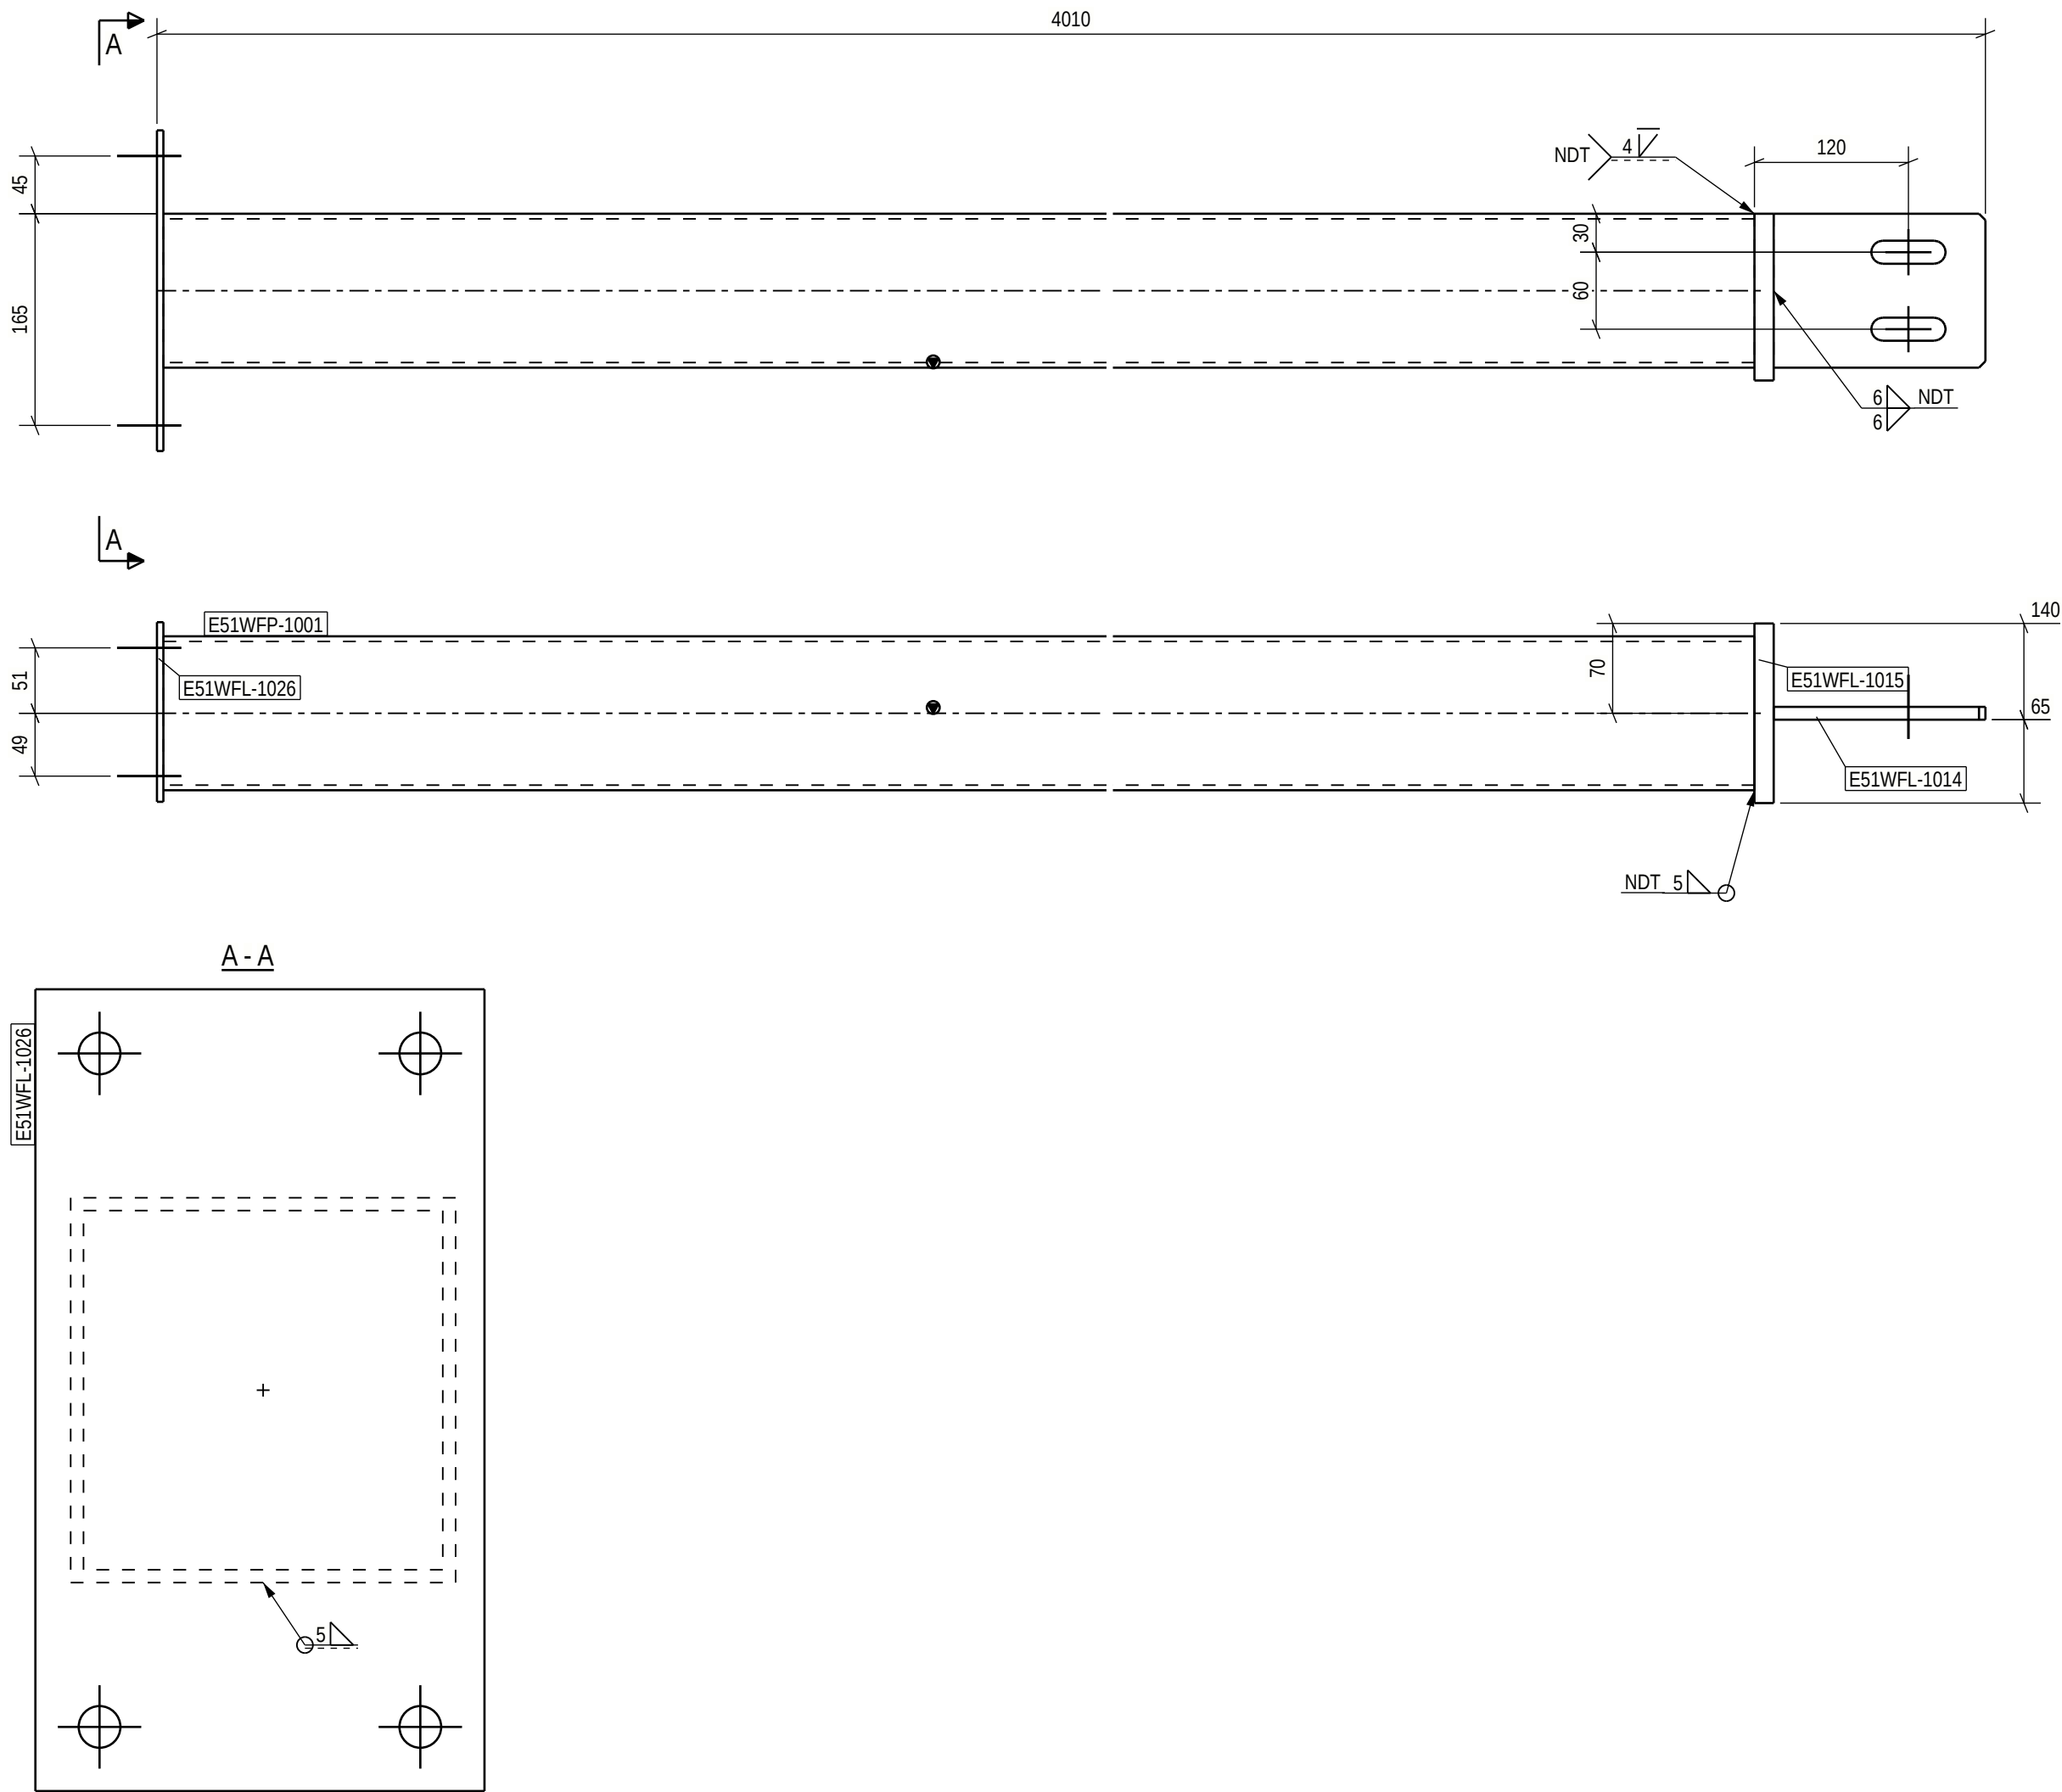

PART LIST FOR ASSEMBLY E51WF-1009, MANUFACTURING AMOUNT 2 PIECES						
PART	PROFILE	MATERIAL	LENGTH [mm]	AREA [m2]	WEIGHT [kg]	PCS
E51WFL-1014	PL10X120	S355J2+N	165	0.05	1.6	1
E51WFL-1015	PL15X130	S355J2+N	140	0.04	2.1	1
E51WFL-1026	PL5X140	S355J2+N	250	0.07	1.4	1
E51WFP-1001	CFRHS120X120X4	S355J2H	3825	1.78	54.5	1
TOTAL:				1.95	59.6	


LIFTING LUG WELDING, WEIGHT < 1,5 t

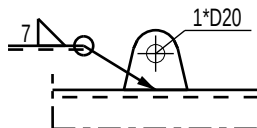

Technical fabrication requirements:		Execution class
Requirements for fabrication, standard EN1090-2, table A.3 : EXC2		EXC2
Execution Specification document nr 25019443-ICC250-0600-0660-000005	Fabrication tolerances EN 1090-2, Appendix B	
Surface preparation grade ISO8501-3, grade P2	Special fabrication tolerances Project specification/ shown on drwg.	
Surface treatment ISO12944-5	Weld inspection, requirements EN 1090-2, Table 24, U>0.5	
Additional requirements on surface treatment C3.07, EPPUR 240/2	Extent of NDT, fillet welds MT-EN1290, 20% of welds	
Shade RAL 7024 (Graphite Gray)	Extent of NDT for splices not shown on drawing UT, EN-ISO17640, 20% of welds	
Welding of built up steel section Appendix 1 / Project spec.	Extent of NDT, butt welds UT, EN-ISO17640, 100% of welds	
Welds, if not specified otherwise EN 9692-1, EN 9692-2	Requirements on holing EN1090-2 Section 6.6.3	
	Weld class C, EN ISO 5817	Additional material inspection Shown on drwg.

For special tolerances of bolt hole location
see specification for steel structures
Approved For Construction

PROJECT NAME
Easpring New Materials Oy
FAIR Phase 1

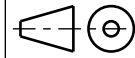


DRAWING CONTENT
ASSEMBLY DRAWING
FRAME
E51WF-1009

SWECO
Sustainable engineering and design


SWECO RAKENNETEKNIikka OY
ILMALANPORTTI 2
00240 HELSINKI
PUH. +358 207 393 000
www.sweco.fi

DATE	ARCHIVING CODE	PAGE	DESIGN GROUP
12.06.2026			STR
DRAWN	DESIGNER	APPROVED	CHECKED
Alexey Serous	Alexey Serous	Pertti Koivumaa	Jere Kallosalmi
PROJECT NUMBER	DWG. NO.	REVISION	
25019443	E51WF-1009		

PART LIST FOR ASSEMBLY E51WF-1010, MANUFACTURING AMOUNT 3 PIECES						
PART	PROFILE	MATERIAL	LENGTH [mm]	AREA [m2]	WEIGHT [kg]	PCS
E51WFL-1014	PL10X120	S355J2+N	165	0.05	1.6	1
E51WFL-1015	PL15X130	S355J2+N	140	0.04	2.1	1
E51WFL-1027	PL5X140	S355J2+N	250	0.07	1.4	1
E51WFP-1001	CFRHS120X120X4	S355J2H	3825	1.78	54.5	1
TOTAL:				1.95	59.6	

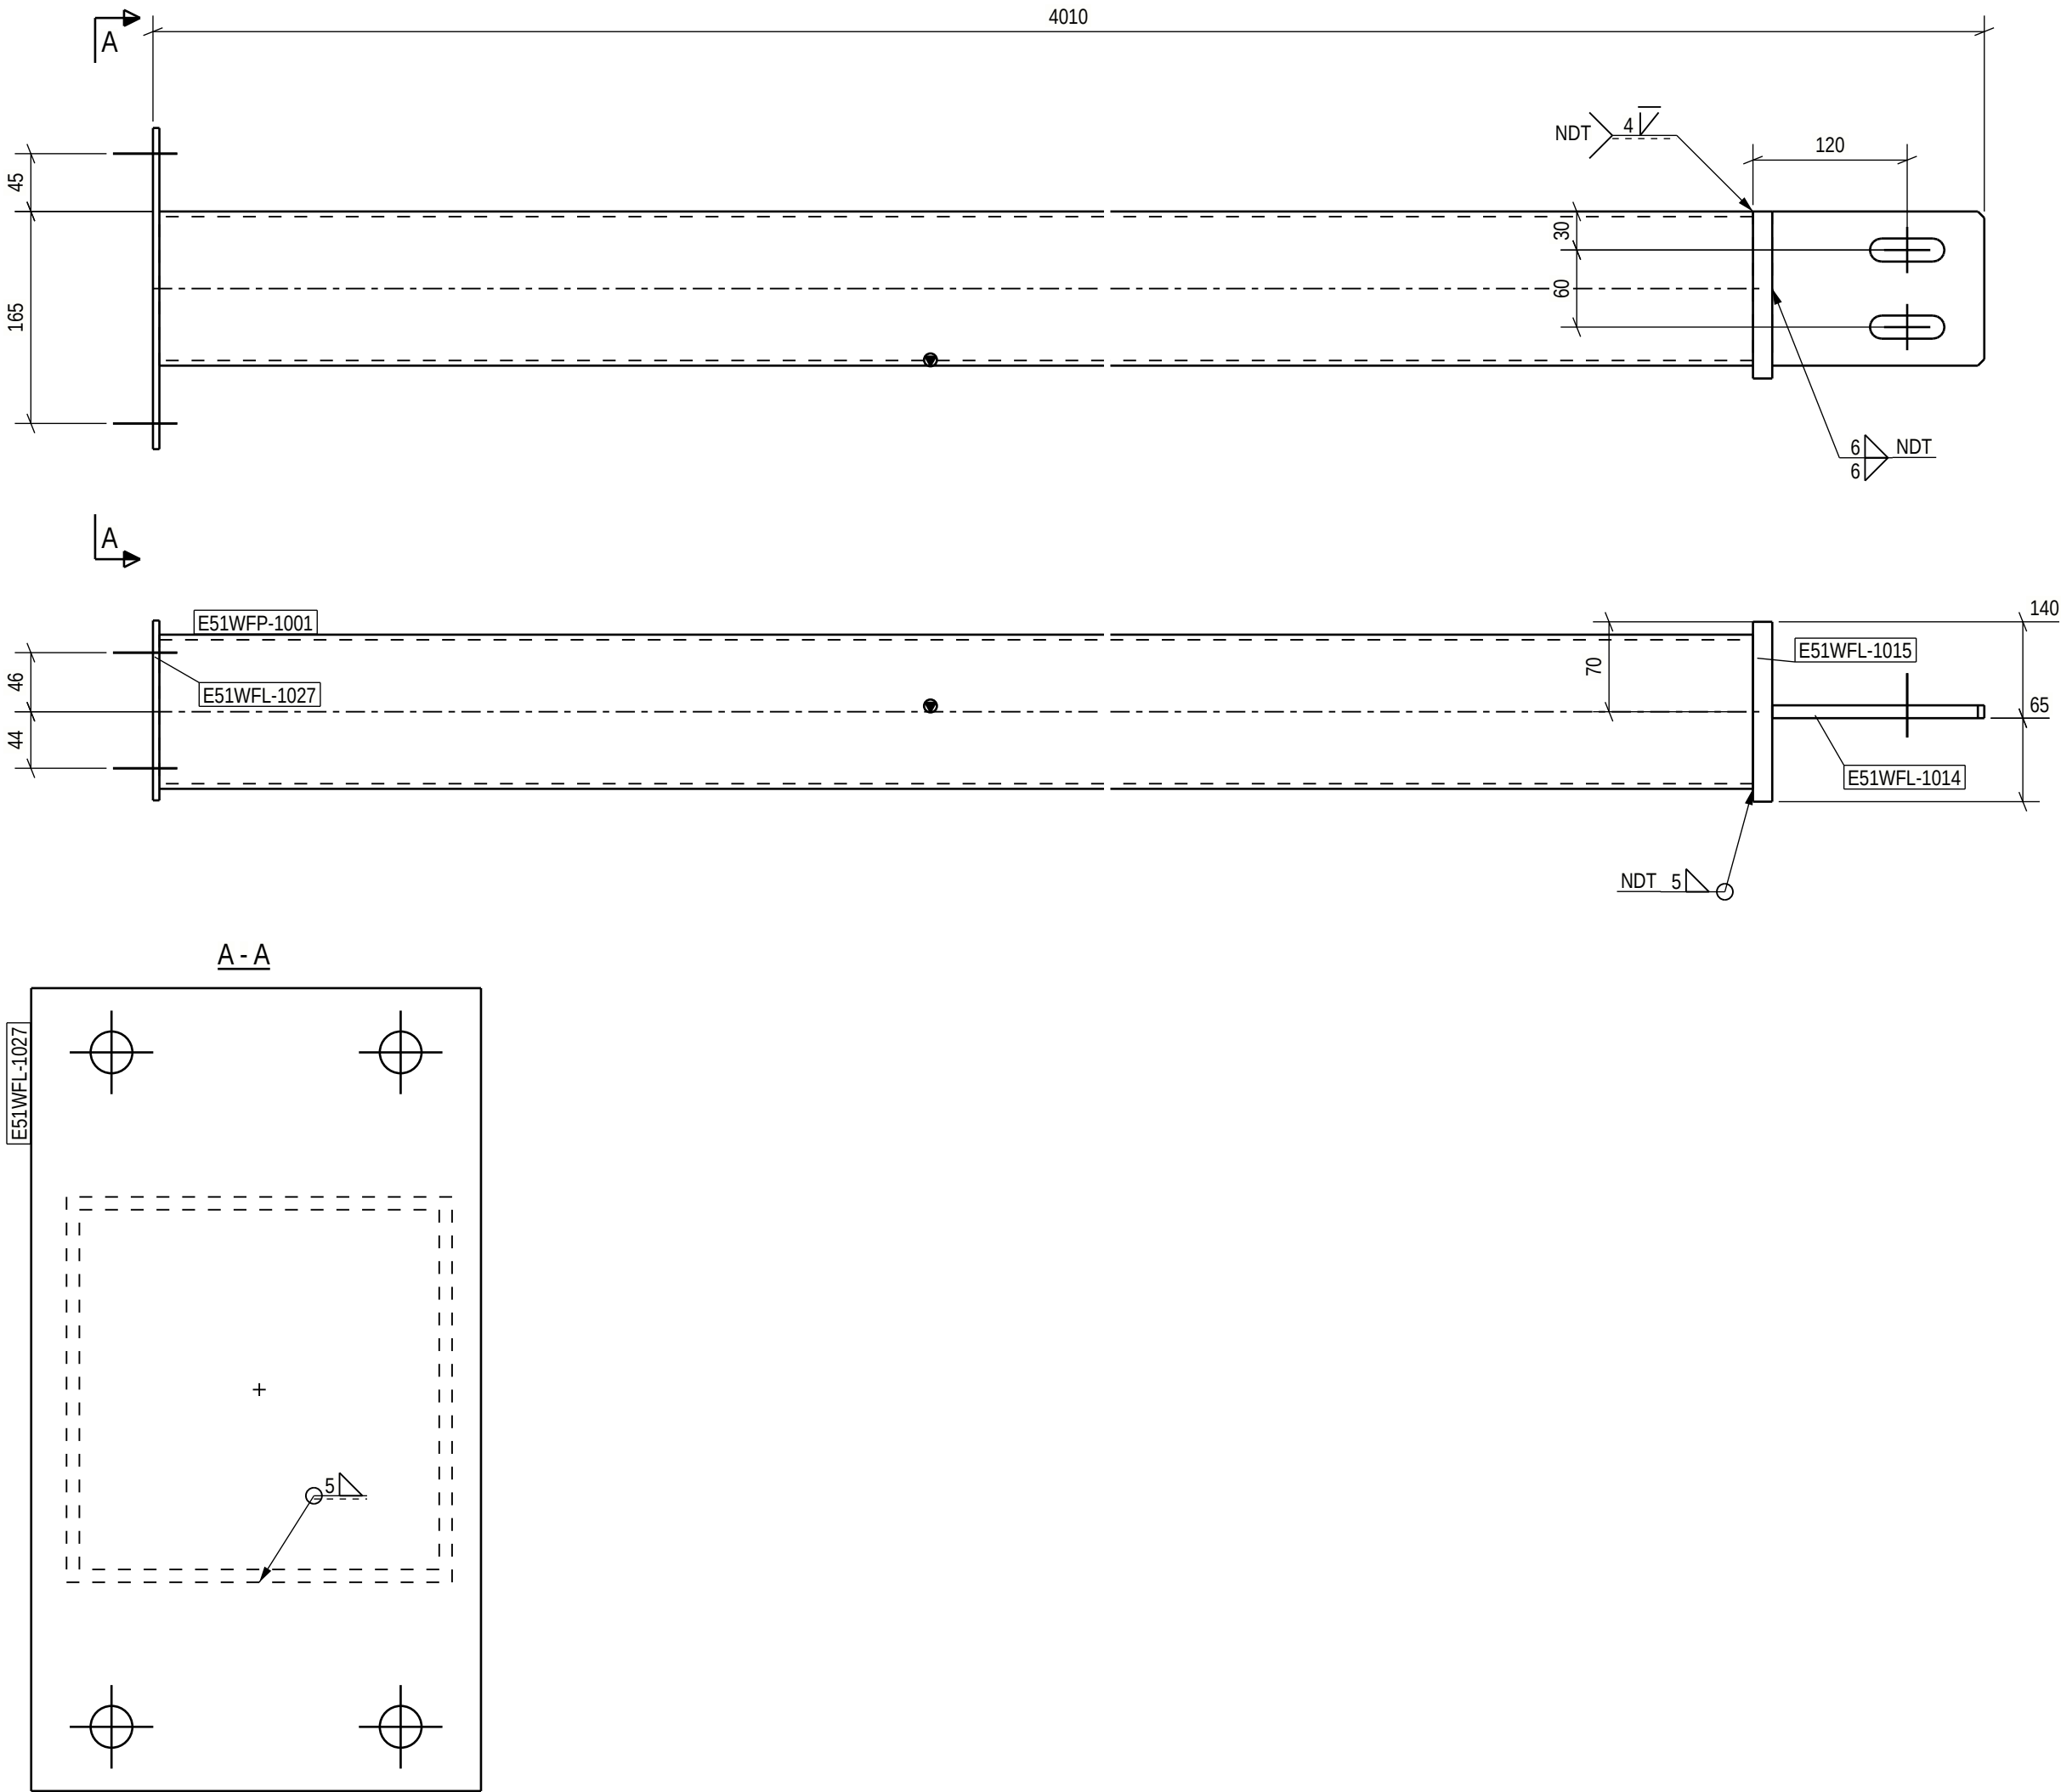

LIFTING LUG WELDING, WEIGHT < 1,5 t

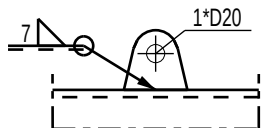

Technical fabrication requirements:		Execution class	
Requirements for fabrication, standard EN1090-2, table A.3 : EXC2		EXC2	
Execution Specification document nr 25019443-ICC250-0600-0660-000005		Fabrication tolerances EN 1090-2, Appendix B	
Surface preparation grade ISO8501-3, grade P2		Special fabrication tolerances Project specification/ shown on drwg.	
Surface treatment ISO12944-5		Weld inspection, requirements EN 1090-2, Table 24, U>0.5	
Additional requirements on surface treatment C3.07, EPPUR 240/2		Extent of NDT, fillet welds MT-EN1290, 20% of welds	
Shade RAL 7024 (Graphite Gray)		Extent of NDT, butt welds UT, EN-ISO17640, 20% of welds	
Welding of built up steel section Appendix 1 / Project spec.		Extent of NDT for splices not shown on drawing UT, EN-ISO17640, 100% of welds	
Welds, if not specified otherwise EN 9692-1, EN 9692-2		Requirements on bolting EN1090-2 Section 6.6.3	
		Weld class C, EN ISO 5817	
		Additional material inspection Shown on drwg.	

PROJECT NAME		DRAWING CONTENT	
Easpring New Materials Oy		ASSEMBLY DRAWING	
FAIR Phase 1		FRAME	
		E51WF-1010	

PROJECT NUMBER		DATE	
25019443		12.06.2026	
		ARCHIVING CODE	
		PAGE	
		DESIGN GROUP	
		STR	



DRAWN		DESIGNER	
Alexey Serous		Alexey Serous	
APPROVED		CHECKED	
Pertti Koivumaa		Jere Kallosalmi	
REVISION			

PUH. +358 207 393 000		E51WF-1010	
www.sweco.fi			


SWECO		Sustainable engineering and design	

SWECO RAKENNETEKNIikka OY		ILMALANPORTTI 2	
00240 HELSINKI			

For special tolerances of bolt hole location
see specification for steel structures
Approved For Construction

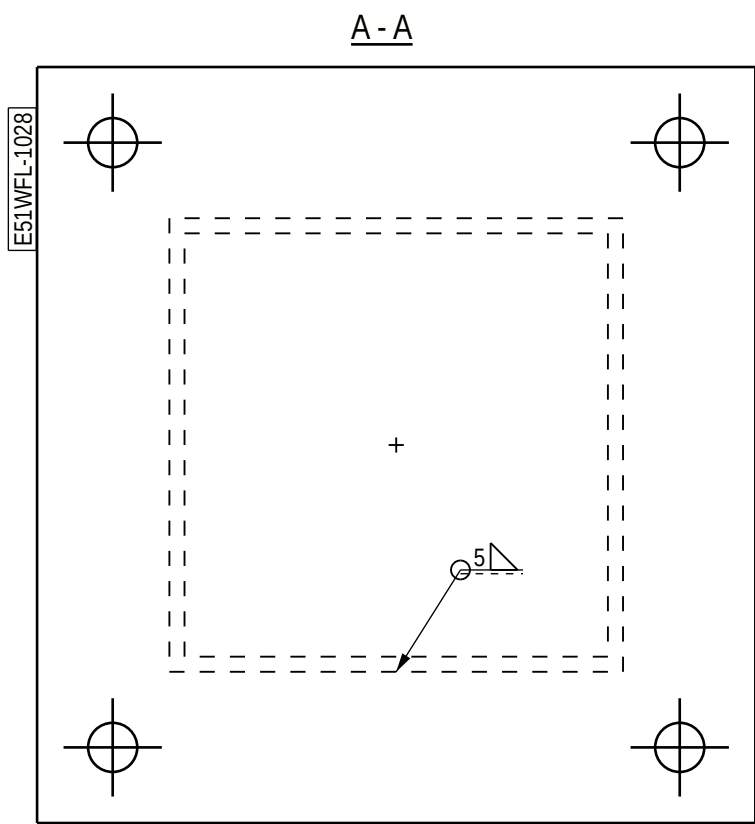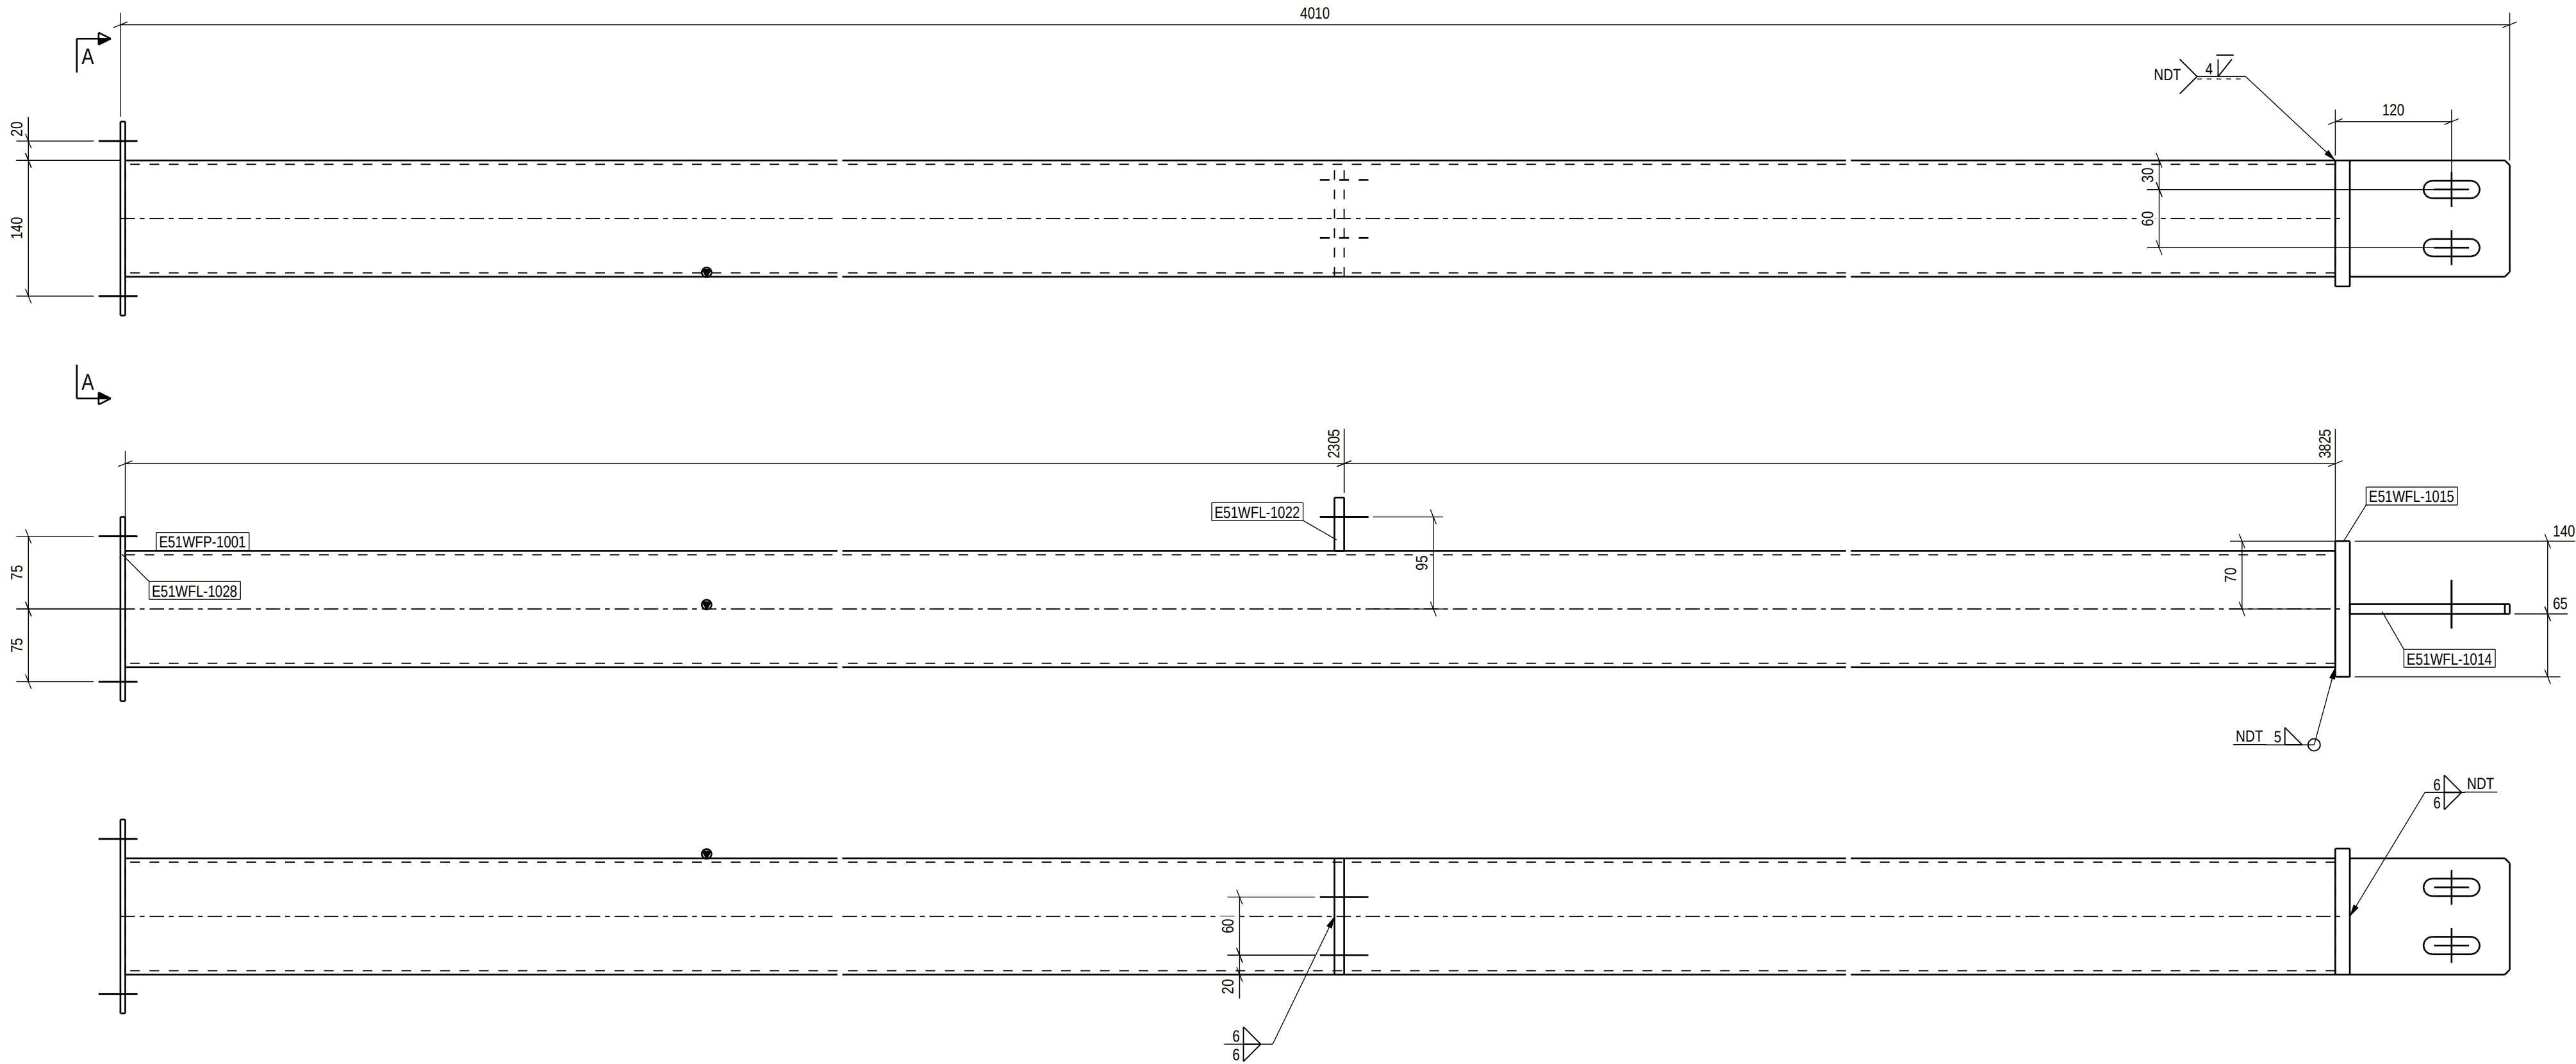

PART LIST FOR ASSEMBLY E51WF-1011, MANUFACTURING AMOUNT 1 PIECES						
PART	PROFILE	MATERIAL	LENGTH [mm]	AREA [m2]	WEIGHT [kg]	PCS
E51WFL-1014	PL10X120	S355J2+N	165	0.05	1.6	1
E51WFL-1015	PL15X130	S355J2+N	140	0.04	2.1	1
E51WFL-1022	PL10X55	S355J2+N	120	0.02	0.5	1
E51WFL-1028	PL5X190	S355J2+N	200	0.08	1.5	1
E51WFP-1001	CFRHS120X120X4	S355J2H	3825	1.78	54.5	1
TOTAL:				1.97	60.2	

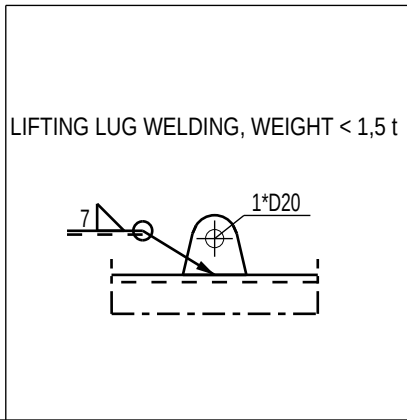

Technical fabrication requirements:		Execution class
EXC2		
Requirements for fabrication, standard	Fabrication tolerances	
EN1090-2, table A.3 : EXC2	EN 1090-2, Appendix B	
Execution Specification document nr	Special fabrication tolerances	
25019443-ICC250-0600-0660-000005	Project specification/ shown on drwg.	
Surface preparation grade	Weld inspection, requirements	
ISO8501-3, grade P2	EN 1090-2,Table 24, U>0.5	
Surface treatment	Extent of NDT, fillet welds	
ISO12944-5	MT-EN1290,20% of welds	
Additional requirements on surface treatment	Extent of NDT, butt welds	
C3.07, EPPUR 240/2	UT, EN-ISO17640, 20% of welds	
Shade	Extent of NDT for splices not shown on drawing	
RAL 7024 (Graphite Gray)	UT, EN-ISO17640, 100%of welds	
Welding of built up steel section	Requirements on holing	
Appendix 1 / Project spec.	EN1090-2 Section 6.6.3	
Welds, if not specified otherwise	Weld class	Additional material inspection
EN 9692-1, EN 9692-2	C, EN ISO 5817	Shown on drwg.

For special tolerances of bolt hole location
see specification for steel structures
Approved For Construction


PROJECT NAME		DRAWING CONTENT	
Easpring New Materials Oy		ASSEMBLY DRAWING	
FAIR Phase 1		FRAME	
		E51WF-1011	
		DATE	ARCHIVING CODE
		12.06.2026	
		PAGE	DESIGN GROUP
			STR
		DRAWN	CHECKED
		Alexey Serous	Pertti Koivumaa
		DESIGNER	REVISION
		Alexey Serous	Jere Kallosalmi
		PROJECT NUMBER	
		25019443	
		DWG. NO.	
		E51WF-1011	



SWECO RAKENNETEKNIikka OY
ILMALANPORTTI 2
00240 HELSINKI
PUH. +358 207 393 000
www.sweco.fi

PART LIST FOR ASSEMBLY E51WF-1012, MANUFACTURING AMOUNT 1 PIECES						
PART	PROFILE	MATERIAL	LENGTH [mm]	AREA [m2]	WEIGHT [kg]	PCS
E51WFL-1019	PL10X100	S355J2+N	150	0.07	1.2	2
E51WFL-1023	PL10X55	S355J2+N	100	0.03	0.4	2
E51WFL-1024	PL15X110	S355J2+N	120	0.07	1.6	2
E51WFL-1056	PL16X162	S355J2	150	0.05	2.6	1
E51WFP-1004	CFRHS100X100X4	S355J2H	3611	1.40	42.4	1
TOTAL:				1.61	51.2	

LIFTING LUG WELDING, WEIGHT < 1,5 t

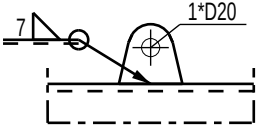


Technical fabrication requirements:		Execution class
EXC2		
Requirements for fabrication, standard	Fabrication tolerances	
EN1090-2, table A.3 : EXC2	EN 1090-2, Appendix B	
Execution Specification document nr	Special fabrication tolerances	
25019443-ICC250-0600-0660-000005	Project specification/ shown on drwg.	
Surface preparation grade	Weld inspection, requirements	
ISO8501-3, grade P2	EN 1090-2,Table 24, U>0.5	
Surface treatment	Extent of NDT, fillet welds	
ISO12944-5	MT-EN1290,20% of welds	
Additional requirements on surface treatment	Extent of NDT, butt welds	
C3.07, EPPUR 240/2	UT, EN-ISO17640, 20% of welds	
Shade	Extent of NDT for splices not shown on drawing	
RAL 7024 (Graphite Gray)	UT, EN-ISO17640, 100%of welds	
Welding of built up steel section	Requirements on holing	
Appendix 1 / Project spec.	EN1090-2 Section 6.6.3	
Welds, if not specified otherwise	Weld class	Additional material inspection
EN 9692-1, EN 9692-2	C, EN ISO 5817	Shown on drwg.

For special tolerances of bolt hole location
see specification for steel structures
Approved For Construction

PROJECT NAME		DRAWING CONTENT			
Easpring New Materials Oy		ASSEMBLY DRAWING			
FAIR Phase 1		FRAME			
		E51WF-1012			
		DATE	ARCHIVING CODE	PAGE	DESIGN GROUP
		12.06.2026			STR
		DRAWN	DESIGNER	APPROVED	CHECKED
		Alexey Serous	Alexey Serous	Pertti Koivumaa	Jere Kallosalmi
		PROJECT NUMBER	DWG. NO.	REVISION	
		25019443	E51WF-1012		




SWECO RAKENNETEKNIikka OY
ILMALANPORTTI 2
00240 HELSINKI
PUH. +358 207 393 000
www.sweco.fi

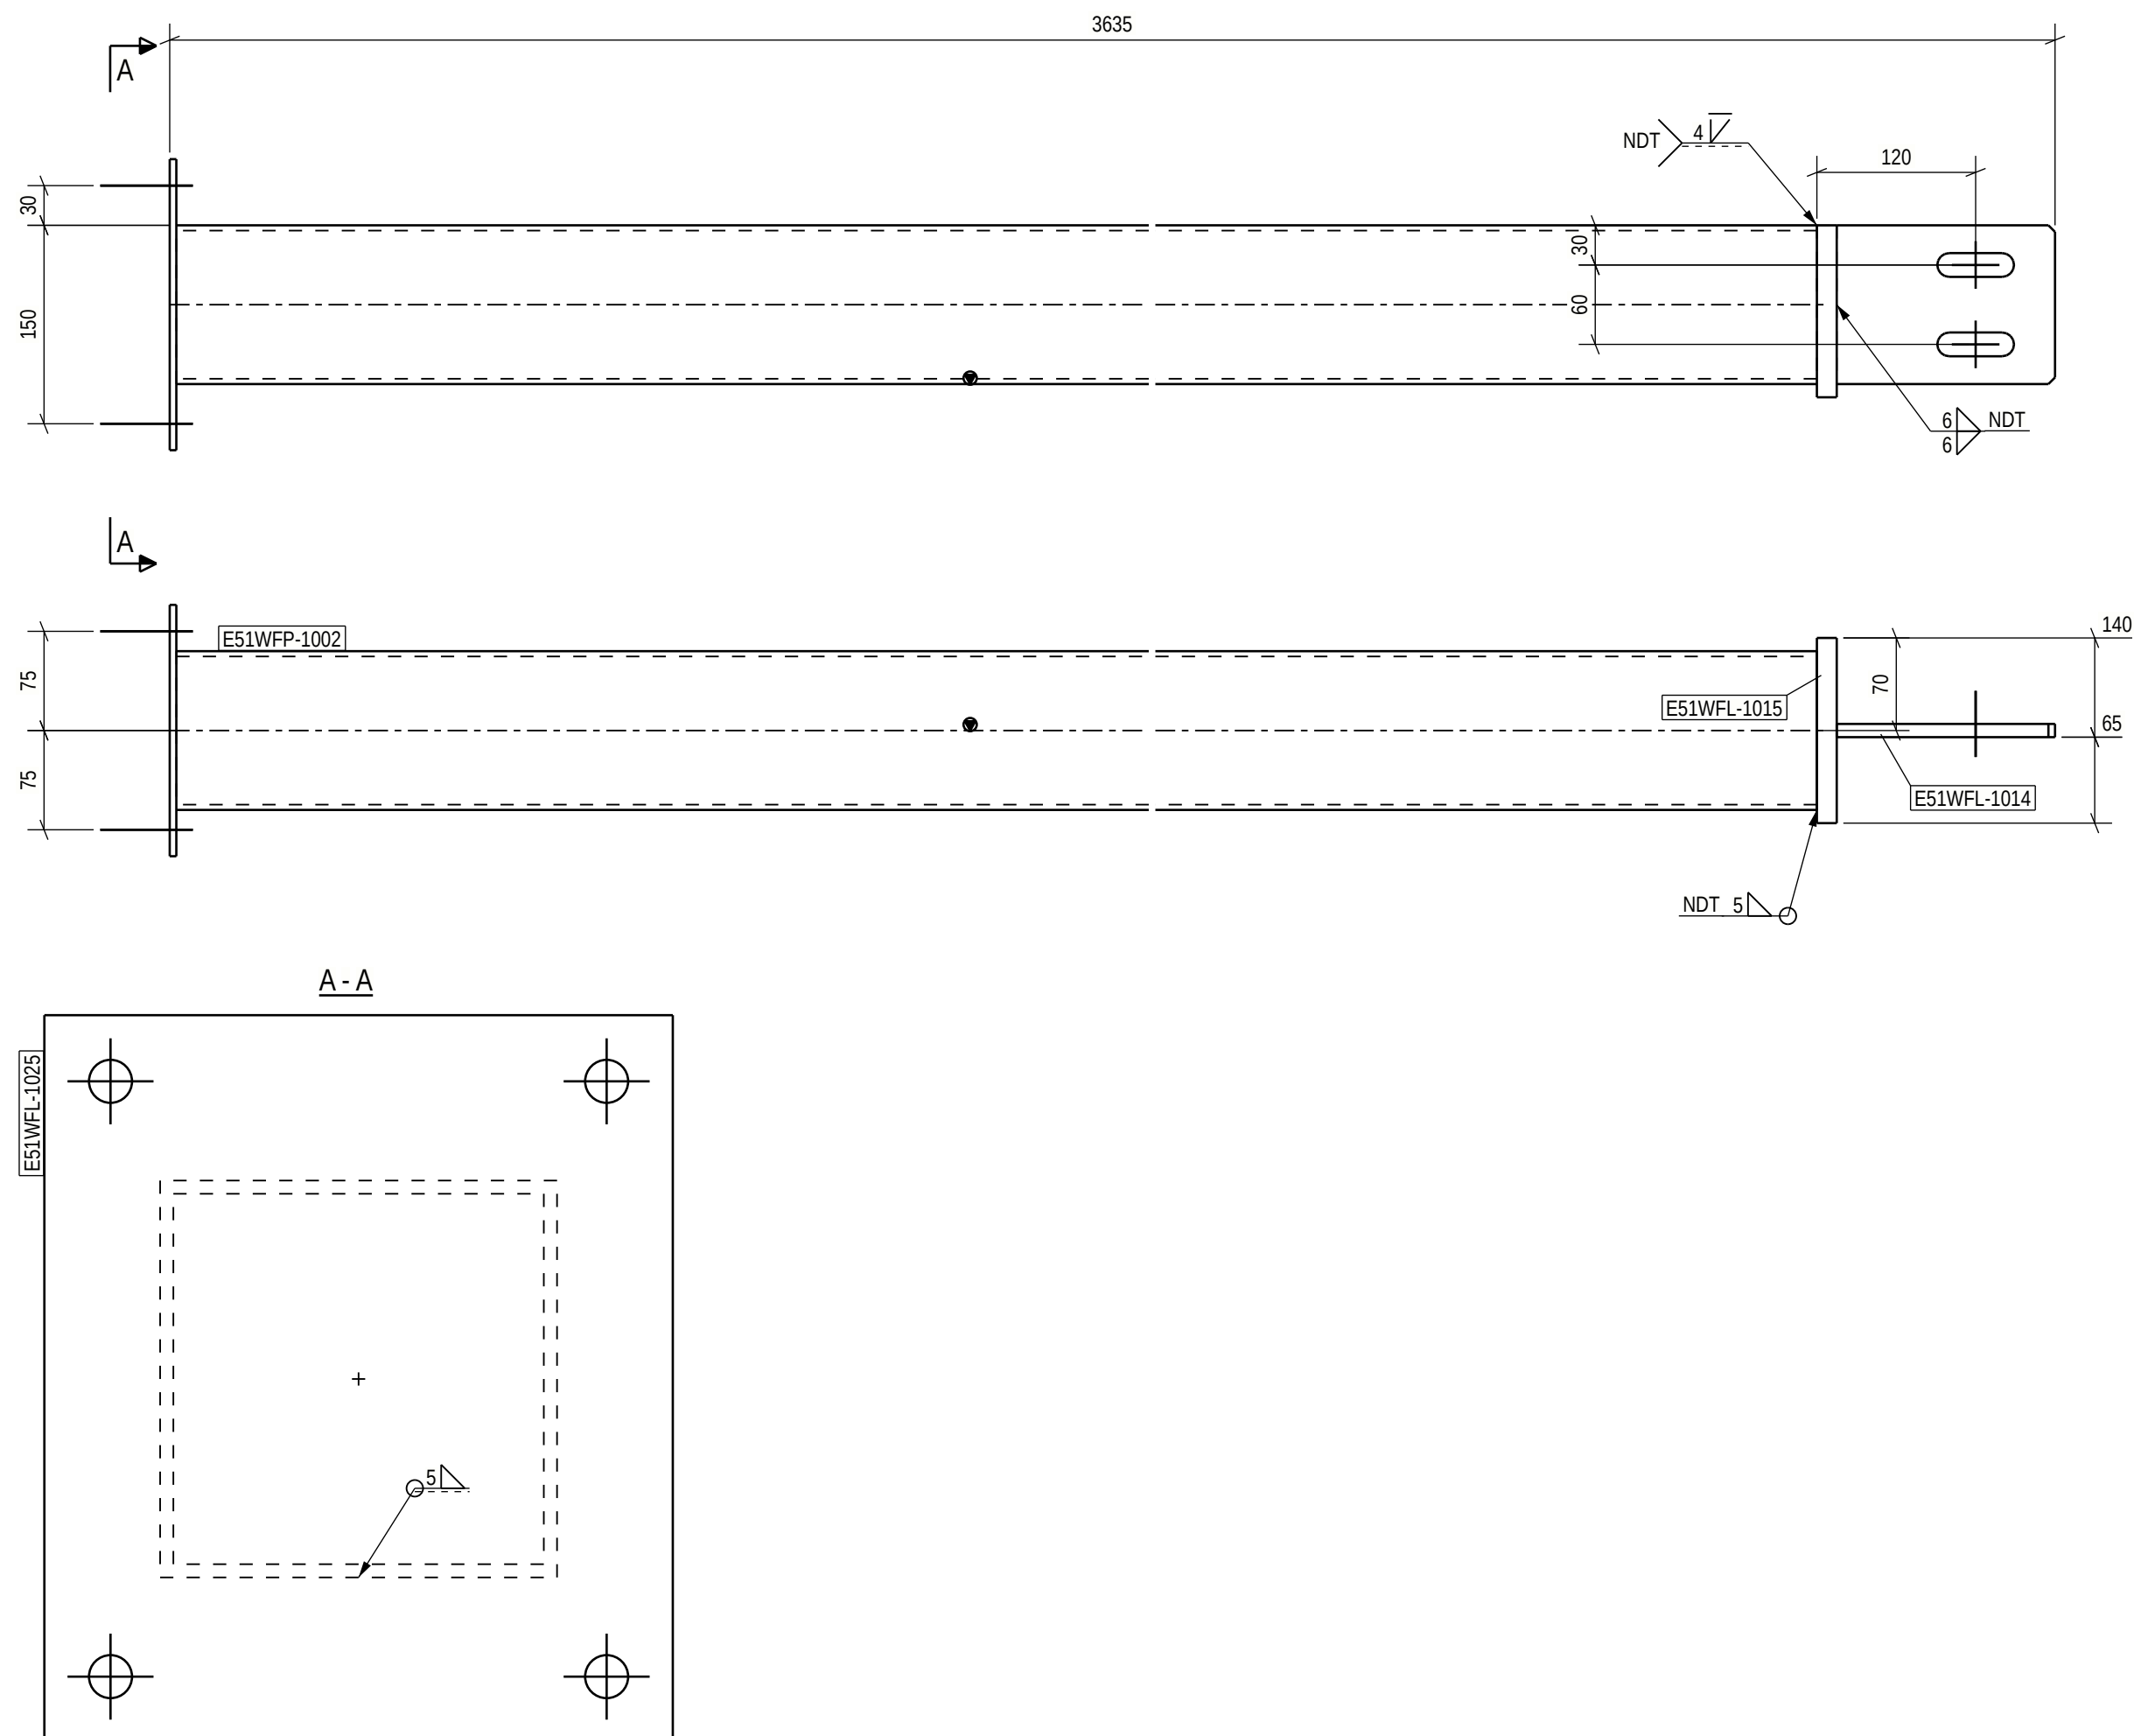


PART LIST FOR ASSEMBLY E51WF-1013, MANUFACTURING AMOUNT 1 PIECES						
PART	PROFILE	MATERIAL	LENGTH [mm]	AREA [m2]	WEIGHT [kg]	PCS
E51WFL-1014	PL10X120	S355J2+N	165	0.05	1.6	1
E51WFL-1015	PL15X130	S355J2+N	140	0.04	2.1	1
E51WFL-1025	PL5X190	S355J2+N	220	0.09	1.6	1
E51WFP-1002	CFRHS120X120X4	S355J2H	3450	1.61	49.1	1
TOTAL:				1.79	54.5	

LIFTING LUG WELDING, WEIGHT < 1,5 t


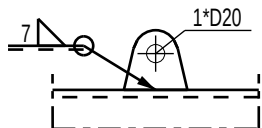


Technical fabrication requirements:		Execution class EXC2
Requirements for fabrication, standard EN1090-2, table A.3 : EXC2 Execution Specification document nr 25019443-ICC2500-0660-000005 Surface preparation grade ISO8501-3, grade P2 Surface treatment ISO12944-5 Additional requirements on surface treatment C3.07, EPPUR 240/2 Shade RAL 7024 (Graphite Gray) Welding of built up steel section Appendix 1 / Project spec. Weeds, if not specified otherwise EN 9692-1, EN 9692-2	Fabrication tolerances EN 1090-2, Appendix B Special fabrication tolerances Project specification/ shown on dwg. Weld inspection, requirements EN 1090-2, Table 24, U>0.5 Extent of NDT, fillet welds MT-EN1290, 20% of welds Extent of NDT, butt welds UT, EN-ISO17640, 20% of welds Extent of NDT for splices not shown on drawing UT, EN-ISO17640, 100%of welds Requirements on holding EN1090-2 Section 6.6.3 Weld class C, EN ISO 5817	Additional material inspection Shown on dwg.

For special tolerances of bolt hole location
see specification for steel structures

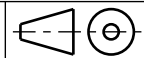


SWECO Sustainable engineering and design	SWECO RAKENNETEKNIikka OY ILMALANPORTTI 2 00240 HELSINKI PUH. +358 207 393 000 www.sweco.fi	DATE	ARCHIVING CODE	PAGE	DESIGN GROUP
		12.06.2026			STR
		DRAWN	DESIGNER	APPROVED	CHECKED
		Alexey Serous	Alexey Serous	Pertti Koivumäenaho	Jere Kalliosalmi
		PROJECT NUMBER	DWG. NO.	REVISION	
25019443	E51WF-1013				

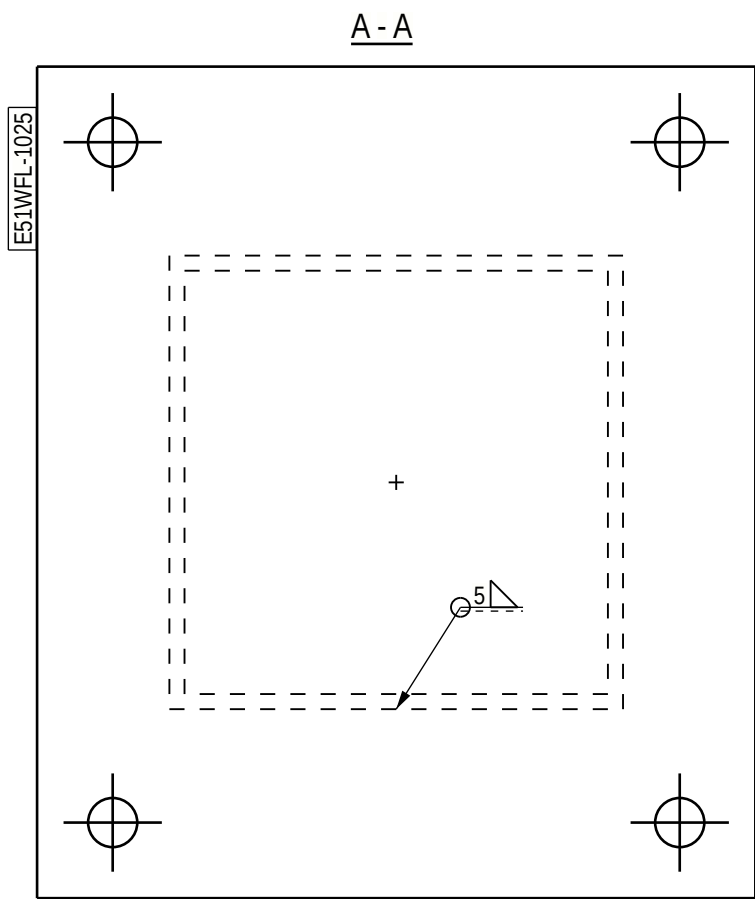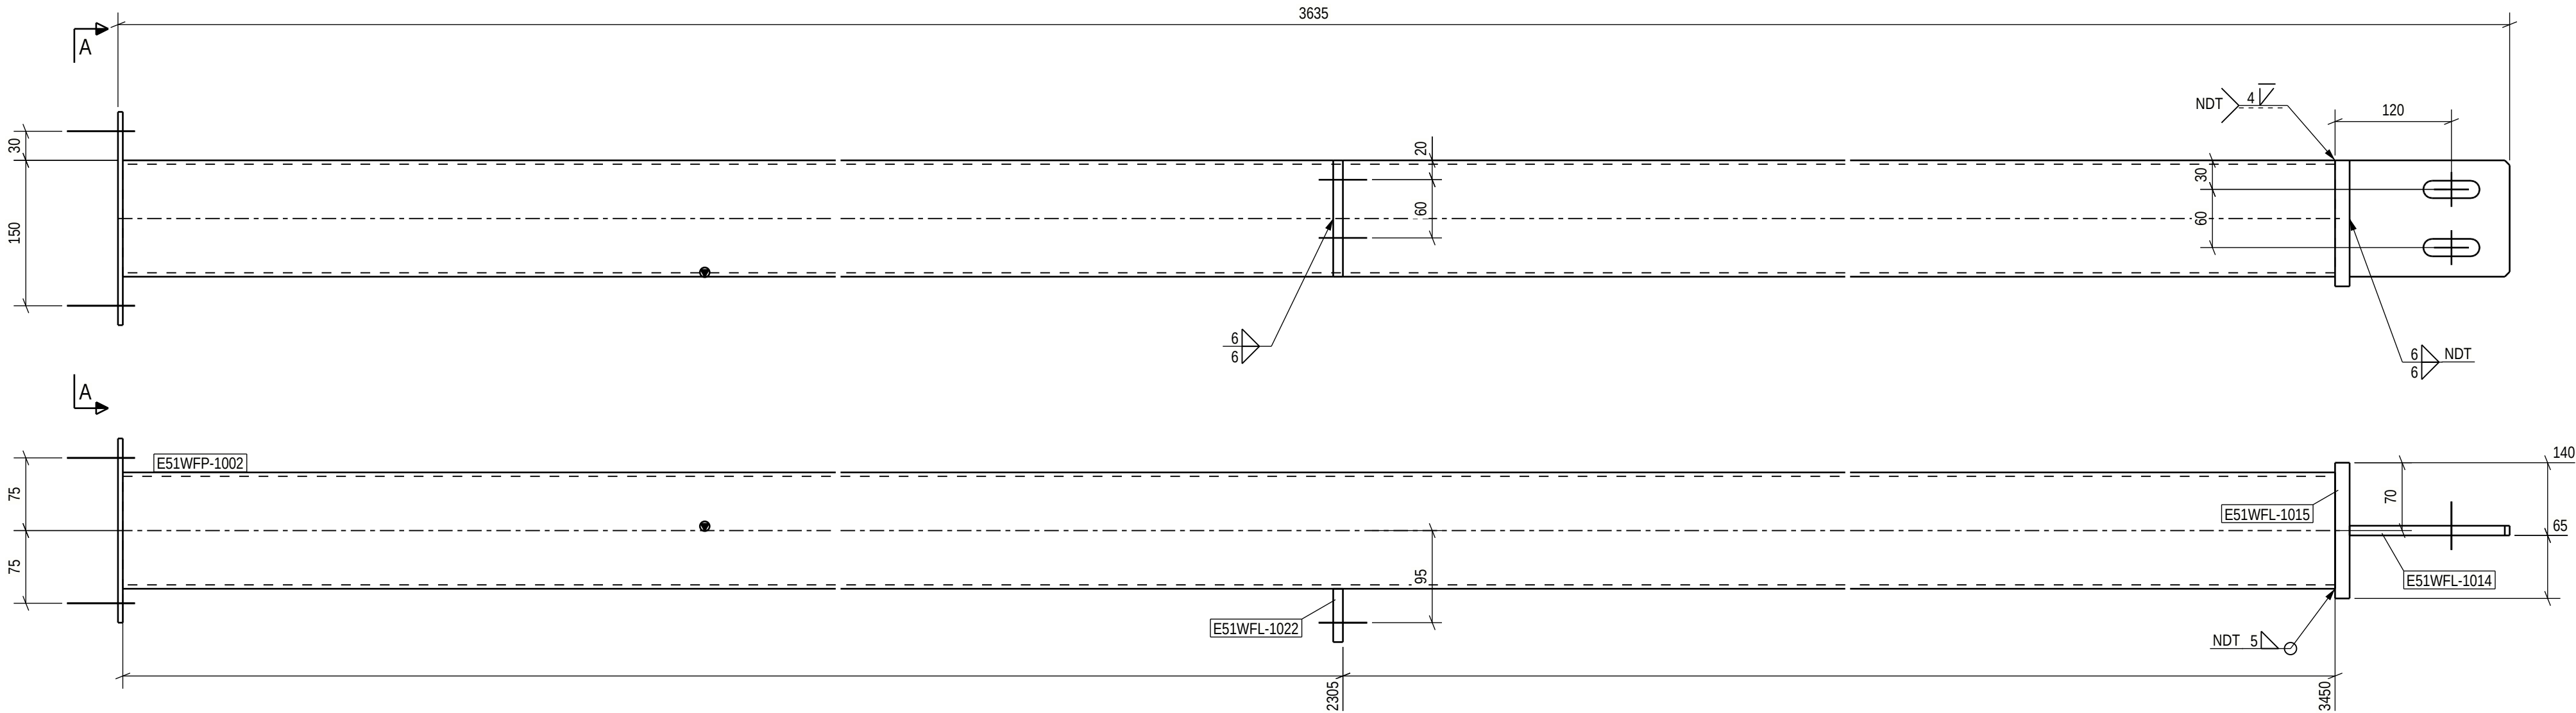

PART LIST FOR ASSEMBLY E51WF-1014, MANUFACTURING AMOUNT 1 PIECES						
PART	PROFILE	MATERIAL	LENGTH [mm]	AREA [m2]	WEIGHT [kg]	PCS
E51WFL-1014	PL10X120	S355J2+N	165	0.05	1.6	1
E51WFL-1015	PL15X130	S355J2+N	140	0.04	2.1	1
E51WFL-1022	PL10X55	S355J2+N	120	0.02	0.5	1
E51WFL-1025	PL5X190	S355J2+N	220	0.09	1.6	1
E51WFP-1002	CFRHS120X120X4	S355J2H	3450	1.61	49.1	1
TOTAL:			1.80	55.0		


LIFTING LUG WELDING, WEIGHT < 1,5 t

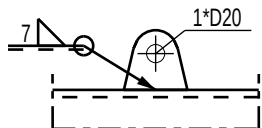

Technical fabrication requirements:		Execution class
Requirements for fabrication, standard EN1090-2, table A.3 : EXC2		EXC2
Execution Specification document nr 25019443-ICC250-0600-0660-000005	Fabrication tolerances EN 1090-2, Appendix B	
Surface preparation grade ISO8501-3, grade P2	Special fabrication tolerances Project specification/ shown on drwg.	
Surface treatment ISO12944-5	Weld inspection, requirements EN 1090-2, Table 24, U>0.5	
Additional requirements on surface treatment C3.07, EPPUR 240/2	Extent of NDT, fillet welds MT-EN1290, 20% of welds	
Shade RAL 7024 (Graphite Gray)	Extent of NDT, butt welds UT, EN-ISO17640, 20% of welds	
Welding of built up steel section Appendix 1 / Project spec.	Extent of NDT for splices not shown on drawing UT, EN-ISO17640, 100% of welds	
Welds, if not specified otherwise EN 9692-1, EN 9692-2	Requirements on holing EN1090-2 Section 6.6.3	
	Weld class C, EN ISO 5817	Additional material inspection Shown on drwg.

For special tolerances of bolt hole location
see specification for steel structures
Approved For Construction

PROJECT NAME
Easpring New Materials Oy
FAIR Phase 1


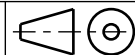


DRAWING CONTENT
ASSEMBLY DRAWING
FRAME
E51WF-1014

SWECO
Sustainable engineering and design


SWECO RAKENNETEKNIikka OY
ILMALANPORTTI 2
00240 HELSINKI
PUH. +358 207 393 000
www.sweco.fi

DATE	ARCHIVING CODE	PAGE	DESIGN GROUP
12.06.2026			STR
DRAWN	DESIGNER	APPROVED	CHECKED
Alexey Serous	Alexey Serous	Pertti Koivumaa	Jere Kallosalmi
PROJECT NUMBER	DWG. NO.	REVISION	
25019443	E51WF-1014		

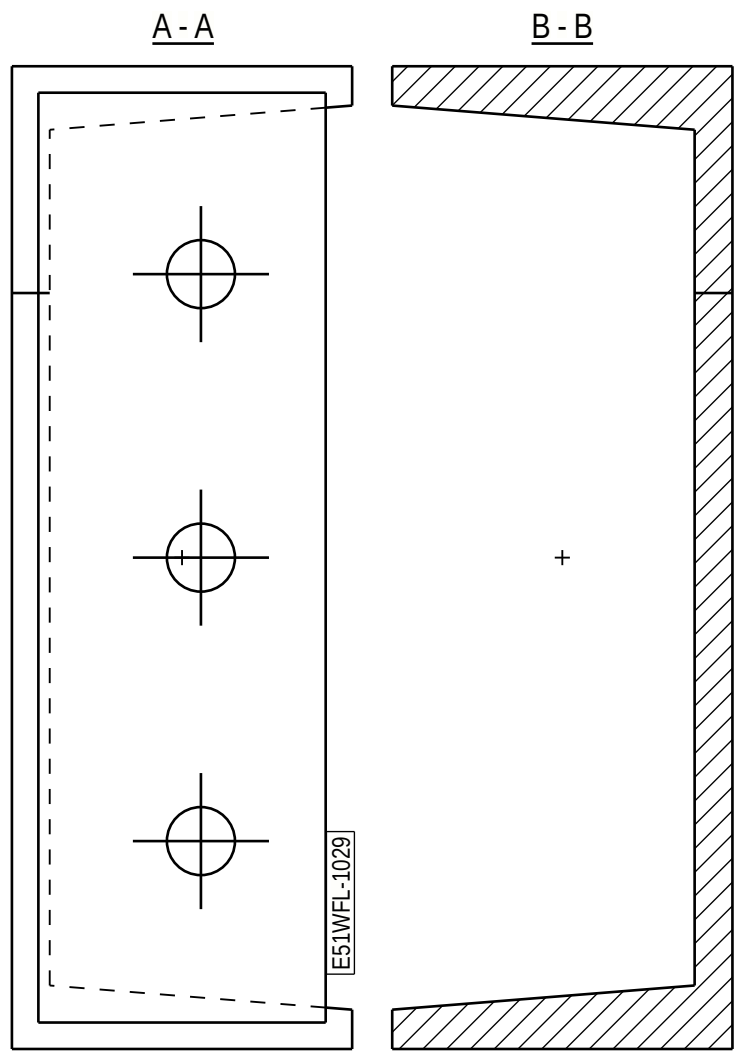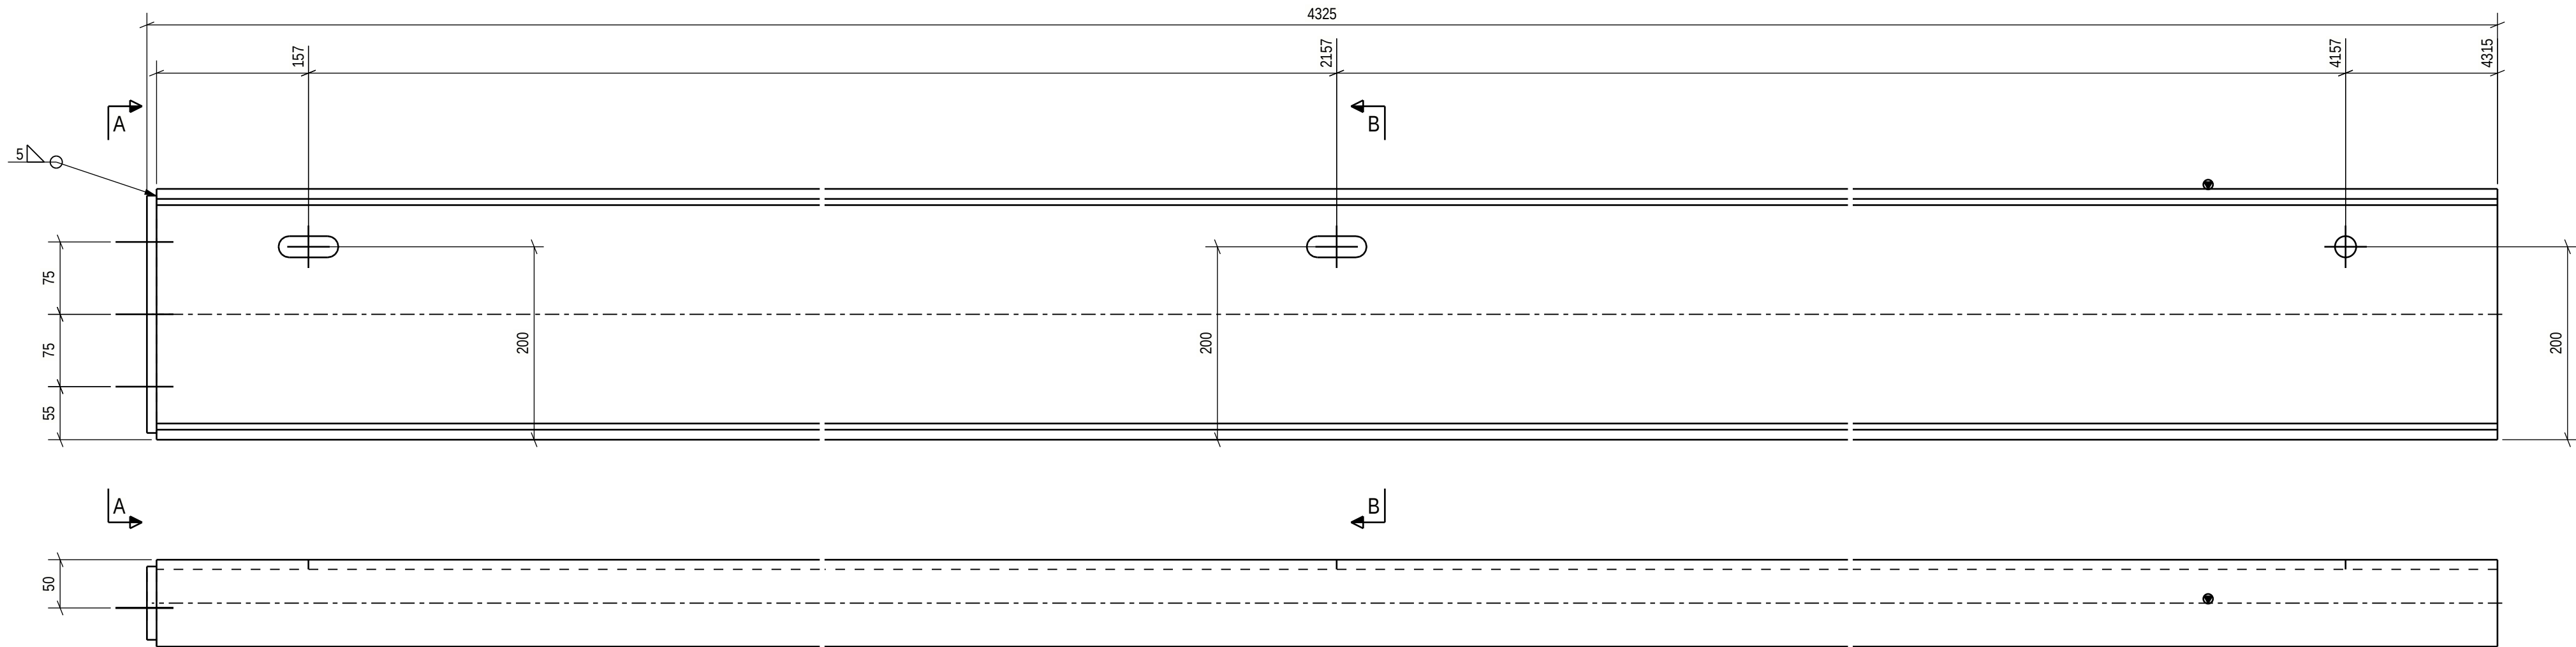

PART LIST FOR ASSEMBLY E51WF-1030, MANUFACTURING AMOUNT 1 PIECES						
PART	PROFILE	MATERIAL	LENGTH [mm]	AREA [m2]	WEIGHT [kg]	PCS
E51WFL-1029	PL10X76	S355J2+N	246	0.04	1.5	1
E51WFP-1033	UNP260	S355J2	4315	3.60	163.6	1
TOTAL:			3.64	165.1		

LIFTING LUG WELDING, WEIGHT < 1,5 t

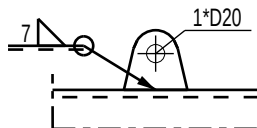

Technical fabrication requirements:

Execution class

EXC2

Approved For Construction

Requirements for fabrication, standard
EN1090-2, table A.3 : EXC2
Execution Specification document nr
25019443-ICC250-0600-0660-000005

Fabrication tolerances
EN 1090-2, Appendix B
Special fabrication tolerances
Project specification/ shown on drwg.

Surface preparation grade
ISO8501-3, grade P2
Surface treatment
ISO12944-5
Additional requirements on surface treatment
C3.07, EPPUR 240/2
Shade
RAL 7024 (Graphite Gray)
Welding of built up steel section
Appendix 1 / Project spec.
Welds, if not specified otherwise
EN 9692-1, EN 9692-2

Weld inspection, requirements
EN 1090-2, Table 24, U>0.5
Extent of NDT, fillet welds
MT-EN1290, 20% of welds
Extent of NDT, butt welds
UT, EN-ISO17640, 20% of welds
UT, EN-ISO17640, 100% of welds
Requirements on holing
EN1090-2 Section 6.6.3
Weld class
C, EN ISO 5817
Additional material inspection
Shown on drwg.

PROJECT NAME
Easpring New Materials Oy
FAIR Phase 1

SWECO




Sustainable engineering and design

SWECO RAKENNETEKNIikka OY
ILMALANPORTTI 2
00240 HELSINKI
PUH. +358 207 393 000
www.sweco.fi


DRAWING CONTENT
ASSEMBLY DRAWING
FRAME
E51WF-1030

DATE 12.06.2026	ARCHIVING CODE	PAGE	DESIGN GROUP STR
DRAWN Alexey Serous	DESIGNER Alexey Serous	APPROVED Pertti Koivumaa	CHECKED Jere Kallosalmi
PROJECT NUMBER 25019443	DWG. NO.	REVISION	

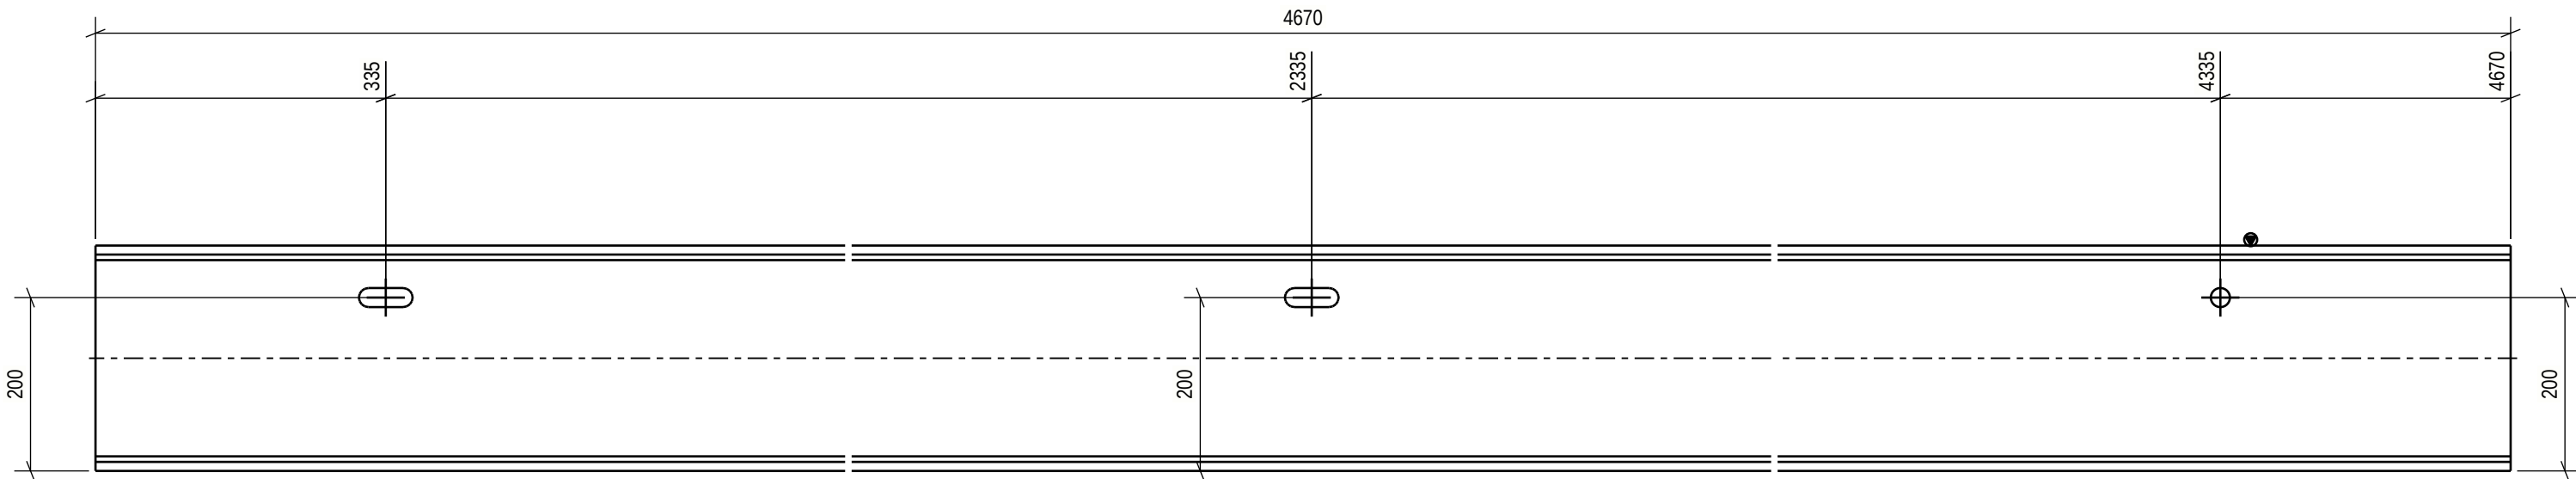

PART LIST FOR ASSEMBLY E51WF-1031, MANUFACTURING AMOUNT 1 PIECES						
PART	PROFILE	MATERIAL	LENGTH [mm]	AREA [m2]	WEIGHT [kg]	PCS
E51WFP-1024	UNP260	S355J2	4670	3.89	177.1	1
TOTAL:				3.89	177.1	

LIFTING LUG WELDING, WEIGHT < 1,5 t

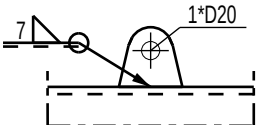


Technical fabrication requirements:		Execution class
Requirements for fabrication, standard	Fabrication tolerances	EXC2
EN1090-2, table A.3 : EXC2	EN 1090-2, Appendix B	
Execution Specification document nr	Special fabrication tolerances	
25019443-ICC250-0600-0660-000005	Project specification/ shown on drwg.	
Surface preparation grade	Weld inspection, requirements	
ISO8501-3, grade P2	EN 1090-2,Table 24, U>0.5	
Surface treatment	Extent of NDT, fillet welds	
ISO12944-5	MT-EN1290,20% of welds	
Additional requirements on surface treatment	Extent of NDT, butt welds	
C3.07, EPPUR 240/2	UT, EN-ISO17640, 20% of welds	
Shade	Extent of NDT for splices not shown on drawing	C, EN ISO 5817
RAL 7024 (Graphite Gray)	UT, EN-ISO17640, 100%of welds	
Welding of built up steel section	Requirements on holing	
Appendix 1 / Project spec.	EN1090-2 Section 6.6.3	
Welds, if not specified otherwise	Additional material inspection	
EN 9692-1, EN 9692-2	Shown on drwg.	

Approved For Construction

Easpring New Materials Oy
FAIR Phase 1




SWECO RAKENNETEKNIikka OY
ILMALANPORTTI 2
00240 HELSINKI
PUH. +358 207 393 000
www.sweco.fi

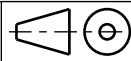


DRAWING CONTENT
ASSEMBLY DRAWING
FRAME
E51WF-1031

DATE	ARCHIVING CODE	PAGE	DESIGN GROUP
12.06.2026			STR
DRAWN	DESIGNER	APPROVED	CHECKED
Alexey Serous	Alexey Serous	Pertti Koivumaaanaho	Jere Kallosalmi
PROJECT NUMBER	DWG. NO.	REVISION	
25019443	E51WF-1031		

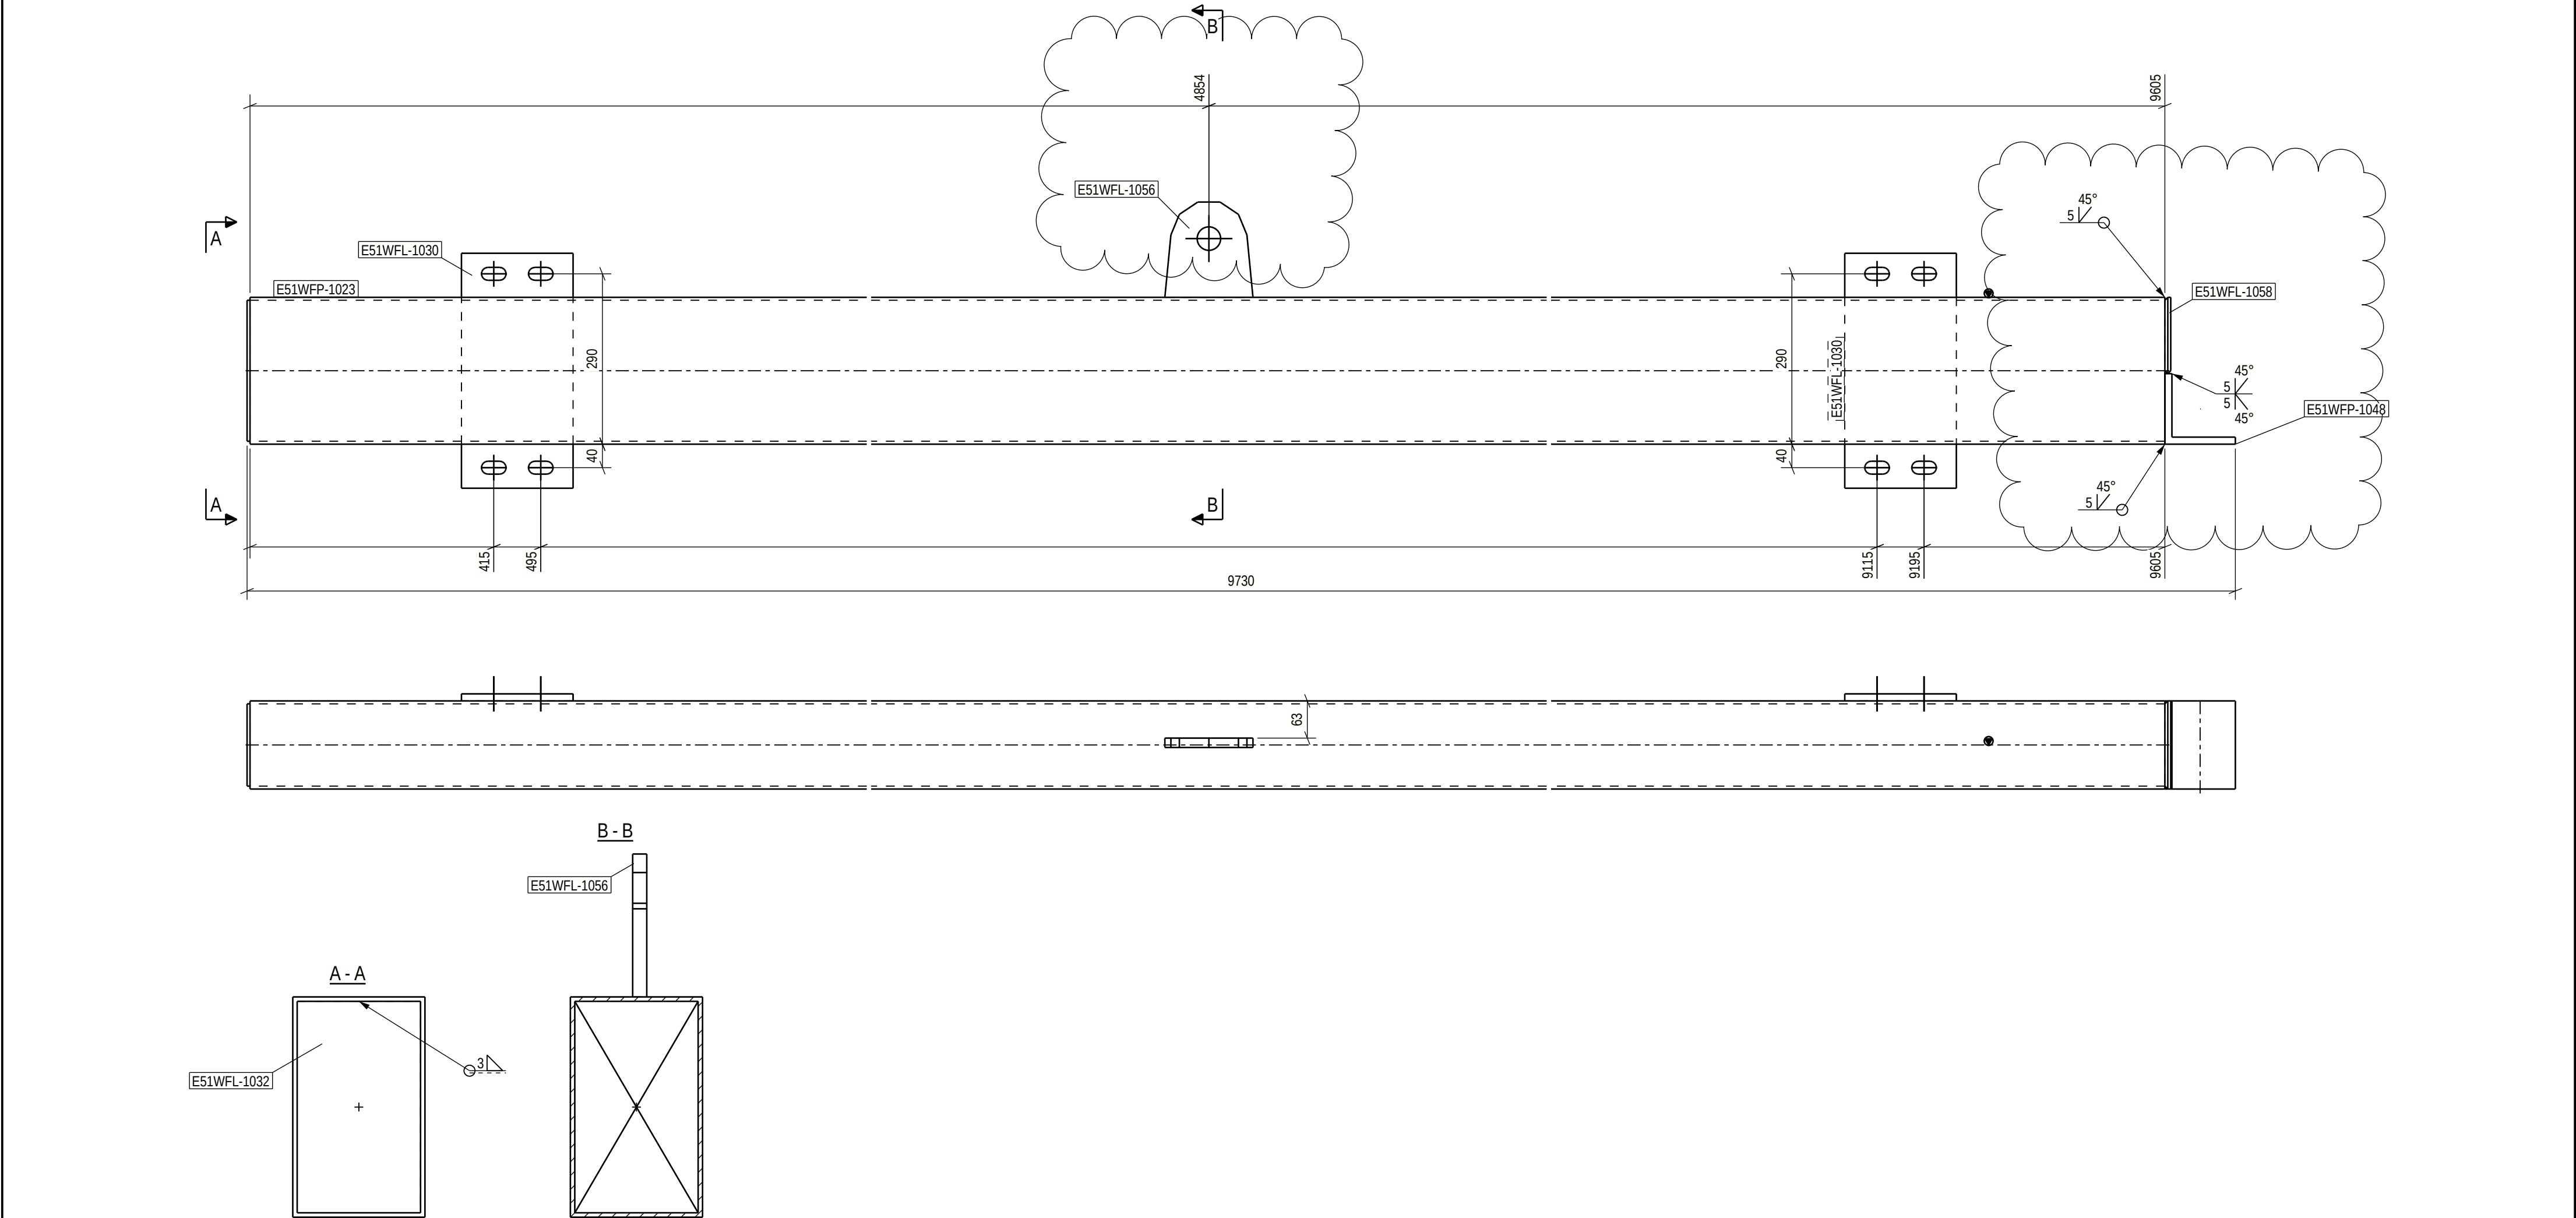

PART LIST FOR ASSEMBLY E51WF-1032, MANUFACTURING AMOUNT 1 PIECES						
PART	PROFILE	MATERIAL	LENGTH [mm]	AREA [m2]	WEIGHT [kg]	PCS
E51WFL-1030	PL12X190	S355J2+N	400	0.33	7.2	2
E51WFL-1032	PL5X140	S355J2+N	240	0.07	1.3	1
E51WFL-1056	PL16X162	S355J2	150	0.05	2.6	1
E51WFL-1058	PL10X150	S355J2+N	130	0.04	1.5	1
E51WFP-1023	CFRHS250X150X5	S355J2H	9605	7.52	289.2	1
E51WFP-1048	L120*12	S355J2	150	0.07	3.2	1
TOTAL:				8.09	312.1	

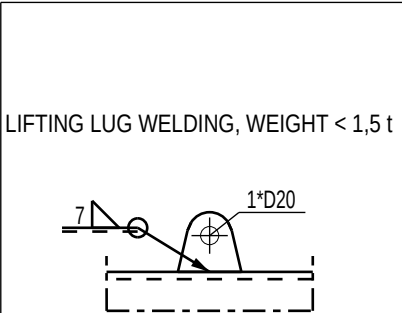


Technical fabrication requirements:		Execution class
EXC2		
Requirements for fabrication, standard	Fabrication tolerances	
EN1090-2, table A.3 : EXC2	EN 1090-2, Appendix B	
Execution Specification document nr	Special fabrication tolerances	
25019443-ICC250-0600-0660-000005	Project specification/ shown on drwg.	
Surface preparation grade	Weld inspection, requirements	
ISO8501-3, grade P2	EN 1090-2,Table 24, U>0.5	
Surface treatment	Extent of NDT, fillet welds	
ISO12944-5	MT-EN1290,20% of welds	
Additional requirements on surface treatment	Extent of NDT, butt welds	
C3.07, EPPUR 240/2	UT, EN-ISO17640, 20% of welds	
Shade	Extent of NDT for splices not shown on drawing	
RAL 7024 (Graphite Gray)	UT, EN-ISO17640, 100% of welds	
Welding of built up steel section	Requirements on holing	
Appendix 1 / Project spec.	EN1090-2 Section 6.6.3	
Welds, if not specified otherwise	Weld class	Additional material inspection
EN 9692-1, EN 9692-2	C, EN ISO 5817	Shown on drwg.

Approved For Construction

01	End updated	FIALES	29.06.2026	FIKJER
REV.	REVISION	CHANGED BY	DATE	CHECKED BY
PROJECT NAME		DRAWING CONTENT		
Easpring New Materials Oy		ASSEMBLY DRAWING		
FAIR Phase 1		FRAME		
		E51WF-1032		
PROJECT NUMBER		DATE	ARCHIVING CODE	PAGE
25019443		12.06.2026		
DESIGNER		APPROVED	CHECKED	DESIGN GROUP
Alexey Serous		Pertti Koivumaa	Jere Kallosalmi	STR
DWS: NO		REVISION		
25019443		E51WF-1032 01		




SWECO RAKENNETEKNIikka OY
ILMALANPORTTI 2
00240 HELSINKI
PUH. +358 207 393 000
www.sweco.fi

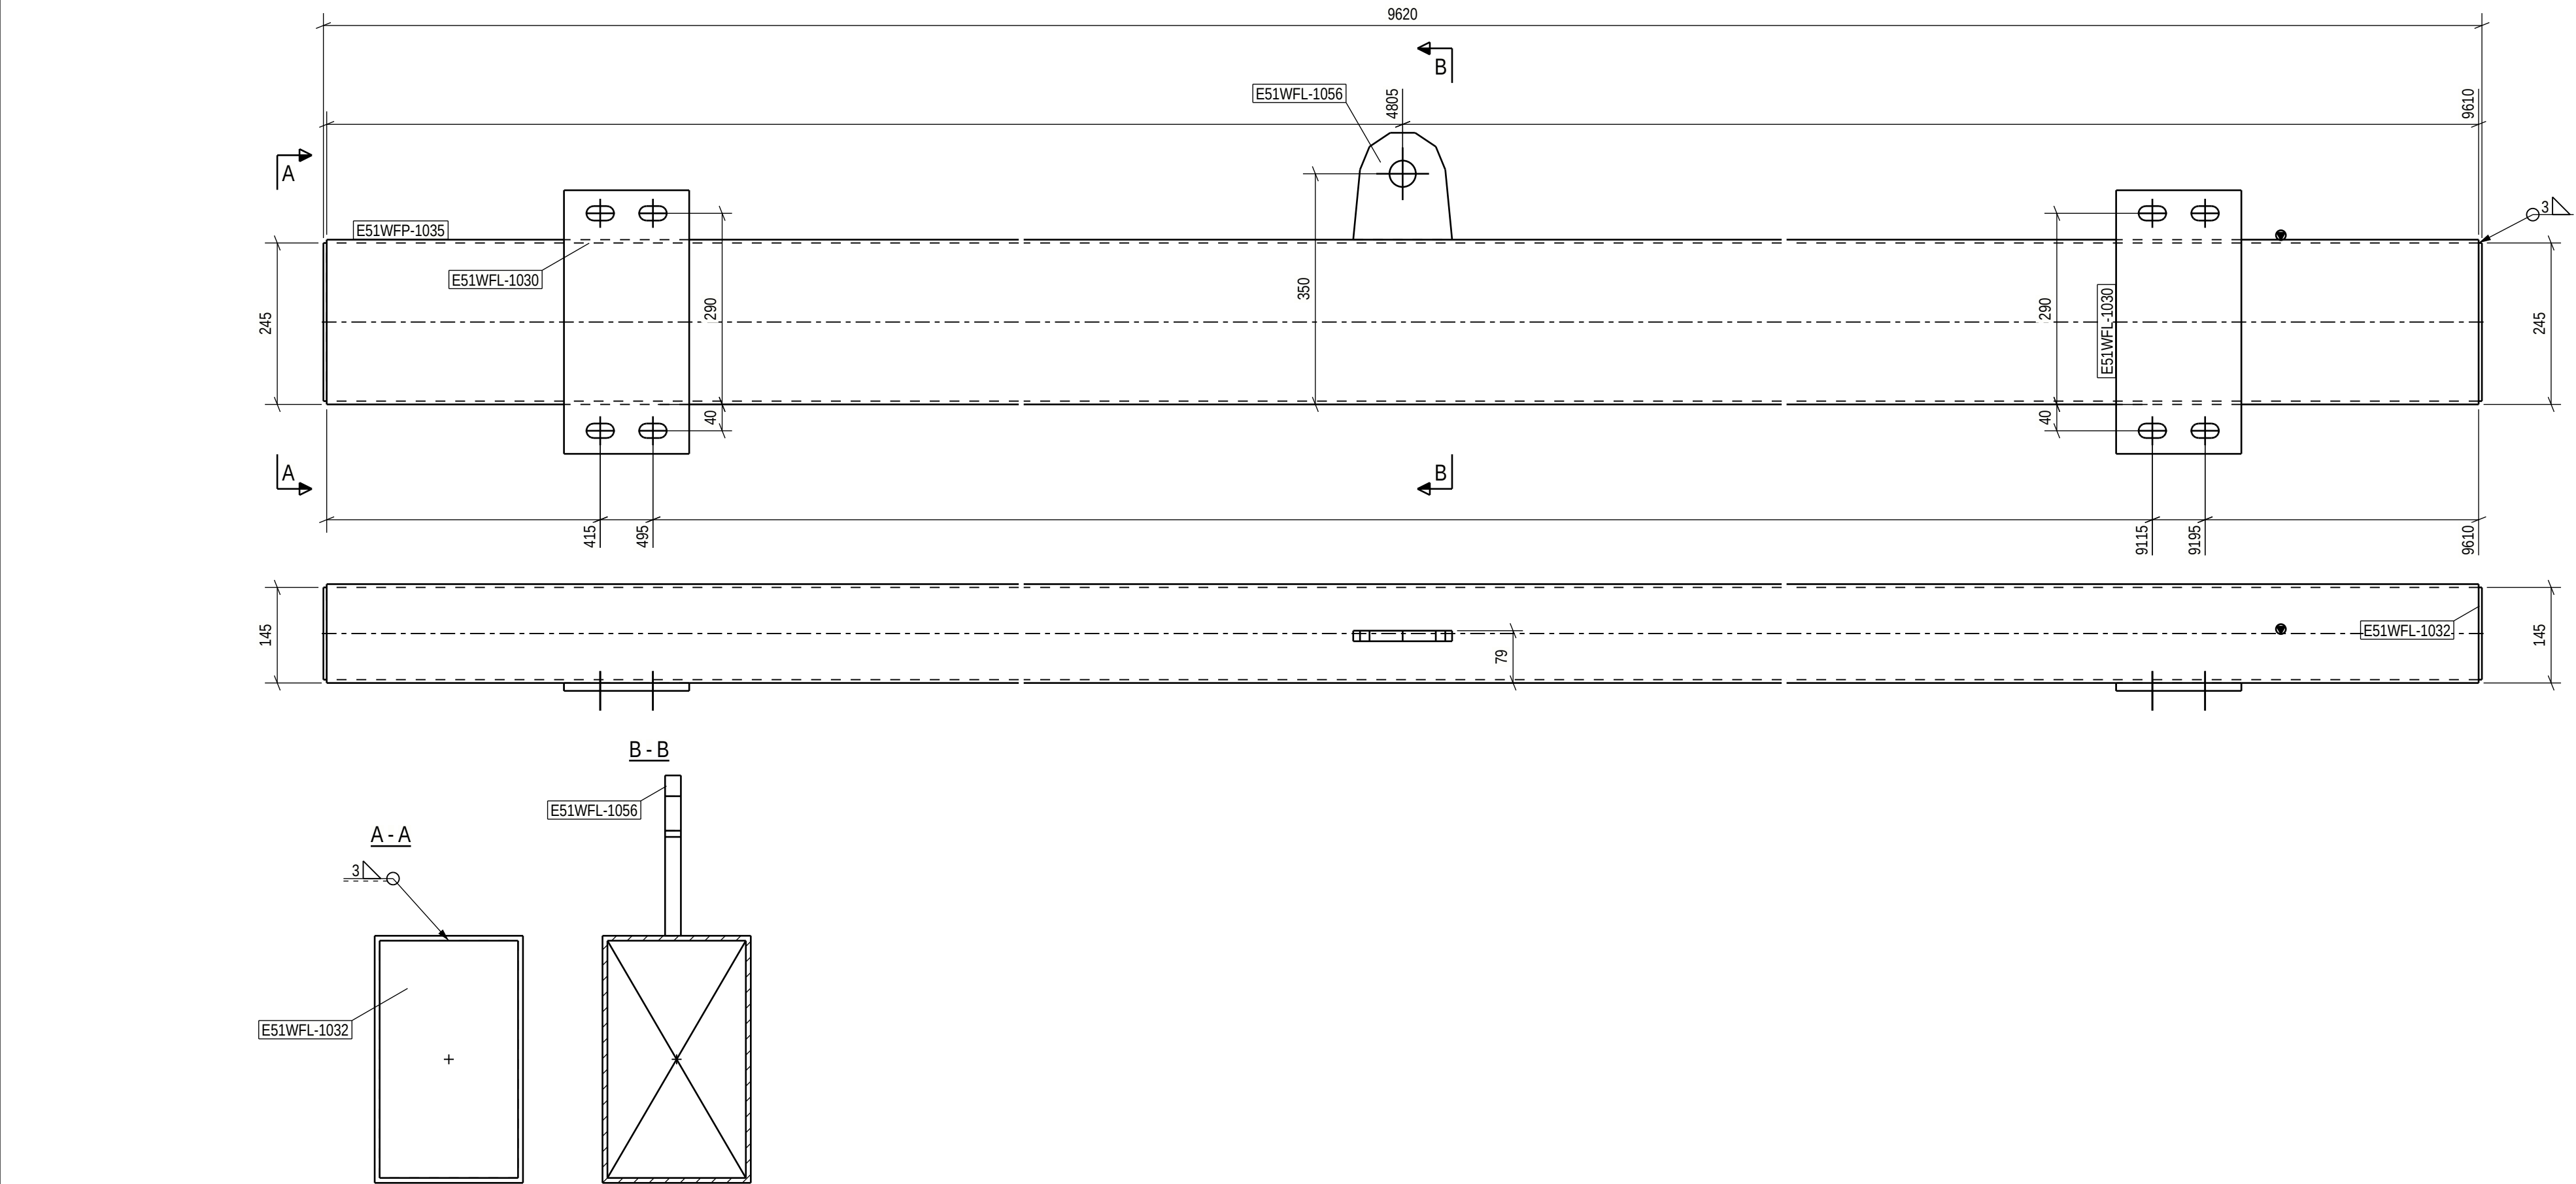

PART LIST FOR ASSEMBLY E51WF-1033, MANUFACTURING AMOUNT 2 PIECES						
PART	PROFILE	MATERIAL	LENGTH [mm]	AREA [m2]	WEIGHT [kg]	PCS
E51WFL-1030	PL12X190	S355J2+N	400	0.33	7.2	2
E51WFL-1032	PL5X140	S355J2+N	240	0.14	1.3	2
E51WFL-1056	PL16X162	S355J2	150	0.05	2.6	1
E51WFP-1035	CFRHS250X150X5	S355J2H	9610	7.52	289.4	1
TOTAL:				8.05	308.9	

LIFTING LUG WELDING, WEIGHT < 1,5 t

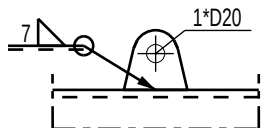

Technical fabrication requirements:		Execution class
Requirements for fabrication, standard	EN1090-2, table A.3 : EXC2	EXC2
Execution Specification document nr	25019443-ICC250-0600-0660-000005	
Surface preparation grade	ISO8501-3, grade P2	
Surface treatment	ISO12944-5	
Additional requirements on surface treatment	C3.07, EPPUR 240/2	
Shade	RAL 7024 (Graphite Gray)	
Welding of built up steel section	Appendix 1 / Project spec.	
Welds, if not specified otherwise	EN 9692-1, EN 9692-2	
Fabrication tolerances	EN 1090-2, Appendix B	
Special fabrication tolerances	Project specification/ shown on drwg.	
Weld inspection, requirements	EN 1090-2, Table 24, U>0.5	
Extent of NDT, fillet welds	MT-EN1290, 20% of welds	
Extent of NDT, butt welds	UT, EN-ISO17640, 20% of welds	
Extent of NDT for splices not shown on drawing	UT, EN-ISO17640, 100% of welds	
Requirements on holing	EN1090-2 Section 6.6.3	
Weld class	C, EN ISO 5817	
Additional material inspection	Shown on drwg.	

Approved For Construction

PROJECT NAME
Easpring New Materials Oy
FAIR Phase 1




SWECO RAKENNETEKNIikka OY
ILMALANPORTTI 2
00240 HELSINKI
PUH. +358 207 393 000
www.sweco.fi


DRAWING CONTENT
ASSEMBLY DRAWING
FRAME
E51WF-1033


DATE	ARCHIVING CODE	PAGE	DESIGN GROUP
12.06.2026			STR
DRAWN	DESIGNER	APPROVED	CHECKED
Alexey Serous	Alexey Serous	Pertti Koivumaa	Jere Kallosalmi
PROJECT NUMBER	DWG. NO.	REVISION	
25019443	E51WF-1033		

PART LIST FOR ASSEMBLY E51WF-1034, MANUFACTURING AMOUNT 1 PIECES						
PART	PROFILE	MATERIAL	LENGTH [mm]	AREA [m2]	WEIGHT [kg]	PCS
E51WFL-1031	PL12X190	S355J2+N	300	0.25	5.4	2
E51WFL-1033	PL5X140	S355J2+N	140	0.08	0.8	2
E51WFL-1056	PL16X162	S355J2	150	0.05	2.6	1
E51WFP-1026	CFRHS150X150X5	S355J2H	9610	5.60	213.9	1
TOTAL:				5.99	228.7	

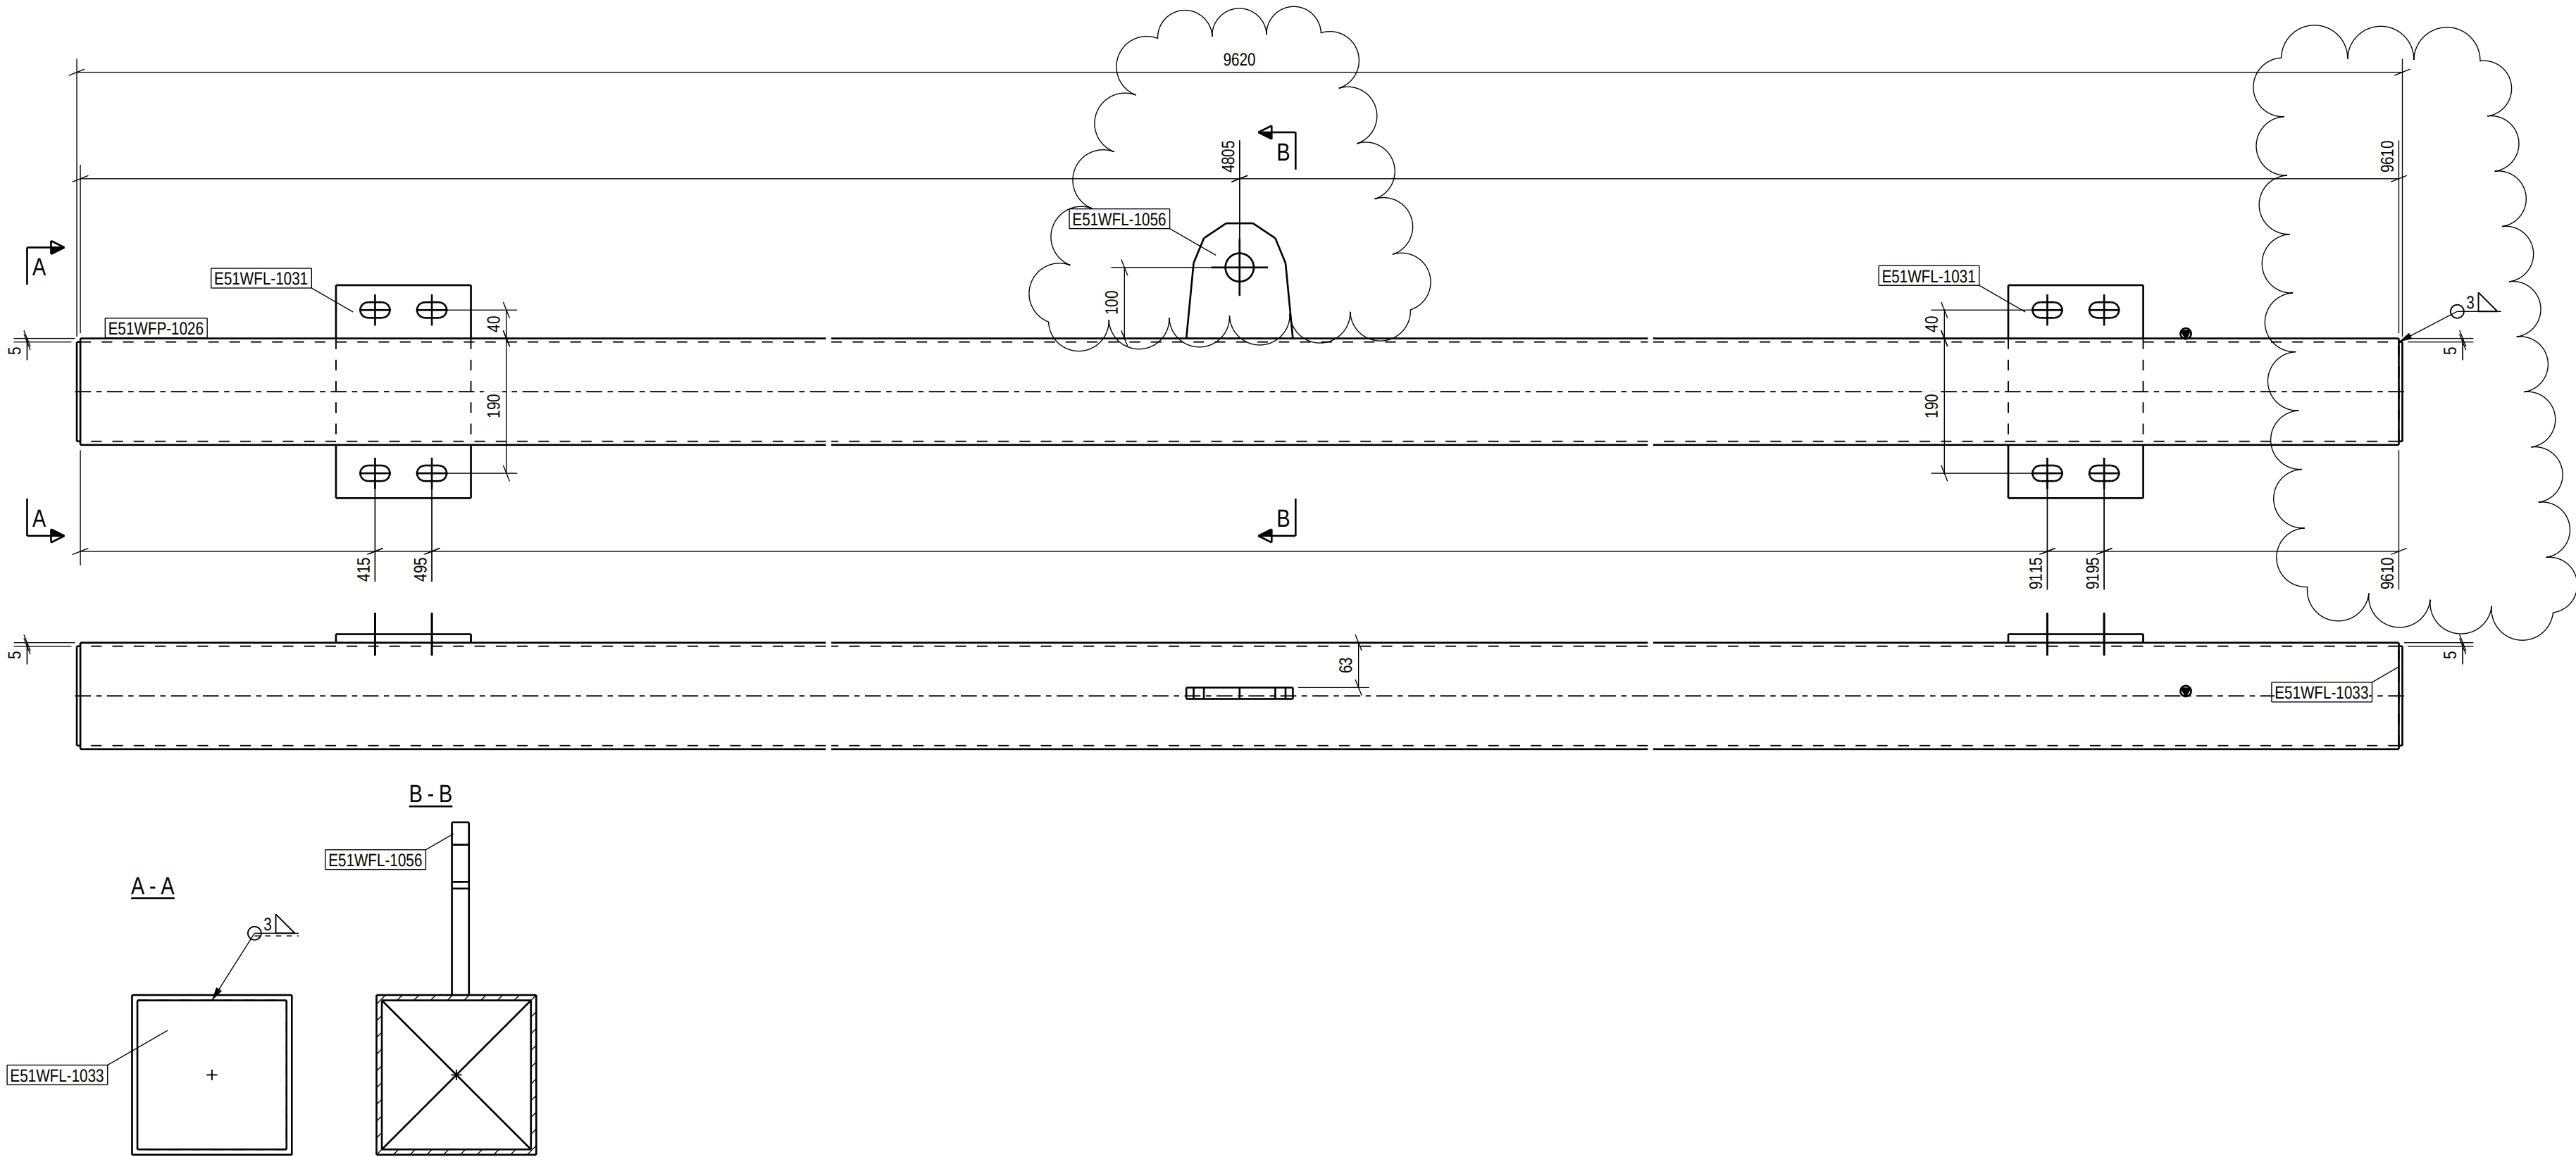


Approved For Construction

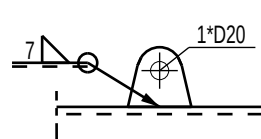LIFTING LUG WELDING, WEIGHT < 1,5 t 	Technical fabrication requirements:		Execution class EXC2		01Length decreased		FIALES		29.06.2026		FIKJER											
	Requirements for fabrication, standard EN1090-2, table A.3 : EXC2				Fabrication tolerances EN 1090-2, Appendix B				REV. REVISION				CHANGED BY DATE CHECKED BY									
	Execution Specification document nr 25019443-ICC250-0600-0660-000005				Special fabrication tolerances Project specification/ shown on drwg.				PROJECT NAME				DRAWING CONTENT									
	Surface preparation grade ISO8501-3, grade P2				Weld inspection, requirements EN 1090-2, Table 24, U>0.5				Easpring New Materials Oy				ASSEMBLY DRAWING									
	Surface treatment ISO12944-5				Extent of NDT, fillet welds MT-EN1290, 20% of welds				FAIR Phase 1				FRAME									
	Additional requirements on surface treatment C3.07, EPPUR 240/2				Extent of NDT, butt welds UT, EN-ISO17640, 20% of welds				 SWECO Sustainable engineering and design				DATE 12.06.2026				ARCHIVING CODE		PAGE		DESIGN GROUP STR	
	Shade RAL 7024 (Graphite Gray)				Extent of NDT for splices not shown on drawing UT, EN-ISO17640, 100% of welds								DRAWN Alexey Serous		DESIGNER Alexey Serous		APPROVED Pertti Kouvumaaanaho		CHECKED Jere Kallosalmi			
Welding of built up steel section Appendix 1 / Project spec.				Requirements on holing EN1090-2 Section 6.6.3				PUH. +358 207 393 000 www.sweco.fi				PROJECT NUMBER 25019443				DWG. NO. E51WF-1034		REVISION 01				
Welds, if not specified otherwise EN 9692-1, EN 9692-2				Weld class C, EN ISO 5817				Additional material inspection Shown on drwg.														

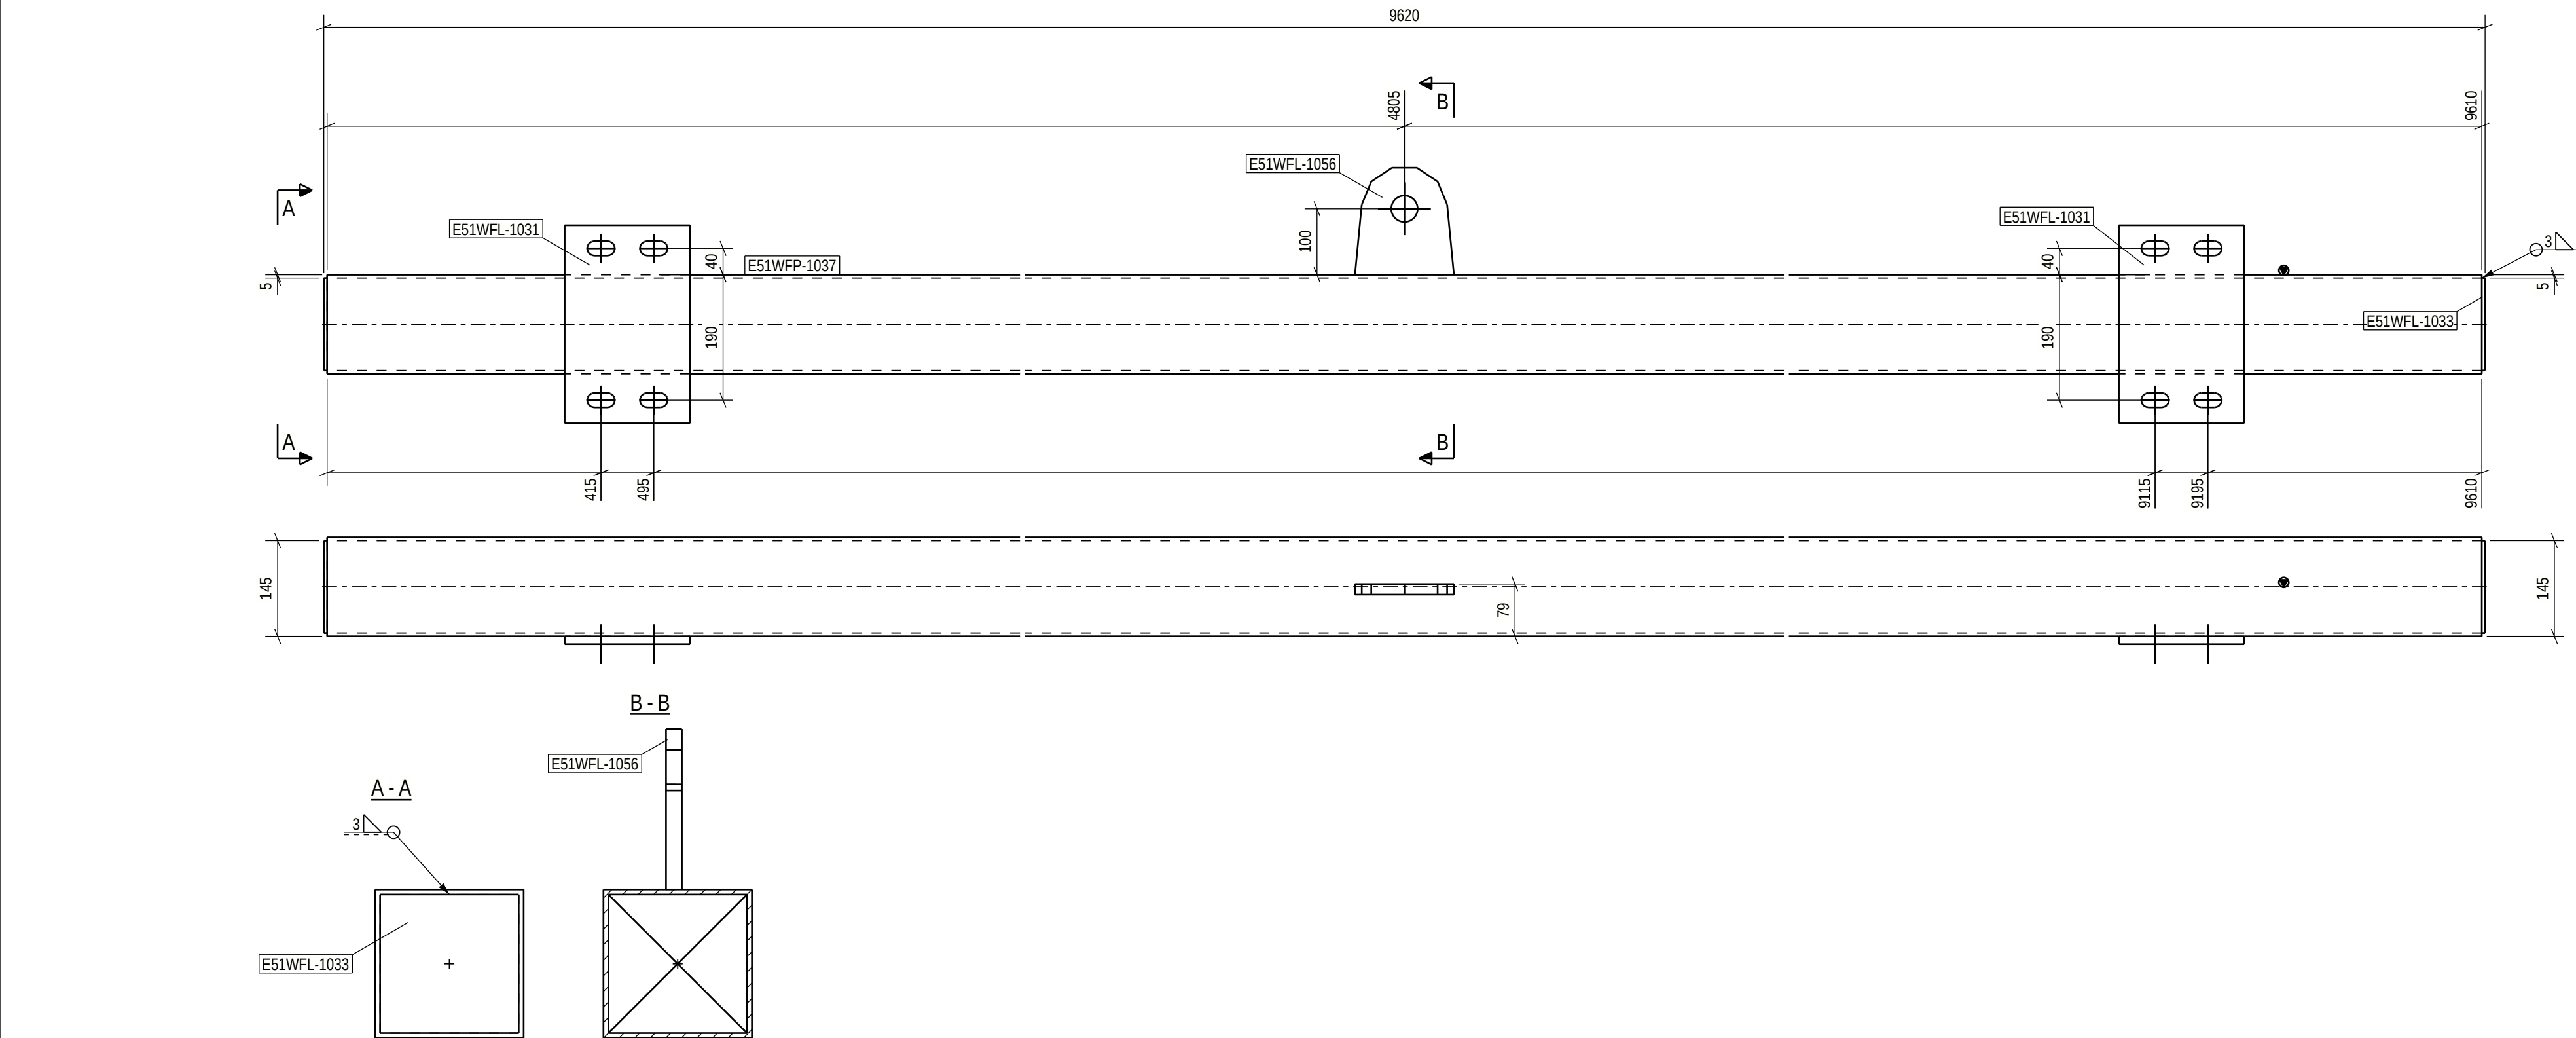

PART LIST FOR ASSEMBLY E51WF-1035, MANUFACTURING AMOUNT 2 PIECES						
PART	PROFILE	MATERIAL	LENGTH [mm]	AREA [m ²]	WEIGHT [kg]	PCS
E51WFL-1031	PL12X190	S355J2+N	300	0.25	5.4	2
E51WFL-1033	PL5X140	S355J2+N	140	0.08	0.8	2
E51WFL-1056	PL16X162	S355J2	150	0.05	2.6	1
E51WFP-1037	CFRHS150X150X5	S355J2H	9610	5.60	213.9	1
TOTAL:				5.99	228.7	

LIFTING LUG WELDING, WEIGHT < 1,5 t

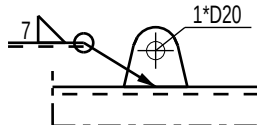


Technical fabrication requirements:		Execution class
Requirements for fabrication, standard	EN1090-2, table A.3 : EXC2	EXC2
Execution Specification document nr	25019443-ICC250-0600-0660-000005	
Surface preparation grade	ISO8501-3, grade P2	
Surface treatment	ISO12944-5	
Additional requirements on surface treatment	C3.07, EPPUR 240/2	
Shade	RAL 7024 (Graphite Gray)	
Welding of built up steel section	Appendix 1 / Project spec.	
Welds, if not specified otherwise	EN 9692-1, EN 9692-2	
Fabrication tolerances	EN 1090-2, Appendix B	
Special fabrication tolerances	Project specification/ shown on drwg.	
Weld inspection, requirements	EN 1090-2, Table 24, U>0.5	
Extent of NDT, fillet welds	MT-EN1290, 20% of welds	
Extent of NDT, butt welds	UT, EN-ISO17640, 20% of welds	
Extent of NDT for splices not shown on drawing	UT, EN-ISO17640, 100% of welds	
Requirements on holing	EN1090-2 Section 6.6.3	
Weld class	C, EN ISO 5817	
Additional material inspection	Shown on drwg.	

Approved For Construction

Easpring New Materials Oy
FAIR Phase 1




SWECO RAKENNETEKNIikka OY
ILMALANPORTTI 2
00240 HELSINKI
PUH. +358 207 393 000
www.sweco.fi

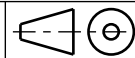


DRAWING CONTENT
ASSEMBLY DRAWING
FRAME
E51WF-1035


DATE	ARCHIVING CODE	PAGE	DESIGN GROUP
12.06.2026			STR
DRAWN	DESIGNER	APPROVED	CHECKED
Alexey Serous	Alexey Serous	Pertti Koivumaa	Jere Kallosalmi
PROJECT NUMBER	DWG. NO.	REVISION	
25019443	E51WF-1035		

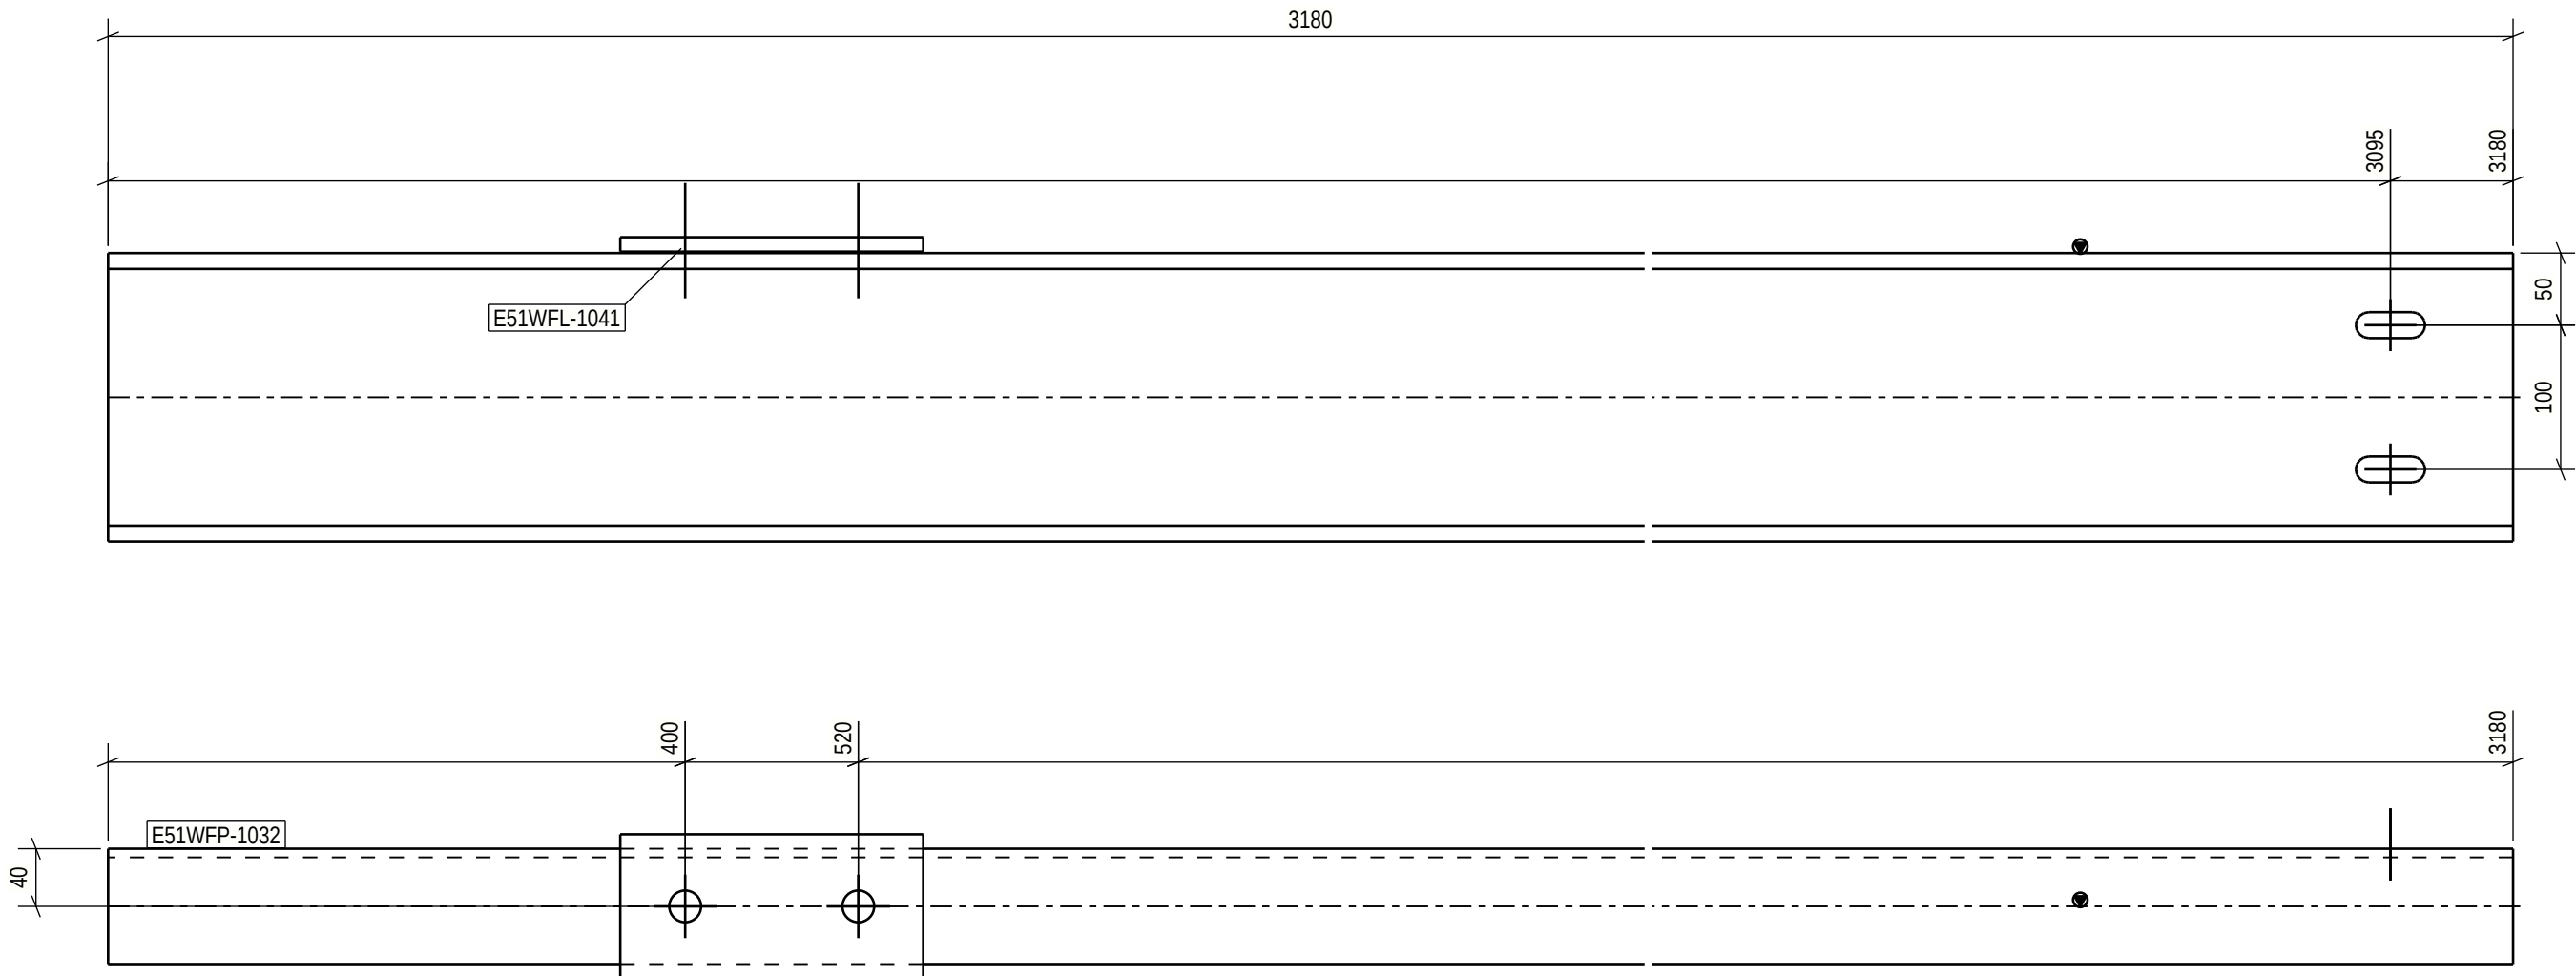


PART LIST FOR ASSEMBLY E51WF-1036, MANUFACTURING AMOUNT 2 PIECES						
PART	PROFILE	MATERIAL	LENGTH [mm]	AREA [m2]	WEIGHT [kg]	PCS
E51WFL-1041	PL10X100	S355J2+N	210	0.05	1.6	1
E51WFP-1032	UPE200	S355J2H	3180	2.22	72.4	1
TOTAL:				2.26	74.0	

LIFTING LUG WELDING, WEIGHT < 1,5 t

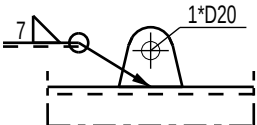


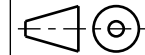Technical fabrication requirements:		Execution class EXC2		Approved For Construction											
Requirements for fabrication, standard EN1090-2, table A.3 : EXC2		Fabrication tolerances EN 1090-2, Appendix B		PROJECT NAME Easpring New Materials Oy FAIR Phase 1				DRAWING CONTENT ASSEMBLY DRAWING BEAM E51WF-1036							
Execution Specification document nr 25019443-ICC250-0600-0660-000005		Special fabrication tolerances Project specification/ shown on drwg.													
Surface preparation grade ISO8501-3, grade P2		Weld inspection, requirements EN 1090-2, Table 24, U>0.5		 SWECO Sustainable engineering and design		SWECO RAKENNETEKNIikka OY ILMALANPORTTI 2 00240 HELSINKI PUH. +358 207 393 000 www.sweco.fi		DATE 12.06.2026		ARCHIVING CODE		PAGE		DESIGN GROUP STR	
Surface treatment ISO12944-5		Extent of NDT, fillet welds MT-EN1290, 20% of welds						DRAWN Alexey Serous		DESIGNER Alexey Serous		APPROVED Pertti Koivumaaanaho		CHECKED Jere Kalliosalmi	
Additional requirements on surface treatment C3.07, EPPUR 240/2		Extent of NDT, butt welds UT, EN-ISO17640, 20% of welds				PROJECT NUMBER 25019443		DWG. NO. E51WF-1036							
Shade RAL 7024 (Graphite Gray)		Extent of NDT for splices not shown on drawing UT, EN-ISO17640, 100% of welds													
Welding of built up steel section Appendix 1 / Project spec.		Requirements on holding EN1090-2 Section 6.6.3													
Welds, if not specified otherwise EN 9692-1, EN 9692-2		Weld class C, EN ISO 5817		Additional material inspection Shown on drwg.											

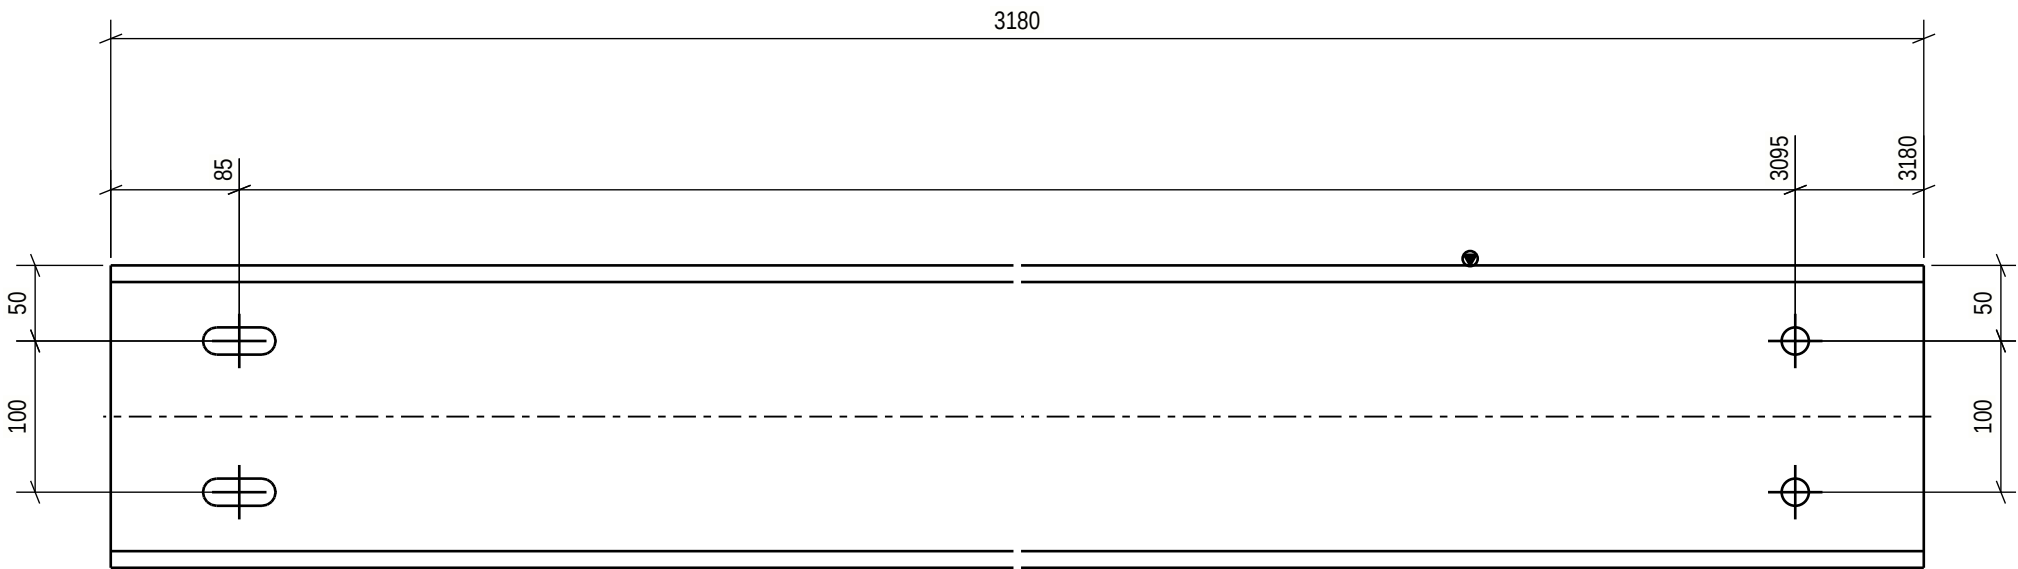

PART LIST FOR ASSEMBLY E51WF-1037, MANUFACTURING AMOUNT 3 PIECES						
PART	PROFILE	MATERIAL	LENGTH [mm]	AREA [m2]	WEIGHT [kg]	PCS
E51WFP-1031	UPE200	S355J2H	3180	2.22	72.4	1
TOTAL:				2.22	72.4	

LIFTING LUG WELDING, WEIGHT < 1,5 t

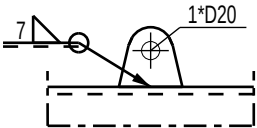


Technical fabrication requirements:		Execution class
Requirements for fabrication, standard	Fabrication tolerances	EXC2
EN1090-2, table A.3 : EXC2	EN 1090-2, Appendix B	
Execution Specification document nr	Special fabrication tolerances	
25019443-ICC250-0600-0660-000005	Project specification/ shown on drwg.	
Surface preparation grade	Weld inspection, requirements	
ISO8501-3, grade P2	EN 1090-2,Table 24, U>0.5	
Surface treatment	Extent of NDT, fillet welds	
ISO12944-5	MT-EN1290,20% of welds	
Additional requirements on surface treatment	Extent of NDT, butt welds	
C3.07, EPPUR 240/2	UT, EN-ISO17640, 20% of welds	
Shade	Extent of NDT for splices not shown on drawing	C, EN ISO 5817
RAL 7024 (Graphite Gray)	UT, EN-ISO17640, 100%of welds	
Welding of built up steel section	Requirements on holing	
Appendix 1 / Project spec.	EN1090-2 Section 6.6.3	
Welds, if not specified otherwise	Weld class	
EN 9692-1, EN 9692-2	Additional material inspection	Shown on drwg.

Approved For Construction

PROJECT NAME
Easpring New Materials Oy
FAIR Phase 1




SWECO RAKENNETEKNIikka OY
ILMALANPORTTI 2
00240 HELSINKI
PUH. +358 207 393 000
www.sweco.fi

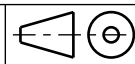


DRAWING CONTENT
ASSEMBLY DRAWING
BEAM
E51WF-1037

DATE	ARCHIVING CODE	PAGE	DESIGN GROUP
12.06.2026			STR
DRAWN	DESIGNER	APPROVED	CHECKED
Alexey Serous	Alexey Serous	Pertti Koivumaaanaho	Jere Kallosalmi
PROJECT NUMBER	DWG. NO.	REVISION	
25019443	E51WF-1037		

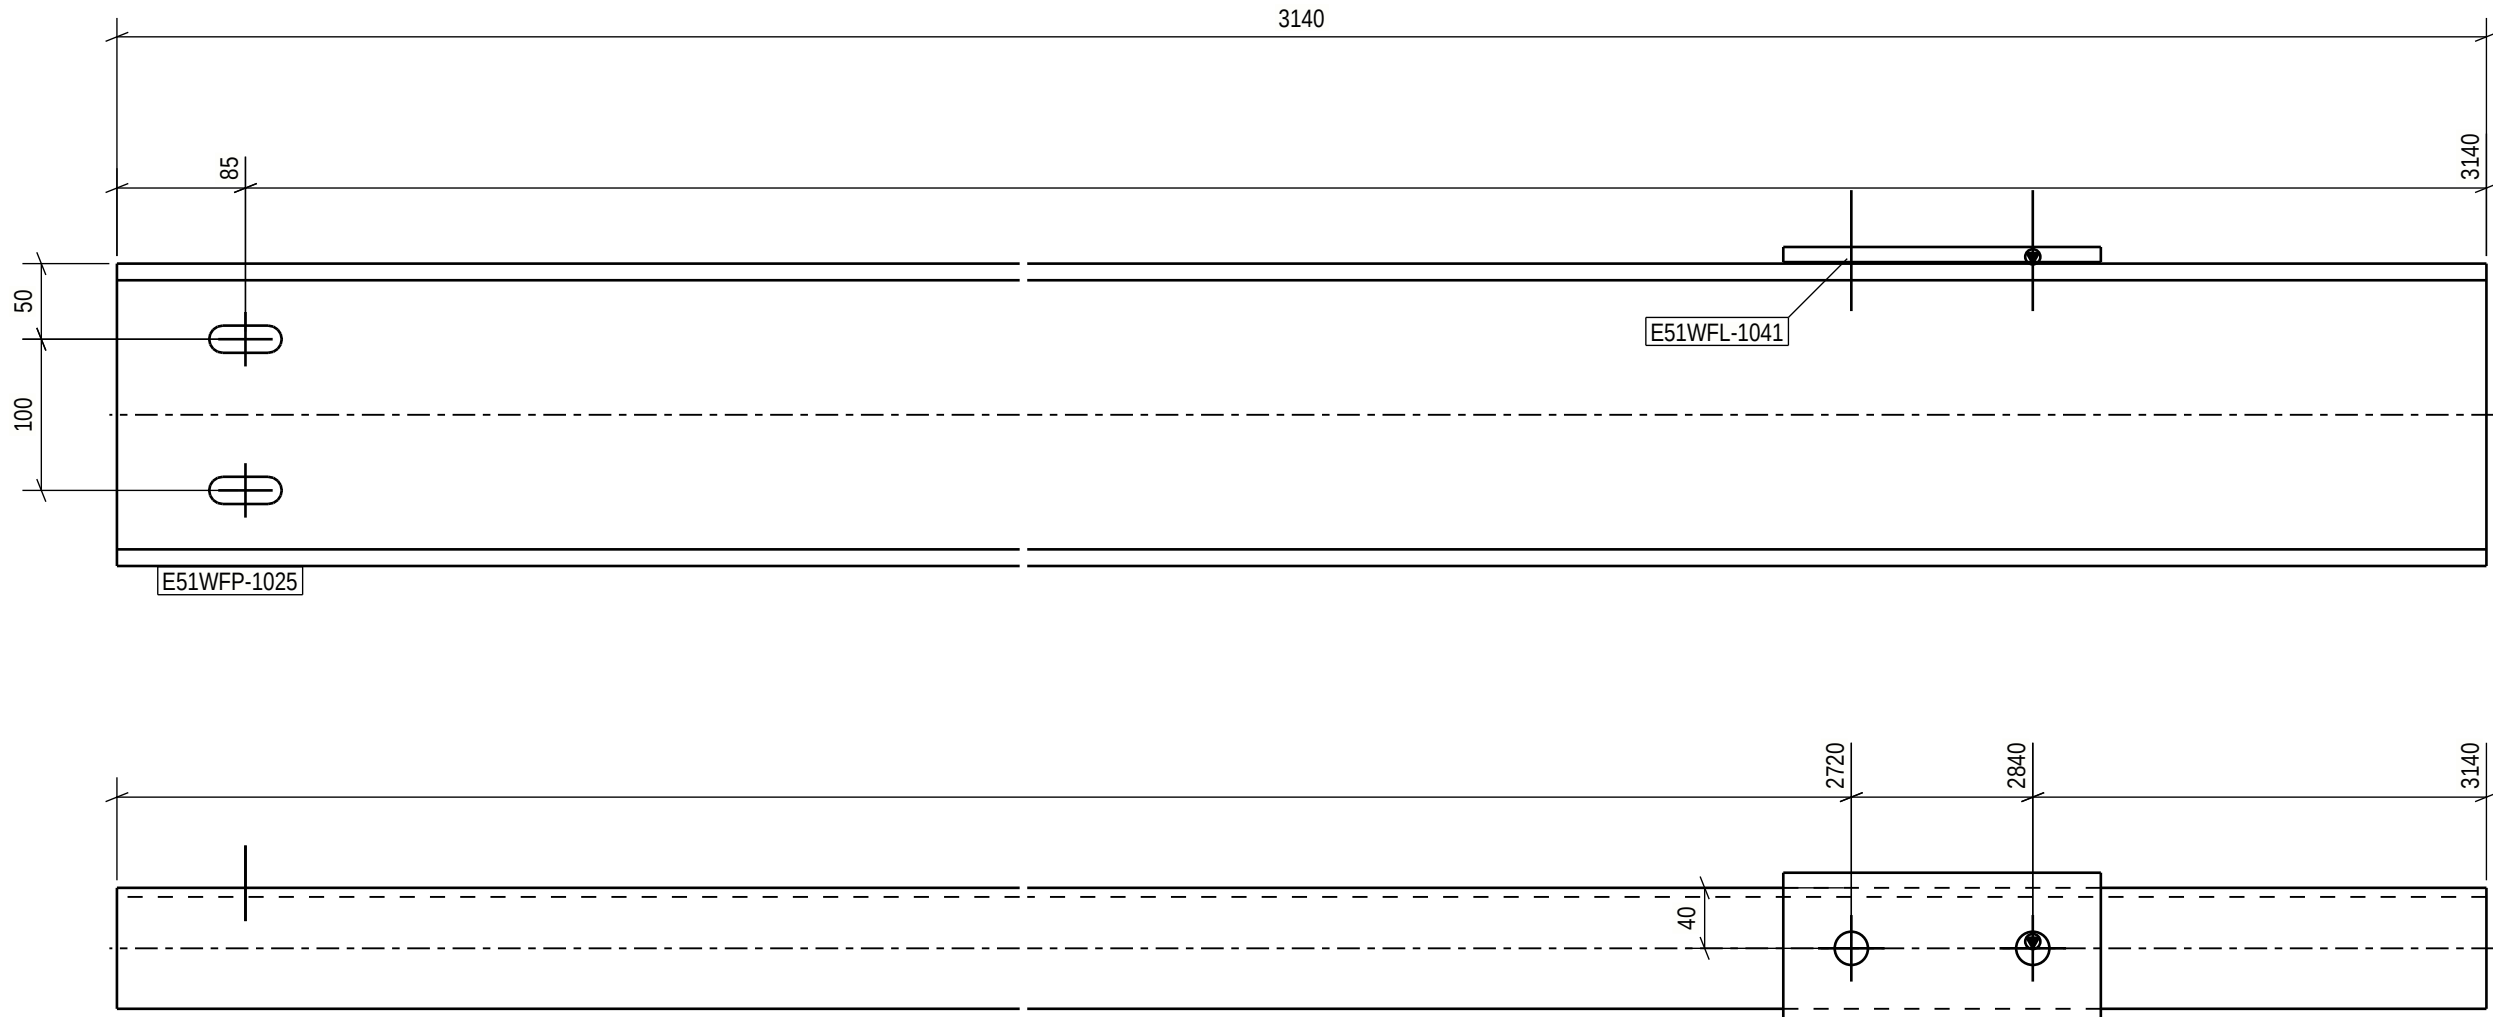

PART LIST FOR ASSEMBLY E51WF-1038, MANUFACTURING AMOUNT 2 PIECES						
PART	PROFILE	MATERIAL	LENGTH [mm]	AREA [m2]	WEIGHT [kg]	PCS
E51WFL-1041	PL10X100	S355J2+N	210	0.05	1.6	1
E51WFP-1025	UPE200	S355J2H	3140	2.19	71.5	1
TOTAL:				2.24	73.1	

LIFTING LUG WELDING, WEIGHT < 1,5 t

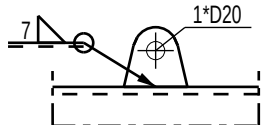

Technical fabrication requirements:		Execution class EXC2	
Requirements for fabrication, standard EN1090-2, table A.3 : EXC2		Fabrication tolerances EN 1090-2, Appendix B	
Execution Specification document nr 25019443-ICC250-0600-0660-000005		Special fabrication tolerances Project specification/ shown on drwg.	
Surface preparation grade ISO8501-3, grade P2		Weld inspection, requirements EN 1090-2, Table 24, U>0.5	
Surface treatment ISO12944-5		Extent of NDT, fillet welds MT-EN1290, 20% of welds	
Additional requirements on surface treatment C3.07, EPPUR 240/2		Extent of NDT, butt welds UT, EN-ISO17640, 20% of welds	
Shade RAL 7024 (Graphite Gray)		Extent of NDT for splices not shown on drawing UT, EN-ISO17640, 100% of welds	
Welding of built up steel section Appendix 1 / Project spec.		Requirements on hoisting EN1090-2 Section 6.6.3	
Welds, if not specified otherwise EN 9692-1, EN 9692-2		Weld class C, EN ISO 5817	
		Additional material inspection Shown on drwg.	

Approved For Construction


Easpring New Materials Oy

FAIR Phase 1




SWECO RAKENNETEKNIikka OY
ILMALANPORTTI 2
00240 HELSINKI
PUH. +358 207 393 000
www.sweco.fi

DRAWING CONTENT ASSEMBLY DRAWING BEAM E51WF-1038			
DATE 12.06.2026	ARCHIVING CODE	PAGE	DESIGN GROUP STR
DRAWN Alexey Serous	DESIGNER Alexey Serous	APPROVED Pertti Koivumaa	CHECKED Jere Kallosalmi
PROJECT NUMBER 25019443		REVISION E51WF-1038	

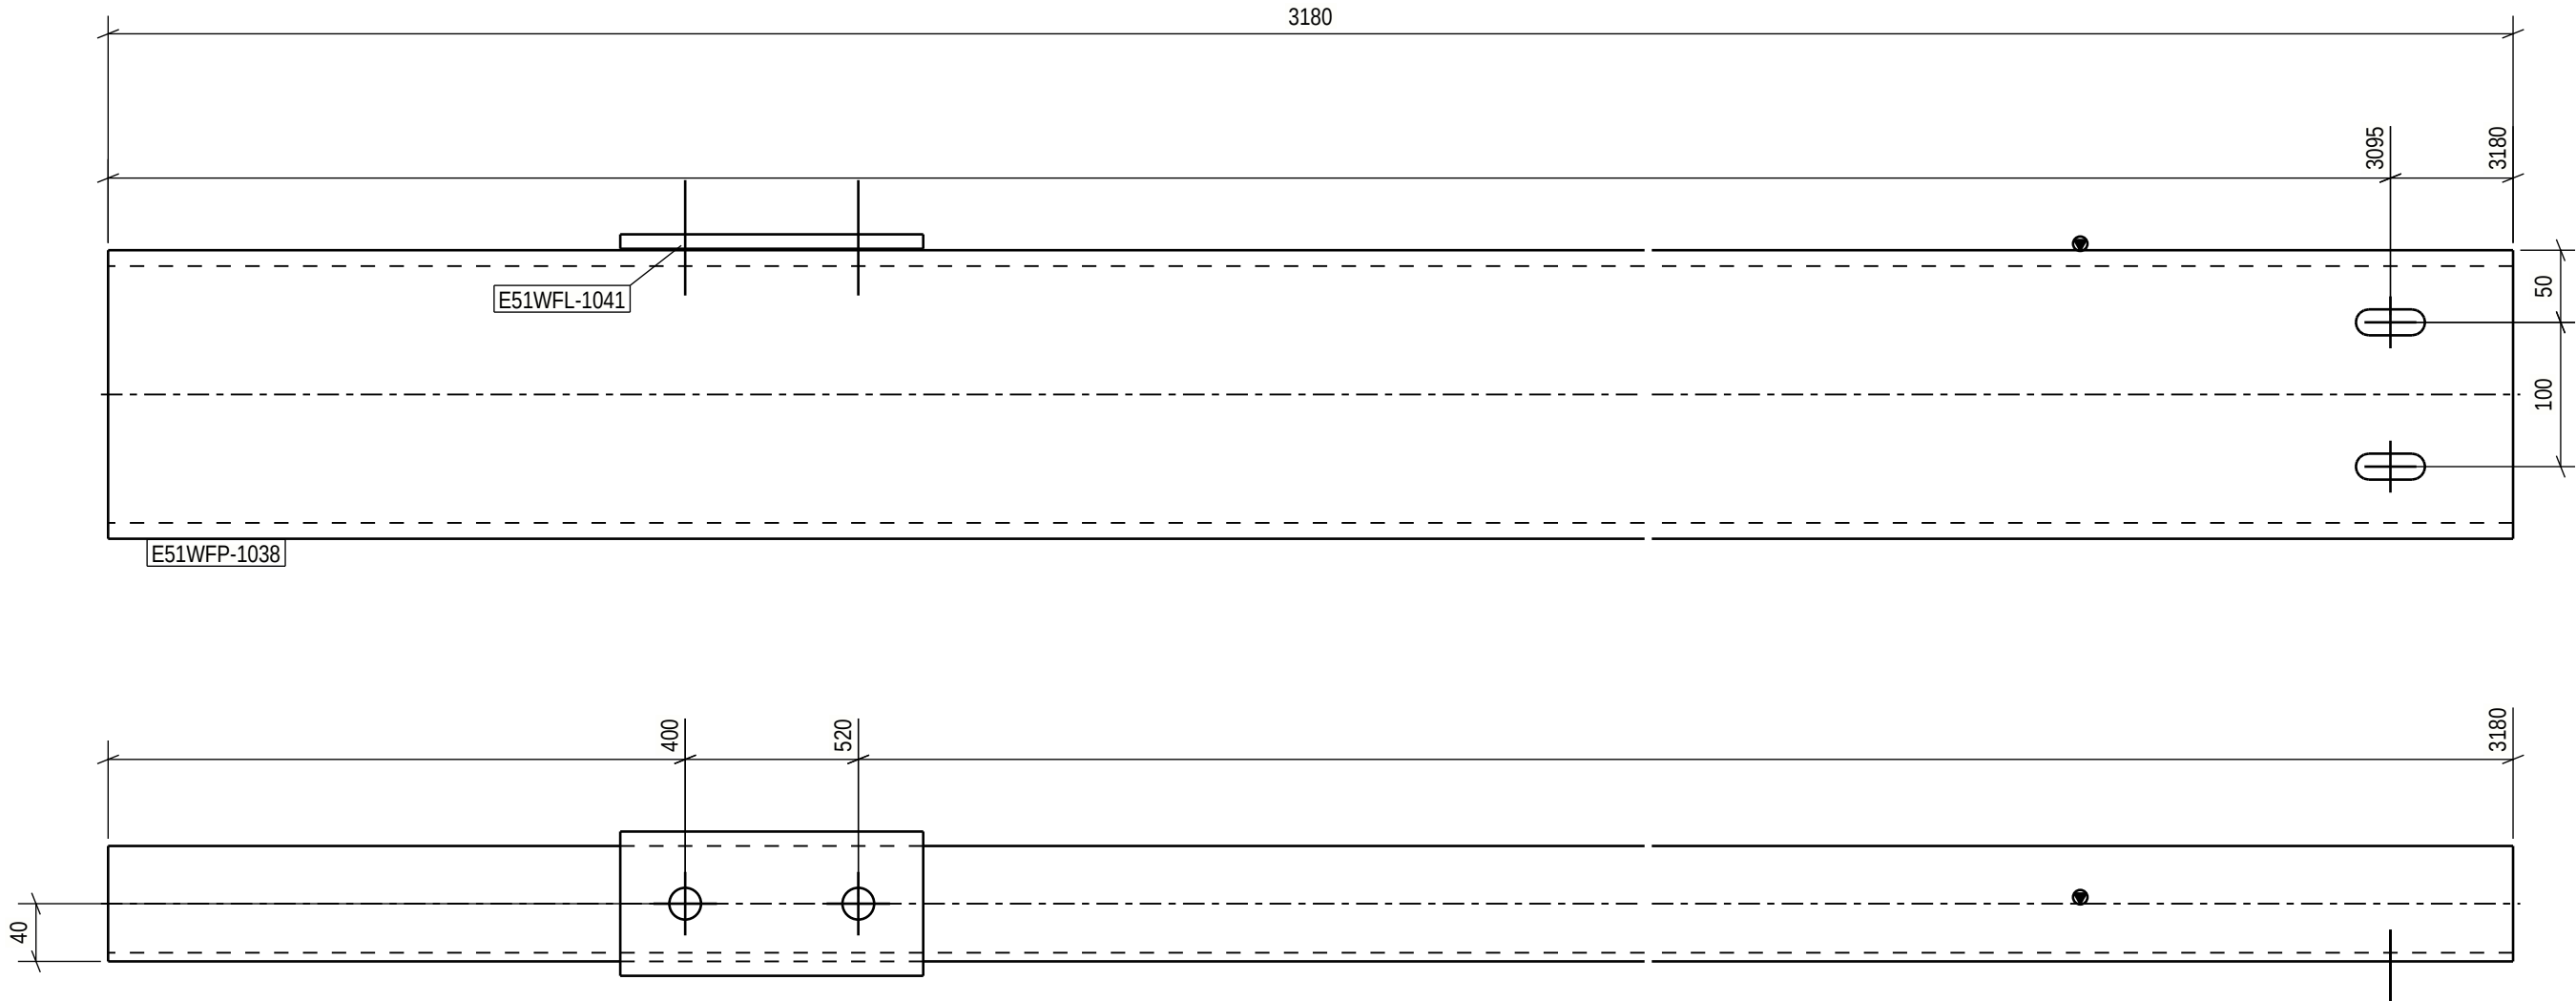

PART LIST FOR ASSEMBLY E51WF-1039, MANUFACTURING AMOUNT 1 PIECES						
PART	PROFILE	MATERIAL	LENGTH [mm]	AREA [m2]	WEIGHT [kg]	PCS
E51WFL-1041	PL10X100	S355J2+N	210	0.05	1.6	1
E51WFP-1038	UPE200	S355J2H	3180	2.22	72.4	1
TOTAL:				2.26	74.0	

LIFTING LUG WELDING, WEIGHT < 1,5 t

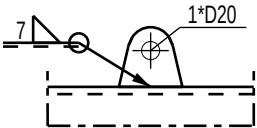


Technical fabrication requirements:		Execution class	
Requirements for fabrication, standard EN1090-2, table A.3 : EXC2		EXC2	
Execution Specification document nr 25019443-ICC250-0600-0660-000005		Fabrication tolerances EN 1090-2, Appendix B	
Surface preparation grade ISO8501-3, grade P2		Special fabrication tolerances Project specification/ shown on drwg.	
Surface treatment ISO12944-5		Weld inspection, requirements EN 1090-2,Table 24, U>0.5	
Additional requirements on surface treatment C3.07, EPPUR 240/2		Extent of NDT, fillet welds MT-EN1290,20% of welds	
Shade RAL 7024 (Graphite Gray)		Extent of NDT, butt welds UT, EN-ISO17640, 20% of welds	
Welding of built up steel section Appendix 1 / Project spec.		UT, EN-ISO17640, 100%of welds	
Welds, if not specified otherwise EN 9692-1, EN 9692-2		Requirements on holing EN1090-2 Section 6.6.3	
		Weld class C, EN ISO 5817	
		Additional material inspection Shown on drwg.	

PROJECT NAME		DRAWING CONTENT	
Easpring New Materials Oy		ASSEMBLY DRAWING	
FAIR Phase 1		BEAM	
		E51WF-1039	
PROJECT NUMBER		DATE	ARCHIVING CODE
25019443		12.06.2026	
		DRAWN	PAGE
		Alexey Serous	
		DESIGNER	DESIGN GROUP
		Alexey Serous	STR
		APPROVED	CHECKED
		Pertti Koivumaa	Jere Kallosalmi
		DWG. NO.	REVISION


SWECO		SWEKO RAKENNETEKNIikka OY	
Sustainable engineering and design		ILMALANPORTTI 2	
		00240 HELSINKI	
		PUH. +358 207 393 000	
		www.sweco.fi	

Approved For Construction

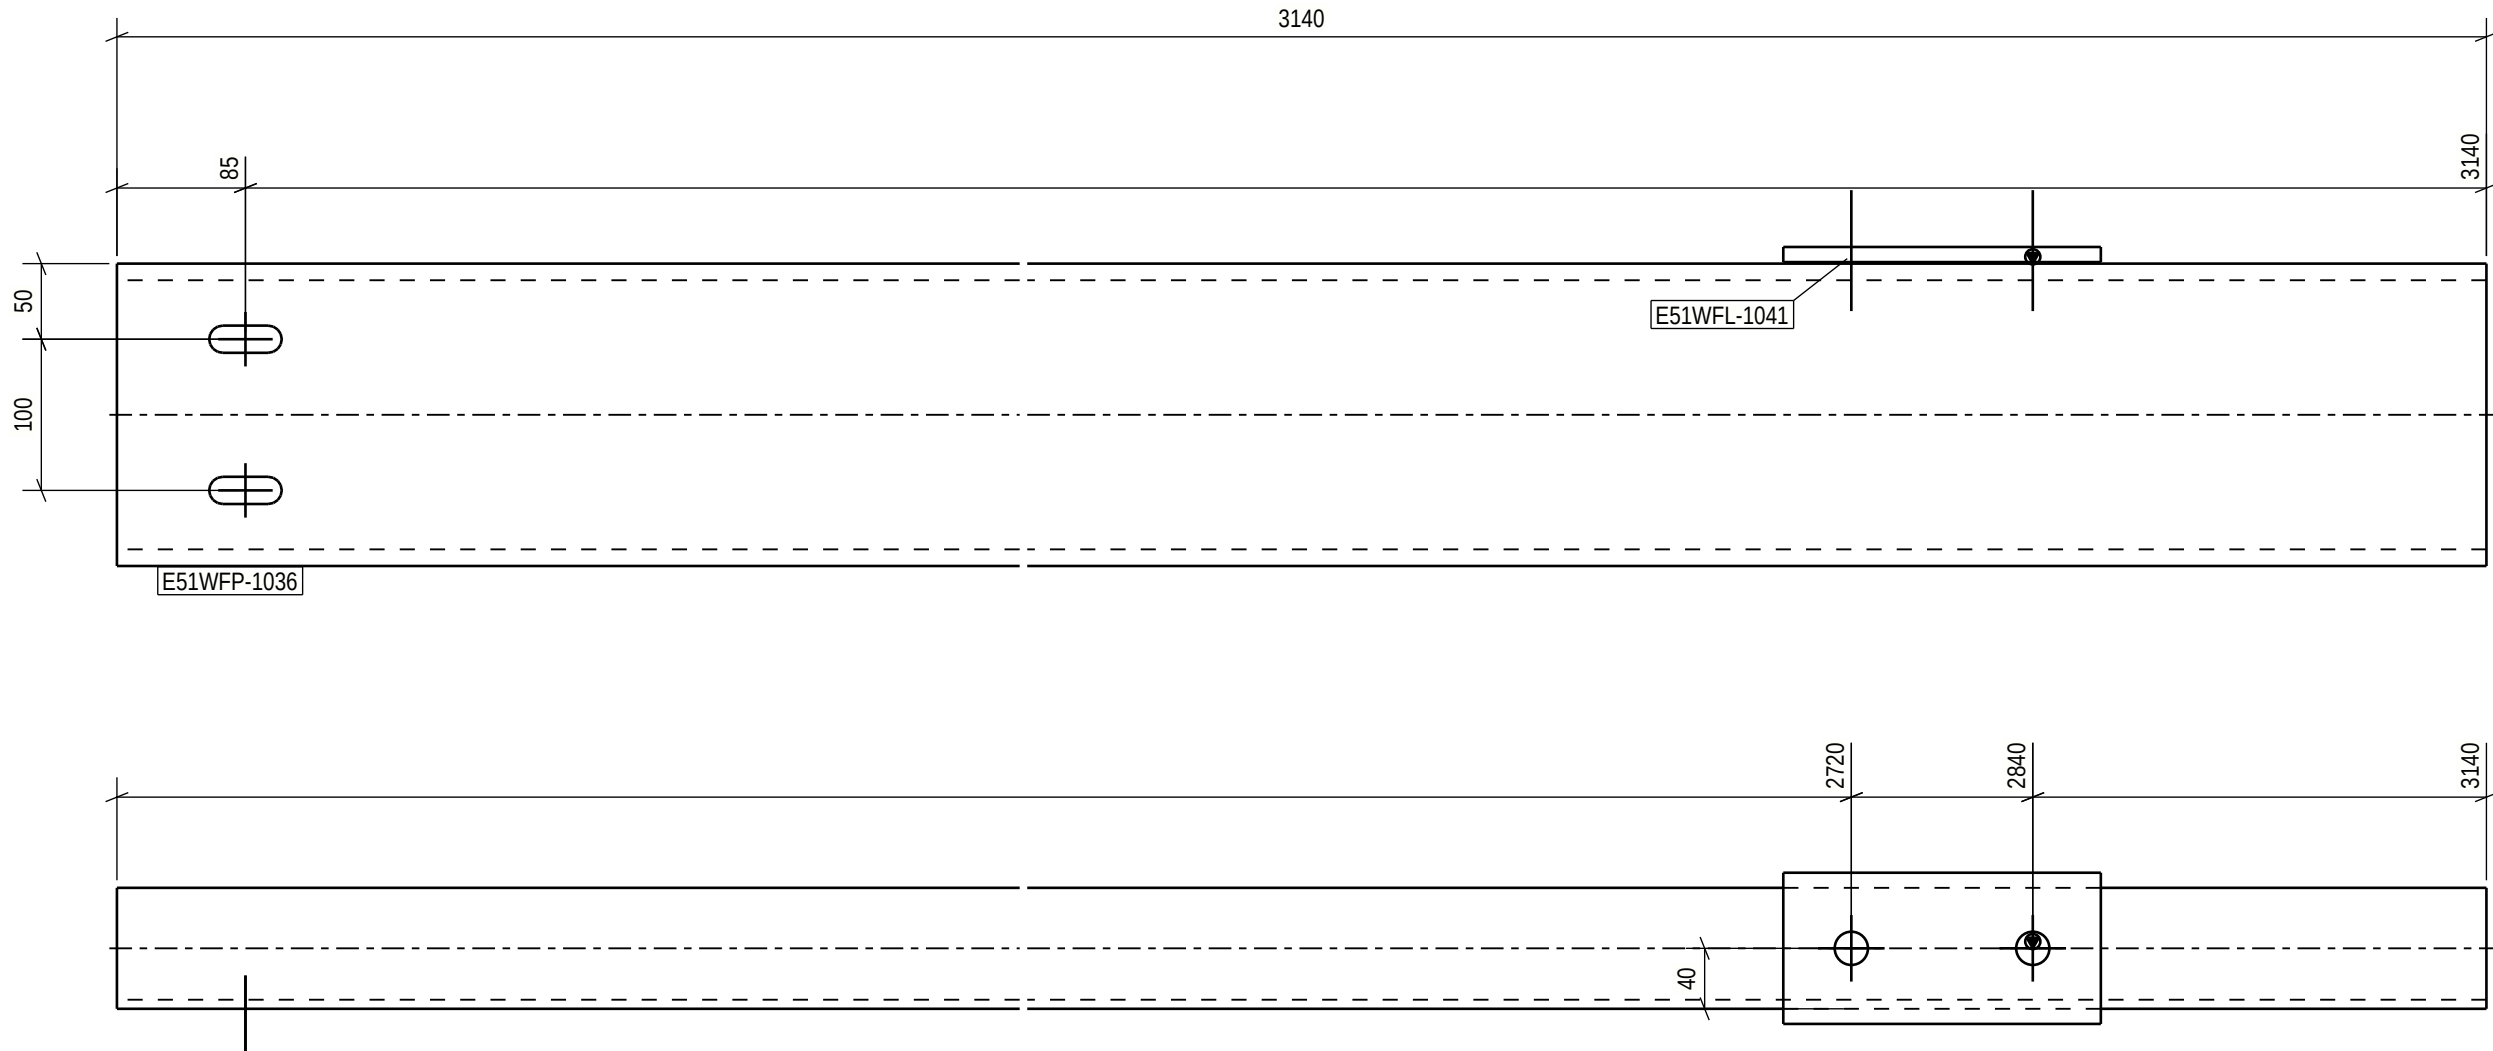

PART LIST FOR ASSEMBLY E51WF-1040, MANUFACTURING AMOUNT 1 PIECES						
PART	PROFILE	MATERIAL	LENGTH [mm]	AREA [m2]	WEIGHT [kg]	PCS
E51WFL-1041	PL10X100	S355J2+N	210	0.05	1.6	1
E51WFP-1036	UPE200	S355J2H	3140	2.19	71.5	1
TOTAL:				2.24	73.1	

LIFTING LUG WELDING, WEIGHT < 1,5 t

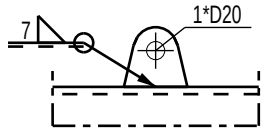

Technical fabrication requirements:

EXC2

Requirements for fabrication, standard
EN1090-2, table A.3 : EXC2
Execution Specification document nr
25019443-ICC250-0600-0660-000005
Surface preparation grade
ISO8501-3, grade P2
Surface treatment
ISO12944-5
Additional requirements on surface treatment
C3.07, EPPUR 240/2
Shade
RAL 7024 (Graphite Gray)
Welding of built up steel section
Appendix 1 / Project spec.
Welds, if not specified otherwise
EN 9692-1, EN 9692-2

Fabrication tolerances
EN 1090-2, Appendix B
Special fabrication tolerances
Project specification/ shown on drwg.
Weld inspection, requirements
EN 1090-2,Table 24, U>0.5
Extent of NDT, fillet welds
MT-EN1290,20% of welds
Extent of NDT, butt welds
UT, EN-ISO17640, 20% of welds
UT, EN-ISO17640, 100%of welds
Requirements on holing
EN1090-2 Section 6.6.3
Weld class
C, EN ISO 5817
Additional material inspection
Shown on drwg.

PROJECT NAME
Easpring New Materials Oy
FAIR Phase 1


SWECO

Sustainable engineering and design

SWECO RAKENNETEKNIikka OY
ILMALANPORTTI 2
00240 HELSINKI
PUH. +358 207 393 000
www.sweco.fi


DRAWING CONTENT
ASSEMBLY DRAWING
BEAM
E51WF-1040

DATE 12.06.2026	ARCHIVING CODE	PAGE	DESIGN GROUP STR
DRAWN Alexey Serous	DESIGNER Alexey Serous	APPROVED Pertti Koivumaaanaho	CHECKED Jere Kallosalmi
PROJECT NUMBER 25019443	DWG. NO. E51WF-1040	REVISION	

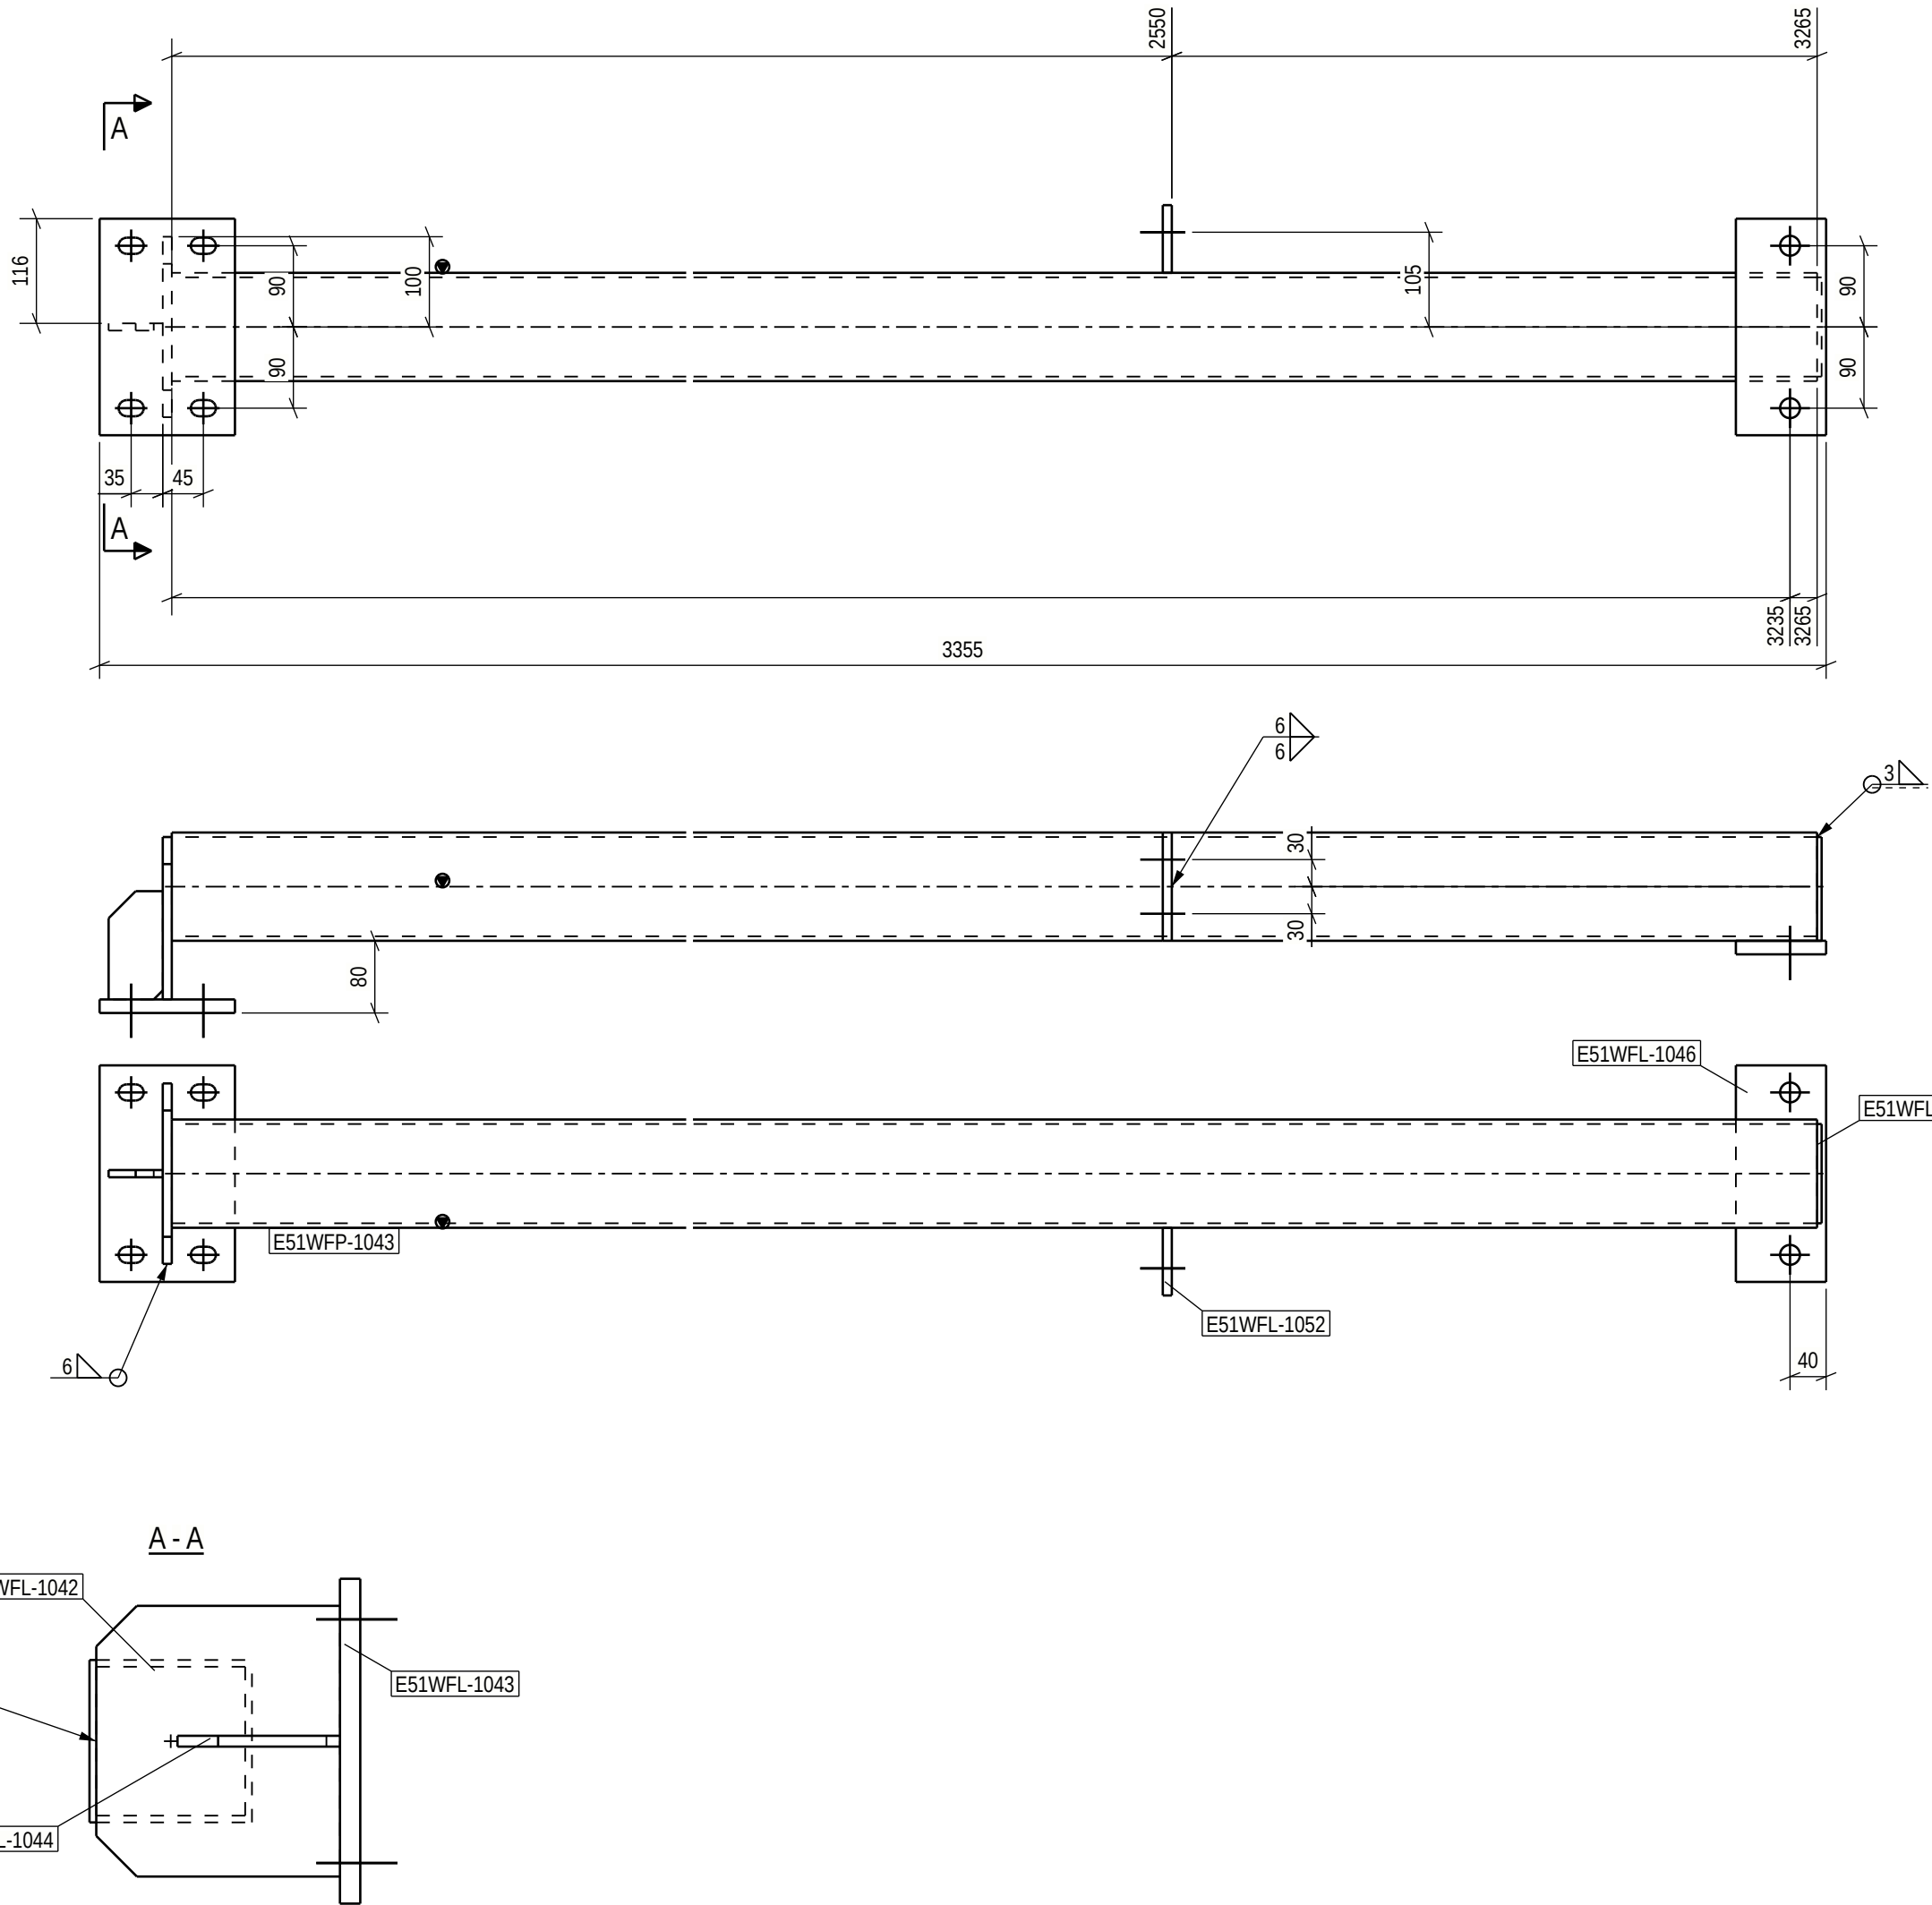

PART LIST FOR ASSEMBLY E51WF-1041, MANUFACTURING AMOUNT 1 PIECES						
PART	PROFILE	MATERIAL	LENGTH [mm]	AREA [m2]	WEIGHT [kg]	PCS
E51WFL-1042	PL10X200	S355J2+N	180	0.08	2.8	1
E51WFL-1043	PL15X150	S355J2+N	240	0.08	4.2	1
E51WFL-1044	PL8X60	S355J2+N	120	0.02	0.4	1
E51WFL-1045	PL5X110	S355J2+N	115	0.03	0.5	1
E51WFL-1046	PL15X100	S355J2+N	240	0.06	2.8	1
E51WFL-1052	PL10X75	S355J2+N	120	0.02	0.7	1
E51WFP-1043	CFRHS120X120X5	S355J2H	3265	1.51	57.3	1
TOTAL:				1.80	68.7	


LIFTING LUG WELDING, WEIGHT < 1,5 t

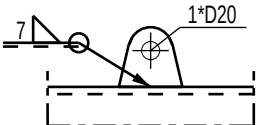

Technical fabrication requirements:		Execution class	
Requirements for fabrication, standard EN1090-2, table A.3 : EXC2		EXC2	
Execution Specification document nr 25019443-ICC250-0600-0660-000005		Fabrication tolerances EN 1090-2, Appendix B	
Surface preparation grade ISO8501-3, grade P2		Special fabrication tolerances Project specification/ shown on drwg.	
Surface treatment ISO12944-5		Weld inspection, requirements EN 1090-2, Table 24, U>0.5	
Additional requirements on surface treatment C3.07, EPPUR 240/2		Extent of NDT, fillet welds MT-EN1290, 20% of welds	
Shade RAL 7024 (Graphite Gray)		Extent of NDT, butt welds UT, EN-ISO17640, 20% of welds	
Welding of built up steel section Appendix 1 / Project spec.		Requirements on holing EN1090-2 Section 6.6.3	
Welds, if not specified otherwise EN 9692-1, EN 9692-2		Weld class C, EN ISO 5817	
		Additional material inspection Shown on drwg.	
		Approved For Construction	
		PROJECT NAME Easpring New Materials Oy FAIR Phase 1	
		DRAWING CONTENT ASSEMBLY DRAWING FRAME E51WF-1041	
		DATE 12.06.2026	
		ARCHIVING CODE	
		PAGE	
		DESIGN GROUP STR	
		DRAWN Alexey Serous	
		DESIGNER Alexey Serous	
		APPROVED Pertti Koivumaa	
		CHECKED Jere Kallosalmi	
		PROJECT NUMBER 25019443	
		DWS. NO. E51WF-1041	
		REVISION	



SWECO RAKENNETEKNIikka OY
ILMALANPORTTI 2
00240 HELSINKI
PUH. +358 207 393 000
www.sweco.fi

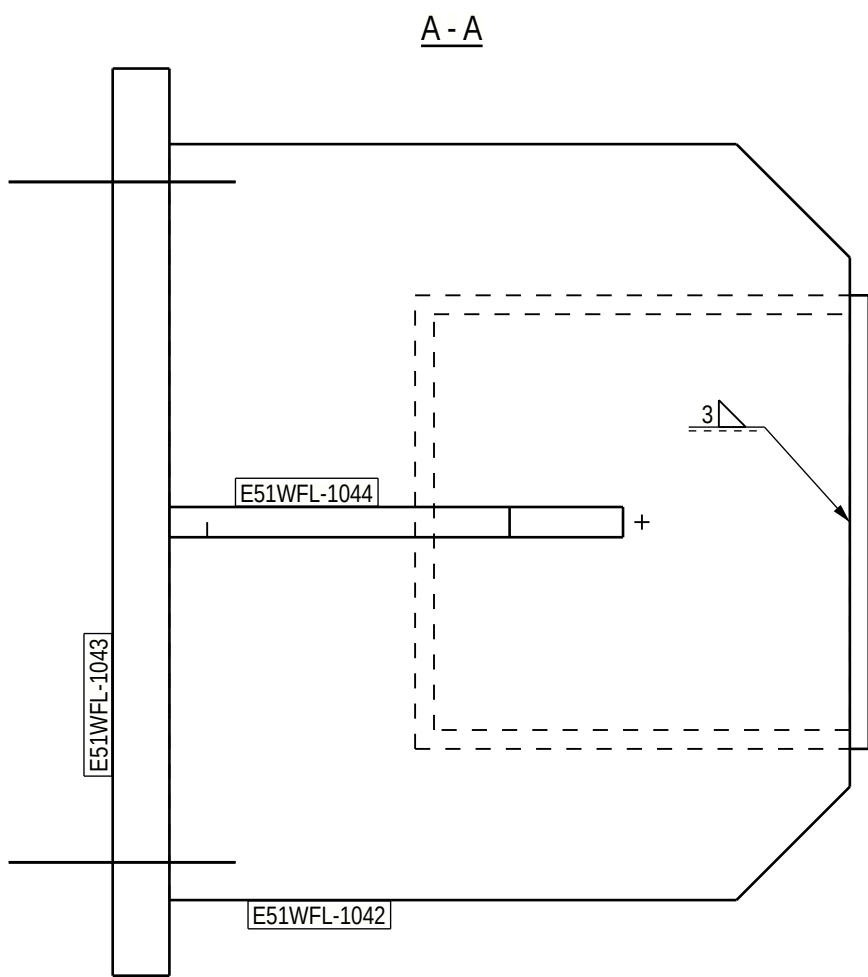


LIFTING LUG WELDING, WEIGHT < 1,5 t

Approved For Construction


SWECO 
Sustainable engineering and design

DRAWING CONTENT			
ASSEMBLY DRAWING			
FRAME			
E51WF-1042			
DATE 12.06.2026	ARCHIVING CODE	PAGE	DESIGN GROUP STR
DRAWN Alexey Serous	DESIGNER Alexey Serous	APPROVED Pertti Koivumaaanaho	CHECKED Jere Kalliosalmi
PROJECT NUMBER 25019443		DWG. NO. E51WF-1042	
		REVISION	

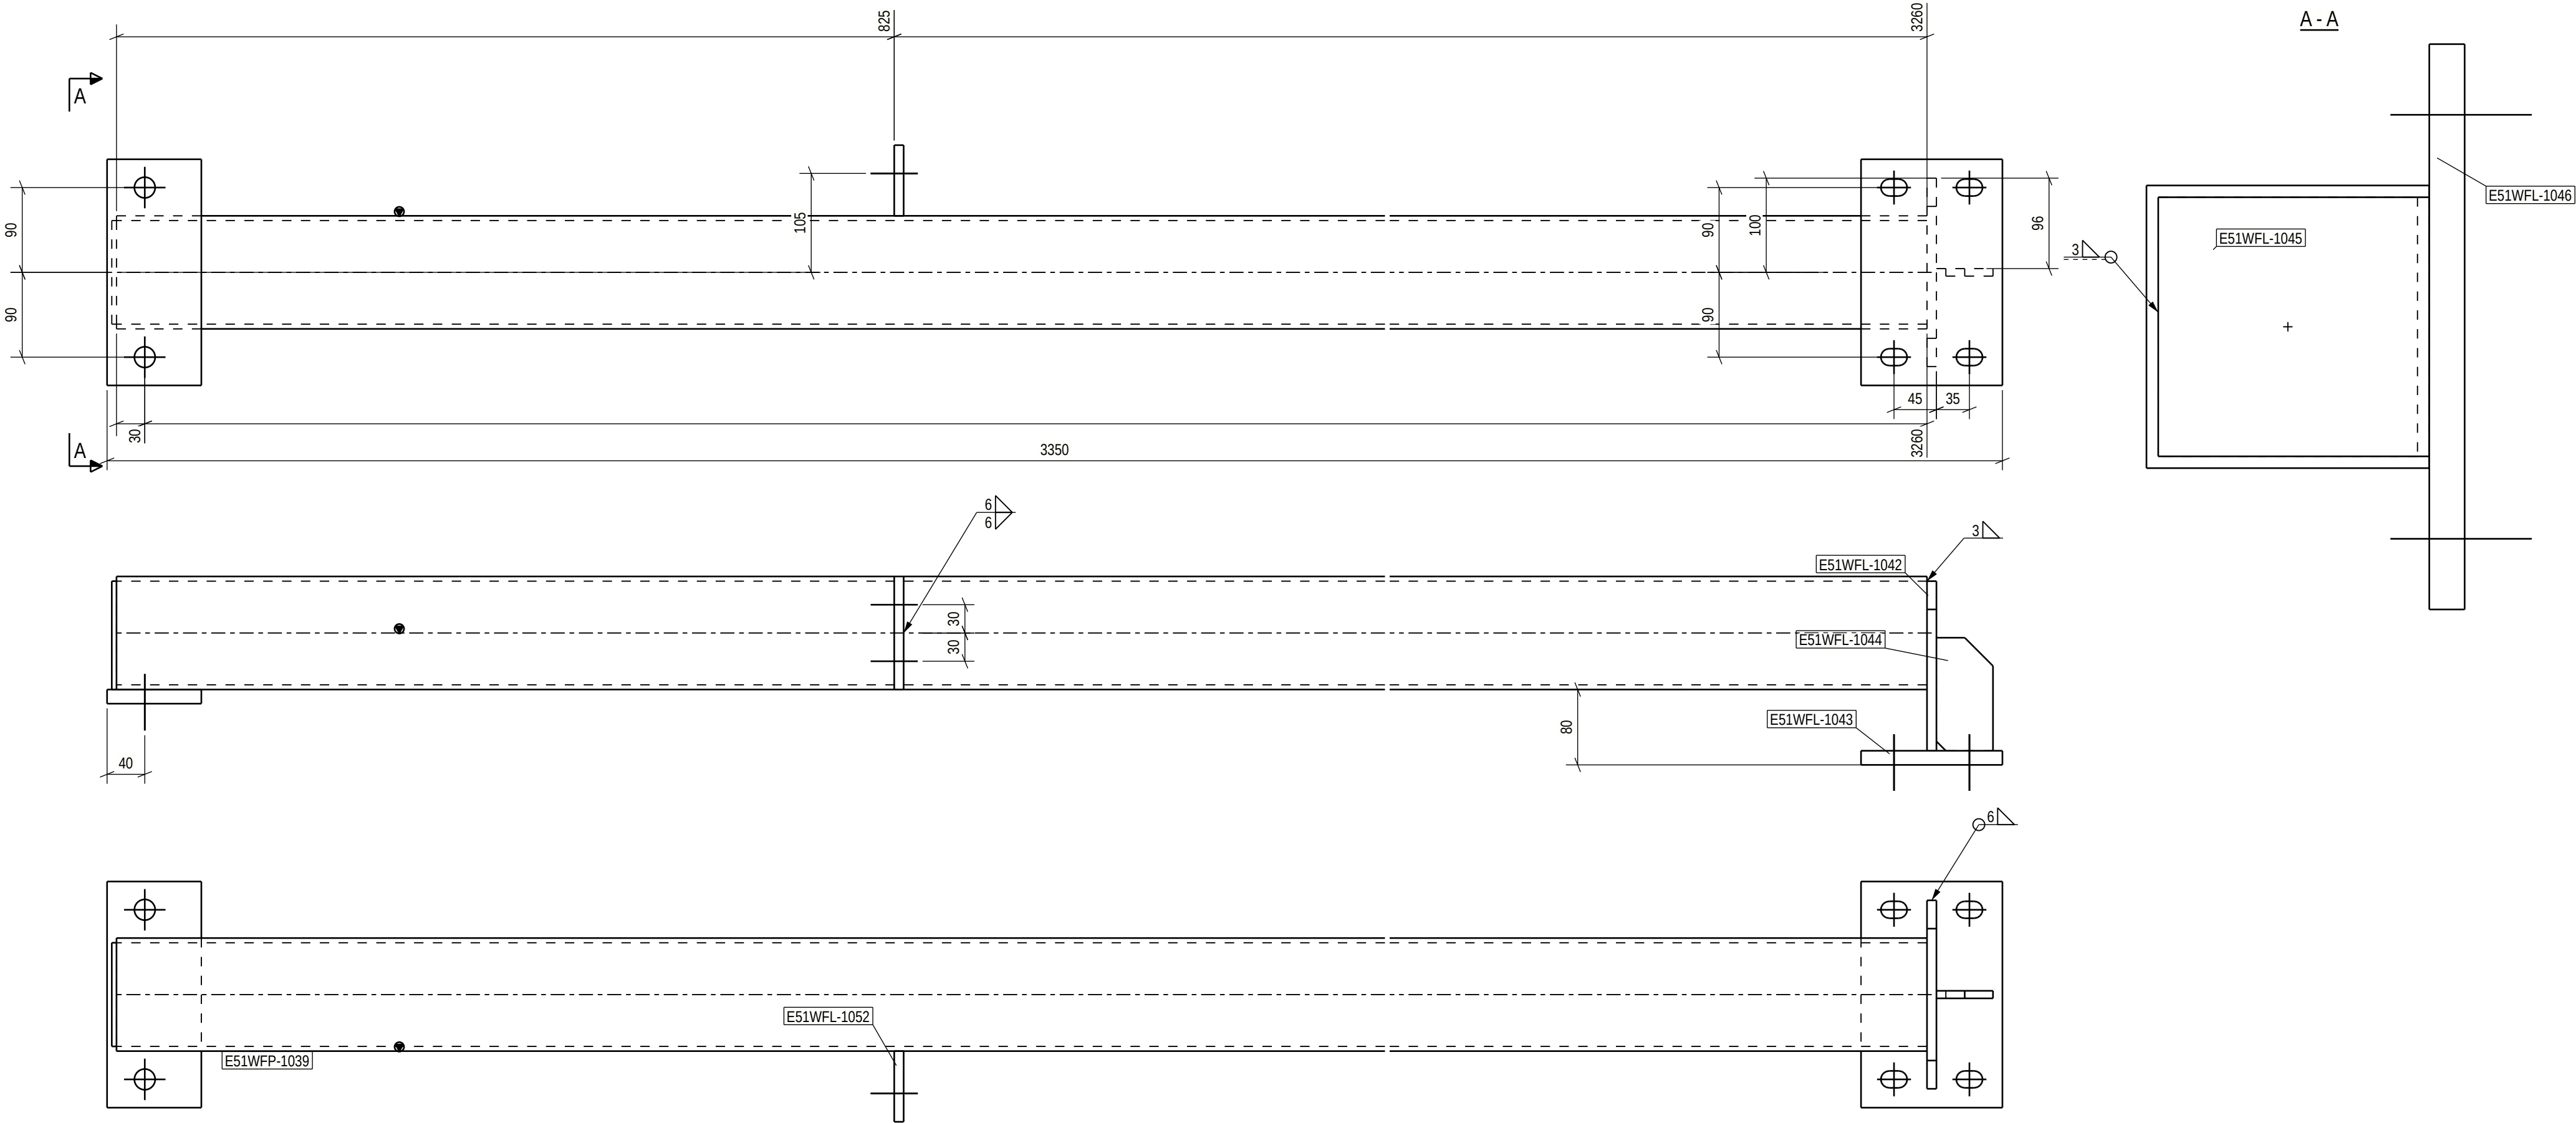

PART LIST FOR ASSEMBLY E51WF-1043, MANUFACTURING AMOUNT 1 PIECES						
PART	PROFILE	MATERIAL	LENGTH [mm]	AREA [m2]	WEIGHT [kg]	PCS
E51WFL-1042	PL10X200	S355J2+N	180	0.08	2.8	1
E51WFL-1043	PL15X150	S355J2+N	240	0.08	4.2	1
E51WFL-1044	PL8X60	S355J2+N	120	0.02	0.4	1
E51WFL-1045	PL5X110	S355J2+N	115	0.03	0.5	1
E51WFL-1046	PL15X100	S355J2+N	240	0.06	2.8	1
E51WFL-1052	PL10X75	S355J2+N	120	0.02	0.7	1
E51WFP-1039	CFRHS120X120X5	S355J2H	3260	1.51	57.2	1
TOTAL:				1.79	68.7	

LIFTING LUG WELDING, WEIGHT < 1,5 t

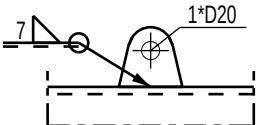

Technical fabrication requirements:

Requirements for fabrication, standard
EN1090-2, table A.3 : EXC2
Execution Specification document nr
25019443-ICC250-0600-0660-000005
Surface preparation grade
ISO8501-3, grade P2
Surface treatment
ISO12944-5
Additional requirements on surface treatment
C3.07, EPPUR 240/2
Shade
RAL 7024 (Graphite Gray)
Welding of built up steel section
Appendix 1 / Project spec.
Welds, if not specified otherwise
EN 9692-1, EN 9692-2

Fabrication tolerances
EN 1090-2, Appendix B
Special fabrication tolerances
Project specification/ shown on drwg.
Weld inspection, requirements
EN 1090-2, Table 24, U>0.5
Extent of NDT, fillet welds
MT-EN1290, 20% of welds
Extent of NDT, butt welds
UT, EN-ISO17640, 20% of welds
Extent of NDT for splices not shown on drawing
UT, EN-ISO17640, 100% of welds
Requirements on holing
EN1090-2 Section 6.6.3
Weld class
C, EN ISO 5817
Additional material inspection
Shown on drwg.

Execution class


EXC2

Approved For Construction

PROJECT NAME
Easpring New Materials Oy
FAIR Phase 1



SWECO
Sustainable engineering and design

SWECO RAKENNETEKNIikka OY
ILMALANPORTTI 2
00240 HELSINKI
PUH. +358 207 393 000
www.sweco.fi

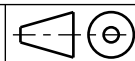


DRAWING CONTENT
ASSEMBLY DRAWING
FRAME
E51WF-1043

DATE	ARCHIVING CODE	PAGE	DESIGN GROUP
12.06.2026			STR
DRAWN	DESIGNER	APPROVED	CHECKED
Alexey Serous	Alexey Serous	Pertti Koivumaa	Jere Kallosalmi
PROJECT NUMBER	DWG. NO.	REVISION	
25019443	E51WF-1043		

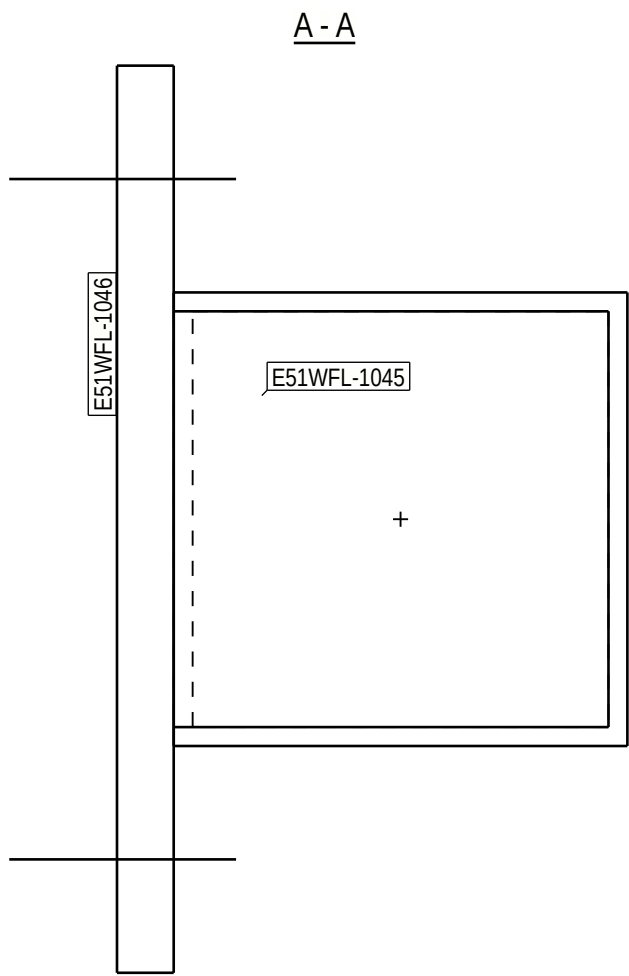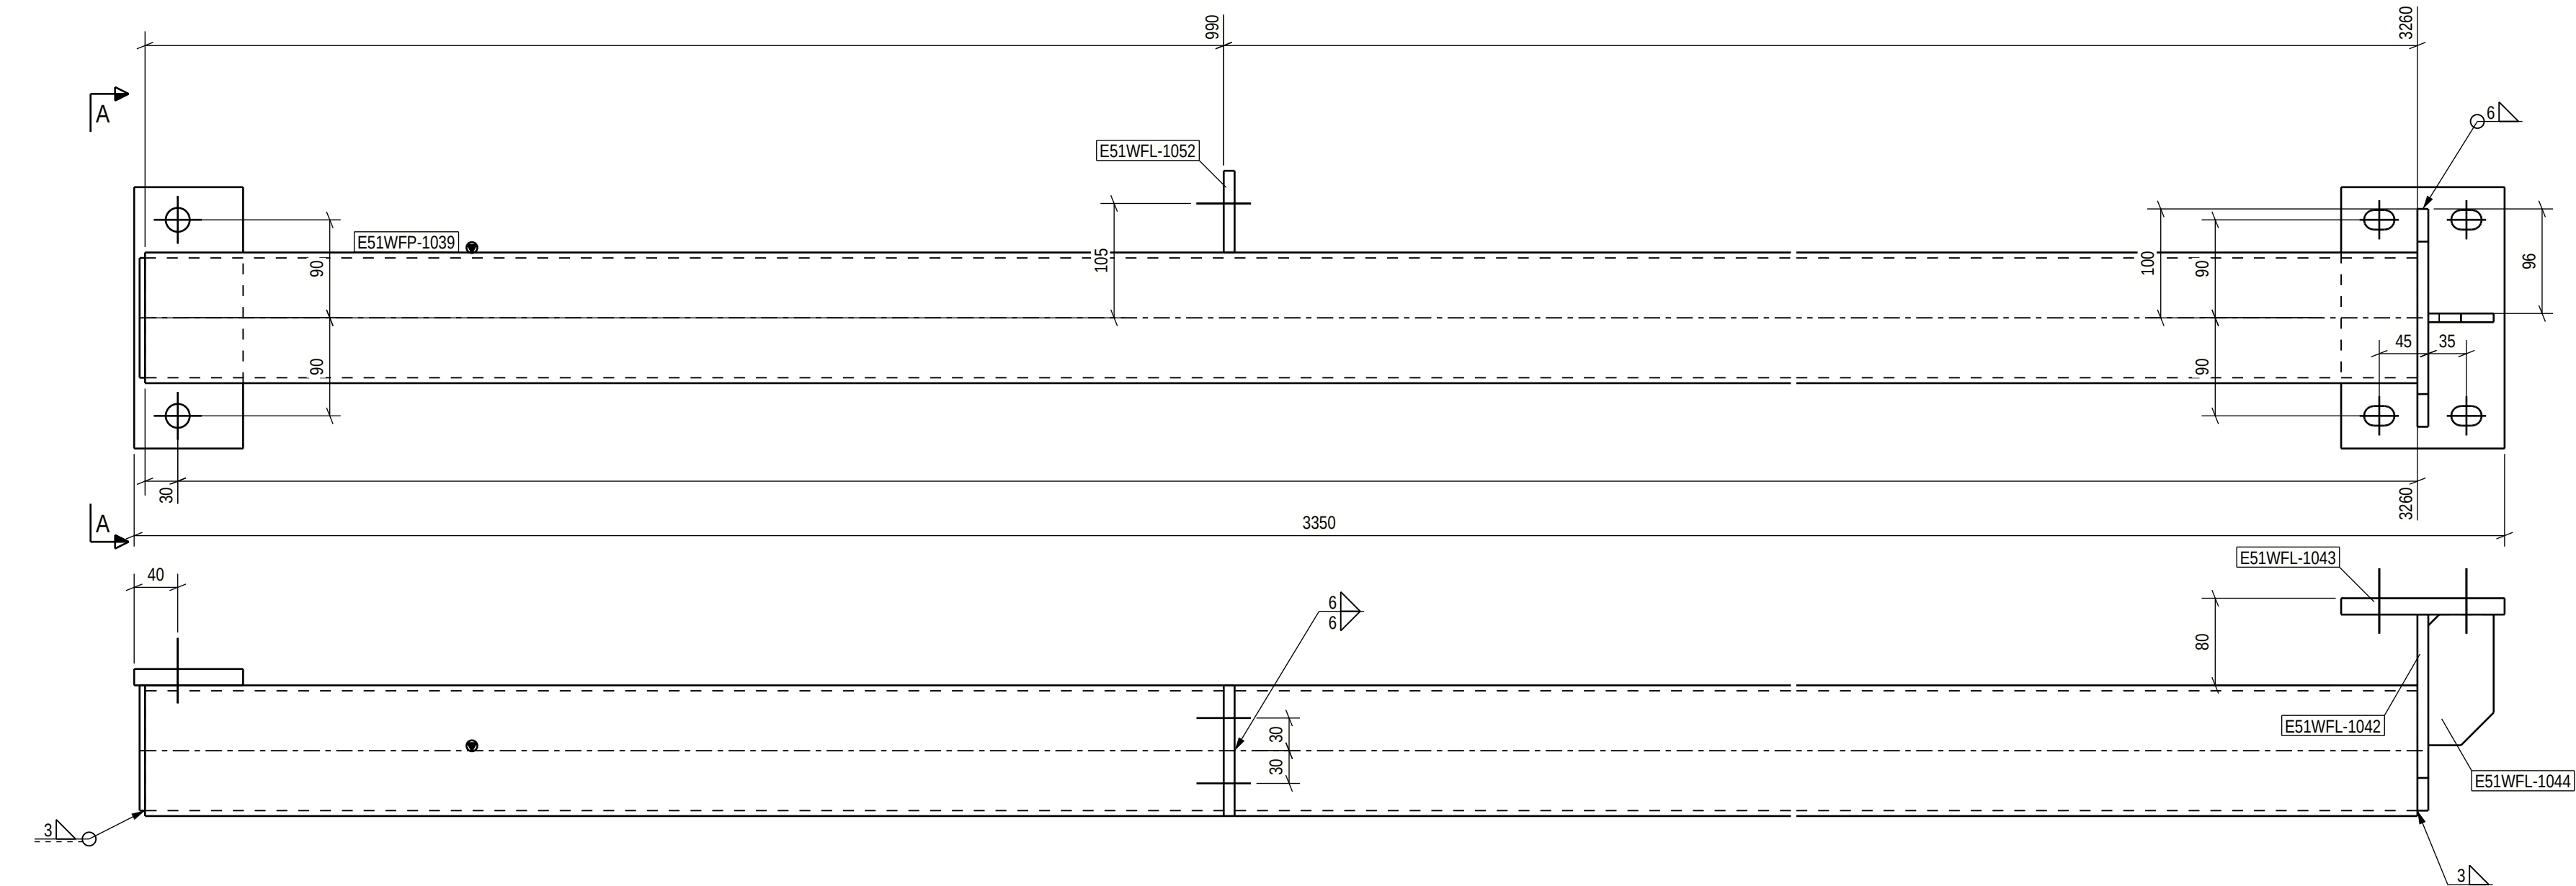

PART LIST FOR ASSEMBLY E51WF-1044, MANUFACTURING AMOUNT 1 PIECES						
PART	PROFILE	MATERIAL	LENGTH [mm]	AREA [m2]	WEIGHT [kg]	PCS
E51WFL-1042	PL10X200	S355J2+N	180	0.08	2.8	1
E51WFL-1043	PL15X150	S355J2+N	240	0.08	4.2	1
E51WFL-1044	PL8X60	S355J2+N	120	0.02	0.4	1
E51WFL-1045	PL5X110	S355J2+N	115	0.03	0.5	1
E51WFL-1046	PL15X100	S355J2+N	240	0.06	2.8	1
E51WFL-1052	PL10X75	S355J2+N	120	0.02	0.7	1
E51WFP-1039	CFRHS120X120X5	S355J2H	3260	1.51	57.2	1
TOTAL:				1.79	68.7	

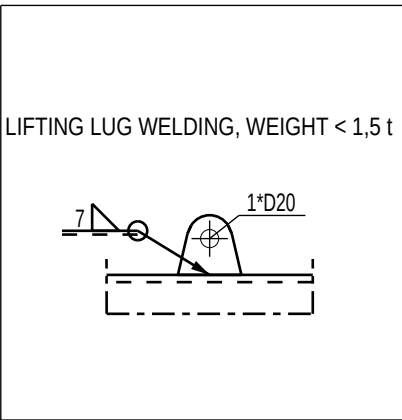


Technical fabrication requirements:		Execution class
Requirements for fabrication, standard EN1090-2, table A.3 : EXC2		EXC2
Execution Specification document nr 25019443-ICC250-0600-0660-000005		
Surface preparation grade ISO8501-3, grade P2		
Surface treatment ISO12944-5		
Additional requirements on surface treatment C3.07, EPPUR 240/2		
Shade RAL 7024 (Graphite Gray)		
Welding of built up steel section Appendix 1 / Project spec.		
Welds, if not specified otherwise EN 9692-1, EN 9692-2		
Fabrication tolerances EN 1090-2, Appendix B		
Special fabrication tolerances Project specification/ shown on drwg.		
Weld inspection, requirements EN 1090-2, Table 24, U>0.5		
Extent of NDT, fillet welds MT-EN1290, 20% of welds		
Extent of NDT, butt welds UT, EN-ISO17640, 20% of welds		
Requirements on holing EN1090-2 Section 6.6.3		
Weld class C, EN ISO 5817		
Additional material inspection Shown on drwg.		

Approved For Construction

PROJECT NAME
Easpring New Materials Oy
FAIR Phase 1




SWECO RAKENNETEKNIikka OY
ILMALANPORTTI 2
00240 HELSINKI
PUH. +358 207 393 000
www.sweco.fi

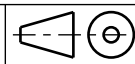

DRAWING CONTENT
ASSEMBLY DRAWING
FRAME
E51WF-1044

DATE	ARCHIVING CODE	PAGE	DESIGN GROUP
12.06.2026			STR
DRAWN	DESIGNER	APPROVED	CHECKED
Alexey Serous	Alexey Serous	Pertti Koivumaa	Jere Kallosalmi
PROJECT NUMBER	DWG. NO.	REVISION	
25019443	E51WF-1044		

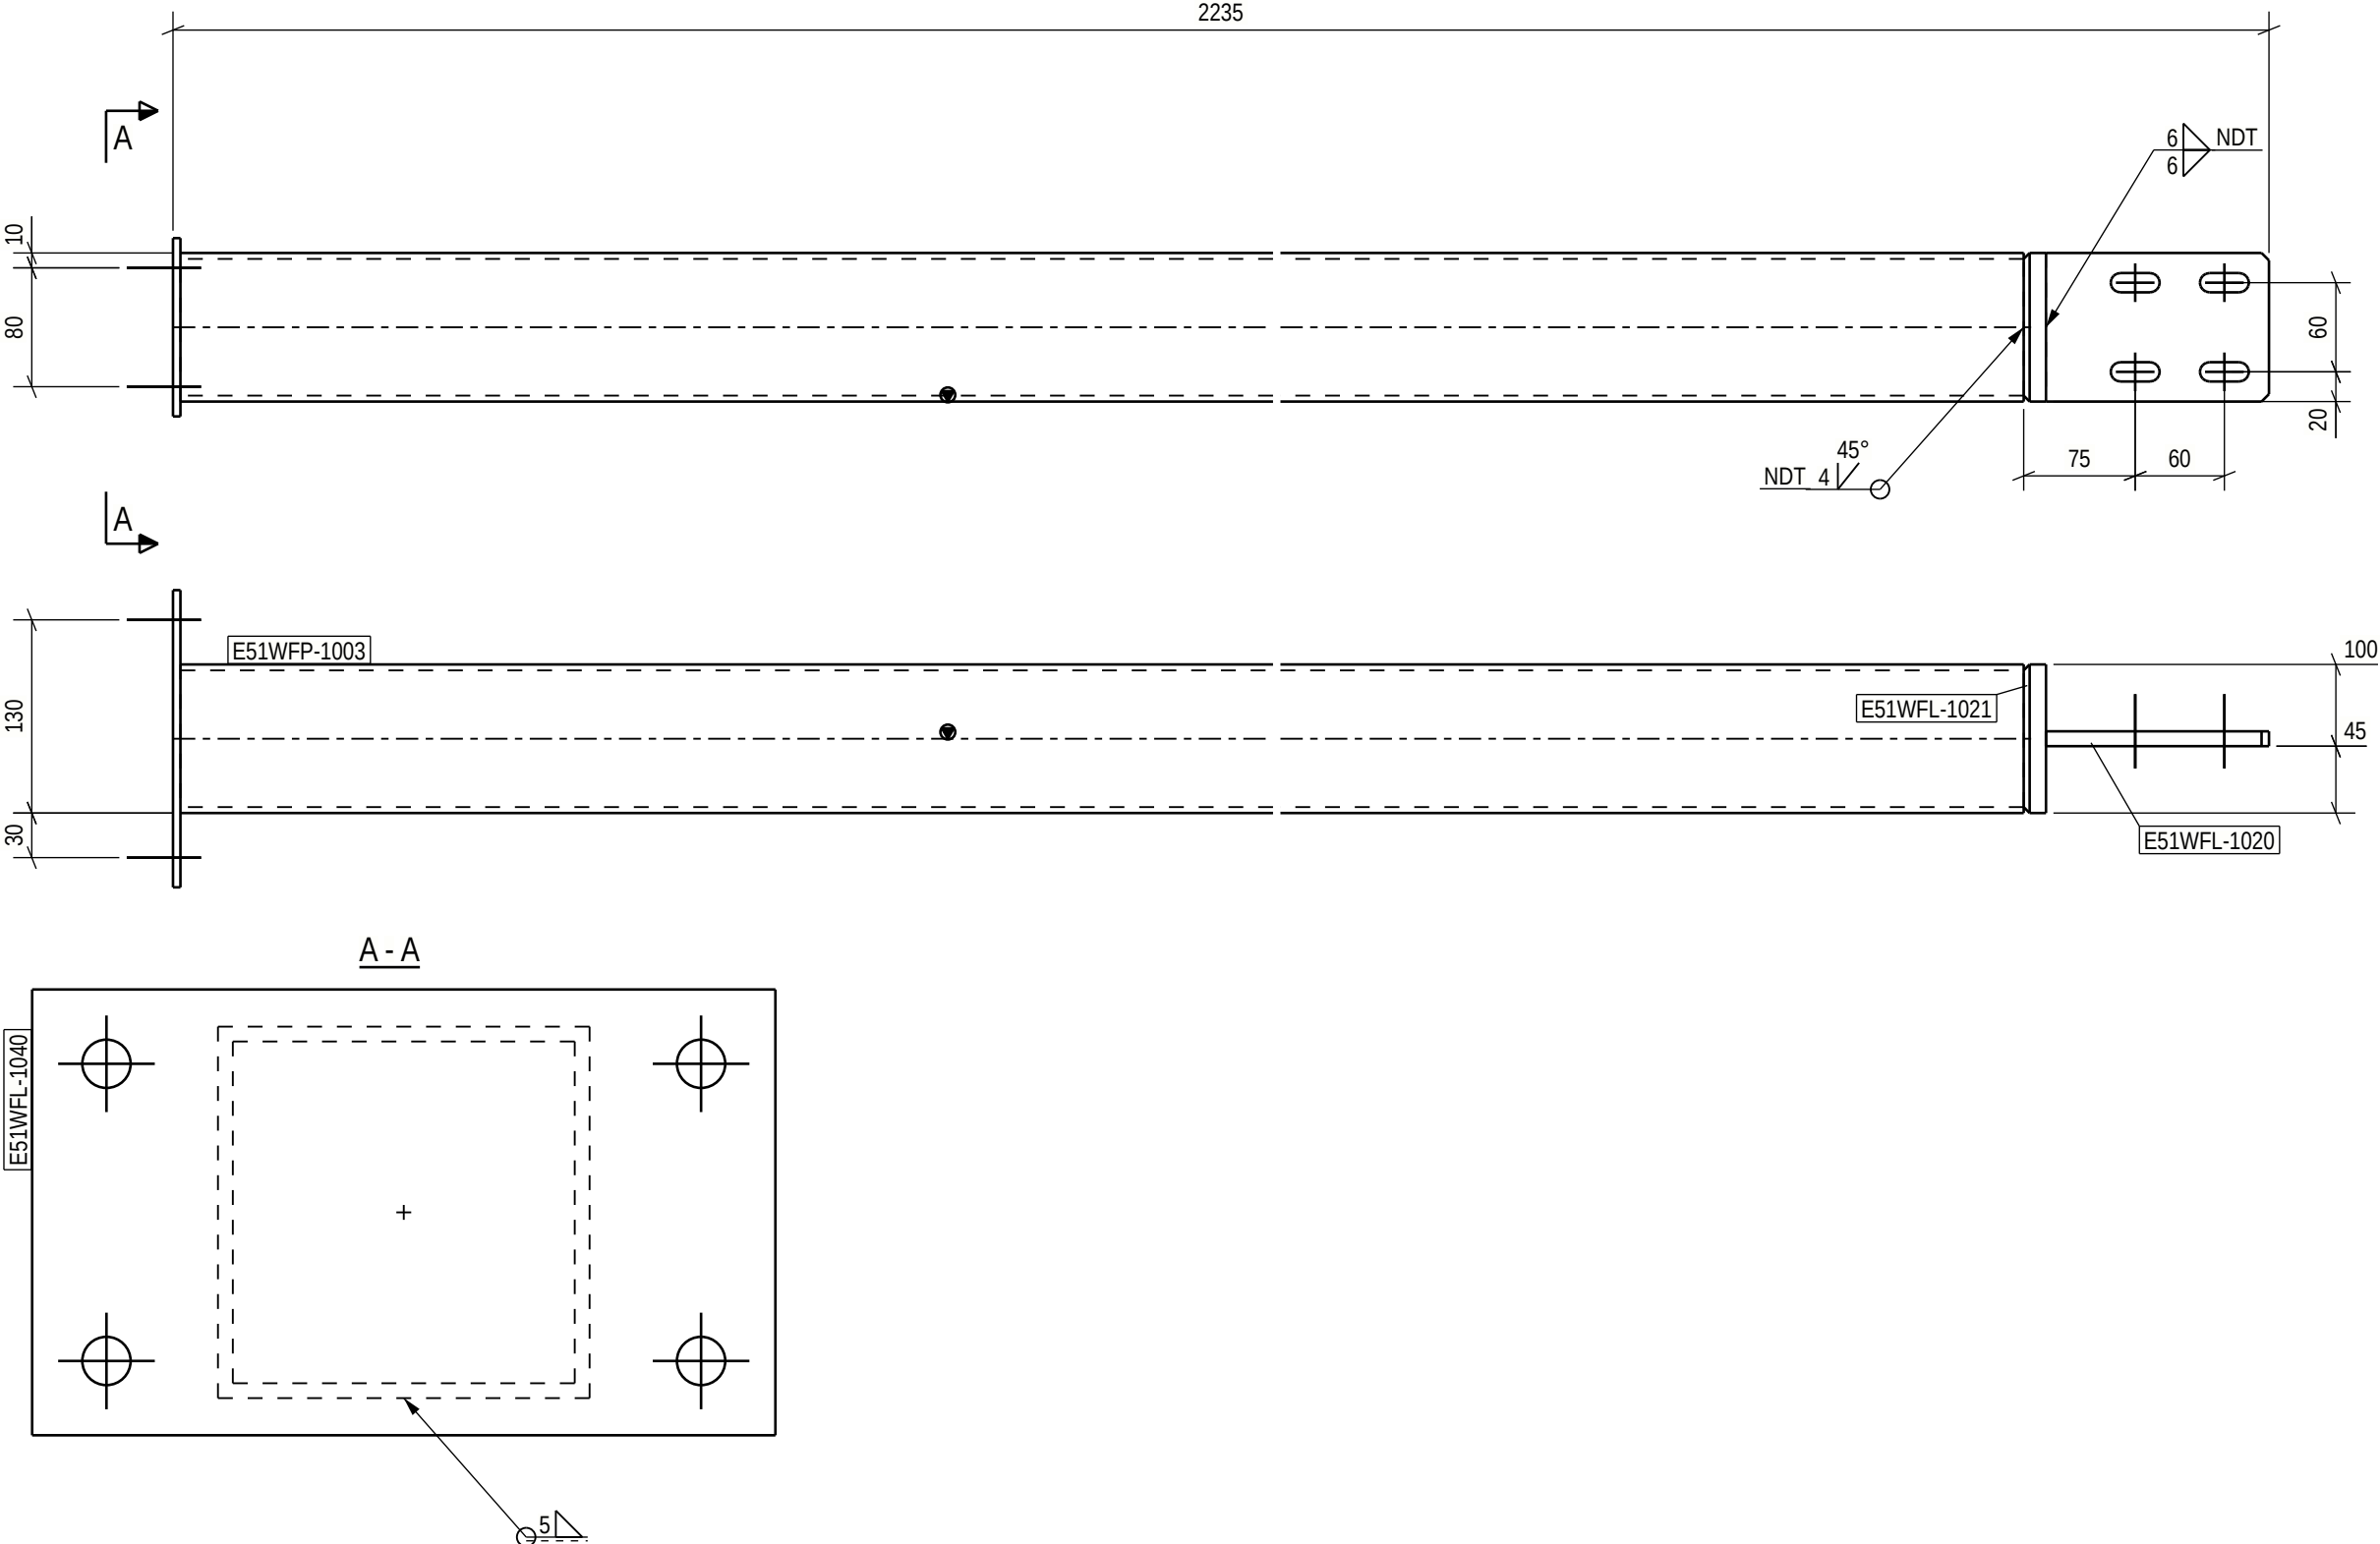





PART LIST FOR ASSEMBLY E51WF-1045, MANUFACTURING AMOUNT 1 PIECES						
PART	PROFILE	MATERIAL	LENGTH [mm]	AREA [m ²]	WEIGHT [kg]	PCS
E51WFL-1020	PL10X100	S355J2+N	150	0.03	1.2	1
E51WFL-1021	PL15X100	S355J2+N	100	0.03	1.2	1
E51WFL-1040	PL5X200	S355J2+N	120	0.05	0.9	1
E51WFP-1003	CFRHS100X100X4	S355J2H	2065	0.80	24.2	1
TOTAL:				0.91	27.5	

		Execution class	
Technical fabrication requirements:		EXC2	
Requirements for fabrication, standard EN1090-2, table A.3 : EXC2 Execution specification document nr 25019443-ICC250-0600-0660-000005 Surface preparation grade ISO8501-3, grade P2 Surface treatment ISO12944-5 Additional requirements on surface treatment C3.07, EPPUR 240/2 Shade RAL 7024 (Graphite Gray) Welding of built up steel section Appendix 1 / Project spec. Welds, if not specified otherwise EN 9692-1, EN 9692-2		Fabrication tolerances EN 1090-2, Appendix B Special fabrication tolerances Project specification/ shown on drwg. Weld inspection, requirements EN 1090-2, Table 24, U>0.5 Extent of NDT, fillet welds MT-EN1290, 20% of welds Extent of NDT, butt welds UT, EN-ISO17640, 20% of welds Extent of NDT for splices not shown on drawing UT, EN-ISO17640, 100% of welds Requirements on holing EN1090-2 Section 6.6.3 Weld class C, EN ISO 5817	
		Additional material inspection Shown on drawing	

For special tolerances of bolt hole location
see specification for steel structures


Approved For Construction

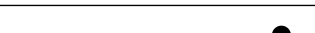PROJECT NAME				DRAWING CONTENT				
Easpring New Materials Oy FAIR Phase 1				ASSEMBLY DRAWING FRAME E51WF-1045				
 SWECO Sustainable engineering and design		SWECO RAKENNETEKNIIKKA OY ILMALANPORTTI 2 00240 HELSINKI		DATE 12.06.2026	ARCHIVING CODE	PAGE	DESIGN GROUP STR	
		PUH. +358 207 393 000 www.sweco.fi		DRAWN Alexey Serous	DESIGNER Alexey Serous	APPROVED Pertti Koivumaaanaho	CHECKED Jere Kalliosalmi	
				PROJECT NUMBER 25019443	DWG. NO. E51WF-1045		REVISION	

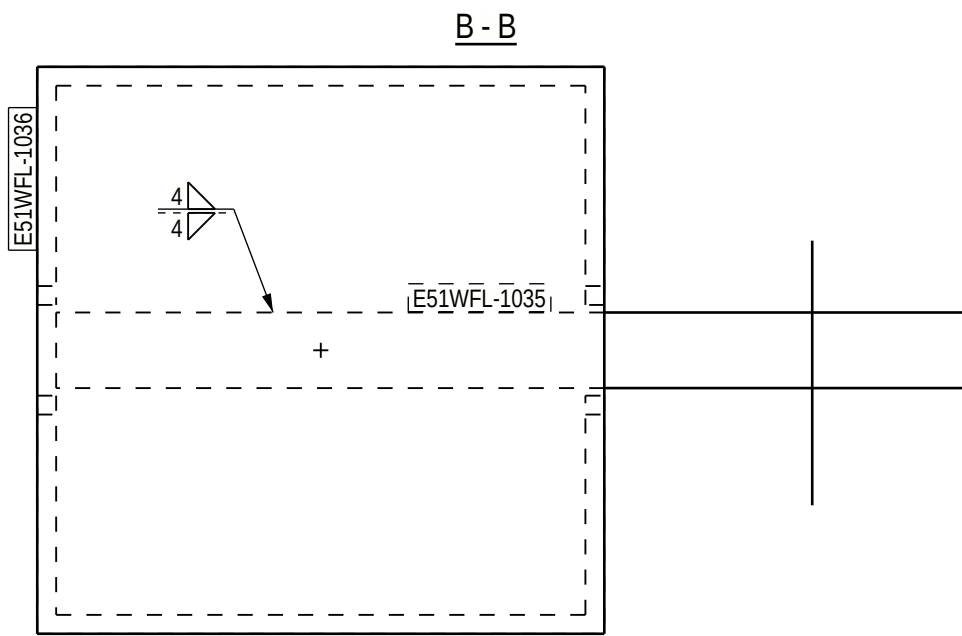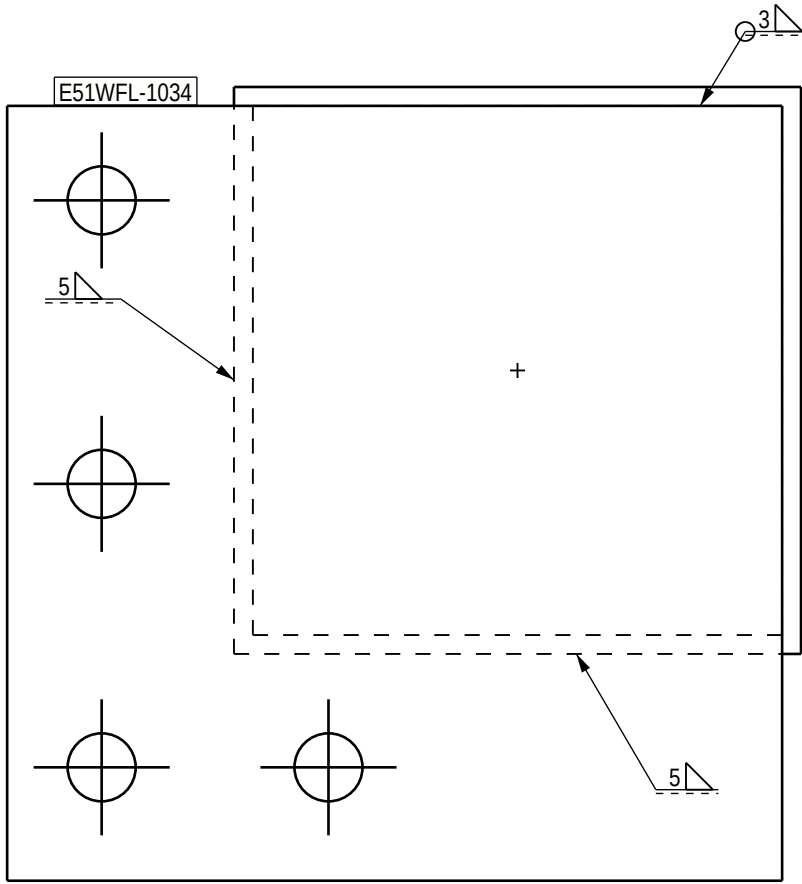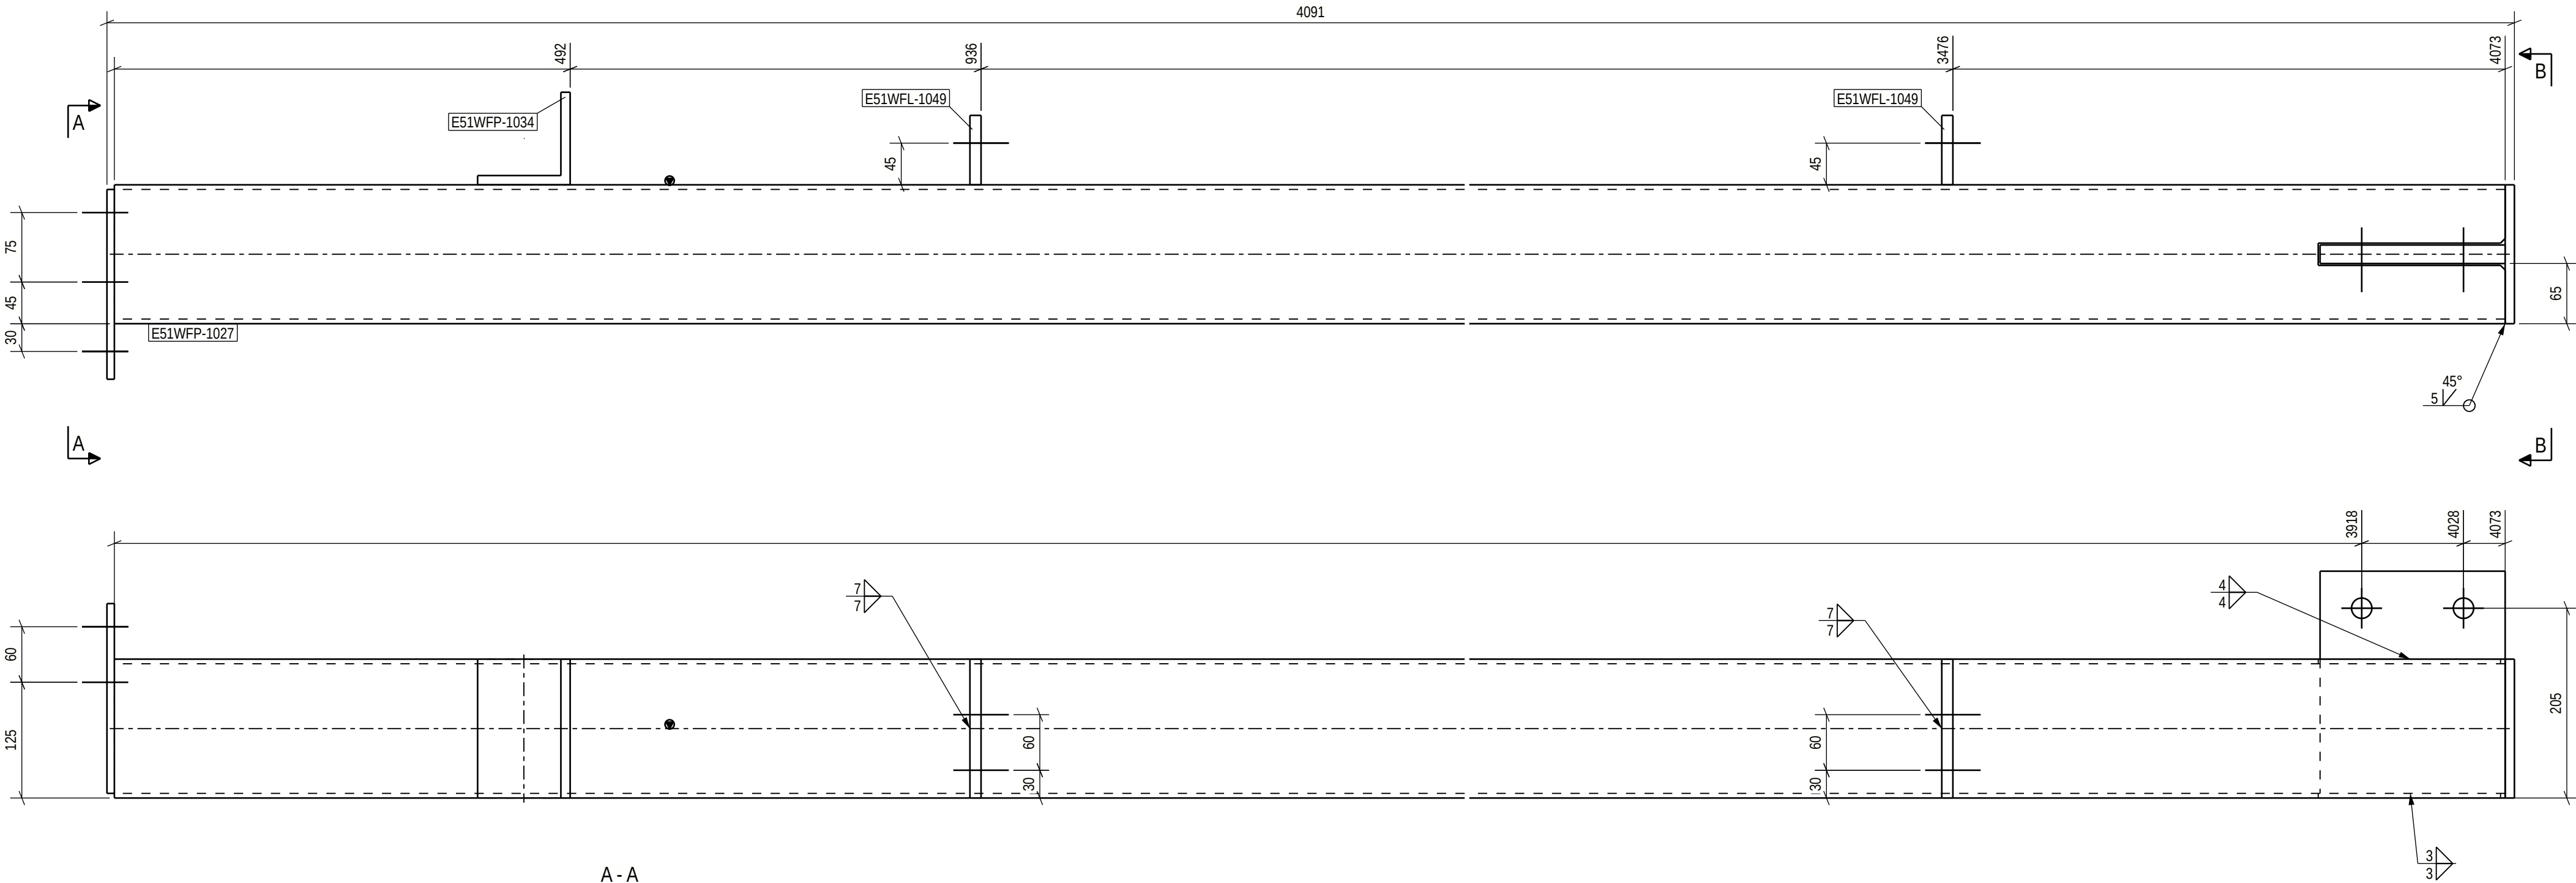

PART LIST FOR ASSEMBLY E51WF-1046, MANUFACTURING AMOUNT 1 PIECES						
PART	PROFILE	MATERIAL	LENGTH [mm]	AREA [m ²]	WEIGHT [kg]	PCS
E51WFL-1034	PL8X205	S355J2+N	205	0.09	2.6	1
E51WFL-1035	PL20X200	S355J2+N	240	0.11	7.5	1
E51WFL-1036	PL10X150	S355J2+N	150	0.05	1.8	1
E51WFL-1049	PL12X75	S355J2+N	150	0.06	1.1	2
E51WFP-1027	CFRHS150X150X5	S355J2H	4073	2.37	90.7	1
E51WFP-1034	L100*10	S355J2	150	0.06	2.3	1
TOTAL:				2.74	107.0	

LIFTING LUG WELDING, WEIGHT < 1,5 t

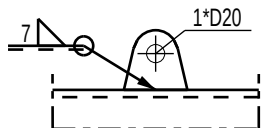


Technical fabrication requirements:		Execution class
Requirements for fabrication, standard EN1090-2, table A.3 : EXC2		EXC2
Execution Specification document nr 25019443-ICC250-0600-0660-000005		Approved For Construction
Surface preparation grade ISO8501-3, grade P2		
Surface treatment ISO12944-5		
Additional requirements on surface treatment C3.07, EPPUR 240/2		
Shade RAL 7024 (Graphite Gray)		
Welding of built up steel section Appendix 1 / Project spec.		
Welds, if not specified otherwise EN 9692-1, EN 9692-2		
Fabrication tolerances EN 1090-2, Appendix B		
Special fabrication tolerances Project specification/ shown on drwg.		
Weld inspection, requirements EN 1090-2, Table 24, U>0.5		
Extent of NDT, fillet welds MT-EN1290, 20% of welds		
Extent of NDT, butt welds UT, EN-ISO17640, 20% of welds		
Requirements on holing EN1090-2 Section 6.6.3		
Weld class C, EN ISO 5817		
Additional material inspection Shown on drwg.		

Approved For Construction

Easpring New Materials Oy
FAIR Phase 1




SWECO RAKENNETEKNIikka OY
ILMALANPORTTI 2
00240 HELSINKI
PUH. +358 207 393 000
www.sweco.fi

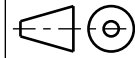


DRAWING CONTENT
ASSEMBLY DRAWING
FRAME
E51WF-1046

DATE	ARCHIVING CODE	PAGE	DESIGN GROUP
12.06.2026			STR
DRAWN	DESIGNER	APPROVED	CHECKED
Alexey Serous	Alexey Serous	Pertti Koivumaa	Jere Kallosalmi
PROJECT NUMBER		DWG. NO.	REVISION
25019443		E51WF-1046	

PART LIST FOR ASSEMBLY E51WF-1047, MANUFACTURING AMOUNT 4 PIECES						
PART	PROFILE	MATERIAL	LENGTH [mm]	AREA [m2]	WEIGHT [kg]	PCS
E51WFL-1051	PL15X120	S355J2+N	120	0.07	1.6	2
E51WFL-1053	PL10X75	S355J2+N	120	0.04	0.7	2
E51WFP-1041	CFRHS120X120X5	S355J2H	2210	1.02	38.8	1
TOTAL:				1.14	43.5	

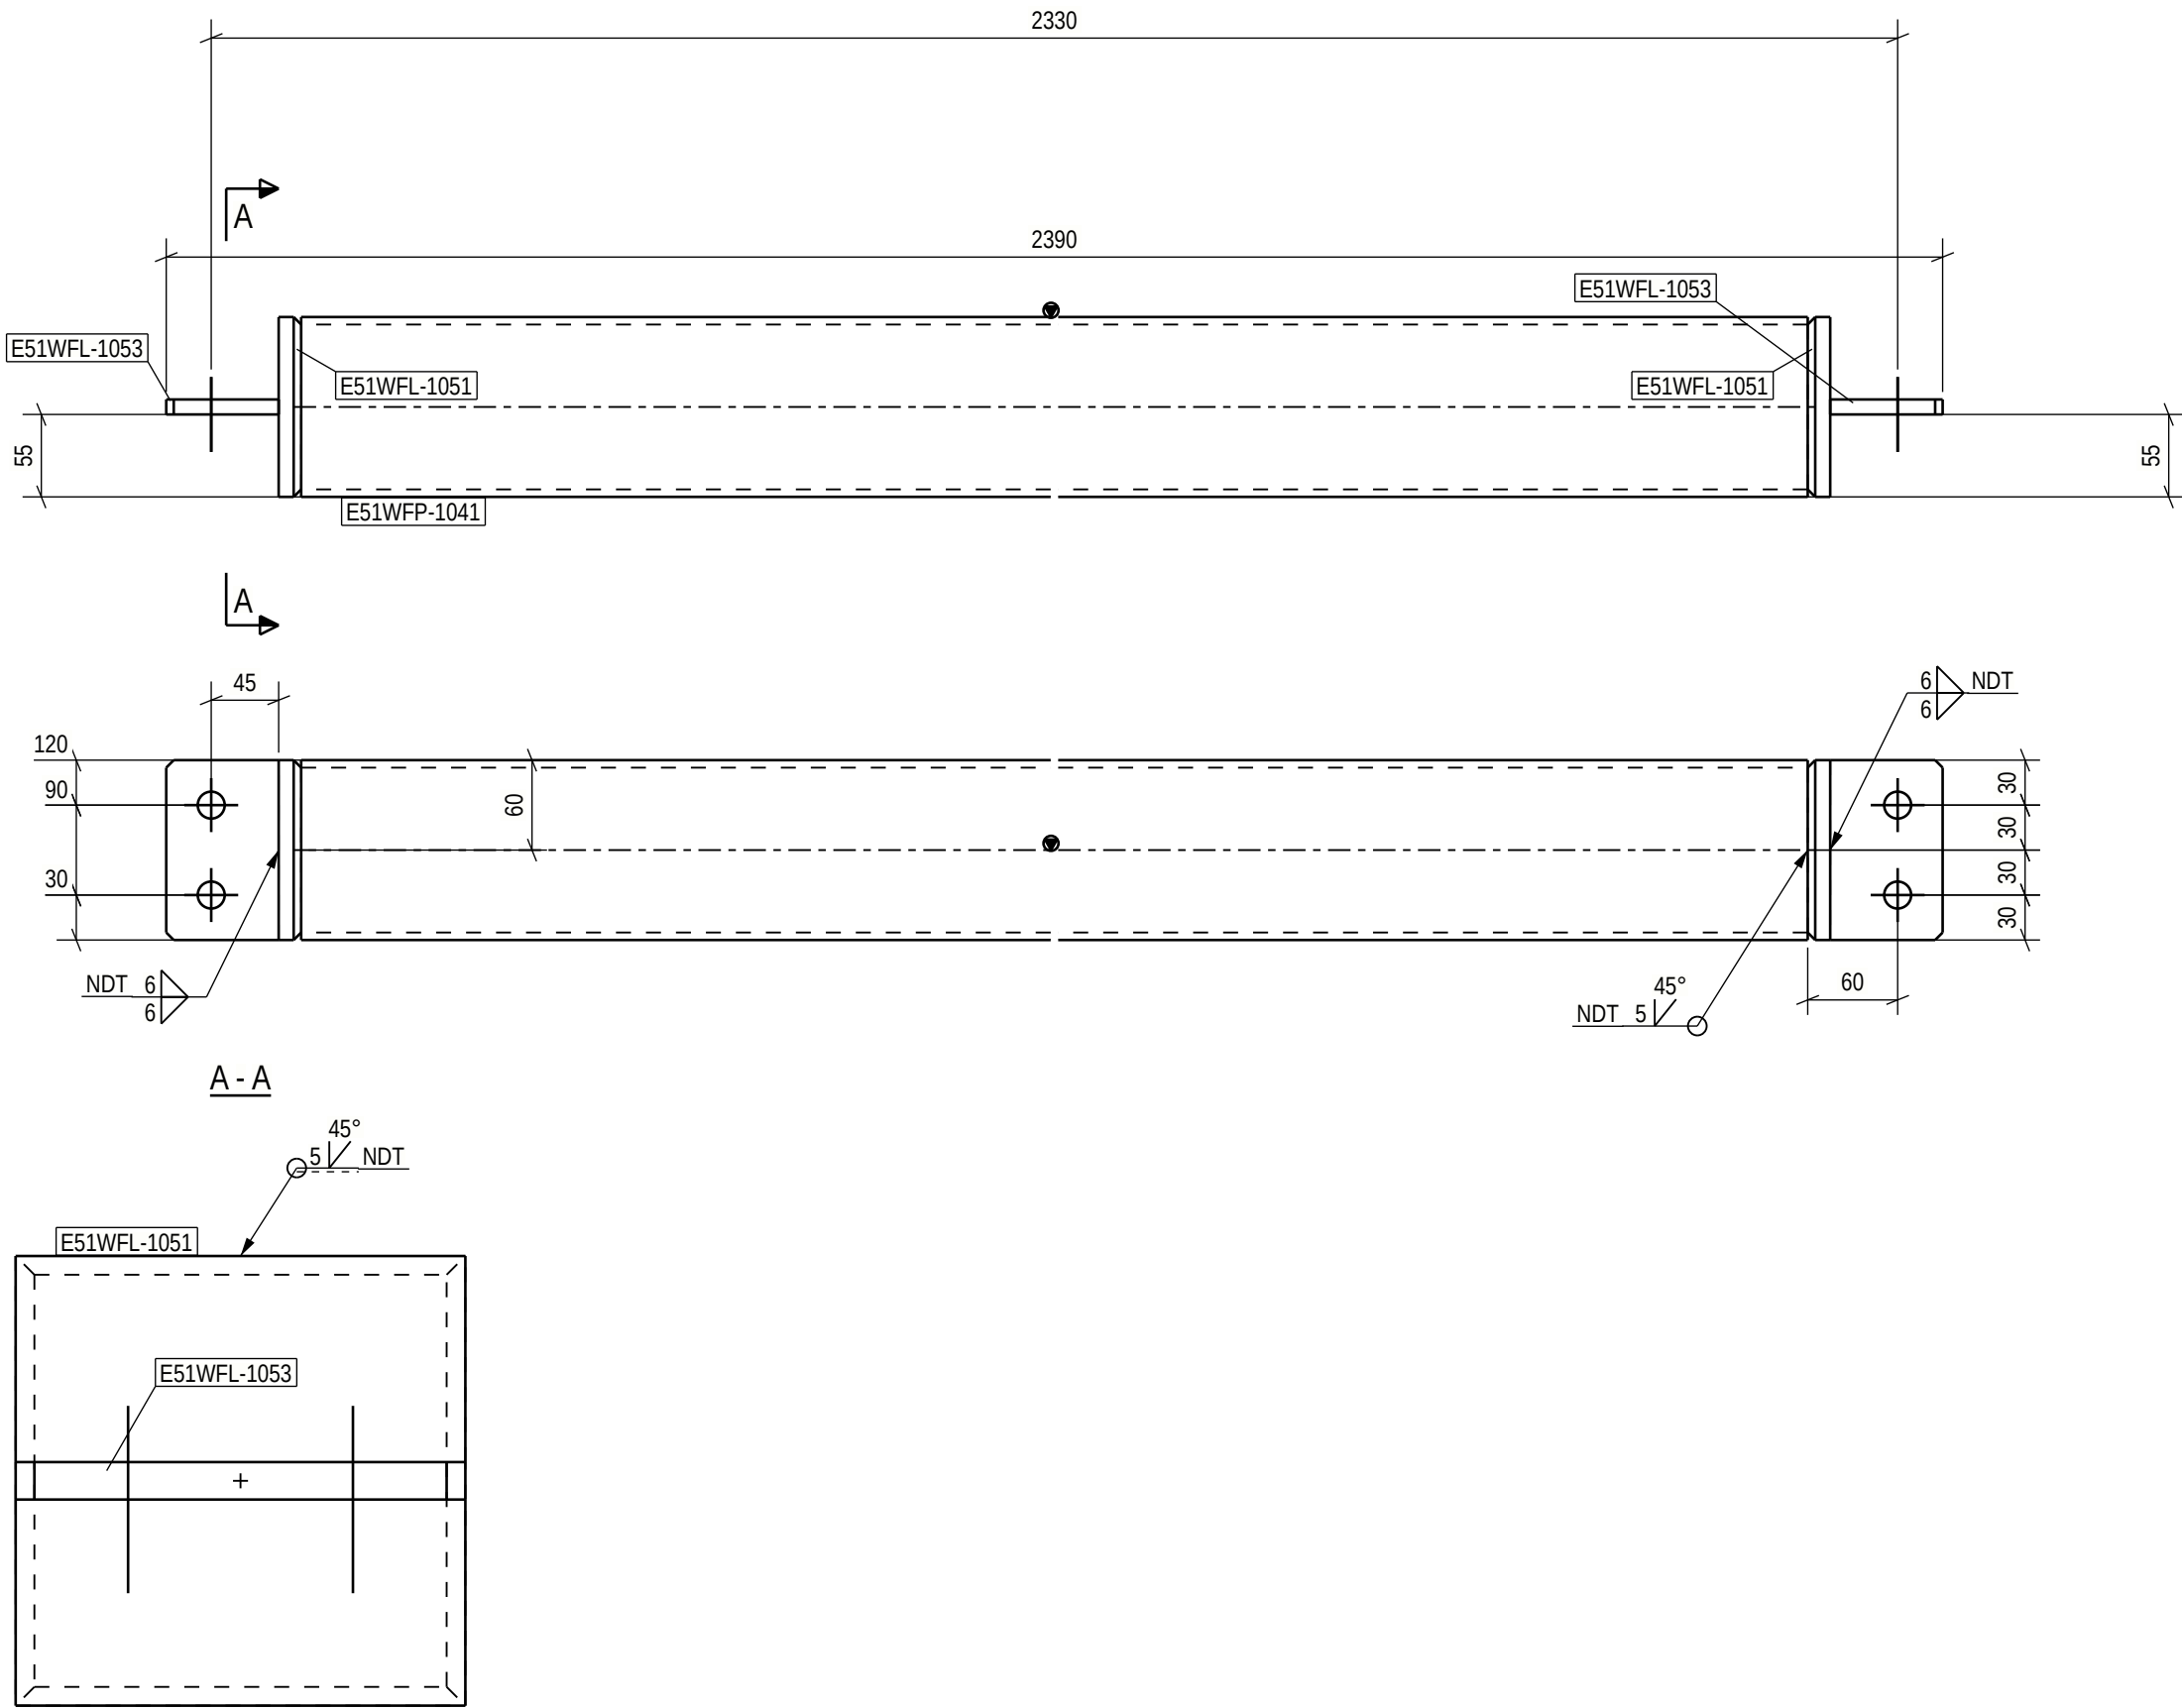

LIFTING LUG WELDING, WEIGHT < 1,5 t

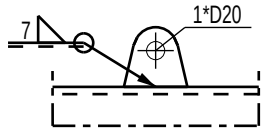


Technical fabrication requirements:		Execution class	
Requirements for fabrication, standard EN1090-2, table A.3 : EXC2		EXC2	
Execution Specification document nr 25019443-ICC250-0600-0660-000005		Fabrication tolerances EN 1090-2, Appendix B	
Surface preparation grade ISO8501-3, grade P2		Special fabrication tolerances Project specification/ shown on drwg.	
Surface treatment ISO12944-5		Weld inspection, requirements EN 1090-2, Table 24, U>0.5	
Additional requirements on surface treatment C3.07, EPPUR 240/2		Extent of NDT, fillet welds MT-EN1290, 20% of welds	
Shade RAL 7024 (Graphite Gray)		Extent of NDT, butt welds UT, EN-ISO17640, 20% of welds	
Welding of built up steel section Appendix 1 / Project spec.		Requirements on holing EN1090-2 Section 6.6.3	
Welds, if not specified otherwise EN 9692-1, EN 9692-2		Weld class C, EN ISO 5817	
		Additional material inspection Shown on drwg.	


PROJECT NAME		DRAWING CONTENT	
Easpring New Materials Oy		ASSEMBLY DRAWING	
FAIR Phase 1		FRAME	
		E51WF-1047	

DATE		ARCHIVING CODE		PAGE		DESIGN GROUP	
12.06.2026						STR	
DRAWN		DESIGNER		APPROVED		CHECKED	
Alexey Serous		Alexey Serous		Pertti Koivumaaanaho		Jere Kallosalmi	
PROJECT NUMBER		DWS. NO.		REVISION			
25019443						E51WF-1047	

SWECO		SWEKO RAKENNETEKNIikka OY	
Sustainable engineering and design		ILMALANPORTTI 2	
		00240 HELSINKI	
		PUH. +358 207 393 000	
		www.sweco.fi	

Approved For Construction

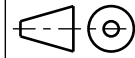

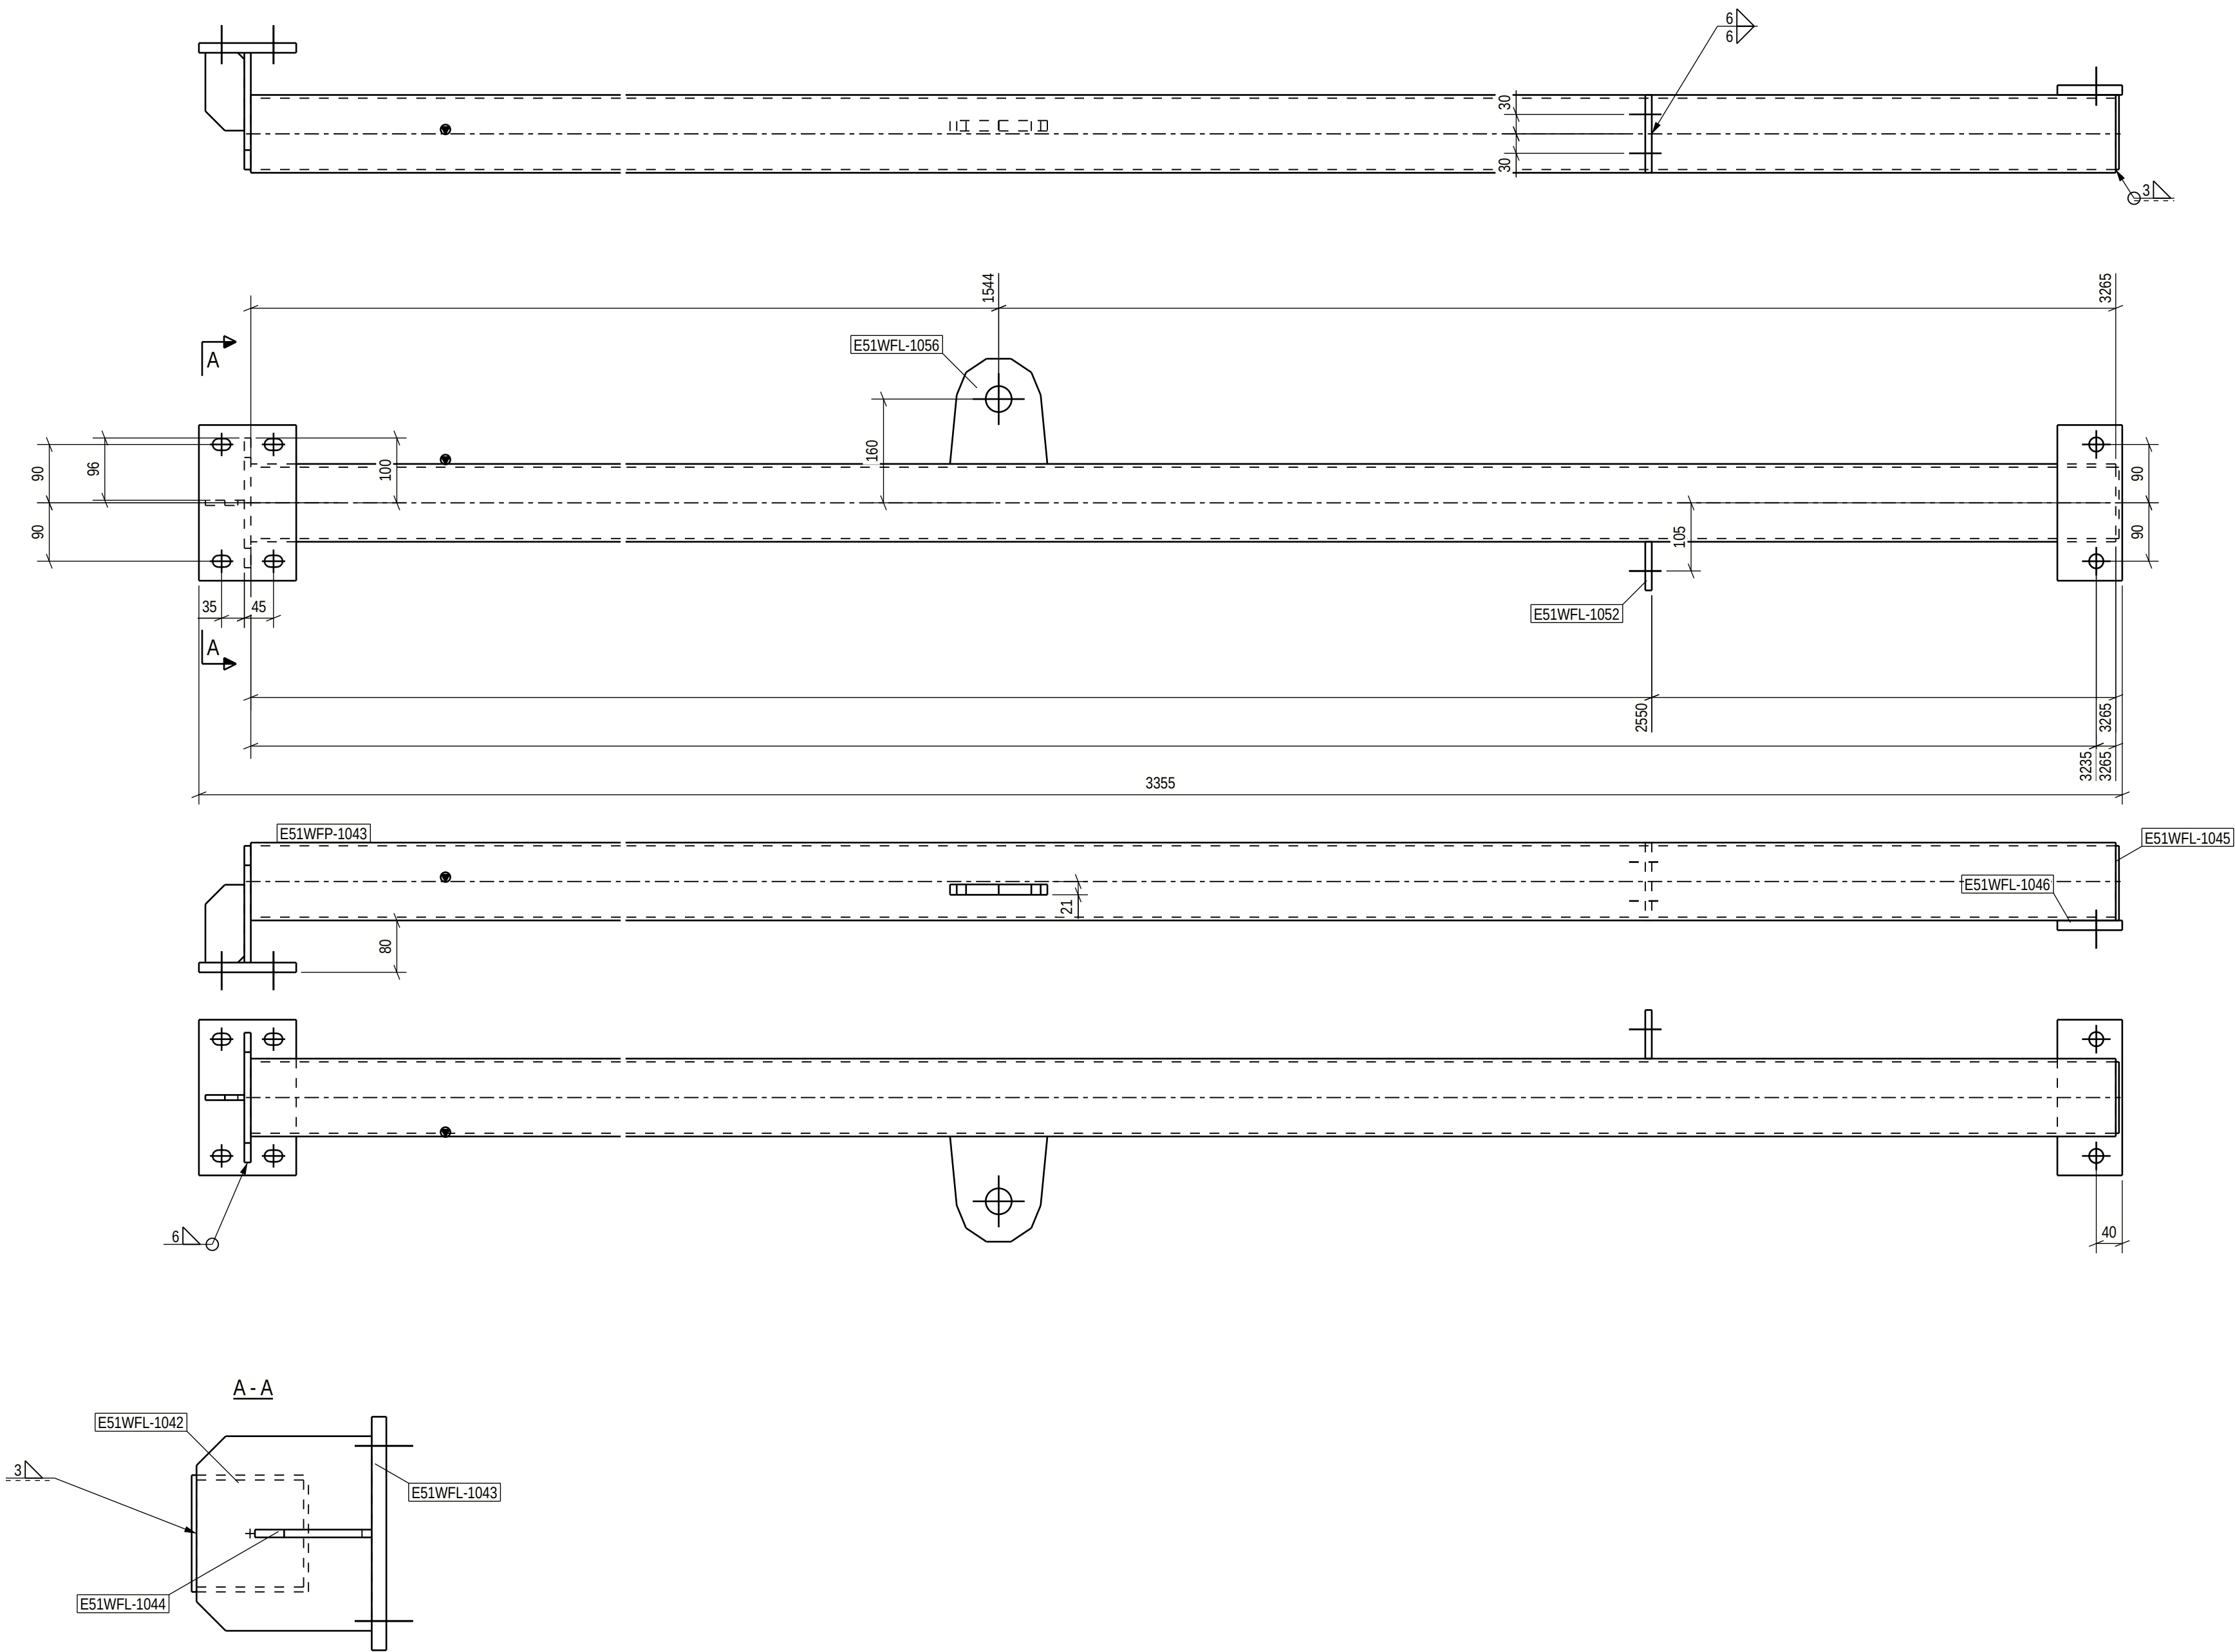

PART LIST FOR ASSEMBLY E51WF-1048, MANUFACTURING AMOUNT 1 PIECES						
PART	PROFILE	MATERIAL	LENGTH [mm]	AREA [m2]	WEIGHT [kg]	PCS
E51WFL-1042	PL10X200	S355J2+N	180	0.08	2.8	1
E51WFL-1043	PL15X150	S355J2+N	240	0.08	4.2	1
E51WFL-1044	PL8X60	S355J2+N	120	0.02	0.4	1
E51WFL-1045	PL5X110	S355J2+N	115	0.03	0.5	1
E51WFL-1046	PL15X100	S355J2+N	240	0.06	2.8	1
E51WFL-1052	PL10X75	S355J2+N	120	0.02	0.7	1
E51WFL-1056	PL16X162	S355J2	150	0.05	2.6	1
E51WFP-1043	CFRHS120X120X5	S355J2H	3265	1.51	57.3	1
TOTAL:				1.85	71.3	

LIFTING LUG WELDING, WEIGHT < 1,5 t

Technical fabrication requirements:

Execution class

EXC2


Requirements for fabrication, standard EN1090-2, table A.3 : EXC2	Fabrication tolerances EN 1090-2, Appendix B
Execution Specification document nr 25019443-ICC250-0600-0660-000005	Special fabrication tolerances Project specification/ shown on drwg.
Surface preparation grade ISO8501-3, grade P2	Weld inspection, requirements EN 1090-2, Table 24, U>0.5
Surface treatment ISO12944-5	Extent of NDT, fillet welds MT-EN1290, 20% of welds
Additional requirements on surface treatment C3.07, EPPUR 240/2	Extent of NDT, butt welds UT, EN-ISO17640, 20% of welds
Shade RAL 7024 (Graphite Gray)	Extent of NDT for splices not shown on drawing UT, EN-ISO17640, 100% of welds
Welding of built up steel section Appendix 1 / Project spec.	Requirements on holing EN1090-2 Section 6.6.3
Welds, if not specified otherwise EN 9692-1, EN 9692-2	Weld class C, EN ISO 5817
	Additional material inspection Shown on drwg.

Approved For Construction

PROJECT NAME
Easpring New Materials Oy
FAIR Phase 1





SWECO RAKENNETEKNIikka OY
ILMALANPORTTI 2
00240 HELSINKI
PUH. +358 207 393 000
www.sweco.fi

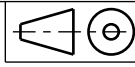


DRAWING CONTENT
ASSEMBLY DRAWING
FRAME
E51WF-1048

DATE	ARCHIVING CODE	PAGE	DESIGN GROUP
12.06.2026			STR
DRAWN	DESIGNER	APPROVED	CHECKED
Alexey Serous	Alexey Serous	Pertti Koivumaa	Jere Kallosalmi
PROJECT NUMBER	DWG. NO.	REVISION	
25019443	E51WF-1048		

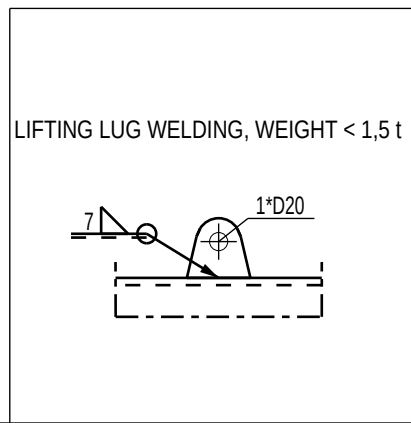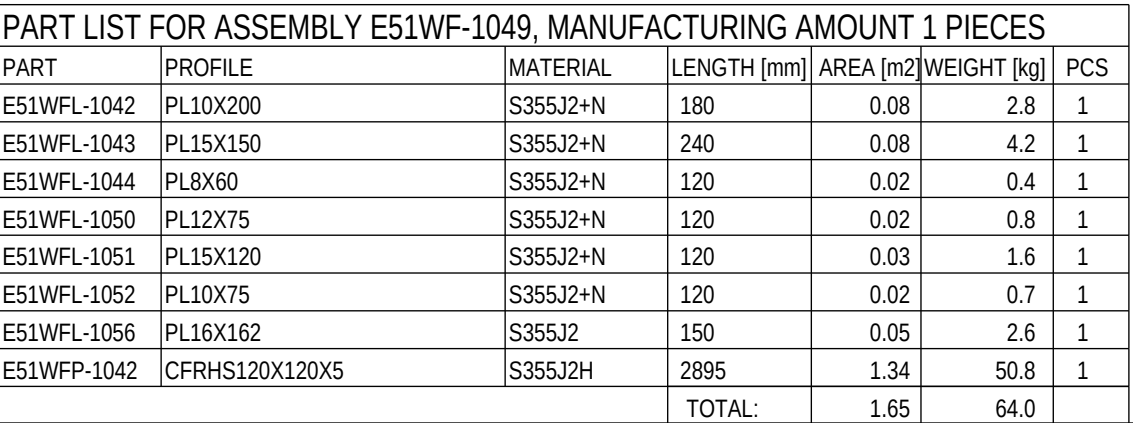

Technical fabrication requirements:		Execution class EXC2
Requirements for fabrication, standard EN1090-2, table A.3 : EXC2 Execution specification document nr Z5019443-ICC25-0600-0660-000005 Surface preparation grade ISO8501-3, grade P2 Surface treatment ISO12944-5 Additional requirements on surface treatment C3.07, EPPUR 240/2 Shade RAL 7024 (Graphite Gray) Welding of built up steel section Appendix 1, Project spec. Welds, if not specified otherwise EN 9692-1, EN 9692-2	Fabrication tolerances EN 1090-2, Appendix B Special fabrication tolerances Project specification/ shown on drwg. Weld inspection, requirements EN 1090-2, Table 24, U>0.5 Extent of NDT, fillet welds MT-EN1290, 20% of welds Extent of NDT, butt welds UT, EN-ISO17640, 20% of welds Extent of NDT for splices not shown on drawing UT, EN-ISO17640, 100%of welds Requirements on hinging EN1090-2 Section 6.6.3	Additional material inspection Weld class EN ISO 5817 Shown on drwg.


Easpring New Materials Oy

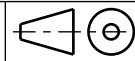

DRAWING CONTENT

ASSEMBLY DRAWING
FRAME
E51WF-1049

 SWECO Sustainable engineering and design	SWECO RAKENNETEKNIikka OY ILMALANPORTTI 2 00240 HELSINKI	DATE 12.06.2026	ARCHIVING CODE	PAGE	DESIGN GROUP STR
	PUH. +358 207 393 000 www.sweco.fi	DRAWN Alexey Serous	DESIGNER Alexey Serous	APPROVED Pertti Koivumaanaho	CHECKED Jere Kalliosalmi
		PROJECT NUMBER 25019443	DWG. NO. E51WF-1049		REVISION

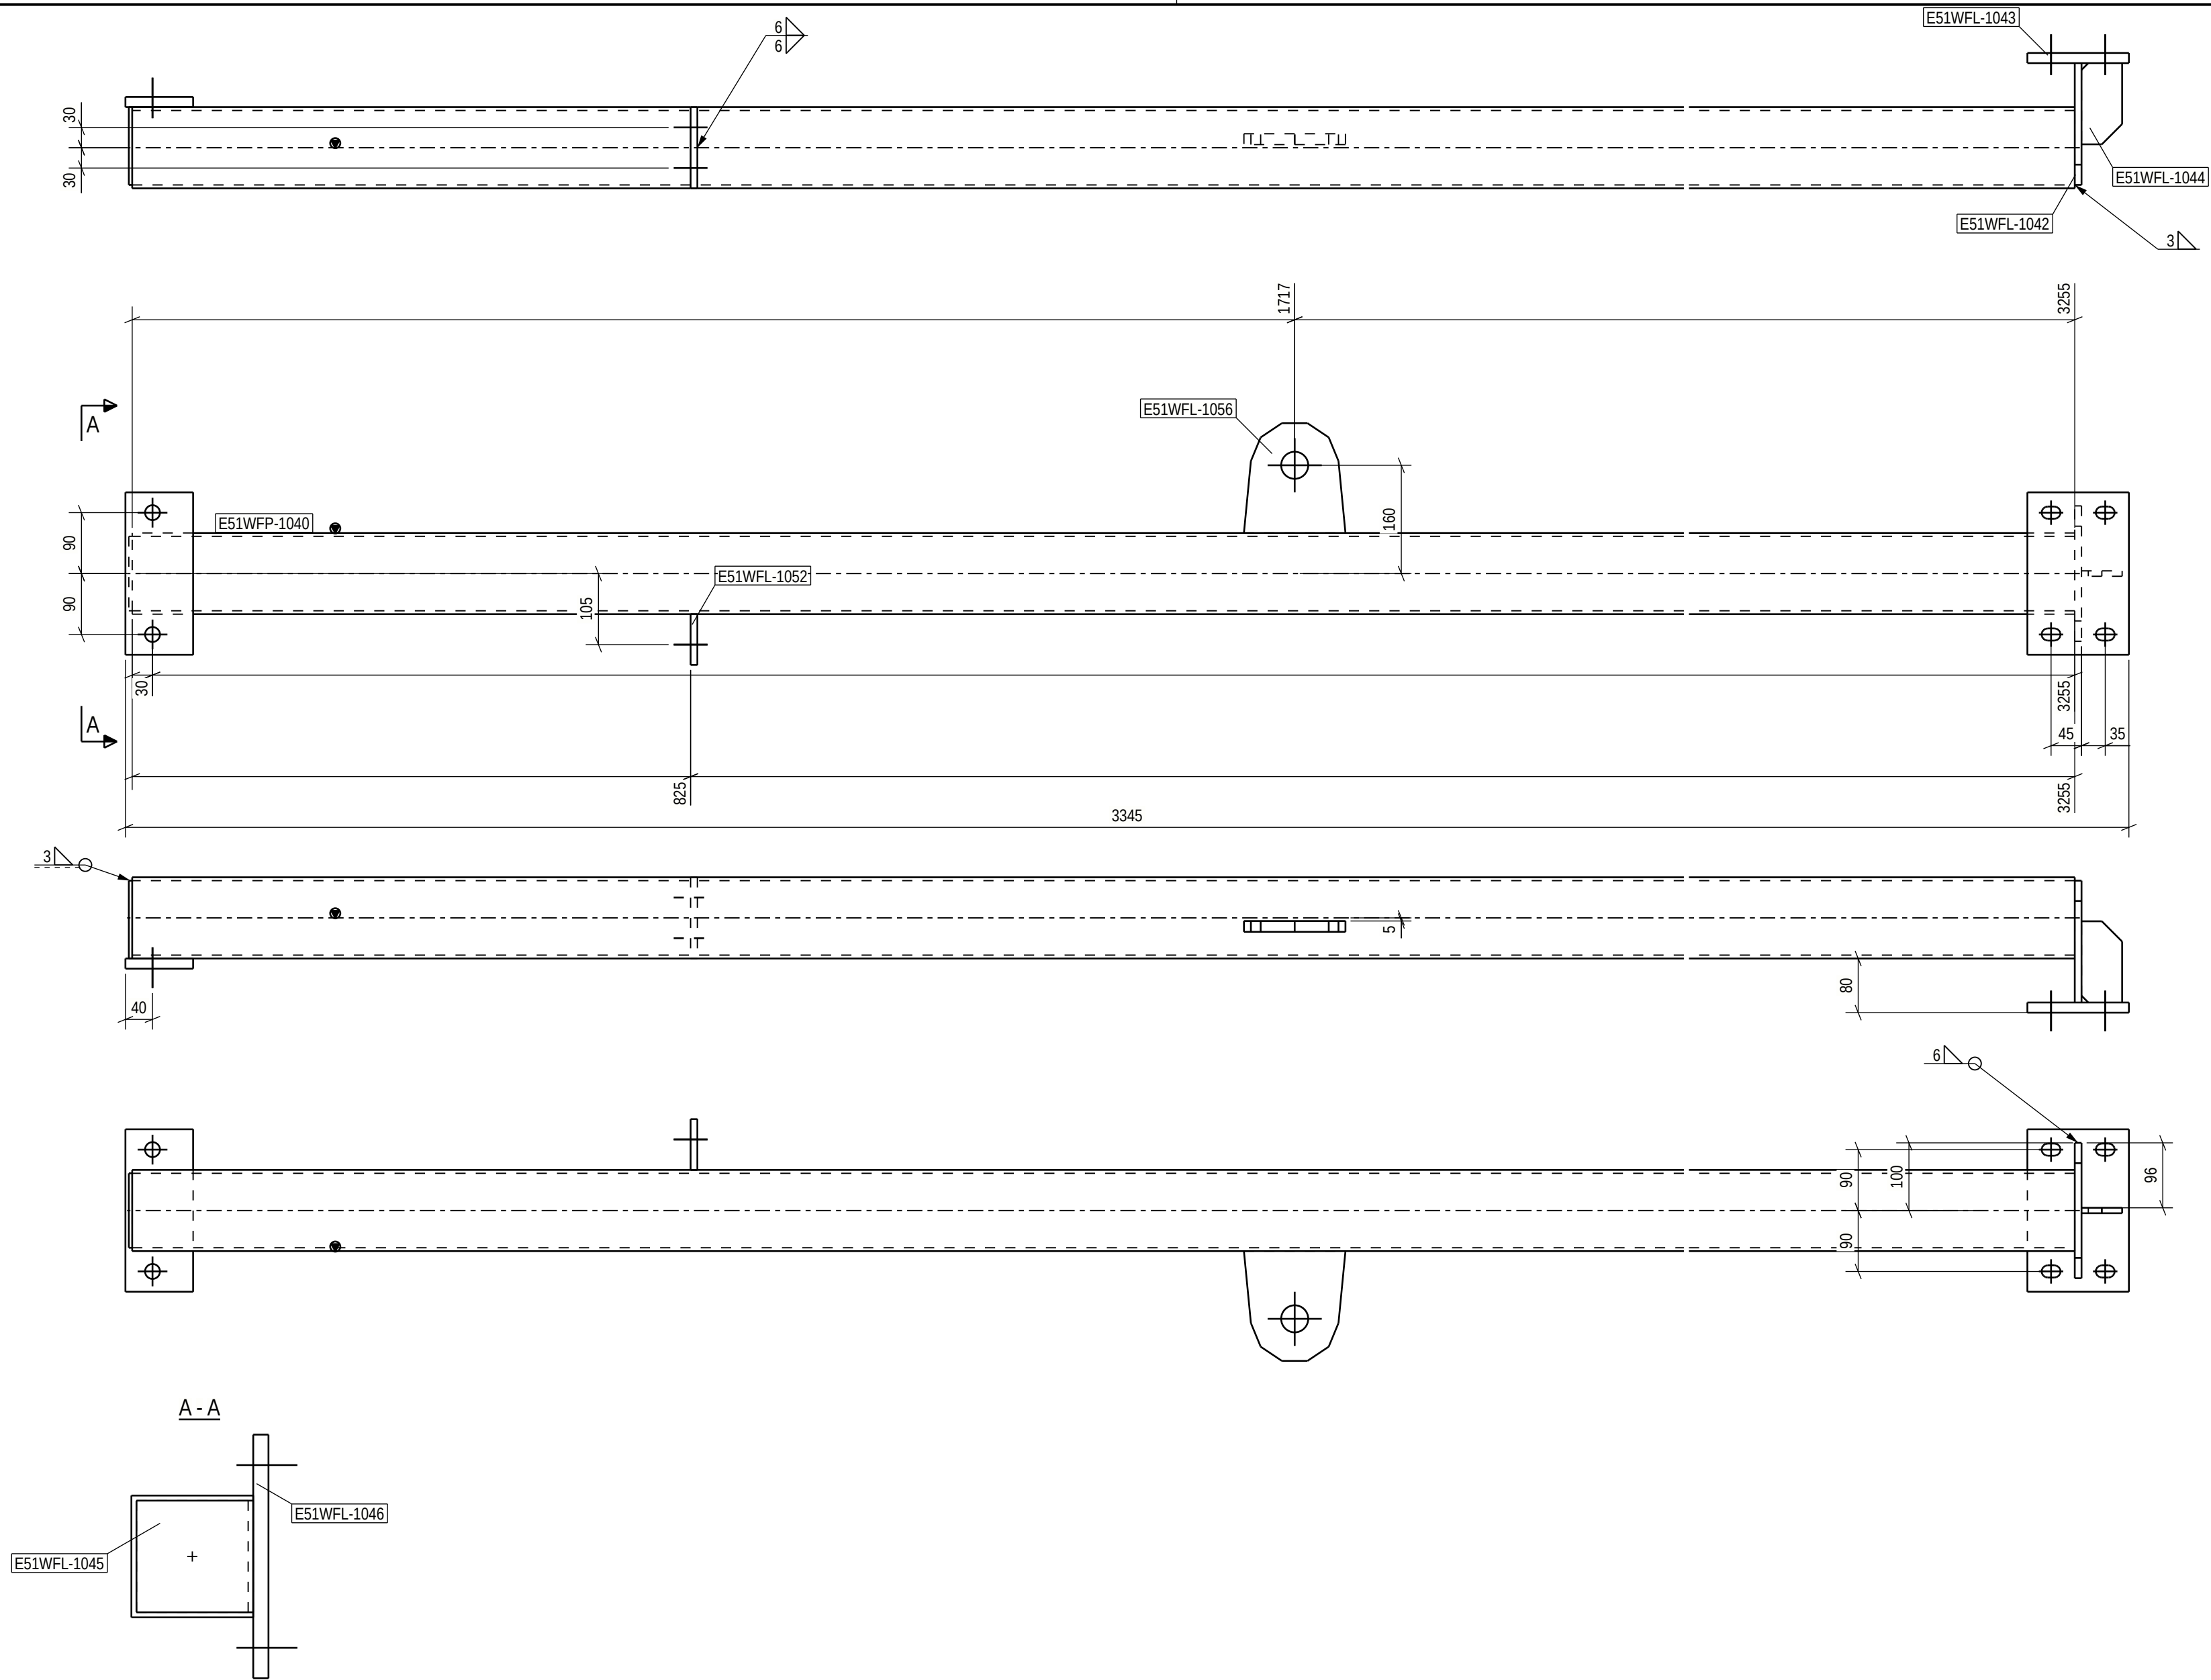

PART LIST FOR ASSEMBLY E51WF-1050, MANUFACTURING AMOUNT 1 PIECES						
PART	PROFILE	MATERIAL	LENGTH [mm]	AREA [m2]	WEIGHT [kg]	PCS
E51WFL-1042	PL10X200	S355J2+N	180	0.08	2.8	1
E51WFL-1043	PL15X150	S355J2+N	240	0.08	4.2	1
E51WFL-1044	PL8X60	S355J2+N	120	0.02	0.4	1
E51WFL-1045	PL5X110	S355J2+N	115	0.03	0.5	1
E51WFL-1046	PL15X100	S355J2+N	240	0.06	2.8	1
E51WFL-1052	PL10X75	S355J2+N	120	0.02	0.7	1
E51WFL-1056	PL16X162	S355J2	150	0.05	2.6	1
E51WFP-1040	CFRHS120X120X5	S355J2H	3255	1.51	57.1	1
TOTAL:				1.84	71.1	

LIFTING LUG WELDING, WEIGHT < 1,5 t

Technical fabrication requirements:

Requirements for fabrication, standard
EN1090-2, table A.3 : EXC2

Execution Specification document nr
25019443-ICC250-0600-0660-000005

Surface preparation grade
ISO8501-3, grade P2

Surface treatment
ISO12944-5

Additional requirements on surface treatment
C3.07, EPPUR 240/2

Shade
RAL 7024 (Graphite Gray)

Welding of built up steel section
Appendix 1 / Project spec.

Welds, if not specified otherwise
EN 9692-1, EN 9692-2

Fabrication tolerances
EN 1090-2, Appendix B

Special fabrication tolerances
Project specification/ shown on drwg.

Weld inspection, requirements
EN 1090-2, Table 24, U>0.5

Extent of NDT, fillet welds
MT-EN1290, 20% of welds

Extent of NDT, butt welds
UT, EN-ISO17640, 20% of welds

Extent of NDT for splices not shown on drawing
UT, EN-ISO17640, 100% of welds

Requirements on holing
EN1090-2 Section 6.6.3

Weld class
C, EN ISO 5817

Additional material inspection
Shown on drwg.

Execution class
EXC2


Approved For Construction

PROJECT NAME
Easpring New Materials Oy
FAIR Phase 1




SWECO RAKENNETEKNIikka OY
ILMALANPORTTI 2
00240 HELSINKI
PUH. +358 207 393 000
www.sweco.fi

DRAWING CONTENT				
ASSEMBLY DRAWING FRAME E51WF-1050				
DATE 12.06.2026	ARCHIVING CODE	PAGE	DESIGN GROUP STR	
DRAWN Alexey Serous	DESIGNER Alexey Serous	APPROVED Pertti Koivumaa	CHECKED Jere Kallosalmi	REVISION
PROJECT NUMBER 25019443		E51WF-1050		

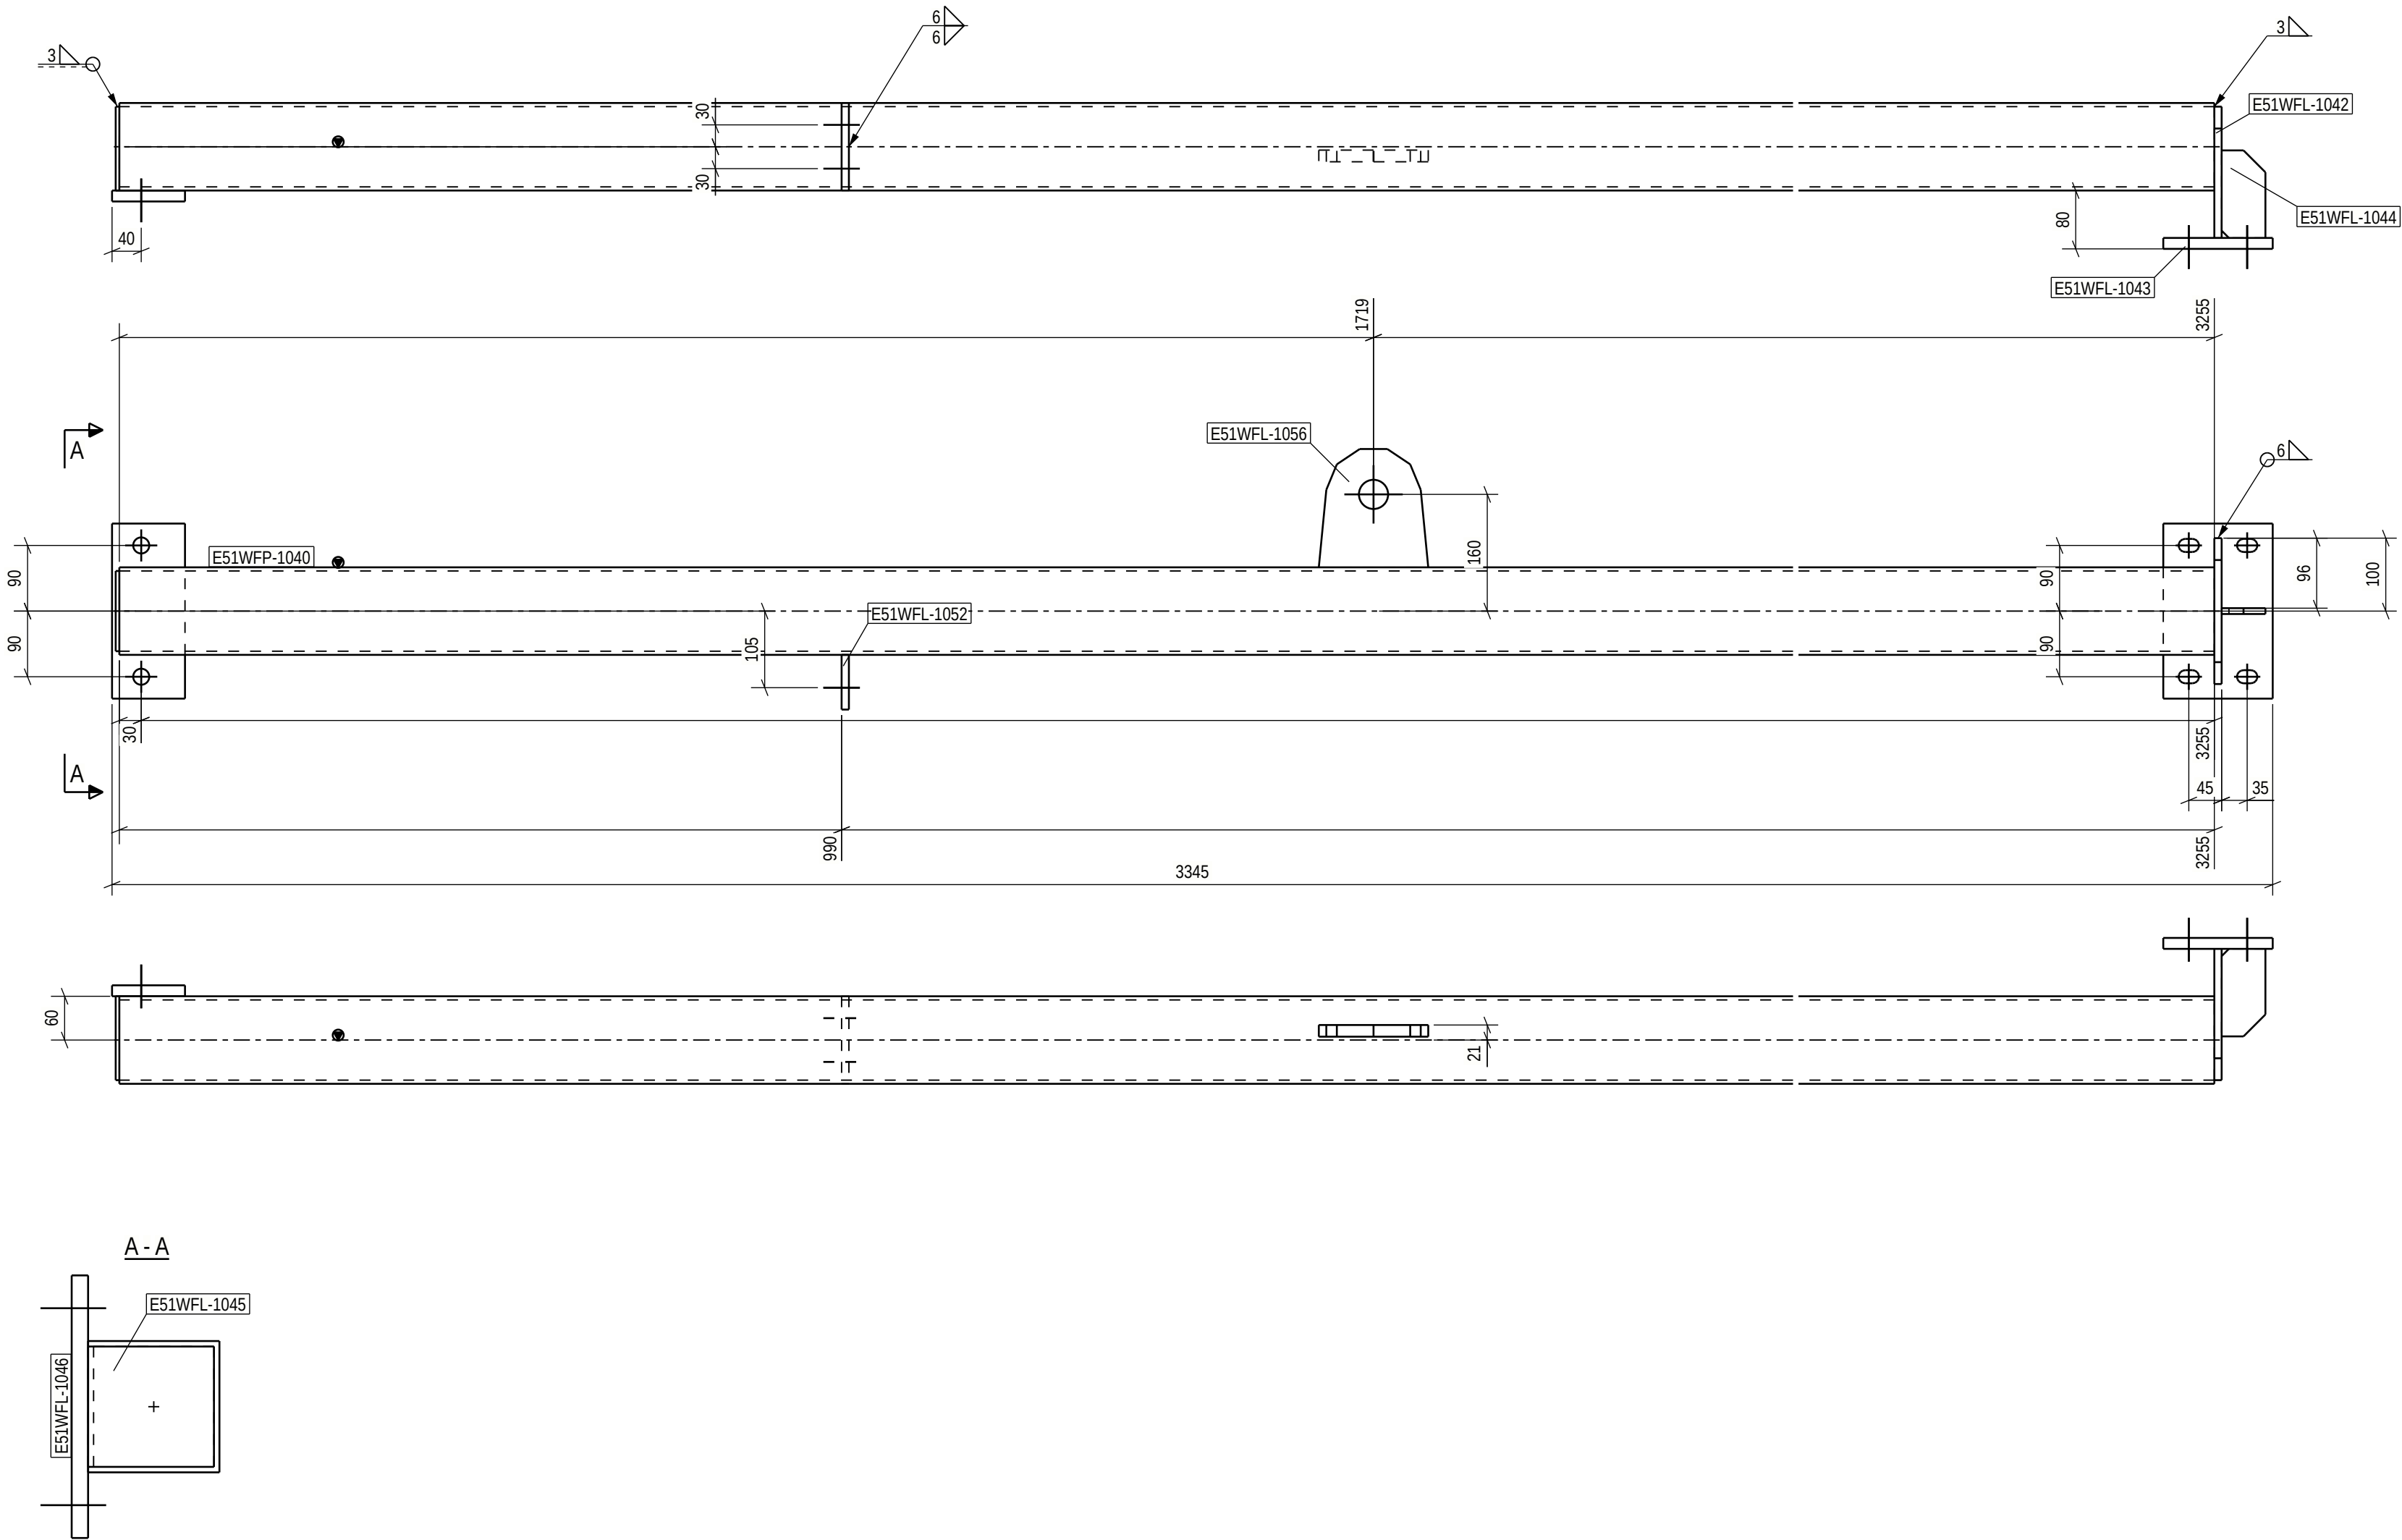

PART LIST FOR ASSEMBLY E51WF-1051, MANUFACTURING AMOUNT 1 PIECES						
PART	PROFILE	MATERIAL	LENGTH [mm]	AREA [m2]	WEIGHT [kg]	PCS
E51WFL-1042	PL10X200	S355J2+N	180	0.08	2.8	1
E51WFL-1043	PL15X150	S355J2+N	240	0.08	4.2	1
E51WFL-1044	PL8X60	S355J2+N	120	0.02	0.4	1
E51WFL-1045	PL5X110	S355J2+N	115	0.03	0.5	1
E51WFL-1046	PL15X100	S355J2+N	240	0.06	2.8	1
E51WFL-1052	PL10X75	S355J2+N	120	0.02	0.7	1
E51WFL-1056	PL16X162	S355J2	150	0.05	2.6	1
E51WFP-1040	CFRHS120X120X5	S355J2H	3255	1.51	57.1	1
TOTAL:				1.84	71.1	

LIFTING LUG WELDING, WEIGHT < 1,5 t

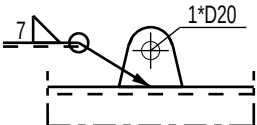


Technical fabrication requirements:		Execution class
Requirements for fabrication, standard EN1090-2, table A.3 : EXC2		EXC2
Execution Specification document nr 25019443-ICC250-0600-0660-000005		
Surface preparation grade ISO8501-3, grade P2		
Surface treatment ISO12944-5		
Additional requirements on surface treatment C3.07, EPPUR 240/2		
Shade RAL 7024 (Graphite Gray)		
Welding of built up steel section Appendix 1 / Project spec.		
Welds, if not specified otherwise EN 9692-1, EN 9692-2		
Fabrication tolerances EN 1090-2, Appendix B		
Special fabrication tolerances Project specification/ shown on drwg.		
Weld inspection, requirements EN 1090-2, Table 24, U>0.5		
Extent of NDT, filled welds MT-EN1290, 20% of welds		
Extent of NDT, butt welds UT, EN-ISO17640, 20% of welds		
Requirements on holing EN1090-2 Section 6.6.3		
Weld class C, EN ISO 5817		
Additional material inspection Shown on drwg.		

Approved For Construction

Easpring New Materials Oy
FAIR Phase 1




SWECO RAKENNETEKNIikka OY
ILMALANPORTTI 2
00240 HELSINKI
PUH. +358 207 393 000
www.sweco.fi

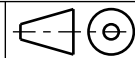


DRAWING CONTENT
ASSEMBLY DRAWING
FRAME
E51WF-1051

DATE	ARCHIVING CODE	PAGE	DESIGN GROUP
12.06.2026			STR
DRAWN	DESIGNER	APPROVED	CHECKED
Alexey Serous	Alexey Serous	Pertti Kivumaa	Jere Kallosalmi
PROJECT NUMBER	DWG. NO.	REVISION	
25019443	E51WF-1051		




PART LIST FOR ASSEMBLY E51WF-1052, MANUFACTURING AMOUNT 1 PIECES						
PART	PROFILE	MATERIAL	LENGTH [mm]	AREA [m2]	WEIGHT [kg]	PCS
E51WFL-1035	PL20X200	S355J2+N	240	0.11	7.5	1
E51WFL-1036	PL10X150	S355J2+N	150	0.05	1.8	1
E51WFL-1037	PL15X210	S355J2+N	160	0.08	4.0	1
E51WFL-1038	PL10X150	S355J2+N	150	0.05	1.7	1
E51WFP-1028	CFRHS150X150X5	S355J2H	4736	2.76	105.4	1
TOTAL:				3.05	120.4	

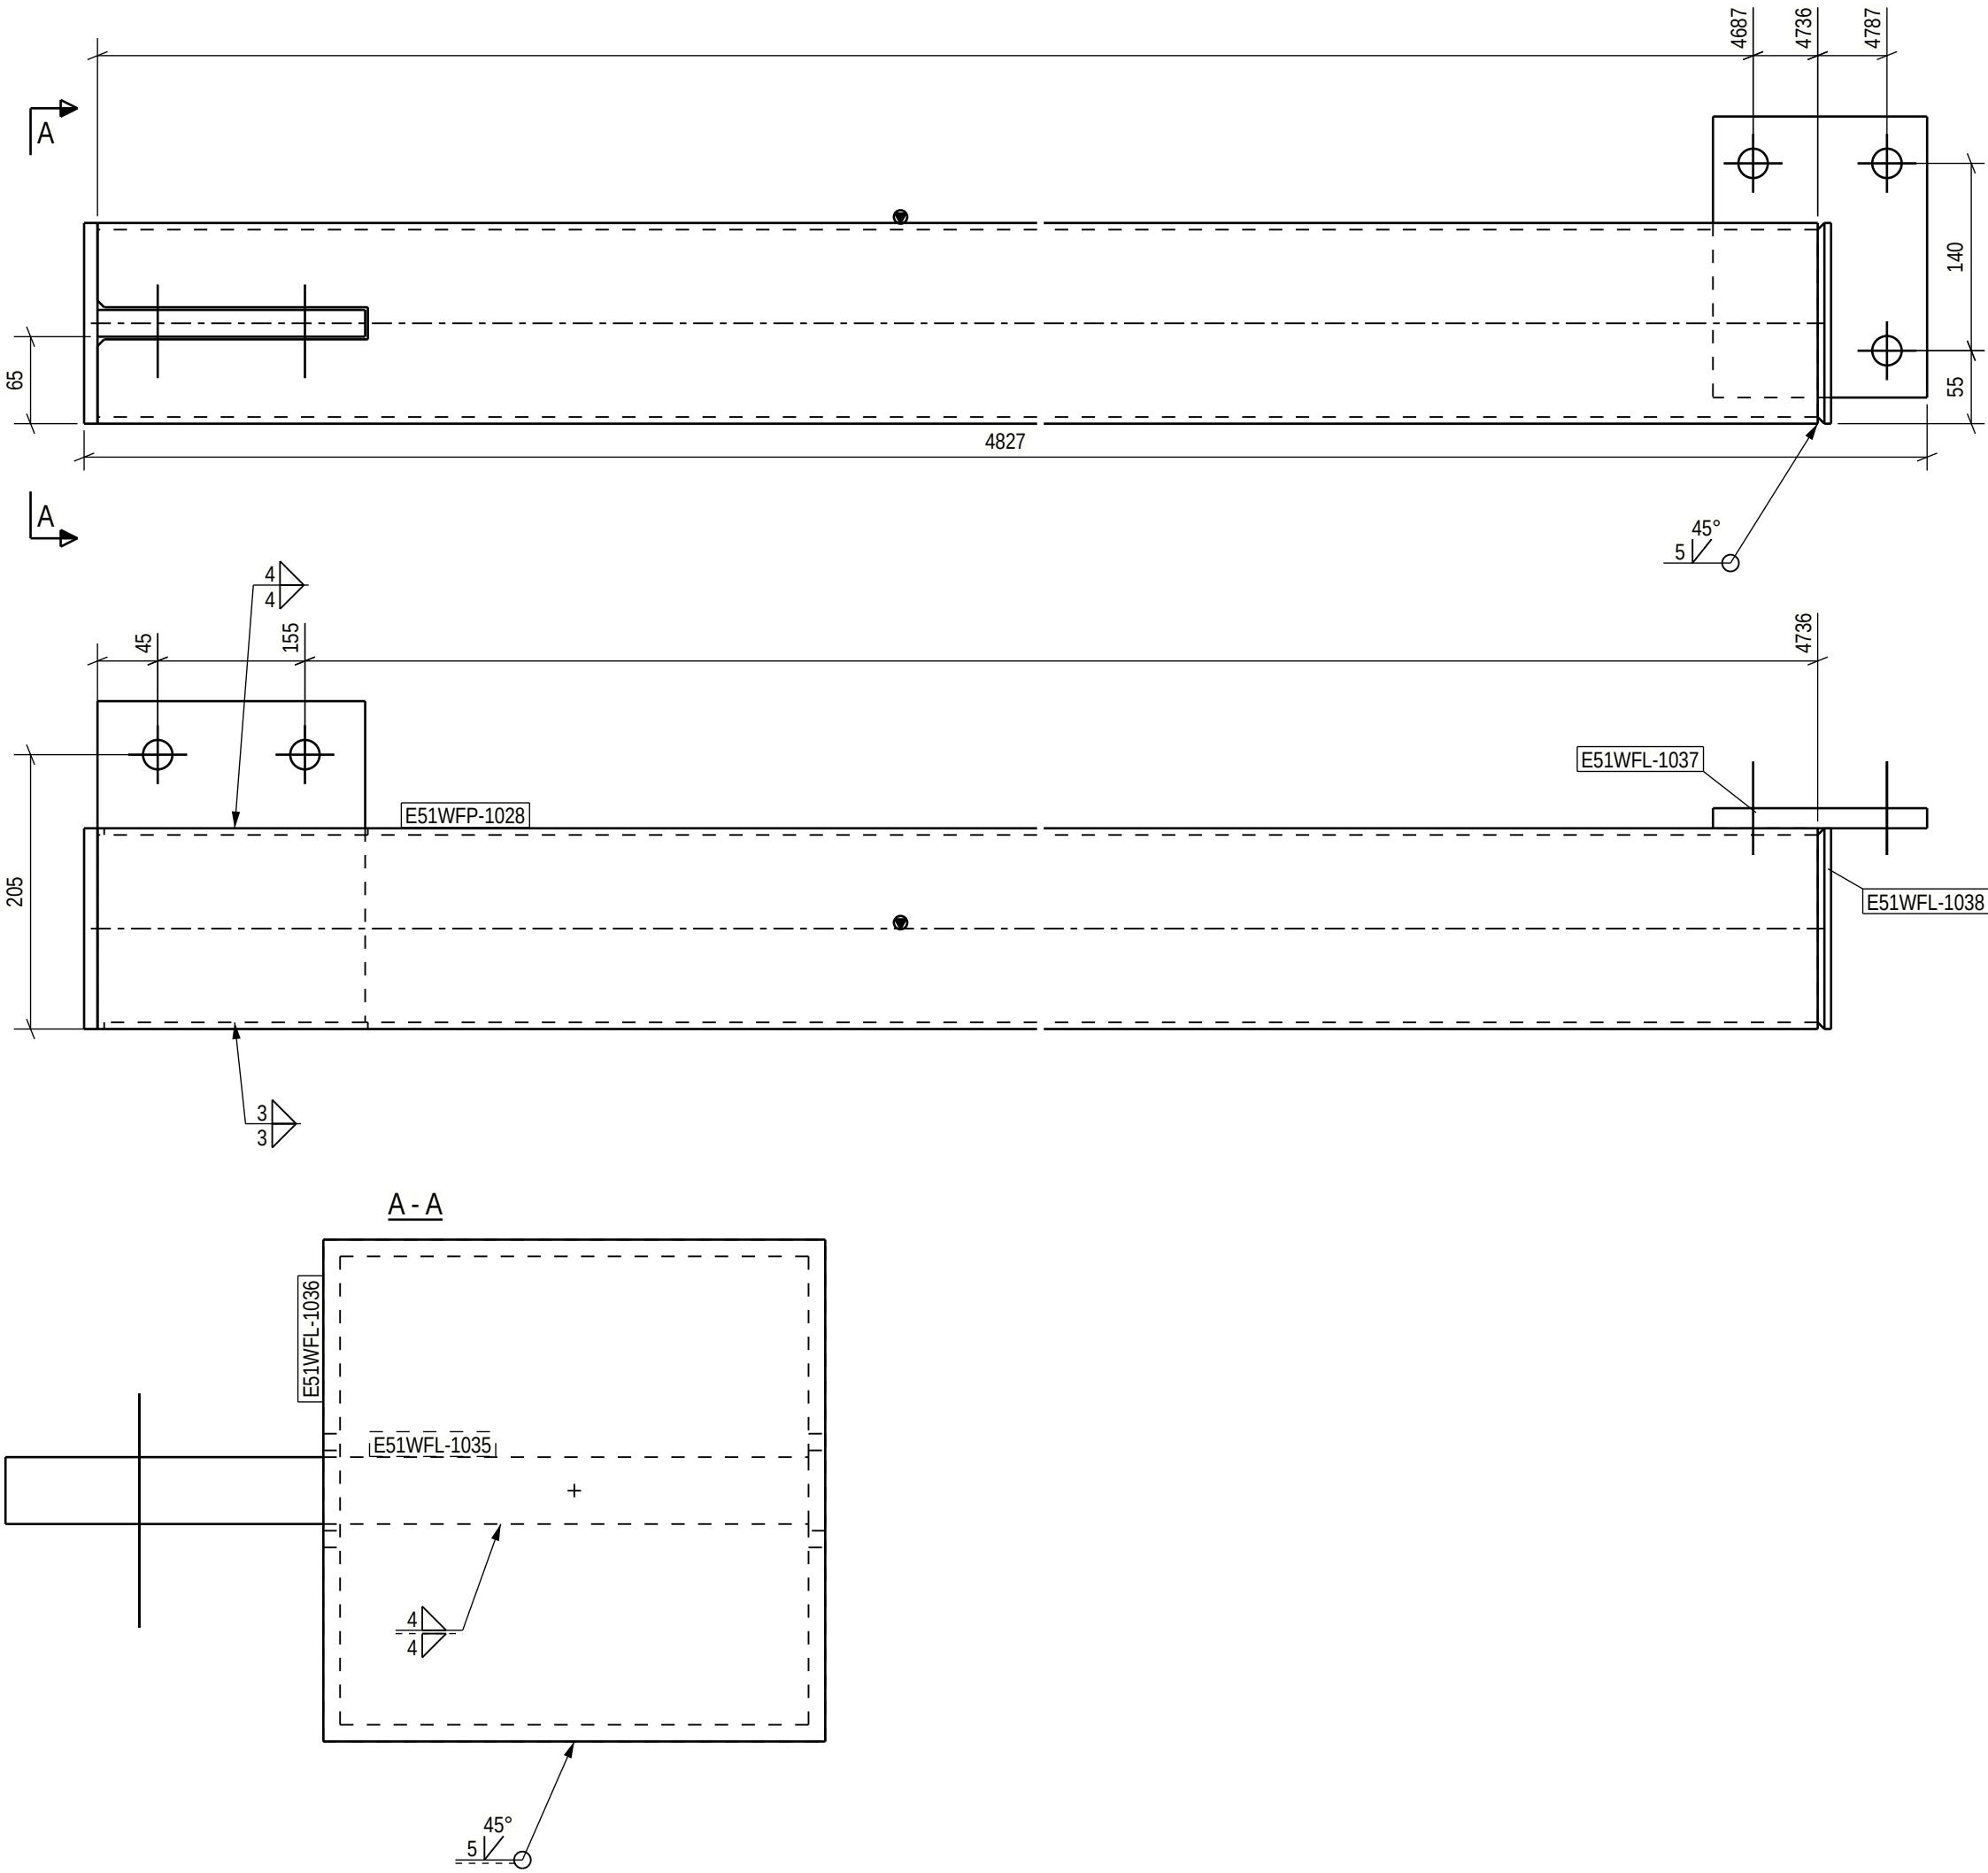

LIFTING LUG WELDING, WEIGHT < 1,5 t

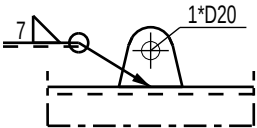


Technical fabrication requirements:		Execution class		Approved For Construction									
Requirements for fabrication, standard EN1090-2, table A.3 : EXC2		Fabrication tolerances EN 1090-2, Appendix B		PROJECT NAME Easpring New Materials Oy FAIR Phase 1		DRAWING CONTENT ASSEMBLY DRAWING FRAME E51WF-1052							
Execution Specification document nr 25019443-ICC250-0600-0660-000005		Special fabrication tolerances Project specification/ shown on drwg.											
Surface preparation grade ISO8501-3, grade P2		Weld inspection, requirements EN 1090-2, Table 24, U>0.5											
Surface treatment ISO12944-5		Extent of NDT, fillet welds MT-EN1290, 20% of welds											
Additional requirements on surface treatment C3.07, EPPUR 240/2		Extent of NDT, butt welds UT, EN-ISO17640, 20% of welds				DATE 12.06.2026		ARCHIVING CODE		PAGE		DESIGN GROUP STR	
Shade RAL 7024 (Graphite Gray)		Extent of NDT for splices not shown on drawing UT, EN-ISO17640, 100% of welds											
Welding of built up steel section Appendix 1 / Project spec.		Requirements on holing EN1090-2 Section 6.6.3				DRAWN Alexey Serous		DESIGNER Alexey Serous		APPROVED Pertti Koivumaa		CHECKED Jere Kallosalmi	
Welds, if not specified otherwise EN 9692-1, EN 9692-2		Weld class C, EN ISO 5817											
		Additional material inspection Shown on drwg.		PUH. +358 207 393 000 www.sweco.fi		PROJECT NUMBER 25019443		DWG. NO. E51WF-1052		REVISION			

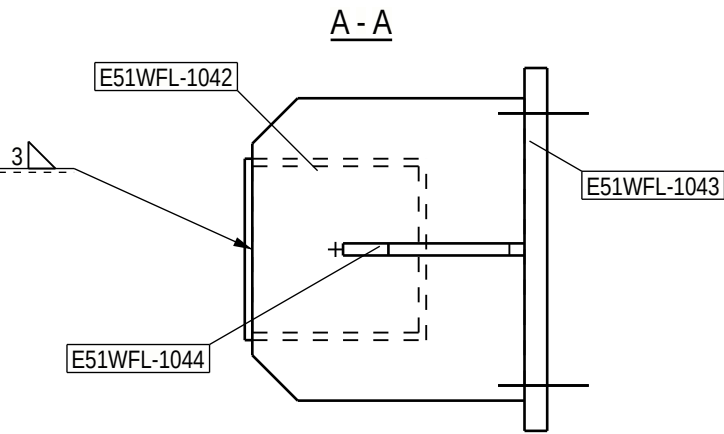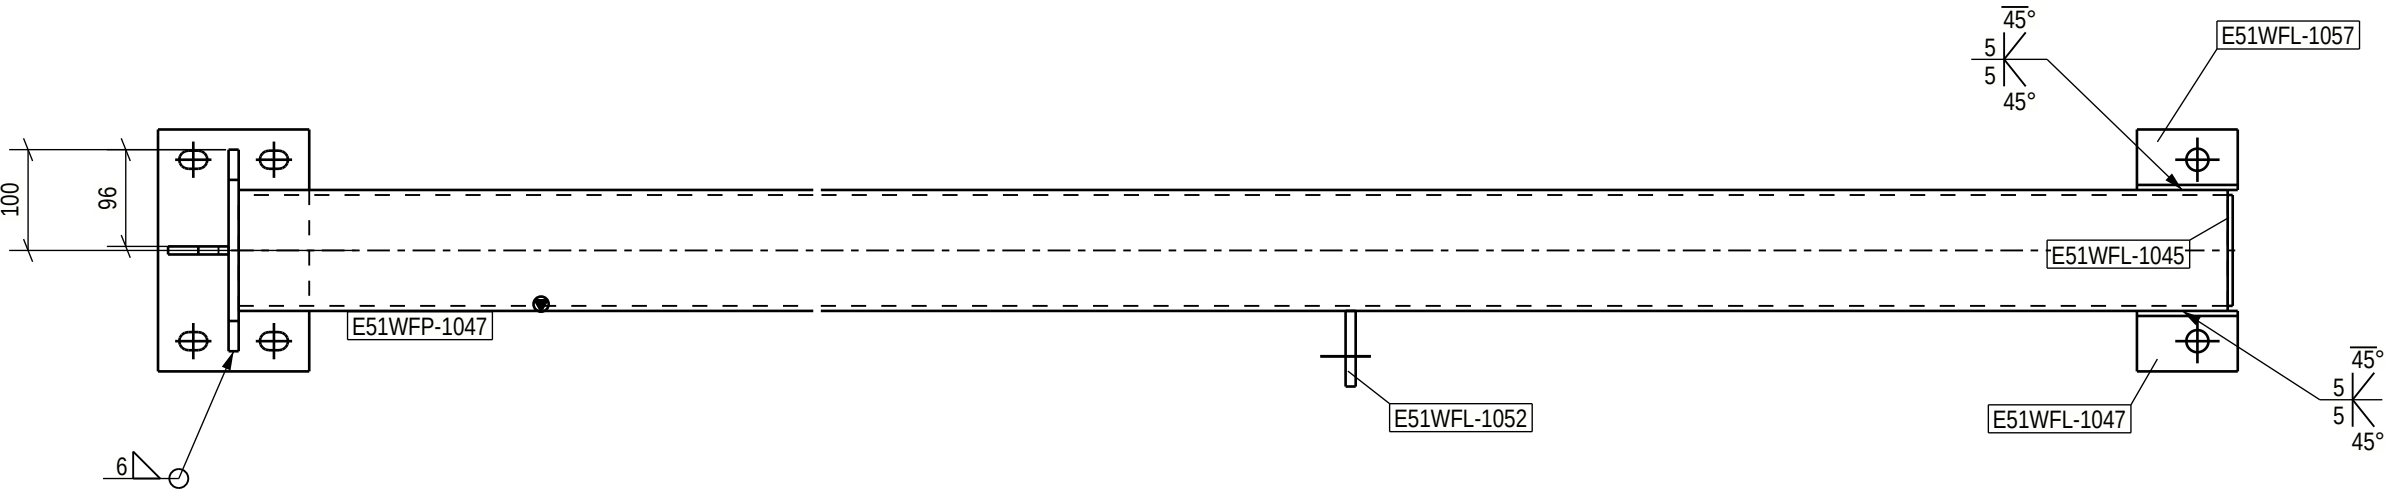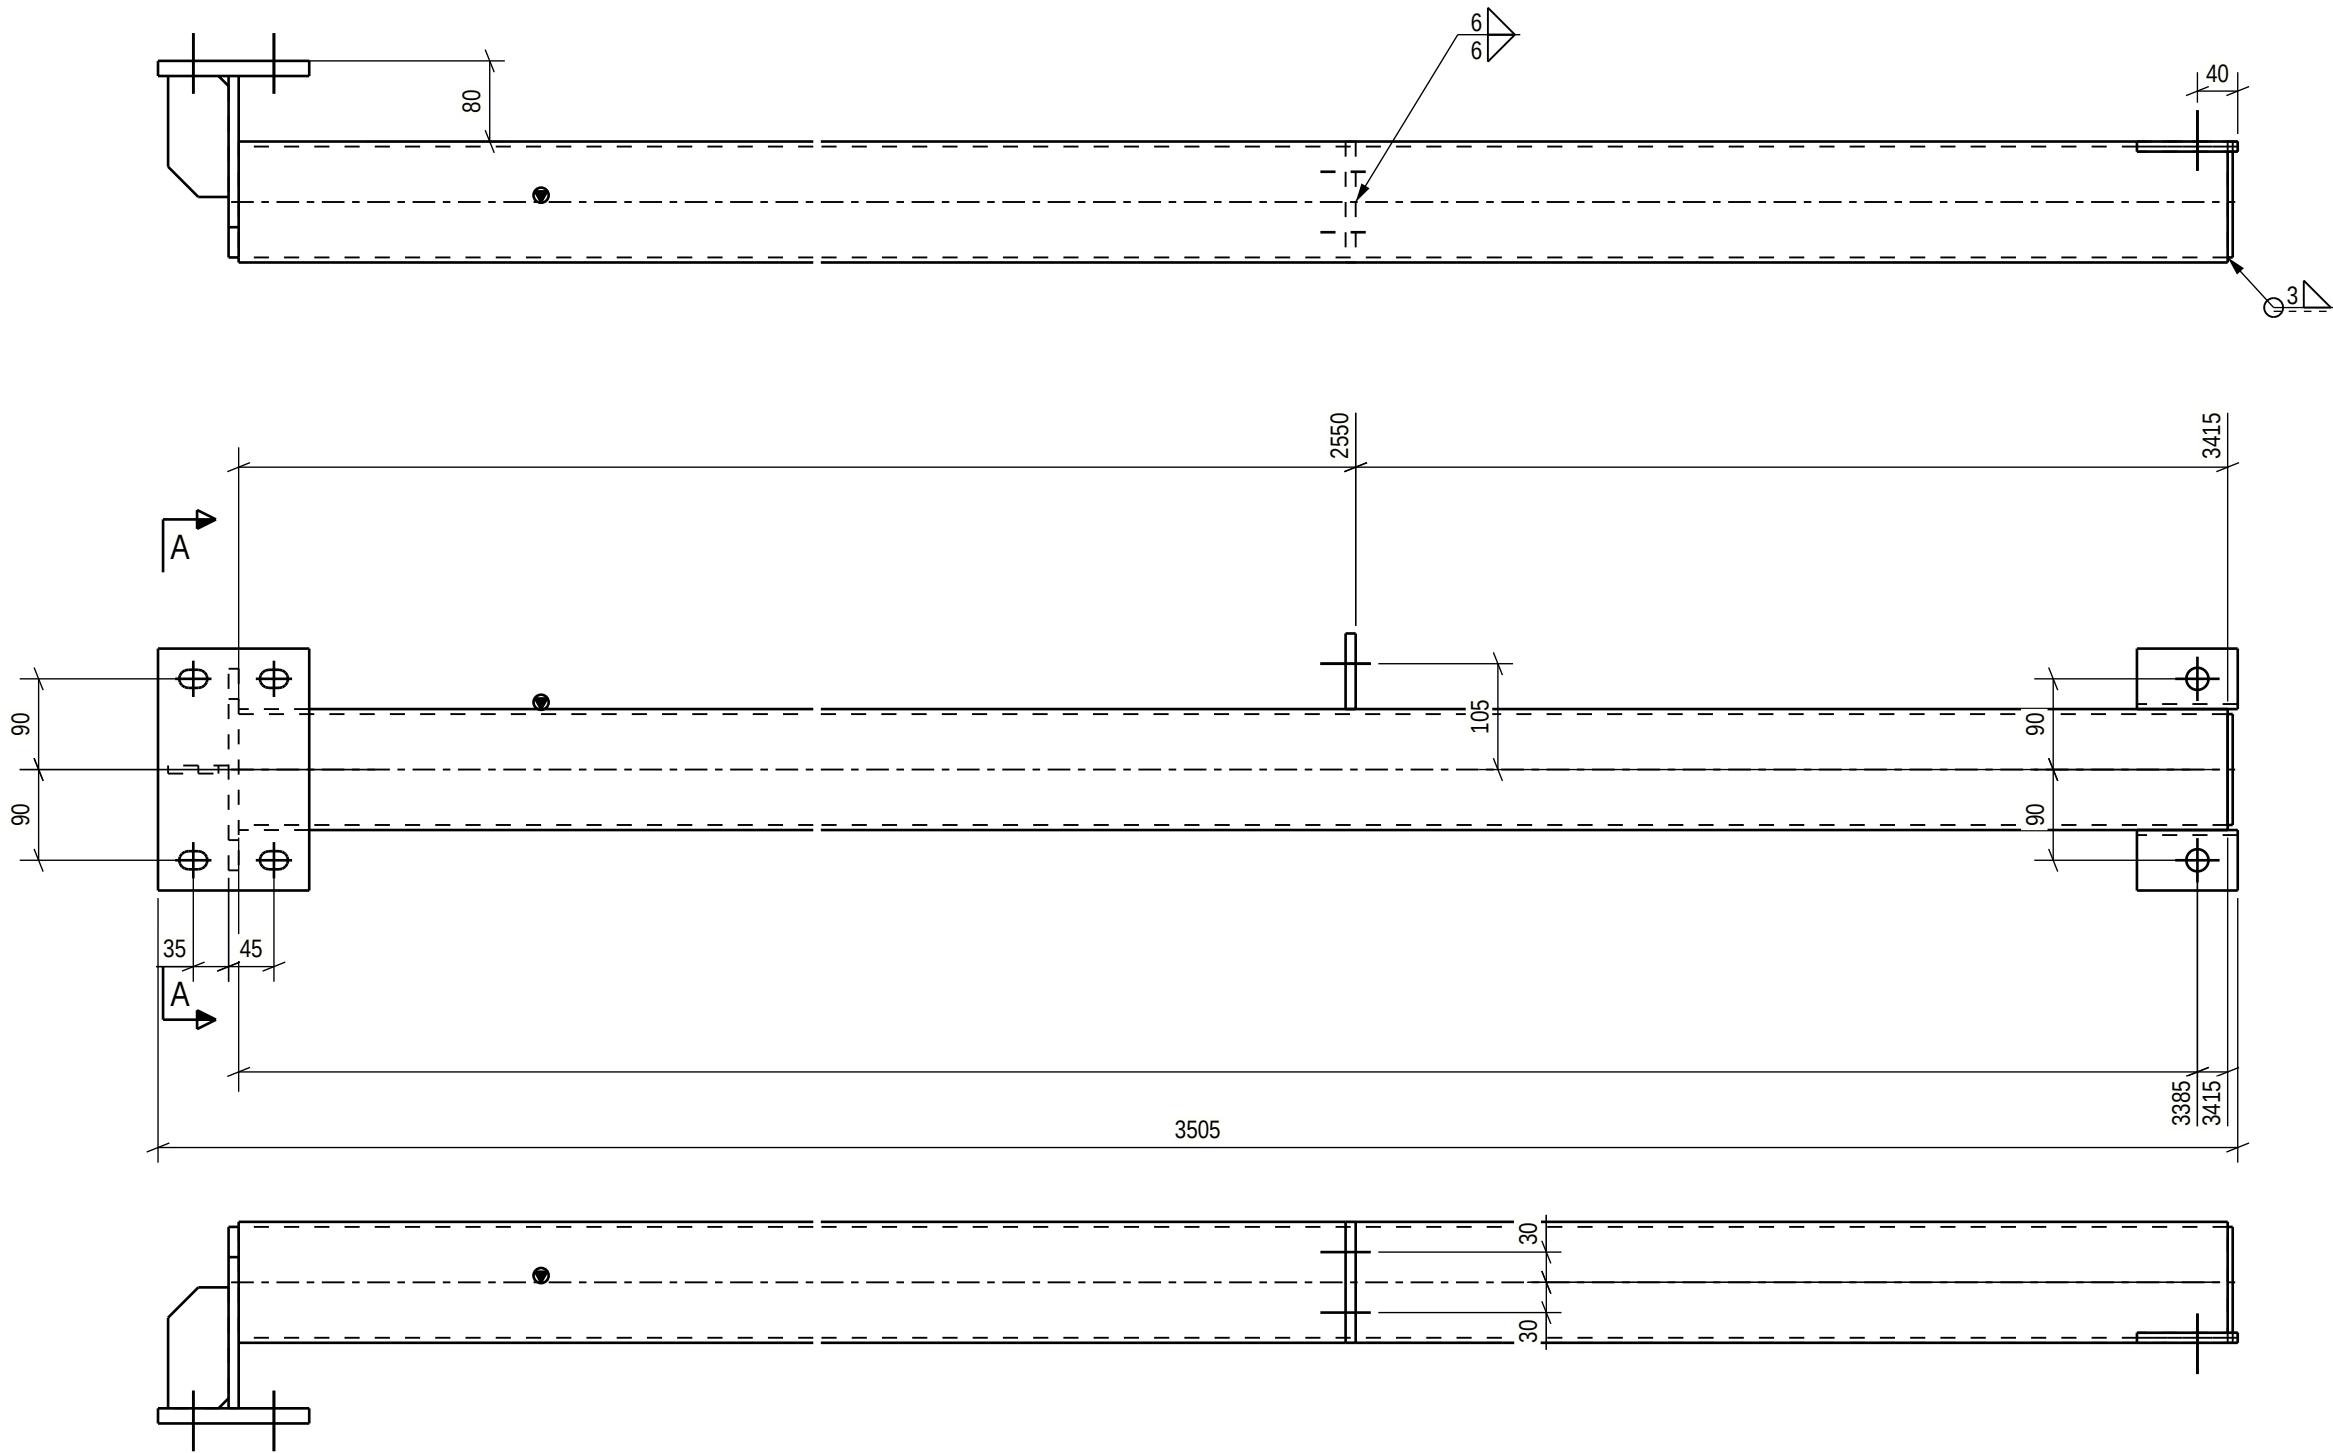

PART LIST FOR ASSEMBLY E51WF-1053, MANUFACTURING AMOUNT 1 PIECES						
PART	PROFILE	MATERIAL	LENGTH [mm]	AREA [m2]	WEIGHT [kg]	PCS
E51WFL-1042	PL10X200	S355J2+N	180	0.08	2.8	1
E51WFL-1043	PL15X150	S355J2+N	240	0.08	4.2	1
E51WFL-1044	PL8X60	S355J2+N	120	0.02	0.4	1
E51WFL-1045	PL5X110	S355J2+N	115	0.03	0.5	1
E51WFL-1047	PL10X60	S355J2+N	100	0.01	0.5	1
E51WFL-1052	PL10X75	S355J2+N	120	0.02	0.7	1
E51WFL-1057	PL10X60	S355J2+N	100	0.01	0.5	1
E51WFP-1047	CFRHS120X120X5	S355J2H	3415	1.58	59.9	1
TOTAL:				1.84	69.5	

Technical fabrication requirements:		Execution class
Requirements for fabrication, standard EN1090-2, table A.3 : EXC2 Execution Specification document nr 25019443-ICC250-0600-0660-000005		EXC2
Surface preparation grade ISO8501-3, grade P2	Fabrication tolerances EN 1090-2, Appendix B Special fabrication tolerances Project specification/ shown on drwg.	
Surface treatment ISO12944-5	Weld inspection, requirements EN 1090-2, Table 24, U>0.5	
Additional requirements on surface treatment C3.07, EPPUR 240/2	Extent of NDT, fillet welds MT-EN1290, 20% of welds	
Shade RAL 7024 (Graphite Gray)	Extent of NDT, butt welds UT, EN-ISO17640, 20% of welds	
Welding of built up steel section Appendix 1 / Project spec.	Requirements on holing EN1090-2 Section 6.6.3	
Welds, if not specified otherwise EN 9692-1, EN 9692-2	Weld class C, EN ISO 5817	Additional material inspection Shown on drwg.

LIFTING LUG WELDING, WEIGHT < 1,5 t

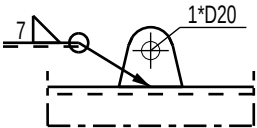


Approved For Construction

Easpring New Materials Oy
FAIR Phase 1




SWECO RAKENNETEKNIikka OY
ILMALANPORTTI 2
00240 HELSINKI
PUH. +358 207 393 000
www.sweco.fi

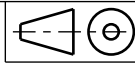

DRAWING CONTENT
ASSEMBLY DRAWING
FRAME
E51WF-1053

DATE	ARCHIVING CODE	PAGE	DESIGN GROUP
12.06.2026			STR
DRAWN Alexey Serous	DESIGNER Alexey Serous	APPROVED Pertti Koivumaa	CHECKED Jere Kallosalmi
PROJECT NUMBER 25019443	DWG. NO. E51WF-1053	REVISION	

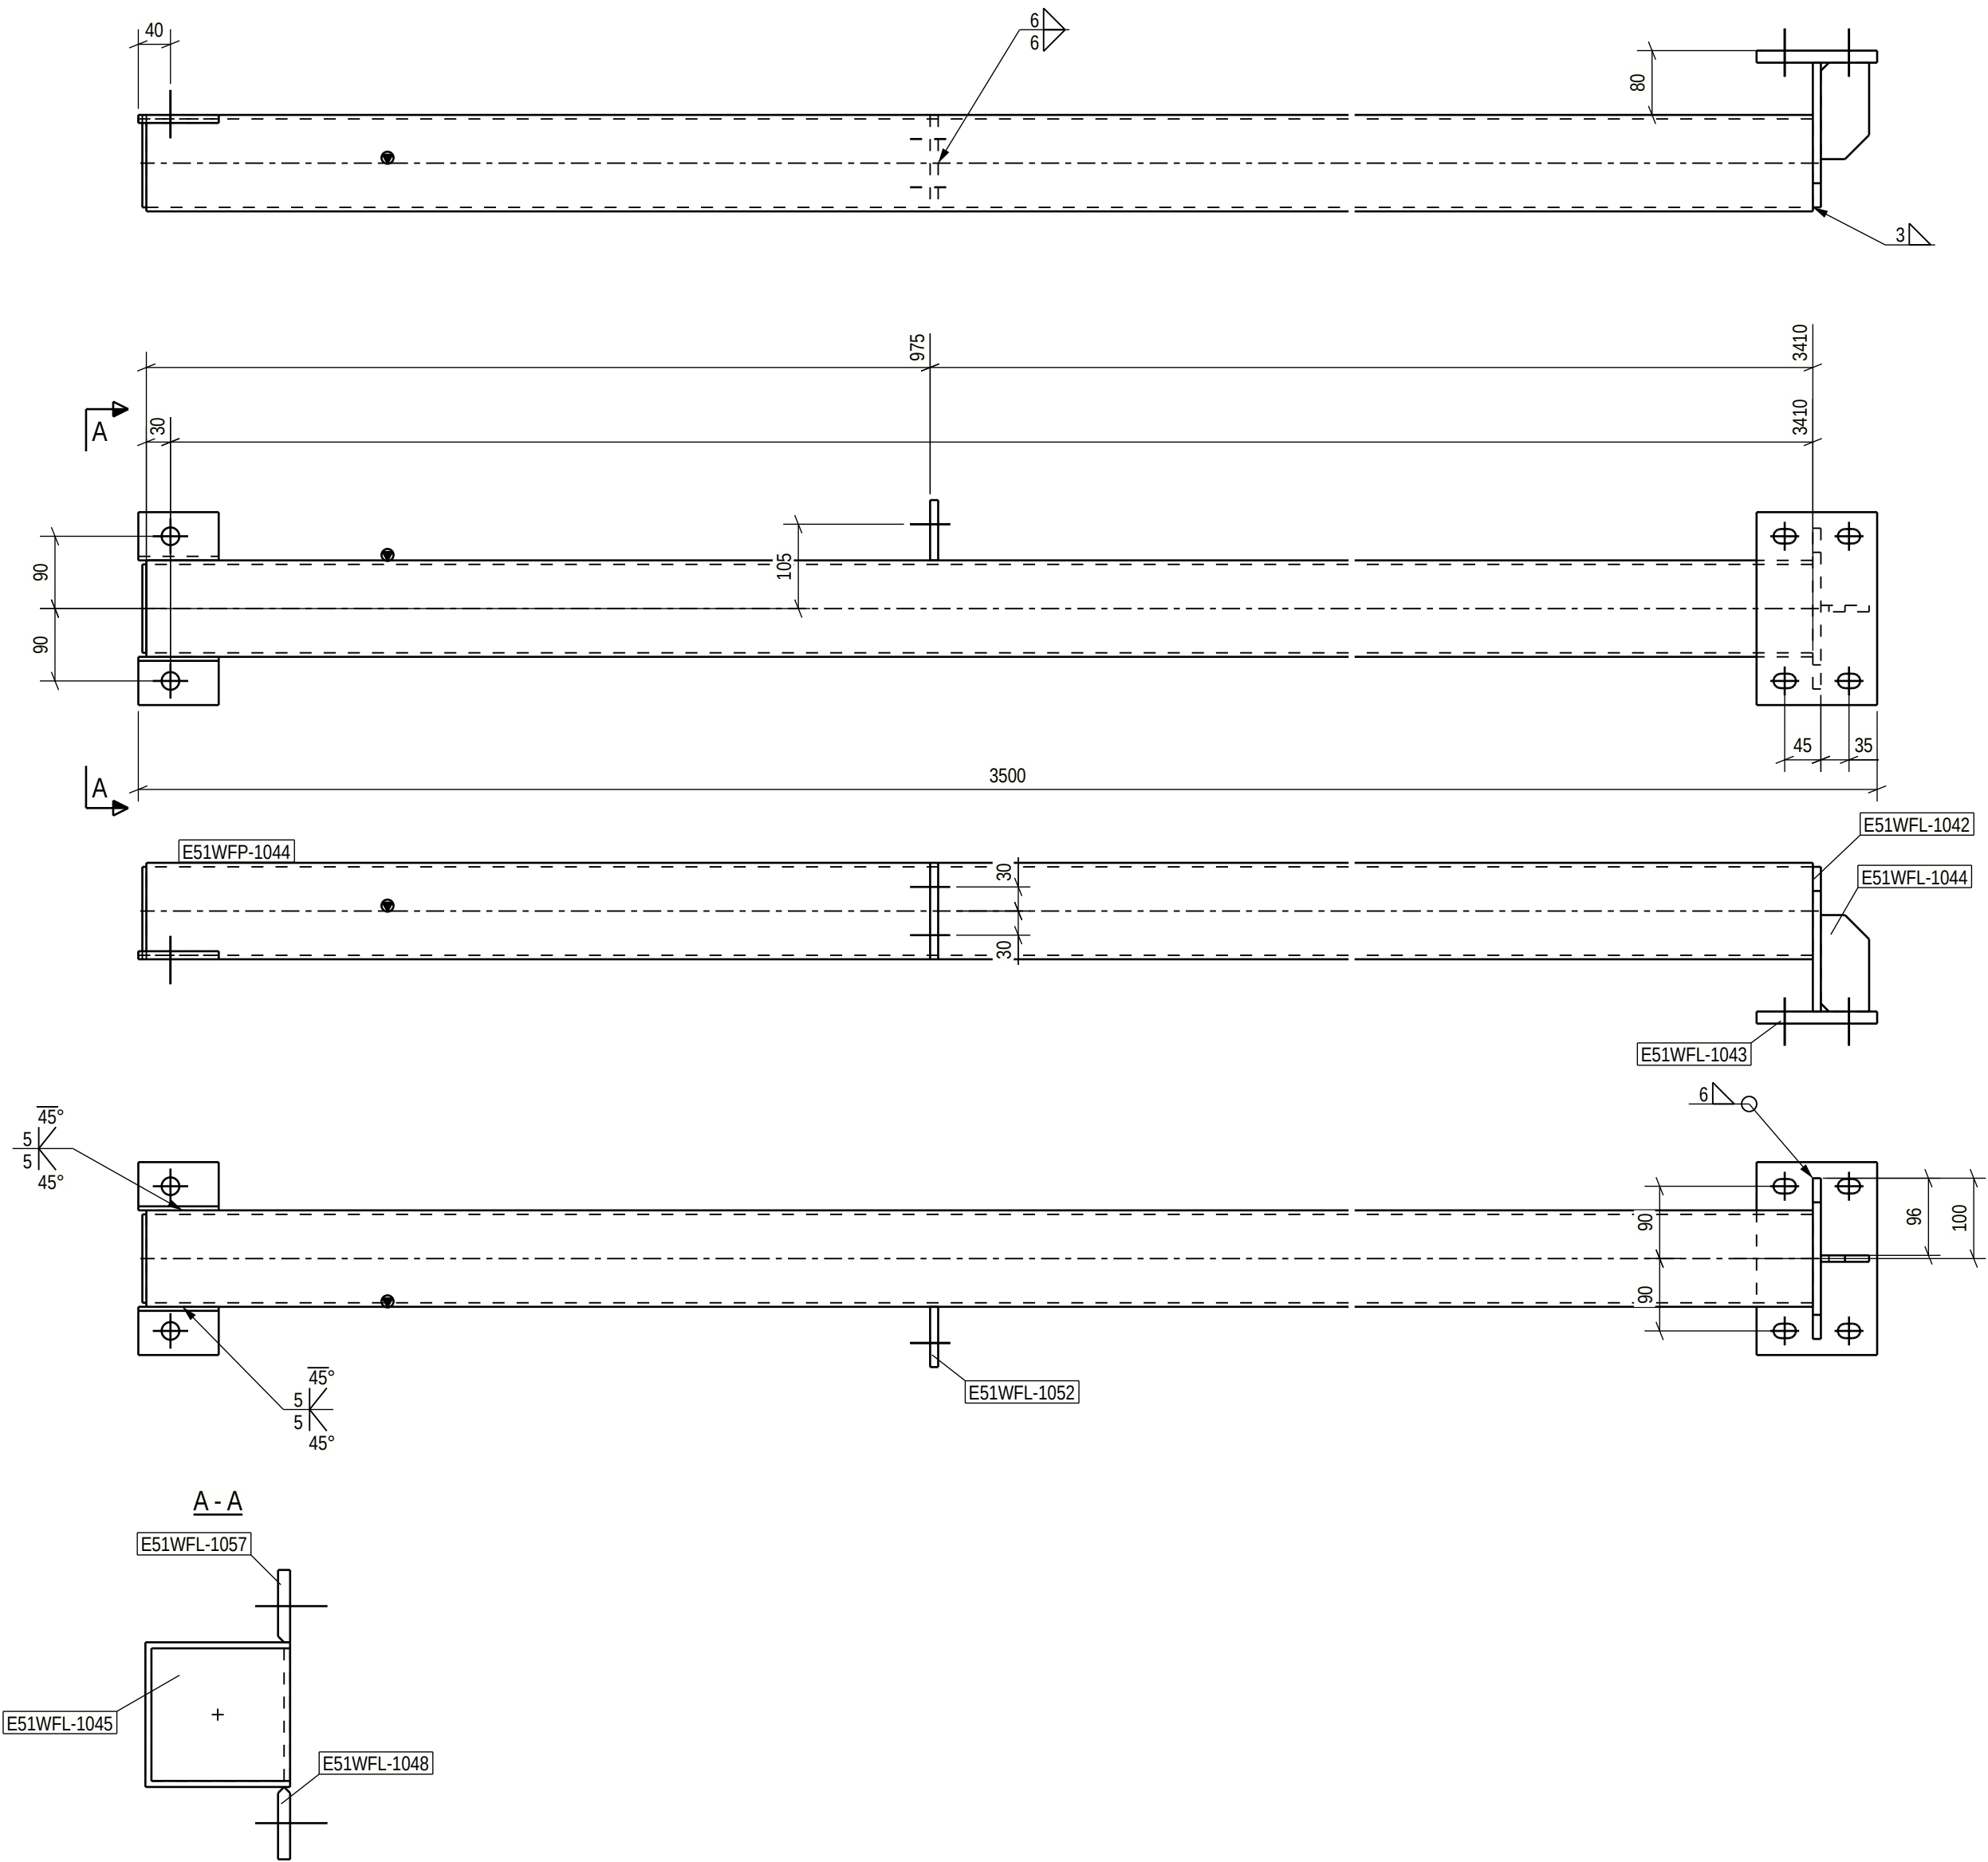

PART LIST FOR ASSEMBLY E51WF-1054, MANUFACTURING AMOUNT 1 PIECES						
PART	PROFILE	MATERIAL	LENGTH [mm]	AREA [m2]	WEIGHT [kg]	PCS
E51WFL-1042	PL10X200	S355J2+N	180	0.08	2.8	1
E51WFL-1043	PL15X150	S355J2+N	240	0.08	4.2	1
E51WFL-1044	PL8X60	S355J2+N	120	0.02	0.4	1
E51WFL-1045	PL5X110	S355J2+N	115	0.03	0.5	1
E51WFL-1048	PL10X60	S355J2+N	100	0.01	0.5	1
E51WFL-1052	PL10X75	S355J2+N	120	0.02	0.7	1
E51WFL-1057	PL10X60	S355J2+N	100	0.01	0.5	1
E51WFP-1044	CFRHS120X120X5	S355J2H	3410	1.58	59.8	1
TOTAL:				1.83	69.4	

Technical fabrication requirements:

Requirements for fabrication, standard
EN1090-2, table A.3 : EXC2

Execution Specification document nr
25019443-ICC250-0600-0660-000005

Surface preparation grade
ISO8501-3, grade P2

Surface treatment
ISO12944-5

Additional requirements on surface treatment
C3.07, EPPUR 240/2

Shade
RAL 7024 (Graphite Gray)

Welding of built up steel section
Appendix 1 / Project spec.

Welds, if not specified otherwise
EN 9692-1, EN 9692-2

Fabrication tolerances
EN 1090-2, Appendix B

Special fabrication tolerances
Project specification/ shown on drwg.

Weld inspection, requirements
EN 1090-2, Table 24, U>0.5

Extent of NDT, fillet welds
MT-EN1290, 20% of welds

Extent of NDT, butt welds
UT, EN-ISO17640, 20% of welds

Extent of NDT for splices not shown on drawing
UT, EN-ISO17640, 100% of welds

Requirements on hoisting
EN1090-2 Section 6.6.3

Weld class
C, EN ISO 5817

Execution class
EXC2

LIFTING LUG WELDING, WEIGHT < 1,5 t

Approved For Construction


Easpring New Materials Oy
FAIR Phase 1



SWECO RAKENNETEKNIikka OY
ILMALANPORTTI 2
00240 HELSINKI


PUH. +358 207 393 000
www.sweco.fi

DRAWING CONTENT				
ASSEMBLY DRAWING FRAME E51WF-1054				
DATE 12.06.2026	ARCHIVING CODE	PAGE	DESIGN GROUP STR	
DRAWN Alexey Serous	DESIGNER Alexey Serous	APPROVED Pertti Koivumaa	CHECKED Jere Kallosalmi	REVISION
PROJECT NUMBER 25019443		DWG. NO. E51WF-1054		

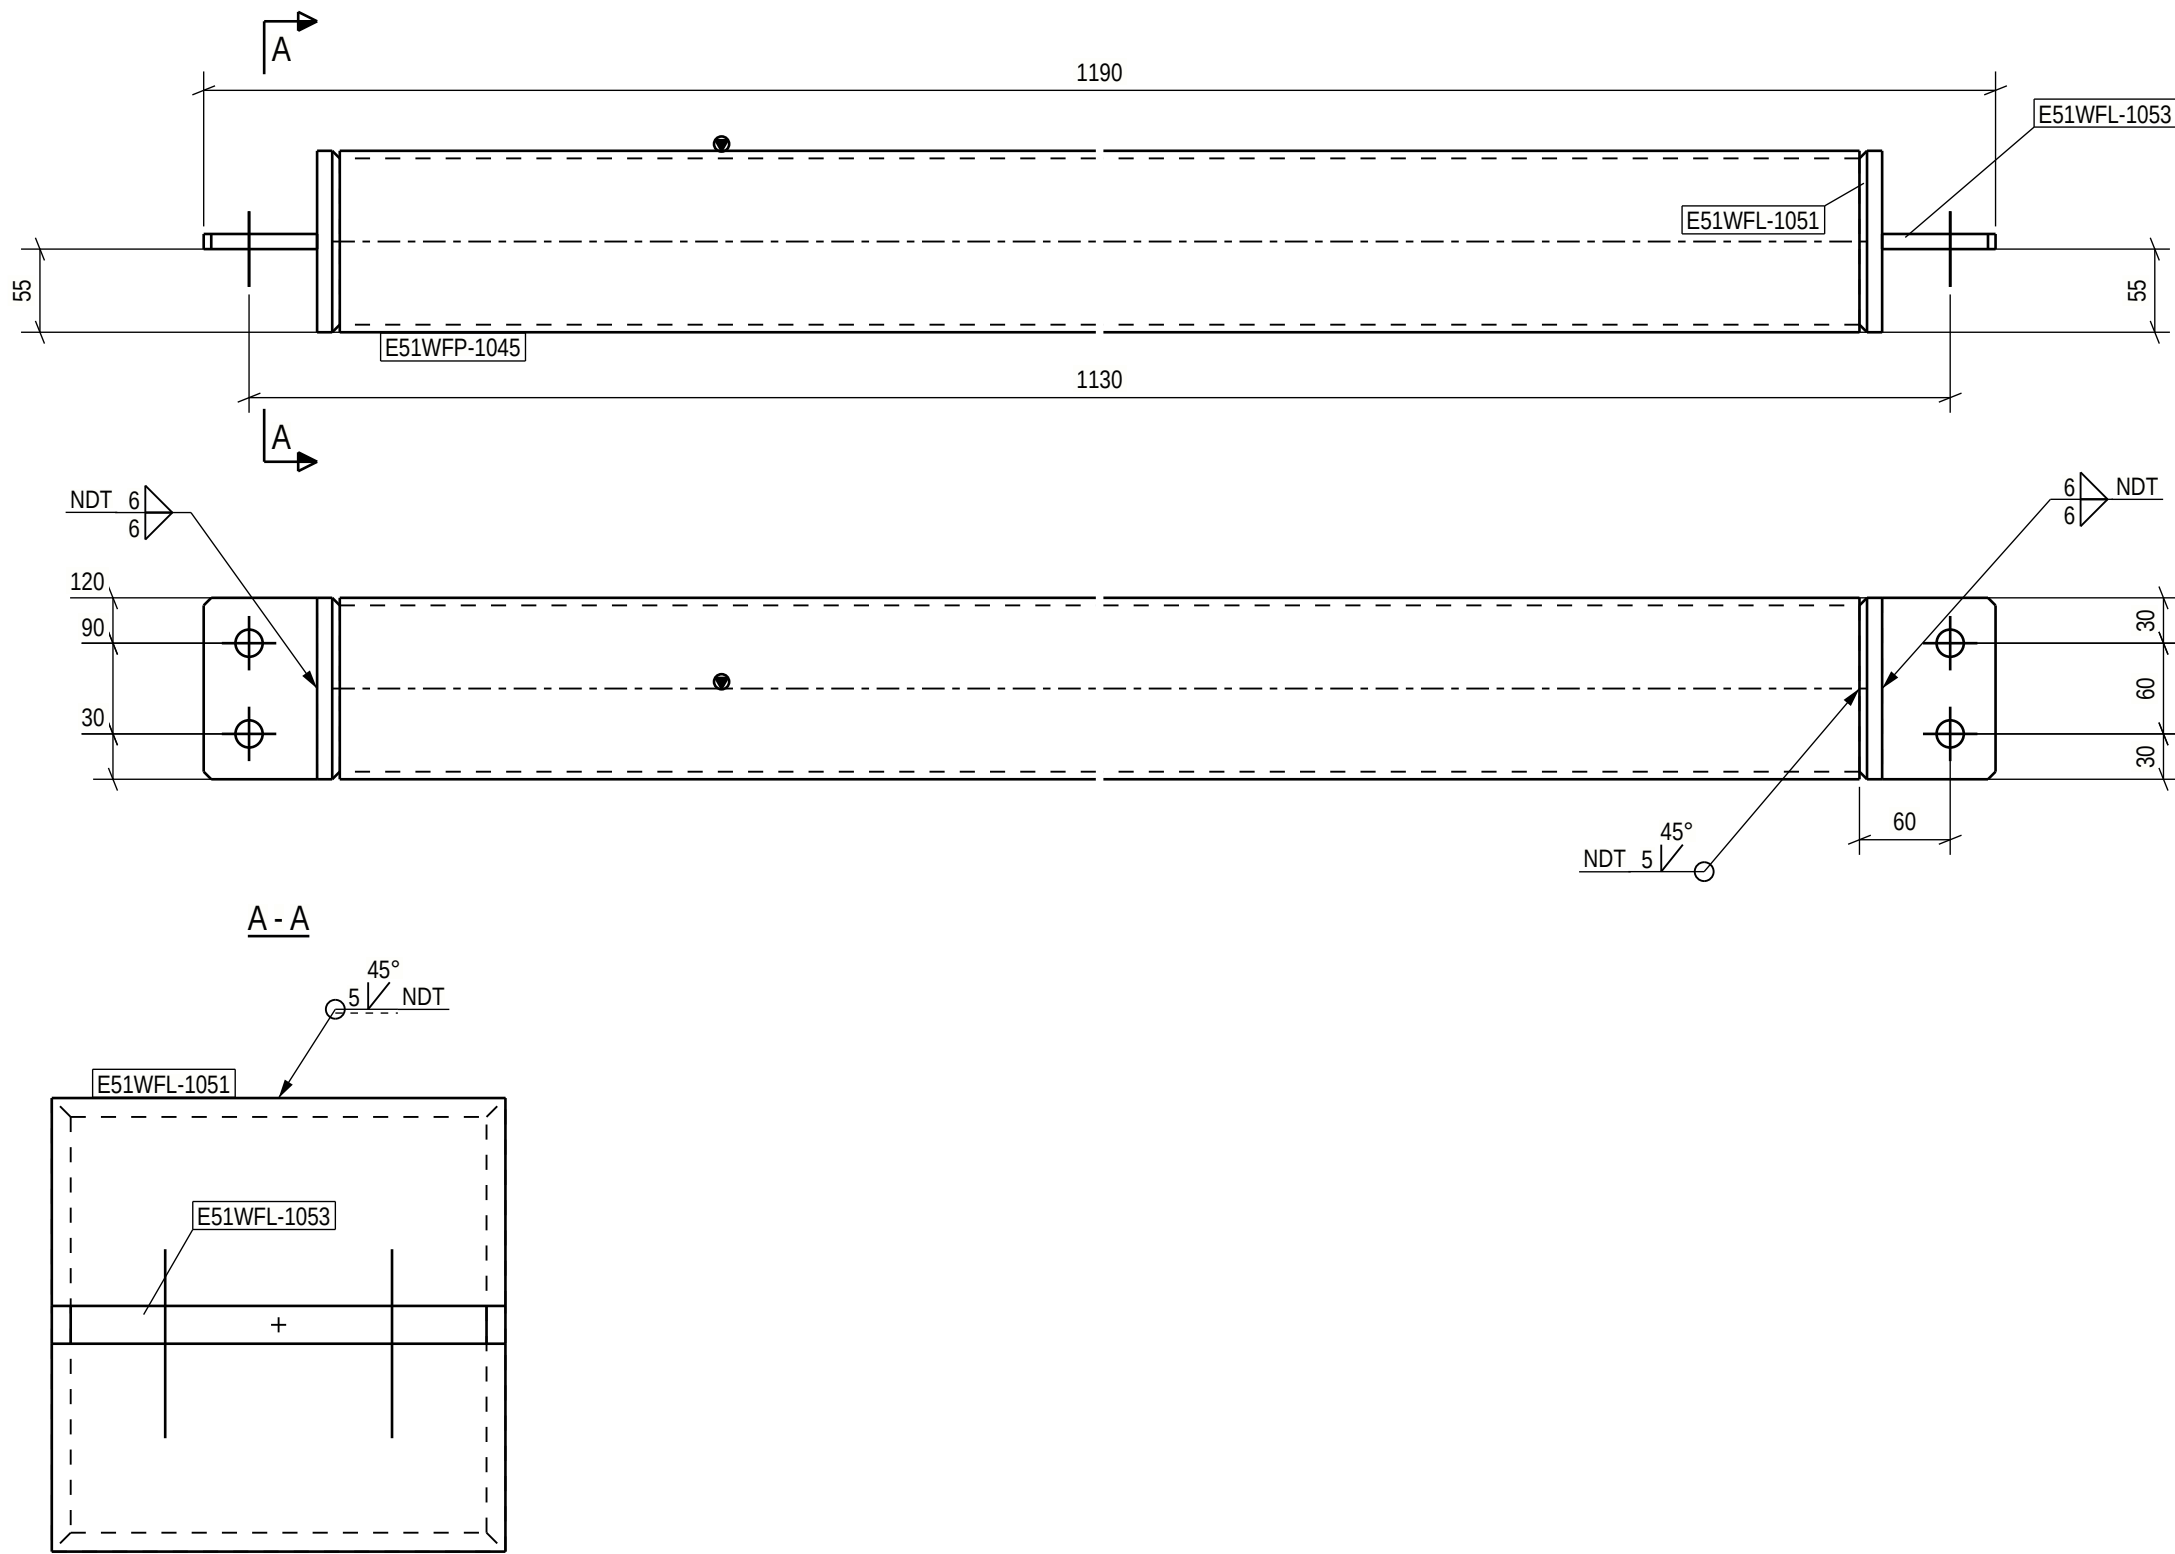


PART LIST FOR ASSEMBLY E51WF-1056, MANUFACTURING AMOUNT 4 PIECES						
PART	PROFILE	MATERIAL	LENGTH [mm]	AREA [m2]	WEIGHT [kg]	PCS
E51WFL-1051	PL15X120	S355J2+N	120	0.07	1.6	2
E51WFL-1053	PL10X75	S355J2+N	120	0.04	0.7	2
E51WFP-1045	CFRHS120X120X5	S355J2H	1010	0.47	17.7	1
TOTAL:				0.58	22.4	

LIFTING LUG WELDING, WEIGHT < 1,5 t

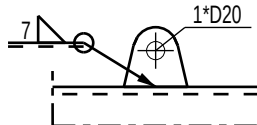

Technical fabrication requirements:		Execution class		EXC2 Approved For Construction									
Requirements for fabrication, standard EN1090-2, table A.3 : EXC2		Fabrication tolerances EN 1090-2, Appendix B		PROJECT NAME Easpring New Materials Oy FAIR Phase 1				DRAWING CONTENT ASSEMBLY DRAWING FRAME E51WF-1056					
Execution Specification document nr 25019443-ICC250-0600-0660-000005		Special fabrication tolerances Project specification/ shown on drwg.											
Surface preparation grade ISO8501-3, grade P2		Weld inspection, requirements EN 1090-2, Table 24, U>0.5		SWECO  SWECO RAKENNETEKNIikka OY ILMALANPORTTI 2 00240 HELSINKI PUH. +358 207 393 000 www.sweco.fi		DATE 12.06.2026		ARCHIVING CODE		PAGE		DESIGN GROUP STR	
Surface treatment ISO12944-5		Extent of NDT, fillet welds MT-EN1290, 20% of welds				DRAWN Alexey Serous		DESIGNER Alexey Serous		APPROVED Pertti Koivumaaanaho		CHECKED Jere Kalliosalmi	
Additional requirements on surface treatment C3.07, EPPUR 240/2		Extent of NDT, butt welds UT, EN-ISO17640, 20% of welds		SWECO Sustainable engineering and design		PROJECT NUMBER 25019443		DWS. NO. E51WF-1056					
Shade RAL 7024 (Graphite Gray)		Extent of NDT for splices not shown on drawing UT, EN-ISO17640, 100% of welds											
Welding of built up steel section Appendix 1 / Project spec.		Requirements on holing EN1090-2 Section 6.6.3											
Welds, if not specified otherwise EN 9692-1, EN 9692-2		Weld class C, EN ISO 5817		Additional material inspection Shown on drwg.									
													

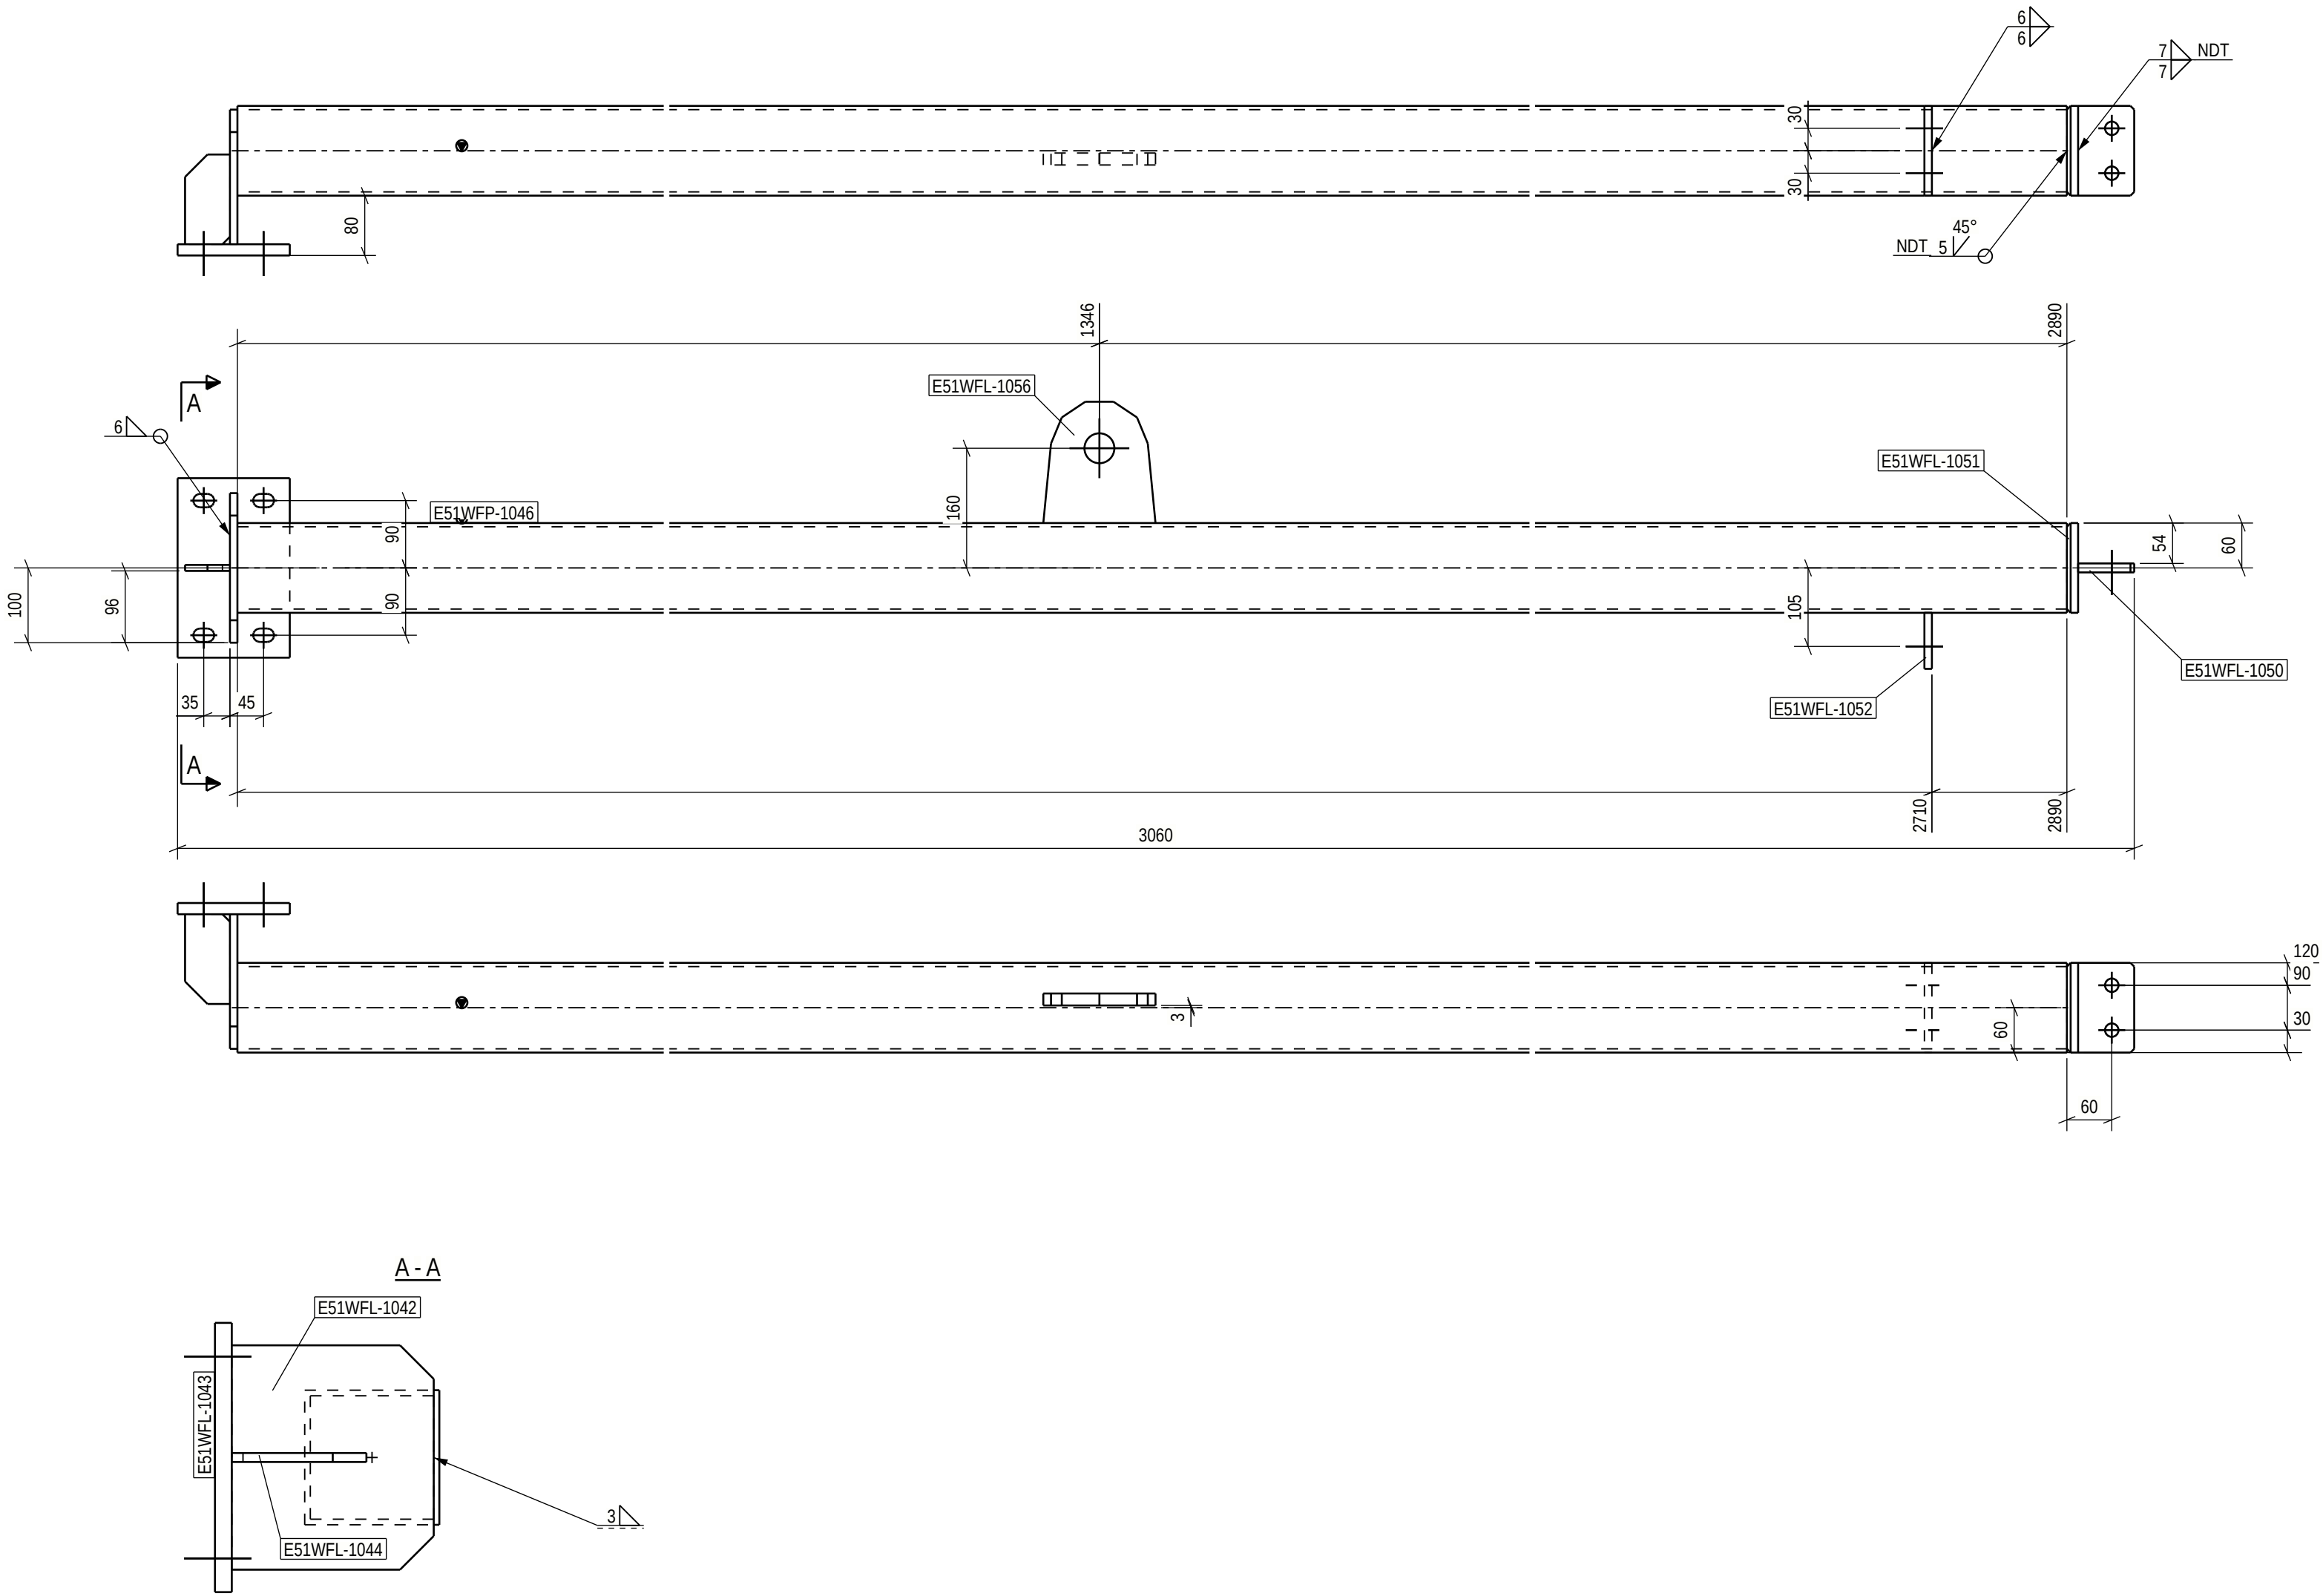

PART LIST FOR ASSEMBLY E51WF-1059, MANUFACTURING AMOUNT 1 PIECES						
PART	PROFILE	MATERIAL	LENGTH [mm]	AREA [m2]	WEIGHT [kg]	PCS
E51WFL-1042	PL10X200	S355J2+N	180	0.08	2.8	1
E51WFL-1043	PL15X150	S355J2+N	240	0.08	4.2	1
E51WFL-1044	PL8X60	S355J2+N	120	0.02	0.4	1
E51WFL-1050	PL12X75	S355J2+N	120	0.02	0.8	1
E51WFL-1051	PL15X120	S355J2+N	120	0.03	1.6	1
E51WFL-1052	PL10X75	S355J2+N	120	0.02	0.7	1
E51WFL-1056	PL16X162	S355J2	150	0.05	2.6	1
E51WFP-1046	CFRHS120X120X5	S355J2H	2890	1.34	50.7	1
TOTAL:				1.64	63.9	

LIFTING LUG WELDING, WEIGHT < 1,5 t

Technical fabrication requirements:

Requirements for fabrication, standard
EN1090-2, table A.3 : EXC2

Execution Specification document nr
25019443-ICC250-0600-0660-000005

Surface preparation grade
ISO8501-3, grade P2

Surface treatment
ISO12944-5

Additional requirements on surface treatment
C3.07, EPPUR 240/2

Shade
RAL 7024 (Graphite Gray)

Welding of built up steel section
Appendix 1 / Project spec.

Welds, if not specified otherwise
EN 9692-1, EN 9692-2

Fabrication tolerances
EN 1090-2, Appendix B

Special fabrication tolerances
Project specification/ shown on drwg.

Weld inspection, requirements
EN 1090-2, Table 24, U>0.5

Extent of NDT, fillet welds
MT-EN1290, 20% of welds

Extent of NDT, butt welds
UT, EN-ISO17640, 20% of welds

Extent of NDT for splices not shown on drawing
UT, EN-ISO17640, 100% of welds

Requirements on holing
EN1090-2 Section 6.6.3

Weld class
C, EN ISO 5817

Additional material inspection
Shown on drwg.


Execution class
EXC2

Approved For Construction

Easpring New Materials Oy
FAIR Phase 1




SWECO RAKENNETEKNIikka OY
ILMALANPORTTI 2
00240 HELSINKI
PUH. +358 207 393 000
www.sweco.fi

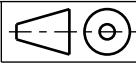


DRAWING CONTENT
ASSEMBLY DRAWING
FRAME
E51WF-1059

DATE	ARCHIVING CODE	PAGE	DESIGN GROUP
12.06.2026			STR
DRAWN	DESIGNER	APPROVED	CHECKED
Alexey Serous	Alexey Serous	Pertti Koivumaa	Jere Kallosalmi
PROJECT NUMBER	DWG. NO.	REVISION	
25019443	E51WF-1059		

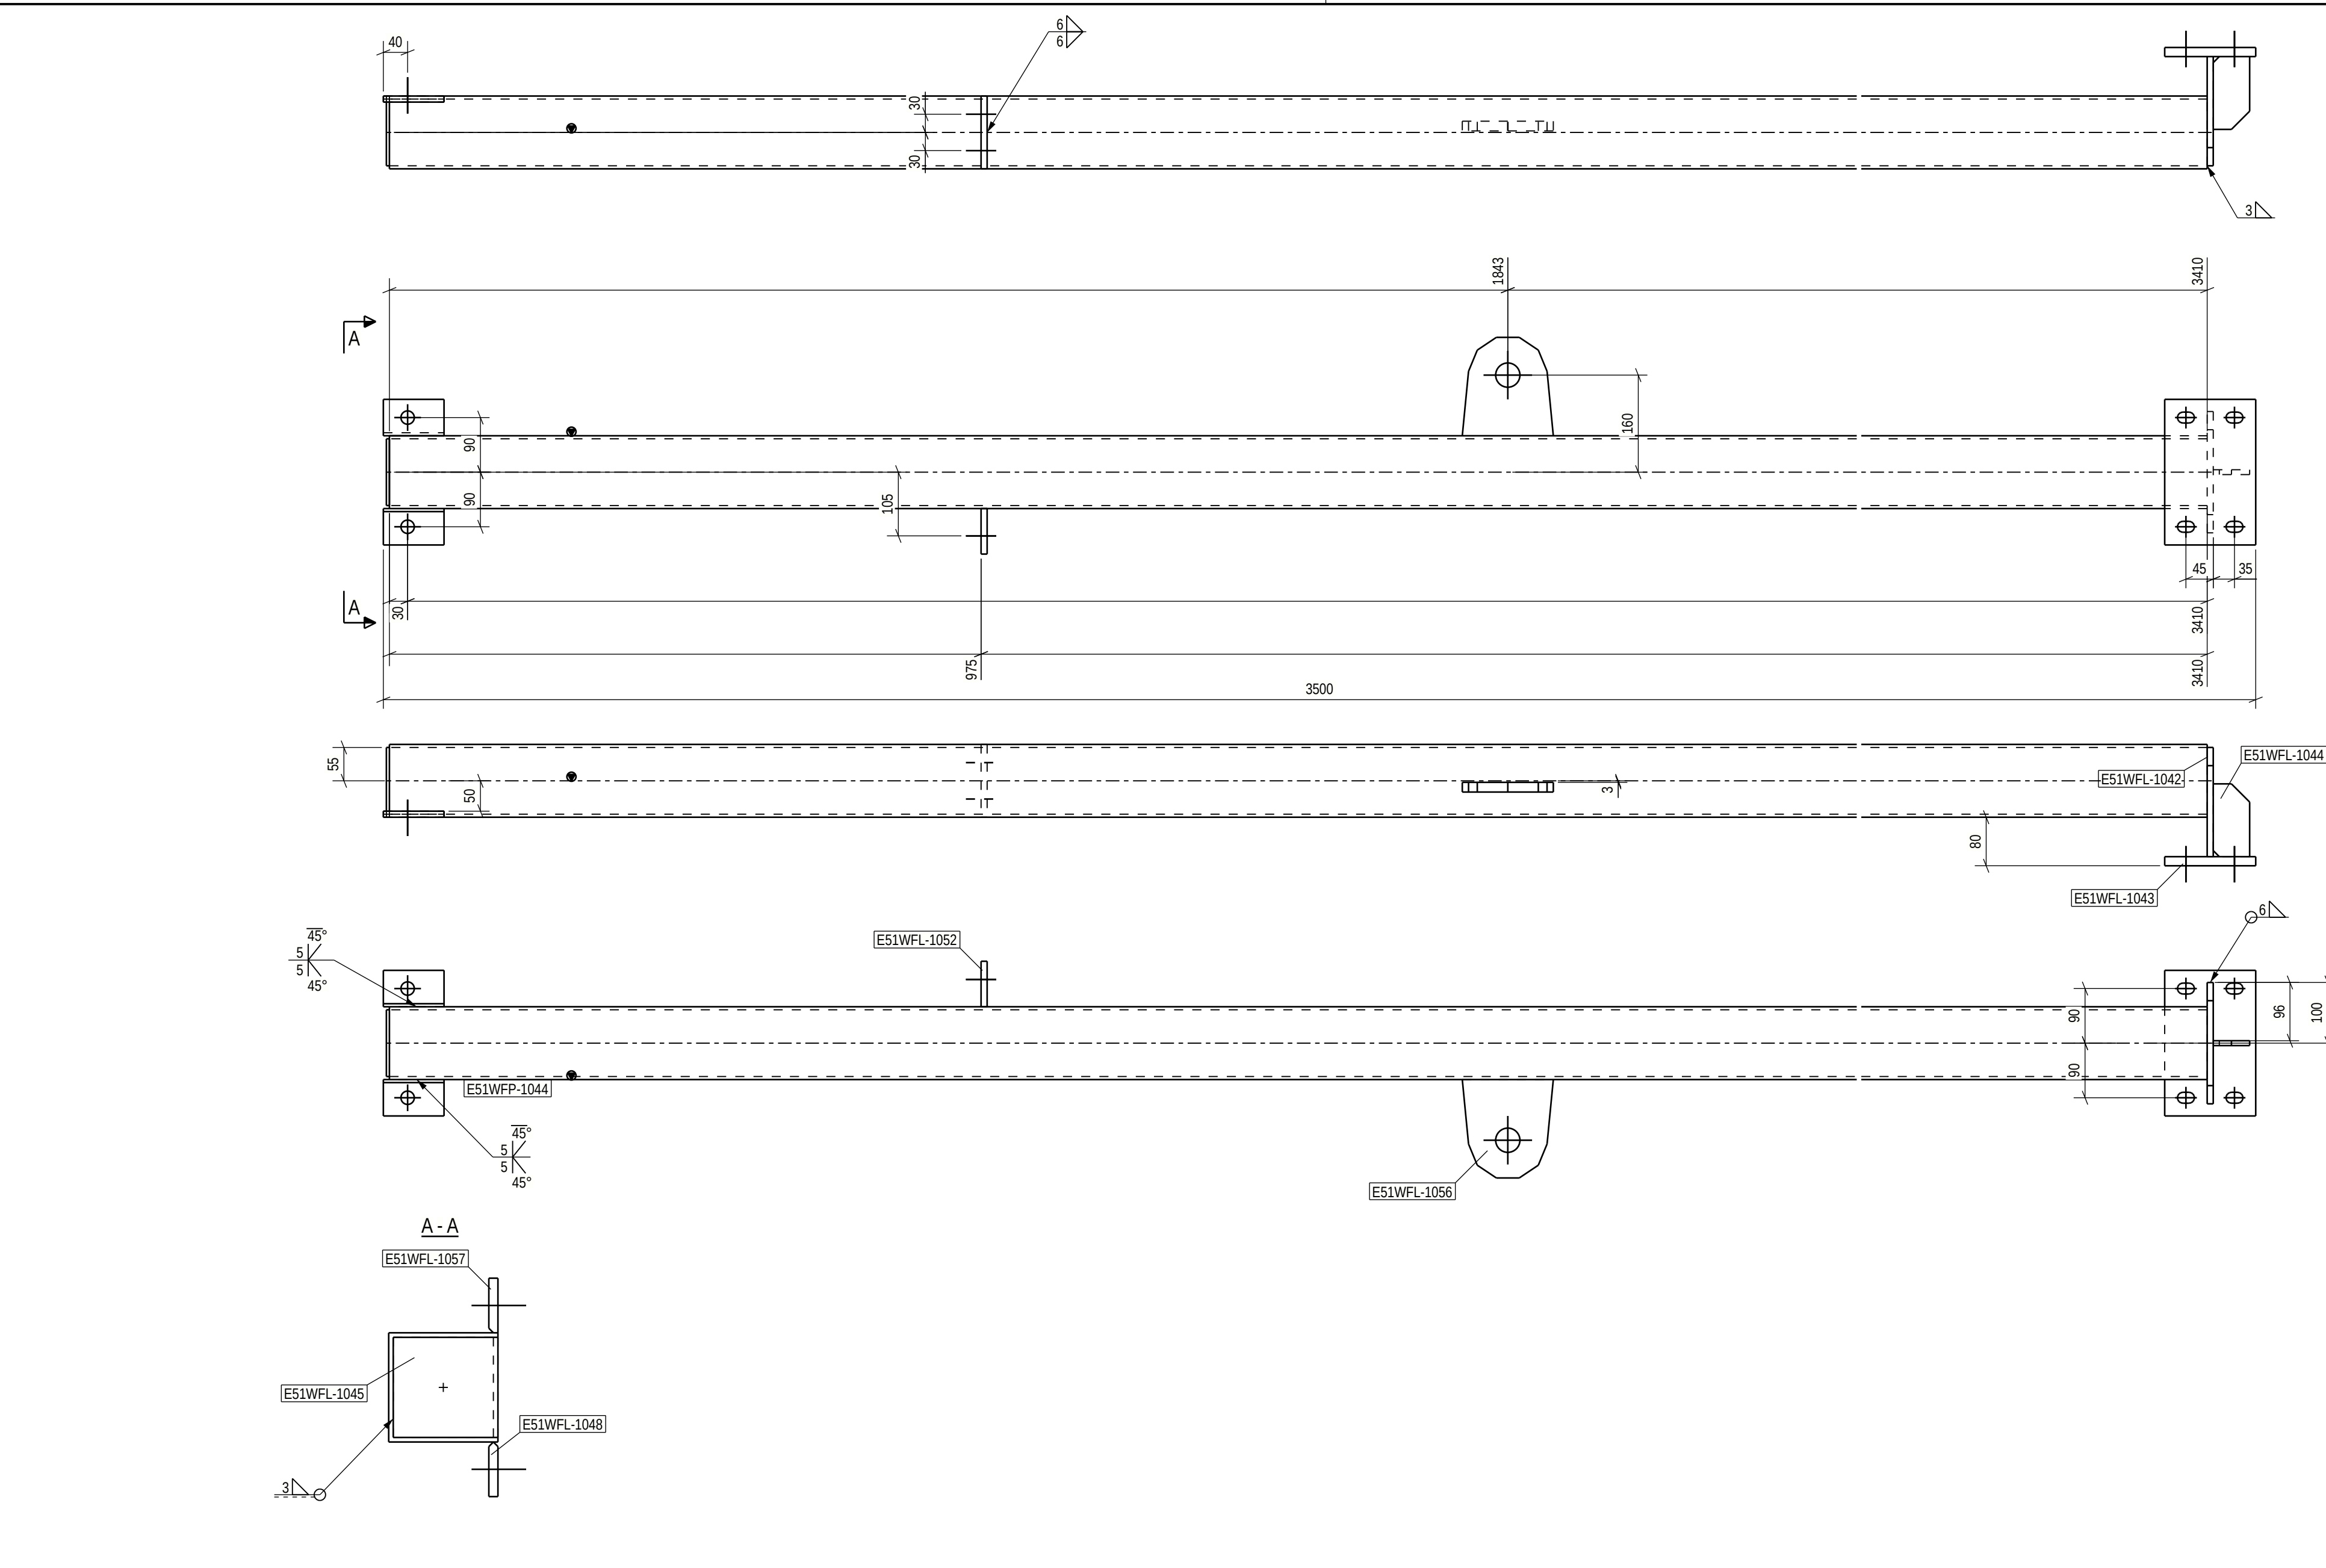

PART LIST FOR ASSEMBLY E51WF-1060, MANUFACTURING AMOUNT 1 PIECES						
PART	PROFILE	MATERIAL	LENGTH [mm]	AREA [m ²]	WEIGHT [kg]	PCS
E51WFL-1042	PL10X200	S355J2+N	180	0.08	2.8	1
E51WFL-1043	PL15X150	S355J2+N	240	0.08	4.2	1
E51WFL-1044	PL8X60	S355J2+N	120	0.02	0.4	1
E51WFL-1045	PL5X110	S355J2+N	115	0.03	0.5	1
E51WFL-1048	PL10X60	S355J2+N	100	0.01	0.5	1
E51WFL-1052	PL10X75	S355J2+N	120	0.02	0.7	1
E51WFL-1056	PL16X162	S355J2	150	0.05	2.6	1
E51WFL-1057	PL10X60	S355J2+N	100	0.01	0.5	1
E51WFP-1044	CFRHS120X120X5	S355J2H	3410	1.58	59.8	1
TOTAL:				1.88	71.9	

LIFTING LUG WELDING, WEIGHT < 1,5 t

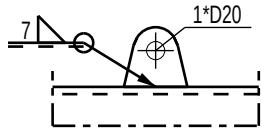


Technical fabrication requirements:		Execution class
Requirements for fabrication, standard EN1090-2, table A.3 : EXC2		EXC2
Execution Specification document nr 25019443-ICC250-0600-0660-000005		
Surface preparation grade ISO8501-3, grade P2		Fabrication tolerances EN 1090-2, Appendix B Special fabrication tolerances Project specification/ shown on drwg.
Surface treatment ISO12944-5		Weld inspection, requirements EN 1090-2, Table 24, U>0.5
Additional requirements on surface treatment C3.07, EPPUR 240/2		Extent of NDT, fillet welds MT-EN1290, 20% of welds
Shade RAL 7024 (Graphite Gray)		Extent of NDT, butt welds UT, EN-ISO17640, 20% of welds
Welding of built up steel section Appendix 1 / Project spec.		Requirements on holing EN1090-2 Section 6.6.3
Welds, if not specified otherwise EN 9692-1, EN 9692-2		Weld class C, EN ISO 5817
		Additional material inspection Shown on drwg.

Approved For Construction

Easpring New Materials Oy
FAIR Phase 1





SWECO RAKENNETEKNIikka OY
ILMALANPORTTI 2
00240 HELSINKI
PUH. +358 207 393 000
www.sweco.fi

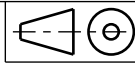


DRAWING CONTENT
ASSEMBLY DRAWING
FRAME
E51WF-1060

DATE	ARCHIVING CODE	PAGE	DESIGN GROUP
12.06.2026			STR
DRAWN	DESIGNER	APPROVED	CHECKED
Alexey Serous	Alexey Serous	Pertti Koivumaa	Jere Kallosalmi
PROJECT NUMBER	DWG. NO.	REVISION	
25019443	E51WF-1060		

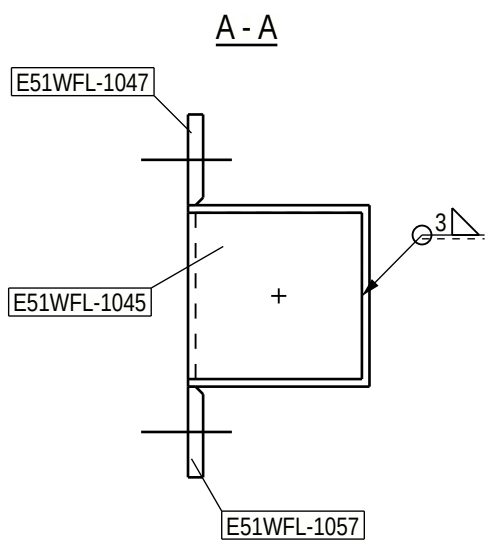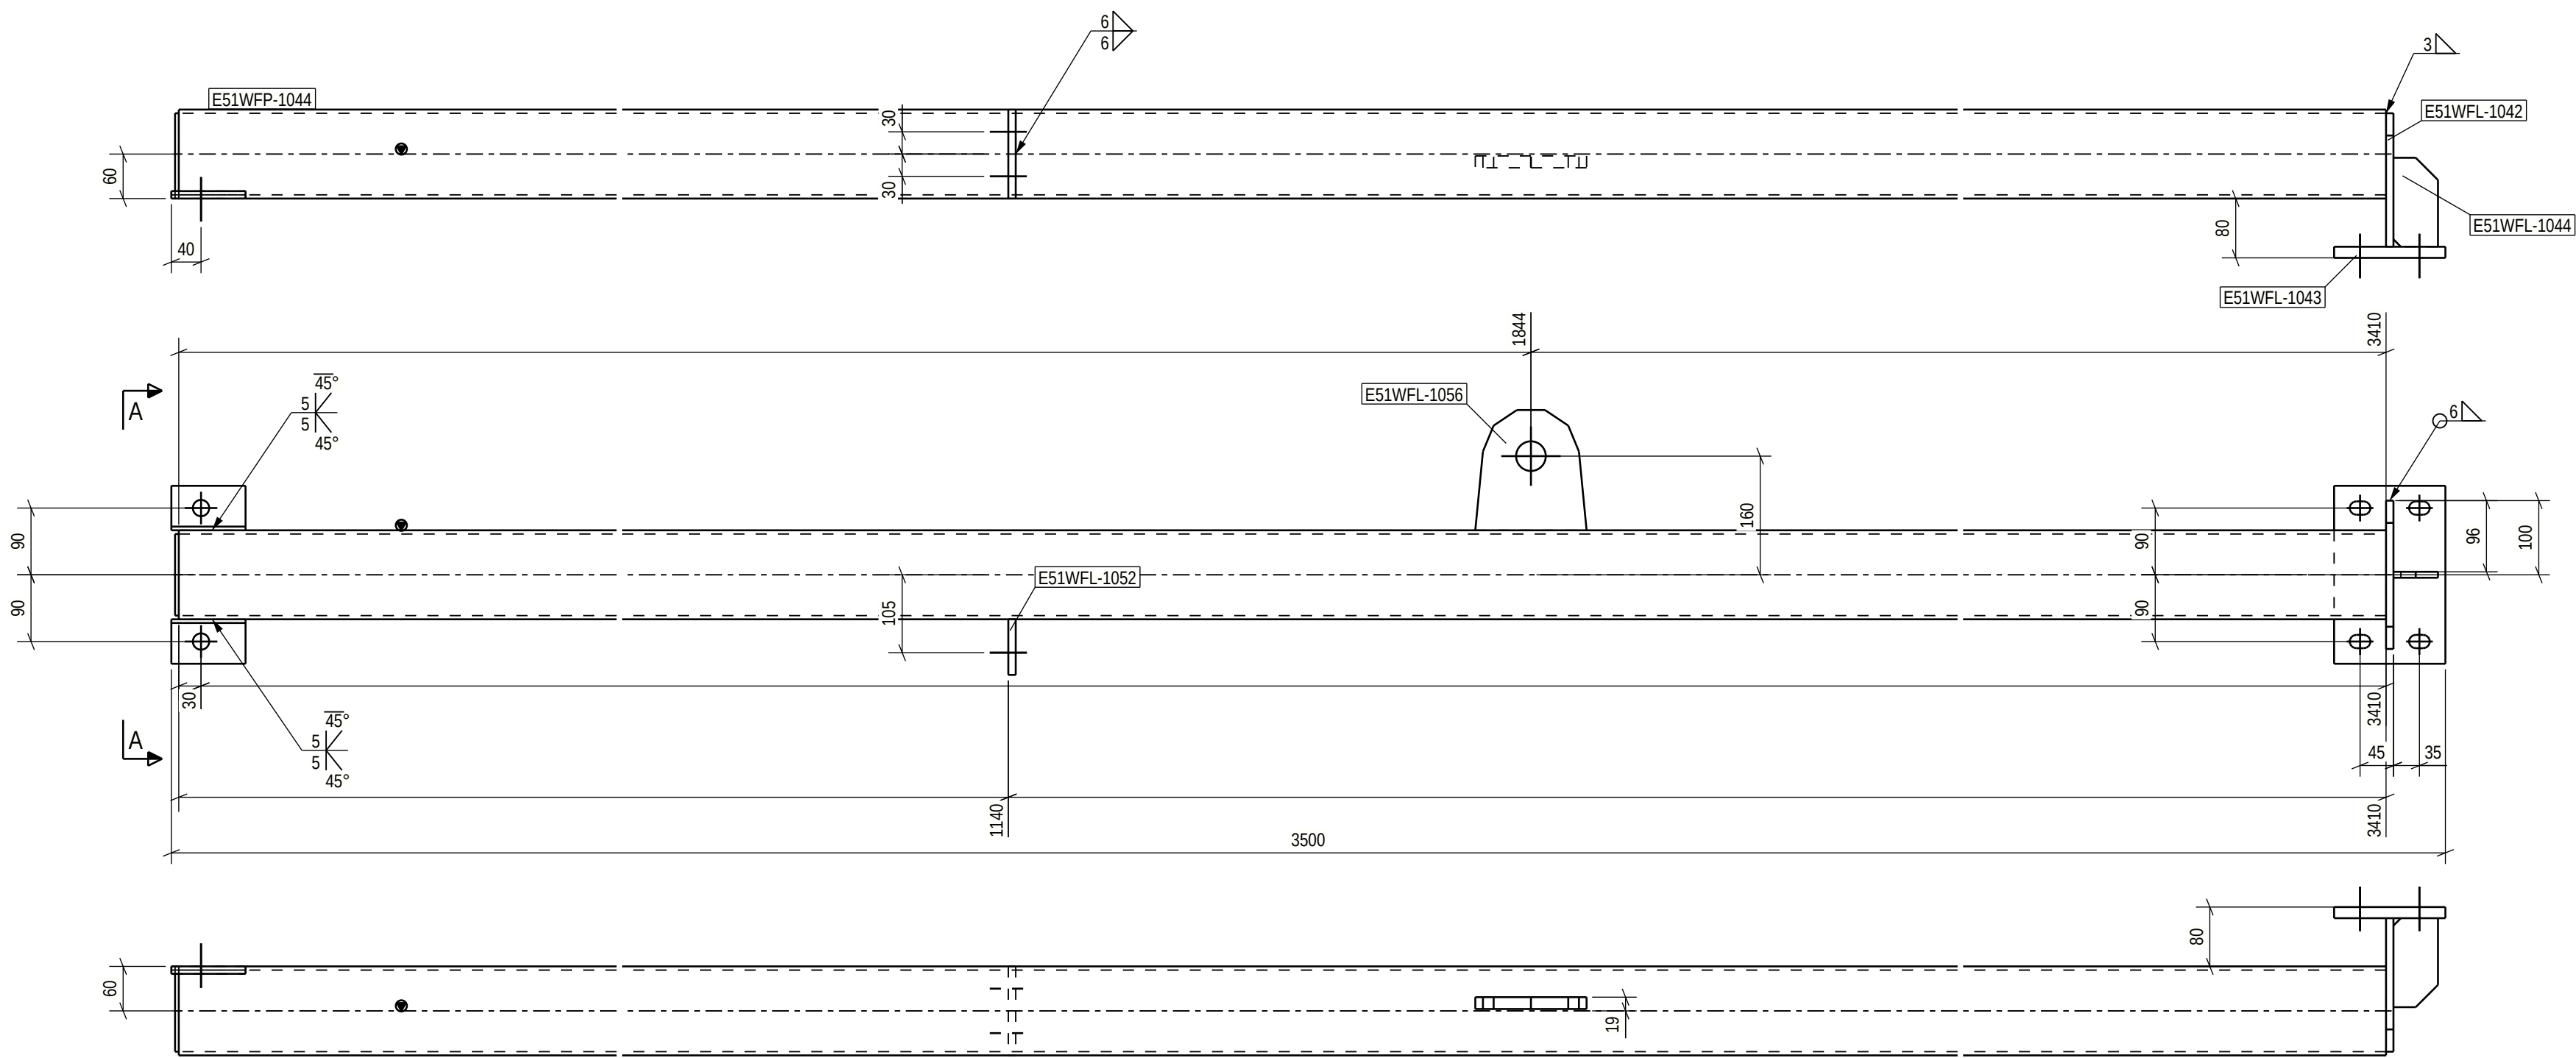

PART LIST FOR ASSEMBLY E51WF-1061, MANUFACTURING AMOUNT 1 PIECES						
PART	PROFILE	MATERIAL	LENGTH [mm]	AREA [m ²]	WEIGHT [kg]	PCS
E51WFL-1042	PL10X200	S355J2+N	180	0.08	2.8	1
E51WFL-1043	PL15X150	S355J2+N	240	0.08	4.2	1
E51WFL-1044	PL8X60	S355J2+N	120	0.02	0.4	1
E51WFL-1045	PL5X110	S355J2+N	115	0.03	0.5	1
E51WFL-1047	PL10X60	S355J2+N	100	0.01	0.5	1
E51WFL-1052	PL10X75	S355J2+N	120	0.02	0.7	1
E51WFL-1056	PL16X162	S355J2	150	0.05	2.6	1
E51WFL-1057	PL10X60	S355J2+N	100	0.01	0.5	1
E51WFP-1044	CFRHS120X120X5	S355J2H	3410	1.58	59.8	1
TOTAL:				1.88	71.9	

LIFTING LUG WELDING, WEIGHT < 1,5 t

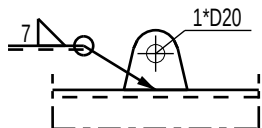


Technical fabrication requirements:		Execution class
Requirements for fabrication, standard EN1090-2, table A.3 : EXC2		EXC2
Execution Specification document nr 25019443-ICC250-0600-0660-000005		
Surface preparation grade ISO8501-3, grade P2	Fabrication tolerances EN 1090-2, Appendix B	
Surface treatment ISO12944-5	Special fabrication tolerances Project specification/ shown on drwg.	
Additional requirements on surface treatment RAL 7024 (Graphite Gray)	Weld inspection, requirements EN 1090-2, Table 24, U>0.5	
Welding of built up steel section Appendix 1 / Project spec.	Extent of NDT, fillet welds MT-EN1290, 20% of welds	
Welds, if not specified otherwise EN 9692-1, EN 9692-2	Extent of NDT, butt welds UT, EN-ISO17640, 20% of welds	
	Requirements on holing EN1090-2 Section 6.6.3	
	Weld class C, EN ISO 5817	Additional material inspection Shown on drwg.

Approved For Construction

Easpring New Materials Oy
FAIR Phase 1



SWECO RAKENNETEKNIikka OY
ILMALANPORTTI 2
00240 HELSINKI
PUH. +358 207 393 000
www.sweco.fi

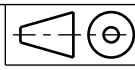

DRAWING CONTENT
ASSEMBLY DRAWING
FRAME
E51WF-1061

DATE	ARCHIVING CODE	PAGE	DESIGN GROUP
12.06.2026			STR
DRAWN	DESIGNER	APPROVED	CHECKED
Alexey Serous	Alexey Serous	Pertti Koivumaa	Jere Kallosalmi
PROJECT NUMBER	DWG. NO.	REVISION	
25019443	E51WF-1061		