


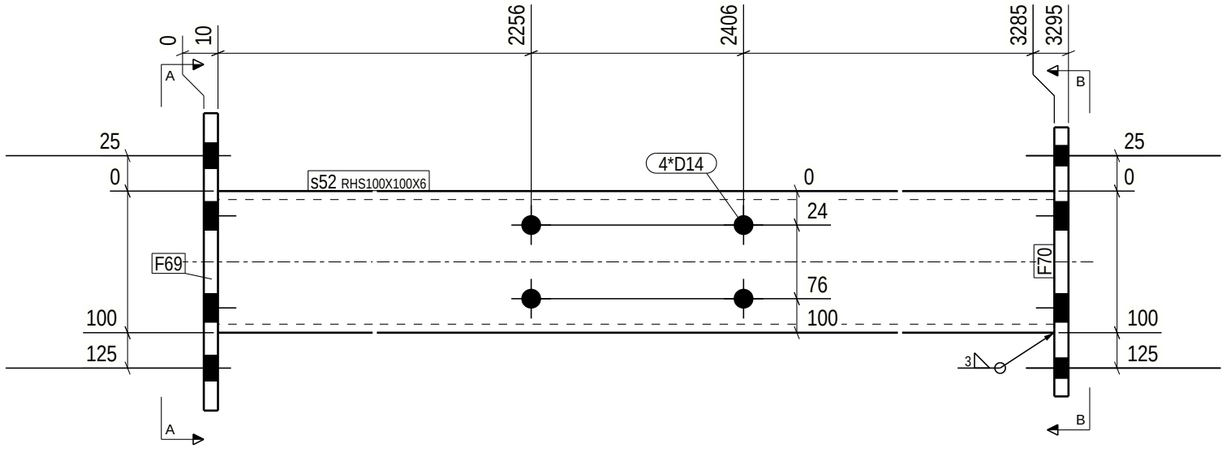


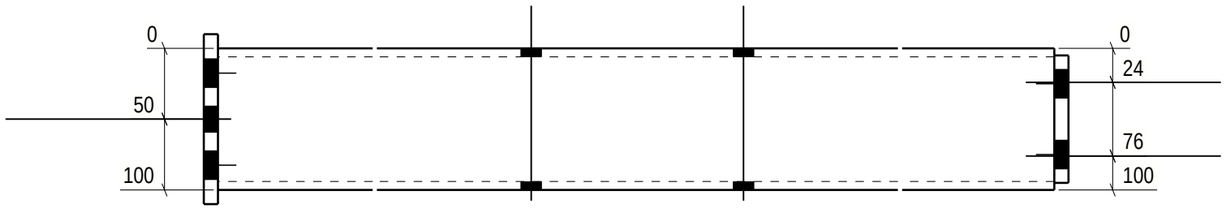


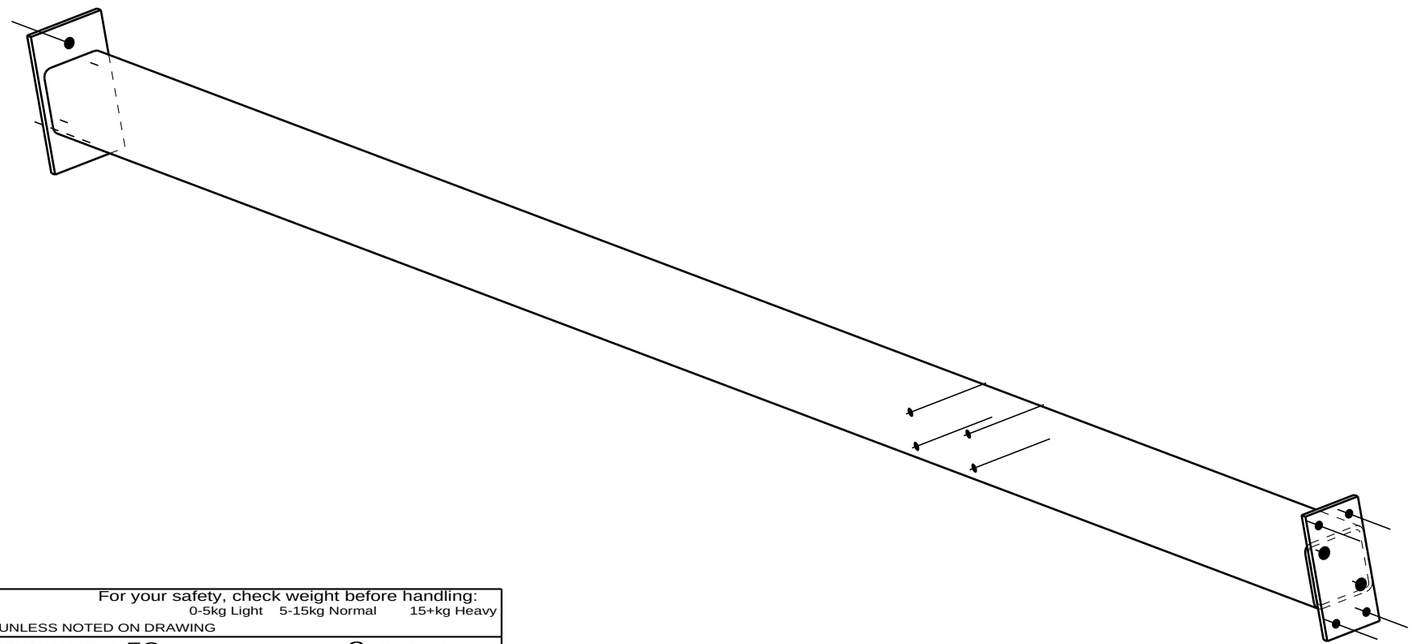

A - A
1:2

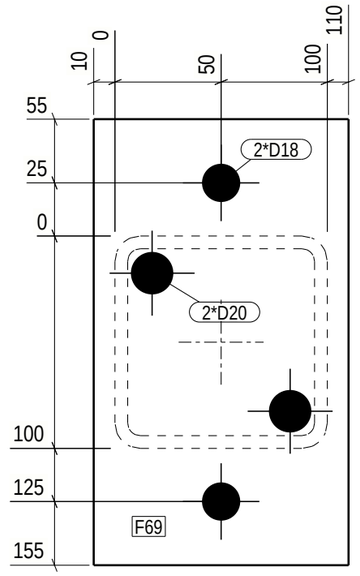

B - B
1:2

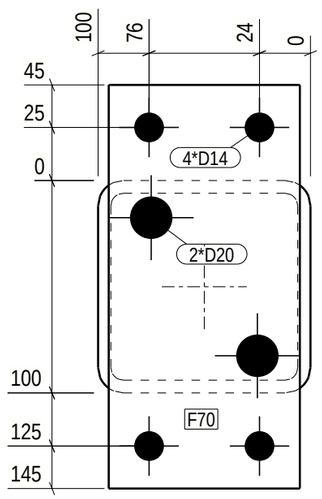

GENERAL NOTES: For your safety, check weight before handling: 0-5kg Light 5-15kg Normal 15+kg Heavy

ALL WELDS ARE 4 UNLESS NOTED ON DRAWING

MATERIAL LIST FOR ASSEMBLY MK'D s.52 2 No. Required

Mark	Profile	Material	No.	Length	Area	Weight
s52	RHS100X100X6	S355J2H	1	3275	1.3	55.4 !!
F69	FL10*120	S355J2	1	210	0.1	2.0
F70	FL10*90	S355J2	1	190	0.0	1.3
				Total	1.4	58.7

Finish Class
Standard

Surface treatment info:	Thickness/start point--> length	No.
Galvanised	/	2

Special surface treatment

weld a = 4

PHASE	QUANTITY
3	2

* o 3 0 4 8 0 - 3 * DS Stålkonstruktion * A s 5 2 *

PROJECT	Akkasæter Lager- og vedlikeholdshall			EXEC. CLASS	EXC 2
MEMBER	Søjle		QUANTITY: 2	PROJECT No	30480-3
REVISION		ISSUED: 04.11.2025	DRAFTER: ZLL BIM control: SST	DRAWING No.	s.52

Tekla Structures