
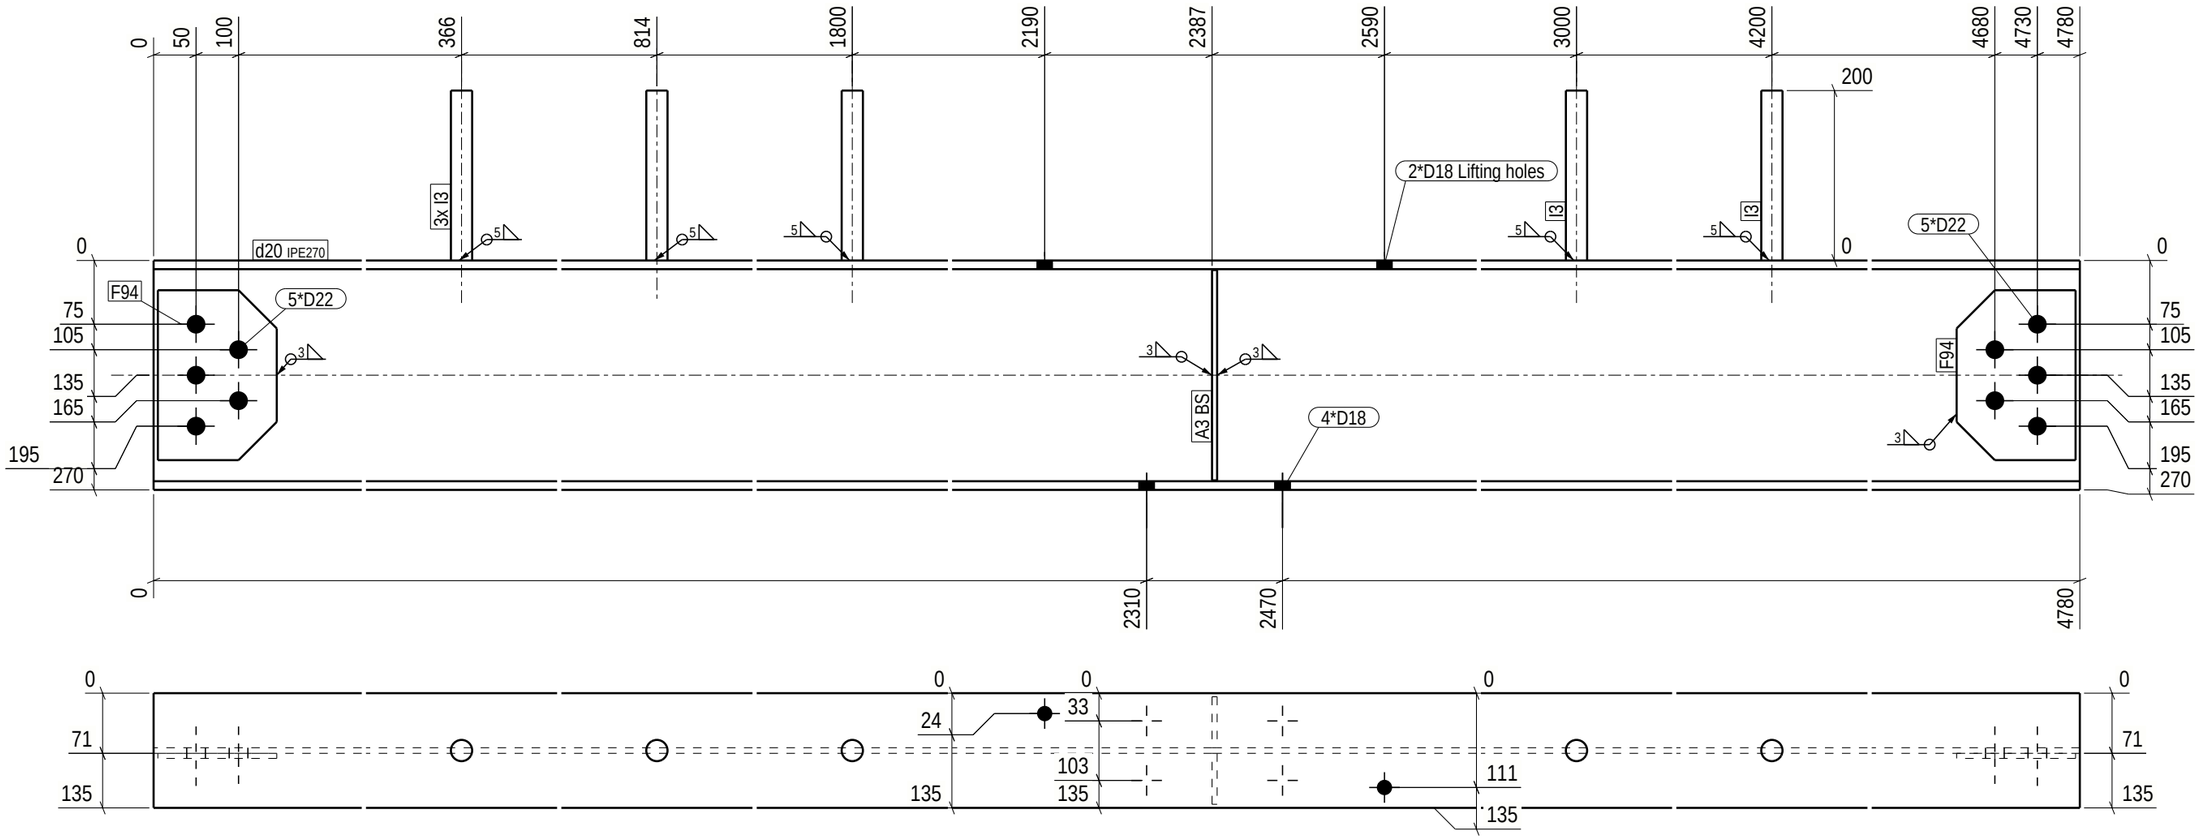


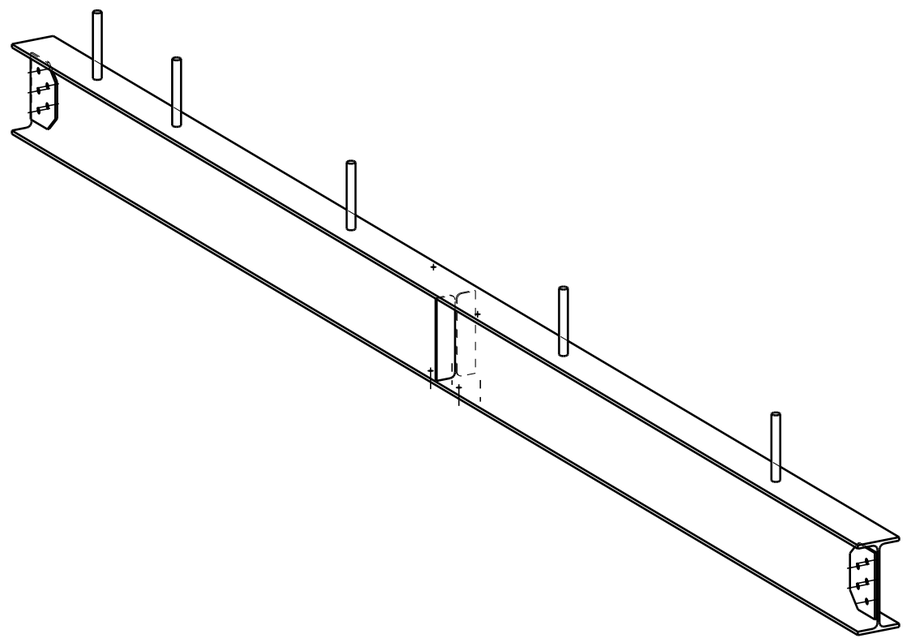

GENERAL NOTES: For your safety, check weight before handling: 0-5kg Light 5-15kg Normal 15+kg Heavy

ALL WELDS ARE 4 ◺ UNLESS NOTED ON DRAWING

MATERIAL LIST FOR ASSEMBLY MK'D d.20 1 No. Required

Mark	Profile	Material	No.	Length	Area	Weight
d20	IPE270	S355J2	1	4780	5.0	172.2 !!
A3	FL6*60	S355J2	2	248	0.0	0.7
F94	FL6*140	S355J2	2	200	0.1	1.2
I3	REBAR25	B550B	5	200	0.0	0.7
				Total	5.2	179.7

Finish Class
Standard

Surface treatment info:	Thickness/start point--> length	No.
Overall Painting	C2M RAL7016µm whole	***1

Special surface treatment

weld a = 4◺

PHASE	QUANTITY
1	1

* o 3 0 4 8 0 - 1 * DS Stålkonstruktion * A d 2 0 *

PROJECT	Akkasæter Lager- og vedlikeholdshall			EXEC. CLASS	EXC 2
MEMBER	Drager		QUANTITY: 1	PROJECT No	30480-1
REVISION		ISSUED: 07.11.2025	DRAFTER: ZLL BIM control: SST	DRAWING No.	d.20

Tekla Structures