

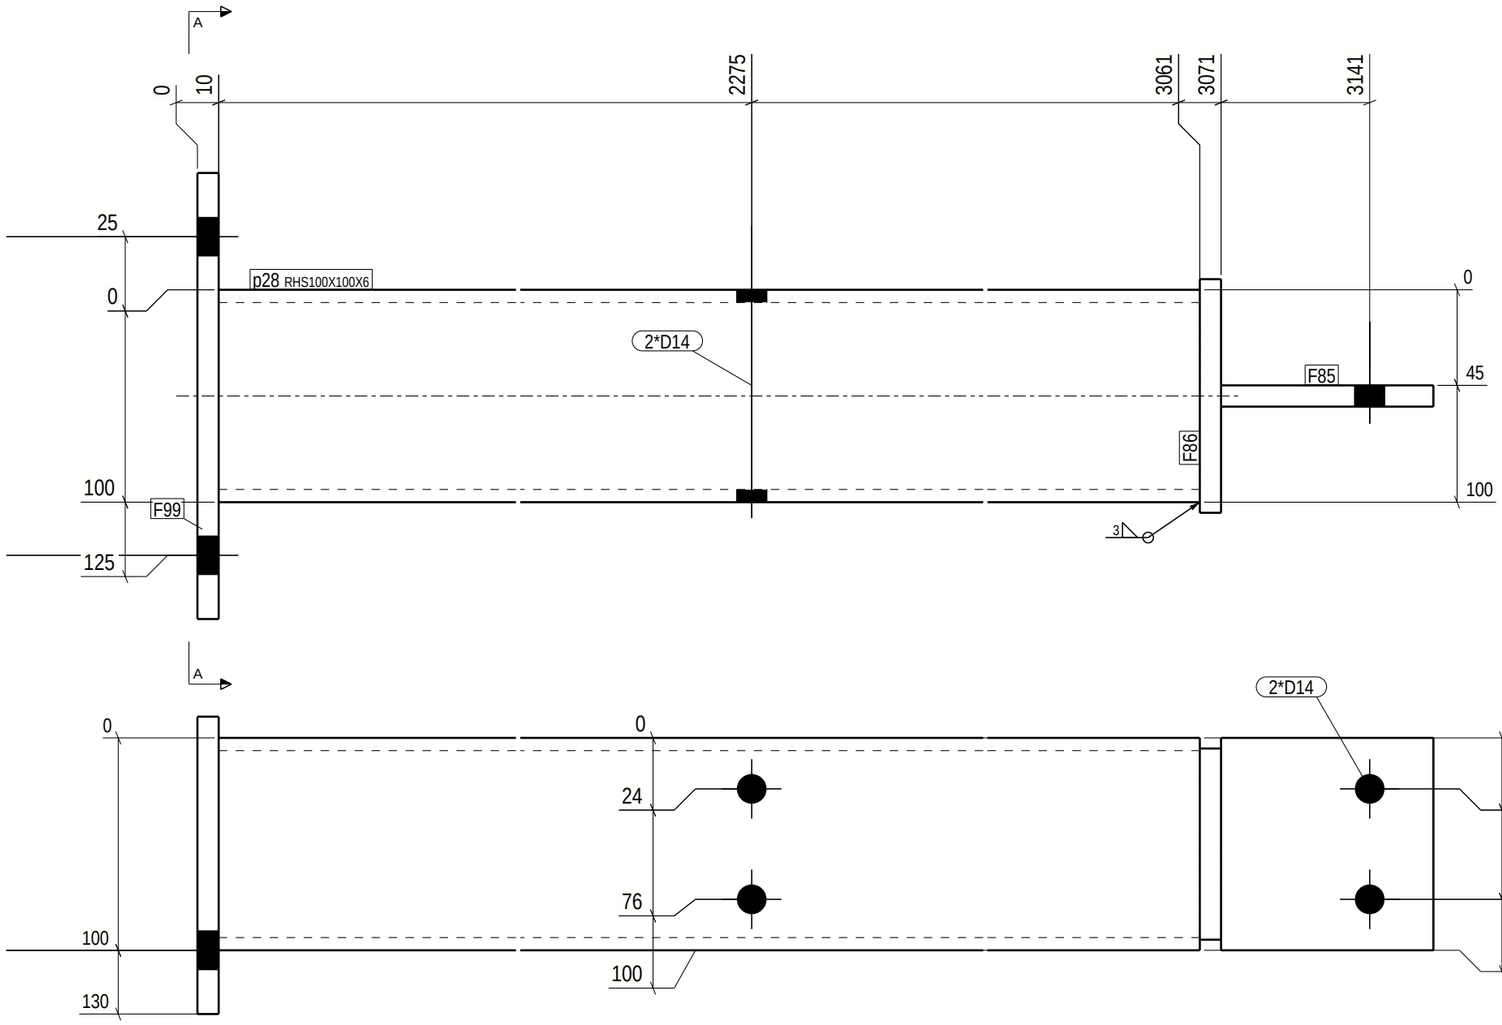


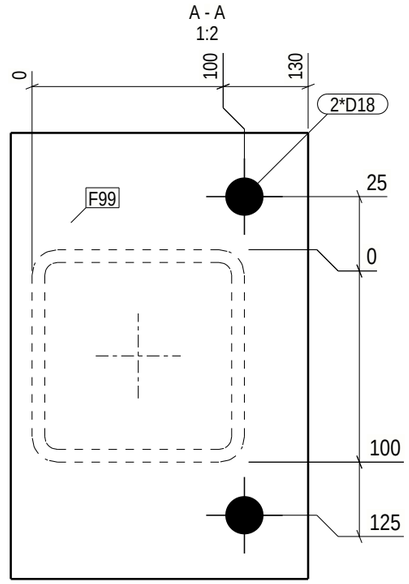

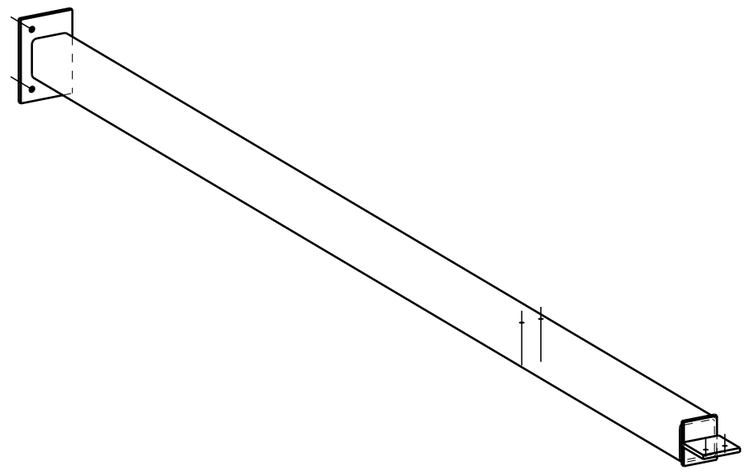

GENERAL NOTES: For your safety, check weight before handling: 0-5kg Light 5-15kg Normal 15+kg Heavy

ALL WELDS ARE 4 ◺ UNLESS NOTED ON DRAWING

MATERIAL LIST FOR ASSEMBLY MK'D p.28 1 No. Required

Mark	Profile	Material	No.	Length	Area	Weight
p28	RHS100X100X6	S355J2H	1	3051	1.2	51.6 !!
F85	FL10*100	S355J2	1	100	0.0	0.8
F86	FL10*90	S355J2	1	110	0.0	0.8
F99	FL10*140	S355J2	1	210	0.1	2.3
				Total	1.3	55.5

Finish Class
Standard

Surface treatment info:	Thickness/start point--> length	No.
Overall Painting	Primerµm whole asse***	1

Special surface treatment

weld a = 4◺

PHASE	QUANTITY
1	1

* o 3 0 4 8 0 - 1 * DS Stålkonstruktion * A p 2 8 *

PROJECT	Akkasæter Lager- og vedlikeholdshall			EXEC. CLASS	EXC 2
MEMBER	Portomfatning	QUANTITY:	1	PROJECT No	30480-1
REVISION	ISSUED: 07.11.2025	DRAFTER: ZLL BIM control: SST		DRAWING No.	p.28

Tekla Structures