


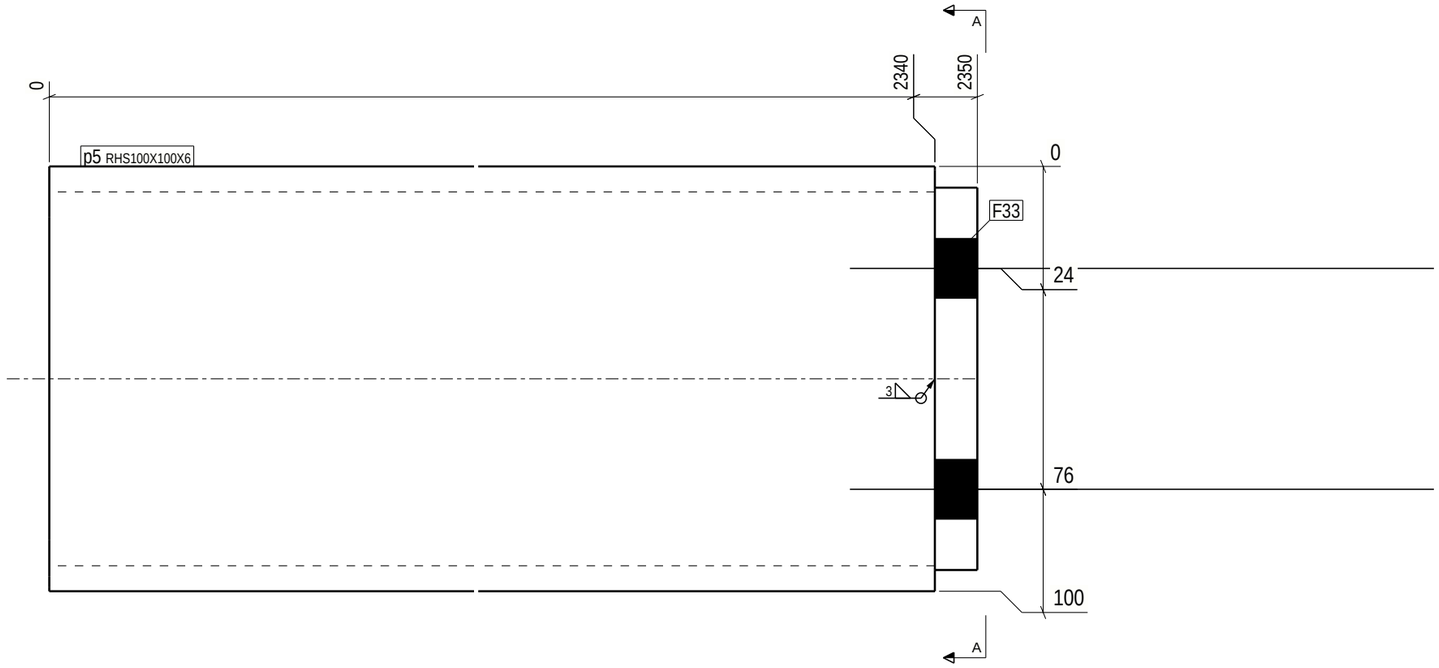


A - A
1:1

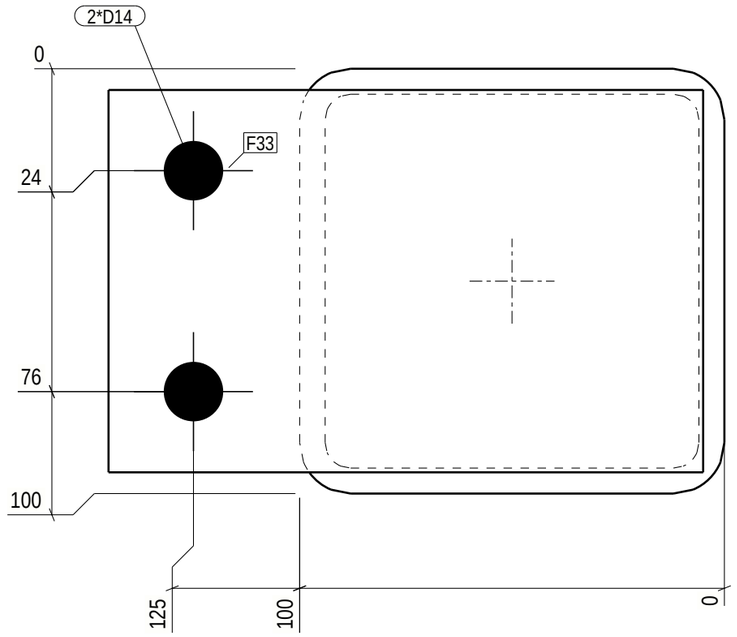

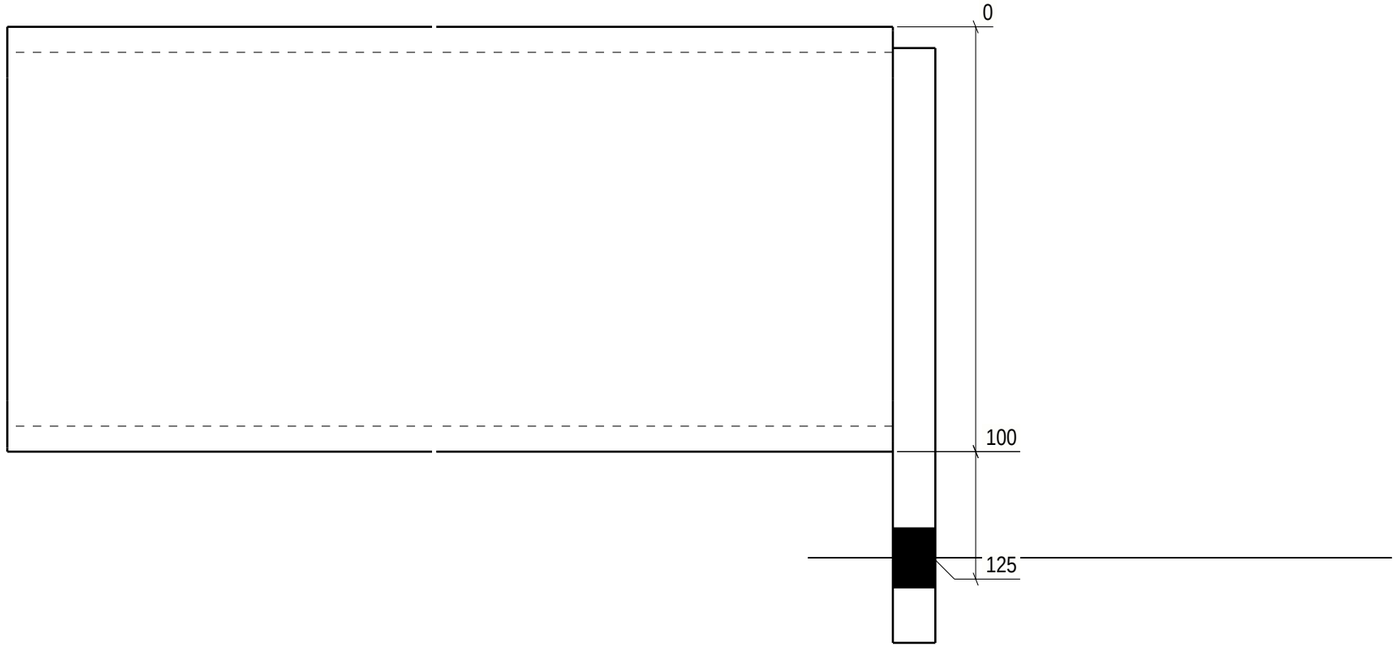

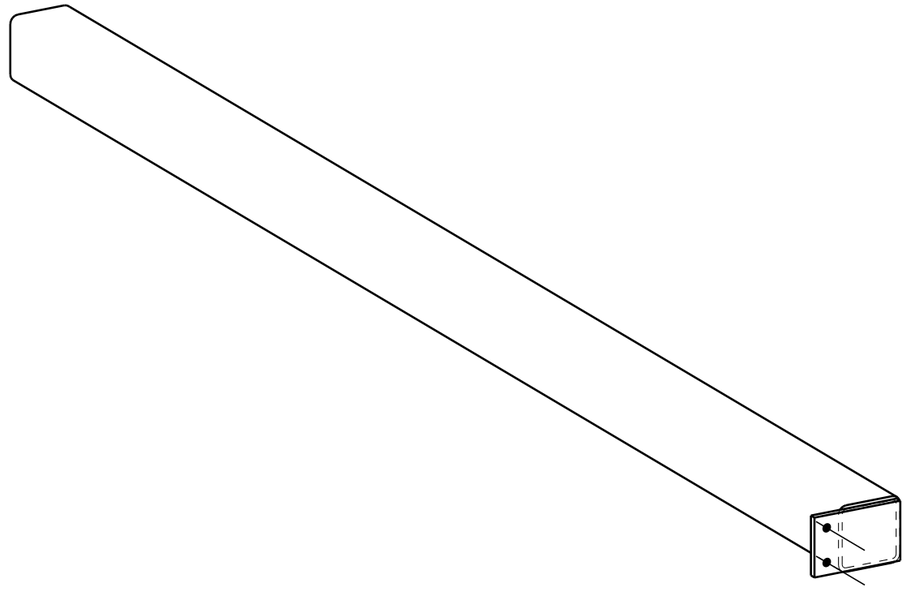

GENERAL NOTES: For your safety, check weight before handling: 0-5kg Light 5-15kg Normal 15+kg Heavy

ALL WELDS ARE 4 ◺ UNLESS NOTED ON DRAWING

MATERIAL LIST FOR ASSEMBLY MK'D p.5 1 No. Required

Mark	Profile	Material	No.	Length	Area	Weight
p5	RHS100X100X6	S355J2H	1	2340	0.9	39.6 !!
F33	FL10*90	S355J2	1	140	0.0	1.0
				Total	0.9	40.6

Finish Class
Standard

Surface treatment info:	Thickness/start point--> length	No.
Overall Painting	Primerµm whole asse***	1

Special surface treatment

weld a = 4◺

PHASE	QUANTITY
1	1

* o 3 0 4 8 0 - 1 * DS Stålkonstruktion * A p 5 *

PROJECT	Akkasæter Lager- og vedlikeholdshall			EXEC. CLASS	EXC 2
MEMBER	Portomfatning		QUANTITY: 1	PROJECT No	30480-1
REVISION		ISSUED: 07.11.2025	DRAFTER: ZLL BIM control: SST	DRAWING No.	p.5

Tekla Structures