



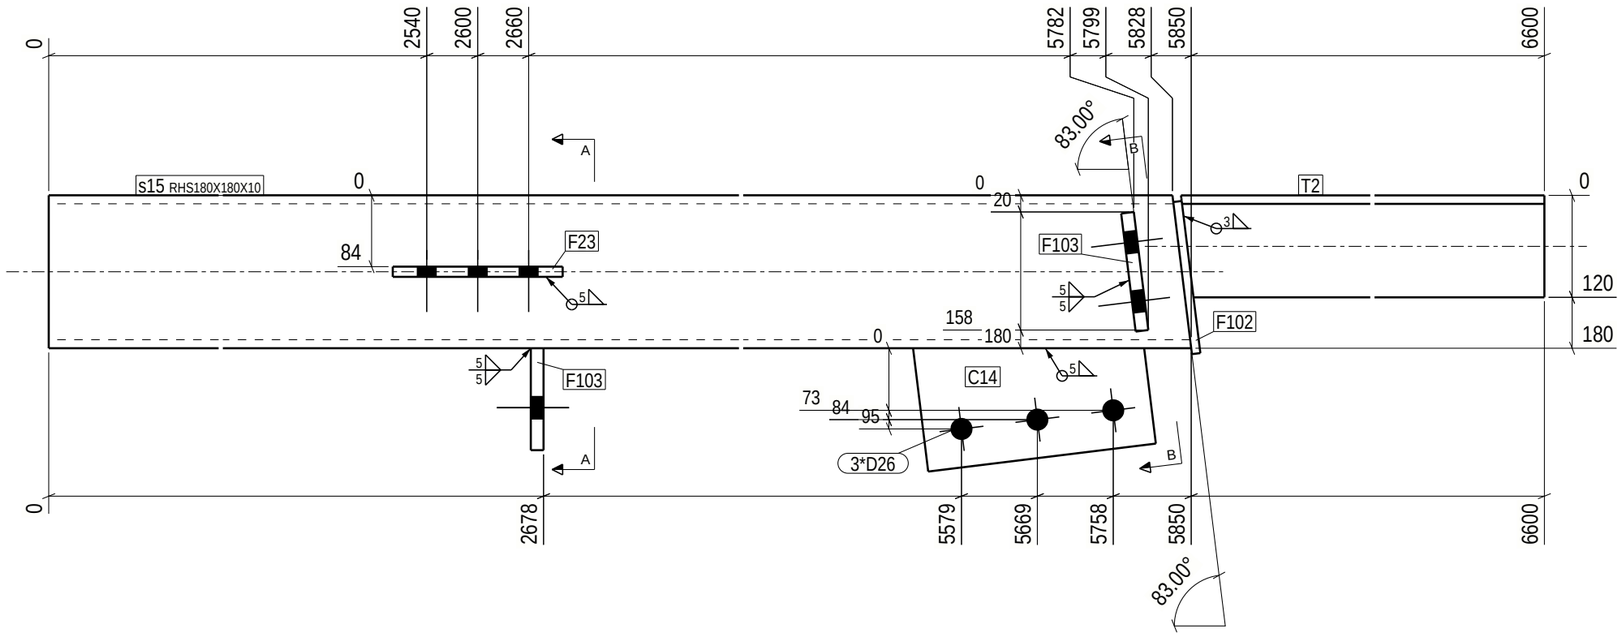


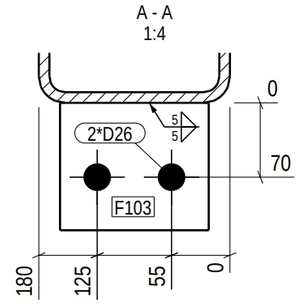

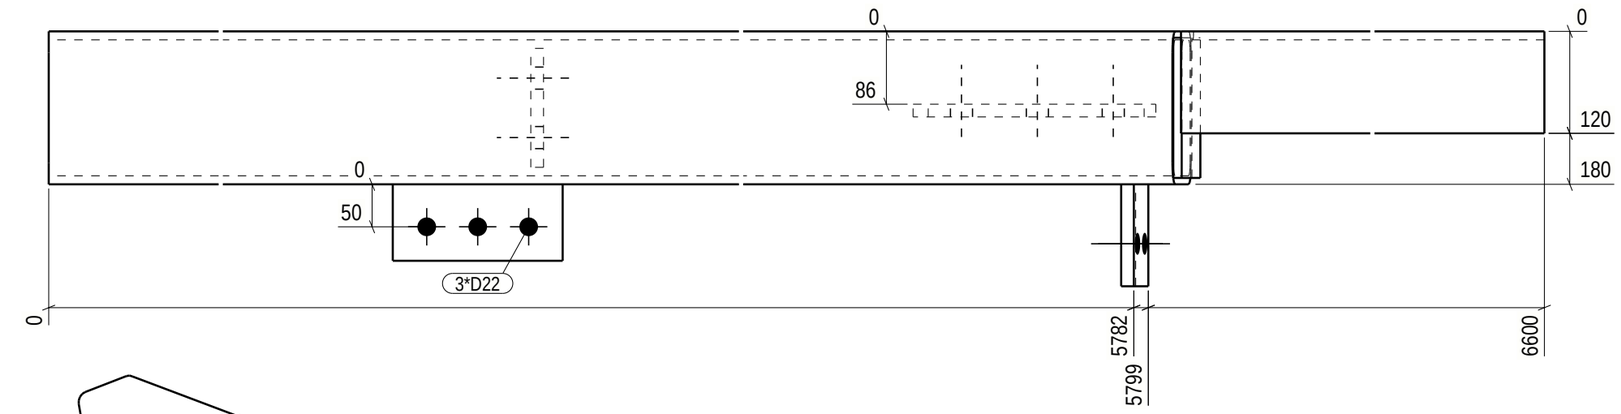

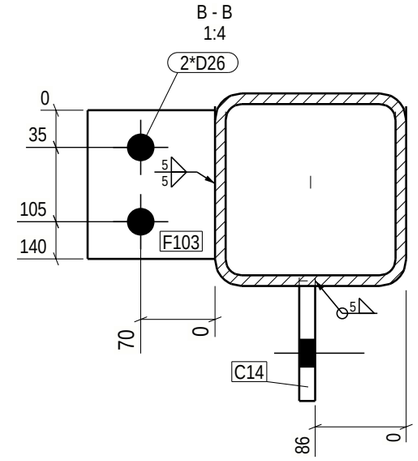

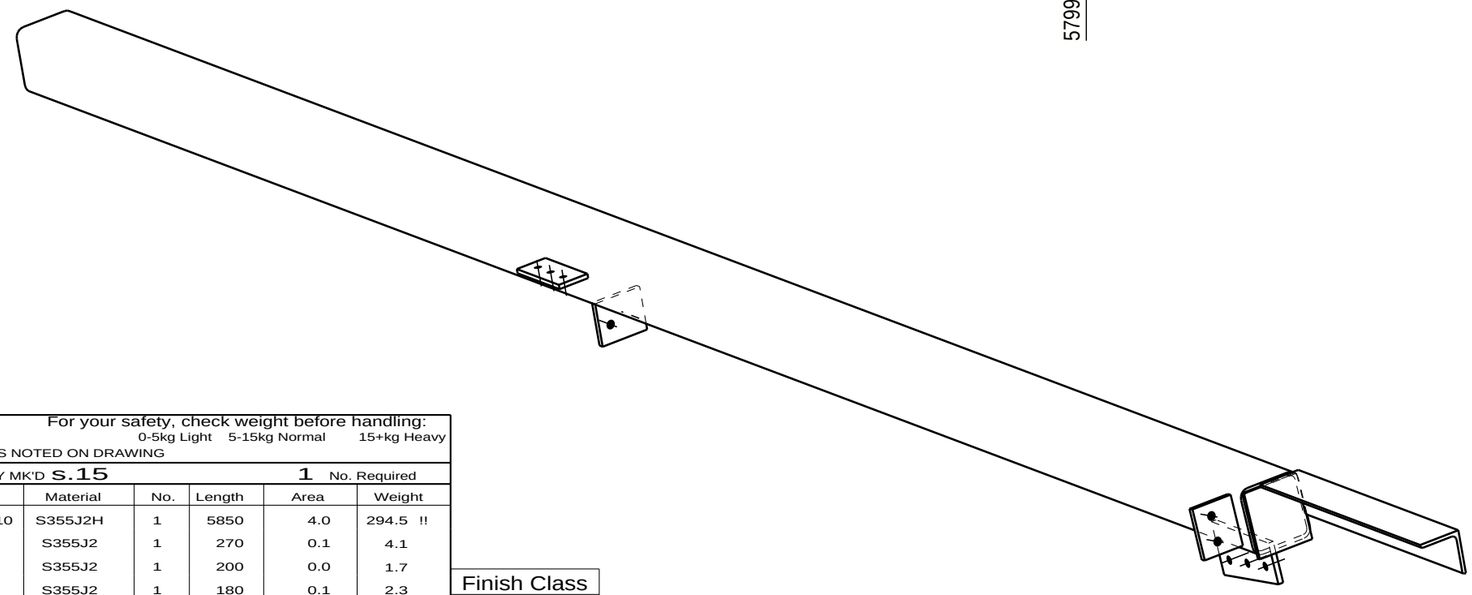

GENERAL NOTES: For your safety, check weight before handling: 0-5kg Light 5-15kg Normal 15+kg Heavy

ALL WELDS ARE 4 ◺ UNLESS NOTED ON DRAWING

MATERIAL LIST FOR ASSEMBLY MK'D S.15 1 No. Required

Mark	Profile	Material	No.	Length	Area	Weight
s15	RHS180X180X10	S355J2H	1	5850	4.0	294.5 !!
C14	PL15*146	S355J2	1	270	0.1	4.1
F23	FL12*90	S355J2	1	200	0.0	1.7
F102	FL10*165	S355J2	1	180	0.1	2.3
F103	FL15*120	S355J2	2	140	0.0	2.0
T2	L120*10	S355J2	1	762	0.4	13.8
				Total	4.6	320.4

Finish Class
Standard

Surface treatment info:	Thickness/start point--> length	No.
Overall Painting	C2M RAL7016µm whole	***1

Special surface treatment

weld a = 4◺

PHASE	QUANTITY
1	1

* o 3 0 4 8 0 - 1 * DS Stålkonstruktion * A s 1 5 *

PROJECT	Akkasæter Lager- og vedlikeholdshall			EXEC. CLASS	EXC 2
MEMBER	Søjle		QUANTITY: 1	PROJECT No	30480-1
REVISION		ISSUED: 07.11.2025	DRAFTER: ZLL BIM control: SST	DRAWING No.	s.15

Tekla Structures