



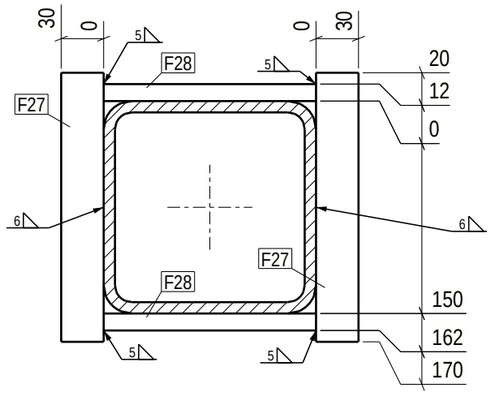


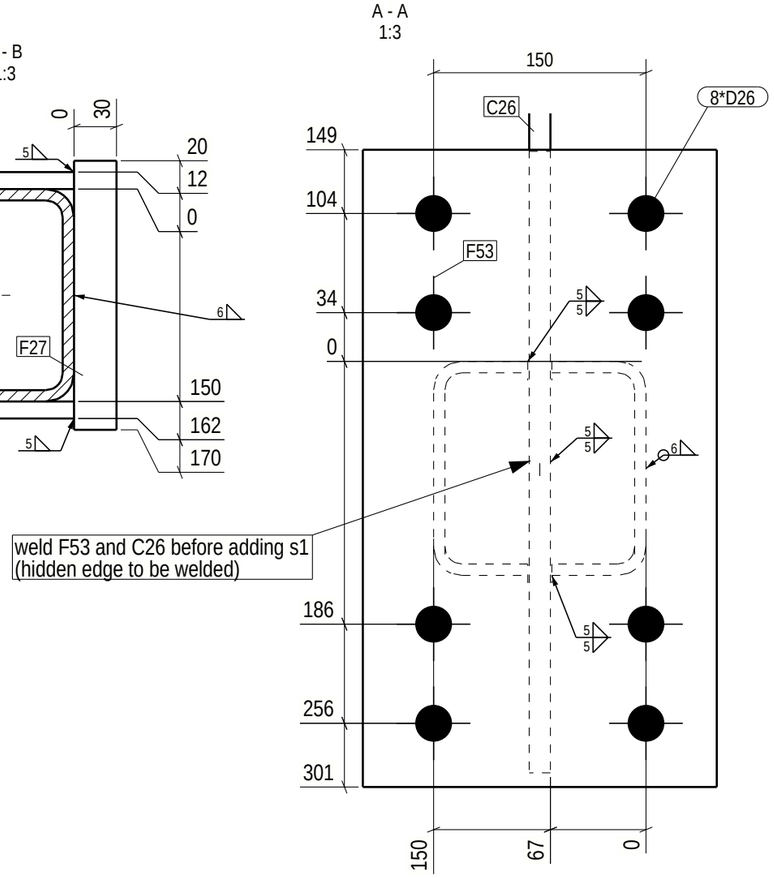

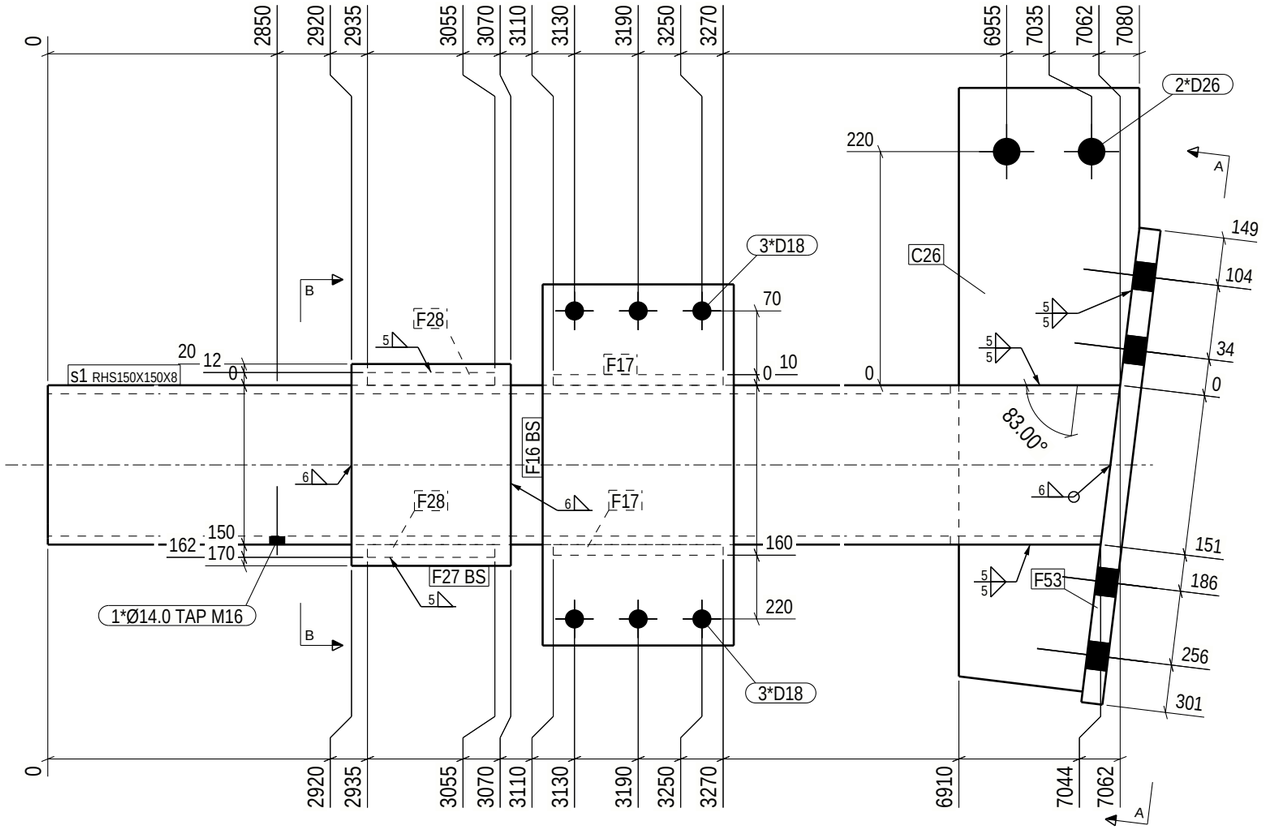

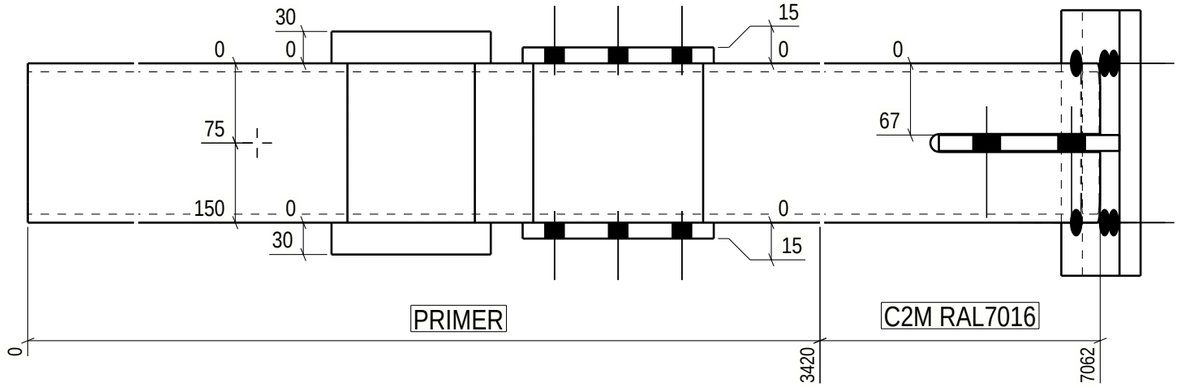

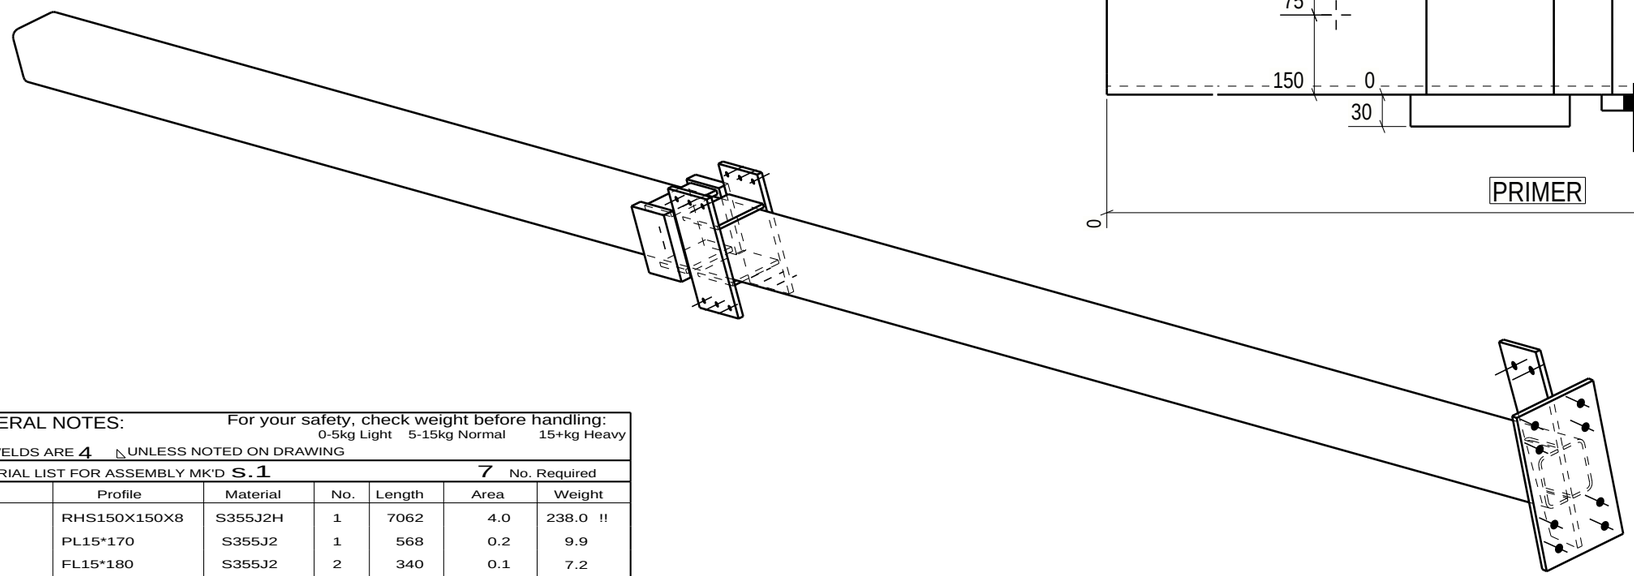

GENERAL NOTES: For your safety, check weight before handling: 0-5kg Light 5-15kg Normal 15+kg Heavy

ALL WELDS ARE 4 UNLESS NOTED ON DRAWING

MATERIAL LIST FOR ASSEMBLY MK'D S.1 7 No. Required

Mark	Profile	Material	No.	Length	Area	Weight
s1	RHS150X150X8	S355J2H	1	7062	4.0	238.0 !!
C26	PL15*170	S355J2	1	568	0.2	9.9
F16	FL15*180	S355J2	2	340	0.1	7.2
F17	FL10*150	S355J2	2	160	0.1	1.9
F27	FL30*150	S355J2	2	190	0.1	6.7
F28	FL12*120	S355J2	2	150	0.0	1.7
F53	FL20*250	S355J2	1	450	0.3	17.7 !!
				Total	5.1	300.5

Finish Class		
Standard	C2M RAL7016 upper part	
Surface treatment info:	Thickness/start point--> length	No.
Partial Painting	Primerµm/0 -->3420mm	7

Special surface treatment

weld a = 4

PHASE	QUANTITY
1	7

* o 3 0 4 8 0 - 1 * DS Stålkonstruktion * A s 1 *

PROJECT	Akkasæter Lager- og vedlikeholdshall			EXEC. CLASS	EXC 2
MEMBER	Søjle		QUANTITY: 7	PROJECT No	30480-1
REVISION		ISSUED: 07.11.2025	DRAFTER: ZLL BIM control: SST	DRAWING No.	S.1

Tekla Structures