
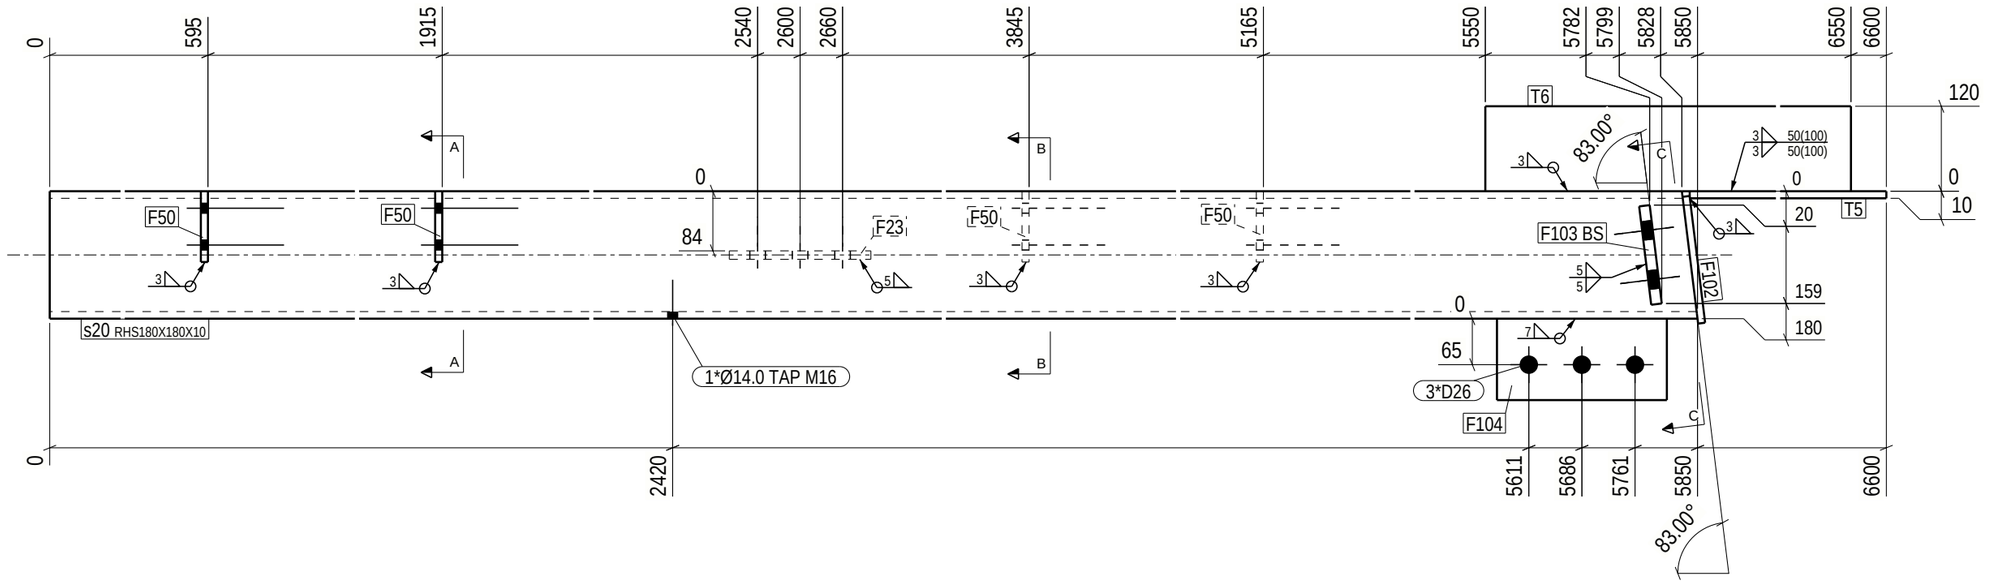
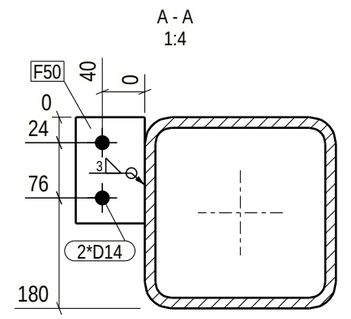
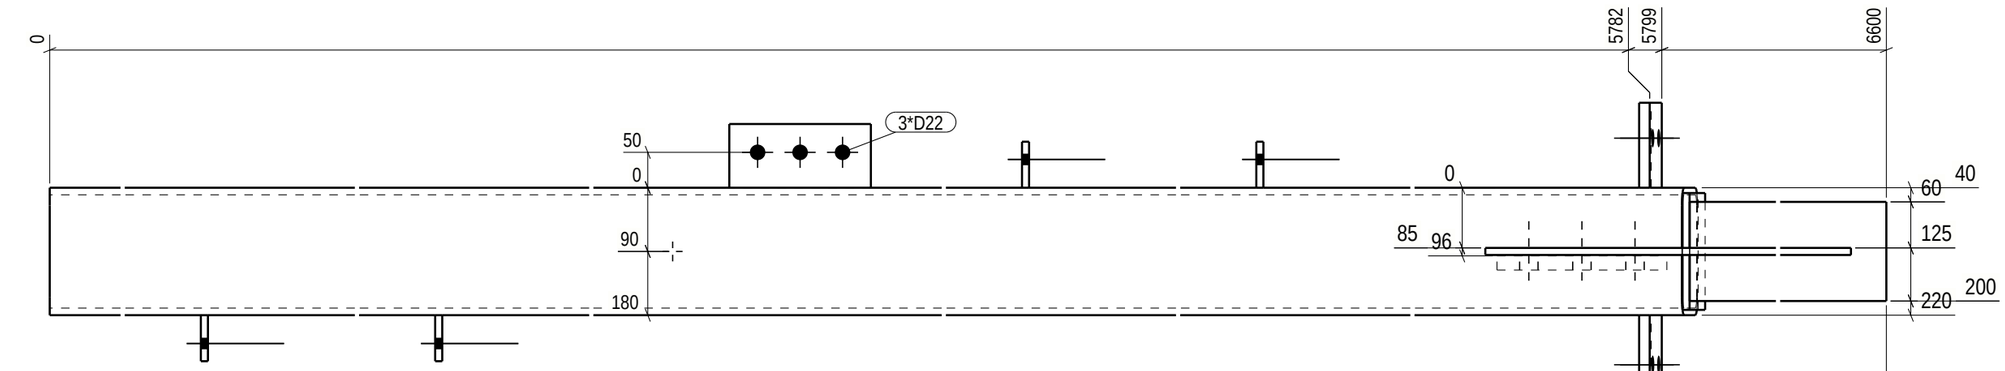
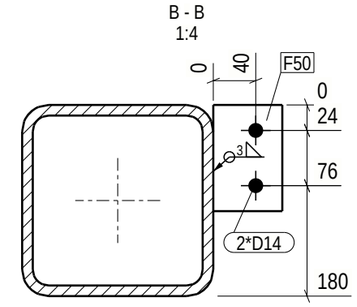
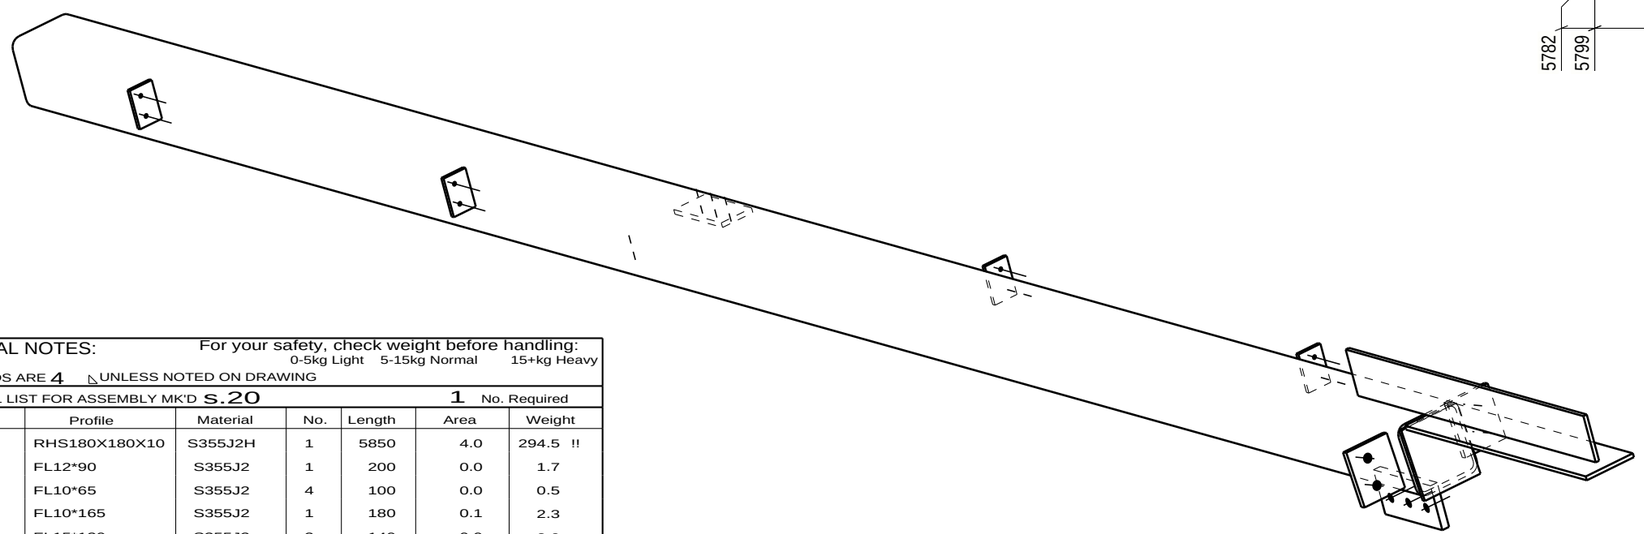


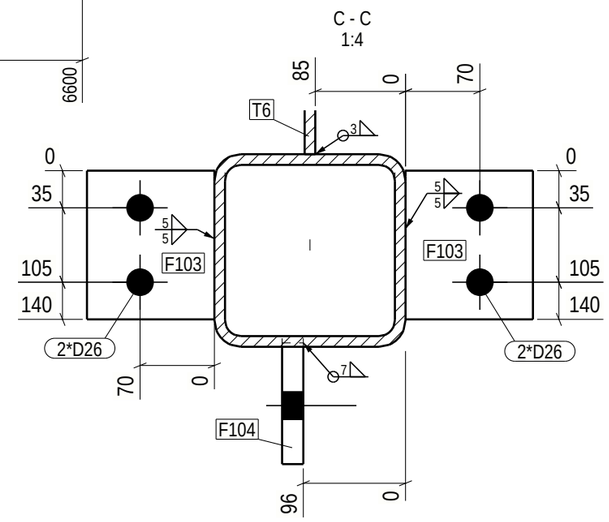


GENERAL NOTES: For your safety, check weight before handling: 0-5kg Light 5-15kg Normal 15+kg Heavy

ALL WELDS ARE 4 UNLESS NOTED ON DRAWING

MATERIAL LIST FOR ASSEMBLY MK'D s.20 — 1 No. Required

| Mark | Profile | Material | No. | Length | Area | Weight |
|---|---|---|---|---|---|---|
| s20 | RHS180X180X10 | S355J2H | 1 | 5850 | 4.0 | 294.5 !! |
| F23 | FL12*90 | S355J2 | 1 | 200 | 0.0 | 1.7 |
| F50 | FL10*65 | S355J2 | 4 | 100 | 0.0 | 0.5 |
| F102 | FL10*165 | S355J2 | 1 | 180 | 0.1 | 2.3 |
| F103 | FL15*120 | S355J2 | 2 | 140 | 0.0 | 2.0 |
| F104 | FL20*115 | S355J2 | 1 | 240 | 0.1 | 4.3 |
| T5 | FL10*140 | S355J2 | 1 | 761 | 0.2 | 8.4 |
| T6 | FL10*120 | S355J2 | 1 | 1000 | 0.3 | 9.4 |
| | | | | Total | 4.8 | 326.6 |

Finish Class: Standard

| Surface treatment info: | Thickness/start point--> length | No. |
|---|---|---|
| Overall Painting | C2M RAL7016µm whole | ***1 |

Special surface treatment

weld a = 4

| PHASE | QUANTITY |
|---|---|
| 1 | 1 |

* o 3 0 4 8 0 - 1 * D5 Stålkonstruktion * A s 2 0 *

| | | | | | |
|---|---|---|---|---|---|
| PROJECT | Akkasæter Lager- og vedlikeholdshall | | | EXEC. CLASS | EXC 2 |
| MEMBER | Søjle | | QUANTITY: 1 | PROJECT No | 30480-1 |
| REVISION | | ISSUED: 07.11.2025 | DRAFTER: ZLL<br>BIM control: SST | DRAWING No. | s.20 |

Tekla Structures