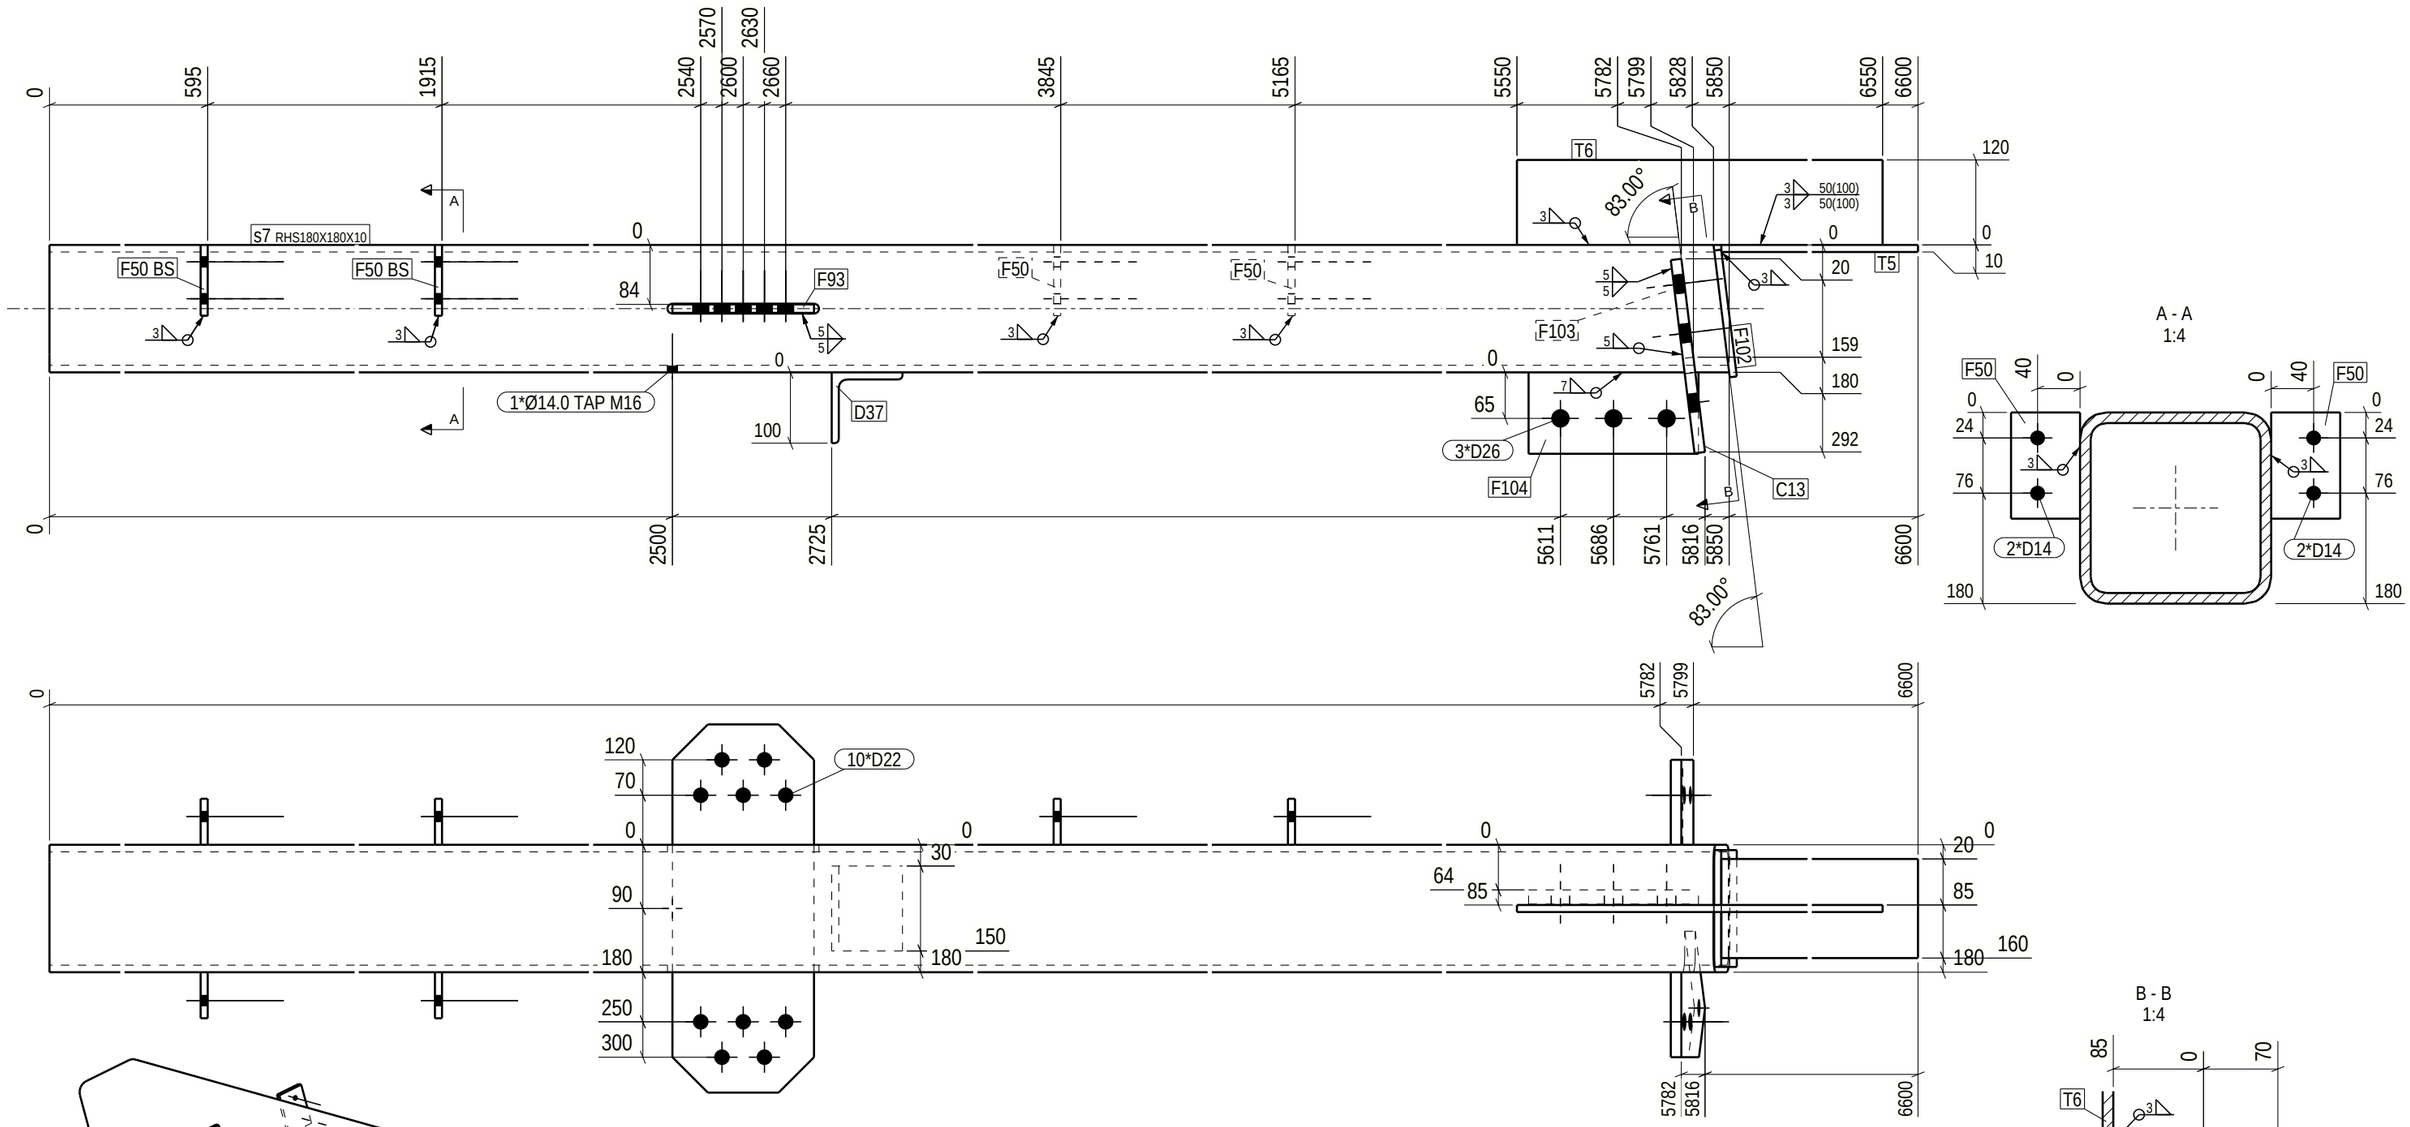


GENERAL NOTES: For your safety, check weight before handling: 0-5kg Light 5-15kg Normal 15+kg Heavy

ALL WELDS ARE 4 ◺ UNLESS NOTED ON DRAWING

MATERIAL LIST FOR ASSEMBLY MK'D S.7 — 1 No. Required

Mark	Profile	Material	No.	Length	Area	Weight
s7	RHS180X180X10	S355J2H	1	5850	4.0	294.0 !!
C13	PL15*178	S355J2	1	275	0.1	3.7
D37	L100*10	S355J2	1	120	0.0	1.8
F50	FL10*65	S355J2	6	100	0.0	0.5
F93	FL12*200	S355J2	1	520	0.2	9.3
F102	FL10*165	S355J2	1	180	0.1	2.3
F103	FL15*120	S355J2	1	140	0.0	2.0
F104	FL20*115	S355J2	1	240	0.1	4.3
T5	FL10*140	S355J2	1	761	0.2	8.4
T6	FL10*120	S355J2	1	1000	0.3	9.4
				Total	5.1	338.3

Finish Class: Standard

Surface treatment info:	Thickness/start point--> length	No.
Overall Painting	C2M RAL7016µm whole	***1

Special surface treatment

weld a = 4◺

PHASE	QUANTITY
1	1

* o 3 0 4 8 0 - 1 * DS Stålkonstruktion * A s 7 *

PROJECT	Akkasæter Lager- og vedlikeholdshall			EXEC. CLASS	EXC 2
MEMBER	Søjle		QUANTITY: 1	PROJECT No	30480-1
REVISION		ISSUED: 07.11.2025	DRAFTER: ZLL BIM control: SST	DRAWING No.	S.7

Tekla Structures