




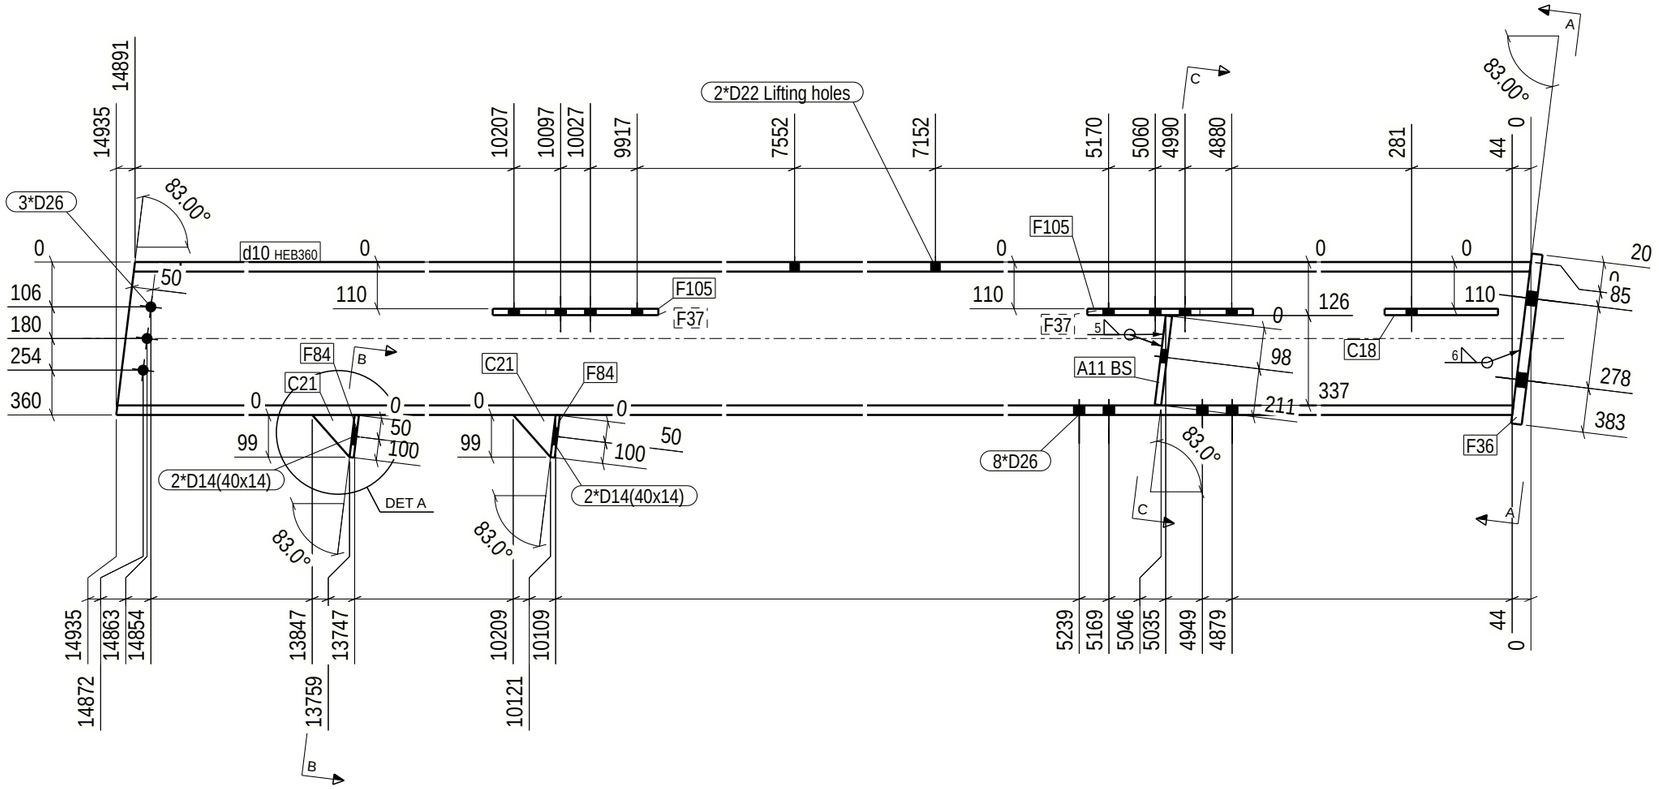


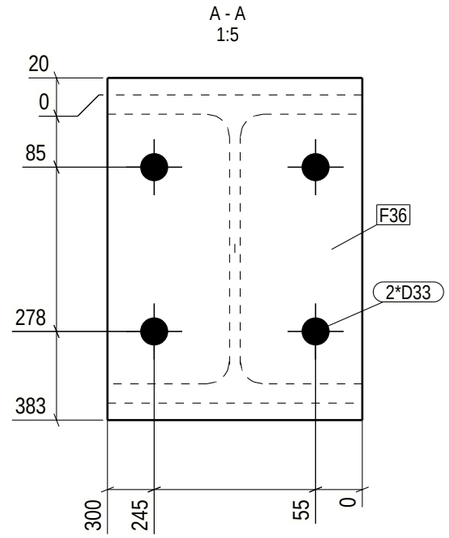


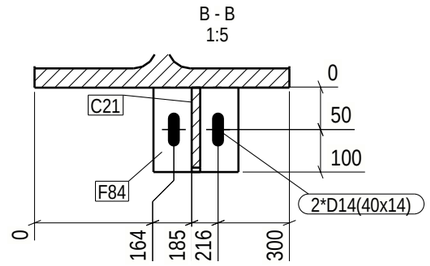

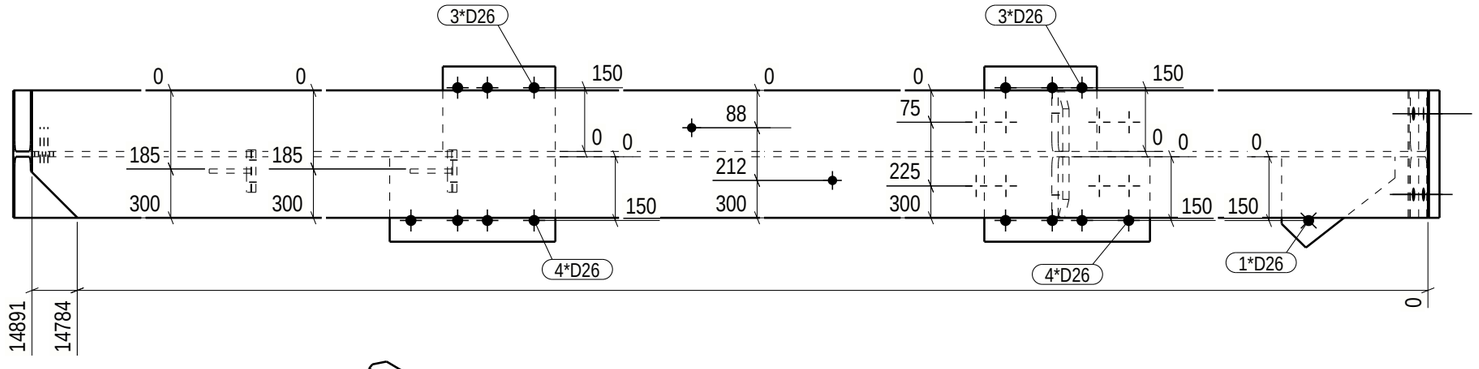

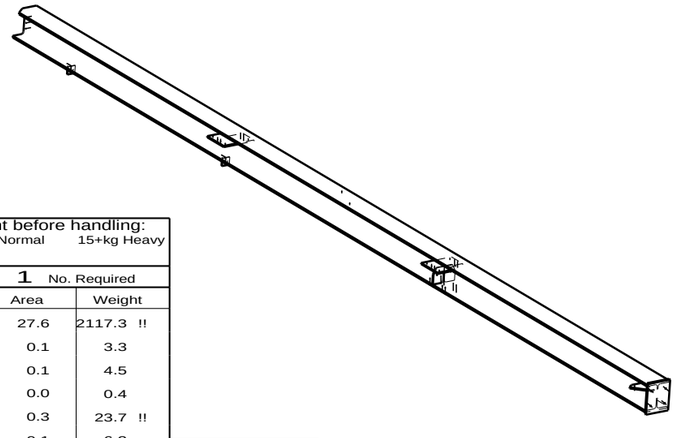

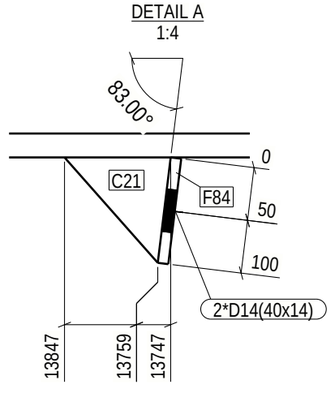

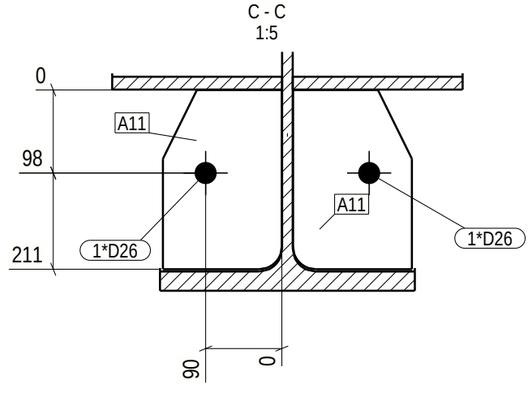

GENERAL NOTES: For your safety, check weight before handling: 0-5kg Light 5-15kg Normal 15+kg Heavy

ALL WELDS ARE 4 ◺ UNLESS NOTED ON DRAWING

MATERIAL LIST FOR ASSEMBLY MK'D d.10 1 No. Required

Mark	Profile	Material	No.	Length	Area	Weight
d10	HEB360	S355J2	1	14935	27.6	2117.3 !!
A11	FL15*140	S355J2	2	211	0.1	3.3
C18	PL15*214	S355J2	1	267	0.1	4.5
C21	PL10*75	S355J2	2	133	0.0	0.4
F36	FL25*300	S355J2	1	403	0.3	23.7 !!
F37	FL15*200	S355J2	2	265	0.1	6.2
F84	FL10*100	S355J2	2	100	0.0	0.8
F105	FL15*200	S355J2	2	390	0.2	9.2
				Total	28.8	2185.2

Finish Class: Standard

Surface treatment info: | Thickness/start point--> length | No.

weld a = 4◺

PHASE	QUANTITY
1	1

* o 3 0 4 8 0 - 1 * DS Stålkonstruktion * A d 1 0 *

PROJECT	Akkasæter Lager- og vedlikeholdshall			EXEC. CLASS	EXC 2
MEMBER	Drager		QUANTITY: 1	PROJECT No	30480-1
REVISION		ISSUED: 03.11.2025	DRAFTER: ZLL BIM control: SST	DRAWING No.	d.10

Tekla Structures