

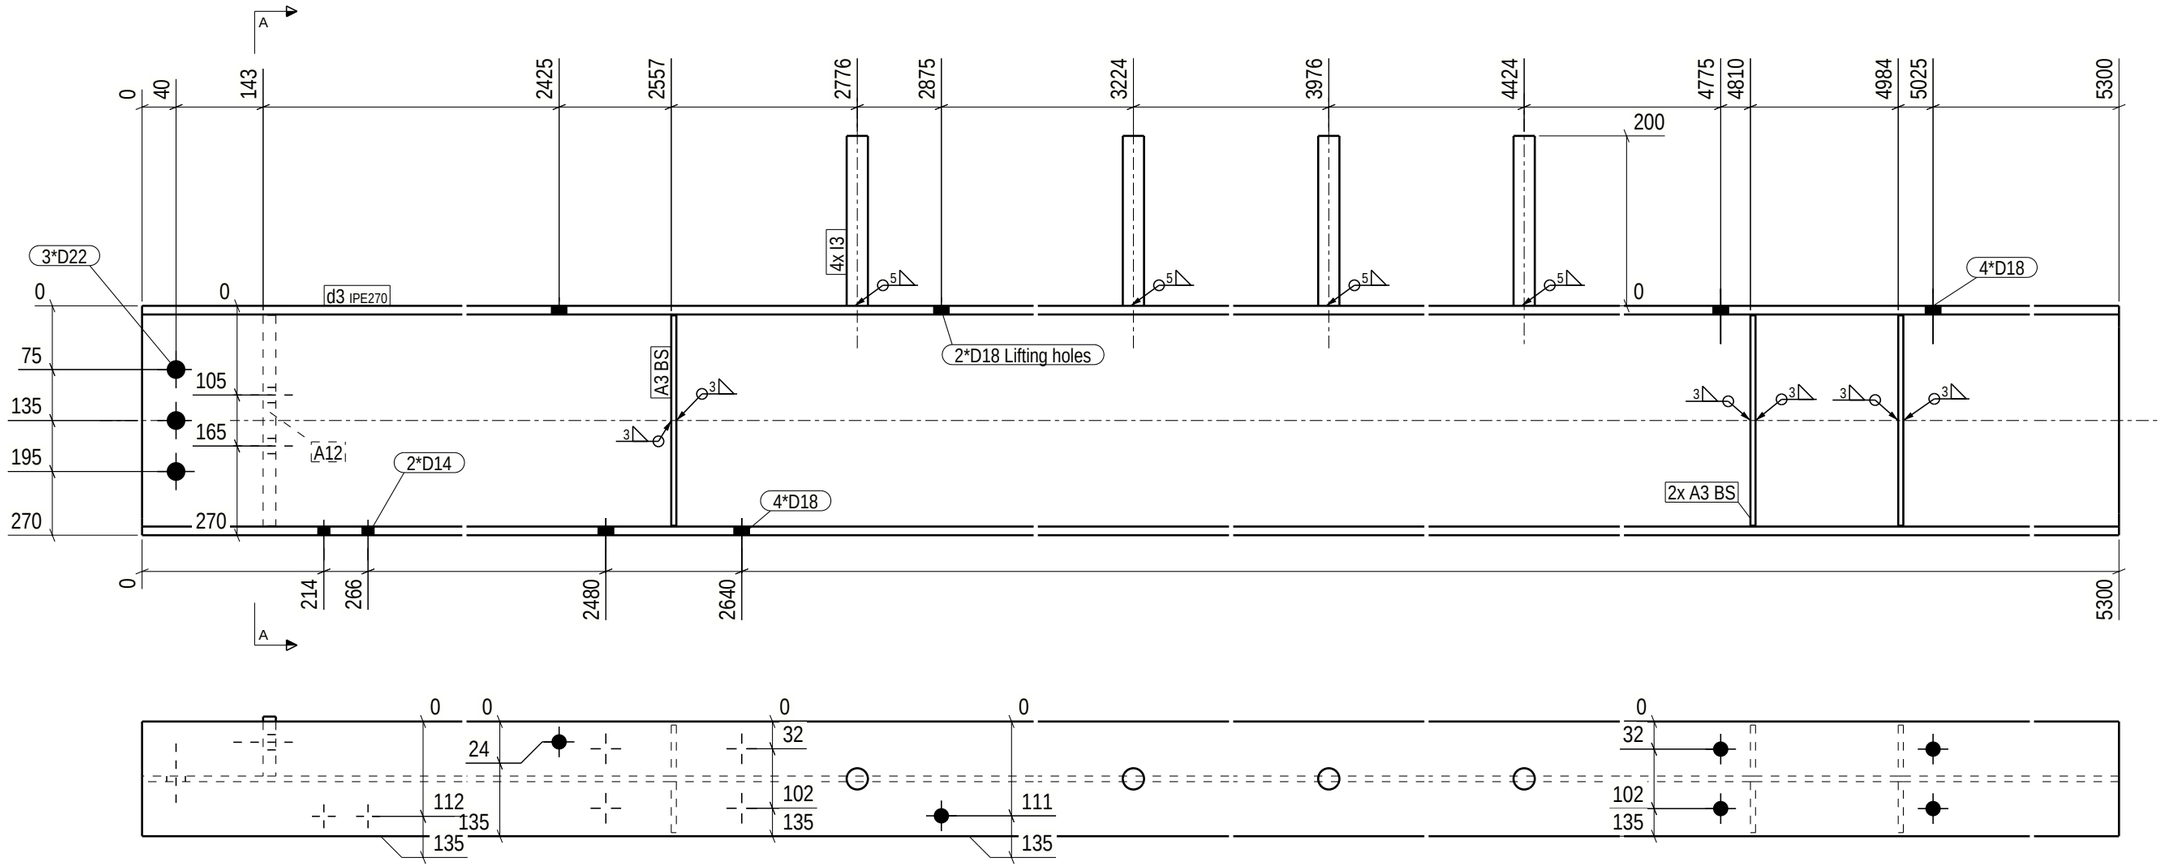


A - A
1:4

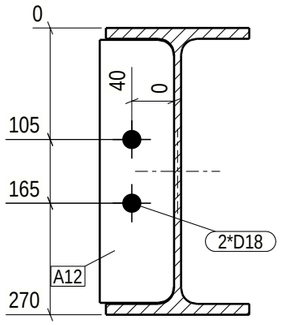

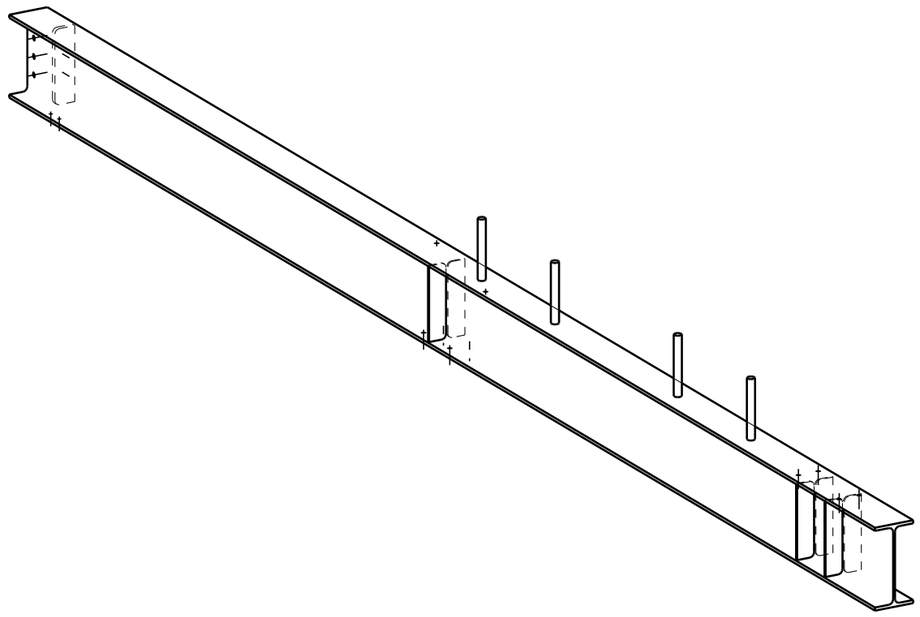

GENERAL NOTES: For your safety, check weight before handling: 0-5kg Light 5-15kg Normal 15+kg Heavy

ALL WELDS ARE 4 UNLESS NOTED ON DRAWING

MATERIAL LIST FOR ASSEMBLY MK'D d.3 1 No. Required

Mark	Profile	Material	No.	Length	Area	Weight
d3	IPE270	S355J2	1	5300	5.5	191.0 !!
A3	FL6*60	S355J2	6	248	0.0	0.7
A12	FL15*70	S355J2	1	248	0.0	2.0
I3	REBAR25	B550B	4	200	0.0	0.7
				Total	5.8	200.1

Finish Class		
Standard		
Surface treatment info:	Thickness/start point--> length	No.

weld a = 4

PHASE	QUANTITY
1	1

* o 3 0 4 8 0 - 1 * DS Stålkonstruktion * A d 3 *

PROJECT	Akkasæter Lager- og vedlikeholdshall			EXEC. CLASS	EXC 2
MEMBER	Drager		QUANTITY: 1	PROJECT No	30480-1
REVISION		ISSUED: 05.11.2025	DRAFTER: ZLL BIM control: SST	DRAWING No.	d.3

Tekla Structures