


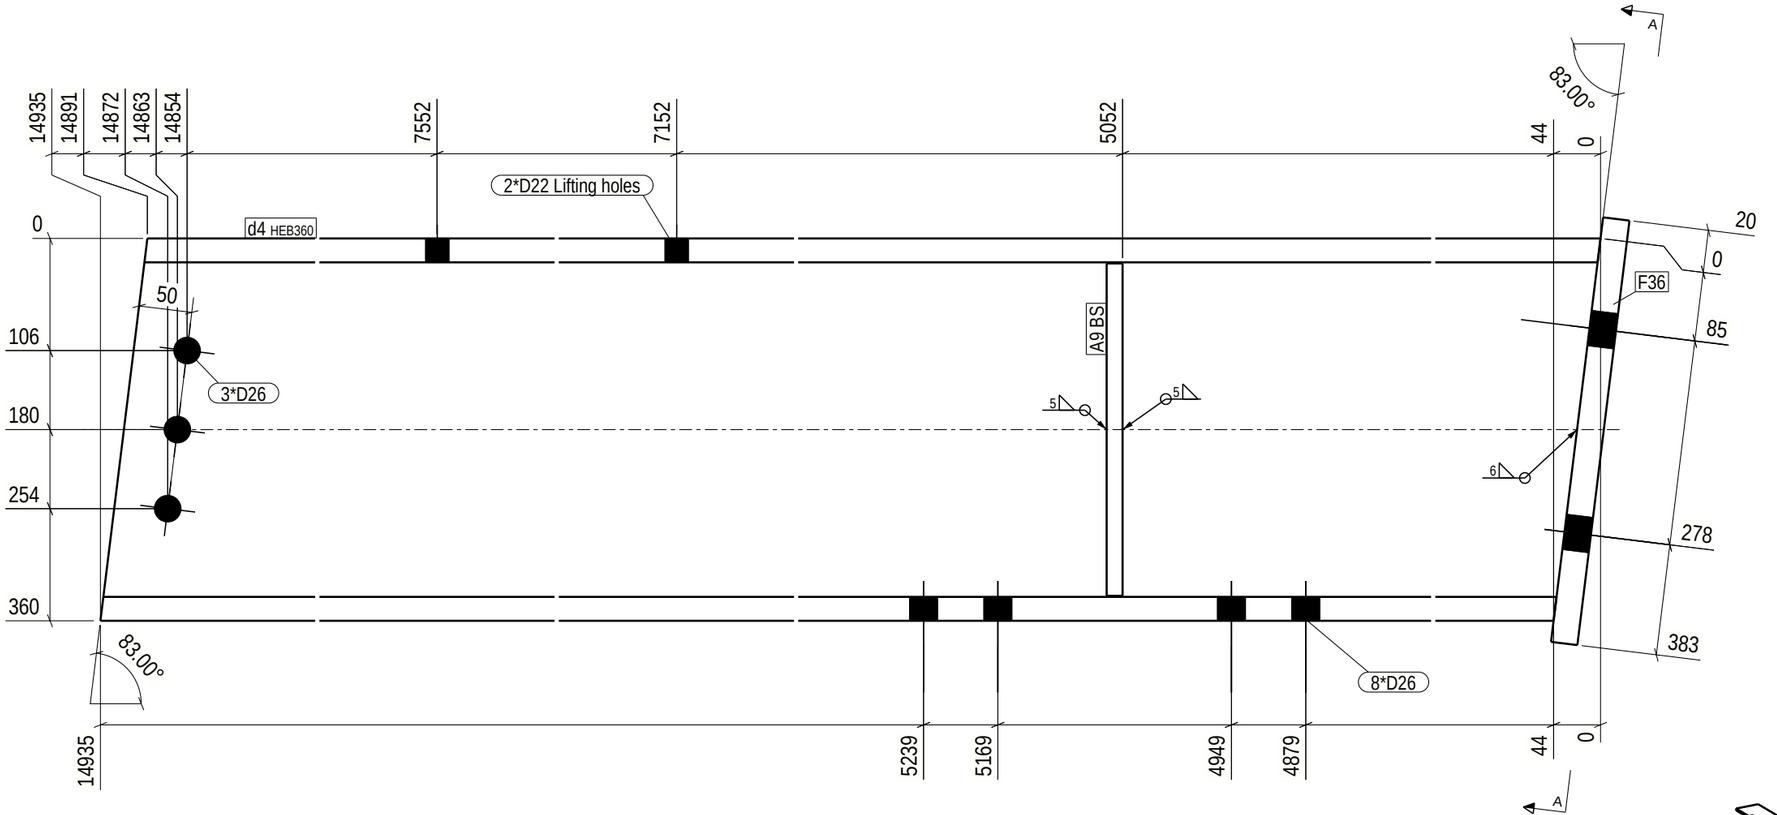


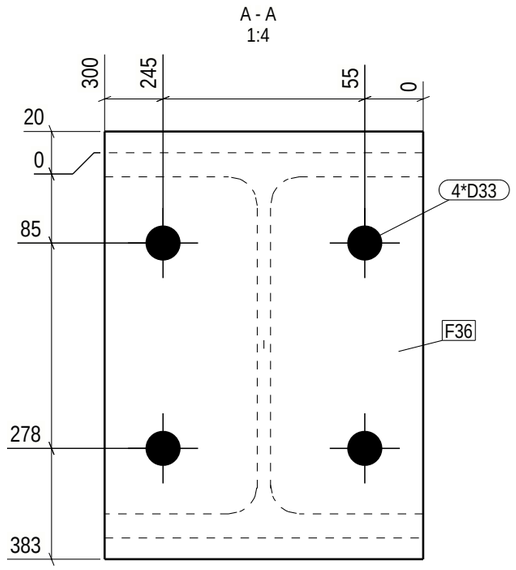

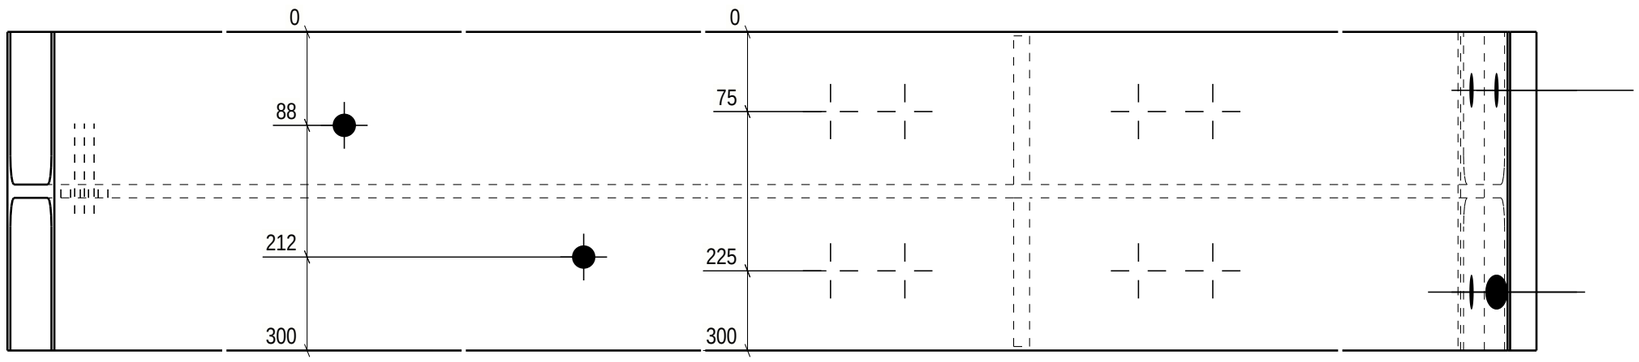

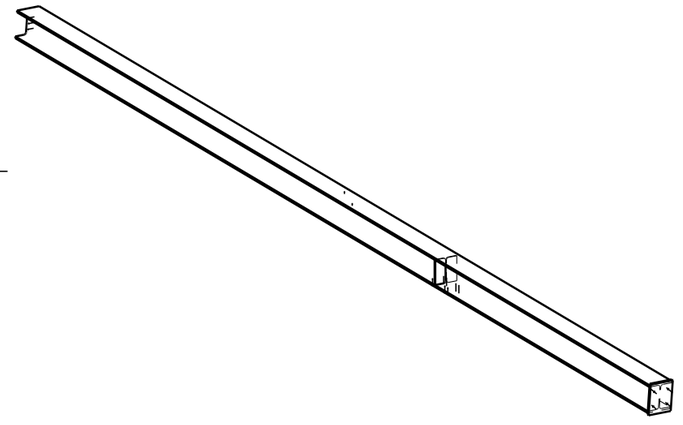

GENERAL NOTES: For your safety, check weight before handling: 0-5kg Light 5-15kg Normal 15+kg Heavy

ALL WELDS ARE 4 UNLESS NOTED ON DRAWING

MATERIAL LIST FOR ASSEMBLY MK'D d.4 6 No. Required

Mark	Profile	Material	No.	Length	Area	Weight
d4	HEB360	S355J2	1	14935	27.6	2117.4 !!
A9	FL15*140	S355J2	2	313	0.1	5.1
F36	FL25*300	S355J2	1	403	0.3	23.7 !!
				Total	28.1	2151.3

Finish Class
Standard

Surface treatment info: | Thickness/start point--> length | No.

weld a = 4

PHASE	QUANTITY
1	6

* o 3 0 4 8 0 - 1 * DS Stålkonstruktion * A d 4 *

PROJECT	Akkasæter Lager- og vedlikeholdshall			EXEC. CLASS	EXC 2
MEMBER	Drager		QUANTITY: 6	PROJECT No	30480-1
REVISION		ISSUED: 03.11.2025	DRAFTER: ZLL BIM control: SST	DRAWING No.	d.4

Tekla Structures