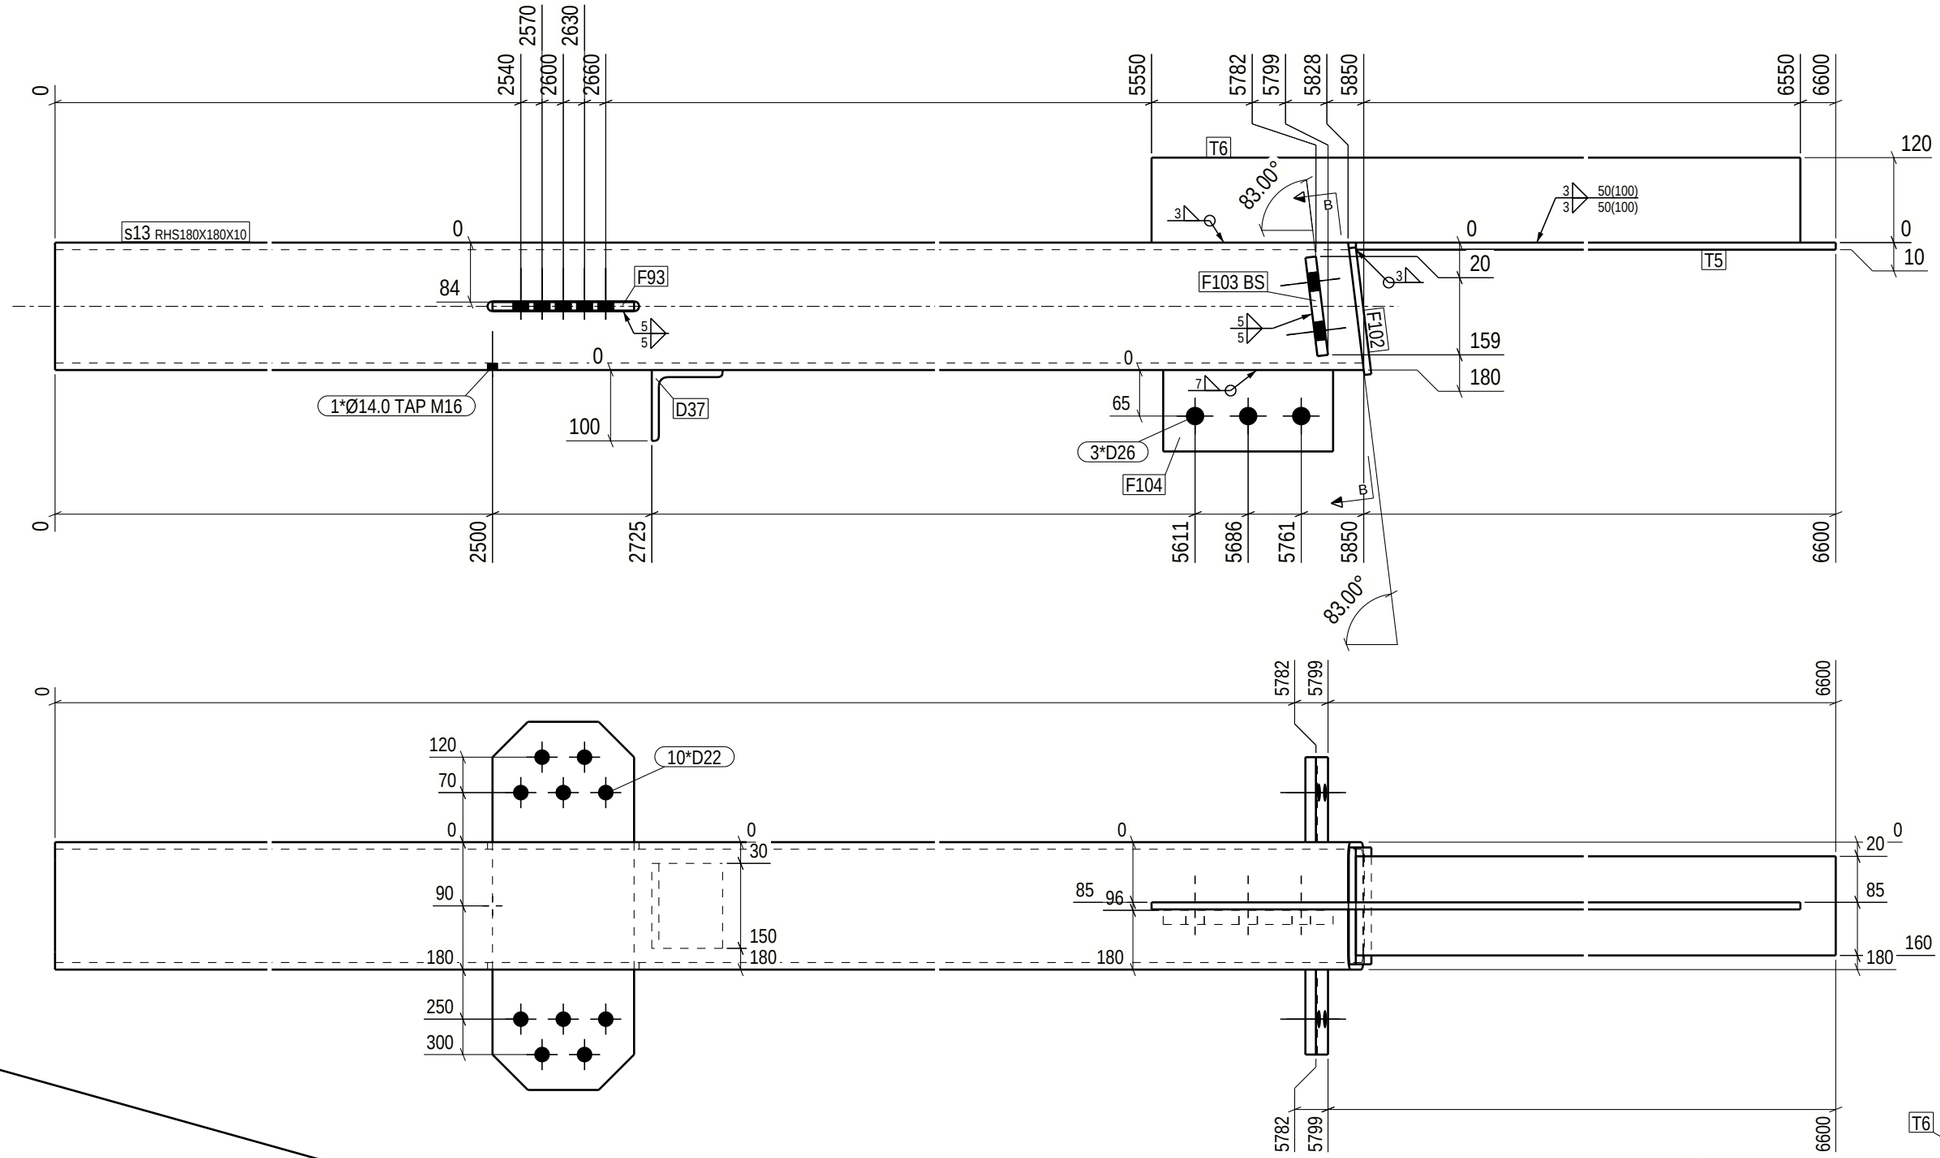


GENERAL NOTES: For your safety, check weight before handling: 0-5kg Light 5-15kg Normal 15+kg Heavy

ALL WELDS ARE 4 UNLESS NOTED ON DRAWING

MATERIAL LIST FOR ASSEMBLY MK'D s.13 3 No. Required

Mark	Profile	Material	No.	Length	Area	Weight
s13	RHS180X180X10	S355J2H	1	5850	4.0	294.0 !!
D37	L100*10	S355J2	1	120	0.0	1.8
F93	FL12*200	S355J2	1	520	0.2	9.3
F102	FL10*165	S355J2	1	180	0.1	2.3
F103	FL15*120	S355J2	2	140	0.0	2.0
F104	FL20*115	S355J2	1	240	0.1	4.3
T5	FL10*140	S355J2	1	761	0.2	8.4
T6	FL10*120	S355J2	1	1000	0.3	9.4
				Total	5.0	333.5

Finish Class: Standard

Surface treatment info: | Thickness/start point--> length | No.

weld a = 4

PHASE	QUANTITY
1	3

* o 3 0 4 8 0 - 1 * DS Stålkonstruktion * A s 1 3 *

PROJECT	Akkasæter Lager- og vedlikeholdshall			EXEC. CLASS	EXC 2
MEMBER	Søjle		QUANTITY: 3	PROJECT No	30480-1
REVISION		ISSUED: 03.11.2025	DRAFTER: ZLL BIM control: SST	DRAWING No.	s.13

Tekla Structures