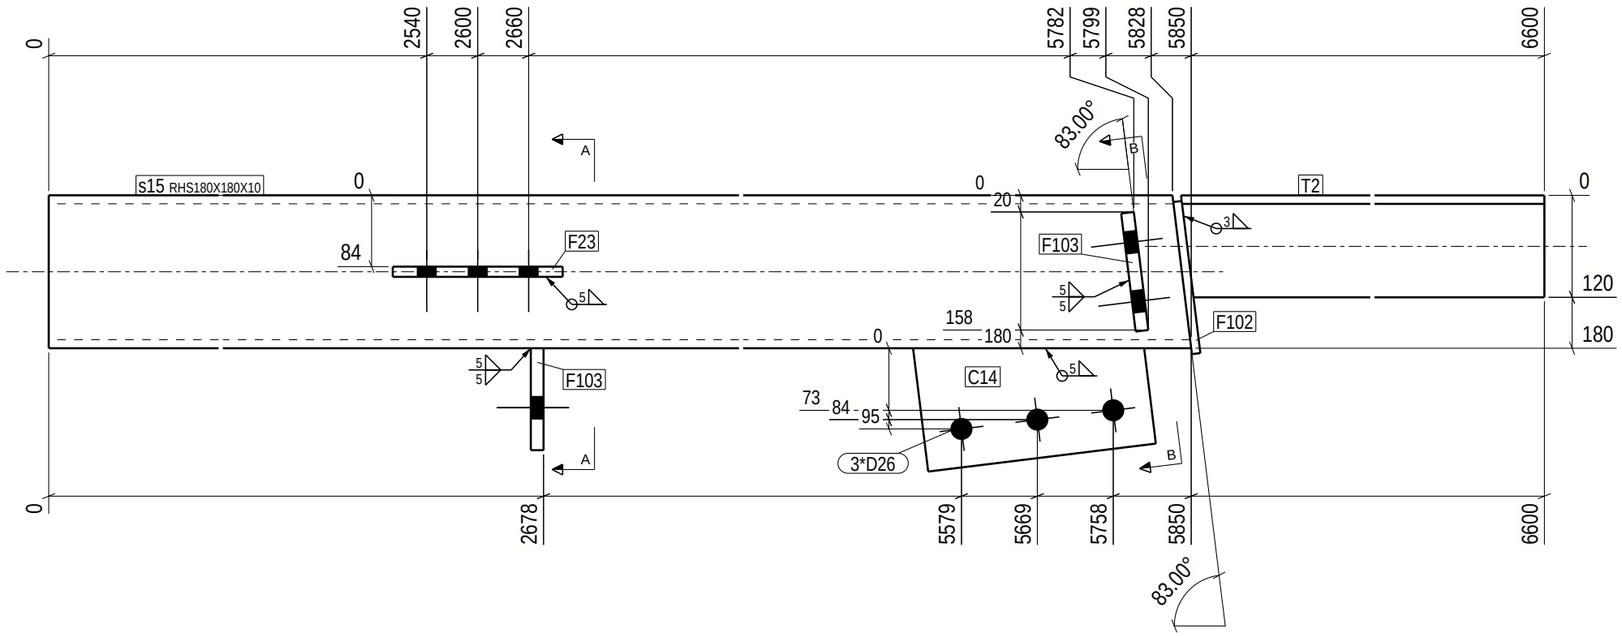
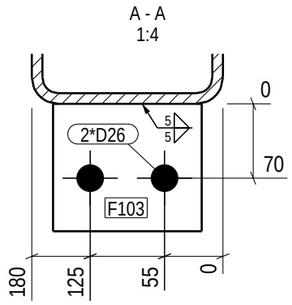
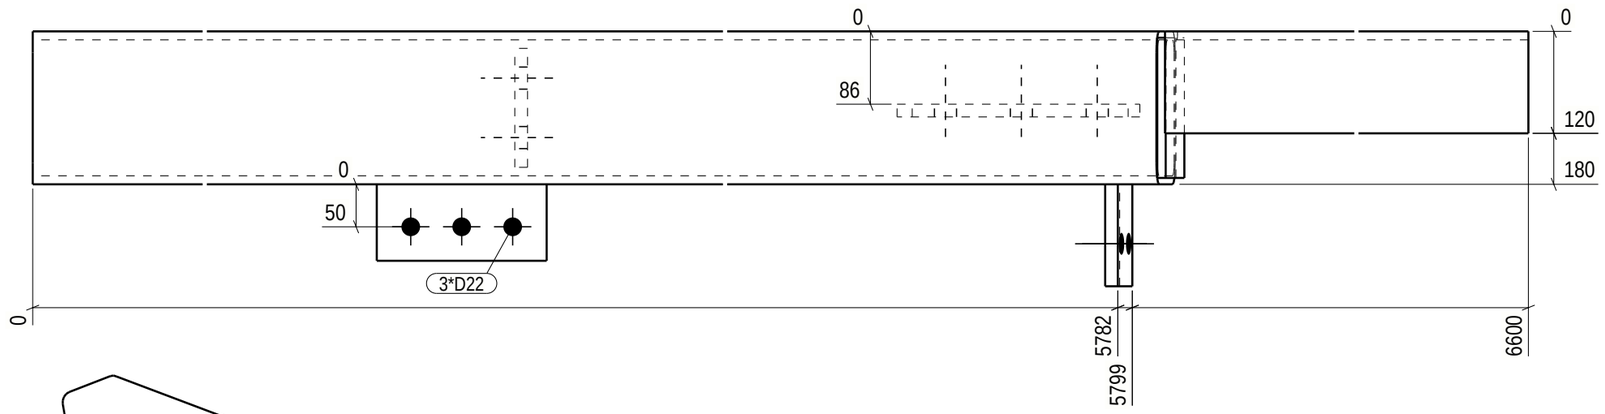
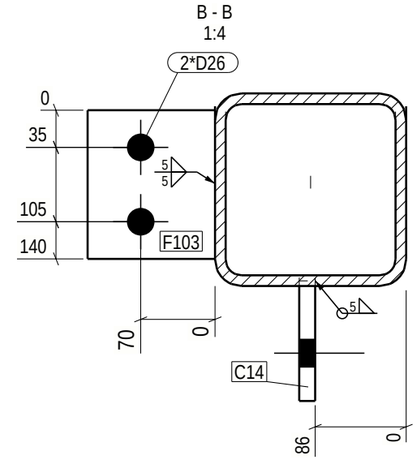
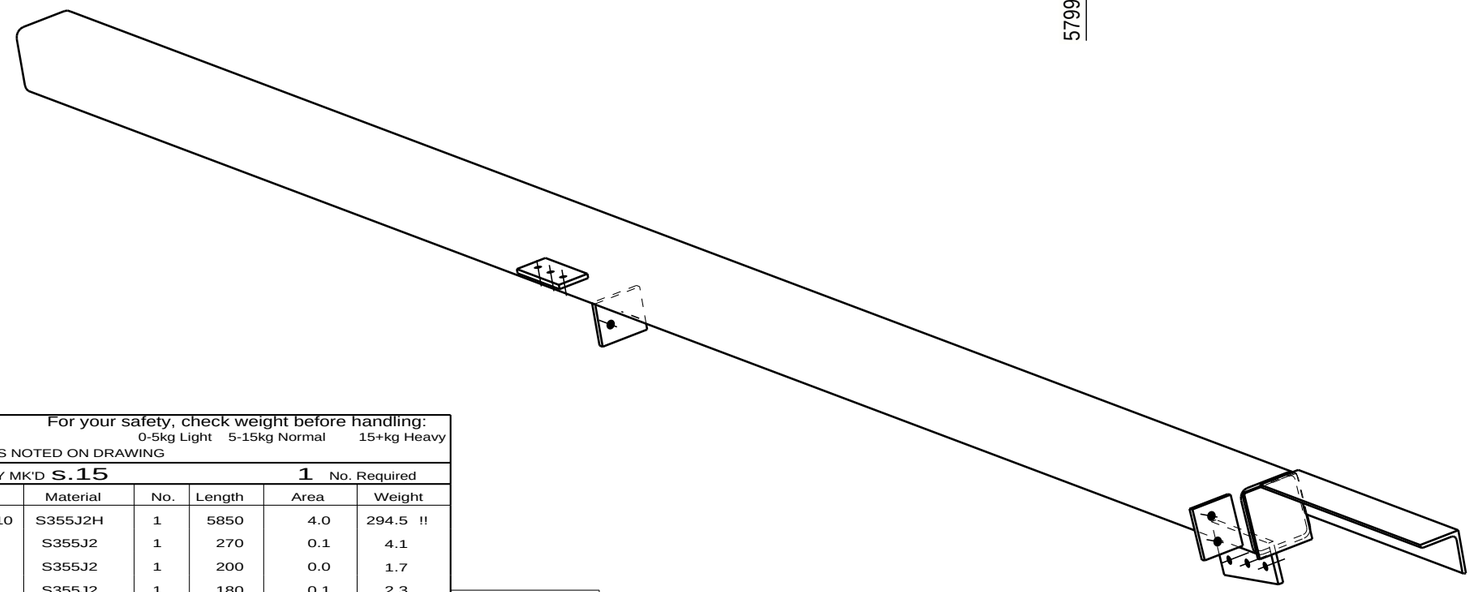


GENERAL NOTES: For your safety, check weight before handling: 0-5kg Light 5-15kg Normal 15+kg Heavy

ALL WELDS ARE 4 ◺ UNLESS NOTED ON DRAWING

MATERIAL LIST FOR ASSEMBLY MK'D S.15 1 No. Required

| Mark | Profile | Material | No. | Length | Area | Weight |
|---|---|---|---|---|---|---|
| s15 | RHS180X180X10 | S355J2H | 1 | 5850 | 4.0 | 294.5 !! |
| C14 | PL15*146 | S355J2 | 1 | 270 | 0.1 | 4.1 |
| F23 | FL12*90 | S355J2 | 1 | 200 | 0.0 | 1.7 |
| F102 | FL10*165 | S355J2 | 1 | 180 | 0.1 | 2.3 |
| F103 | FL15*120 | S355J2 | 2 | 140 | 0.0 | 2.0 |
| T2 | L120*10 | S355J2 | 1 | 762 | 0.4 | 13.8 |
| | | | | Total | 4.6 | 320.4 |

Finish Class: Standard

Surface treatment info: | Thickness/start point--> length | No.

weld a = 4◺

| PHASE | QUANTITY |
|---|---|
| 1 | 1 |

* o 3 0 4 8 0 - 1 * DS Stålkonstruktion * A s 1 5 *

| | | | | | |
|---|---|---|---|---|---|
| PROJECT | Akkasæter Lager- og vedlikeholdshall | | | EXEC. CLASS | EXC 2 |
| MEMBER | Søjle | | QUANTITY: 1 | PROJECT No | 30480-1 |
| REVISION | | ISSUED: 05.11.2025 | DRAFTER: ZLL<br>BIM control: SST | DRAWING No. | s.15 |

Tekla Structures