


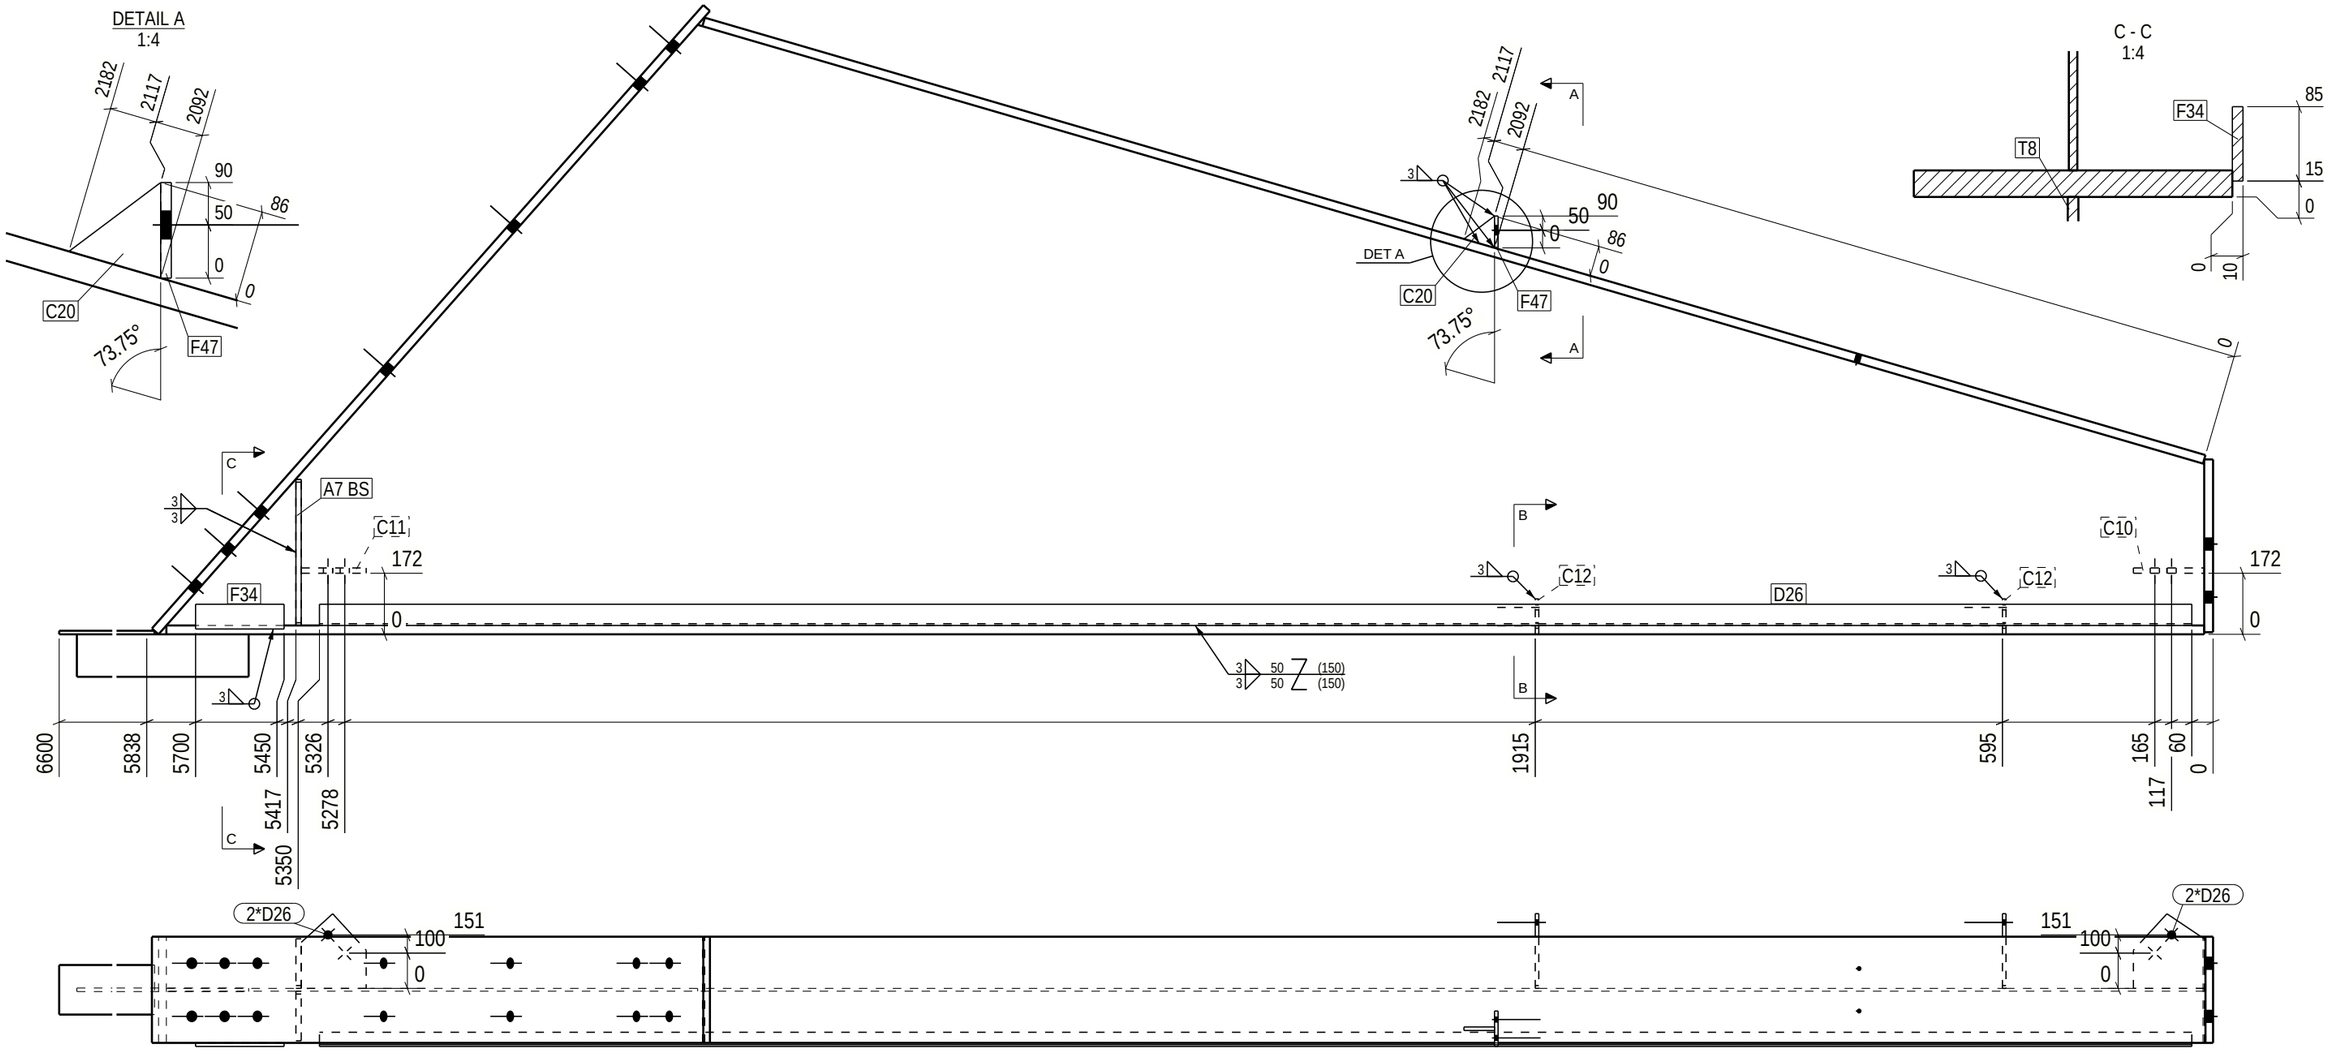


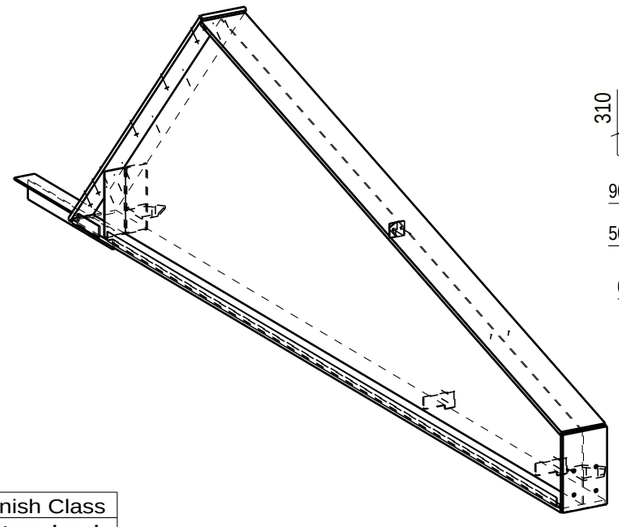

A - A
1:4

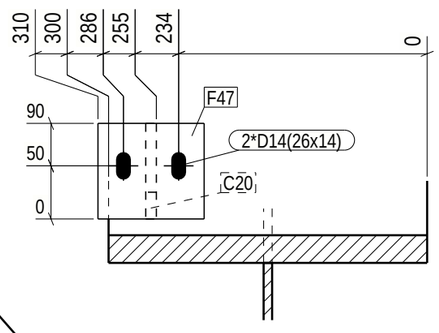

B - B
1:4

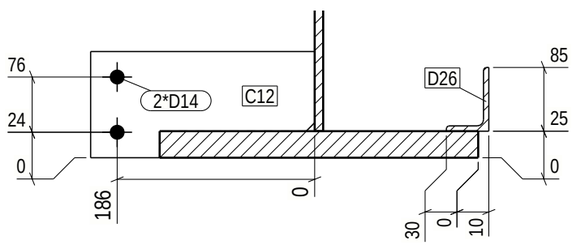

GENERAL NOTES: For your safety, check weight before handling: 0-5kg Light 5-15kg Normal 15+kg Heavy

ALL WELDS ARE 4 UNLESS NOTED ON DRAWING

MATERIAL LIST FOR ASSEMBLY MK'D j.3 — 1 No. Required

Mark	Profile	Material	No.	Length	Area	Weight
j3	PL8*1697	S355J2	1	5758	11.8	367.7 !!
A7	FL15*140	S355J2	2	413	0.1	6.8
C10	PL15*200	S355J2	1	211	0.1	4.0
C11	PL15*183	S355J2	1	211	0.1	3.6
C12	PL10*100	S355J2	2	211	0.0	1.4
C20	PL10*72	S355J2	1	108	0.0	0.3
D26	L60*40*5	S355J2	1	5290	1.0	19.9 !!
F3	FL25*300	S355J2	1	2351	1.5	138.4 !!
F5	FL25*300	S355J2 Z15	1	488	0.3	28.7 !!
F34	FL10*70	S355J2	1	250	0.0	1.4
F47	FL10*90	S355J2	1	100	0.0	0.7
H1	FL25*300	S355J2	1	4416	2.9	260.0 !!
H2	FL25*300	S355J2	1	5758	3.8	339.0 !!
T7	FL10*140	S355J2	1	784	0.2	8.6
T8	FL10*120	S355J2	1	1000	0.3	9.4
				Total	22.4	1198.0

Finish Class: Standard

Surface treatment info: | Thickness/start point--> length | No.

weld a = 4

PHASE	QUANTITY
2	1

Undertype of j5 - 2

* o 3 0 4 8 0 - 2 * DS Stålkonstruktion * A j 3 *

PROJECT	Akkasæter Lager- og vedlikeholdshall		EXEC. CLASS EXC 2
MEMBER	Benkile - UT af j5-2	QUANTITY: 1	PROJECT No 30480-2
REVISION	ISSUED: 07.11.2025	DRAFTER: ZLL BIM control: SST	DRAWING No. j.3

Tekla Structures