


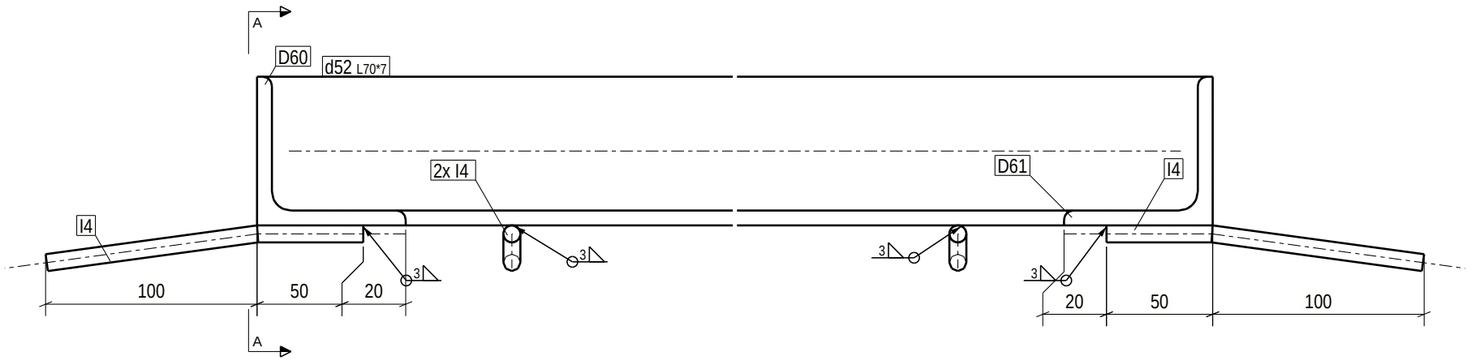


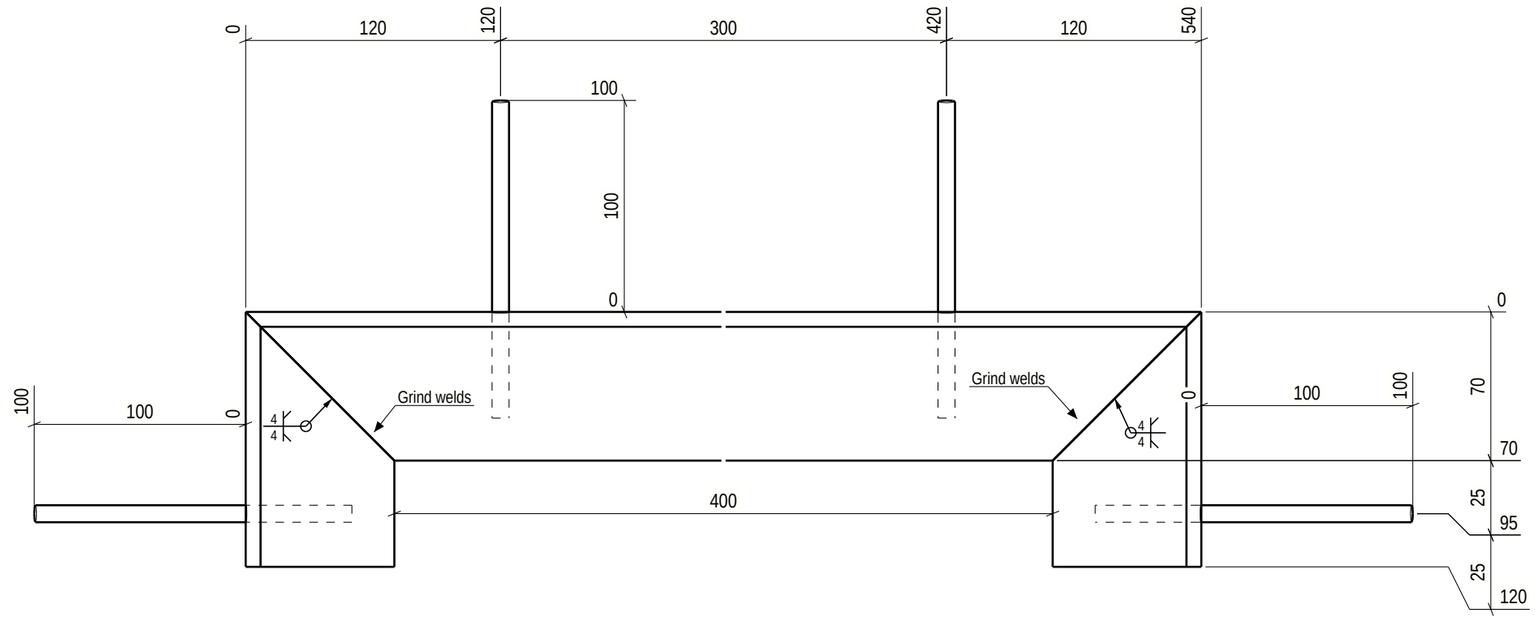

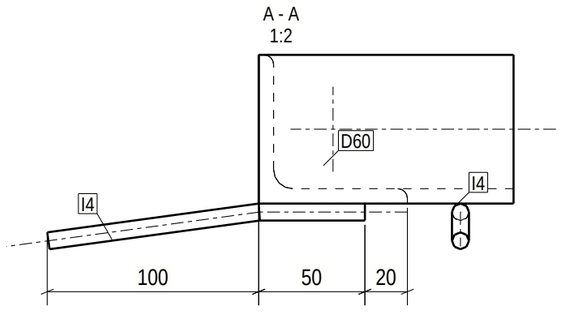

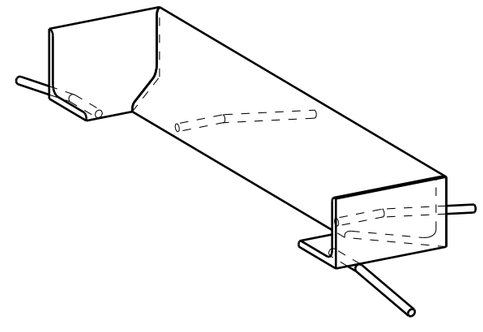

GENERAL NOTES: For your safety, check weight before handling: 0-5kg Light 5-15kg Normal 15+kg Heavy

ALL WELDS ARE 4 UNLESS NOTED ON DRAWING

MATERIAL LIST FOR ASSEMBLY MK'D d.52 6 No. Required

Mark	Profile	Material	No.	Length	Area	Weight
d52	L70*7	S355J2	1	540	0.1	3.7
D60	L70*7	S355J2	1	120	0.0	0.7
D61	L70*7	S355J2	1	120	0.0	0.7
I4	REBAR8	B550B	4	150	0.0	0.1
				Total	0.2	5.4

Finish Class
Standard

Surface treatment info:	Thickness/start point--> length	No.
Galvanised	/	1

Special surface treatment

weld a = 4

PHASE	QUANTITY
4	6

* o 3 0 4 8 0 - 4 * DS Stålkonstruktion * A d 5 2 *

PROJECT	Akkasæter Lager- og vedlikeholdshall			EXEC. CLASS	EXC 2
MEMBER	Drager		QUANTITY: 6	PROJECT No	30480-4
REVISION	ISSUED: 19.11.2025		DRAFTER: ZLL BIM control: SST	DRAWING No.	d.52

Tekla Structures