


APPROVED FOR CONSTRUCTION 12.06.2026

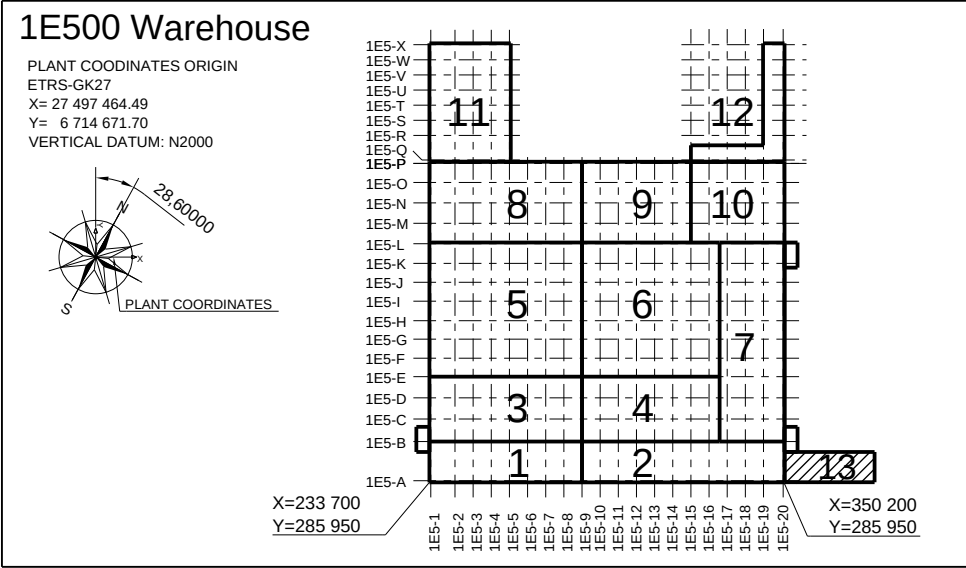

01	E51WC-1027: hollow section added, list updated				FIALES	18.06.2026	FIKJER
REV.		REVISION			CHANGED BY	DATE	CHECKED BY
Date	Designed	Checked	Approved	Status			
05.06.2026	FIALES	FIKJER	FIKOPE	AFC			
Document ID		Area	Relates		Scale	Size	
25019443-ICC250-0600-0660-001333		1E500				A4	
Project ID		Sub area	Position ID		Discipline		
25019443					CIVIL		
		Title Easpring New Materials Oy FAIR phase 1 Warehouse, Steel Structures, Access bridge between 1A100-1E500, Welded Sections, Assembly Drawings					
Drawing number					Revision	Page/Pages	
25019443-ICC250-0600-0660-001333					01	1/1	



Sweco Finland Oy
Ilmalantori 4
00240 Helsinki
Puh. 0207 393 000
etunimi.sukunimi@sweco.fi

ASSEMBLY PART LIST

Project Number		25019443					Content	Access bridge between 1A100-1E500, Welded Sections								
Project Name		Easpring New Materials Oy					Document	25019443-ICC250-0600-0660-001333								
Project Address		FAIR Phase 1					Status	AFC						Revisio	01	
Author	FIALES	Inspector	FIKJER	Approver	FIPEKO		Rev. Comment:		E51WC-1027: hollow section added					Date	18.06.2026	
Phase	Position	Main part name	Main part profile	Exec. Class	Shade (assembly) / Material (part)		Pcs.	Length [mm]	Width [mm]	Height [mm]	Paino [kg]	Weight sum [kg]	Area [m²]	Date	Rev.	Rev. Date
9000	E51W-1001	Beam_WI		EXC2	RAL 7024 (Graphite Gray)		1	7884	948	1600	3641.5	3768.9	42.57	12.06.2026		
9000	E51WL-1020		PL30X600		S355J2+N		1	1600	600	30	226.1	226.1		12.06.2026		
9000	E51WL-1021		PL30X600		S355J2+N		1	1600	600	30	226.1	226.1		12.06.2026		
9000	E51WL-1022		PL15X223		S355J2+N		1	286	223	15	6.3	6.3		12.06.2026		
9000	E51WL-1023		PL5X37		S355J2+N		8	94	37	5	0.1	1.1		12.06.2026		
9000	E51WL-1026		PL12X260		S355J2+N		4	220	260	12	5.4	21.6		12.06.2026		
9000	E51WL-1027		PL15X183		S355J2+N		4	1216	183	15	26.1	104.4		12.06.2026		
9000	E51WP-1001		WI1300-15-40X400		S355J2		1	7824	0	0	3095.7	3095.7		12.06.2026		
9000	E51WP-1029		CFRHS200X100X5		S355J2H		4	454	0	0	10.1	40.5		12.06.2026		
9000	E51WP-1030		CFRHS100X40X3		S355J2H		1	2225	0	0	13.6	13.6		12.06.2026		
9000	E51WP-1031		CFRHS100X40X3		S355J2H		1	4965	0	0	30.4	30.4		12.06.2026		
9000	E51WP-1032		CFRHS100X40X3		S355J2H		2	260	0	0	1.6	3.2		12.06.2026		
9000	E51W-1003	Beam_WI		EXC2	RAL 7024 (Graphite Gray)		2	7884	600	1559	2589.7	5622.6	36.91	12.06.2026		
9000	E51WL-1003		PL15X359		S355J2+N		2	892	359	15	20.2	40.4		12.06.2026		
9000	E51WL-1017		PL10X120		S355J2+N		2	165	120	10	1.6	3.1		12.06.2026		
9000	E51WL-1019		PL30X300		S355J2+N		4	1280	300	30	90.4	361.7		12.06.2026		
9000	E51WP-1002		WI1000-15-30X400		S355J2		2	7824	0	0	2346.4	4692.8		12.06.2026		
9000	E51WP-1007		L100*10		S355J2		4	7510	0	0	113.2	452.8		12.06.2026		
9000	E51WP-1028		L100*10		S355J2		4	1190	0	0	17.9	71.7		12.06.2026		
9000	E51W-1004	Beam_WI		EXC2	RAL 7024 (Graphite Gray)		2	7884	400	1499	2537.0	5255.3	32.25	12.06.2026		
9000	E51WL-1002		PL30X300		S355J2+N		4	1280	300	30	90.4	361.7		12.06.2026		
9000	E51WL-1003		PL15X359		S355J2+N		2	892	359	15	20.2	40.4		12.06.2026		
9000	E51WL-1024		PL5X47		S355J2+N		4	94	47	5	0.2	0.7		12.06.2026		
9000	E51WP-1005		WI1000-15-30X400		S355J2		2	7824	0	0	2346.4	4692.8		12.06.2026		
9000	E51WP-1035		CFRHS100X50X5		S355J2H		2	7610	0	0	79.8	159.6		12.06.2026		
9000	E51W-1005	Beam_WI		EXC2	RAL 7024 (Graphite Gray)		1	8354	565	850	1338.6	1373.0	27.32	12.06.2026		
9000	E51WL-1005		PL20X220		S355J2+N		2	791	220	20	27.3	54.6		12.06.2026		
9000	E51WL-1009		PL15X297		S355J2+N		1	1040	297	15	35.7	35.7		12.06.2026		
9000	E51WL-1014		PL10X146		S355J2+N		2	602	146	10	6.9	13.8		12.06.2026		
9000	E51WL-1024		PL5X47		S355J2+N		2	94	47	5	0.2	0.3		12.06.2026		
9000	E51WP-1012		WI800-8-20X300		S355J2		1	8314	0	0	1181.9	1181.9		12.06.2026		
9000	E51WP-1033		CFRHS100X50X5		S355J2H		1	8264	0	0	86.7	86.7		12.06.2026		

9000	E51W-1006	Beam_WI		EXC2	RAL 7024 (Graphite Gray)	1	8070	400	800	1155.0	1178.4	23.77	12.06.2026		
9000	E51WL-1018		PL10X120		S355J2+N	4	440	120	10	3.9	15.8		12.06.2026		
9000	E51WL-1028		PL5X50		S355J2+N	4	2000	50	5	3.9	15.4		12.06.2026		
9000	E51WP-1027		WI800-8-20X300		S355J2	1	8070	0	0	1147.2	1147.2		12.06.2026		
9000	E51W-1007	Beam_WI		EXC2	RAL 7024 (Graphite Gray)	2	7938	300	842	1224.2	2561.9	25.05	12.06.2026		
9000	E51WL-1001		PL30X300		S355J2+N	4	801	300	30	56.6	226.4		12.06.2026		
9000	E51WL-1023		PL5X37		S355J2+N	4	94	37	5	0.1	0.5		12.06.2026		
9000	E51WP-1004		WI800-8-20X300		S355J2	2	7877	0	0	1119.7	2239.4		12.06.2026		
9000	E51WP-1008		CFRHS100X40X3		S355J2H	2	7791	0	0	47.8	95.5		12.06.2026		
9000	E51W-1008	Beam_WI		EXC2	RAL 7024 (Graphite Gray)	1	8070	400	800	1155.0	1178.4	23.77	12.06.2026		
9000	E51WL-1018		PL10X120		S355J2+N	4	440	120	10	3.9	15.8		12.06.2026		
9000	E51WL-1028		PL5X50		S355J2+N	4	2000	50	5	3.9	15.4		12.06.2026		
9000	E51WP-1003		WI800-8-20X300		S355J2	1	8070	0	0	1147.2	1147.2		12.06.2026		
9000	E51W-1009	Beam_WI		EXC2	RAL 7024 (Graphite Gray)	2	8354	300	850	1328.2	2711.4	27.15	12.06.2026		
9000	E51WL-1005		PL20X220		S355J2+N	4	791	220	20	27.3	109.2		12.06.2026		
9000	E51WL-1025		PL5X47		S355J2+N	4	144	47	5	0.3	1.1		12.06.2026		
9000	E51WP-1006		WI800-8-20X300		S355J2	2	8314	0	0	1181.9	2363.8		12.06.2026		
9000	E51WP-1034		CFRHS150X50X5		S355J2H	2	8264	0	0	118.7	237.4		12.06.2026		
9000	E51W-1010	Beam_WI		EXC2	RAL 7024 (Graphite Gray)	5	8070	300	850	1231.7	6159.5	24.80	12.06.2026		
9000	E51WL-1024		PL5X47		S355J2+N	10	94	47	5	0.2	1.7		12.06.2026		
9000	E51WP-1009		WI800-8-20X300		S355J2	5	8070	0	0	1147.2	5736.1		12.06.2026		
9000	E51WP-1036		CFRHS100X50X5		S355J2H	5	8040	0	0	84.3	421.6		12.06.2026		
9000	E51W-1011	Beam_WI		EXC2	RAL 7024 (Graphite Gray)	1	8354	565	850	1331.5	1366.0	27.32	12.06.2026		
9000	E51WL-1005		PL20X220		S355J2+N	2	791	220	20	27.3	54.6		12.06.2026		
9000	E51WL-1010		PL12X297		S355J2+N	1	1040	297	12	28.6	28.6		12.06.2026		
9000	E51WL-1024		PL5X47		S355J2+N	2	94	47	5	0.2	0.3		12.06.2026		
9000	E51WL-1029		PL10X146		S355J2+N	2	607	146	10	7.0	13.9		12.06.2026		
9000	E51WP-1011		WI800-8-20X300		S355J2	1	8314	0	0	1181.9	1181.9		12.06.2026		
9000	E51WP-1033		CFRHS100X50X5		S355J2H	1	8264	0	0	86.7	86.7		12.06.2026		
9000	E51W-1012	Beam_WI		EXC2	RAL 7024 (Graphite Gray)	1	8354	471	850	1323.6	1358.0	27.15	12.06.2026		
9000	E51WL-1005		PL20X220		S355J2+N	2	791	220	20	27.3	54.6		12.06.2026		
9000	E51WL-1011		PL12X247		S355J2+N	1	904	247	12	20.6	20.6		12.06.2026		
9000	E51WL-1024		PL5X47		S355J2+N	2	94	47	5	0.2	0.3		12.06.2026		
9000	E51WL-1029		PL10X146		S355J2+N	2	607	146	10	7.0	13.9		12.06.2026		
9000	E51WP-1013		WI800-8-20X300		S355J2	1	8314	0	0	1181.9	1181.9		12.06.2026		
9000	E51WP-1033		CFRHS100X50X5		S355J2H	1	8264	0	0	86.7	86.7		12.06.2026		
9000	E51W-1013	Beam_WI		EXC2	RAL 7024 (Graphite Gray)	1	8354	471	850	1323.6	1358.0	27.15	12.06.2026		
9000	E51WL-1005		PL20X220		S355J2+N	2	791	220	20	27.3	54.6		12.06.2026		
9000	E51WL-1011		PL12X247		S355J2+N	1	904	247	12	20.6	20.6		12.06.2026		
9000	E51WL-1024		PL5X47		S355J2+N	2	94	47	5	0.2	0.3		12.06.2026		

9000	E51WL-1029		PL10X146		S355J2+N	2	607	146	10	7.0	13.9		12.06.2026		
9000	E51WP-1013		WI800-8-20X300		S355J2	1	8314	0	0	1181.9	1181.9		12.06.2026		
9000	E51WP-1033		CFRHS100X50X5		S355J2H	1	8264	0	0	86.7	86.7		12.06.2026		
9000	E51W-1014	Beam_WI		EXC2	RAL 7024 (Graphite Gray)	1	8354	565	850	1331.5	1366.0	27.32	12.06.2026		
9000	E51WL-1005		PL20X220		S355J2+N	2	791	220	20	27.3	54.6		12.06.2026		
9000	E51WL-1010		PL12X297		S355J2+N	1	1040	297	12	28.6	28.6		12.06.2026		
9000	E51WL-1024		PL5X47		S355J2+N	2	94	47	5	0.2	0.3		12.06.2026		
9000	E51WL-1029		PL10X146		S355J2+N	2	607	146	10	7.0	13.9		12.06.2026		
9000	E51WP-1011		WI800-8-20X300		S355J2	1	8314	0	0	1181.9	1181.9		12.06.2026		
9000	E51WP-1033		CFRHS100X50X5		S355J2H	1	8264	0	0	86.7	86.7		12.06.2026		
9000	E51W-1015	Beam_WI		EXC2	RAL 7024 (Graphite Gray)	1	8354	565	850	1338.6	1373.0	27.32	12.06.2026		
9000	E51WL-1005		PL20X220		S355J2+N	2	791	220	20	27.3	54.6		12.06.2026		
9000	E51WL-1009		PL15X297		S355J2+N	1	1040	297	15	35.7	35.7		12.06.2026		
9000	E51WL-1014		PL10X146		S355J2+N	2	602	146	10	6.9	13.8		12.06.2026		
9000	E51WL-1024		PL5X47		S355J2+N	2	94	47	5	0.2	0.3		12.06.2026		
9000	E51WP-1012		WI800-8-20X300		S355J2	1	8314	0	0	1181.9	1181.9		12.06.2026		
9000	E51WP-1033		CFRHS100X50X5		S355J2H	1	8264	0	0	86.7	86.7		12.06.2026		
9000	E51W-1028	Beam_WI		EXC2	RAL 7024 (Graphite Gray)	1	7884	774	1600	3641.5	3737.9	41.78	12.06.2026		
9000	E51WL-1020		PL30X600		S355J2+N	1	1600	600	30	226.1	226.1		12.06.2026		
9000	E51WL-1021		PL30X600		S355J2+N	1	1600	600	30	226.1	226.1		12.06.2026		
9000	E51WL-1022		PL15X223		S355J2+N	1	286	223	15	6.3	6.3		12.06.2026		
9000	E51WL-1023		PL5X37		S355J2+N	8	94	37	5	0.1	1.1		12.06.2026		
9000	E51WL-1026		PL12X260		S355J2+N	2	220	260	12	5.4	10.8		12.06.2026		
9000	E51WL-1027		PL15X183		S355J2+N	4	1216	183	15	26.1	104.4		12.06.2026		
9000	E51WP-1001		WI1300-15-40X400		S355J2	1	7824	0	0	3095.7	3095.7		12.06.2026		
9000	E51WP-1029		CFRHS200X100X5		S355J2H	2	454	0	0	10.1	20.2		12.06.2026		
9000	E51WP-1030		CFRHS100X40X3		S355J2H	1	2225	0	0	13.6	13.6		12.06.2026		
9000	E51WP-1031		CFRHS100X40X3		S355J2H	1	4965	0	0	30.4	30.4		12.06.2026		
9000	E51WP-1032		CFRHS100X40X3		S355J2H	2	260	0	0	1.6	3.2		12.06.2026		
9000	E51WC-1001	COLUMN_WI		EXC2	RAL 7024 (Graphite Gray)	1	11910	1230	1620	8131.2	8641.0	67.41	12.06.2026		
9000	E51WCL-1001		PL70X1220		S355J2+N	1	1320	1220	70	884.9	884.9		12.06.2026		
9000	E51WCL-1056		PL35X230		S355J2+N	4	1300	230	35	76.9	307.5		12.06.2026		
9000	E51WCL-1104		PL25X300		S355J2+N	1	505	300	25	29.7	29.7		12.06.2026		
9000	E51WCL-1105		PL15X282		S355J2+N	1	400	282	15	12.1	12.1		12.06.2026		
9000	E51WCL-1116		PL15X232		S355J2+N	2	283	232	15	7.7	15.4		12.06.2026		
9000	E51WCL-1117		PL30X233		S355J2+N	2	726	233	30	37.6	75.3		12.06.2026		
9000	E51WCL-1119		PL40X393		S355J2+N	2	726	393	40	84.3	168.5		12.06.2026		
9000	E51WCL-1121		PL30X582		S355J2+N	1	1123	582	30	131.1	131.1		12.06.2026		
9000	E51WCL-1122		PL35X283		S355J2+N	1	726	283	35	53.3	53.3		12.06.2026		
9000	E51WCL-1123		PL20X349		S355J2+N	4	478	349	20	25.4	101.4		12.06.2026		
9000	E51WCL-1148		PL12X497		S355J2+N	2	403	497	12	18.8	37.6		12.06.2026		
9000	E51WCL-1149		PL20X393		S355J2+N	2	726	393	20	44.2	88.5		12.06.2026		
9000	E51WCL-1150		PL30X460		S355J2+N	1	1141	460	30	121.3	121.3		12.06.2026		

9000	E51WCL-1151		PL30X480		S355J2+N	1	1297	480	30	133.9	133.9		12.06.2026		
9000	E51WCL-1155		PL30X190		S355J2+N	1	200	190	30	8.9	8.9		12.06.2026		
9000	E51WCL-1162		PL5X37		S355J2+N	1	94	37	5	0.1	0.1		12.06.2026	01	18.06.2026
9000	E51WCL-1163		PL5X34		S355J2+N	4	94	34	5	0.1	0.5		12.06.2026		
9000	E51WCL-1165		PL15X282		S355J2+N	1	400	282	15	13.3	13.3		12.06.2026		
9000	E51WCL-1166		PL20X283		S355J2+N	1	726	283	20	32.0	32.0		12.06.2026		
9000	E51WCL-1167		PL12X190		S355J2+N	1	390	190	12	7.0	7.0		12.06.2026		
9000	E51WCL-1168		PL12X190		S355J2+N	1	290	190	12	5.2	5.2		12.06.2026		
9000	E51WCL-1177		PL5X90		S355J2+N	1	90	90	5	0.3	0.3		12.06.2026		
9000	E51WCL-1178		PL12X205		S355J2+N	1	210	205	12	4.1	4.1		12.06.2026		
9000	E51WCL-1179		PL5X100		S355J2+N	1	100	100	5	0.4	0.4		12.06.2026		
9000	E51WCL-1180		PL12X105		S355J2+N	2	200	105	12	1.9	3.9		12.06.2026		
9000	E51WCL-1186		PL25X200		S355J2+N	2	220	200	25	8.1	16.2		12.06.2026		
9000	E51WCL-1195		PL35X283		S355J2+N	1	726	283	35	53.0	53.0		12.06.2026		
9000	E51WCL-1196		PL20X283		S355J2+N	1	726	283	20	32.0	32.0		12.06.2026		
9000	E51WCL-1197		PL12X200		S355J2+N	1	250	200	12	4.6	4.6		12.06.2026		
9000	E51WCP-1026		WI350-25-35X250		S355J2+N	1	420	0	0	81.7	81.7		12.06.2026		
9000	E51WCP-1031		L100*10		S355J2	1	378	0	0	5.7	5.7		12.06.2026		
9000	E51WCP-1082		WI800-35-35X600		S355J2	1	11420	0	0	6106.2	6106.2		12.06.2026		
9000	E51WCP-1092		L100*10		S355J2	1	378	0	0	5.7	5.7		12.06.2026		
9000	E51WCP-1113		IPE550		S355J2	1	560	0	0	58.9	58.9		12.06.2026		
9000	E51WCP-1114		CFRHS100X100X6		S355J2H	1	640	0	0	10.9	10.9		12.06.2026		
9000	E51WCP-1116		CFRHS100X40X3		S355J2H	1	515	0	0	3.2	3.2		12.06.2026	01	18.06.2026
9000	E51WCP-1117		CFRHS100X40X3		S355J2H	1	1030	0	0	6.3	6.3		12.06.2026		
9000	E51WCP-1118		CFRHS100X40X3		S355J2H	1	1065	0	0	6.5	6.5		12.06.2026		
9000	E51WCP-1132		L100*12		S355J2	1	782	0	0	13.9	13.9		12.06.2026		
9000	E51WC-1010	COLUMN_WI		EXC2	RAL 7024 (Graphite Gray)	1	13223	520	1028	1409.5	1411.7	35.77	12.06.2026		
9000	E51WCL-1017		PL12X170		S355J2+N	1	576	170	12	9.1	9.1		12.06.2026		
9000	E51WCL-1053		PL10X170		S355J2+N	1	170	170	10	2.3	2.3		12.06.2026		
9000	E51WCL-1054		PL10X115		S355J2+N	1	700	115	10	6.3	6.3		12.06.2026		
9000	E51WCL-1067		PL10X90		S355J2+N	1	576	90	10	4.1	4.1		12.06.2026		
9000	E51WCL-1115		PL10X228		S355J2+N	1	285	228	10	3.9	3.9		12.06.2026		
9000	E51WCL-1124		PL10X230		S355J2+N	1	621	230	10	11.2	11.2		12.06.2026		
9000	E51WCL-1125		PL10X90		S355J2+N	1	576	90	10	4.0	4.0		12.06.2026		
9000	E51WCL-1145		PL25X520		S355J2+N	1	411	520	25	38.9	38.9		12.06.2026		
9000	E51WCL-1146		PL15X425		S355J2+N	1	496	425	15	21.0	21.0		12.06.2026		
9000	E51WCL-1170		PL5X94		S355J2+N	4	197	94	5	0.7	2.9		12.06.2026		
9000	E51WCL-1174		PL8X90		S355J2+N	1	190	90	8	1.1	1.1		12.06.2026		
9000	E51WCP-1003		WI600-10-10X200		S355J2	1	13187	0	0	1019.3	1019.3		12.06.2026		
9000	E51WCP-1080		L100*10		S355J2	1	586	0	0	8.8	8.8		12.06.2026		
9000	E51WCP-1095		CFRHS200X100X5		S355J2H	1	4170	0	0	92.8	92.8		12.06.2026		
9000	E51WCP-1104		CFRHS200X100X5		S355J2H	1	8166	0	0	181.8	181.8		12.06.2026		
9000	E51WCP-1126		IPE200		S355J2	1	192	0	0	4.3	4.3		12.06.2026		
9000	E51WC-1012	COLUMN_WI		EXC2	RAL 7024 (Graphite Gray)	1	5790	700	1028	740.9	746.4	16.98	12.06.2026		
9000	E51WCL-1011		PL20X170		S355J2+N	1	576	170	20	15.1	15.1		12.06.2026		

9000	E51WCL-1052		PL10X228		S355J2+N	1	284	228	10	3.8	3.8		12.06.2026		
9000	E51WCL-1053		PL10X170		S355J2+N	1	170	170	10	2.3	2.3		12.06.2026		
9000	E51WCL-1143		PL25X700		S355J2+N	1	420	700	25	53.2	53.2		12.06.2026		
9000	E51WCL-1152		PL20X250		S355J2+N	1	582	250	20	22.8	22.8		12.06.2026		
9000	E51WCL-1154		PL20X99		S355J2+N	1	576	99	20	8.9	8.9		12.06.2026		
9000	E51WCL-1156		PL15X365		S355J2+N	1	683	365	15	25.9	25.9		12.06.2026		
9000	E51WCL-1171		PL5X194		S355J2+N	4	197	194	5	1.5	6.0		12.06.2026		
9000	E51WCL-1190		PL5X194		S355J2+N	1	194	194	5	1.5	1.5		12.06.2026		
9000	E51WCL-1192		PL8X194		S355J2+N	1	197	194	8	2.4	2.4		12.06.2026		
9000	E51WCL-1193		PL10X91		S355J2+N	2	150	91	10	1.0	2.0		12.06.2026		
9000	E51WCL-1194		PL30X300		S355J2+N	1	576	300	30	40.7	40.7		12.06.2026		
9000	E51WCP-1080		L100*10		S355J2	1	586	0	0	8.8	8.8		12.06.2026		
9000	E51WCP-1087		WI600-10-10X210		S355J2	1	5175	0	0	408.1	408.1		12.06.2026		
9000	E51WCP-1101		CFRHS200X200X5		S355J2H	1	1690	0	0	50.9	50.9		12.06.2026		
9000	E51WCP-1135		CFRHS200X200X5		S355J2H	1	907	0	0	27.3	27.3		12.06.2026		
9000	E51WCP-1136		CFRHS200X200X5		S355J2H	1	2210	0	0	66.5	66.5		12.06.2026		
9000	E51WC-1013	COLUMN_WI		EXC2	RAL 7024 (Graphite Gray)	1	5790	995	1028	895.2	935.2	18.50	12.06.2026		
9000	E51WCL-1026		PL25X270		S355J2+N	2	566	270	25	29.7	59.3		12.06.2026		
9000	E51WCL-1052		PL10X228		S355J2+N	1	284	228	10	3.8	3.8		12.06.2026		
9000	E51WCL-1053		PL10X170		S355J2+N	1	170	170	10	2.3	2.3		12.06.2026		
9000	E51WCL-1143		PL25X700		S355J2+N	1	420	700	25	53.2	53.2		12.06.2026		
9000	E51WCL-1144		PL30X512		S355J2+N	1	995	512	30	93.0	93.0		12.06.2026		
9000	E51WCL-1171		PL5X194		S355J2+N	2	197	194	5	1.5	3.0		12.06.2026		
9000	E51WCP-1009		WI600-10-15X250		S355J2	1	5175	0	0	538.1	538.1		12.06.2026		
9000	E51WCP-1080		L100*10		S355J2	2	586	0	0	8.8	17.7		12.06.2026		
9000	E51WCP-1102		CFRHS200X200X5		S355J2H	1	5470	0	0	164.7	164.7		12.06.2026		
9000	E51WC-1017	COLUMN_WI		EXC2	RAL 7024 (Graphite Gray)	1	13350	355	1028	1314.5	1334.1	34.05	12.06.2026		
9000	E51WCL-1018		PL12X235		S355J2+N	1	576	235	12	12.6	12.6		12.06.2026		
9000	E51WCL-1053		PL10X170		S355J2+N	1	170	170	10	2.3	2.3		12.06.2026		
9000	E51WCL-1054		PL10X115		S355J2+N	1	700	115	10	6.3	6.3		12.06.2026		
9000	E51WCL-1067		PL10X90		S355J2+N	2	576	90	10	4.1	8.1		12.06.2026		
9000	E51WCL-1124		PL10X230		S355J2+N	1	621	230	10	11.2	11.2		12.06.2026		
9000	E51WCL-1127		PL25X210		S355J2+N	1	593	210	25	24.4	24.4		12.06.2026		
9000	E51WCL-1129		PL10X228		S355J2+N	1	262	228	10	3.4	3.4		12.06.2026		
9000	E51WCL-1147		PL15X95		S355J2+N	4	400	95	15	4.5	17.8		12.06.2026		
9000	E51WCL-1170		PL5X94		S355J2+N	4	197	94	5	0.7	2.9		12.06.2026		
9000	E51WCL-1172		PL8X150		S355J2+N	1	142	150	8	1.3	1.3		12.06.2026		
9000	E51WCP-1080		L100*10		S355J2	1	586	0	0	8.8	8.8		12.06.2026		
9000	E51WCP-1085		WI600-10-10X200		S355J2	1	12285	0	0	949.5	949.5		12.06.2026		
9000	E51WCP-1096		CFRHS200X100X5		S355J2H	1	3670	0	0	81.7	81.7		12.06.2026		
9000	E51WCP-1099		CFRHS200X100X5		S355J2H	1	8890	0	0	197.9	197.9		12.06.2026		
9000	E51WCP-1131		HEA160		S355J2	1	192	0	0	5.8	5.8		12.06.2026		
9000	E51WC-1018	COLUMN_WI		EXC2	RAL 7024 (Graphite Gray)	1	5790	1076	1052	872.4	886.4	18.57	12.06.2026		
9000	E51WCL-1027		PL30X1081		S355J2+N	1	1159	1081	30	229.1	229.1		12.06.2026		

9000	E51WCL-1043		PL15X273		S355J2+N	1	300	273	15	9.5	9.5		12.06.2026		
9000	E51WCL-1044		PL15X250		S355J2+N	1	273	250	15	8.0	8.0		12.06.2026		
9000	E51WCL-1045		PL15X227		S355J2+N	1	280	227	15	5.7	5.7		12.06.2026		
9000	E51WCL-1046		PL15X204		S355J2+N	1	229	204	15	4.0	4.0		12.06.2026		
9000	E51WCL-1052		PL10X228		S355J2+N	1	284	228	10	3.8	3.8		12.06.2026		
9000	E51WCL-1053		PL10X170		S355J2+N	1	170	170	10	2.3	2.3		12.06.2026		
9000	E51WCL-1113		PL15X250		S355J2+N	1	273	250	15	7.5	7.5		12.06.2026		
9000	E51WCL-1114		PL15X273		S355J2+N	1	300	273	15	9.1	9.1		12.06.2026		
9000	E51WCL-1142		PL20X220		S355J2+N	1	420	220	20	14.5	14.5		12.06.2026		
9000	E51WCL-1171		PL5X194		S355J2+N	2	197	194	5	1.5	3.0		12.06.2026		
9000	E51WCP-1010		WI600-10-10X210		S355J2	1	5180	0	0	408.5	408.5		12.06.2026		
9000	E51WCP-1081		L100*10		S355J2	4	278	0	0	4.2	16.8		12.06.2026		
9000	E51WCP-1102		CFRHS200X200X5		S355J2H	1	5470	0	0	164.7	164.7		12.06.2026		
9000	E51WC-1020	COLUMN_WI		EXC2	RAL 7024 (Graphite Gray)	1	5790	1075	1050	872.0	886.1	18.57	12.06.2026		
9000	E51WCL-1028		PL30X1081		S355J2+N	1	1158	1081	30	228.9	228.9		12.06.2026		
9000	E51WCL-1044		PL15X250		S355J2+N	1	273	250	15	8.0	8.0		12.06.2026		
9000	E51WCL-1047		PL15X273		S355J2+N	1	300	273	15	9.5	9.5		12.06.2026		
9000	E51WCL-1052		PL10X228		S355J2+N	1	284	228	10	3.8	3.8		12.06.2026		
9000	E51WCL-1053		PL10X170		S355J2+N	1	170	170	10	2.3	2.3		12.06.2026		
9000	E51WCL-1111		PL15X206		S355J2+N	1	233	206	15	4.2	4.2		12.06.2026		
9000	E51WCL-1112		PL15X221		S355J2+N	1	280	221	15	5.5	5.5		12.06.2026		
9000	E51WCL-1113		PL15X250		S355J2+N	1	273	250	15	7.5	7.5		12.06.2026		
9000	E51WCL-1114		PL15X273		S355J2+N	1	300	273	15	9.1	9.1		12.06.2026		
9000	E51WCL-1142		PL20X220		S355J2+N	1	420	220	20	14.5	14.5		12.06.2026		
9000	E51WCL-1171		PL5X194		S355J2+N	2	197	194	5	1.5	3.0		12.06.2026		
9000	E51WCP-1010		WI600-10-10X210		S355J2	1	5180	0	0	408.5	408.5		12.06.2026		
9000	E51WCP-1081		L100*10		S355J2	4	278	0	0	4.2	16.8		12.06.2026		
9000	E51WCP-1102		CFRHS200X200X5		S355J2H	1	5470	0	0	164.7	164.7		12.06.2026		
9000	E51WC-1024	COLUMN_WI		EXC2	RAL 7024 (Graphite Gray)	1	8083	1225	915	1247.6	1392.9	27.74	12.06.2026		
9000	E51WCL-1054		PL10X115		S355J2+N	1	700	115	10	6.3	6.3		12.06.2026		
9000	E51WCL-1128		PL10X220		S355J2+N	1	621	220	10	10.7	10.7		12.06.2026		
9000	E51WCL-1130		PL30X1147		S355J2+N	1	1278	1147	30	293.8	293.8		12.06.2026		
9000	E51WCL-1131		PL40X430		S355J2+N	2	550	430	40	74.3	148.5		12.06.2026		
9000	E51WCL-1134		PL16X134		S355J2+N	4	1141	134	16	19.2	76.7		12.06.2026		
9000	E51WCL-1171		PL5X194		S355J2+N	8	197	194	5	1.5	12.0		12.06.2026		
9000	E51WCL-1173		PL8X110		S355J2+N	1	230	110	8	1.6	1.6		12.06.2026		
9000	E51WCL-1188		PL10X135		S355J2+N	2	294	135	10	3.0	6.1		12.06.2026		
9000	E51WCP-1088		WI600-10-10X210		S355J2	1	8072	0	0	636.6	636.6		12.06.2026		
9000	E51WCP-1098		CFRHS200X200X5		S355J2H	1	2910	0	0	87.6	87.6		12.06.2026		
9000	E51WCP-1120		IPE240		S355J2	1	192	0	0	5.9	5.9		12.06.2026		
9000	E51WCP-1123		CFRHS200X200X5		S355J2H	1	1635	0	0	49.2	49.2		12.06.2026		
9000	E51WCP-1137		CFRHS200X200X5		S355J2H	1	910	0	0	27.4	27.4		12.06.2026		
9000	E51WCP-1138		CFRHS200X200X5		S355J2H	1	1010	0	0	30.4	30.4		12.06.2026		
9000	E51WC-1025	COLUMN_WI		EXC2	RAL 7024 (Graphite Gray)	2	7620	604	1028	1155.8	2482.5	24.96	12.06.2026		

9000	E51WCL-1054		PL10X115		S355J2+N	2	700	115	10	6.3	12.6		12.06.2026		
9000	E51WCL-1128		PL10X220		S355J2+N	2	621	220	10	10.7	21.4		12.06.2026		
9000	E51WCL-1136		PL40X450		S355J2+N	4	550	450	40	77.7	310.9		12.06.2026		
9000	E51WCL-1164		PL10X228		S355J2+N	2	261	228	10	3.4	6.7		12.06.2026		
9000	E51WCL-1171		PL5X194		S355J2+N	8	197	194	5	1.5	12.0		12.06.2026		
9000	E51WCL-1173		PL8X110		S355J2+N	2	230	110	8	1.6	3.2		12.06.2026		
9000	E51WCL-1189		PL10X145		S355J2+N	4	296	145	10	3.3	13.1		12.06.2026		
9000	E51WCP-1086		WI600-10-15X250		S355J2	2	7610	0	0	791.3	1582.5		12.06.2026		
9000	E51WCP-1098		CFRHS200X200X5		S355J2H	2	2910	0	0	87.6	175.2		12.06.2026		
9000	E51WCP-1112		HEA340		S355J2	2	524	0	0	54.9	109.8		12.06.2026		
9000	E51WCP-1120		IPE240		S355J2	2	192	0	0	5.9	11.8		12.06.2026		
9000	E51WCP-1121		CFRHS200X200X5		S355J2H	2	3706	0	0	111.6	223.2		12.06.2026		
9000	E51WC-1027	COLUMN_WI		EXC2	RAL 7024 (Graphite Gray)	1	7930	604	1360	2415.3	2571.0	27.25	12.06.2026	01	17.06.2026
9000	E51WCL-1005		PL20X125		S355J2+N	2	756	125	20	14.7	29.5		12.06.2026		
9000	E51WCL-1073		PL30X125		S355J2+N	2	756	125	30	20.5	40.9		12.06.2026		
9000	E51WCL-1107		PL8X176		S355J2+N	1	186	176	8	2.1	2.1		12.06.2026		
9000	E51WCL-1108		PL12X115		S355J2+N	1	134	115	12	1.2	1.2		12.06.2026		
9000	E51WCL-1136		PL40X450		S355J2+N	2	550	450	40	77.7	155.4		12.06.2026		
9000	E51WCL-1159		PL8X297		S355J2+N	1	212	297	8	4.0	4.0		12.06.2026		
9000	E51WCL-1160		PL8X297		S355J2+N	1	228	297	8	4.2	4.2		12.06.2026		
9000	E51WCL-1162		PL5X37		S355J2+N	2	94	37	5	0.1	0.3		12.06.2026	01	18.06.2026
9000	E51WCL-1187		PL16X125		S355J2+N	4	228	125	16	3.5	13.9		12.06.2026		
9000	E51WCP-1107		HEA200		S355J2	1	560	0	0	23.7	23.7		12.06.2026		
9000	E51WCP-1110		HEA340		S355J2	2	247	0	0	25.9	51.8		12.06.2026		
9000	E51WCP-1116		CFRHS100X40X3		S355J2H	1	515	0	0	3.2	3.2		12.06.2026	01	18.06.2026
9000	E51WCP-1127		UNP200		S355J2	2	250	0	0	6.3	12.6		12.06.2026		
9000	E51WCP-1134		HEA260		S355J2	1	561	0	0	38.2	38.2		12.06.2026		
9000	E51WCP-1142		WI800-30-20X300		S355J2	1	7922	0	0	2190.0	2190.0		12.06.2026		
9000	E51WC-1028	COLUMN_WI		EXC2	RAL 7024 (Graphite Gray)	1	9030	734	1025	2681.3	2825.7	32.82	12.06.2026		
9000	E51WCL-1005		PL20X125		S355J2+N	2	756	125	20	14.7	29.5		12.06.2026		
9000	E51WCL-1073		PL30X125		S355J2+N	2	756	125	30	20.5	40.9		12.06.2026		
9000	E51WCL-1107		PL8X176		S355J2+N	1	186	176	8	2.1	2.1		12.06.2026		
9000	E51WCL-1108		PL12X115		S355J2+N	1	134	115	12	1.2	1.2		12.06.2026		
9000	E51WCL-1136		PL40X450		S355J2+N	2	550	450	40	77.7	155.4		12.06.2026		
9000	E51WCL-1160		PL8X297		S355J2+N	1	228	297	8	4.2	4.2		12.06.2026		
9000	E51WCL-1161		PL8X297		S355J2+N	1	281	297	8	5.2	5.2		12.06.2026		
9000	E51WCL-1169		PL5X144		S355J2+N	2	97	144	5	0.5	1.1		12.06.2026		
9000	E51WCL-1182		PL15X138		S355J2+N	1	296	138	15	4.8	4.8		12.06.2026		
9000	E51WCL-1183		PL15X296		S355J2+N	1	325	296	15	11.3	11.3		12.06.2026		
9000	E51WCL-1187		PL16X125		S355J2+N	4	228	125	16	3.5	13.9		12.06.2026		
9000	E51WCL-1191		PL10X107		S355J2+N	4	205	107	10	1.7	6.8		12.06.2026		
9000	E51WCP-1015		WI800-30-20X300		S355J2	1	8385	0	0	2317.9	2317.9		12.06.2026		
9000	E51WCP-1037		T140-15-15-150		S355J2+N	1	1050	0	0	34.4	34.4		12.06.2026		
9000	E51WCP-1045		CFRHS200X120X5		S355J2H	1	85	0	0	2.0	2.0		12.06.2026		
9000	E51WCP-1103		CFRHS150X100X3		S355J2H	1	7610	0	0	86.1	86.1		12.06.2026		

9000	E51WCP-1110		HEA340		S355J2	1	247	0	0	25.9	25.9		12.06.2026		
9000	E51WCP-1111		HEA340		S355J2	1	377	0	0	39.5	39.5		12.06.2026		
9000	E51WCP-1119		UNP200		S355J2	1	250	0	0	6.3	6.3		12.06.2026		
9000	E51WCP-1125		UNP200		S355J2	1	250	0	0	6.3	6.3		12.06.2026		
9000	E51WCP-1141		HEA240		S355J2	2	255	0	0	15.4	30.8		12.06.2026		
9000	E51WC-1063	COLUMN_WI		EXC2	RAL 7024 (Graphite Gray)	1	12760	520	1488	1124.5	1126.3	28.20	12.06.2026		
9000	E51WCL-1018		PL12X235		S355J2+N	1	575	235	12	12.6	12.6		12.06.2026		
9000	E51WCL-1053		PL10X170		S355J2+N	1	170	170	10	2.3	2.3		12.06.2026		
9000	E51WCL-1054		PL10X115		S355J2+N	1	700	115	10	6.3	6.3		12.06.2026		
9000	E51WCL-1067		PL10X90		S355J2+N	1	575	90	10	4.1	4.1		12.06.2026		
9000	E51WCL-1124		PL10X230		S355J2+N	1	621	230	10	11.2	11.2		12.06.2026		
9000	E51WCL-1125		PL10X90		S355J2+N	1	575	90	10	4.0	4.0		12.06.2026		
9000	E51WCL-1129		PL10X228		S355J2+N	1	262	228	10	3.4	3.4		12.06.2026		
9000	E51WCL-1145		PL25X520		S355J2+N	1	411	520	25	38.9	38.9		12.06.2026		
9000	E51WCL-1146		PL15X425		S355J2+N	1	496	425	15	21.0	21.0		12.06.2026		
9000	E51WCL-1158		PL10X85		S355J2+N	4	90	85	10	0.6	2.3		12.06.2026		
9000	E51WCP-1080		L100*10		S355J2	1	586	0	0	8.8	8.8		12.06.2026		
9000	E51WCP-1084		WI600-10-10X200		S355J2	1	12725	0	0	983.5	983.5		12.06.2026		
9000	E51WCP-1106		HEA200		S355J2	1	660	0	0	27.9	27.9		12.06.2026		
9000	E51WC-1064	COLUMN_WI		EXC2	RAL 7024 (Graphite Gray)	1	5790	700	1052	747.0	754.0	17.06	12.06.2026		
9000	E51WCL-1013		PL20X240		S355J2+N	1	576	240	20	20.9	20.9		12.06.2026		
9000	E51WCL-1021		PL15X221		S355J2+N	1	280	221	15	5.6	5.6		12.06.2026		
9000	E51WCL-1053		PL10X170		S355J2+N	1	170	170	10	2.3	2.3		12.06.2026		
9000	E51WCL-1143		PL25X700		S355J2+N	1	420	700	25	53.2	53.2		12.06.2026		
9000	E51WCL-1152		PL20X250		S355J2+N	1	582	250	20	22.8	22.8		12.06.2026		
9000	E51WCL-1154		PL20X99		S355J2+N	1	576	99	20	8.9	8.9		12.06.2026		
9000	E51WCL-1156		PL15X365		S355J2+N	1	683	365	15	25.9	25.9		12.06.2026		
9000	E51WCL-1171		PL5X194		S355J2+N	5	197	194	5	1.5	7.5		12.06.2026		
9000	E51WCL-1192		PL8X194		S355J2+N	1	197	194	8	2.4	2.4		12.06.2026		
9000	E51WCL-1193		PL10X91		S355J2+N	2	150	91	10	1.0	2.0		12.06.2026		
9000	E51WCL-1194		PL30X300		S355J2+N	1	576	300	30	40.7	40.7		12.06.2026		
9000	E51WCP-1080		L100*10		S355J2	1	586	0	0	8.8	8.8		12.06.2026		
9000	E51WCP-1087		WI600-10-10X210		S355J2	1	5175	0	0	408.1	408.1		12.06.2026		
9000	E51WCP-1101		CFRHS200X200X5		S355J2H	1	1690	0	0	50.9	50.9		12.06.2026		
9000	E51WCP-1135		CFRHS200X200X5		S355J2H	1	907	0	0	27.3	27.3		12.06.2026		
9000	E51WCP-1136		CFRHS200X200X5		S355J2H	1	2210	0	0	66.5	66.5		12.06.2026		
9000	E51WC-1065	COLUMN_WI		EXC2	RAL 7024 (Graphite Gray)	1	5790	995	1036	926.5	966.7	19.49	12.06.2026		
9000	E51WCL-1025		PL15X251		S355J2+N	2	255	251	15	4.7	9.4		12.06.2026		
9000	E51WCL-1048		PL25X330		S355J2+N	1	770	330	25	49.9	49.9		12.06.2026		
9000	E51WCL-1049		PL15X170		S355J2+N	2	271	170	15	5.4	10.8		12.06.2026		
9000	E51WCL-1050		PL15X225		S355J2+N	2	271	225	15	6.3	12.5		12.06.2026		
9000	E51WCL-1053		PL10X170		S355J2+N	1	170	170	10	2.3	2.3		12.06.2026		
9000	E51WCL-1066		PL10X120		S355J2+N	4	566	120	10	5.3	21.3		12.06.2026		
9000	E51WCL-1099		PL5X149		S355J2+N	4	281	149	5	1.6	6.6		12.06.2026		

9000	E51WCL-1100		PL5X45		S355J2+N	4	271	45	5	0.5	1.9		12.06.2026		
9000	E51WCL-1143		PL25X700		S355J2+N	1	420	700	25	53.2	53.2		12.06.2026		
9000	E51WCL-1144		PL30X512		S355J2+N	1	995	512	30	93.0	93.0		12.06.2026		
9000	E51WCL-1171		PL5X194		S355J2+N	2	197	194	5	1.5	3.0		12.06.2026		
9000	E51WCP-1001		WI600-10-15X250		S355J2	1	5175	0	0	538.1	538.1		12.06.2026		
9000	E51WCP-1102		CFRHS200X200X5		S355J2H	1	5470	0	0	164.7	164.7		12.06.2026		
9000	E51WC-1066	COLUMN_WI		EXC2	RAL 7024 (Graphite Gray)	1	5790	700	1015	743.3	750.4	17.00	12.06.2026		
9000	E51WCL-1014		PL20X215		S355J2+N	1	576	215	20	18.7	18.7		12.06.2026		
9000	E51WCL-1024		PL15X210		S355J2+N	1	260	210	15	4.3	4.3		12.06.2026		
9000	E51WCL-1053		PL10X170		S355J2+N	1	170	170	10	2.3	2.3		12.06.2026		
9000	E51WCL-1143		PL25X700		S355J2+N	1	420	700	25	53.2	53.2		12.06.2026		
9000	E51WCL-1152		PL20X250		S355J2+N	1	582	250	20	22.8	22.8		12.06.2026		
9000	E51WCL-1154		PL20X99		S355J2+N	1	576	99	20	8.9	8.9		12.06.2026		
9000	E51WCL-1157		PL15X365		S355J2+N	1	683	365	15	25.9	25.9		12.06.2026		
9000	E51WCL-1171		PL5X194		S355J2+N	5	197	194	5	1.5	7.5		12.06.2026		
9000	E51WCL-1192		PL8X194		S355J2+N	1	197	194	8	2.4	2.4		12.06.2026		
9000	E51WCL-1193		PL10X91		S355J2+N	2	150	91	10	1.0	2.0		12.06.2026		
9000	E51WCL-1194		PL30X300		S355J2+N	1	576	300	30	40.7	40.7		12.06.2026		
9000	E51WCP-1012		WI600-10-10X210		S355J2	1	5175	0	0	408.1	408.1		12.06.2026		
9000	E51WCP-1080		L100*10		S355J2	1	586	0	0	8.8	8.8		12.06.2026		
9000	E51WCP-1101		CFRHS200X200X5		S355J2H	1	1690	0	0	50.9	50.9		12.06.2026		
9000	E51WCP-1135		CFRHS200X200X5		S355J2H	1	907	0	0	27.3	27.3		12.06.2026		
9000	E51WCP-1136		CFRHS200X200X5		S355J2H	1	2210	0	0	66.5	66.5		12.06.2026		
9000	E51WC-1067	COLUMN_WI		EXC2	RAL 7024 (Graphite Gray)	1	5790	1076	970	841.2	871.8	18.26	12.06.2026		
9000	E51WCL-1027		PL30X1081		S355J2+N	1	1159	1081	30	229.1	229.1		12.06.2026		
9000	E51WCL-1041		PL15X250		S355J2+N	2	273	250	15	7.4	14.9		12.06.2026		
9000	E51WCL-1042		PL15X273		S355J2+N	2	300	273	15	9.0	18.1		12.06.2026		
9000	E51WCL-1053		PL10X170		S355J2+N	1	170	170	10	2.3	2.3		12.06.2026		
9000	E51WCL-1142		PL20X220		S355J2+N	1	420	220	20	14.5	14.5		12.06.2026		
9000	E51WCL-1171		PL5X194		S355J2+N	2	197	194	5	1.5	3.0		12.06.2026		
9000	E51WCP-1010		WI600-10-10X210		S355J2	1	5180	0	0	408.5	408.5		12.06.2026		
9000	E51WCP-1081		L100*10		S355J2	4	278	0	0	4.2	16.8		12.06.2026		
9000	E51WCP-1102		CFRHS200X200X5		S355J2H	1	5470	0	0	164.7	164.7		12.06.2026		
9000	E51WC-1068	COLUMN_WI		EXC2	RAL 7024 (Graphite Gray)	1	5790	1075	970	841.0	871.5	18.25	12.06.2026		
9000	E51WCL-1028		PL30X1081		S355J2+N	1	1158	1081	30	228.9	228.9		12.06.2026		
9000	E51WCL-1041		PL15X250		S355J2+N	2	273	250	15	7.4	14.9		12.06.2026		
9000	E51WCL-1042		PL15X273		S355J2+N	2	300	273	15	9.0	18.1		12.06.2026		
9000	E51WCL-1053		PL10X170		S355J2+N	1	170	170	10	2.3	2.3		12.06.2026		
9000	E51WCL-1142		PL20X220		S355J2+N	1	420	220	20	14.5	14.5		12.06.2026		
9000	E51WCL-1171		PL5X194		S355J2+N	2	197	194	5	1.5	3.0		12.06.2026		
9000	E51WCP-1010		WI600-10-10X210		S355J2	1	5180	0	0	408.5	408.5		12.06.2026		
9000	E51WCP-1081		L100*10		S355J2	4	278	0	0	4.2	16.8		12.06.2026		
9000	E51WCP-1102		CFRHS200X200X5		S355J2H	1	5470	0	0	164.7	164.7		12.06.2026		

9000	E51WC-1071	COLUMN_WI		EXC2	RAL 7024 (Graphite Gray)	1	8930	604	1025	2504.5	2674.8	30.99	12.06.2026		
9000	E51WCL-1005		PL20X125		S355J2+N	2	756	125	20	14.7	29.5		12.06.2026		
9000	E51WCL-1073		PL30X125		S355J2+N	2	756	125	30	20.5	40.9		12.06.2026		
9000	E51WCL-1107		PL8X176		S355J2+N	1	186	176	8	2.1	2.1		12.06.2026		
9000	E51WCL-1108		PL12X115		S355J2+N	1	134	115	12	1.2	1.2		12.06.2026		
9000	E51WCL-1136		PL40X450		S355J2+N	2	550	450	40	77.7	155.4		12.06.2026		
9000	E51WCL-1160		PL8X297		S355J2+N	1	228	297	8	4.2	4.2		12.06.2026		
9000	E51WCL-1161		PL8X297		S355J2+N	1	281	297	8	5.2	5.2		12.06.2026		
9000	E51WCL-1169		PL5X144		S355J2+N	2	97	144	5	0.5	1.1		12.06.2026		
9000	E51WCL-1187		PL16X125		S355J2+N	4	228	125	16	3.5	13.9		12.06.2026		
9000	E51WCL-1191		PL10X107		S355J2+N	4	205	107	10	1.7	6.8		12.06.2026		
9000	E51WCP-1038		T140-15-15-150		S355J2+N	1	1450	0	0	47.5	47.5		12.06.2026		
9000	E51WCP-1045		CFRHS200X120X5		S355J2H	1	85	0	0	2.0	2.0		12.06.2026		
9000	E51WCP-1097		CFRHS150X100X3		S355J2H	1	7110	0	0	80.4	80.4		12.06.2026		
9000	E51WCP-1110		HEA340		S355J2	2	247	0	0	25.9	51.8		12.06.2026		
9000	E51WCP-1119		UNP200		S355J2	1	250	0	0	6.3	6.3		12.06.2026		
9000	E51WCP-1130		UNP180		S355J2	1	250	0	0	5.5	5.5		12.06.2026		
9000	E51WCP-1141		HEA240		S355J2	2	255	0	0	15.4	30.8		12.06.2026		
9000	E51WCP-1142		WI800-30-20X300		S355J2	1	7922	0	0	2190.0	2190.0		12.06.2026		
9000	E51WC-1072	COLUMN_WI		EXC2	RAL 7024 (Graphite Gray)	1	9030	745	1025	2681.7	2826.1	32.83	12.06.2026		
9000	E51WCL-1005		PL20X125		S355J2+N	2	756	125	20	14.7	29.5		12.06.2026		
9000	E51WCL-1073		PL30X125		S355J2+N	2	756	125	30	20.5	40.9		12.06.2026		
9000	E51WCL-1107		PL8X176		S355J2+N	1	186	176	8	2.1	2.1		12.06.2026		
9000	E51WCL-1108		PL12X115		S355J2+N	1	134	115	12	1.2	1.2		12.06.2026		
9000	E51WCL-1136		PL40X450		S355J2+N	2	550	450	40	77.7	155.4		12.06.2026		
9000	E51WCL-1160		PL8X297		S355J2+N	1	228	297	8	4.2	4.2		12.06.2026		
9000	E51WCL-1161		PL8X297		S355J2+N	1	281	297	8	5.2	5.2		12.06.2026		
9000	E51WCL-1169		PL5X144		S355J2+N	2	97	144	5	0.5	1.1		12.06.2026		
9000	E51WCL-1182		PL15X138		S355J2+N	1	296	138	15	4.8	4.8		12.06.2026		
9000	E51WCL-1183		PL15X296		S355J2+N	1	325	296	15	11.3	11.3		12.06.2026		
9000	E51WCL-1187		PL16X125		S355J2+N	4	228	125	16	3.5	13.9		12.06.2026		
9000	E51WCL-1191		PL10X107		S355J2+N	4	205	107	10	1.7	6.8		12.06.2026		
9000	E51WCP-1015		WI800-30-20X300		S355J2	1	8385	0	0	2317.9	2317.9		12.06.2026		
9000	E51WCP-1037		T140-15-15-150		S355J2+N	1	1050	0	0	34.4	34.4		12.06.2026		
9000	E51WCP-1045		CFRHS200X120X5		S355J2H	1	85	0	0	2.0	2.0		12.06.2026		
9000	E51WCP-1103		CFRHS150X100X3		S355J2H	1	7610	0	0	86.1	86.1		12.06.2026		
9000	E51WCP-1109		HEA340		S355J2	1	388	0	0	40.6	40.6		12.06.2026		
9000	E51WCP-1110		HEA340		S355J2	1	247	0	0	25.9	25.9		12.06.2026		
9000	E51WCP-1125		UNP200		S355J2	1	250	0	0	6.3	6.3		12.06.2026		
9000	E51WCP-1128		UNP180		S355J2	1	250	0	0	5.5	5.5		12.06.2026		
9000	E51WCP-1141		HEA240		S355J2	2	255	0	0	15.4	30.8		12.06.2026		
9000	E51WC-1074	COLUMN_WI		EXC2	RAL 7024 (Graphite Gray)	1	11910	1220	1320	8151.7	8696.0	70.36	12.06.2026		
9000	E51WCL-1001		PL70X1220		S355J2+N	1	1320	1220	70	884.9	884.9		12.06.2026		
9000	E51WCL-1056		PL35X230		S355J2+N	4	1300	230	35	76.9	307.5		12.06.2026		
9000	E51WCL-1104		PL25X300		S355J2+N	1	505	300	25	29.7	29.7		12.06.2026		

9000	E51WCL-1105		PL15X282		S355J2+N	1	400	282	15	12.1	12.1		12.06.2026		
9000	E51WCL-1116		PL15X232		S355J2+N	2	283	232	15	7.7	15.4		12.06.2026		
9000	E51WCL-1117		PL30X233		S355J2+N	2	726	233	30	37.6	75.3		12.06.2026		
9000	E51WCL-1119		PL40X393		S355J2+N	2	726	393	40	84.3	168.5		12.06.2026		
9000	E51WCL-1121		PL30X582		S355J2+N	1	1123	582	30	131.1	131.1		12.06.2026		
9000	E51WCL-1122		PL35X283		S355J2+N	1	726	283	35	53.3	53.3		12.06.2026		
9000	E51WCL-1123		PL20X349		S355J2+N	4	478	349	20	25.4	101.4		12.06.2026		
9000	E51WCL-1148		PL12X497		S355J2+N	2	403	497	12	18.8	37.6		12.06.2026		
9000	E51WCL-1149		PL20X393		S355J2+N	2	726	393	20	44.2	88.5		12.06.2026		
9000	E51WCL-1150		PL30X460		S355J2+N	1	1141	460	30	121.3	121.3		12.06.2026		
9000	E51WCL-1151		PL30X480		S355J2+N	1	1297	480	30	133.9	133.9		12.06.2026		
9000	E51WCL-1155		PL30X190		S355J2+N	1	200	190	30	8.9	8.9		12.06.2026		
9000	E51WCL-1163		PL5X34		S355J2+N	4	94	34	5	0.1	0.5		12.06.2026		
9000	E51WCL-1165		PL15X282		S355J2+N	1	400	282	15	13.3	13.3		12.06.2026		
9000	E51WCL-1166		PL20X283		S355J2+N	1	726	283	20	32.0	32.0		12.06.2026		
9000	E51WCL-1167		PL12X190		S355J2+N	1	390	190	12	7.0	7.0		12.06.2026		
9000	E51WCL-1168		PL12X190		S355J2+N	1	290	190	12	5.2	5.2		12.06.2026		
9000	E51WCL-1169		PL5X144		S355J2+N	2	97	144	5	0.5	1.1		12.06.2026		
9000	E51WCL-1184		PL15X262		S355J2+N	1	355	262	15	9.0	9.0		12.06.2026		
9000	E51WCL-1185		PL25X200		S355J2+N	2	220	200	25	8.1	16.2		12.06.2026		
9000	E51WCL-1191		PL10X107		S355J2+N	4	205	107	10	1.7	6.8		12.06.2026		
9000	E51WCL-1195		PL35X283		S355J2+N	1	726	283	35	53.0	53.0		12.06.2026		
9000	E51WCL-1196		PL20X283		S355J2+N	1	726	283	20	32.0	32.0		12.06.2026		
9000	E51WCL-1197		PL12X200		S355J2+N	1	250	200	12	4.6	4.6		12.06.2026		
9000	E51WCP-1026		W1350-25-35X250		S355J2+N	1	420	0	0	81.7	81.7		12.06.2026		
9000	E51WCP-1031		L100*10		S355J2	1	378	0	0	5.7	5.7		12.06.2026		
9000	E51WCP-1032		L100*10		S355J2	1	375	0	0	5.7	5.7		12.06.2026		
9000	E51WCP-1083		W1800-35-35X600		S355J2	1	11420	0	0	6106.2	6106.2		12.06.2026		
9000	E51WCP-1105		CFRHS150X100X3		S355J2H	1	6280	0	0	71.0	71.0		12.06.2026		
9000	E51WCP-1118		CFRHS100X40X3		S355J2H	2	1065	0	0	6.5	13.1		12.06.2026		
9000	E51WCP-1132		L100*12		S355J2	1	782	0	0	13.9	13.9		12.06.2026		
9000	E51WCP-1140		HEA240		S355J2	2	403	0	0	24.3	48.6		12.06.2026		
9000	E51WC-1075	COLUMN_WI		EXC2	RAL 7024 (Graphite Gray)	1	11910	1220	1320	8045.3	8680.4	70.57	12.06.2026		
9000	E51WCL-1001		PL70X1220		S355J2+N	1	1320	1220	70	884.9	884.9		12.06.2026		
9000	E51WCL-1056		PL35X230		S355J2+N	4	1300	230	35	76.9	307.5		12.06.2026		
9000	E51WCL-1116		PL15X232		S355J2+N	2	283	232	15	7.7	15.4		12.06.2026		
9000	E51WCL-1117		PL30X233		S355J2+N	2	726	233	30	37.6	75.3		12.06.2026		
9000	E51WCL-1118		PL30X592		S355J2+N	1	1123	592	30	133.8	133.8		12.06.2026		
9000	E51WCL-1119		PL40X393		S355J2+N	2	726	393	40	84.3	168.5		12.06.2026		
9000	E51WCL-1122		PL35X283		S355J2+N	2	726	283	35	53.3	106.5		12.06.2026		
9000	E51WCL-1123		PL20X349		S355J2+N	4	478	349	20	25.4	101.4		12.06.2026		
9000	E51WCL-1148		PL12X497		S355J2+N	2	403	497	12	18.8	37.6		12.06.2026		
9000	E51WCL-1149		PL20X393		S355J2+N	2	726	393	20	44.2	88.5		12.06.2026		
9000	E51WCL-1150		PL30X460		S355J2+N	1	1141	460	30	121.3	121.3		12.06.2026		
9000	E51WCL-1151		PL30X480		S355J2+N	1	1297	480	30	133.9	133.9		12.06.2026		
9000	E51WCL-1155		PL30X190		S355J2+N	1	200	190	30	8.9	8.9		12.06.2026		


9000	E51WCL-1163		PL5X34		S355J2+N	4	94	34	5	0.1	0.5		12.06.2026		
9000	E51WCL-1165		PL15X282		S355J2+N	2	400	282	15	13.3	26.6		12.06.2026		
9000	E51WCL-1166		PL20X283		S355J2+N	1	726	283	20	32.0	32.0		12.06.2026		
9000	E51WCL-1167		PL12X190		S355J2+N	2	390	190	12	7.0	14.0		12.06.2026		
9000	E51WCL-1168		PL12X190		S355J2+N	2	290	190	12	5.2	10.4		12.06.2026		
9000	E51WCL-1169		PL5X144		S355J2+N	6	97	144	5	0.5	3.3		12.06.2026		
9000	E51WCL-1184		PL15X262		S355J2+N	1	355	262	15	9.0	9.0		12.06.2026		
9000	E51WCL-1186		PL25X200		S355J2+N	2	220	200	25	8.1	16.2		12.06.2026		
9000	E51WCL-1191		PL10X107		S355J2+N	4	205	107	10	1.7	6.8		12.06.2026		
9000	E51WCL-1196		PL20X283		S355J2+N	1	726	283	20	32.0	32.0		12.06.2026		
9000	E51WCL-1197		PL12X200		S355J2+N	1	250	200	12	4.6	4.6		12.06.2026		
9000	E51WCP-1002		WI800-35-35X600		S355J2	1	11420	0	0	6106.2	6106.2		12.06.2026		
9000	E51WCP-1026		WI350-25-35X250		S355J2+N	1	420	0	0	81.7	81.7		12.06.2026		
9000	E51WCP-1093		L100*10		S355J2	1	378	0	0	5.7	5.7		12.06.2026		
9000	E51WCP-1094		L100*10		S355J2	1	375	0	0	5.7	5.7		12.06.2026		
9000	E51WCP-1100		CFRHS150X100X3		S355J2H	1	5380	0	0	60.9	60.9		12.06.2026		
9000	E51WCP-1115		CFRHS150X100X3		S355J2H	2	870	0	0	9.8	19.7		12.06.2026		
9000	E51WCP-1118		CFRHS100X40X3		S355J2H	2	1065	0	0	6.5	13.1		12.06.2026		
9000	E51WCP-1140		HEA240		S355J2	2	403	0	0	24.3	48.6		12.06.2026		
9000	E51WC-1076	COLUMN_WI		EXC2	RAL 7024 (Graphite Gray)	1	11910	1220	1320	8030.6	8671.4	70.40	12.06.2026		
9000	E51WCL-1001		PL70X1220		S355J2+N	1	1320	1220	70	884.9	884.9		12.06.2026		
9000	E51WCL-1056		PL35X230		S355J2+N	4	1300	230	35	76.9	307.5		12.06.2026		
9000	E51WCL-1116		PL15X232		S355J2+N	2	283	232	15	7.7	15.4		12.06.2026		
9000	E51WCL-1117		PL30X233		S355J2+N	2	726	233	30	37.6	75.3		12.06.2026		
9000	E51WCL-1118		PL30X592		S355J2+N	1	1123	592	30	133.8	133.8		12.06.2026		
9000	E51WCL-1119		PL40X393		S355J2+N	2	726	393	40	84.3	168.5		12.06.2026		
9000	E51WCL-1122		PL35X283		S355J2+N	2	726	283	35	53.3	106.5		12.06.2026		
9000	E51WCL-1123		PL20X349		S355J2+N	4	478	349	20	25.4	101.4		12.06.2026		
9000	E51WCL-1148		PL12X497		S355J2+N	2	403	497	12	18.8	37.6		12.06.2026		
9000	E51WCL-1149		PL20X393		S355J2+N	2	726	393	20	44.2	88.5		12.06.2026		
9000	E51WCL-1150		PL30X460		S355J2+N	1	1141	460	30	121.3	121.3		12.06.2026		
9000	E51WCL-1151		PL30X480		S355J2+N	1	1297	480	30	133.9	133.9		12.06.2026		
9000	E51WCL-1155		PL30X190		S355J2+N	1	200	190	30	8.9	8.9		12.06.2026		
9000	E51WCL-1163		PL5X34		S355J2+N	4	94	34	5	0.1	0.5		12.06.2026		
9000	E51WCL-1165		PL15X282		S355J2+N	2	400	282	15	13.3	26.6		12.06.2026		
9000	E51WCL-1166		PL20X283		S355J2+N	1	726	283	20	32.0	32.0		12.06.2026		
9000	E51WCL-1167		PL12X190		S355J2+N	2	390	190	12	7.0	14.0		12.06.2026		
9000	E51WCL-1168		PL12X190		S355J2+N	2	290	190	12	5.2	10.4		12.06.2026		
9000	E51WCL-1169		PL5X144		S355J2+N	6	97	144	5	0.5	3.3		12.06.2026		
9000	E51WCL-1186		PL25X200		S355J2+N	2	220	200	25	8.1	16.2		12.06.2026		
9000	E51WCL-1191		PL10X107		S355J2+N	4	205	107	10	1.7	6.8		12.06.2026		
9000	E51WCL-1196		PL20X283		S355J2+N	1	726	283	20	32.0	32.0		12.06.2026		
9000	E51WCL-1197		PL12X200		S355J2+N	1	250	200	12	4.6	4.6		12.06.2026		
9000	E51WCP-1026		WI350-25-35X250		S355J2+N	1	420	0	0	81.7	81.7		12.06.2026		
9000	E51WCP-1082		WI800-35-35X600		S355J2	1	11420	0	0	6106.2	6106.2		12.06.2026		
9000	E51WCP-1093		L100*10		S355J2	2	378	0	0	5.7	11.4		12.06.2026		

9000	E51WCP-1100		CFRHS150X100X3		S355J2H	1	5380	0	0	60.9	60.9		12.06.2026		
9000	E51WCP-1115		CFRHS150X100X3		S355J2H	2	870	0	0	9.8	19.7		12.06.2026		
9000	E51WCP-1118		CFRHS100X40X3		S355J2H	2	1065	0	0	6.5	13.1		12.06.2026		
9000	E51WCP-1140		HEA240		S355J2	2	403	0	0	24.3	48.6		12.06.2026		
9000	E51WC-1077	COLUMN_WI		EXC2	RAL 7024 (Graphite Gray)	1	5790	700	1028	740.9	746.4	16.98	12.06.2026		
9000	E51WCL-1011		PL20X170		S355J2+N	1	576	170	20	15.1	15.1		12.06.2026		
9000	E51WCL-1052		PL10X228		S355J2+N	1	284	228	10	3.8	3.8		12.06.2026		
9000	E51WCL-1053		PL10X170		S355J2+N	1	170	170	10	2.3	2.3		12.06.2026		
9000	E51WCL-1143		PL25X700		S355J2+N	1	420	700	25	53.2	53.2		12.06.2026		
9000	E51WCL-1152		PL20X250		S355J2+N	1	582	250	20	22.8	22.8		12.06.2026		
9000	E51WCL-1154		PL20X99		S355J2+N	1	576	99	20	8.9	8.9		12.06.2026		
9000	E51WCL-1157		PL15X365		S355J2+N	1	683	365	15	25.9	25.9		12.06.2026		
9000	E51WCL-1171		PL5X194		S355J2+N	4	197	194	5	1.5	6.0		12.06.2026		
9000	E51WCL-1190		PL5X194		S355J2+N	1	194	194	5	1.5	1.5		12.06.2026		
9000	E51WCL-1192		PL8X194		S355J2+N	1	197	194	8	2.4	2.4		12.06.2026		
9000	E51WCL-1193		PL10X91		S355J2+N	2	150	91	10	1.0	2.0		12.06.2026		
9000	E51WCL-1194		PL30X300		S355J2+N	1	576	300	30	40.7	40.7		12.06.2026		
9000	E51WCP-1014		WI600-10-10X210		S355J2	1	5175	0	0	408.1	408.1		12.06.2026		
9000	E51WCP-1080		L100*10		S355J2	1	586	0	0	8.8	8.8		12.06.2026		
9000	E51WCP-1101		CFRHS200X200X5		S355J2H	1	1690	0	0	50.9	50.9		12.06.2026		
9000	E51WCP-1135		CFRHS200X200X5		S355J2H	1	907	0	0	27.3	27.3		12.06.2026		
9000	E51WCP-1136		CFRHS200X200X5		S355J2H	1	2210	0	0	66.5	66.5		12.06.2026		
9000	E51WC-1078	COLUMN_WI		EXC2	RAL 7024 (Graphite Gray)	1	13813	315	1028	1358.4	1378.0	35.20	12.06.2026		
9000	E51WCL-1017		PL12X170		S355J2+N	1	576	170	12	9.1	9.1		12.06.2026		
9000	E51WCL-1053		PL10X170		S355J2+N	1	170	170	10	2.3	2.3		12.06.2026		
9000	E51WCL-1054		PL10X115		S355J2+N	1	700	115	10	6.3	6.3		12.06.2026		
9000	E51WCL-1067		PL10X90		S355J2+N	2	576	90	10	4.1	8.1		12.06.2026		
9000	E51WCL-1115		PL10X228		S355J2+N	1	285	228	10	3.9	3.9		12.06.2026		
9000	E51WCL-1124		PL10X230		S355J2+N	1	621	230	10	11.2	11.2		12.06.2026		
9000	E51WCL-1127		PL25X210		S355J2+N	1	593	210	25	24.4	24.4		12.06.2026		
9000	E51WCL-1147		PL15X95		S355J2+N	4	400	95	15	4.5	17.8		12.06.2026		
9000	E51WCL-1170		PL5X94		S355J2+N	4	197	94	5	0.7	2.9		12.06.2026		
9000	E51WCL-1172		PL8X150		S355J2+N	1	142	150	8	1.3	1.3		12.06.2026		
9000	E51WCP-1005		WI600-10-10X200		S355J2	1	12747	0	0	985.3	985.3		12.06.2026		
9000	E51WCP-1080		L100*10		S355J2	1	586	0	0	8.8	8.8		12.06.2026		
9000	E51WCP-1095		CFRHS200X100X5		S355J2H	1	4170	0	0	92.8	92.8		12.06.2026		
9000	E51WCP-1099		CFRHS200X100X5		S355J2H	1	8890	0	0	197.9	197.9		12.06.2026		
9000	E51WCP-1129		HEA160		S355J2	1	192	0	0	5.8	5.8		12.06.2026		
9000	E51WC-1079	COLUMN_WI		EXC2	RAL 7024 (Graphite Gray)	1	7620	1225	1028	1213.5	1363.4	26.98	12.06.2026		
9000	E51WCL-1054		PL10X115		S355J2+N	1	700	115	10	6.3	6.3		12.06.2026		
9000	E51WCL-1128		PL10X220		S355J2+N	1	621	220	10	10.7	10.7		12.06.2026		
9000	E51WCL-1131		PL40X430		S355J2+N	2	550	430	40	74.3	148.5		12.06.2026		
9000	E51WCL-1132		PL30X1145		S355J2+N	1	1237	1145	30	285.1	285.1		12.06.2026		
9000	E51WCL-1134		PL16X134		S355J2+N	4	1141	134	16	19.2	76.7		12.06.2026		




9000	E51WCL-1137		PL15X297		S355J2+N	1	294	297	15	10.2	10.2		12.06.2026		
9000	E51WCL-1138		PL12X298		S355J2+N	1	294	298	12	8.2	8.2		12.06.2026		
9000	E51WCL-1164		PL10X228		S355J2+N	1	261	228	10	3.4	3.4		12.06.2026		
9000	E51WCL-1171		PL5X194		S355J2+N	8	197	194	5	1.5	12.0		12.06.2026		
9000	E51WCL-1173		PL8X110		S355J2+N	1	230	110	8	1.6	1.6		12.06.2026		
9000	E51WCL-1175		PL15X135		S355J2+N	2	294	135	15	4.7	9.3		12.06.2026		
9000	E51WCL-1188		PL10X135		S355J2+N	2	294	135	10	3.0	6.1		12.06.2026		
9000	E51WCP-1089		WI600-10-10X210		S355J2	1	7610	0	0	600.1	600.1		12.06.2026		
9000	E51WCP-1098		CFRHS200X200X5		S355J2H	1	2910	0	0	87.6	87.6		12.06.2026		
9000	E51WCP-1120		IPE240		S355J2	1	192	0	0	5.9	5.9		12.06.2026		
9000	E51WCP-1122		CFRHS200X200X5		S355J2H	1	1126	0	0	33.9	33.9		12.06.2026		
9000	E51WCP-1137		CFRHS200X200X5		S355J2H	1	910	0	0	27.4	27.4		12.06.2026		
9000	E51WCP-1138		CFRHS200X200X5		S355J2H	1	1010	0	0	30.4	30.4		12.06.2026		
9000	E51WC-1080	COLUMN_WI		EXC2	RAL 7024 (Graphite Gray)	1	7620	883	1028	1260.7	1374.4	26.71	12.06.2026		
9000	E51WCL-1054		PL10X115		S355J2+N	1	700	115	10	6.3	6.3		12.06.2026		
9000	E51WCL-1128		PL10X220		S355J2+N	1	621	220	10	10.7	10.7		12.06.2026		
9000	E51WCL-1131		PL40X430		S355J2+N	2	550	430	40	74.3	148.5		12.06.2026		
9000	E51WCL-1139		PL25X803		S355J2+N	1	797	803	25	116.9	116.9		12.06.2026		
9000	E51WCL-1140		PL16X135		S355J2+N	2	801	135	16	13.5	27.1		12.06.2026		
9000	E51WCL-1141		PL12X267		S355J2+N	1	294	267	12	7.4	7.4		12.06.2026		
9000	E51WCL-1141		PL12X268		S355J2+N	1	294	268	12	7.4	7.4		12.06.2026		
9000	E51WCL-1164		PL10X228		S355J2+N	1	261	228	10	3.4	3.4		12.06.2026		
9000	E51WCL-1171		PL5X194		S355J2+N	4	197	194	5	1.5	6.0		12.06.2026		
9000	E51WCL-1173		PL8X110		S355J2+N	1	230	110	8	1.6	1.6		12.06.2026		
9000	E51WCL-1175		PL15X135		S355J2+N	2	294	135	15	4.7	9.3		12.06.2026		
9000	E51WCL-1188		PL10X135		S355J2+N	2	294	135	10	3.0	6.1		12.06.2026		
9000	E51WCL-1198		PL16X137		S355J2+N	2	801	137	16	13.7	27.4		12.06.2026		
9000	E51WCP-1091		WI600-10-15X250		S355J2	1	7610	0	0	791.3	791.3		12.06.2026		
9000	E51WCP-1098		CFRHS200X200X5		S355J2H	1	2910	0	0	87.6	87.6		12.06.2026		
9000	E51WCP-1120		IPE240		S355J2	1	192	0	0	5.9	5.9		12.06.2026		
9000	E51WCP-1121		CFRHS200X200X5		S355J2H	1	3706	0	0	111.6	111.6		12.06.2026		
9000	E51WC-1081	COLUMN_WI		EXC2	RAL 7024 (Graphite Gray)	1	7620	1225	1028	1213.5	1363.4	26.98	12.06.2026		
9000	E51WCL-1054		PL10X115		S355J2+N	1	700	115	10	6.3	6.3		12.06.2026		
9000	E51WCL-1128		PL10X220		S355J2+N	1	621	220	10	10.7	10.7		12.06.2026		
9000	E51WCL-1131		PL40X430		S355J2+N	2	550	430	40	74.3	148.5		12.06.2026		
9000	E51WCL-1132		PL30X1145		S355J2+N	1	1237	1145	30	285.1	285.1		12.06.2026		
9000	E51WCL-1134		PL16X134		S355J2+N	4	1141	134	16	19.2	76.7		12.06.2026		
9000	E51WCL-1137		PL15X297		S355J2+N	1	294	297	15	10.2	10.2		12.06.2026		
9000	E51WCL-1138		PL12X298		S355J2+N	1	294	298	12	8.2	8.2		12.06.2026		
9000	E51WCL-1164		PL10X228		S355J2+N	1	261	228	10	3.4	3.4		12.06.2026		
9000	E51WCL-1171		PL5X194		S355J2+N	8	197	194	5	1.5	12.0		12.06.2026		
9000	E51WCL-1173		PL8X110		S355J2+N	1	230	110	8	1.6	1.6		12.06.2026		
9000	E51WCL-1175		PL15X135		S355J2+N	2	294	135	15	4.7	9.3		12.06.2026		
9000	E51WCL-1188		PL10X135		S355J2+N	2	294	135	10	3.0	6.1		12.06.2026		
9000	E51WCP-1090		WI600-10-10X210		S355J2	1	7610	0	0	600.1	600.1		12.06.2026		

9000	E51WCP-1098		CFRHS200X200X5		S355J2H	1	2910	0	0	87.6	87.6		12.06.2026		
9000	E51WCP-1120		IPE240		S355J2	1	192	0	0	5.9	5.9		12.06.2026		
9000	E51WCP-1122		CFRHS200X200X5		S355J2H	1	1126	0	0	33.9	33.9		12.06.2026		
9000	E51WCP-1137		CFRHS200X200X5		S355J2H	1	910	0	0	27.4	27.4		12.06.2026		
9000	E51WCP-1138		CFRHS200X200X5		S355J2H	1	1010	0	0	30.4	30.4		12.06.2026		
9000	E51WC-1082	COLUMN_WI		EXC2	RAL 7024 (Graphite Gray)	1	8083	1225	915	1247.6	1392.9	27.74	12.06.2026		
9000	E51WCL-1054		PL10X115		S355J2+N	1	700	115	10	6.3	6.3		12.06.2026		
9000	E51WCL-1128		PL10X220		S355J2+N	1	621	220	10	10.7	10.7		12.06.2026		
9000	E51WCL-1130		PL30X1147		S355J2+N	1	1278	1147	30	293.8	293.8		12.06.2026		
9000	E51WCL-1131		PL40X430		S355J2+N	2	550	430	40	74.3	148.5		12.06.2026		
9000	E51WCL-1134		PL16X134		S355J2+N	4	1141	134	16	19.2	76.7		12.06.2026		
9000	E51WCL-1171		PL5X194		S355J2+N	8	197	194	5	1.5	12.0		12.06.2026		
9000	E51WCL-1173		PL8X110		S355J2+N	1	230	110	8	1.6	1.6		12.06.2026		
9000	E51WCL-1188		PL10X135		S355J2+N	2	294	135	10	3.0	6.1		12.06.2026		
9000	E51WCP-1024		WI600-10-10X210		S355J2	1	8072	0	0	636.6	636.6		12.06.2026		
9000	E51WCP-1098		CFRHS200X200X5		S355J2H	1	2910	0	0	87.6	87.6		12.06.2026		
9000	E51WCP-1120		IPE240		S355J2	1	192	0	0	5.9	5.9		12.06.2026		
9000	E51WCP-1123		CFRHS200X200X5		S355J2H	1	1635	0	0	49.2	49.2		12.06.2026		
9000	E51WCP-1137		CFRHS200X200X5		S355J2H	1	910	0	0	27.4	27.4		12.06.2026		
9000	E51WCP-1138		CFRHS200X200X5		S355J2H	1	1010	0	0	30.4	30.4		12.06.2026		
9000	E51WC-1083	COLUMN_WI		EXC2	RAL 7024 (Graphite Gray)	1	8083	883	915	1287.7	1410.1	27.50	12.06.2026		
9000	E51WCL-1054		PL10X115		S355J2+N	1	700	115	10	6.3	6.3		12.06.2026		
9000	E51WCL-1128		PL10X220		S355J2+N	1	621	220	10	10.7	10.7		12.06.2026		
9000	E51WCL-1131		PL40X430		S355J2+N	2	550	430	40	74.3	148.5		12.06.2026		
9000	E51WCL-1139		PL25X803		S355J2+N	1	797	803	25	116.9	116.9		12.06.2026		
9000	E51WCL-1140		PL16X135		S355J2+N	4	801	135	16	13.5	54.2		12.06.2026		
9000	E51WCL-1171		PL5X194		S355J2+N	4	197	194	5	1.5	6.0		12.06.2026		
9000	E51WCL-1173		PL8X110		S355J2+N	1	230	110	8	1.6	1.6		12.06.2026		
9000	E51WCL-1188		PL10X135		S355J2+N	2	294	135	10	3.0	6.1		12.06.2026		
9000	E51WCP-1025		WI600-10-15X250		S355J2	1	8072	0	0	839.4	839.4		12.06.2026		
9000	E51WCP-1098		CFRHS200X200X5		S355J2H	1	2910	0	0	87.6	87.6		12.06.2026		
9000	E51WCP-1120		IPE240		S355J2	1	192	0	0	5.9	5.9		12.06.2026		
9000	E51WCP-1124		CFRHS200X200X5		S355J2H	1	4215	0	0	126.9	126.9		12.06.2026		
9000	E51WC-1084	COLUMN_WI		EXC2	RAL 7024 (Graphite Gray)	1	8083	836	915	1256.3	1357.8	27.30	12.06.2026		
9000	E51WCL-1054		PL10X115		S355J2+N	1	700	115	10	6.3	6.3		12.06.2026		
9000	E51WCL-1128		PL10X220		S355J2+N	1	621	220	10	10.7	10.7		12.06.2026		
9000	E51WCL-1136		PL40X450		S355J2+N	2	550	450	40	77.7	155.4		12.06.2026		
9000	E51WCL-1171		PL5X194		S355J2+N	4	197	194	5	1.5	6.0		12.06.2026		
9000	E51WCL-1173		PL8X110		S355J2+N	1	230	110	8	1.6	1.6		12.06.2026		
9000	E51WCL-1181		PL15X296		S355J2+N	2	325	296	15	11.3	22.6		12.06.2026		
9000	E51WCL-1182		PL15X138		S355J2+N	2	296	138	15	4.8	9.5		12.06.2026		
9000	E51WCL-1189		PL10X145		S355J2+N	2	296	145	10	3.3	6.6		12.06.2026		
9000	E51WCP-1006		WI600-10-15X250		S355J2	1	8072	0	0	839.4	839.4		12.06.2026		
9000	E51WCP-1098		CFRHS200X200X5		S355J2H	1	2910	0	0	87.6	87.6		12.06.2026		

9000	E51WCP-1108		HEA340		S355J2	1	756	0	0	79.3	79.3		12.06.2026		
9000	E51WCP-1120		IPE240		S355J2	1	192	0	0	5.9	5.9		12.06.2026		
9000	E51WCP-1124		CFRHS200X200X5		S355J2H	1	4215	0	0	126.9	126.9		12.06.2026		
9000	E51WC-1085	COLUMN_WI		EXC2	RAL 7024 (Graphite Gray)	1	8083	836	915	1256.3	1357.8	27.30	12.06.2026		
9000	E51WCL-1054		PL10X115		S355J2+N	1	700	115	10	6.3	6.3		12.06.2026		
9000	E51WCL-1128		PL10X220		S355J2+N	1	621	220	10	10.7	10.7		12.06.2026		
9000	E51WCL-1136		PL40X450		S355J2+N	2	550	450	40	77.7	155.4		12.06.2026		
9000	E51WCL-1171		PL5X194		S355J2+N	4	197	194	5	1.5	6.0		12.06.2026		
9000	E51WCL-1173		PL8X110		S355J2+N	1	230	110	8	1.6	1.6		12.06.2026		
9000	E51WCL-1181		PL15X296		S355J2+N	2	325	296	15	11.3	22.6		12.06.2026		
9000	E51WCL-1182		PL15X138		S355J2+N	2	296	138	15	4.8	9.5		12.06.2026		
9000	E51WCL-1189		PL10X145		S355J2+N	2	296	145	10	3.3	6.6		12.06.2026		
9000	E51WCP-1006		WI600-10-15X250		S355J2	1	8072	0	0	839.4	839.4		12.06.2026		
9000	E51WCP-1098		CFRHS200X200X5		S355J2H	1	2910	0	0	87.6	87.6		12.06.2026		
9000	E51WCP-1108		HEA340		S355J2	1	756	0	0	79.3	79.3		12.06.2026		
9000	E51WCP-1120		IPE240		S355J2	1	192	0	0	5.9	5.9		12.06.2026		
9000	E51WCP-1124		CFRHS200X200X5		S355J2H	1	4215	0	0	126.9	126.9		12.06.2026		

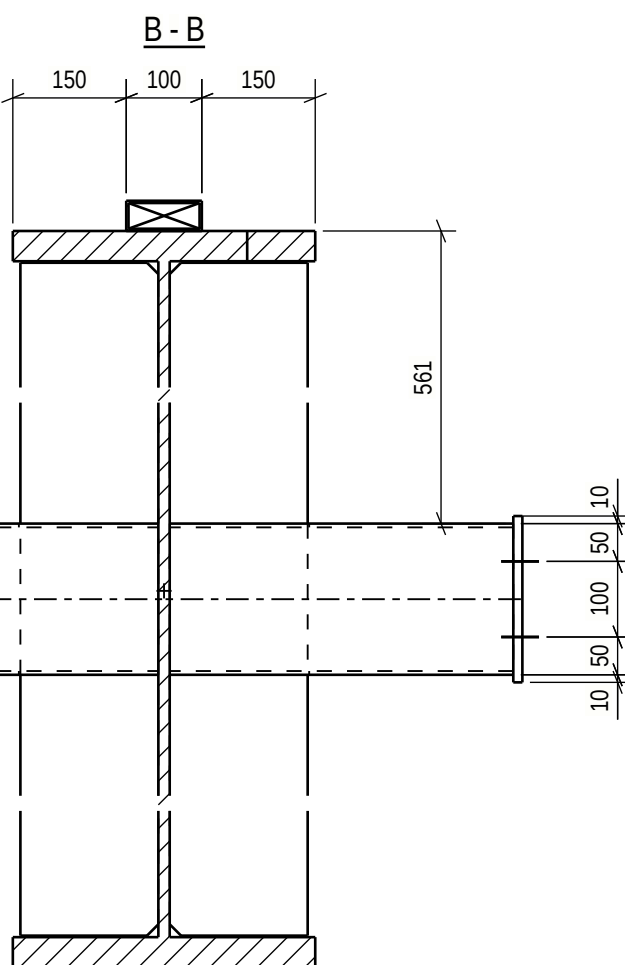


PART LIST FOR ASSEMBLY E51W-1003, MANUFACTURING AMOUNT 2 PIECES						
PART	PROFILE	MATERIAL	LENGTH [mm]	AREA [m ²]	WEIGHT [kg]	PCS
E51WL-1003	PL15X359	S355J2+N	892	0.38	20.2	1
E51WL-1017	PL10X120	S355J2+N	165	0.05	1.6	1
E51WL-1019	PL30X300	S355J2+N	1280	1.73	90.4	2
E51WP-1002	W1000-15-30X400	S355J2	7824	27.98	2346.4	1
E51WP-1007	L100*10	S355J2	7510	5.86	113.2	2
E51WP-1028	L100*10	S355J2	1190	0.93	17.9	2
TOTAL:				36.91	2811.3	

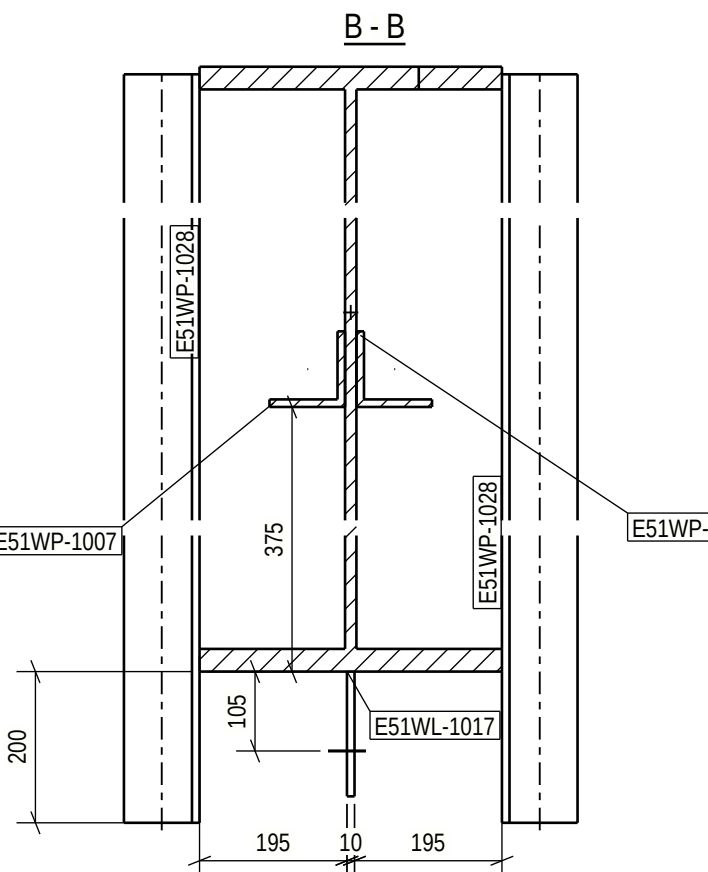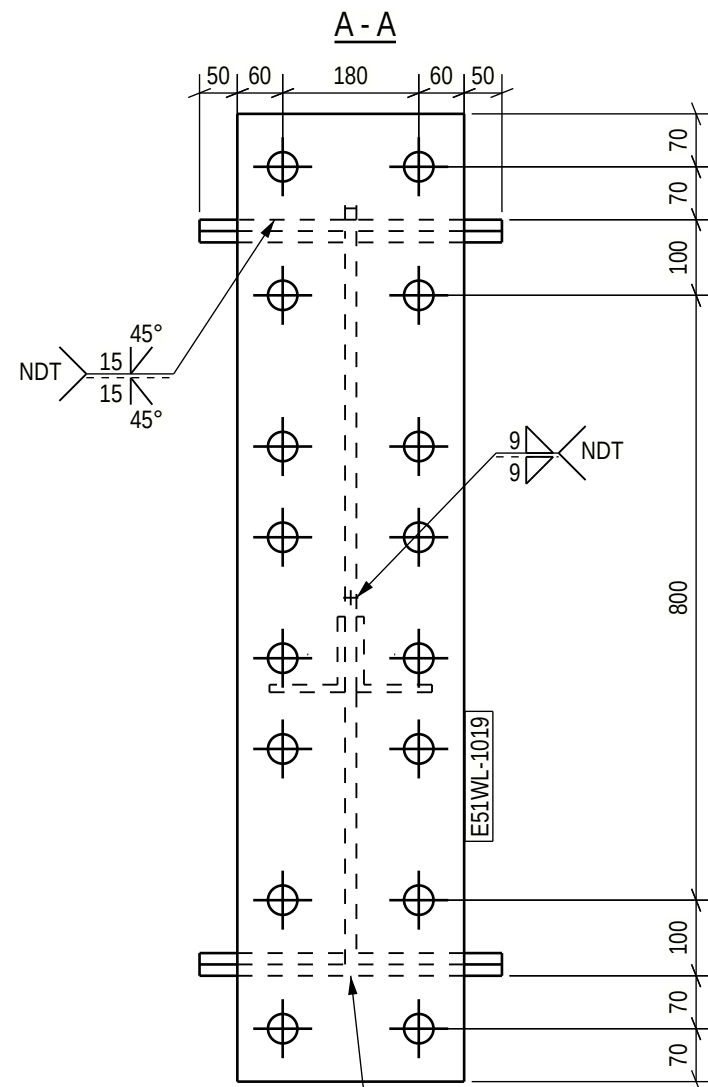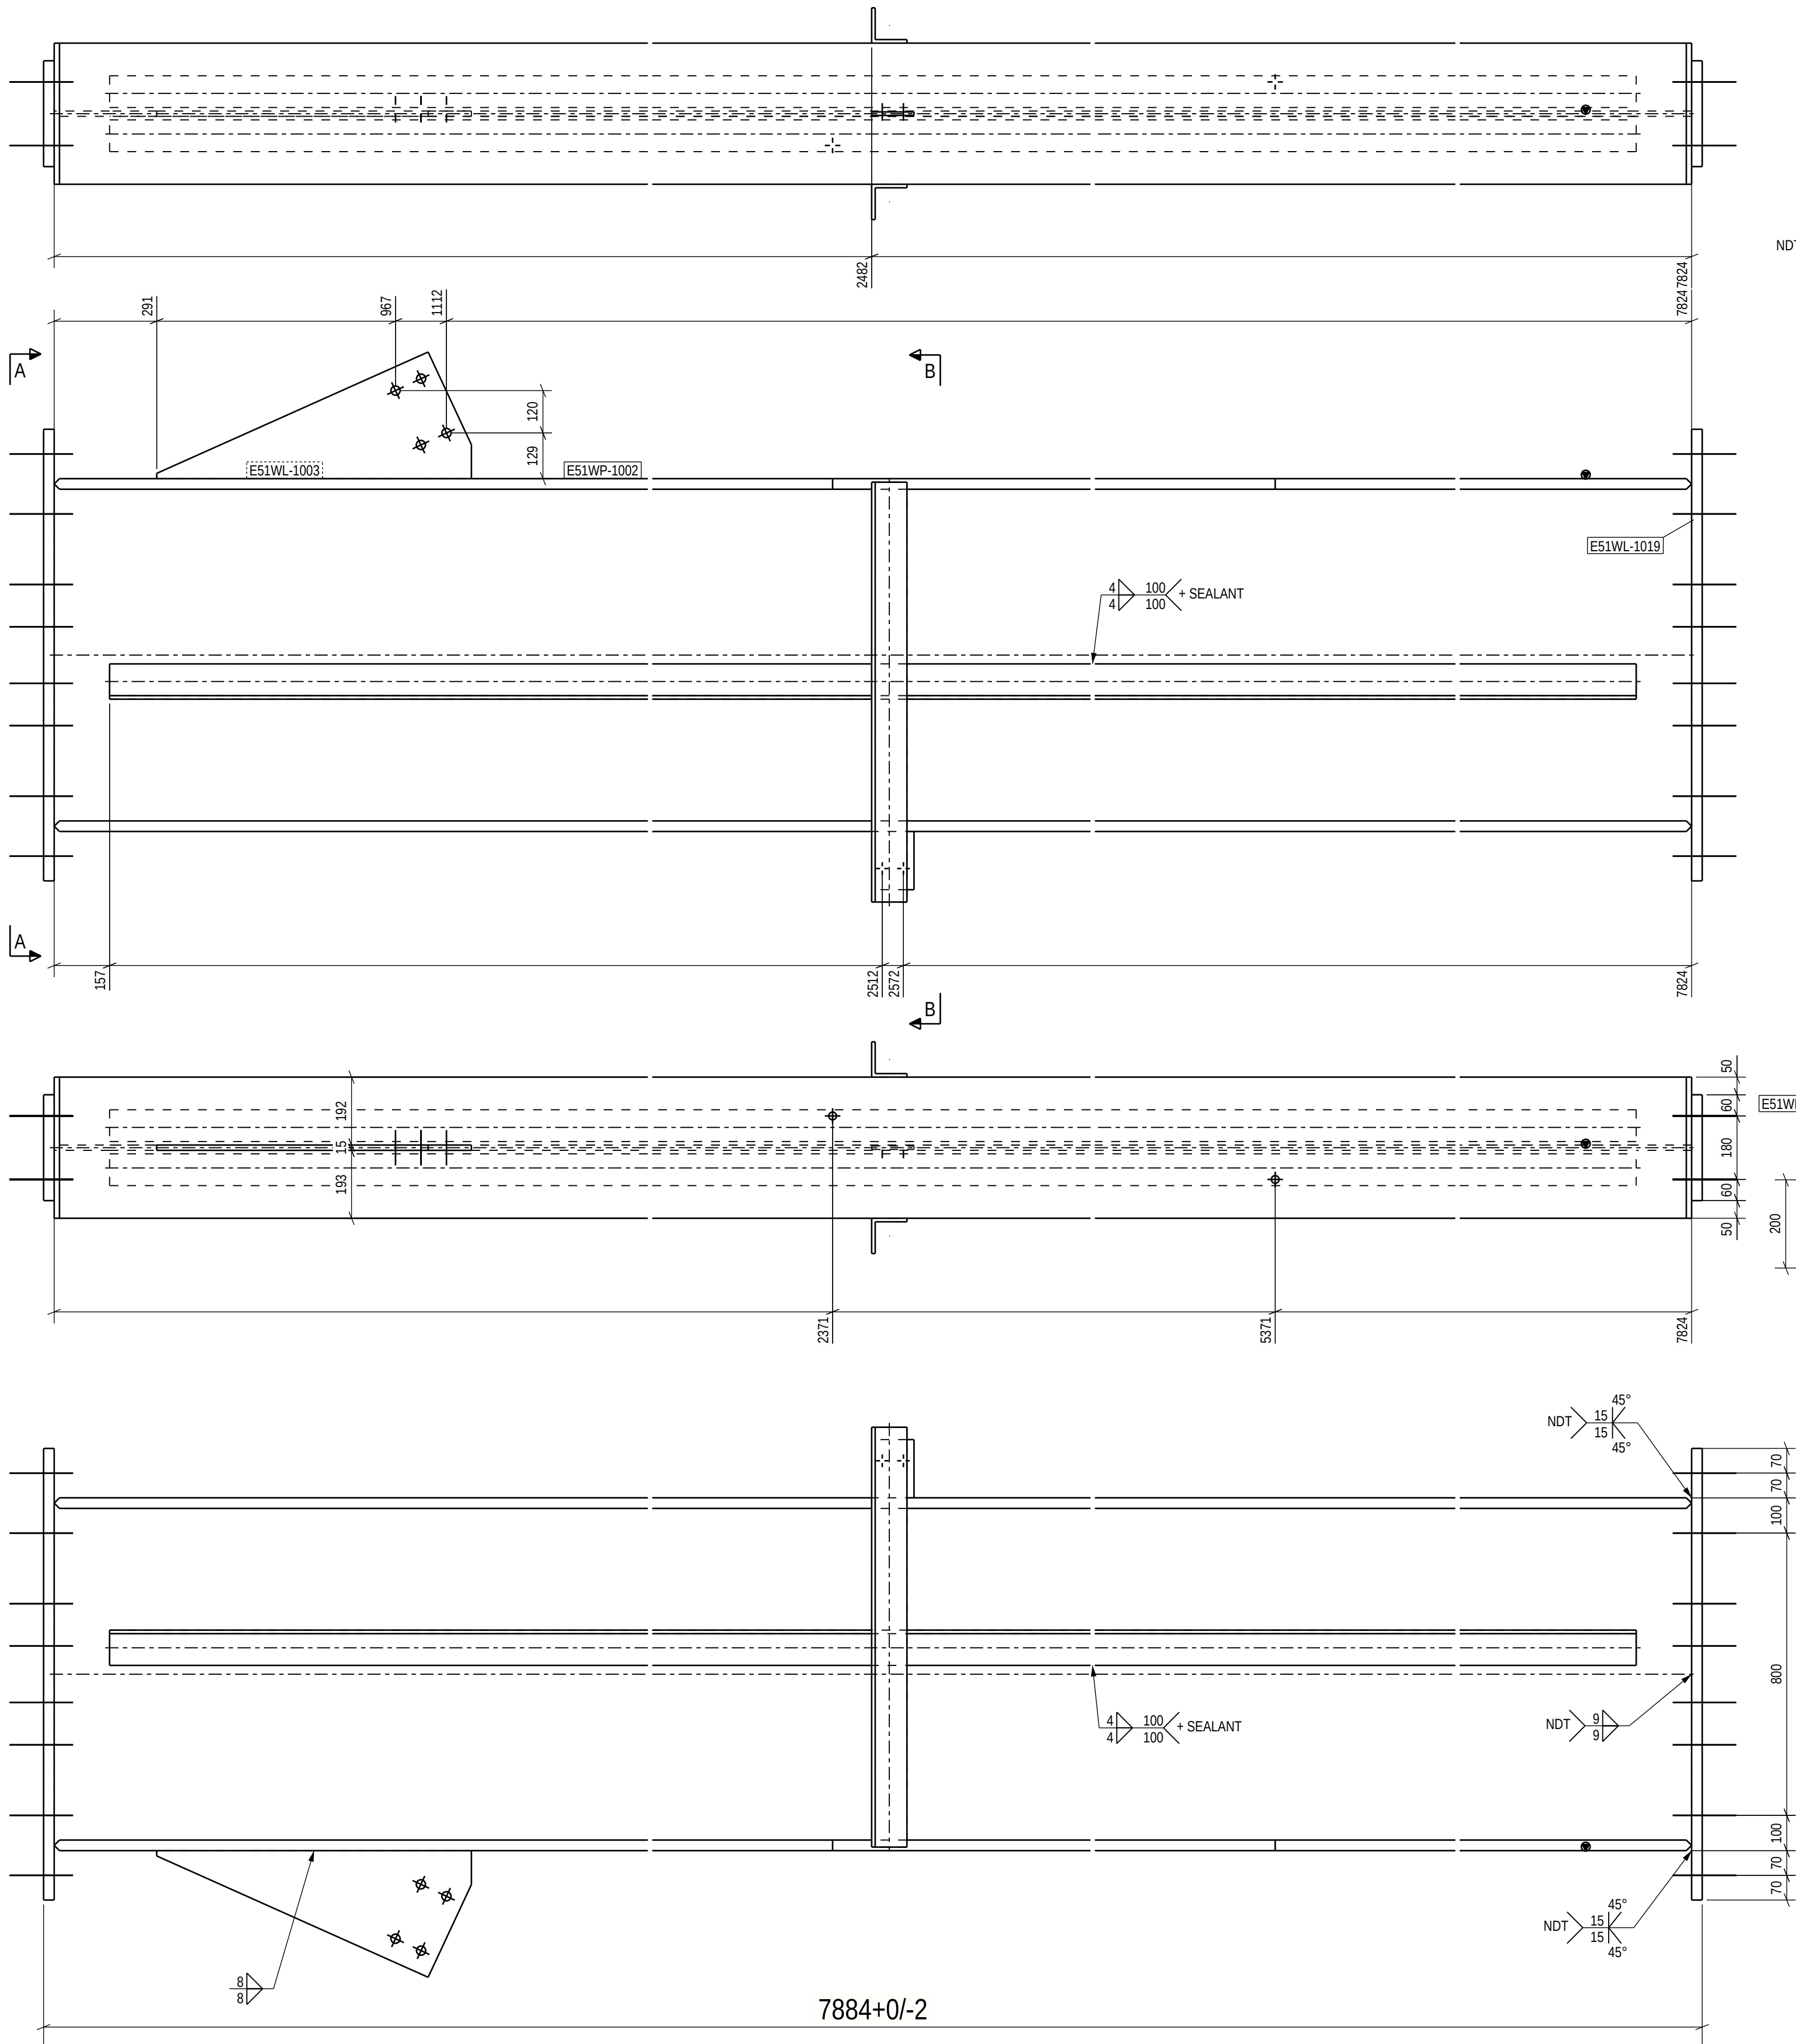


DET 4
Full contact in bearing, requirements acc. to EN 1090-2/6.8 and 11.2.3.5 and project specification

Tolerance for the first bolt group at the end of the beam:

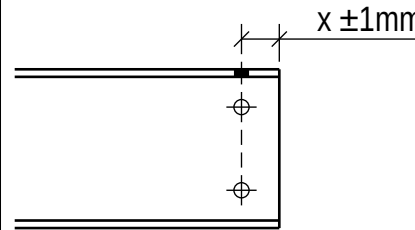

DET 1

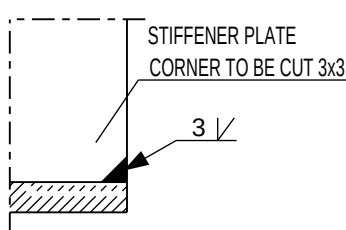

Technical fabrication requirements:		EXC2
Requirements for fabrication, standard	EN 1090-2, Appendix B	
Execution class	EN 1090-2, table A.3: EXC2	
Special fabrication requirements	Project specification/ shown on drwg.	
Surface preparation grade	ISO 8501-3, grade P2	
Surface treatment	ISO 12944-5	
Additional requirements on surface treatment	UT, EN-ISO17640, 20% of welds	
Extent of NDT, full welds	MT, EN1290, 20% of welds	
Extent of NDT, butt welds	UT, EN-ISO17640, 100% of welds	
Requirements on testing	EN1090-2 Section 6.6.3	
Weld class	C, EN ISO 5817	
Additional material inspection	Shown on drwg	

Approved For Construction

PROJECT NAME
Easpring New Materials Oy
FAIR Phase 1



SWECO RAKENNETEKNIIKKA OY
ILMALANPORTTI 2
00240 HELSINKI
PUH. +358 207 393 000
WWW.SWECO.FI

DRAWING CONTENT
ASSEMBLY DRAWING
Beam_WI
E51W-1003

DATE	ARCHIVING CODE	PAGE	DESIGN GROUP
12.06.2026			STR
DESIGNER	APPROVED	CHECKED	REVISION
Alexey Serous	Alexey Serous	Pertti Kolummaaho	Jere Kalliosalmi
PROJECT NUMBER	DWG. NO.		
25019443			

E51W-1003

25019443_Fair_E500

PART LIST FOR ASSEMBLY E51W-1004, MANUFACTURING AMOUNT 2 PIECES						
PART	PROFILE	MATERIAL	LENGTH (mm)	AREA (m ²)	WEIGHT (kg)	PCS
E51WL-1002	PL30X300	S355J2+N	1280	1.73	90.4	2
E51WL-1003	PL15X359	S355J2+N	892	0.38	20.2	1
E51WL-1024	PL5X47	S355J2+N	94	0.02	0.2	2
E51WP-1005	WI1000-15-30X400	S355J2	7824	27.98	2346.4	1
E51WP-1035	CFRHS100X50X5	S355J2H	7610	2.15	79.8	1
TOTAL:				32.25	2627.6	

DET 4

Full contact in bearing, requirements acc. to EN 1090-2/6.8 and 11.2.3.5 and project specification

Tolerance for the first bolt group at the end of the beam:

x ±1mm

DET 1

STIFFENER PLATE

CORNER TO BE CUT 3x3

3

Technical fabrication requirements:

Requirements for fabrication, standard
EN1090-2, table A.3: EXC2
Execution Specification document nr
25019443-ICC250-0600-0660-000005
Surface preparation grade
ISO12944-5
Additional requirements on surface treatment
RAL 7024 (Graphite Gray)
Washing of work up steel section
Appendix 1 / Project spec.
Welds, if not specified otherwise
EN 9692-1, EN 9692-2

Fabrication tolerances
EN 1090-2, Appendix B
Special fabrication tolerances
Project specification/ shown on dwg.
Weld inspection requirements
EN 1090-2, Table 24, U>0.5
Extent of NDT, after welds
MT-EN1290, 20% of welds
Extent of NDT, butt welds
UT, EN-ISO17640, 20% of welds
Extent of NDT for splices not shown on drawing
UT, EN-ISO17640, 100% of welds
Requirements on testing
EN1090-2 Section 6.6.3
Weld class
C, EN ISO 5817
Additional material inspection
Shown on dwg

Approved For Construction

PROJECT NAME
Easpring New Materials Oy
FAIR Phase 1

SWECO

Sustainable engineering and design

SWECO RAKENNETEKNIKKA OY
ILMALANPORTTI 2
00240 HELSINKI
PUH. +358 207 393 000
WWW.SWECO.FI

DRAWING CONTENT
ASSEMBLY DRAWING
Beam_WI
E51W-1004

DATE
12.06.2026

ARCHIVING CODE

PAGE

DESIGNER
Aleksy Serous


APPROVED
Pertti Kolummaaho



CHECKED
Jere Kalliosalmi

DESIGN GROUP
STR

PROJECT NUMBER
25019443


REVISION
E51W-1004

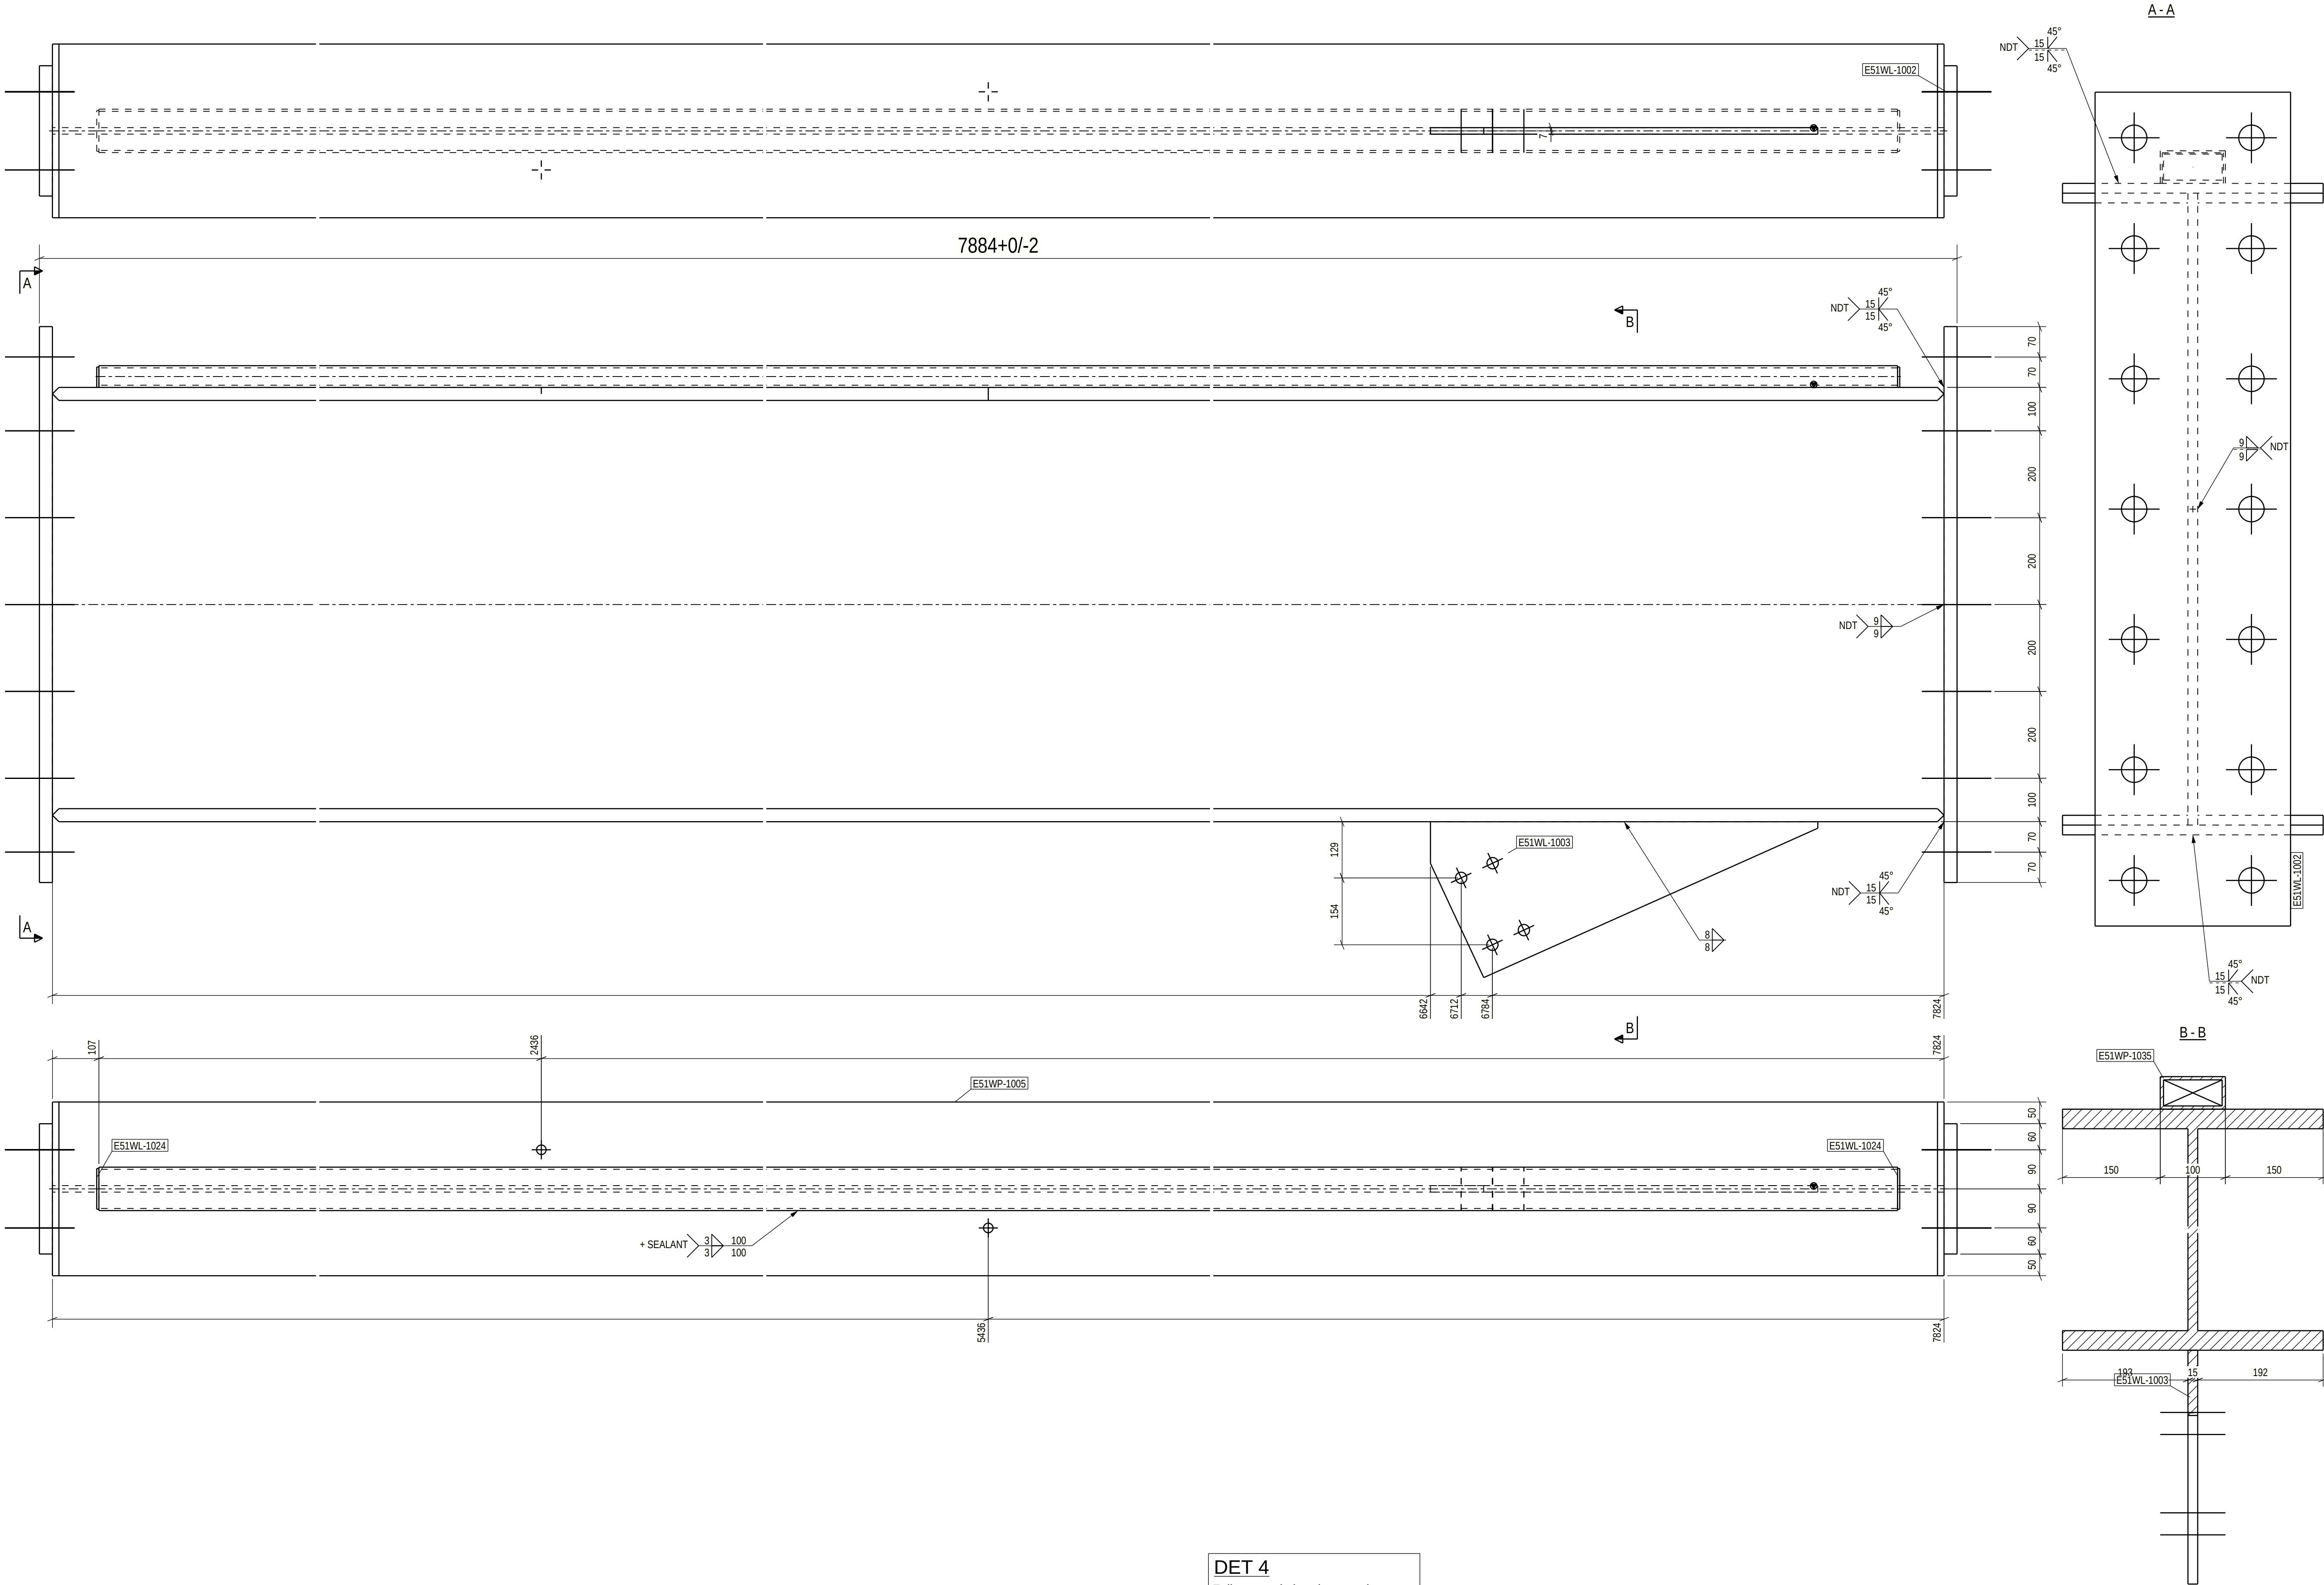

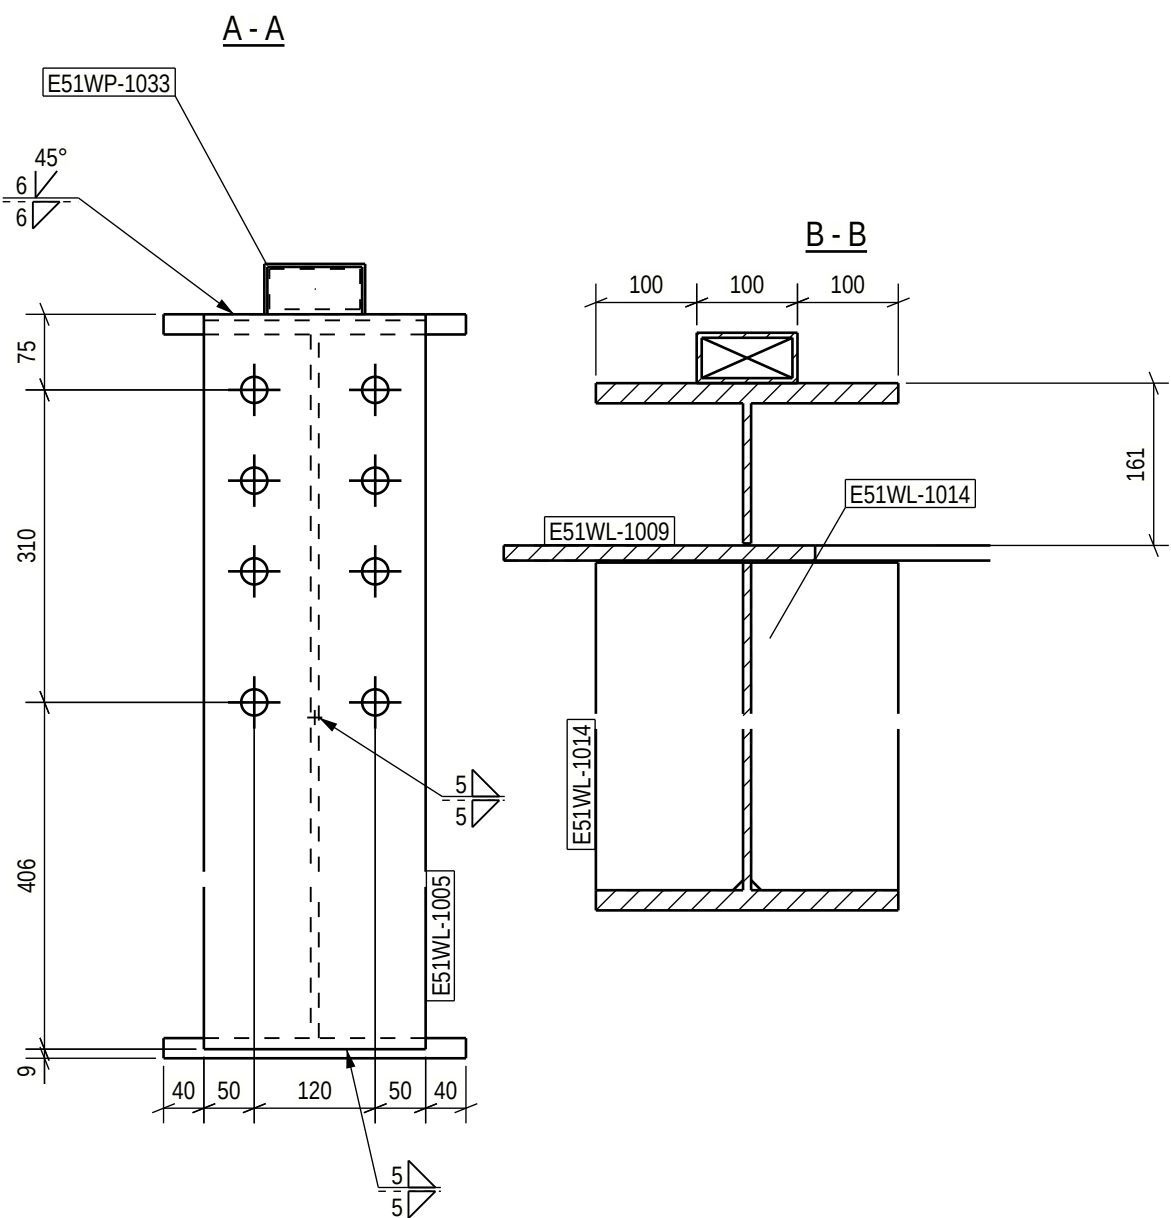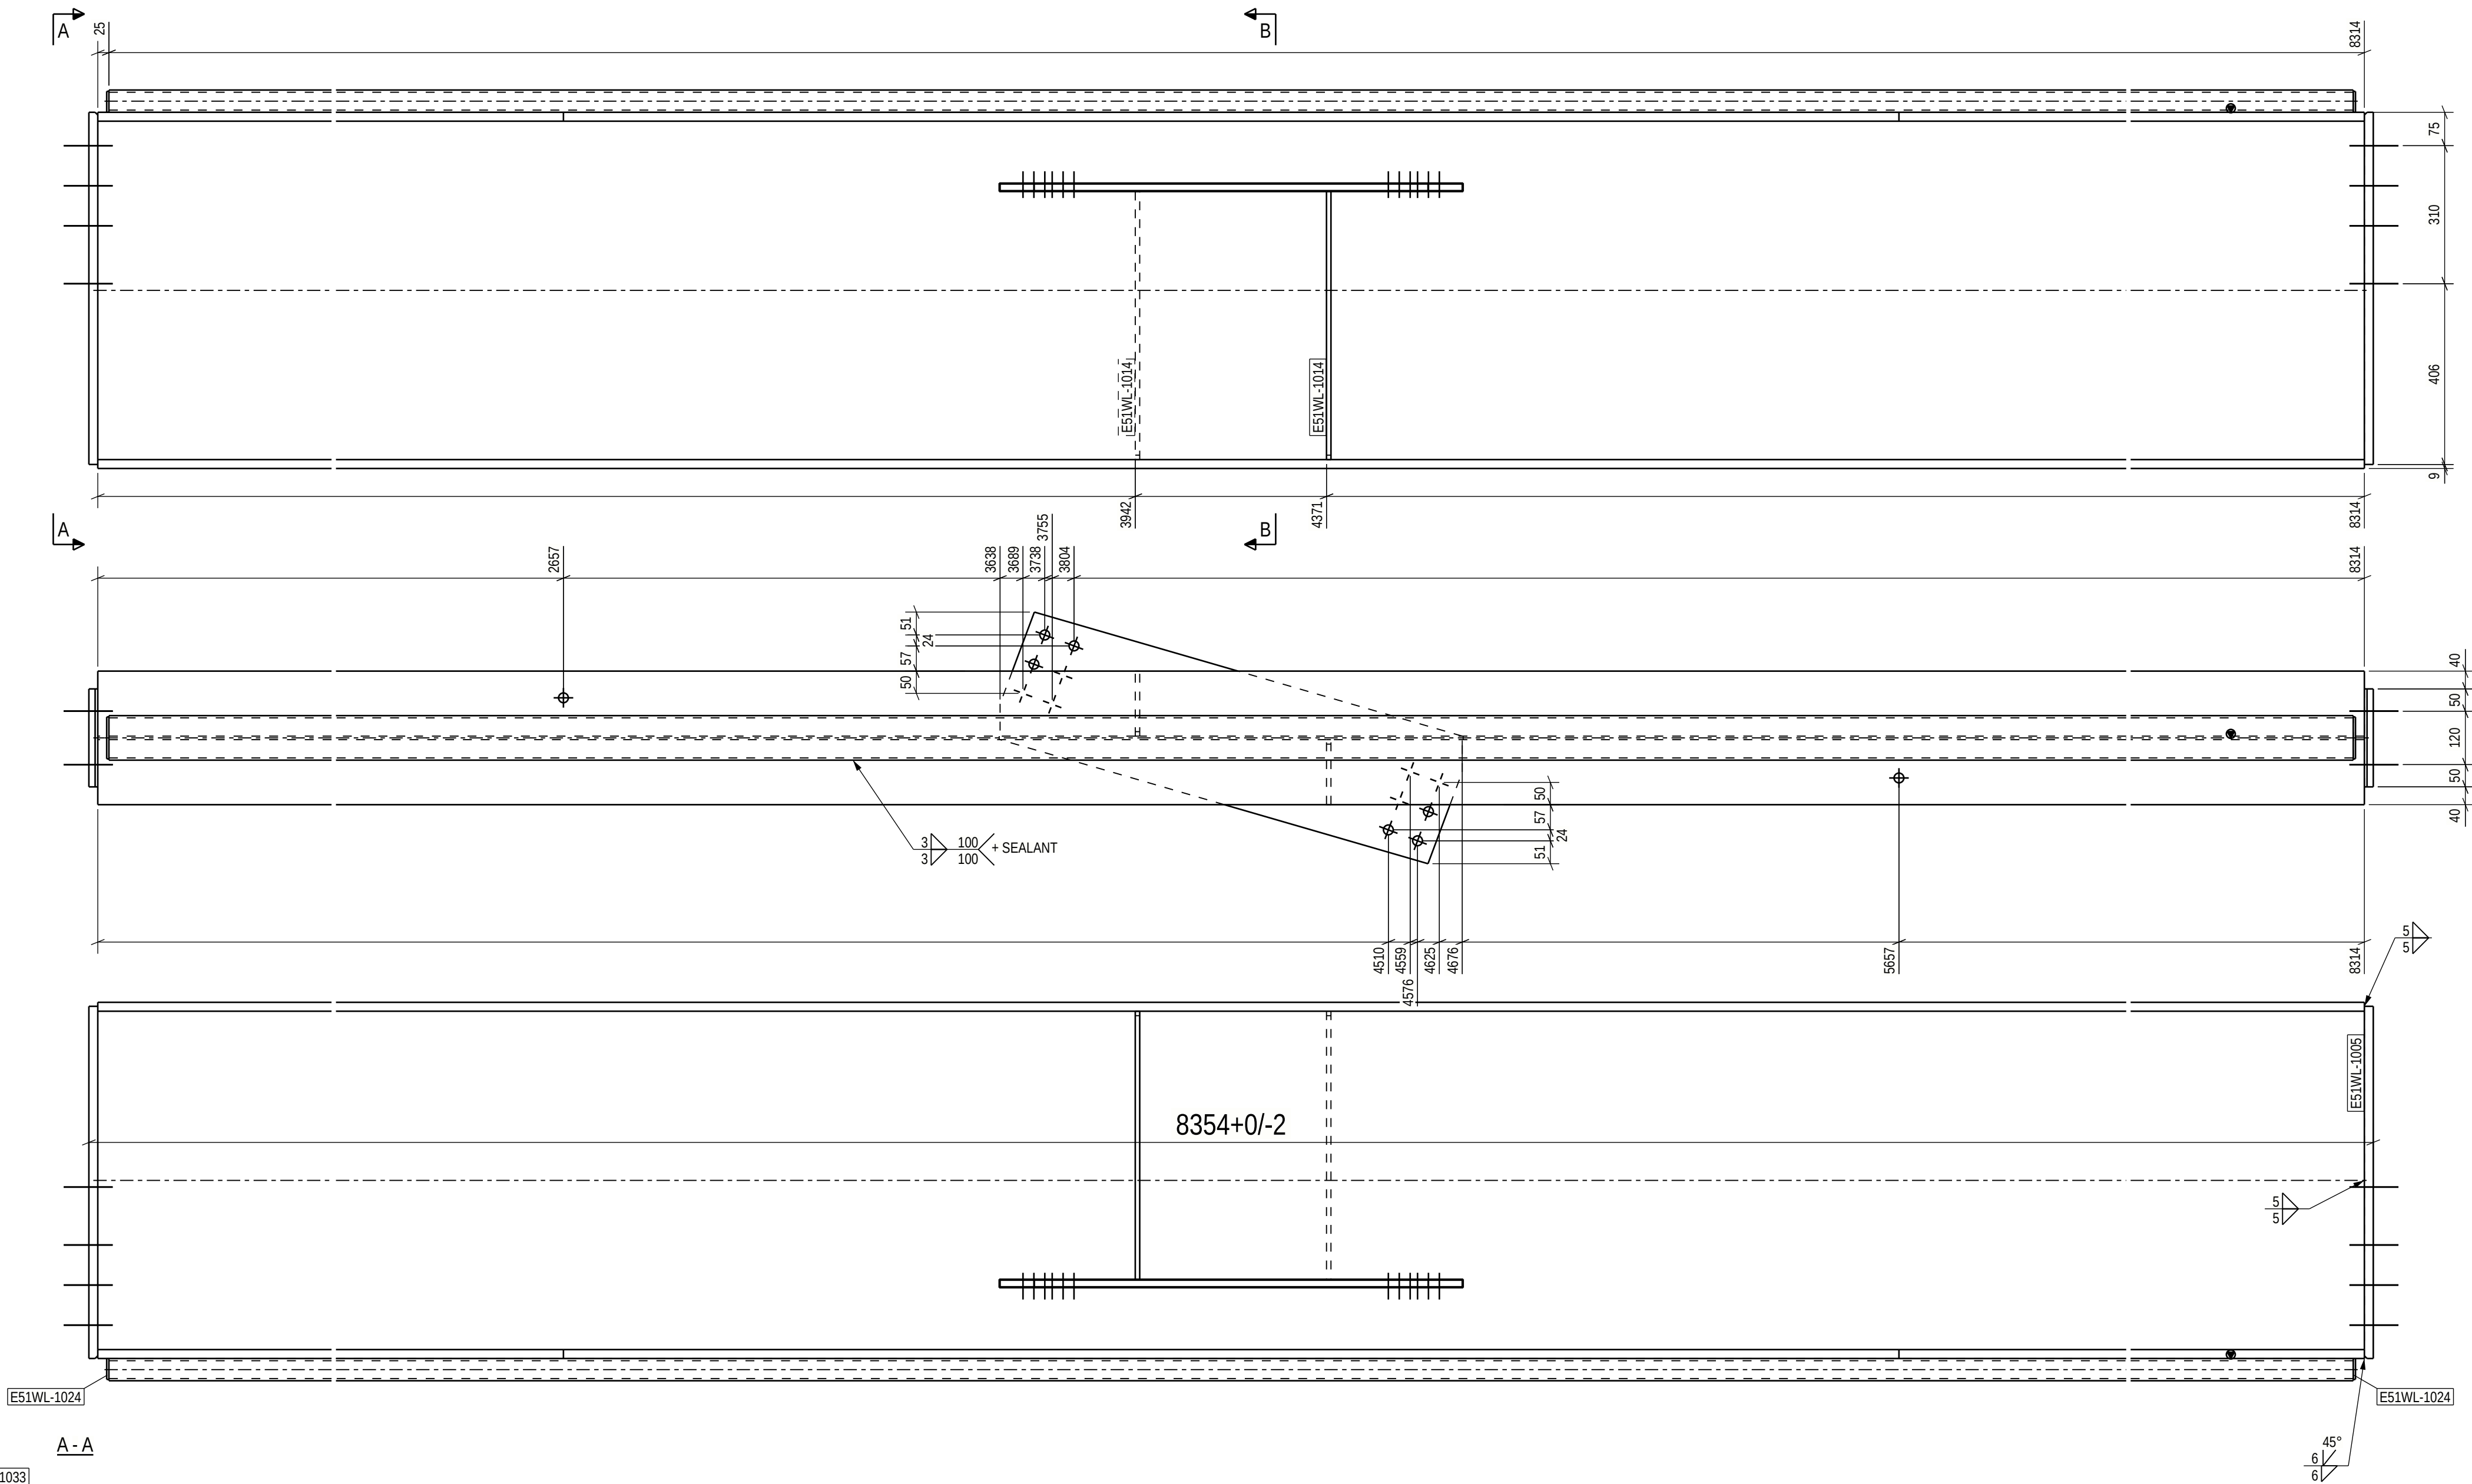


PART LIST FOR ASSEMBLY E51W-1005, MANUFACTURING AMOUNT 1 PIECES						
PART	PROFILE	MATERIAL	LENGTH [mm]	AREA [m ²]	WEIGHT [kg]	PCS
E51WL-1005	PL20X220	S355J2+N	791	0.78	27.3	2
E51WL-1009	PL15X297	S355J2+N	1040	0.65	35.7	1
E51WL-1014	PL10X146	S355J2+N	602	0.38	6.9	2
E51WL-1024	PL5X47	S355J2+N	94	0.02	0.2	2
E51WP-1012	WI800-8-20X300	S355J2	8314	23.16	1181.9	1
E51WP-1033	CFRHS100X50X5	S355J2H	8264	2.34	86.7	1
TOTAL:				27.32	1373.0	

DET 4
Full contact in bearing, requirements acc. to EN 1090-2/6.8 and 11.2.3.5 and project specification
Tolerance for the first bolt group at the end of the beam:

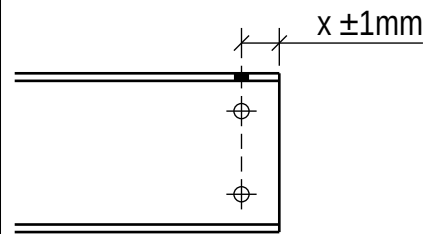

DET 1

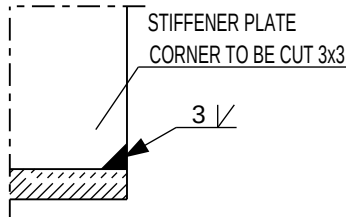

Technical fabrication requirements:		EXC2
Requirements for fabrication, standard EN1090-2, table A.3: EXC2	Fabrication tolerances EN 1090-2, Appendix B	
Execution Specification document nr 25019443-ICC250-0600-0600-000005	Special fabrication tolerances Project specification/ shown on drwg.	
Surface preparation grade ISO8501-3, grade P2	Weld inspection requirements EN 1090-2, Table 24, U>0.5	
Surface treatment ISO12944-5	Extent of NDT, after welds MT-EN1290, 20% of welds	
Additional requirements on surface treatment C3.07, EPPUR 240/2	Extent of NDT, butt welds UT, EN-ISO17640, 20% of welds	
Grades RAL 7024 (Graphite Gray)	Extent of NDT for splices not shown on drawing UT, EN-ISO17640, 100% of welds	
Welding of bulk up steel section Appendix 1 / Project spec.	Requirements on testing EN1090-2 Section 6.6.3	
Welds, first specified otherwise EN 9692-1, EN 9692-2	Weld class C, EN ISO 5817	
	Additional material inspection Shown on drwg	

Approved For Construction



PROJECT NAME
Easpring New Materials Oy
FAIR Phase 1



SWECO RAKENNETEKNIIKKA OY
ILMALANPORTTI 2
00240 HELSINKI
PUH. +358 207 393 000
WWW.SWECO.FI

DRAWING CONTENT
ASSEMBLY DRAWING
Beam_WI
E51W-1005


DATE	ARCHIVING CODE	PAGE	DESIGN GROUP
12.06.2026			STR
DESIGNER	APPROVED	CHECKED	REVISION
Alexey Serov	Alexey Serov	Pertti Kolummaaho	Jere Kallio
PROJECT NUMBER	DWG. NO.		
25019443	E51W-1005		

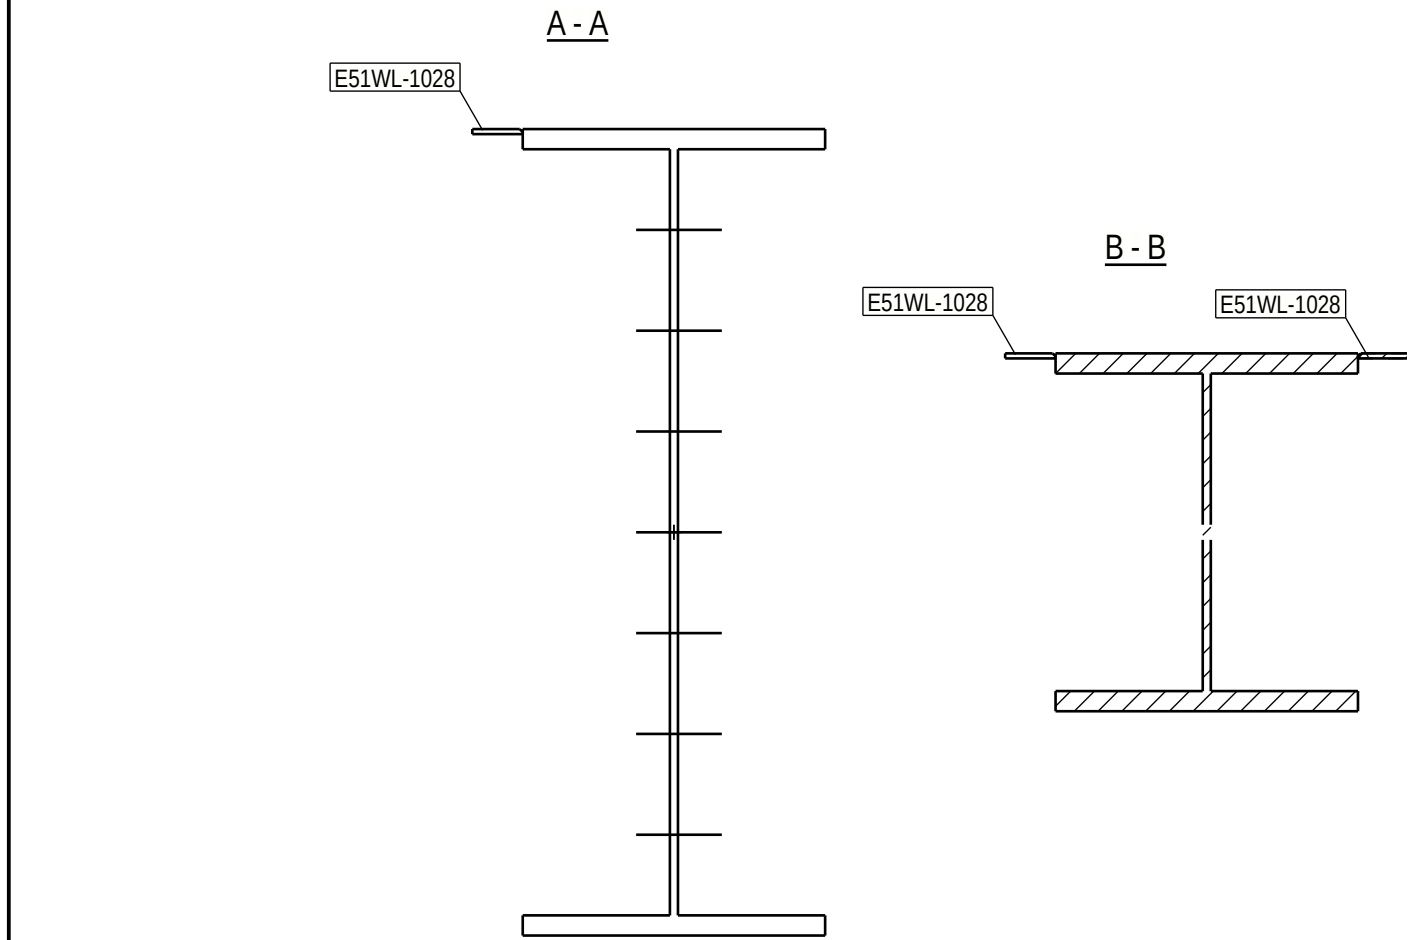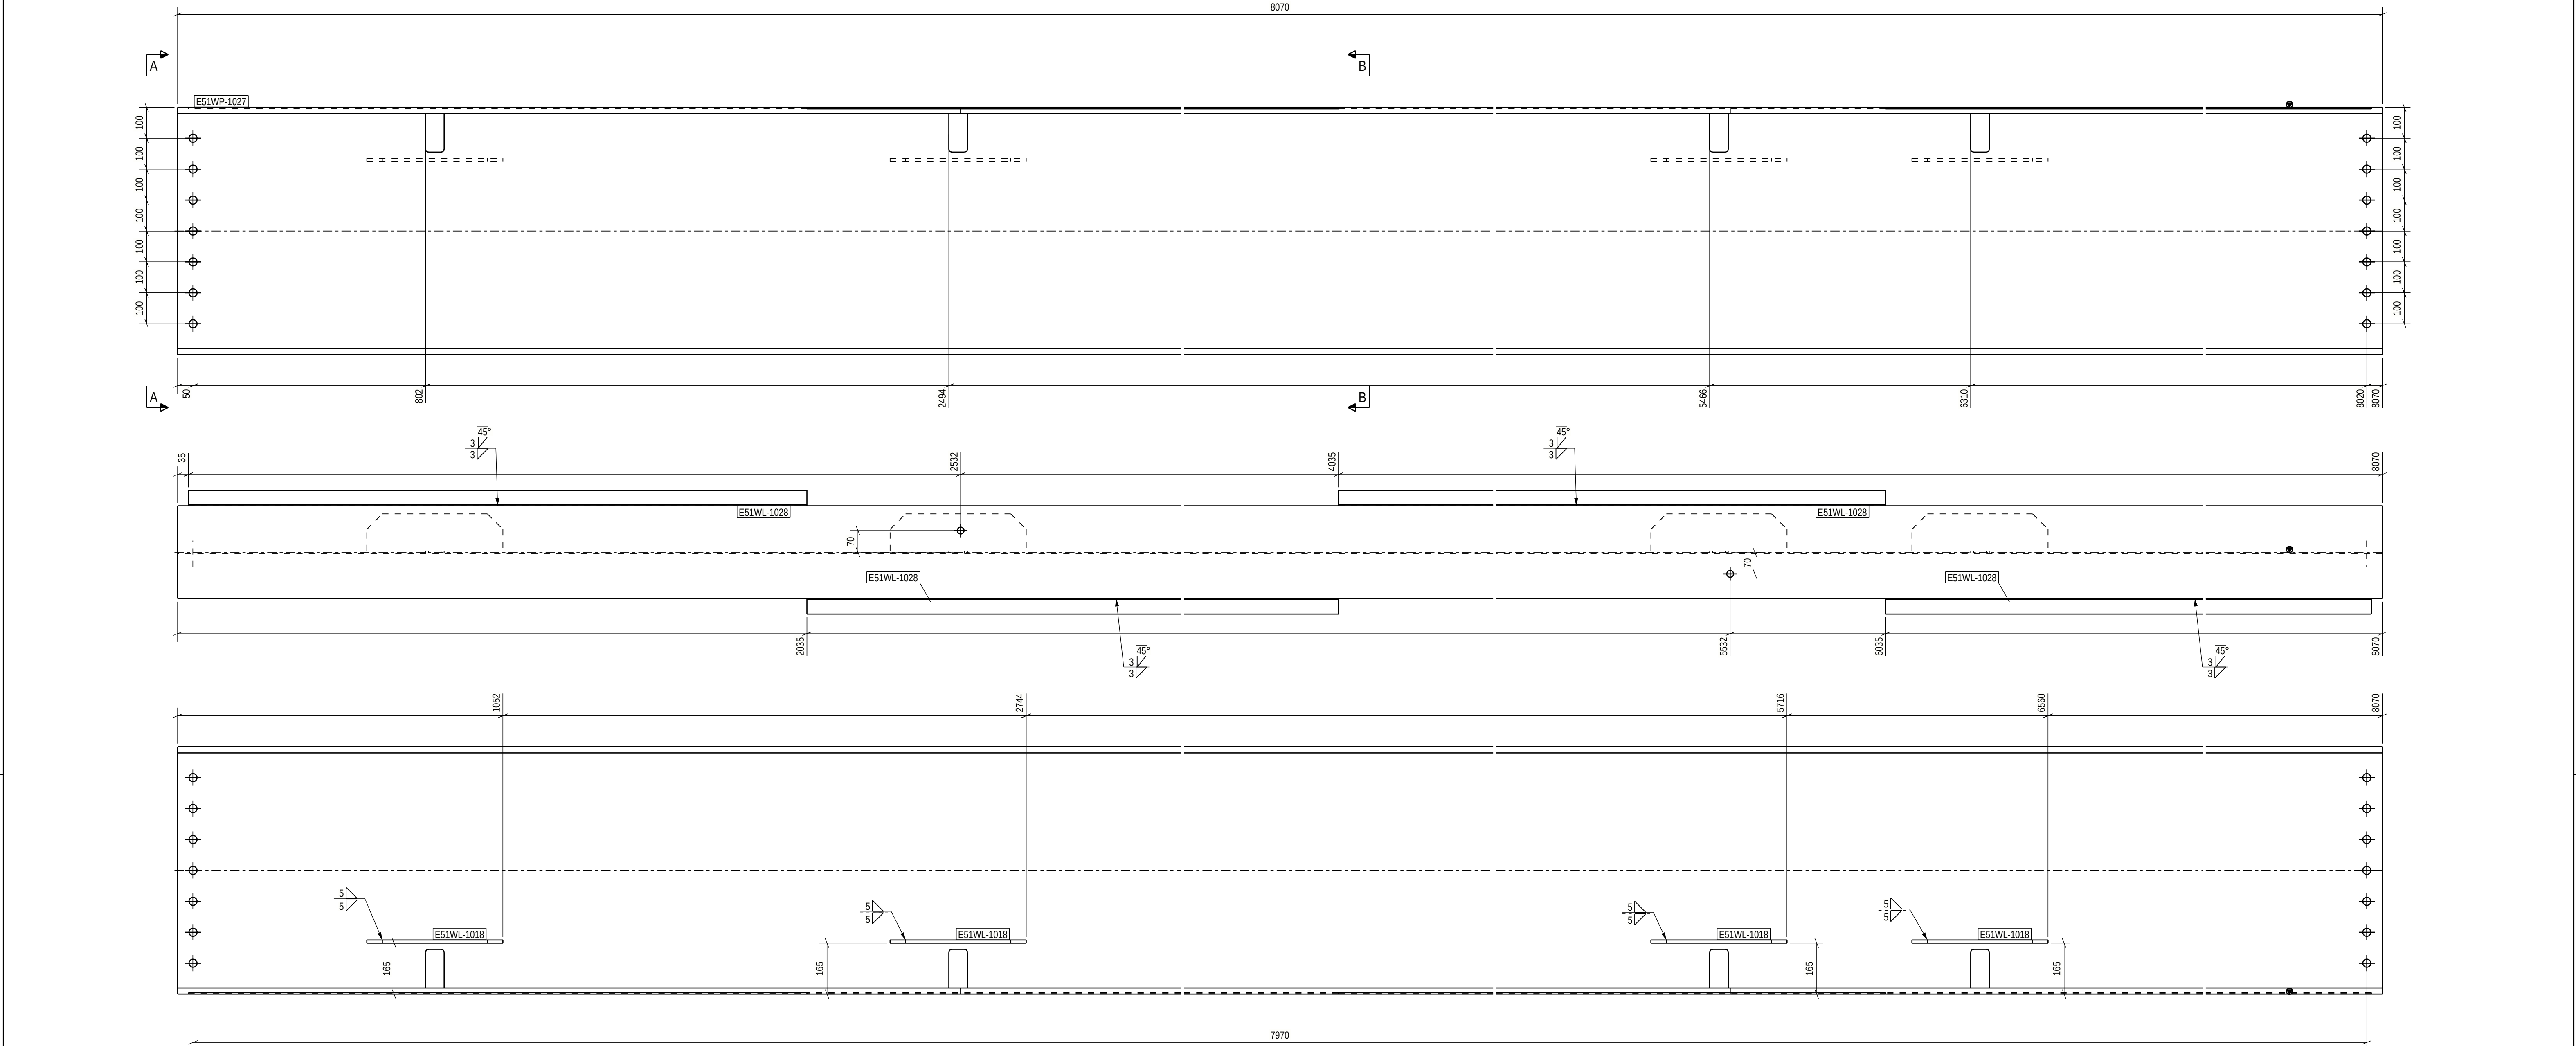


PART LIST FOR ASSEMBLY E51W-1006, MANUFACTURING AMOUNT 1 PIECES						
PART	PROFILE	MATERIAL	LENGTH (mm)	AREA (m ²)	WEIGHT (kg)	PCS
E51WL-1018	PL10X120	S355J2+N	440	0.44	3.9	4
E51WL-1028	PL5X50	S355J2+N	2000	0.87	3.9	4
E51WP-1027	WI800-8-20X300	S355J2	8070	22.45	1147.2	1
TOTAL:				23.77	1178.4	

DET 4
Full contact in bearing, requirements acc. to EN 1090-2/6.8 and 11.2.3.5 and project specification

Tolerance for the first bolt group at the end of the beam:

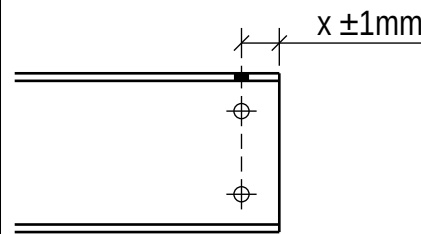

DET 1

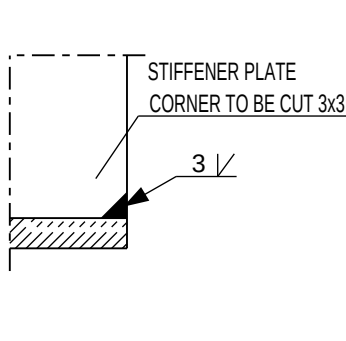

Technical fabrication requirements:		EXC2
Requirements for fabrication, standard	EN 1090-2, table A.3 - EXC2	
Execution Specification document nr	25019443-ICC250-0600-0660-000005	
Surface preparation grade	ISO 8501-3, grade P2	
Surface treatment	ISO 12944-5	
Additional requirements on surface treatment	RAL 7024 (Graphite Gray)	
Welding of bulk up steel section	Appendix 1 / Project spec.	
Welds, first specified reference	EN 9692-1, EN 9692-2	
Fabrication tolerances	EN 1090-2, Appendix B	
Special fabrication references	Project specification/ shown on drwg.	
Weld inspection requirements	EN 1090-2, Table 24, U>0.5	
Extent of NDT, after welds	MT-EN1290, 20% of welds	
Extent of NDT, butt welds	UT, EN-ISO17640, 20% of welds	
Extent of NDT, fillet welds	UT, EN-ISO17640, 100% of welds	
Requirements on testing	EN1090-2 Section 6.6.3	
Weld class	C, EN ISO 5817	
Additional material inspection	Shown on drwg.	

Approved For Construction




PROJECT NAME
Easpring New Materials Oy
FAIR Phase 1



SWECO RAKENNETEKNIKKA OY
ILMALANPORTTI 2
00240 HELSINKI
PUH. +358 207 393 000
WWW.SWECO.FI

DRAWING CONTENT
ASSEMBLY DRAWING
Beam_WI
E51W-1006


DATE	ARCHIVING CODE	PAGE	DESIGN GROUP
12.06.2026			STR
DESIGNER	APPROVED	CHECKED	REVISION
Alexey Serus	Pertti Kollumaaaho	Jere Kalliosalmi	
PROJECT NUMBER 25019443	DWG. NO.		E51W-1006

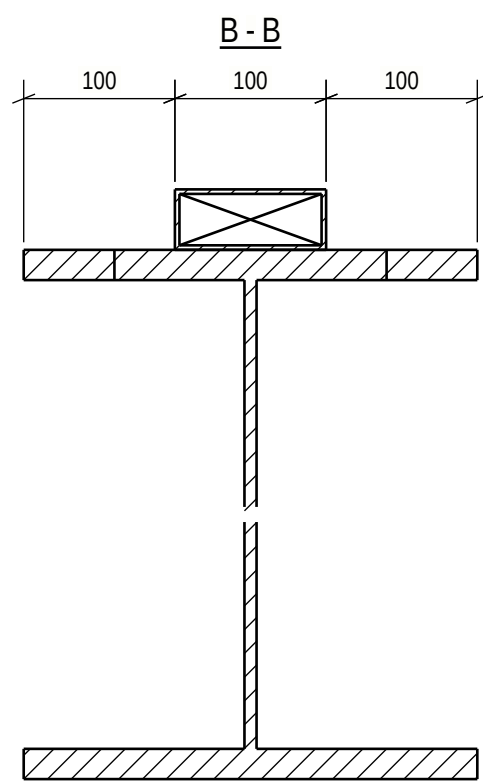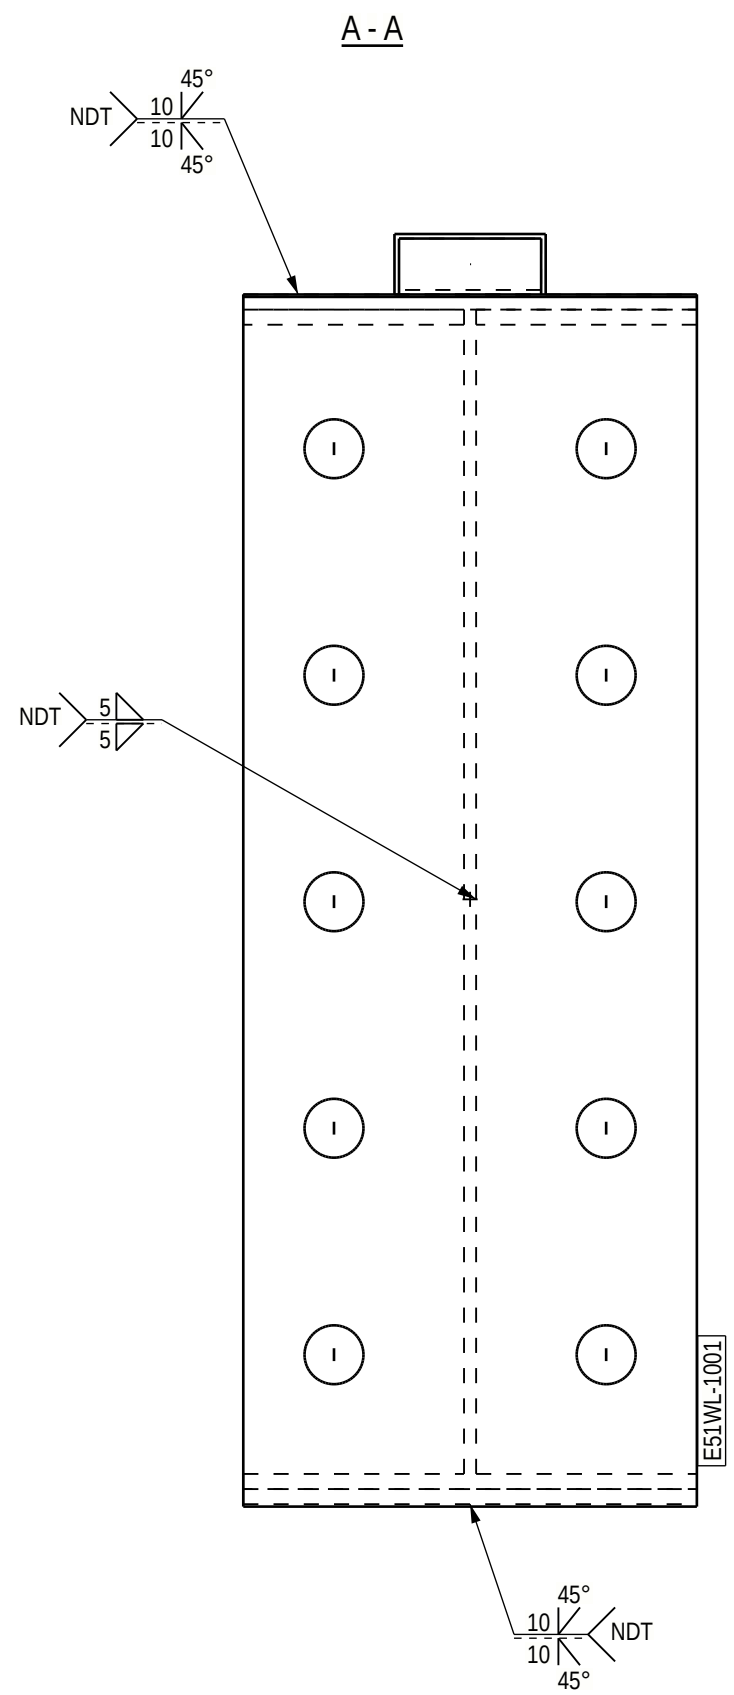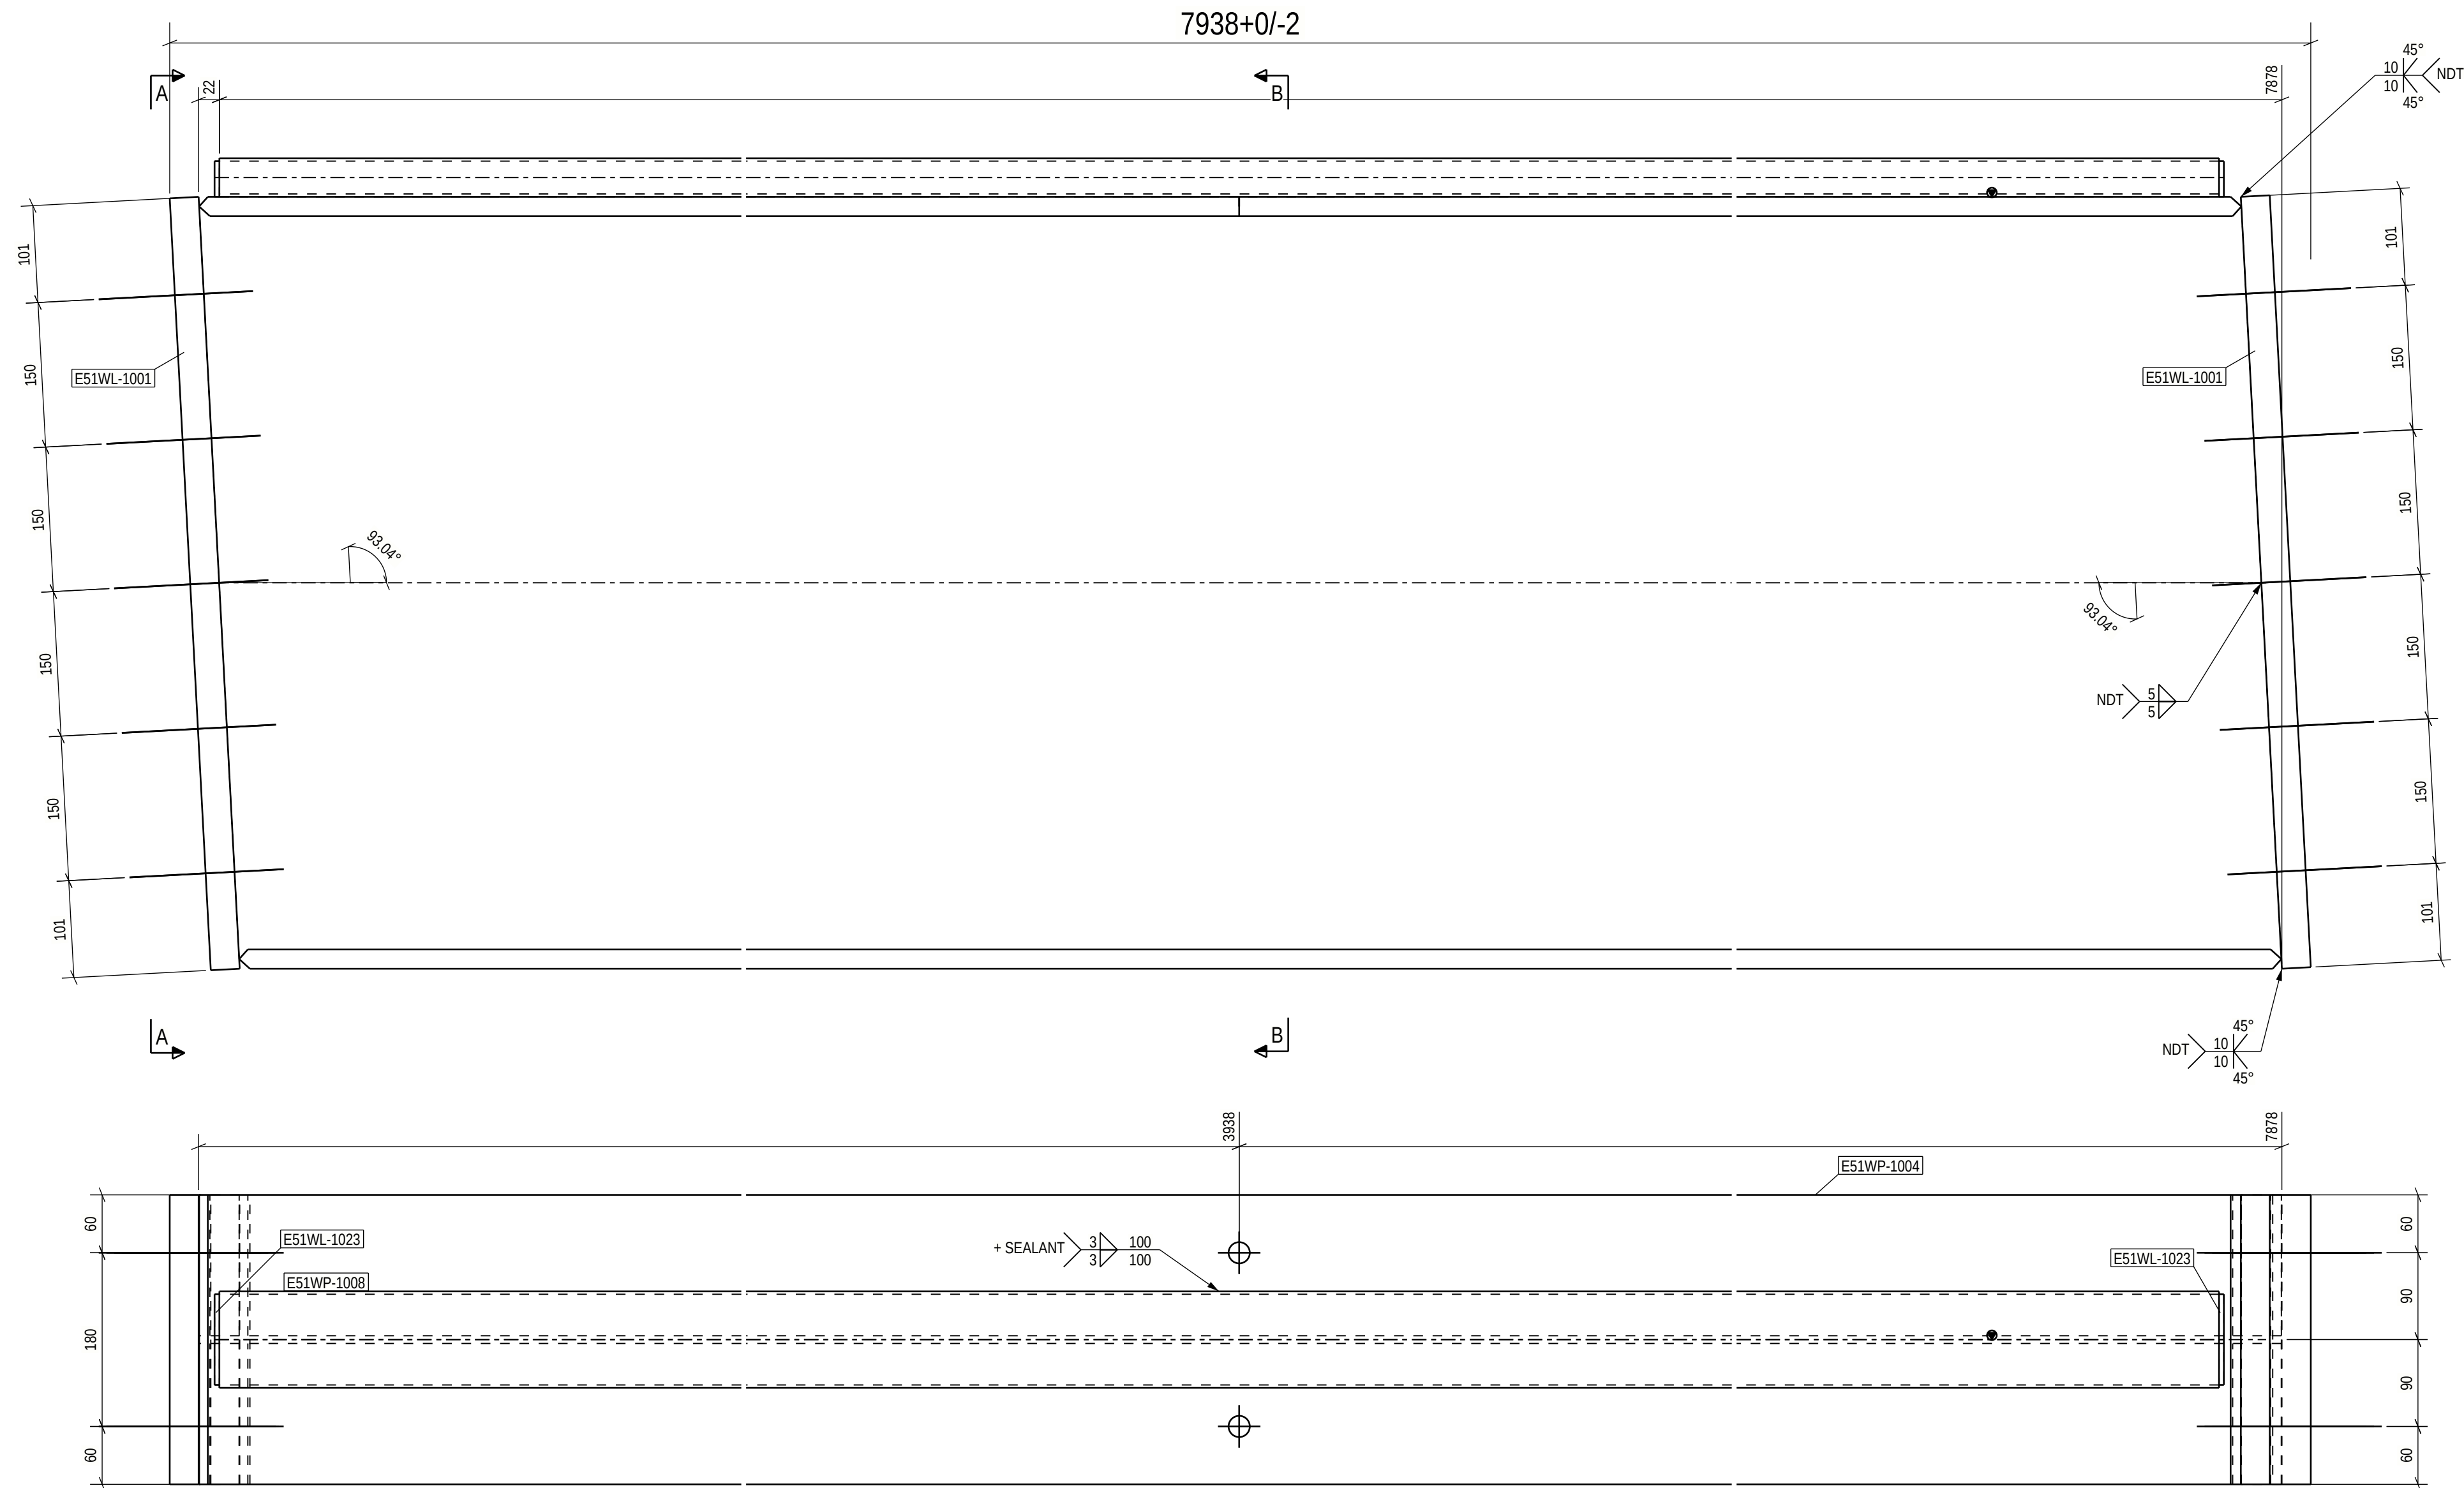


DET 4

Full contact in bearing, requirements acc. to EN 1090-2/6.8 and 11.2.3.5 and project specification

Tolerance for the first bolt group at the end of the beam:

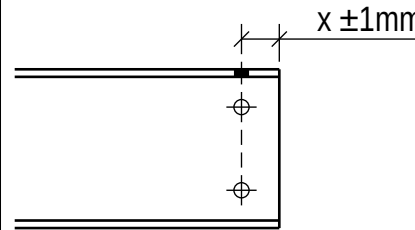

DET 1

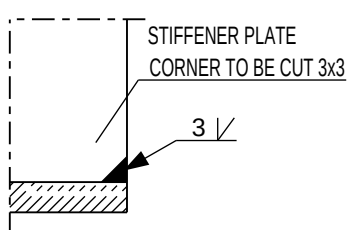

Technical fabrication requirements:		EXC2
Requirements for fabrication, standard EN1090-2, table A3: EXC2	Fabrication tolerances EN 1090-2, Appendix B	
Execution Specification document nr 25019443-ICC250-0600-0660-000005	Special fabrication tolerances Project specification/ shown on drwg.	
Surface preparation grade ISO8501-3, grade P2	Weld inspection requirements EN 1090-2, Table 24, U>0.5	
Surface treatment ISO12944-5	Extent of NDT, after welds MT-EN1290, 20% of welds	
Additional requirements on surface treatment RAL 7024 (Graphite Gray)	Extent of NDT, butt welds UT, EN-ISO17640, 20% of welds	
C3.07, EPPUR 240/2	Extent of NDT for splices not shown on drawing UT, EN-ISO17640, 100% of welds	
Requirements on welding Appendix 1 / Project spec.	Requirements on testing EN1090-2 Section 6.6.3	
Welds, first specified otherwise EN 9692-1, EN 9692-2	Weld class C, EN ISO 5817	
	Additional material inspection Shown on drwg	

Approved For Construction


PROJECT NAME
Easpring New Materials Oy
FAIR Phase 1



SWECO RAKENNETEKNIKKKA OY
ILMALANPORTTI 2
00240 HELSINKI
PUH. +358 207 393 000
WWW.SWECO.FI

DRAWING CONTENT
ASSEMBLY DRAWING
Beam_WI
E51W-1007

DATE	ARCHIVING CODE	PAGE	DESIGN GROUP
12.06.2026			STR
DESIGNER	APPROVED	CHECKED	REVISION
Alexey Serov	Pertti Kollumaa	Jere Kallio	
PROJECT NUMBER	DWG. NO.		
25019443	E51W-1007		

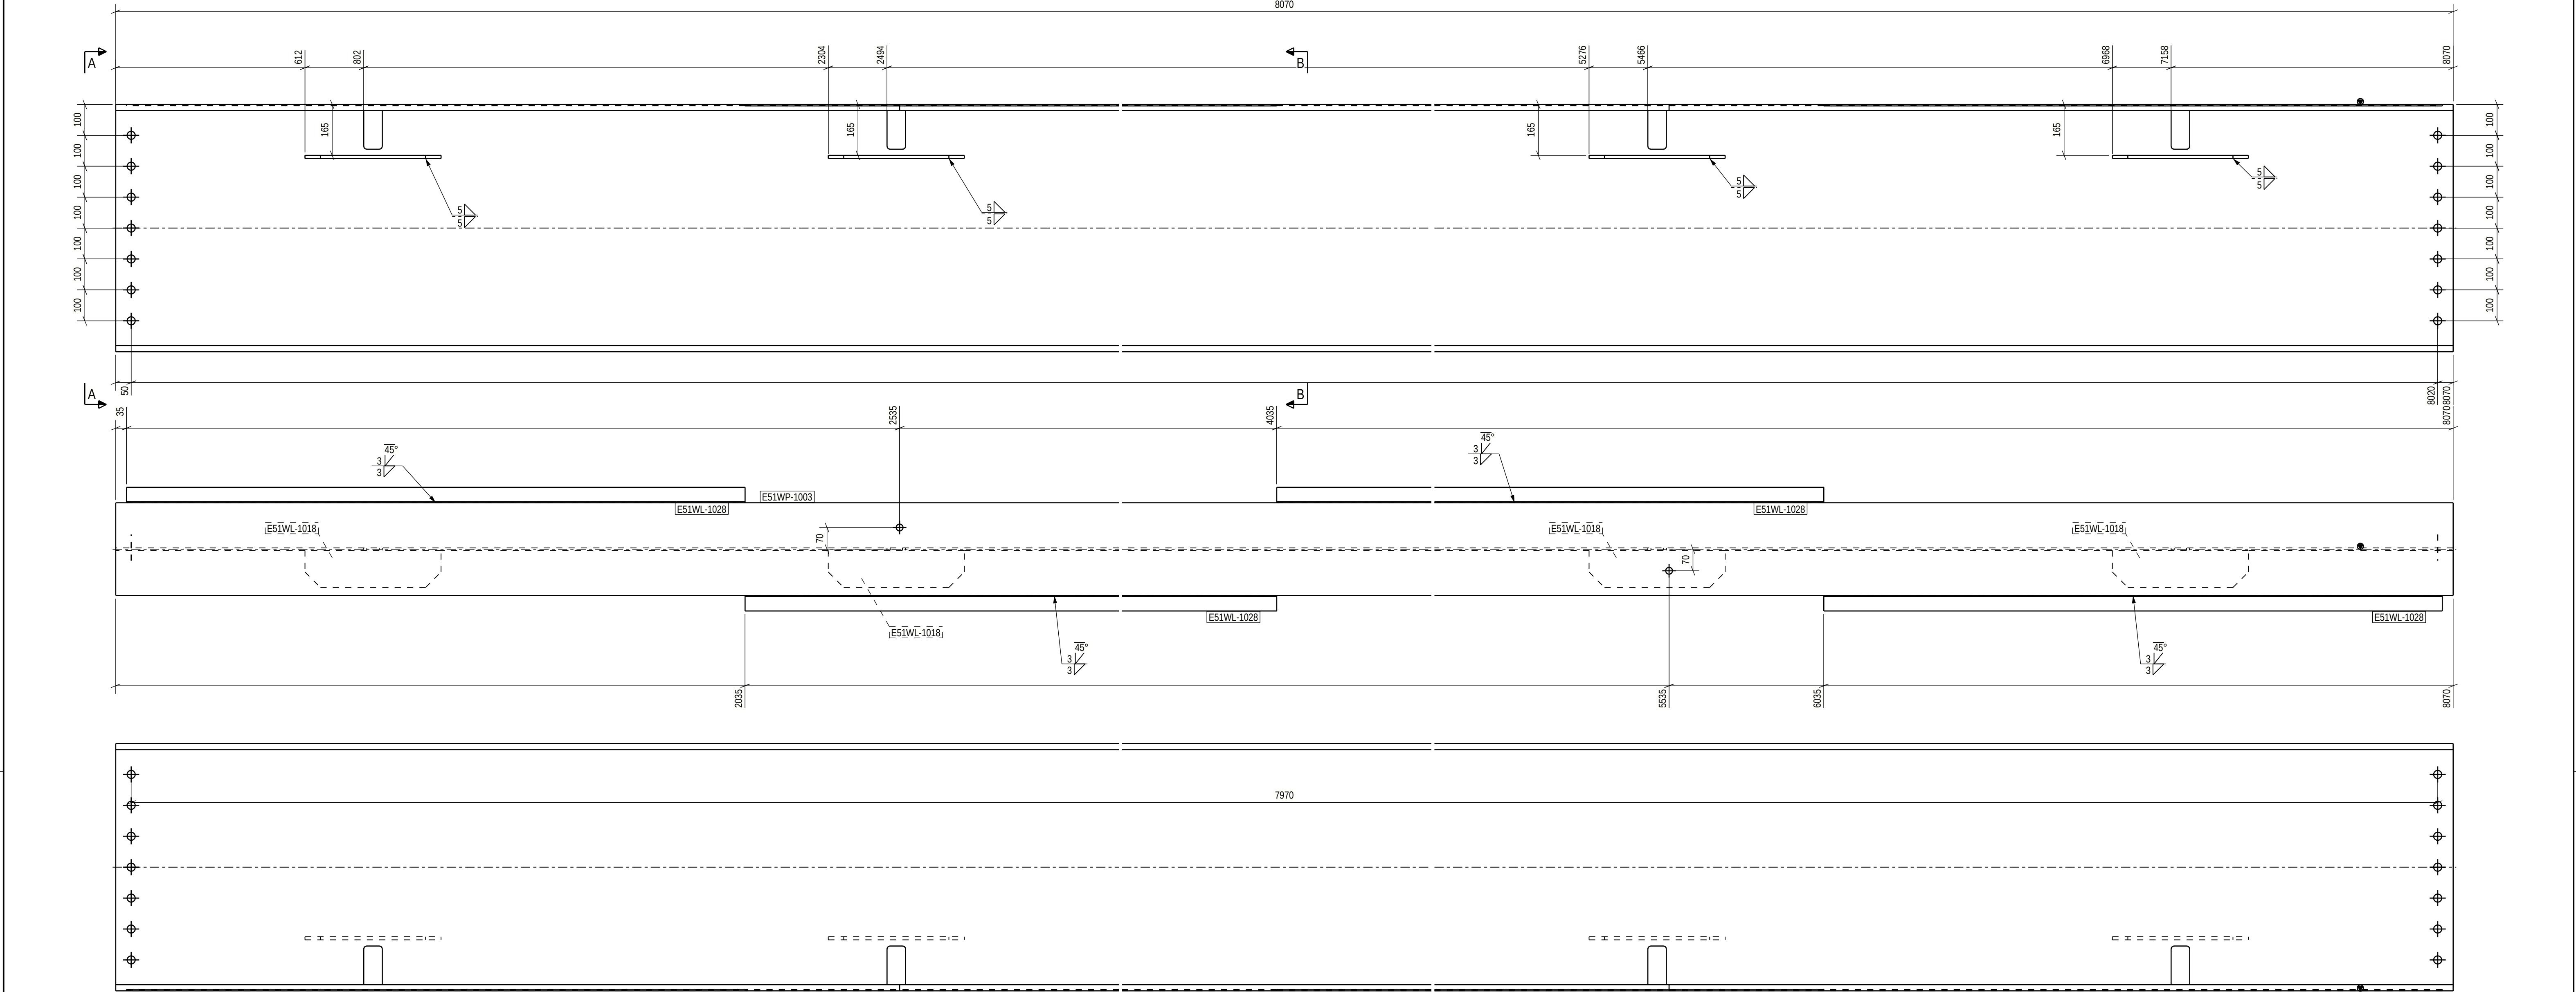

PART LIST FOR ASSEMBLY E51W-1008, MANUFACTURING AMOUNT 1 PIECES						
PART	PROFILE	MATERIAL	LENGTH (mm)	AREA (m ²)	WEIGHT (kg)	PCS
E51WL-1018	PL10X120	S355J2+N	440	0.44	3.9	4
E51WL-1028	PL5X50	S355J2+N	2000	0.87	3.9	4
E51WP-1003	WI800-8-20X300	S355J2	8070	22.45	1147.2	1
TOTAL:				23.77	1178.4	

DET 4
Full contact in bearing, requirements acc. to EN 1090-2/6.8 and 11.2.3.5 and project specification

Tolerance for the first bolt group at the end of the beam:

x ±1mm

DET 1

STIFFENER PLATE
CORNER TO BE CUT 3x3

3

EXC2

Technical fabrication requirements:

Requirements for fabrication, standard EN1090-2, table A.3: EXC2	Fabrication tolerances EN 1090-2, Appendix B
Execution Specification document nr 25019443-IC250-9600-0660-000005	Special fabrication tolerances Project specification/ shown on drwg.
Surface preparation grade ISO8501-3, grade P2	Weld inspection requirements EN 1090-2, Table 24, U>0.5
Surface treatment ISO12944-5	Extent of NDT, after welds MT-EN1290, 20% of welds
Additional requirements on surface treatment RAL 7024 (Graphite Gray)	Extent of NDT, butt welds UT, EN-ISO17640, 20% of welds
Welding of bulk up steel section Appendix 1 / Project spec.	UT, EN-ISO17640, 100% of welds
Welds, first specified otherwise EN 9692-1, EN 9692-2	Requirements on testing EN1090-2 Section 6.6.3
	Weld class C, EN ISO 5817
	Additional material inspection Shown on drwg.

Approved For Construction

PROJECT NAME: Easpring New Materials Oy
FAIR Phase 1

DRAWING CONTENT: ASSEMBLY DRAWING
Beam_WI
E51W-1008

DATE: 12.06.2026
DESIGNER: Alexey Serous
PROJECT NUMBER: 25019443


ARCHIVING CODE: 00240
APPROVED: Alexey Serous
CHECKED: Jere Kalliosalmi
REVISION: STR

DESIGN GROUP: STR


SWECO RAKENNETEKNIikka OY
ILMALANPORTTI 2
00240 HELSINKI
PUH. +358 207 393 000
WWW.SWECO.FI

25019443_Fair_E500


PART LIST FOR ASSEMBLY E51W-1009, MANUFACTURING AMOUNT 2 PIECES						
PART	PROFILE	MATERIAL	LENGTH (mm)	AREA (m ²)	WEIGHT (kg)	PCS
E51WL-1005	PL20X220	S355J2+N	791	0.78	27.3	2
E51WL-1025	PL5X47	S355J2+N	144	0.03	0.3	2
E51WP-1006	W1800-8-20X300	S355J2	8314	23.18	1181.9	1
E51WP-1034	CFRHS150X50X5	S355J2H	8264	3.17	118.7	1
TOTAL:				27.15	1355.7	

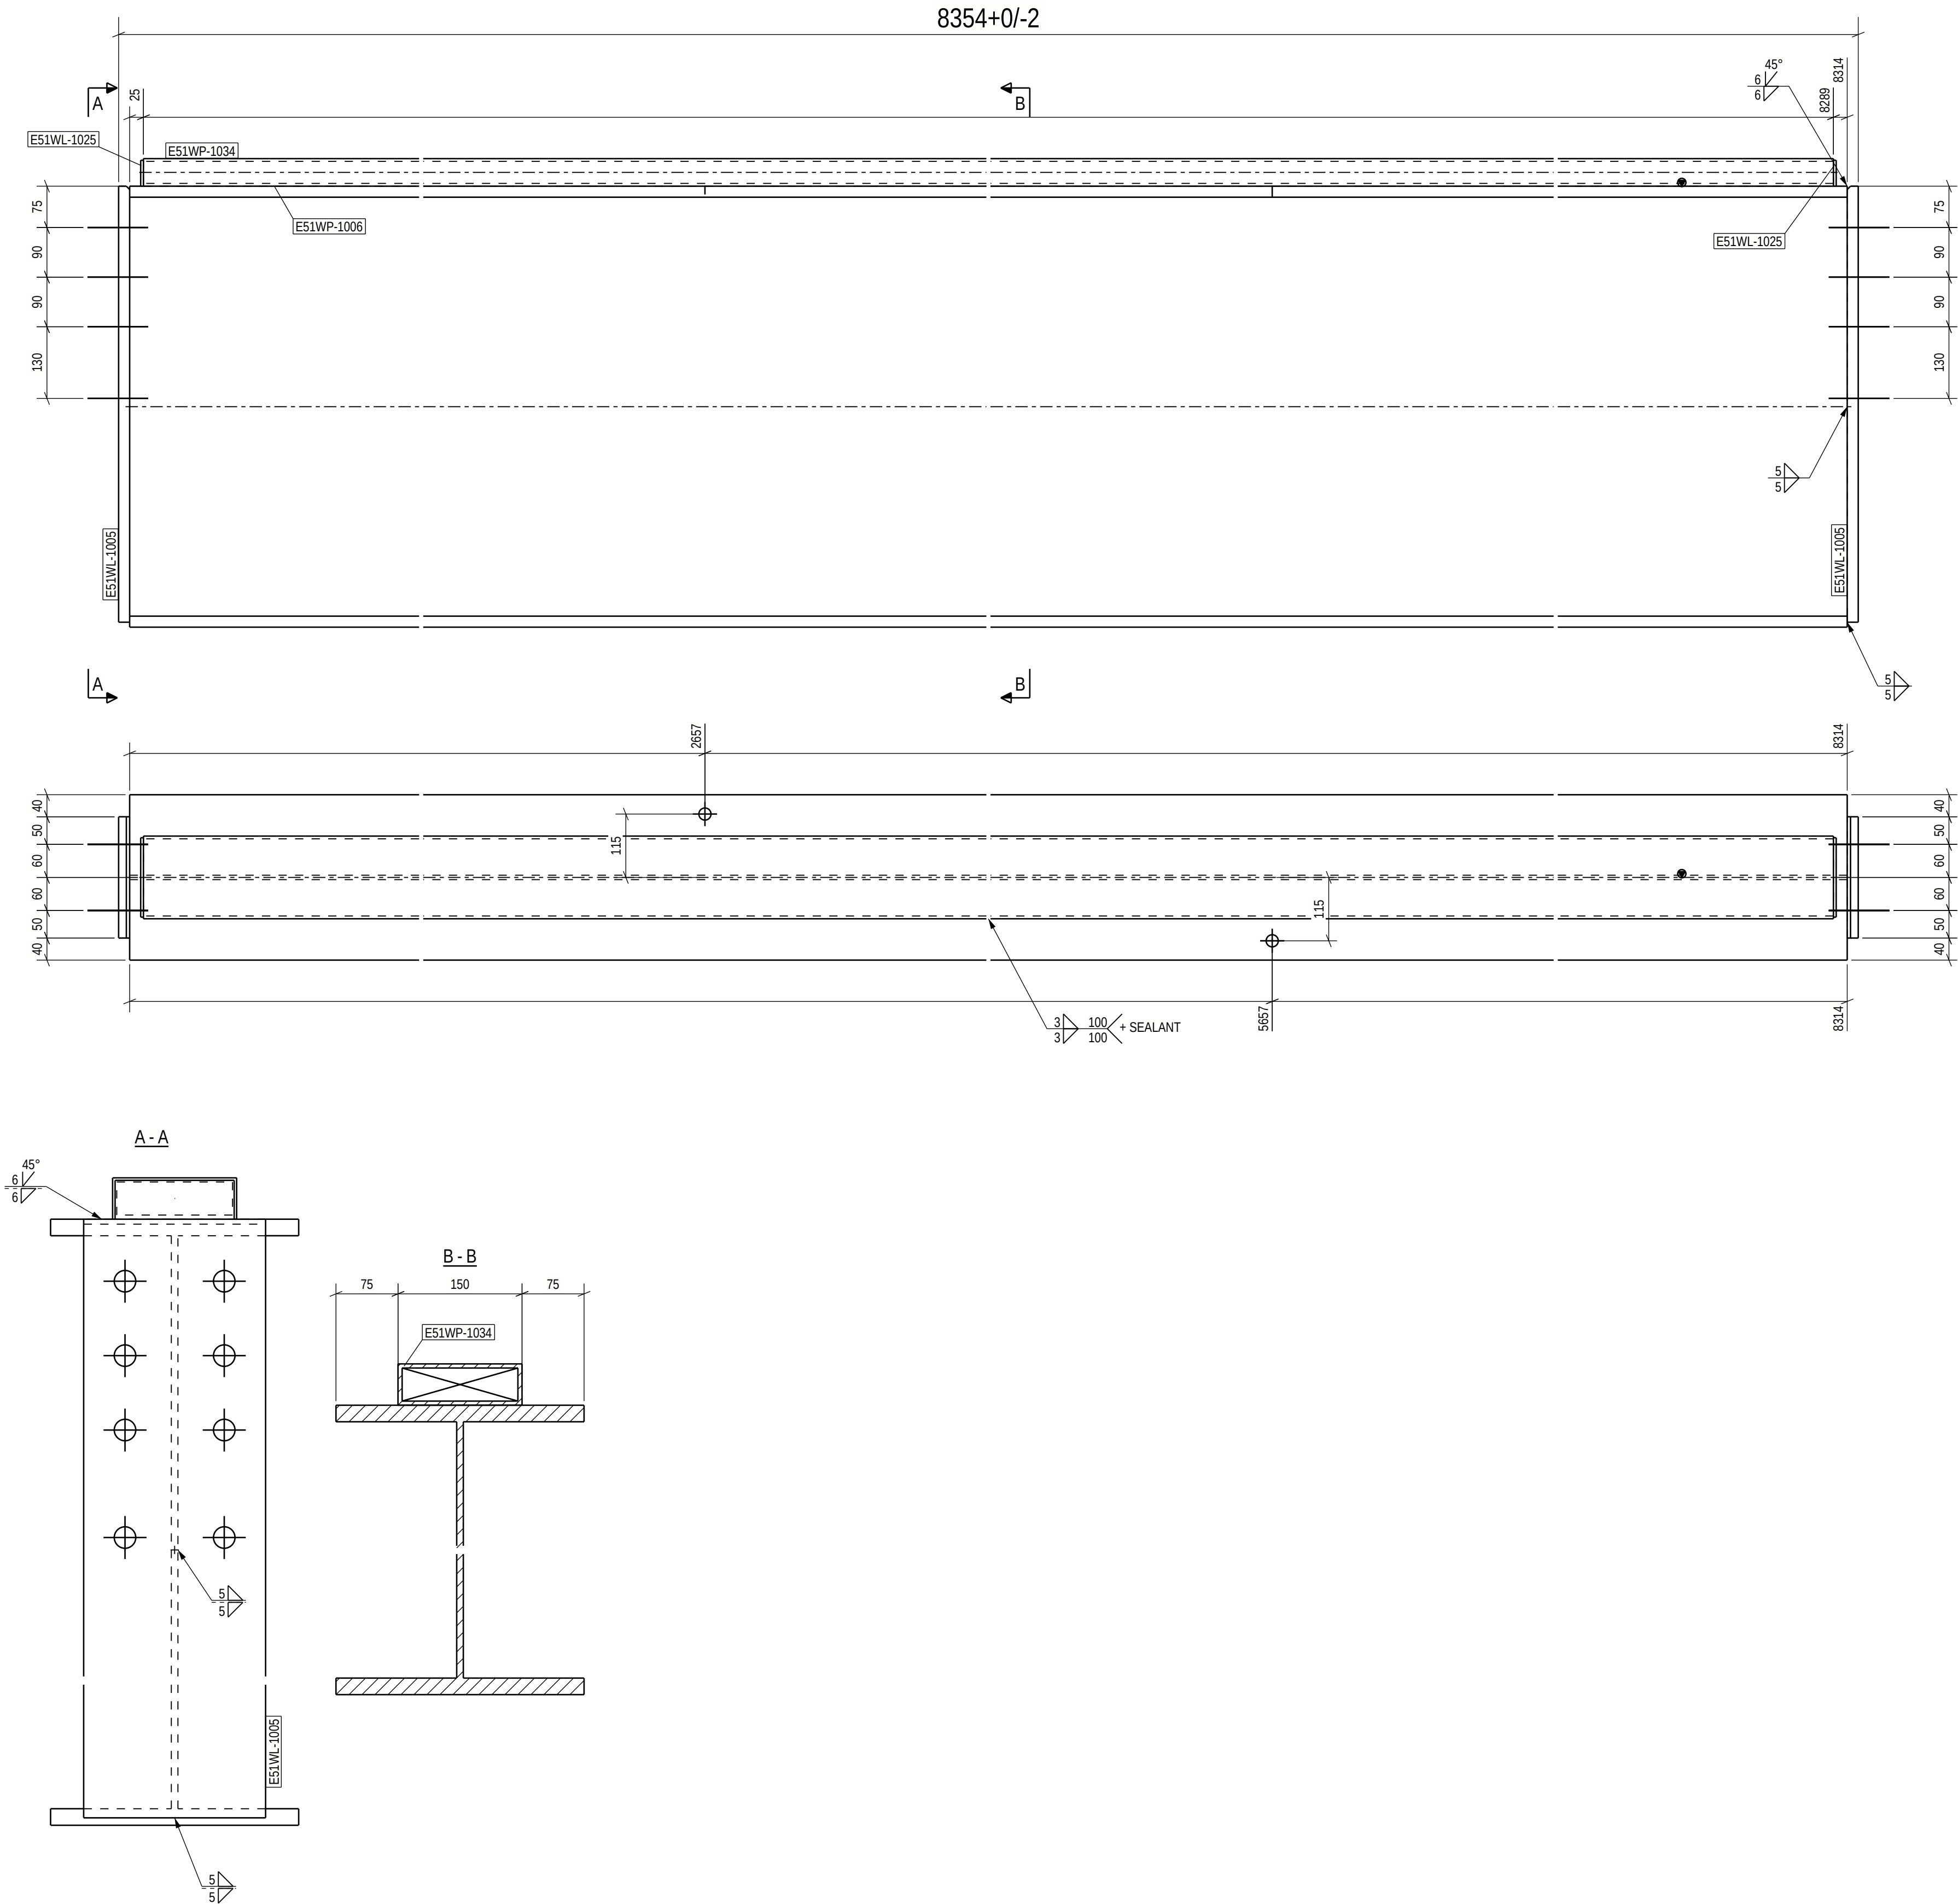

DET 4
Full contact in bearing, requirements acc. to EN 1090-2/6.8 and 11.2.3.5 and project specification
Tolerance for the first bolt group at the end of the beam:

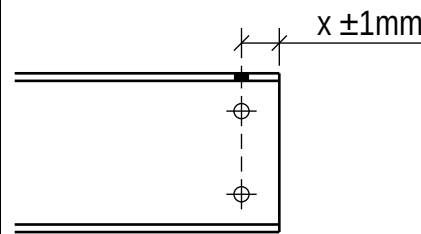

DET 1

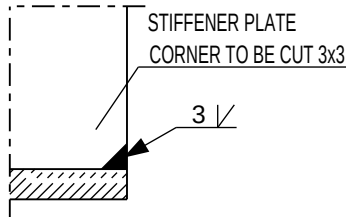

Technical fabrication requirements:		Execution class
Requirements for fabrication, standard EN1090-2, table A.3: EXC2	Fabrication tolerances EN 1090-2, Appendix B	EXC2
Execution Specification document nr 25019443-ICC250-0600-0600-000005	Special fabrication tolerances Project specification/ shown on drwg.	
Surface preparation grade ISO8501-3, grade P2	Weld inspection, requirements EN 1090-2, Table 24, U>0.5	
Surface treatment ISO12944-5	Extent of NDT, after welds	
Additional requirements on surface treatment RAL 7024 (Graphite Gray)	MT-EN1290, 20% of welds	
UT, EN-ISO17640, 20% of welds	Extent of NDT, butt welds	
UT, EN-ISO17640, 100% of welds	UT, EN-ISO17640, 20% of welds	
Requirements on testing Appendix 1 / Project spec.	EN1090-2 Section 6.6.3	
Welds, first specified otherwise EN 9692-1, EN 9692-2	Weld class C, EN ISO 5817	
	Additional material inspection Shown on drwg.	

Approved For Construction



PROJECT NAME
Easpring New Materials Oy
FAIR Phase 1



SWECO RAKENNETEKNIKKA OY
ILMALANPORTTI 2
00240 HELSINKI
PUH. +358 207 393 000
WWW.SWECO.FI

DRAWING CONTENT
ASSEMBLY DRAWING
Beam_WI
E51W-1009

DATE	ARCHIVING CODE	PAGE	DESIGN GROUP
12.06.2026			STR
DESIGNER	APPROVED	CHECKED	REVISION
Alexey Serus	Alexey Serus	Pertti Kolummaaho	Jere Kalliosalmi
PROJECT NUMBER	DWG. NO.		
25019443	E51W-1009		

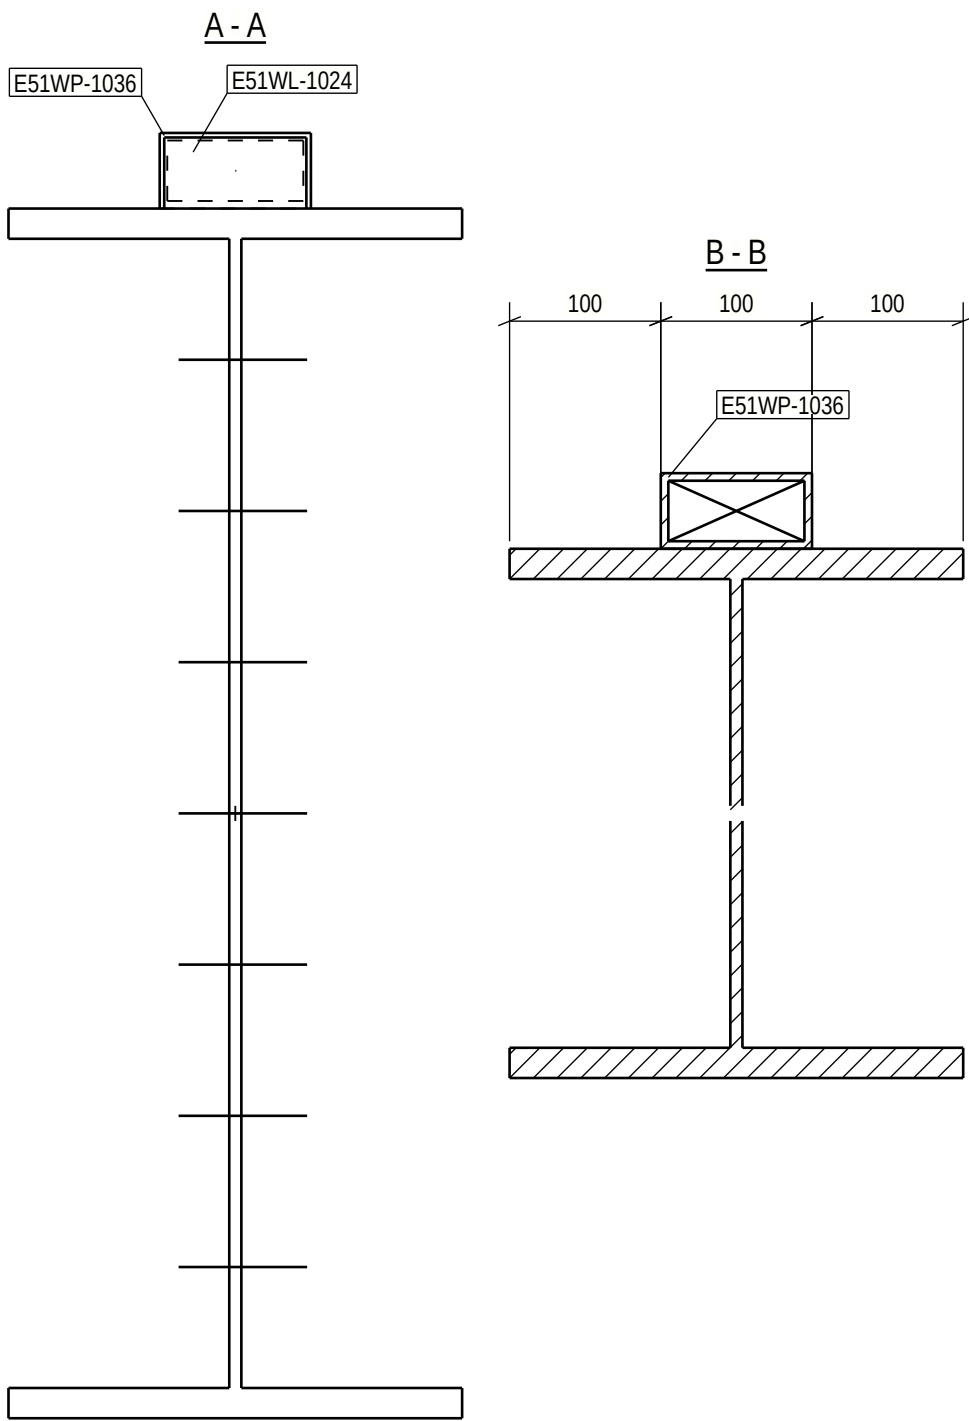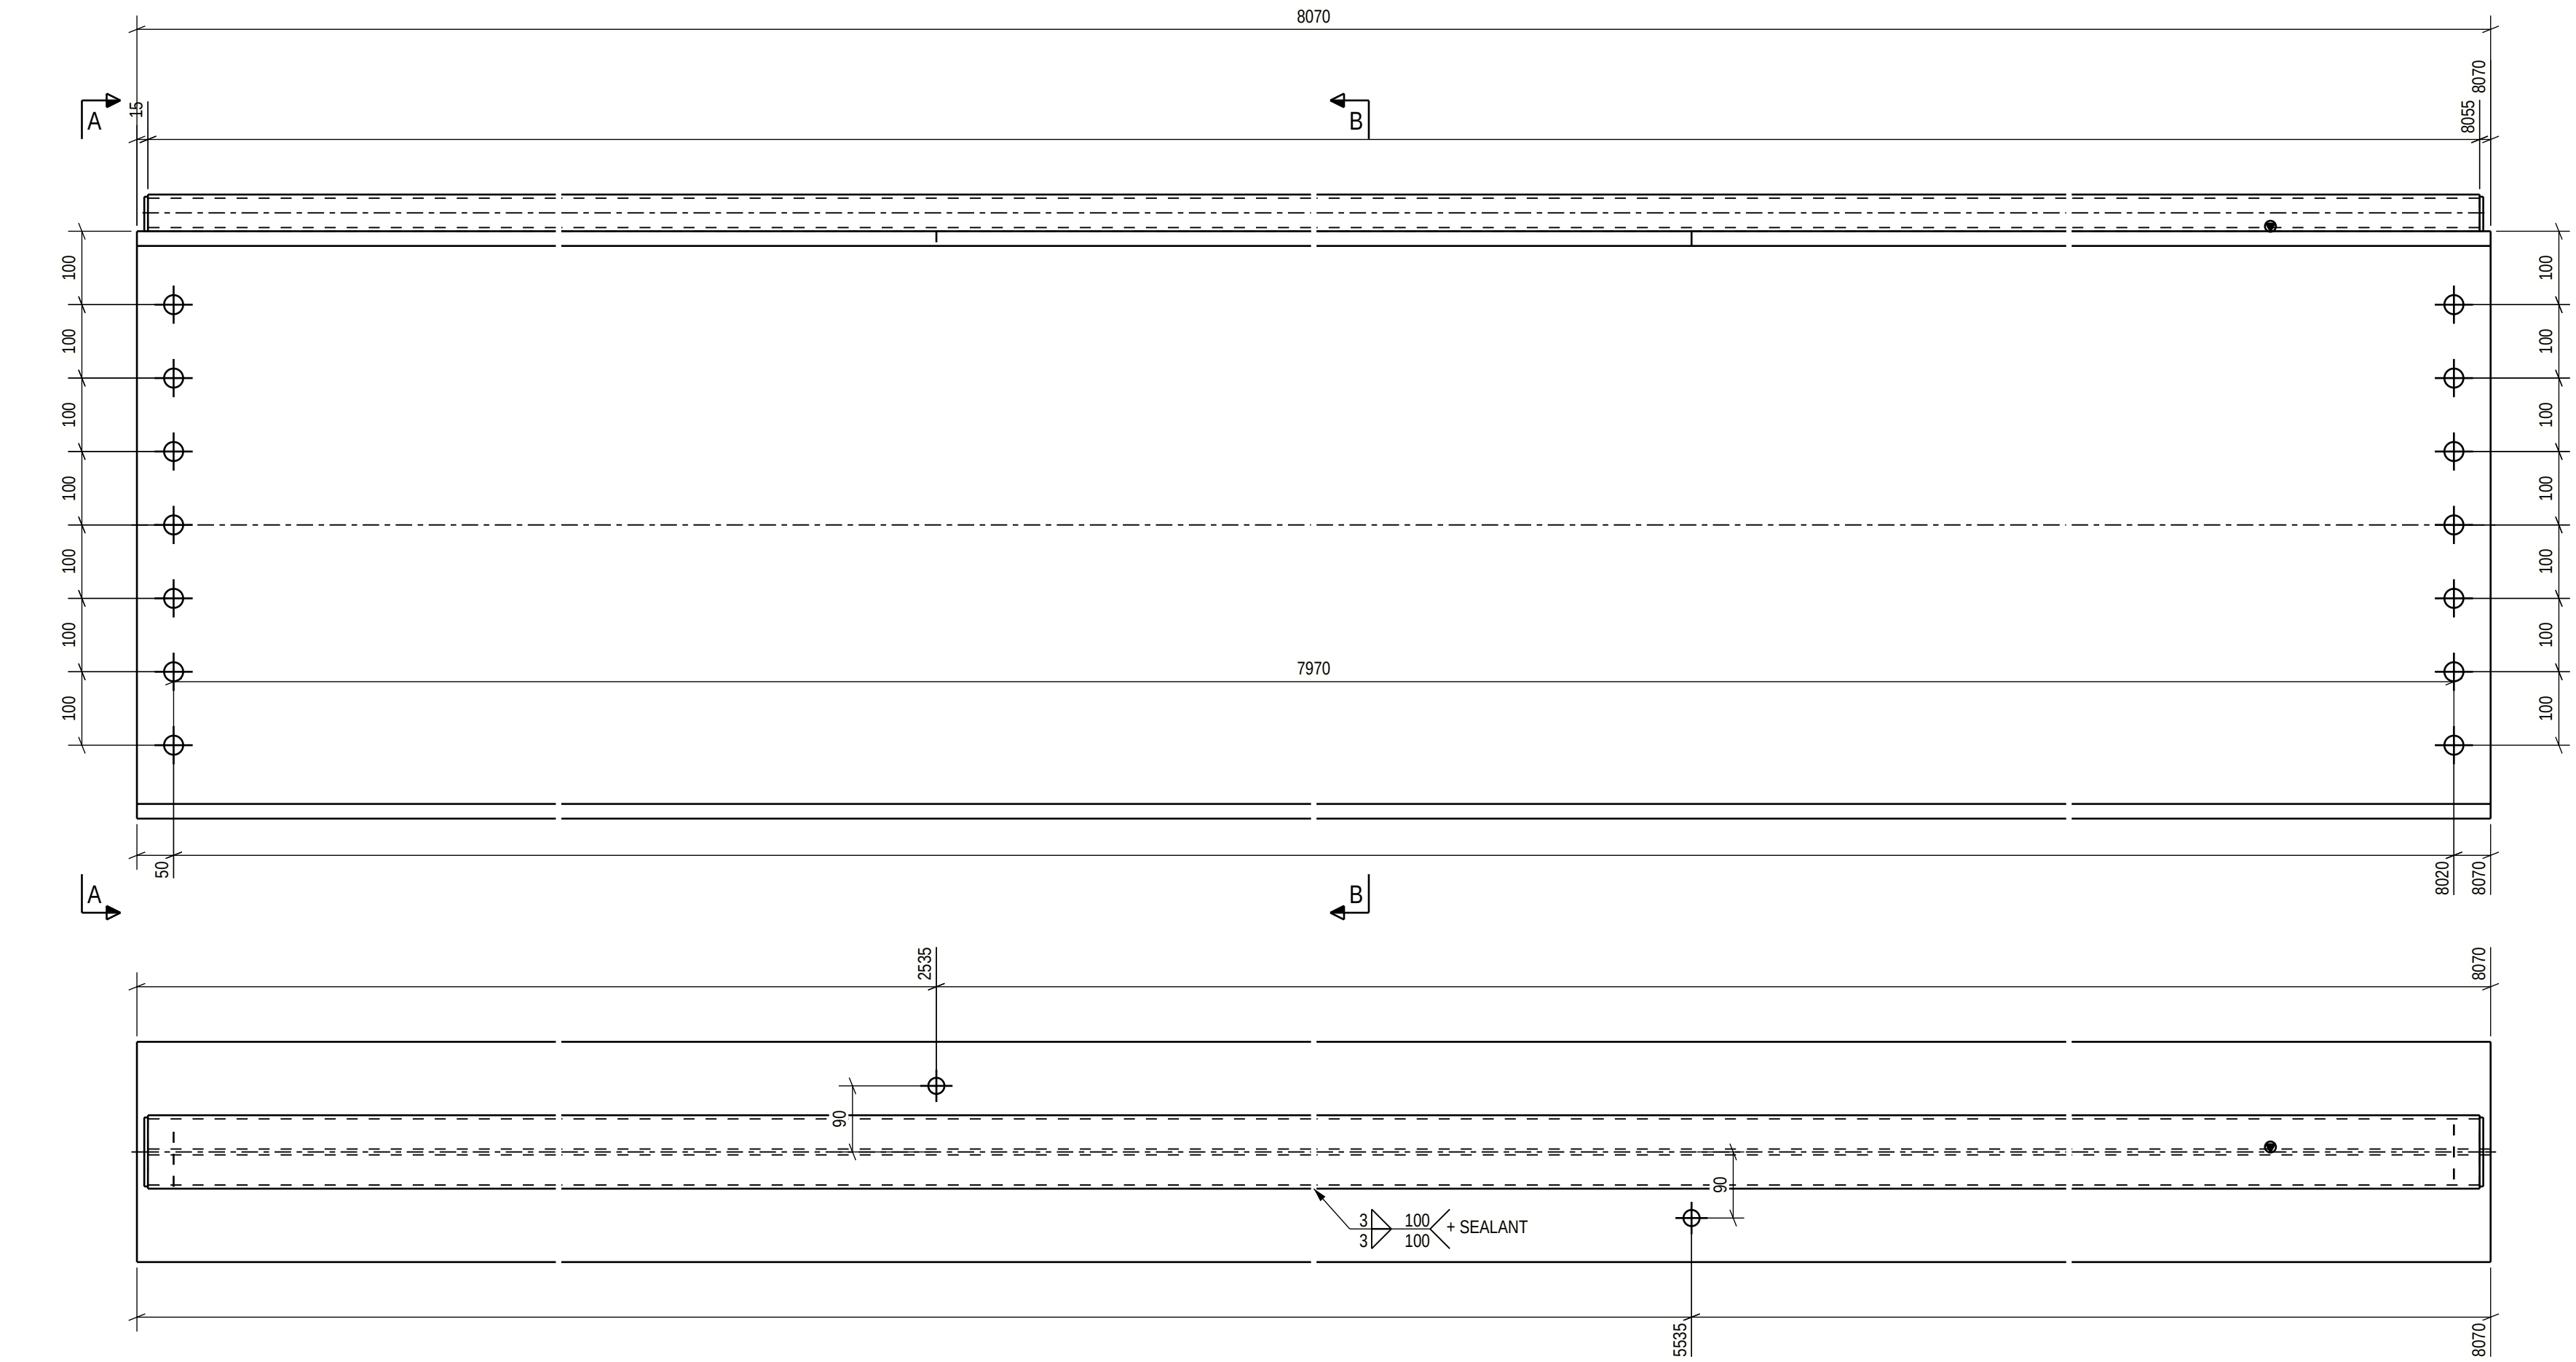

PART LIST FOR ASSEMBLY E51W-1010, MANUFACTURING AMOUNT 5 PIECES						
PART	PROFILE	MATERIAL	LENGTH (mm)	AREA (m2)	WEIGHT (kg)	PCS
E51WL-1024	PLS47	S355J2+N	94	0.02	0.2	2
E51WP-1009	W1800-8-20X300	S355J2	8070	22.50	1147.2	1
E51WP-1036	CFRHS100X50X5	S355J2H	8040	2.28	84.3	1
TOTAL:			24.80	1231.9		

DET 4

Full contact in bearing, requirements acc. to EN 1090-2/6.8 and 11.2.3.5 and project specification

Tolerance for the first bolt group at the end of the beam:

DET 1

Technical fabrication requirements:

EXC2

Requirements for fabrication, standard EN1090-2, table A.3: EXC2

Execution Specification document nr 25019443-ICC250-0600-0660-000005

Surface preparation grade ISO8501-3, grade P2

Surface treatment ISO12944-5

Additional requirements on surface treatment RAL 7024 (Graphite Gray)

Washing of bulk up steel section

Appendix 1 / Project spec:

Welds, first specified otherwise EN 9692-1, EN 9692-2

Fabrication references

EN 1090-2, Appendix B

Project specification/ shown on drwg.

Weld inspection, requirements EN 1090-2, Table 24, U>0.5

Extent of NDT, after welds MT-EN1290, 20% of welds

Extent of NDT, final welds UT, EN-ISO17640, 20% of welds

Extent of NDT for spaces not shown on drawing UT, EN-ISO17640, 100% of welds

Requirements on testing EN1090-2 Section 6.6.3

Weld class C, EN ISO 5817

Additional material inspection Shown on drwg.

Approved For Construction

PROJECT NAME

Easpring New Materials Oy

FAIR Phase 1

DRAWING CONTENT

ASSEMBLY DRAWING

Beam_WI

E51W-1010

DATE

12.06.2026

ARCHIVING CODE

PAGE

DESIGN GROUP

STR

DESIGNER

Alenxey Serus

APPROVED

Perri Kolumaanaho

CHECKED

Jere Kalliosalmi

REVISION

PROJECT NUMBER

25019443

DWG. NO.

E51W-1010

SWECO

Sustainable engineering and design


SWECO RAKENNETEKNIikka OY

ILMALANPORTTI 2


00240 HELSINKI


PUH. +358 207 393 000

WWW.SWECO.FI

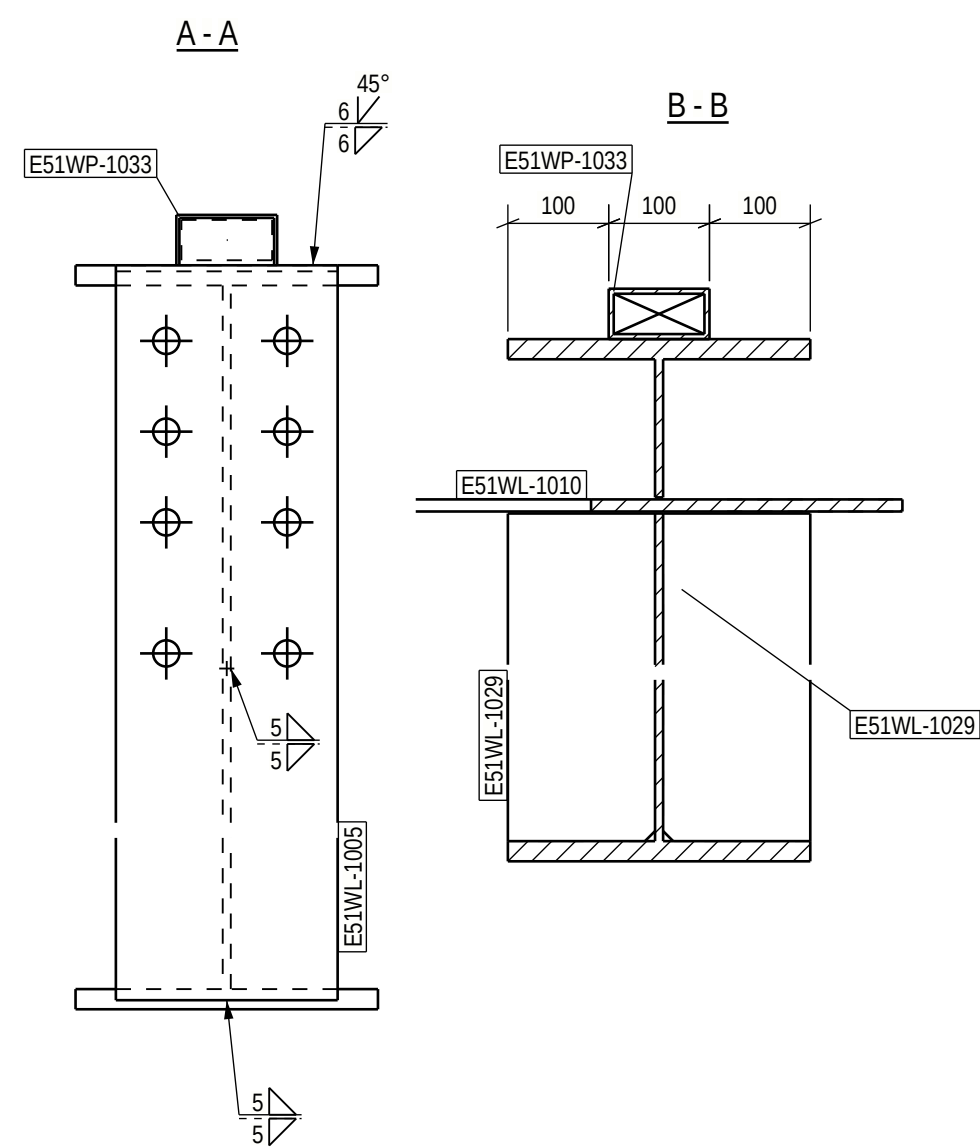


Approved For Construction

 PROJECT NAME Easpring New Materials Oy FAIR Phase 1				DRAWING CONTENT ASSEMBLY DRAWING Beam_WI E51W-1011	
 SWECO Sustainable engineering and design	SWECO RAKENNETEKNIIKKA OY ILMALAINPORTTI 2 00040 HELSINKI		DATE 12.06.2026	ARCHIVING CODE 12.06.2026	PAGE
	PLN : -550 207 393 000 www.sweco.fi		DRAWN Alexy Serus	DESIGNER Alexy Serus	APPROVED Pentti Kuormanaho
			PROJECT NUMBER 25019443	CHECKED Jere Kallioasari	REVISION E51W-1011 00000000000000000000

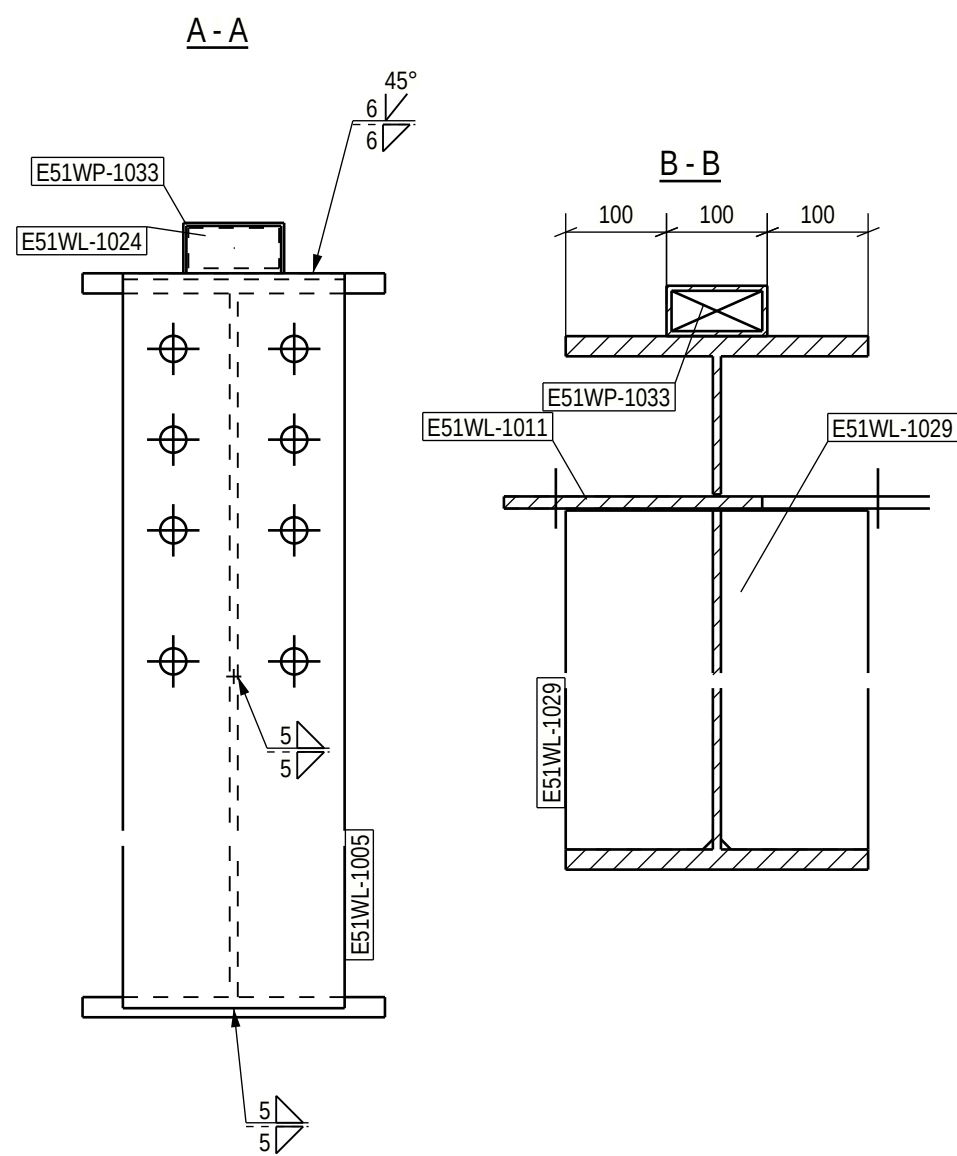


PART LIST FOR ASSEMBLY E51W-1012. MANUFACTURING AMOUNT 1 PIECES						
PART	PROFILE	MATERIAL	LENGTH [mm]	AREA [m ²]	WEIGHT [kg]	PCS
E51W-1005	PL20X220	S355J2+N	791	0.78	27.3	2
E51W-1011	PL12X247	S355J2+N	94	0.46	20.6	1
E51W-1024	PL5X47	S355J2+N	904	0.02	0.2	2
E51W-1029	PL10X146	S355J2+N	607	0.38	7.0	2
E51WP-1013	W800-8-20X300	S355J2	8314	23.17	1181.9	1
E51WP-1033	CFRH50X100X50X5	S355J2H	8264	2.34	86.7	1
TOTAL:				27.15	1358.0	

DET 4
Full contact in bearing, requirements
acc. to EN 1090-2/6.8 and 11.2.3.5
and project specification

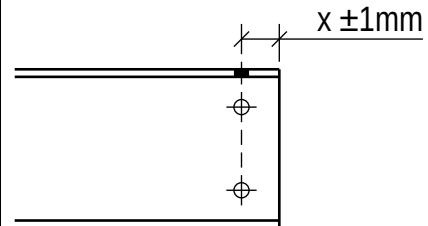


DET 1

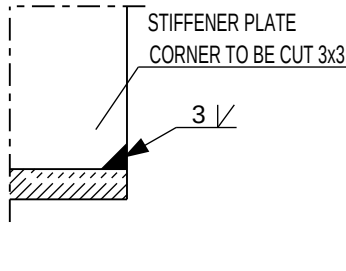

Technical fabrication requirements:		Execution class
Requirements for fabrication, standard EN 1090-2, table A3 : EXC2 Execution Specification document or EN1994-3/EN1994-30-0600-0600-000005 ISO6801-3, grade PR2 ISO12944-5 Additional requirements on surface treatment C3,07, EPPUR 2402 RAL 7024 (Granitine Gray) Welding of all parts in accordance with Appendix 1 / Project spec Welds, first specified inspection EN 9692-1, EN 9692-2	Fabrication instructions EN 1090-2, Appendix B Special fabrication instructions Project specifications/ shown on dwg. Welds, first specified inspection EN 1090-2, Table 24, U>0,5 Steel of EN 10025 MT-EN1990-2, 20% of welds Exent of HT, not welds EN 10051/7840, 20% of welds Exent of HT, not in section on drawing EN 10051/7840, 100% of welds Requirements on rolling EN 9692-2 Section 6.6.3 Weld class EN C EN 5817	EXC2 Additional material inspection Shown on drawing

Approved For Construction


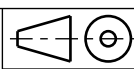


DRAWING CONTENT
ASSEMBLY DRAWING
Beam_WI
E51W-1012



SWECO RAKENNETEKNIikka OY
ILMALANPORTTI 2
00240 HELSINKI
PUH. +358 207 393 000
www.sweco.fi


DATE 12.06.2026	ARCHIVING CODE	PAGE	DESIGN GROUP STR
DRAWN Alexy Serous	DESIGNER Alexy Serous	APPROVED Pertti Kouvumaaanaho	CHECKED Jere Kalliosalo
PROJECT NUMBER 25019443	DWG. NO. E51W-1012	REVISION	

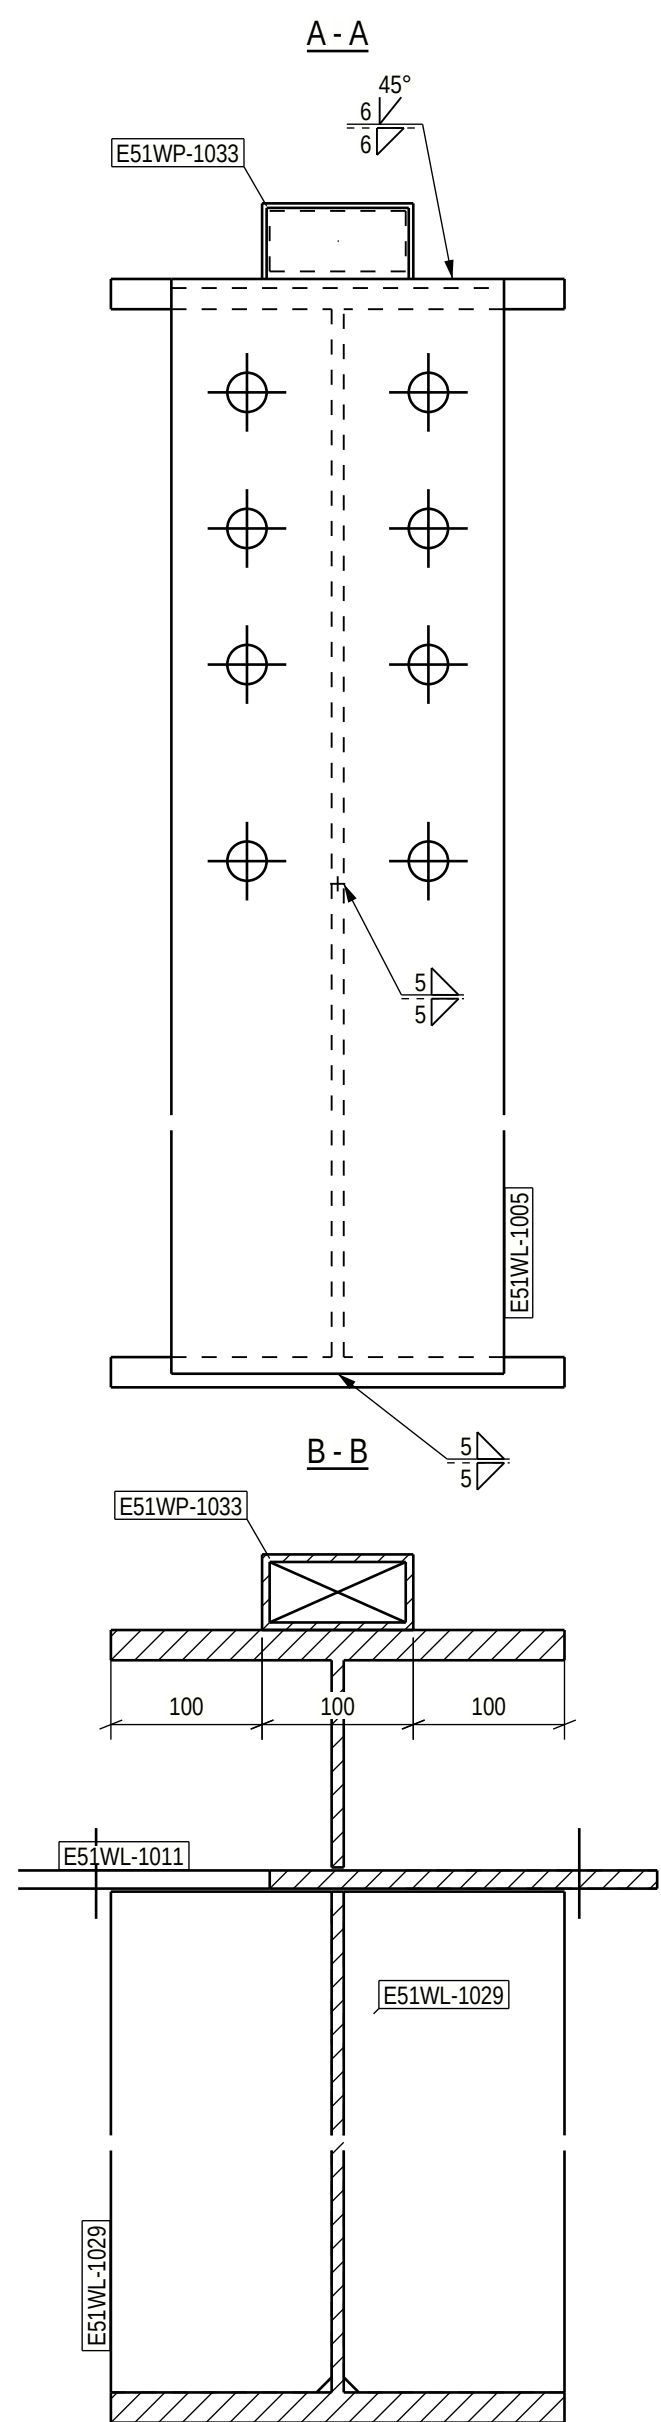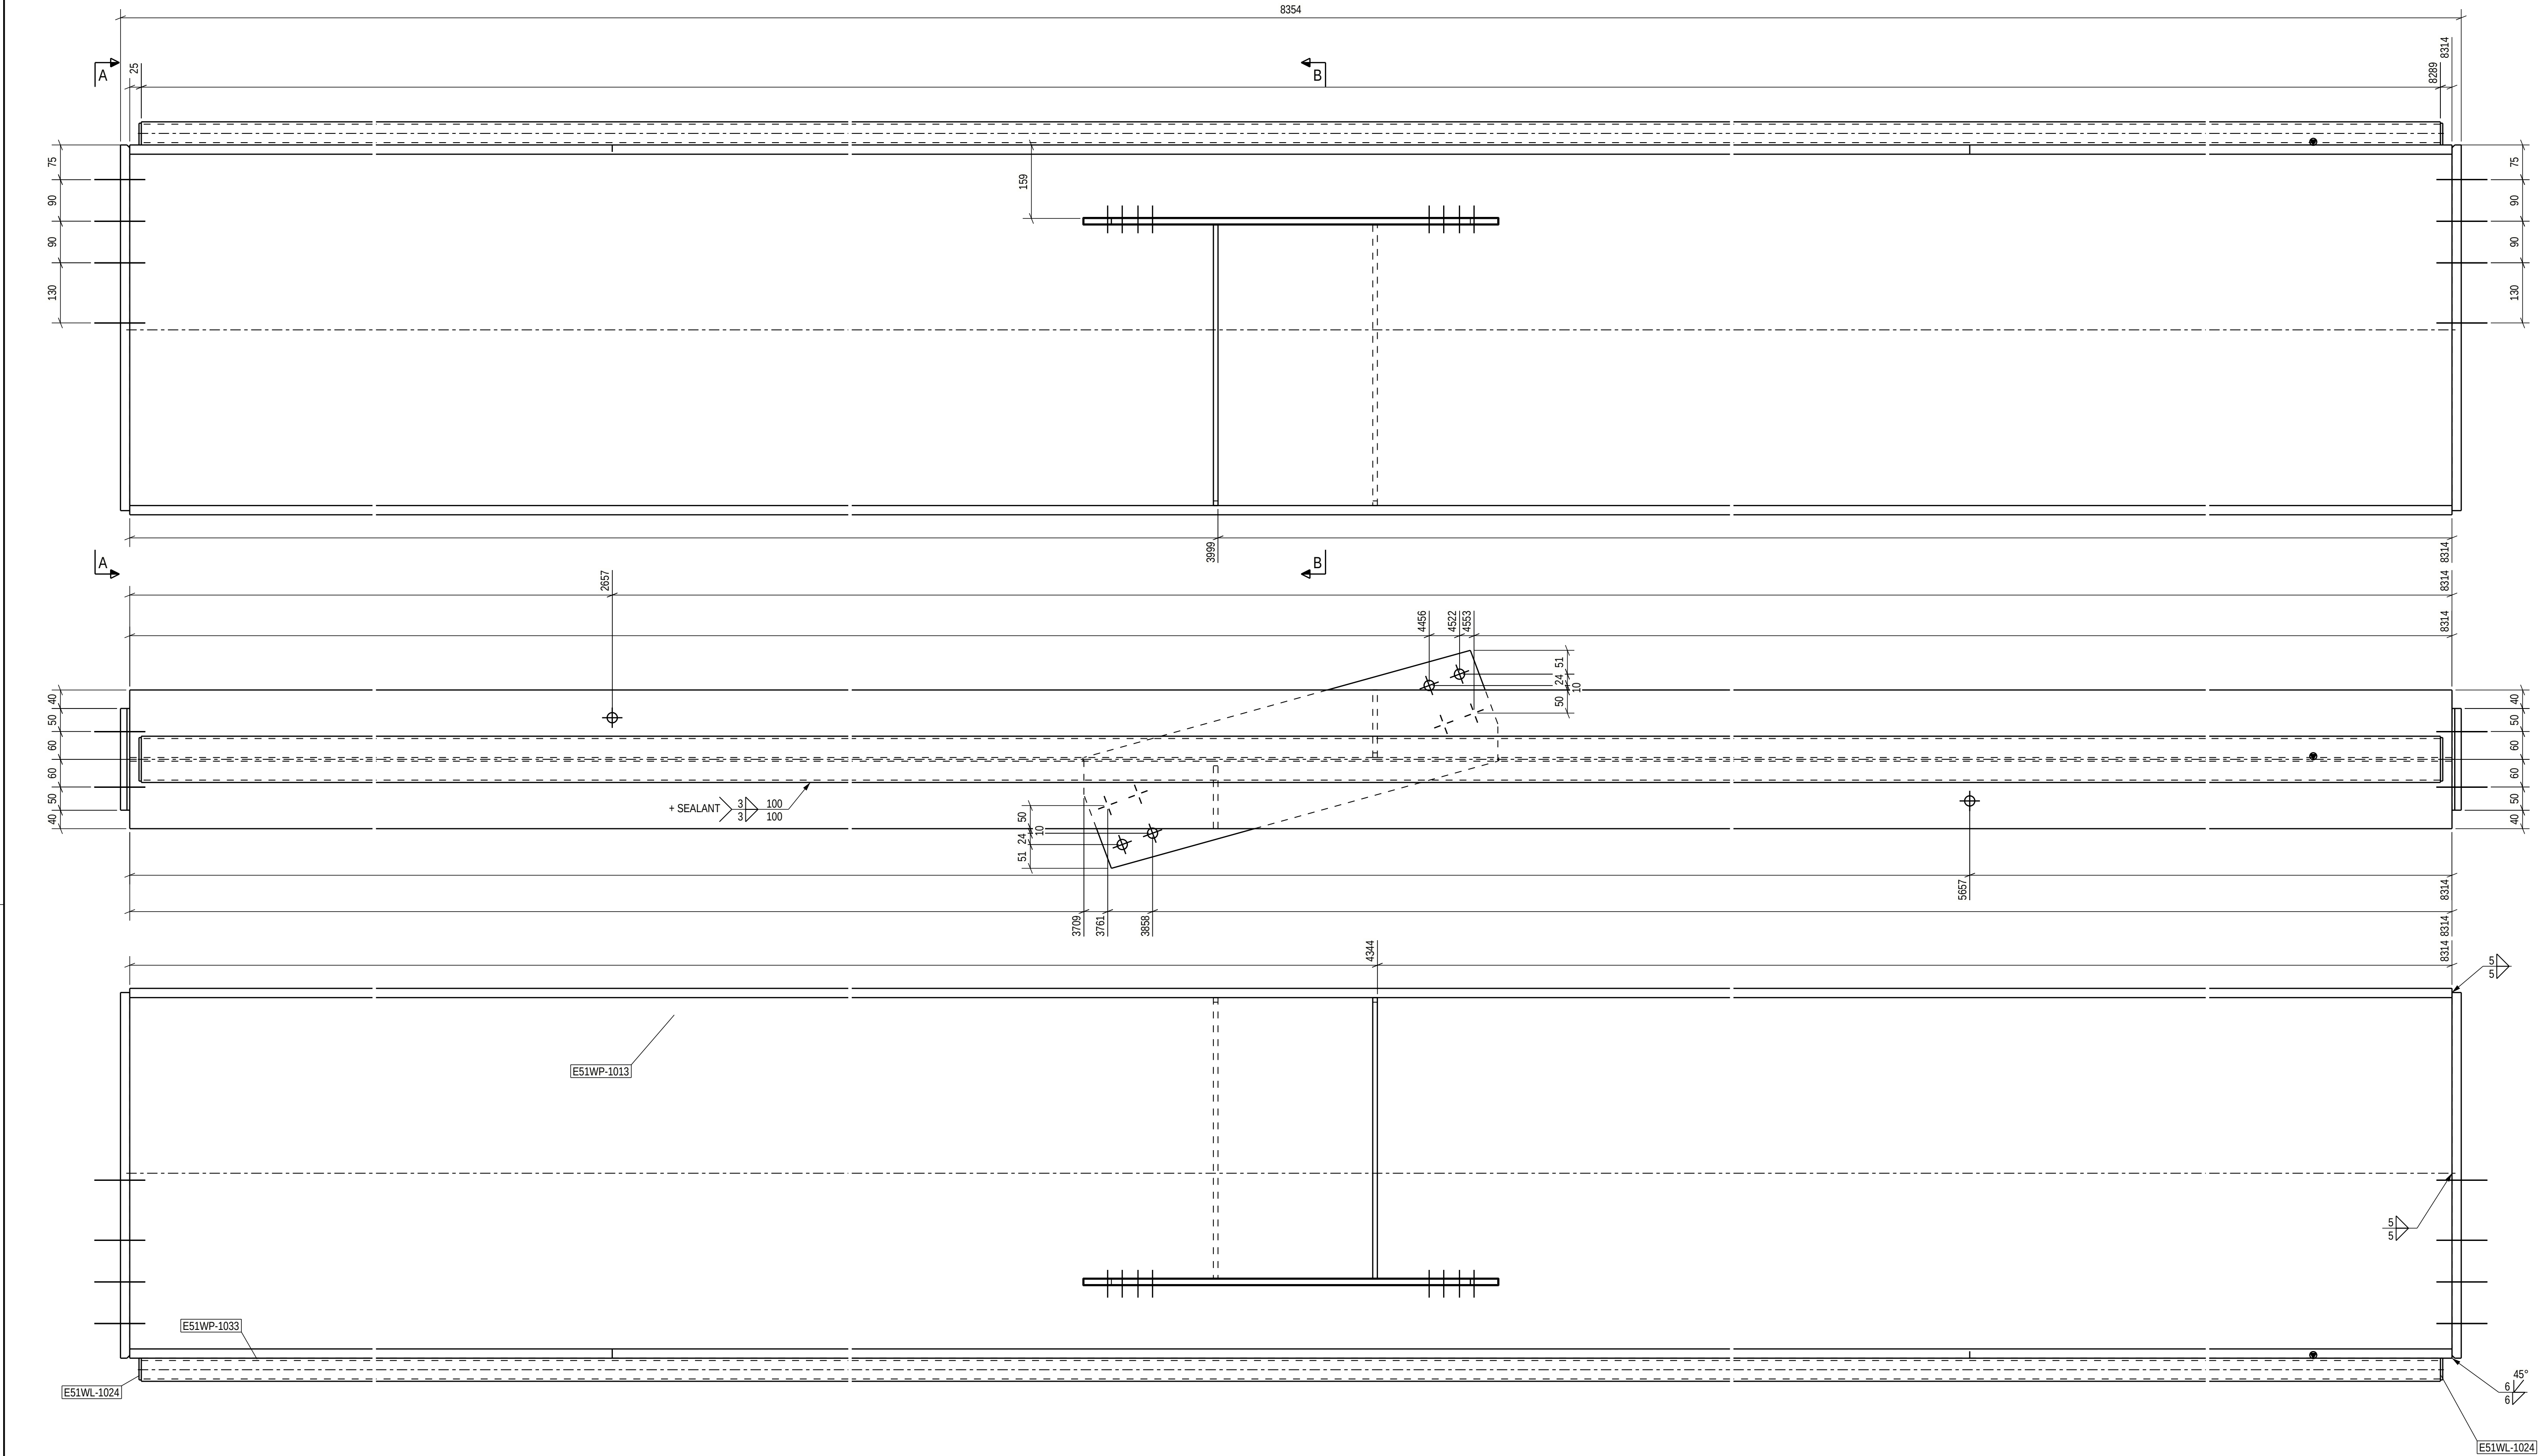


PART LIST FOR ASSEMBLY E51W-1013, MANUFACTURING AMOUNT 1 PIECES						
PART	PROFILE	MATERIAL	LENGTH [mm]	AREA [m ²]	WEIGHT [kg]	PCS
E51WL-1005	PL20X220	S355J2+N	791	0.78	27.3	2
E51WL-1011	PL12X247	S355J2+N	904	0.46	20.6	1
E51WL-1024	PL5X47	S355J2+N	94	0.02	0.2	2
E51WL-1029	PL10X146	S355J2+N	607	0.38	7.0	2
E51WP-1013	WI800-8-20X300	S355J2	8314	23.17	1181.9	1
E51WP-1033	CFRHS100X50X5	S355J2H	8264	2.34	86.7	1
TOTAL:				27.15	1358.0	

DET 4
Full contact in bearing, requirements acc. to EN 1090-2/6.8 and 11.2.3.5 and project specification

Tolerance for the first bolt group at the end of the beam:

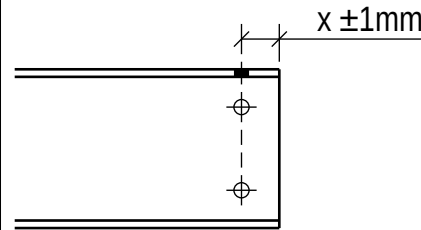

DET 1

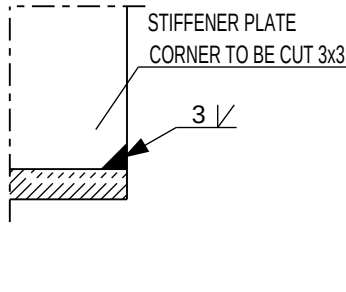

Technical fabrication requirements:		EXC2
Requirements for fabrication, standard	Fabrication tolerances	
EN1090-2, table A.3: EXC2	EN 1090-2, Appendix B	
Execution Specification document nr	Special fabrication tolerances	
25019443-ICC250-0600-0600-000005	Project specification/ shown on drwg.	
Surface preparation grade	Weld inspection, requirements	
ISO8501-3, grade P2	EN 1090-2, Table 24, U>0.5	
Surface treatment	Extent of NDT, after welds	
ISO12944-5	MT-EN1290, 20% of welds	
Additional requirements on surface treatment	Extent of NDT, butt welds	
RAL 7024 (Graphite Gray)	UT, EN-ISO17640, 20% of welds	
C3.07, EPPUR 240/2	UT, EN-ISO17640, 100% of welds	
Grading	Requirements on testing	
Appendix 1 / Project spec.	EN1090-2 Section 6.6.3	
Welds, first specified otherwise	Weld class	
EN 9692-1, EN 9692-2	C, EN ISO 5817	
	Additional material inspection	
	Shown on drwg.	

Approved For Construction



PROJECT NAME
Easpring New Materials Oy
FAIR Phase 1



SWECO RAKENNETEKNIKKÄ OY
ILMALANPORTTI 2
00240 HELSINKI
PUH. +358 207 393 000
WWW.SWECO.FI

DRAWING CONTENT
ASSEMBLY DRAWING
Beam_WI
E51W-1013

DATE	ARCHIVING CODE	PAGE	DESIGNER	APPROVED	CHECKED	DESIGN GROUP
12.06.2026			Aleney Serus	Perri Kolumaanaho	Jere Kalliosalmi	STR
PROJECT NUMBER		DWG. NO.		REVISION		
25019443				E51W-1013		

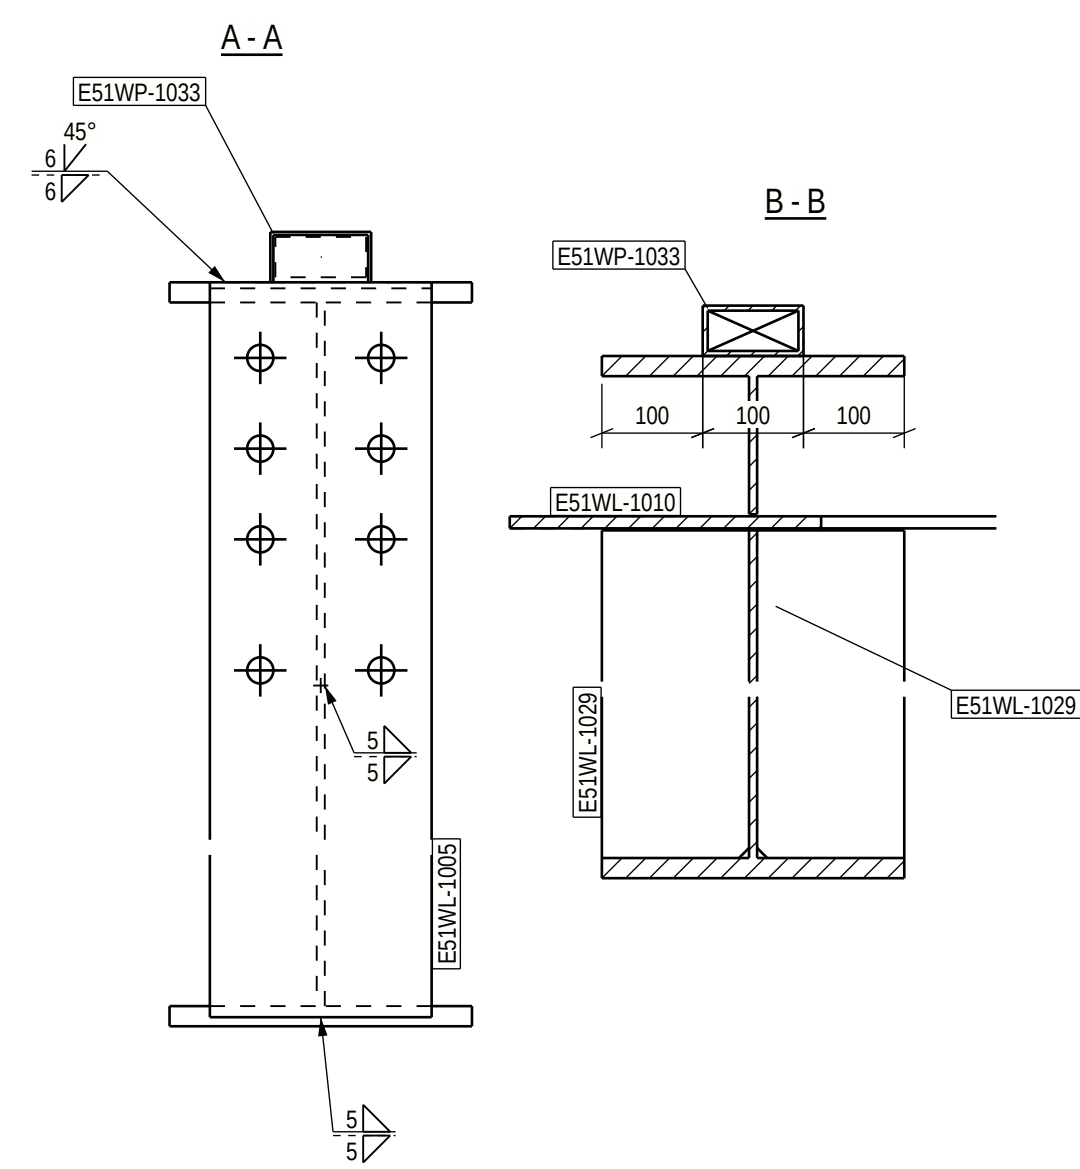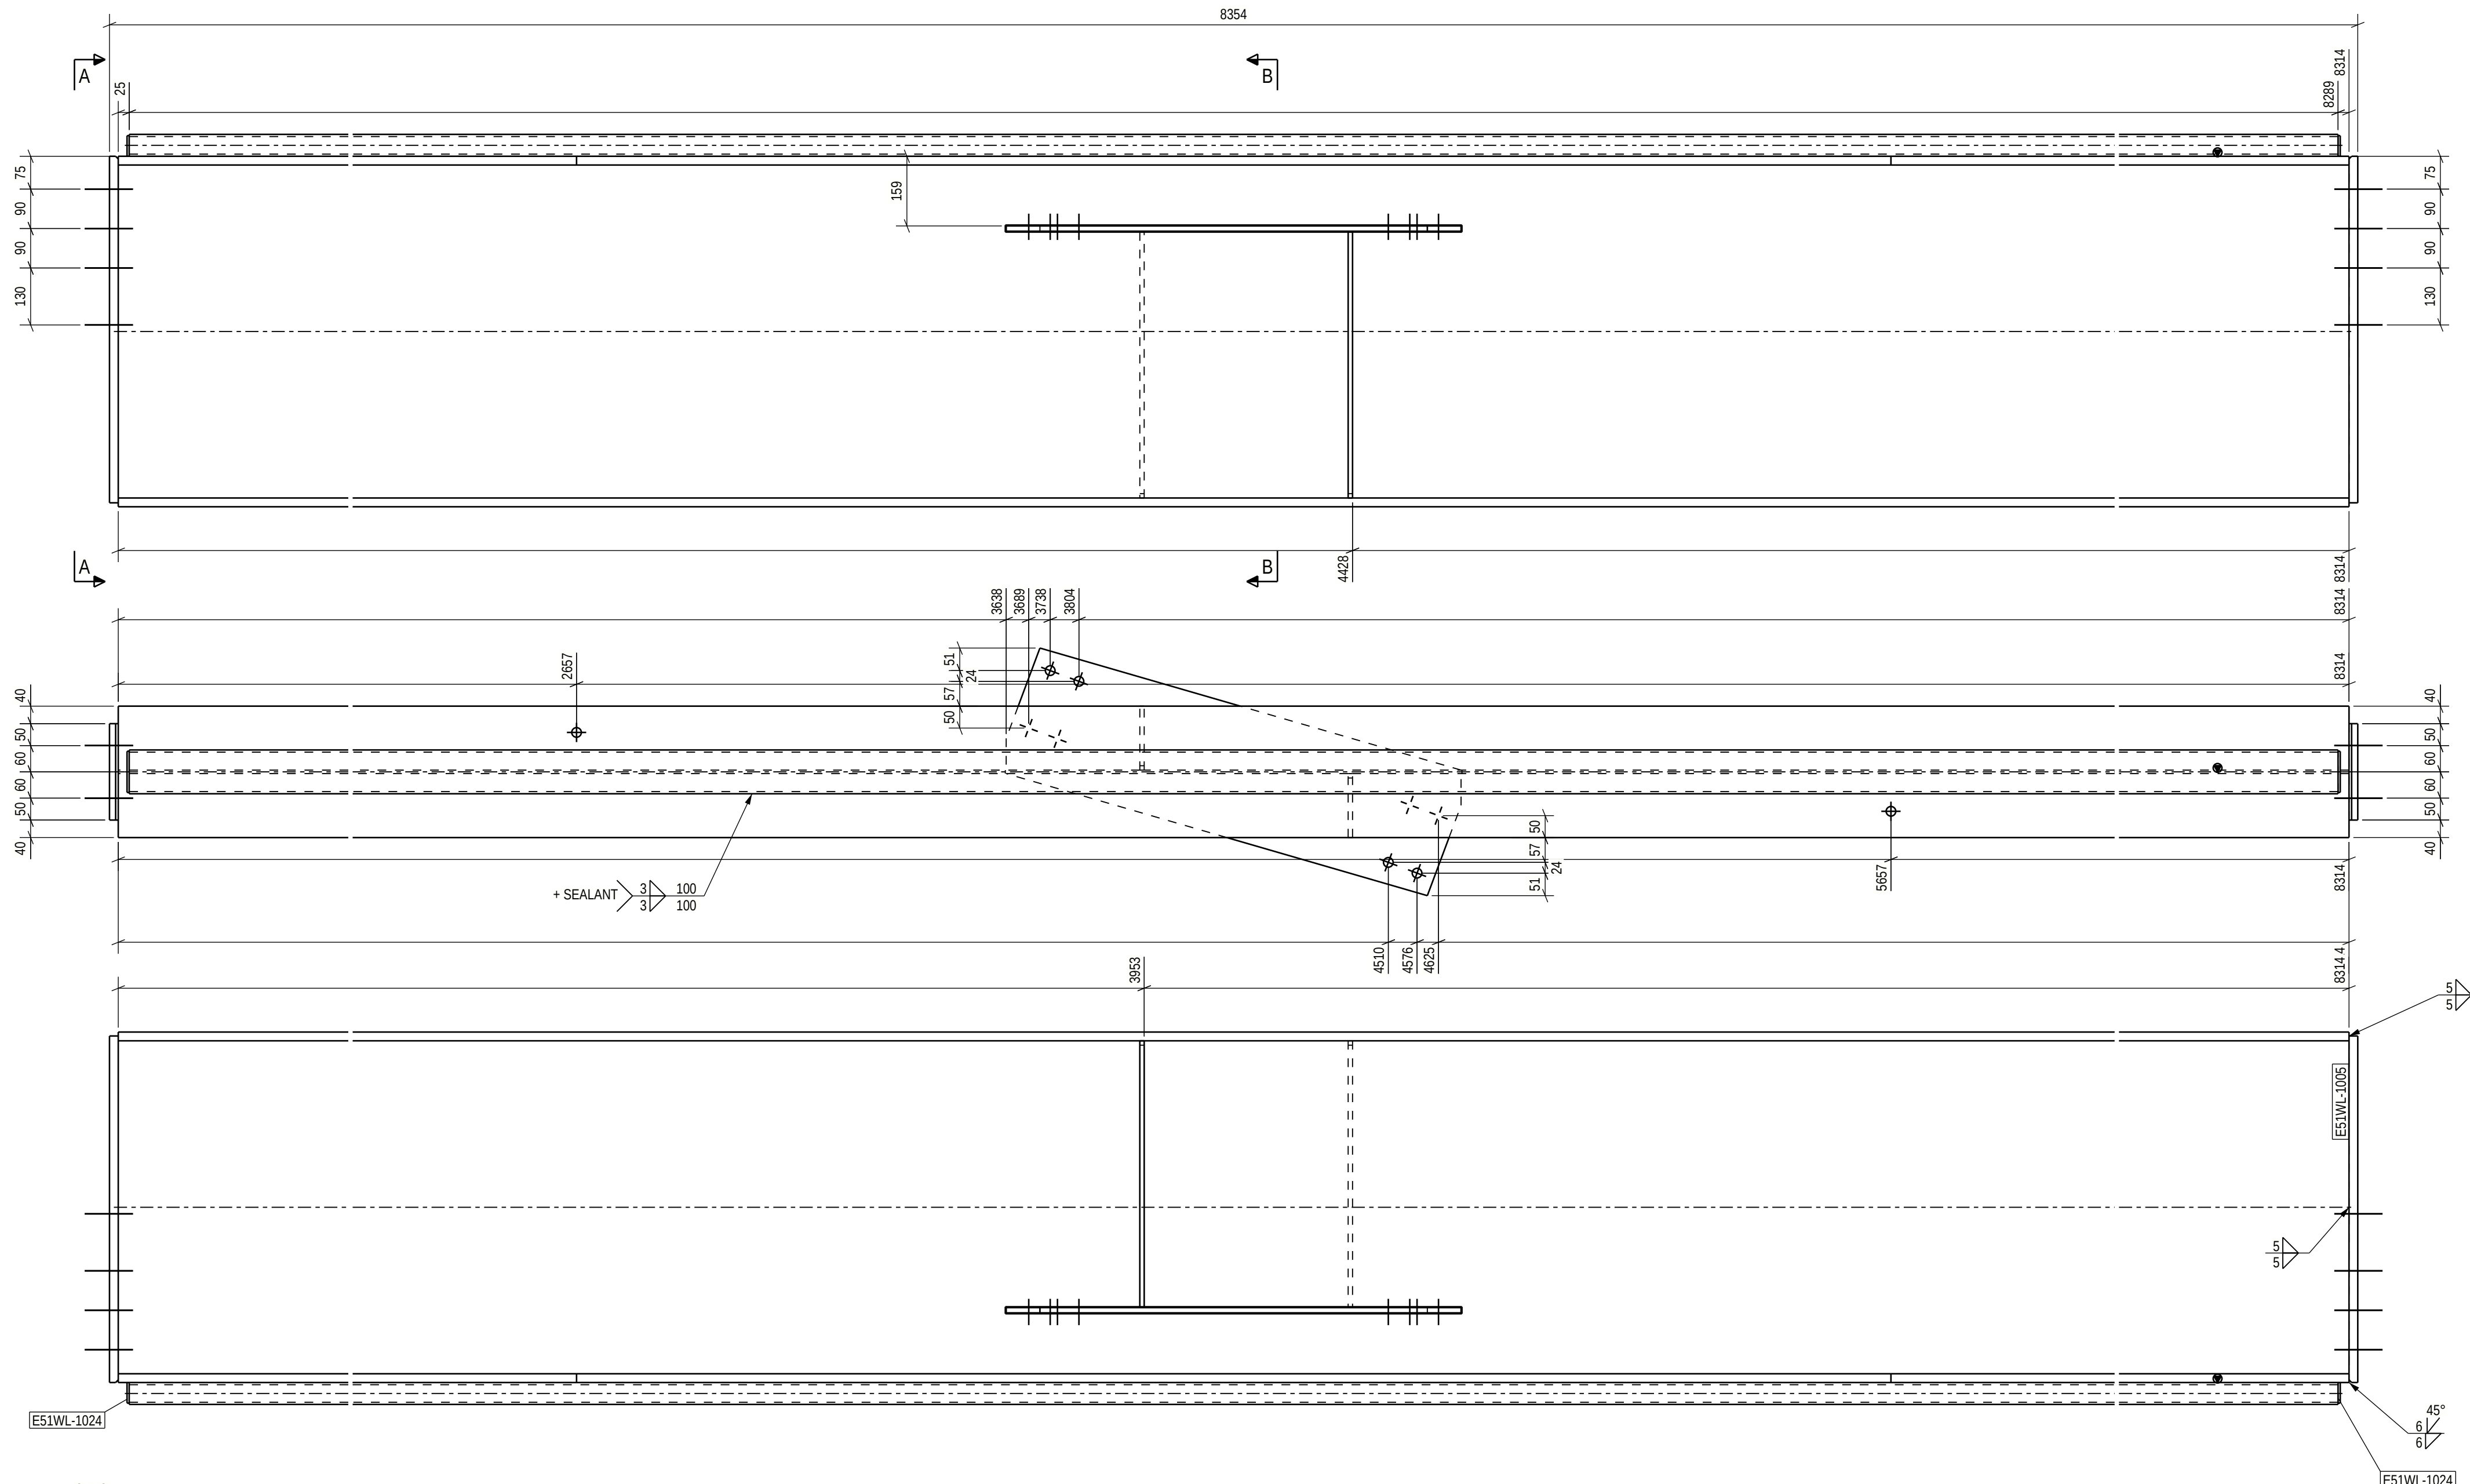

PART LIST FOR ASSEMBLY E51W-1014, MANUFACTURING AMOUNT 1 PIECES						
PART	PROFILE	MATERIAL	LENGTH [mm]	AREA [m ²]	WEIGHT [kg]	PCS
E51WL-1005	PL20X220	S355J2+N	791	0.78	27.3	2
E51WL-1010	PL12X297	S355J2+N	1040	0.64	28.6	1
E51WL-1024	PL5X47	S355J2+N	94	0.02	0.2	2
E51WL-1029	PL10X146	S355J2+N	607	0.38	7.0	2
E51WP-1011	WI800-8-20X300	S355J2	8314	23.17	1181.9	1
E51WP-1033	CFRHS100X50X5	S355J2H	8264	2.34	86.7	1
TOTAL:				27.32	1366.0	

DET 4
Full contact in bearing, requirements acc. to EN 1090-2/6.8 and 11.2.3.5 and project specification

Tolerance for the first bolt group at the end of the beam:

x ±1mm

DET 1

EXC2

Technical fabrication requirements:		Execution class
Requirements for fabrication, standard	EN 1090-2, table A.3: EXC2	Fabrication tolerances
Execution Specification document nr	25019443-ICC250-0600-0660-000005	Special fabrication tolerances
Surface preparation grade	ISO 8501-3, grade P2	Project specification/ shown on drwg.
Surface treatment	ISO 12944-5	Weld inspection requirements
Additional requirements on surface treatment	C3.07, EPPUR 240/2	EN 1090-2, Table 24, U>0.5
Coating	RAL 7024 (Graphite Gray)	Extent of NDT, after welds
Welding of bulk up steel section	Appendix 1 / Project spec.	MT-EN1290, 20% of welds
Welds, first specified otherwise	EN 9692-1, EN 9692-2	Extent of NDT, butt welds
		UT, EN-ISO17640, 20% of welds
		UT, EN-ISO17640, 100% of welds
		Requirements on testing
		EN1090-2 Section 6.6.3
		Weld class
		C, EN ISO 5817
		Additional material inspection
		Shown on drwg


Approved For Construction

PROJECT NAME: Easpring New Materials Oy
FAIR Phase 1

SWECO
Sustainable engineering and design

ILMALANPORTTI 2
00240 HELSINKI
PUH. +358 207 393 000
WWW.SWECO.FI


DRAWING CONTENT			
DATE	ARCHIVING CODE	PAGE	DESIGN GROUP
12.06.2026			STR
DESIGNER	APPROVED	CHECKED	REVISION
Alexey Serov	Alexey Serov	Pertti Kolumaanaho	Jere Kalliosalmi
PROJECT NUMBER	DWG. NO.		
25019443	E51W-1014		

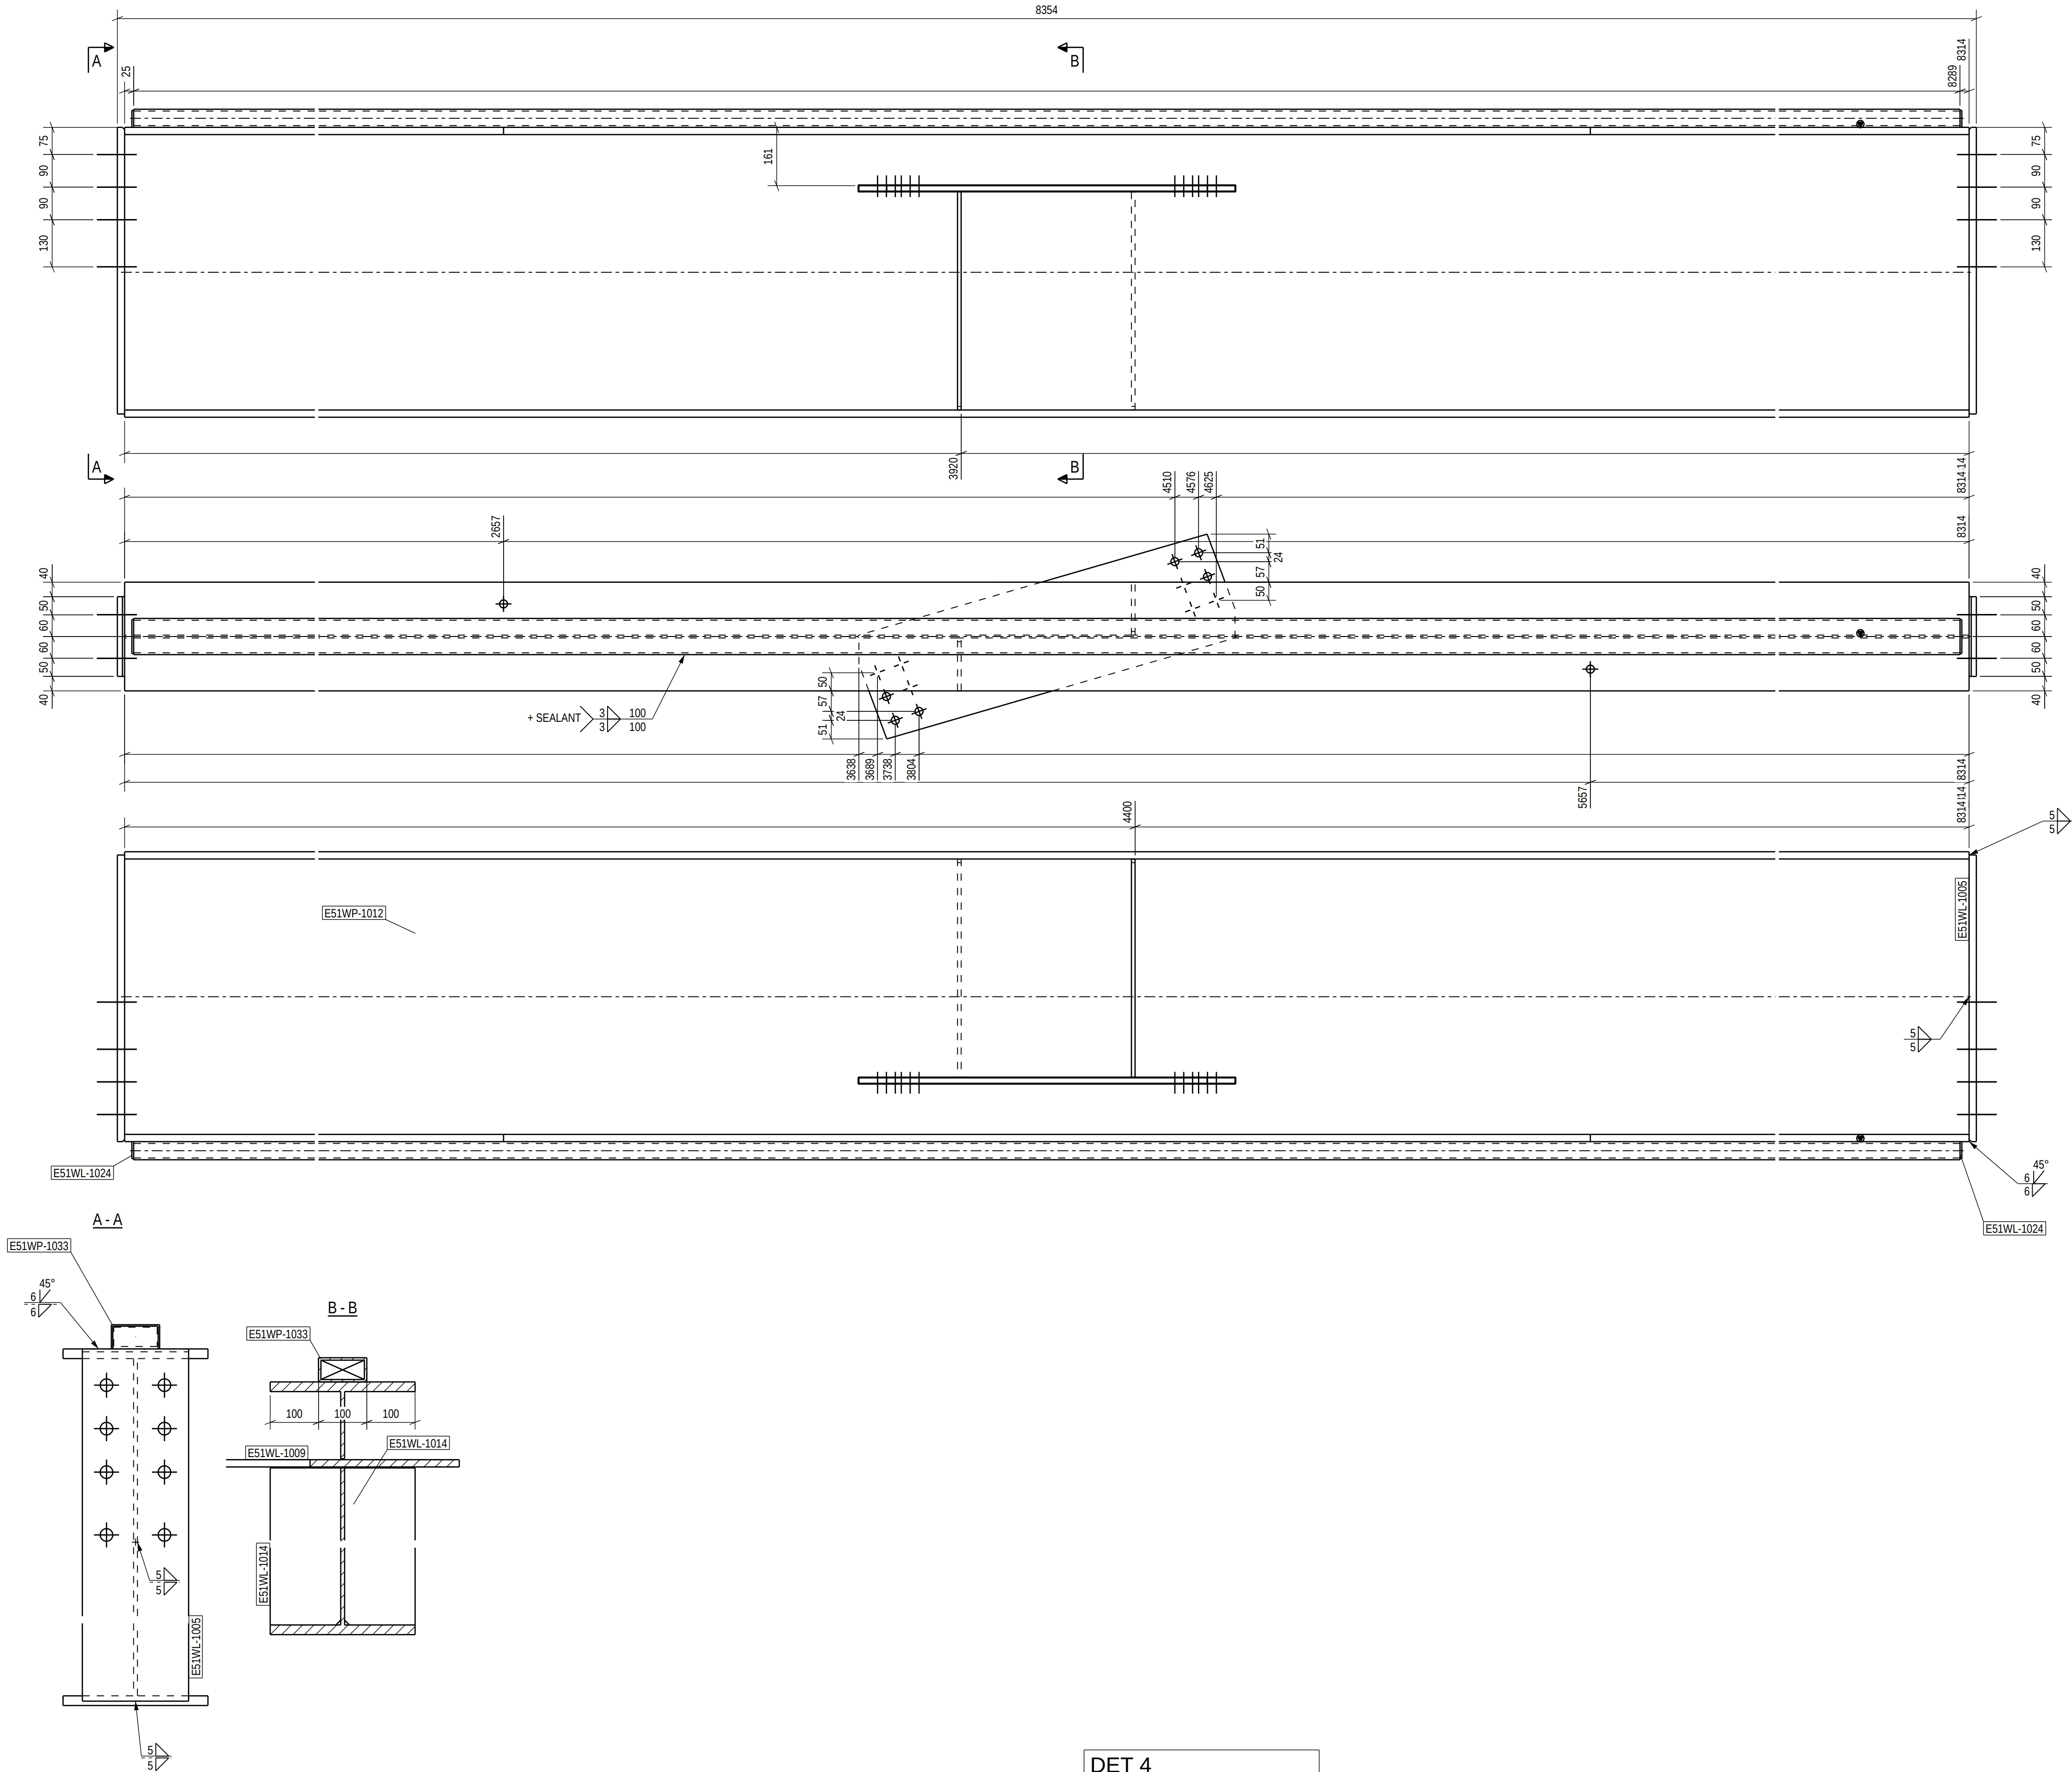


PART LIST FOR ASSEMBLY E51W-1015, MANUFACTURING AMOUNT 1 PIECES						
PART	PROFILE	MATERIAL	LENGTH [mm]	AREA [m ²]	WEIGHT [kg]	PCS
E51WL-1005	PL20X220	S355J2+N	791	0.78	27.3	2
E51WL-1009	PL15X297	S355J2+N	1040	0.65	35.7	1
E51WL-1014	PL10X146	S355J2+N	602	0.38	6.9	2
E51WL-1024	PL5X47	S355J2+N	94	0.02	0.2	2
E51WP-1012	WI800-8-20X300	S355J2	8314	23.16	1181.9	1
E51WP-1033	CFRHS100X50X5	S355J2H	8264	2.34	86.7	1
TOTAL:				27.32	1373.0	

DET 4
Full contact in bearing, requirements acc. to EN 1090-2/6.8 and 11.2.3.5 and project specification

Tolerance for the first bolt group at the end of the beam:

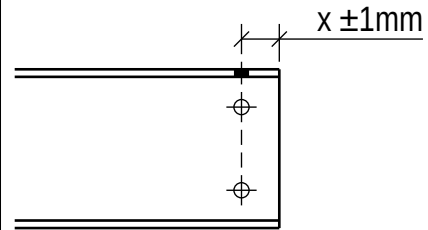

DET 1

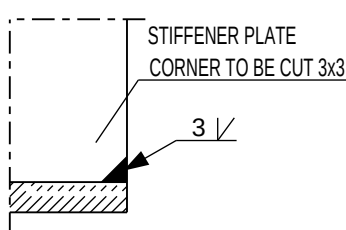

Technical fabrication requirements:		EXC2
Requirements for fabrication, standard EN1090-2, table A.3: EXC2	Fabrication references EN 1090-2, Appendix B	
Execution Specification document nr 25019443-ICC250-0600-0600-000005	Special fabrication references Project specification/ shown on drwg.	
Surface preparation grade ISO8501-3, grade P2	Weld inspection, requirements EN 1090-2, Table 24, U>0.5	
Surface treatment ISO12944-5	Extent of NDT, after welds MT-EN1290, 20% of welds	
Additional requirements on surface treatment RAL 7024 (Graphite Gray)	UT, EN-ISO17640, 20% of welds	
Welding of bulk up steel section Appendix 1 / Project spec.	UT, EN-ISO17640, 100% of welds	
Welds, first specified otherwise EN 9692-1, EN 9692-2	Requirements on testing EN1090-2 Section 6.6.3	
	Weld class C, EN ISO 5817	
	Additional material inspection Shown on drwg	

Approved For Construction



PROJECT NAME
Easpring New Materials Oy
FAIR Phase 1




SWECO RAKENNETEKNIKKKA OY
ILMALANPORTTI 2
00240 HELSINKI
PUH. +358 207 393 000
WWW.SWECO.FI

DRAWING CONTENT
ASSEMBLY DRAWING
Beam_WI
E51W-1015

DATE	ARCHIVING CODE	PAGE	DESIGNER	APPROVED	CHECKED	DESIGN GROUP
12.06.2026			Alexey Serov	Peri Kolumaanaho	Jere Kalliosalmi	STR
PROJECT NUMBER 25019443			DWG. NO. E51W-1015			REVISION

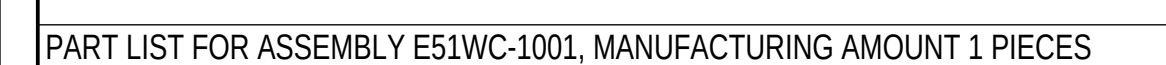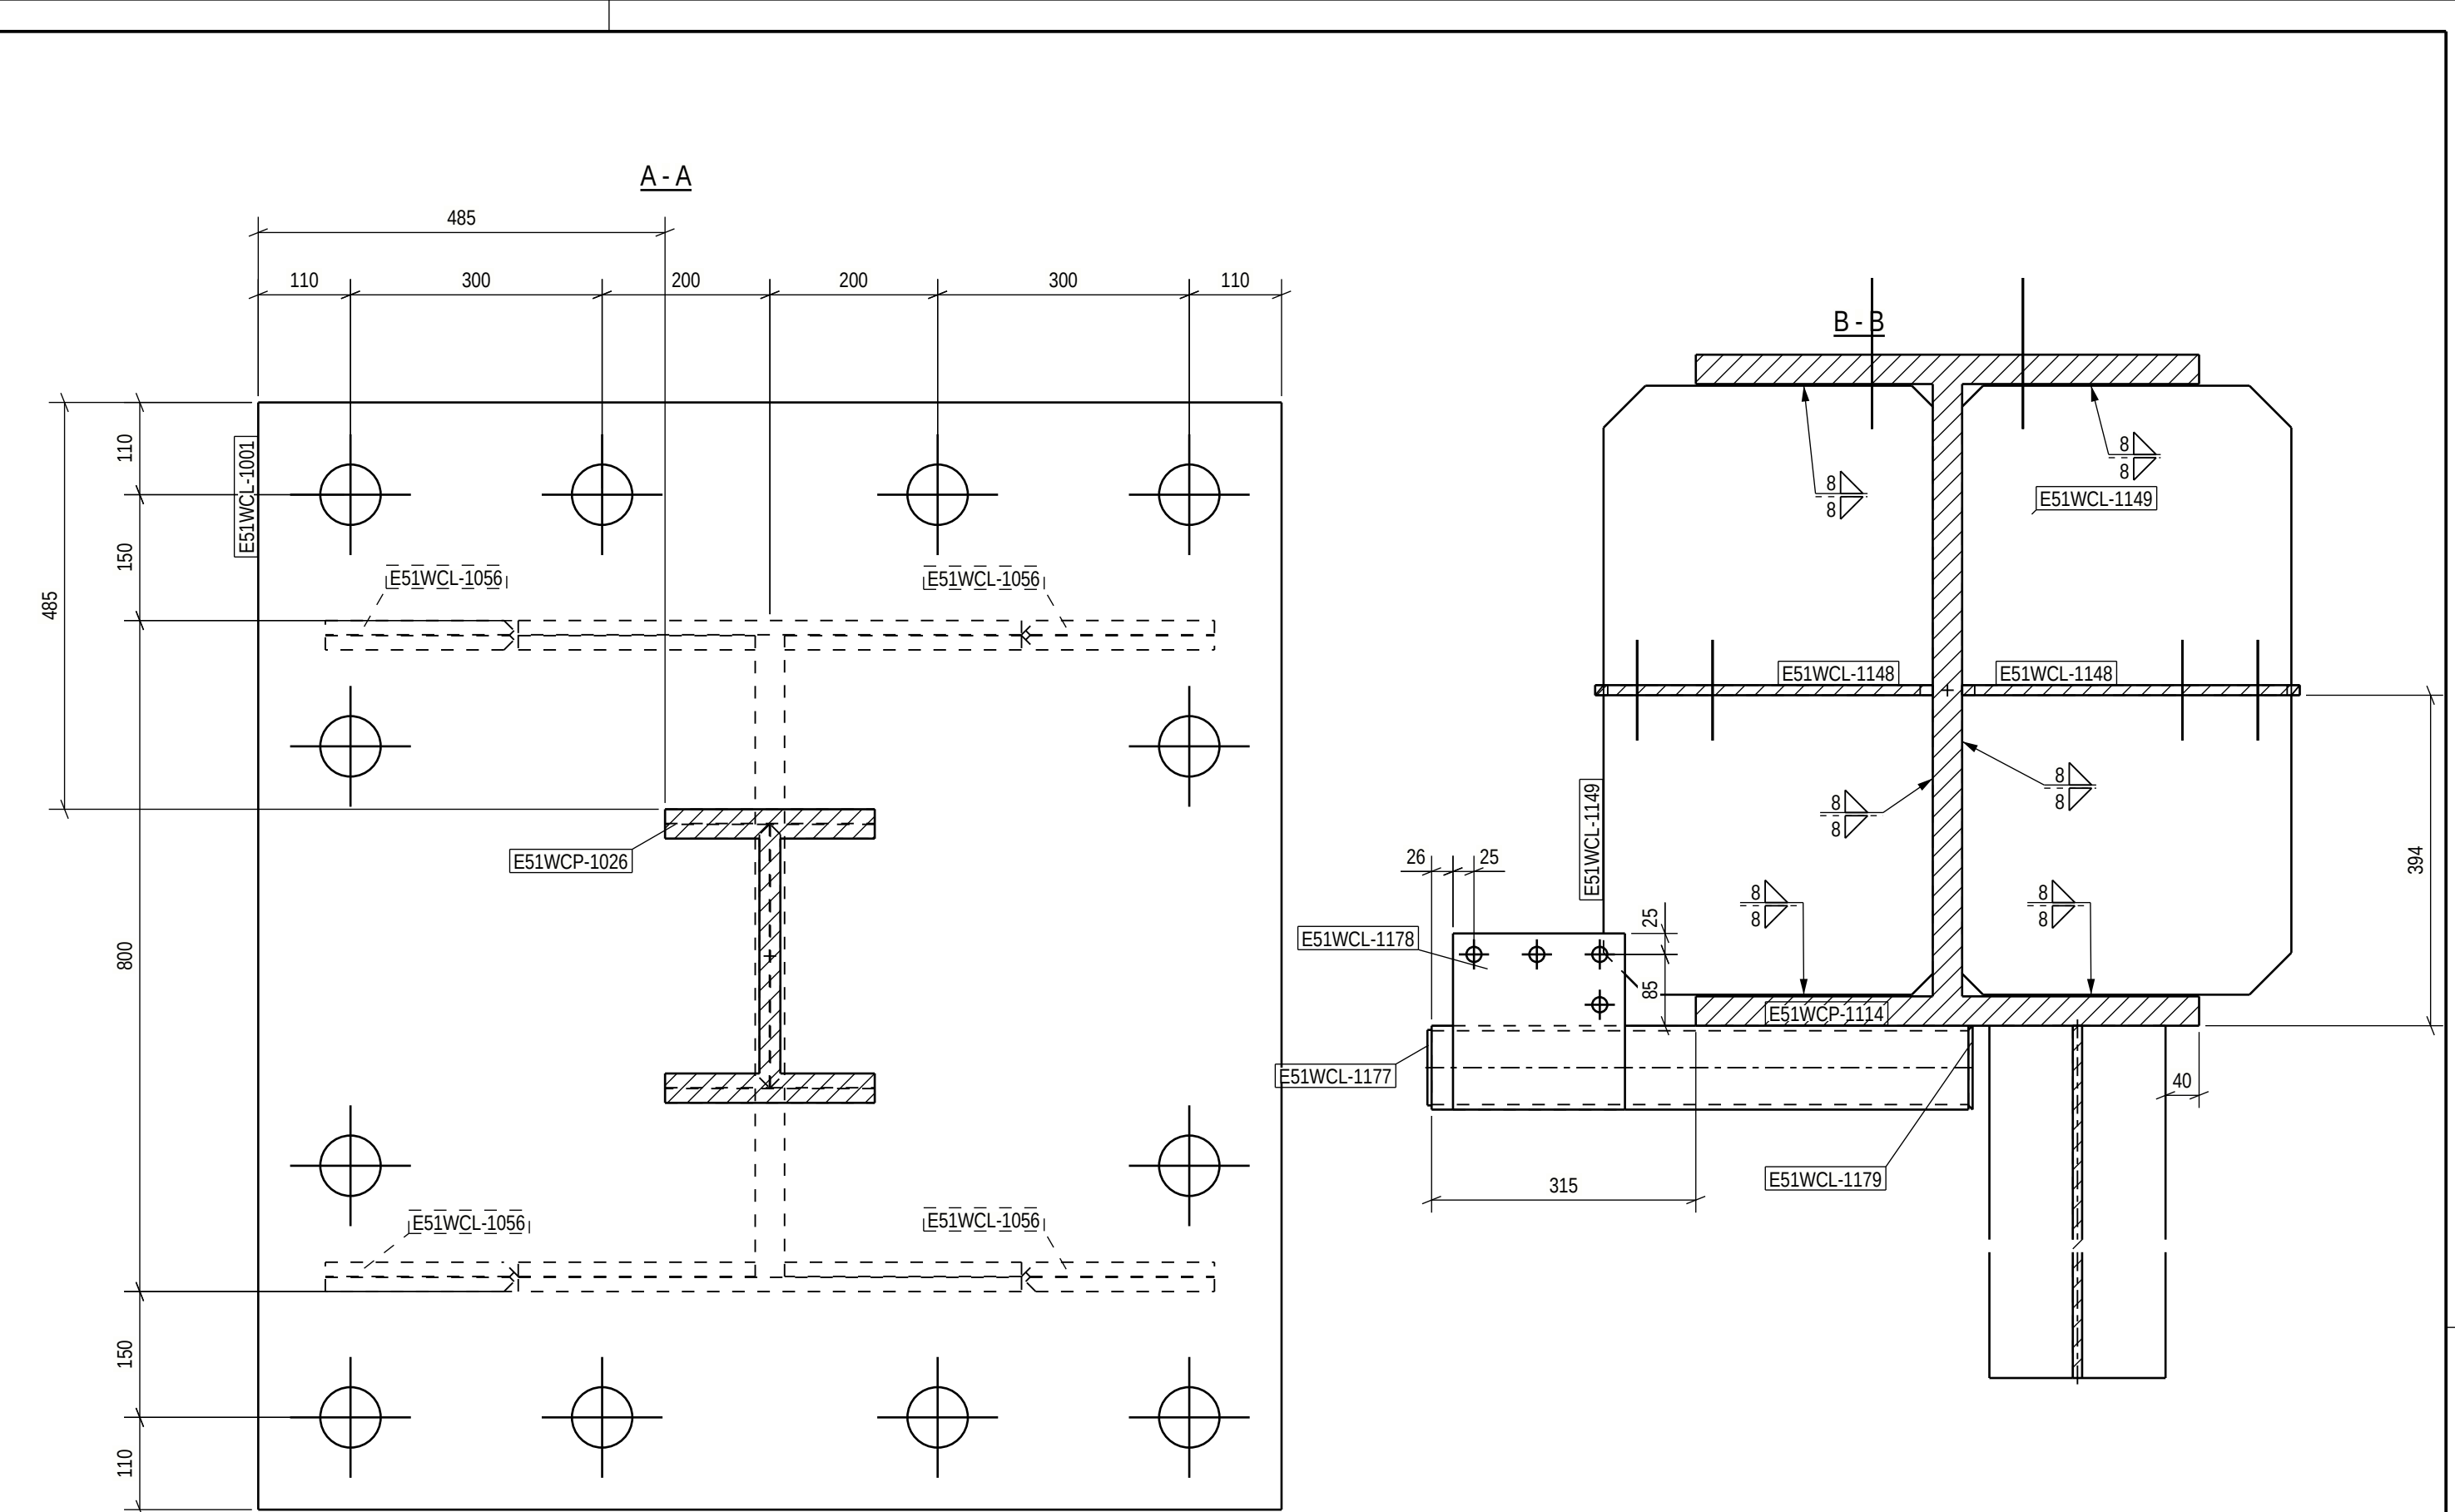


Technical drawing of a reinforced concrete slab cross-section. The drawing shows a central vertical column and a horizontal beam. The slab is divided into four quadrants. Dimensions are given in millimeters (mm). The total width of the slab is 165 mm, and the total height is 50 mm. The reinforcement is shown with circles and crosses, indicating the direction of the bars. The drawing is labeled with 'G-G' at the top, indicating a cross-section through the center. The reinforcement is labeled with 'ES1WCL-1123' and 'ES1WCL-1121'. The drawing also shows the 'NBT' (Not to Be Tolerated) symbol, indicating areas where the reinforcement is not to be tolerated.

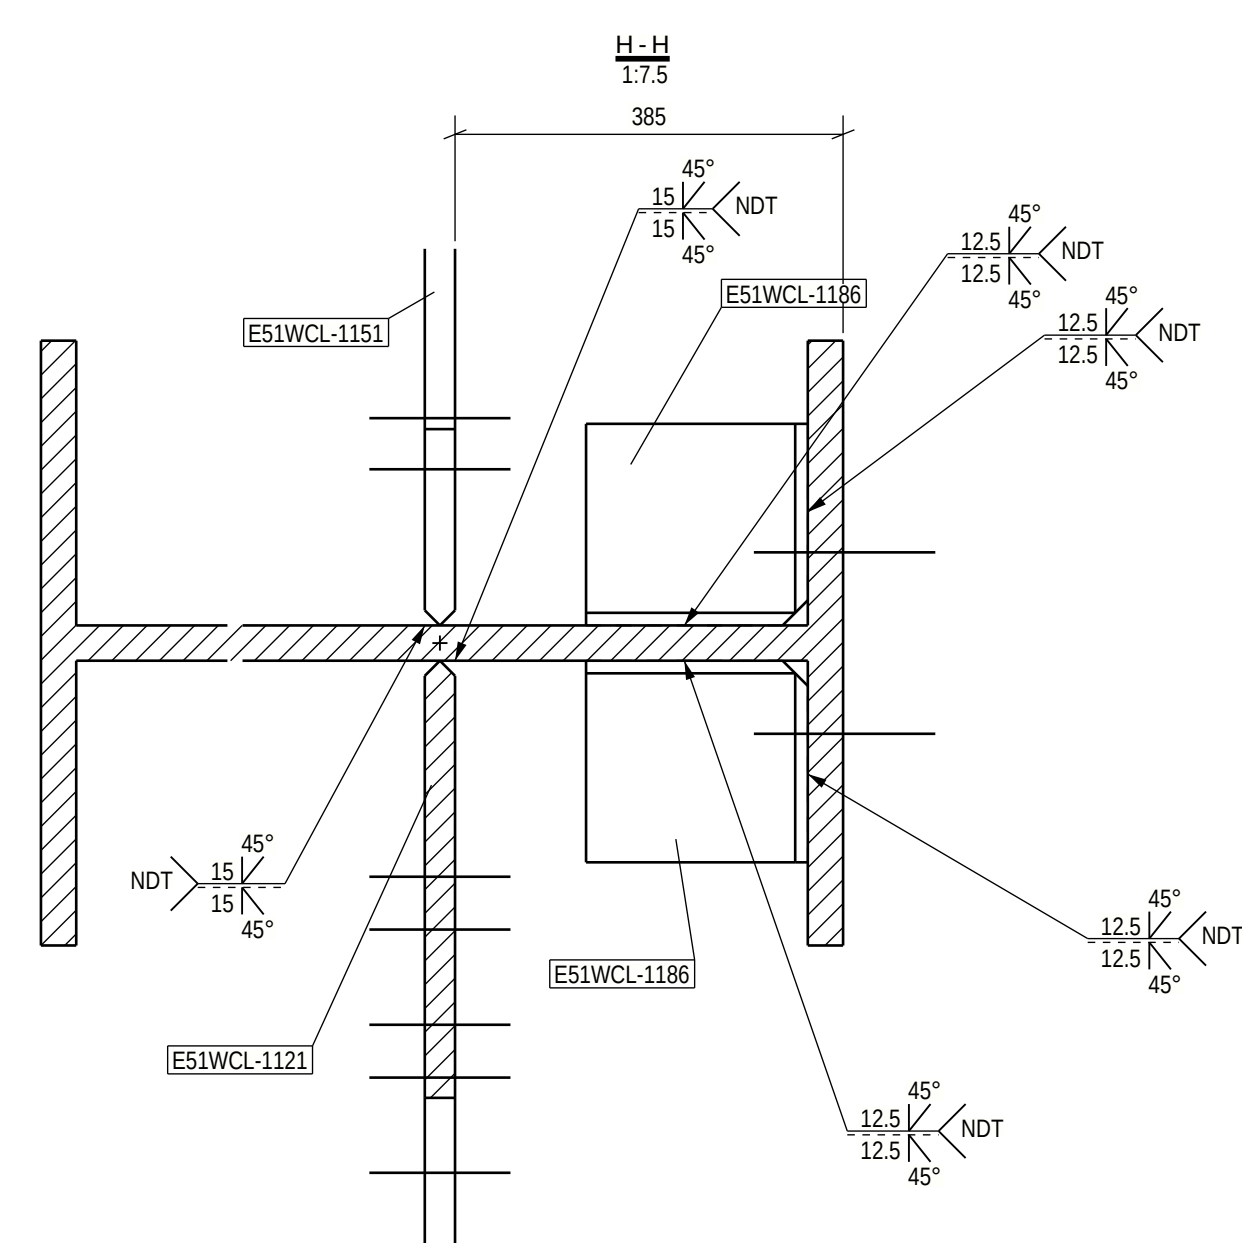




Tolerance for the first bolt group at the end of the beam:

$x \pm 1\text{mm}$

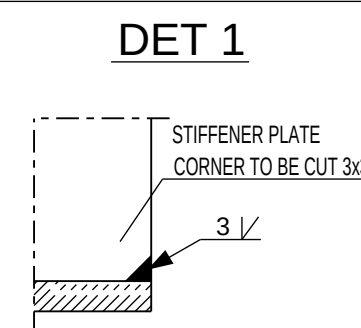

For special tolerances of bolt hole location
see specification for steel structures
Approved For Construction

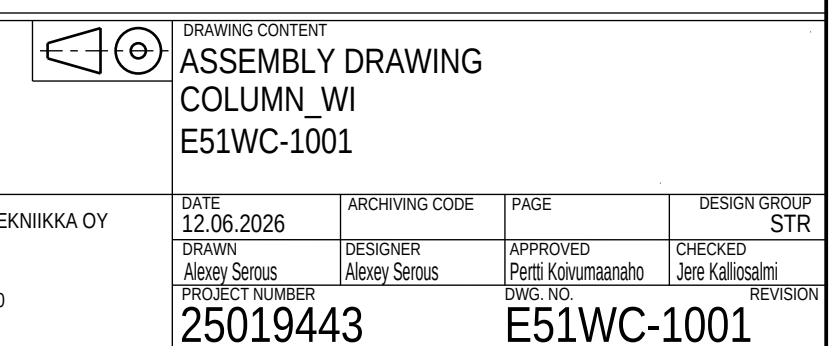

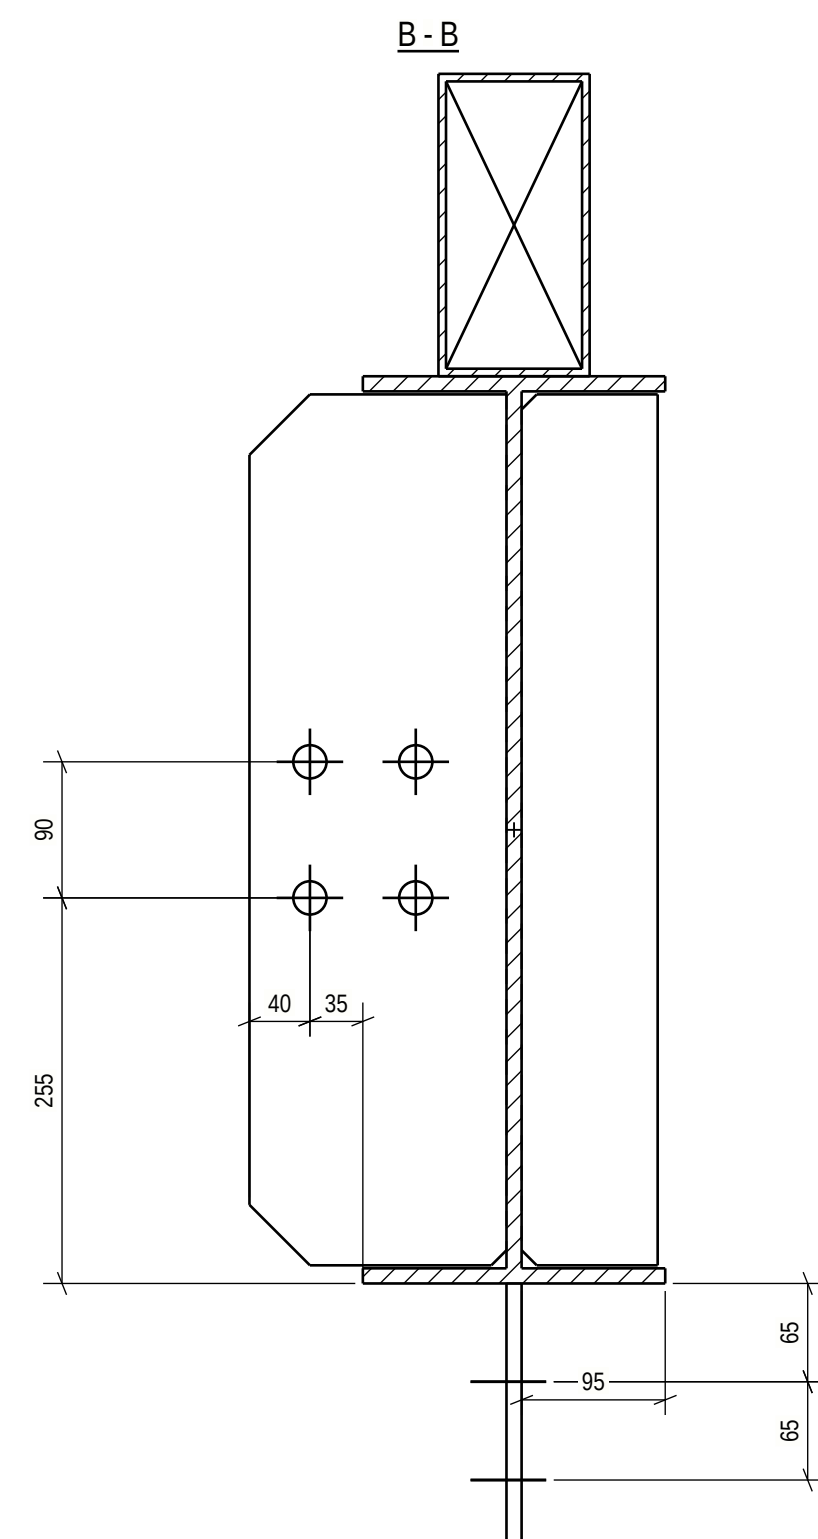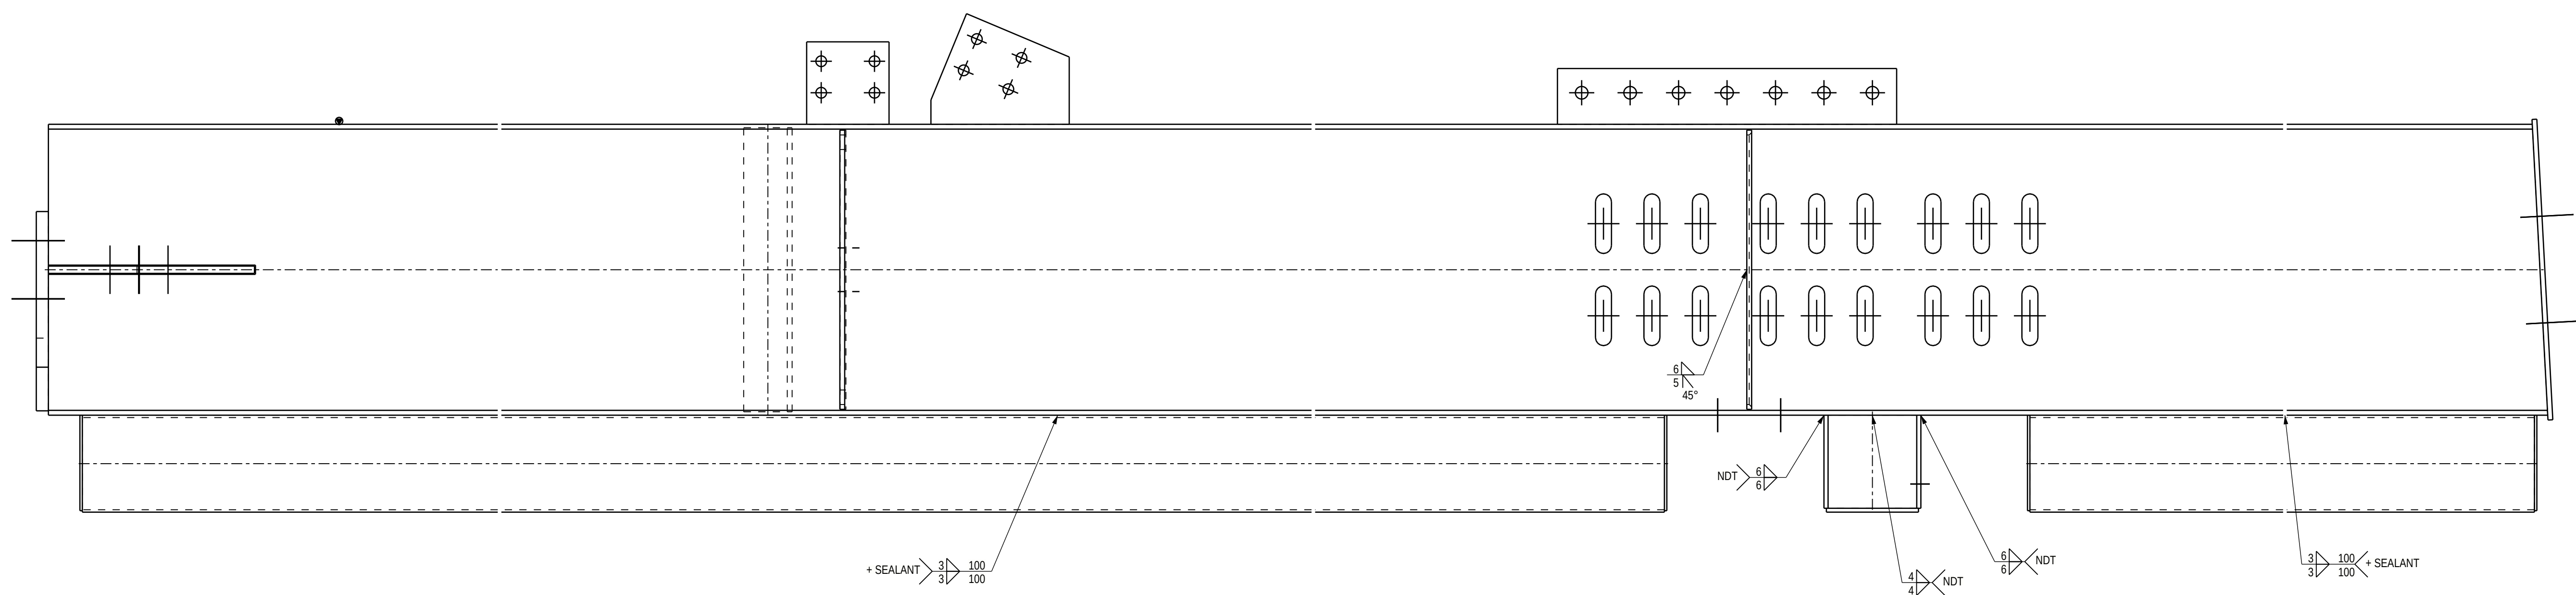


DET 4
Full contact in bearing, requirements acc. to EN 1090-2/6.8 and 11.2.3.5 and project specification

Tolerance for the first bolt group at the end of the beam:




The diagram shows a cross-section of a beam with a vertical web and horizontal flanges. Two bolt groups are shown: one at the end of the beam and another further along. A dimension line with arrows indicates a tolerance zone of $x \pm 1mm$ for the first bolt group, measured from the end face of the beam.

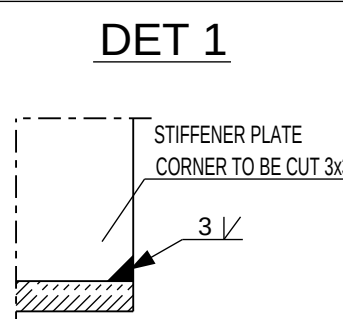

EXC2 Approved For Construction

PROJECT NAME
Easpring New Materials C
FAIR Phase 1

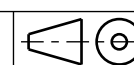

DRAWING CONTENT
ASSEMBLY DRAWING
COLUMN_WI
E51WC-1010







SWECO RAKENNETS
ILMALANPORTTI 2
00240 HELSINKI
PUH. +358 207 393 000
WWW.SWECO.FI


DATE	12.05.2026
DRAWN	Alexy Serrus
PROJECT NUMBER	250194

PAGE	DESIGN
APPROVED Peri Kovummasahe	CHECKED Jere Kallio
DWG. NO.	
E51WC-1010	

PART LIST FOR ASSEMBLY E51WC-1013, MANUFACTURING AMOUNT 1 PIECES						
PART	PROFILE	MATERIAL	LENGTH [mm]	AREA [m ²]	WEIGHT [kg]	PCS
E51WCL-1026	PL25X270	S355J2+N	566	0.09	29.7	2
E51WCL-1052	PL10X228	S355J2+N	284	0.11	3.8	1
E51WCL-1053	PL10X170	S355J2+N	170	0.06	2.3	1
E51WCL-1143	PL25X700	S355J2+N	420	0.59	53.2	1
E51WCL-1144	PL30X512	S355J2+N	995	0.86	93.0	1
E51WCL-1171	PL5X194	S355J2+N	197	0.16	1.5	2
E51WCP-1009	W800-10-15X250	S355J2	5175	11.28	538.1	1
E51WCP-1080	L100*10	S355J2	586	0.46	8.8	2
E51WCP-1102	CPHHS200X200X5	S355J2H	5470	4.28	164.7	1
TOTAL:				18.59	595.2	

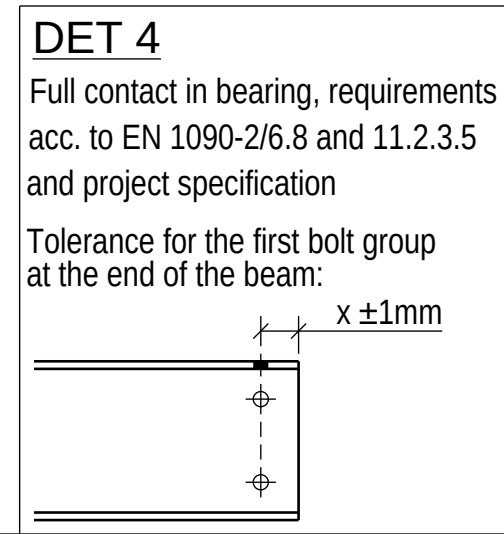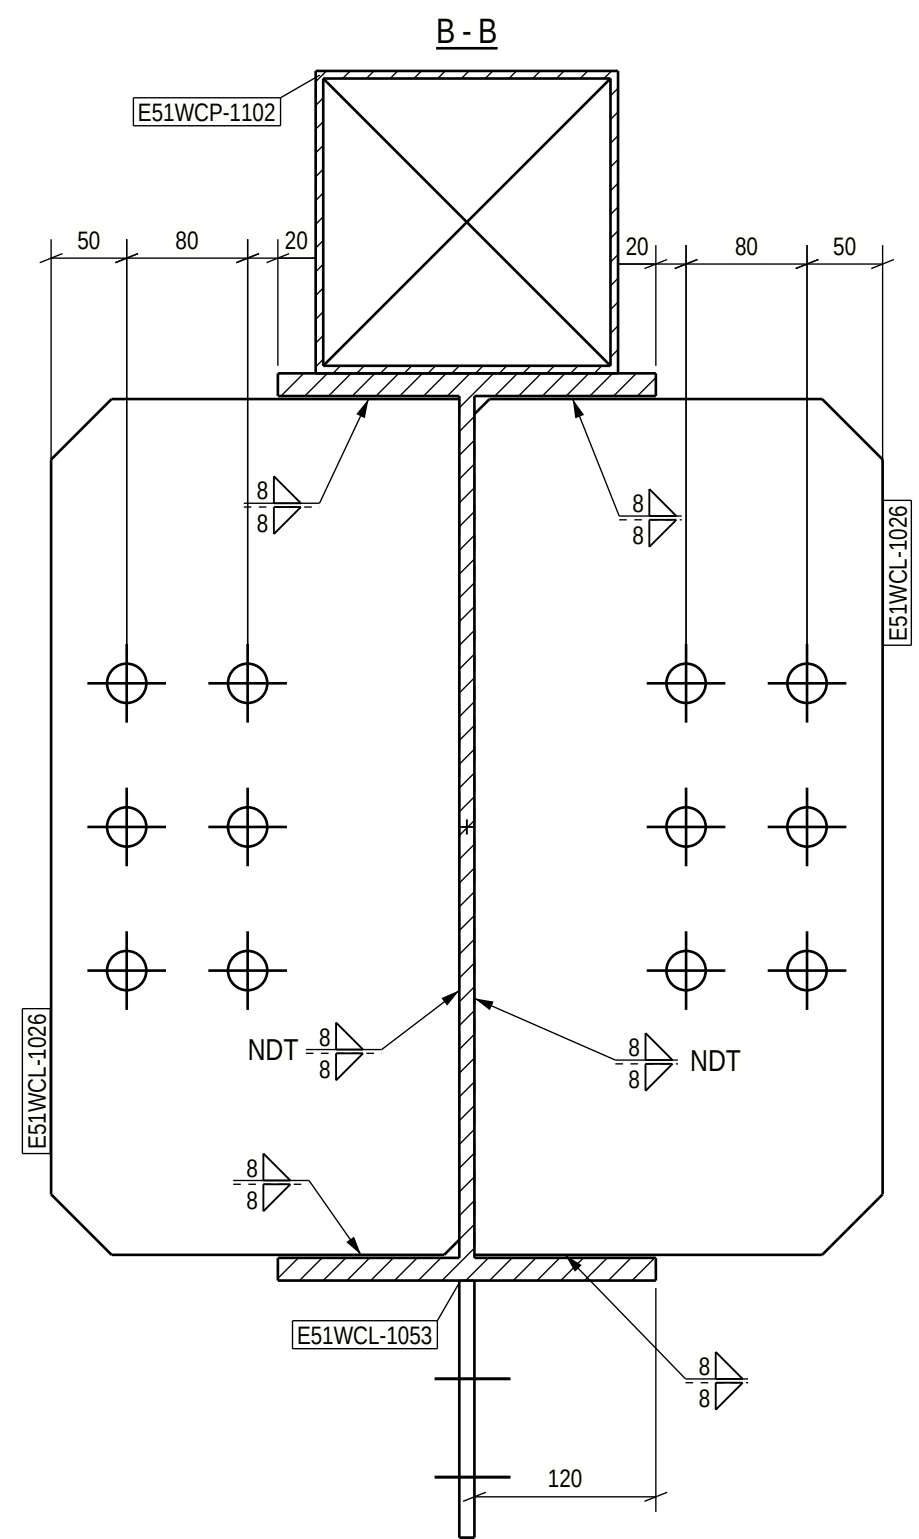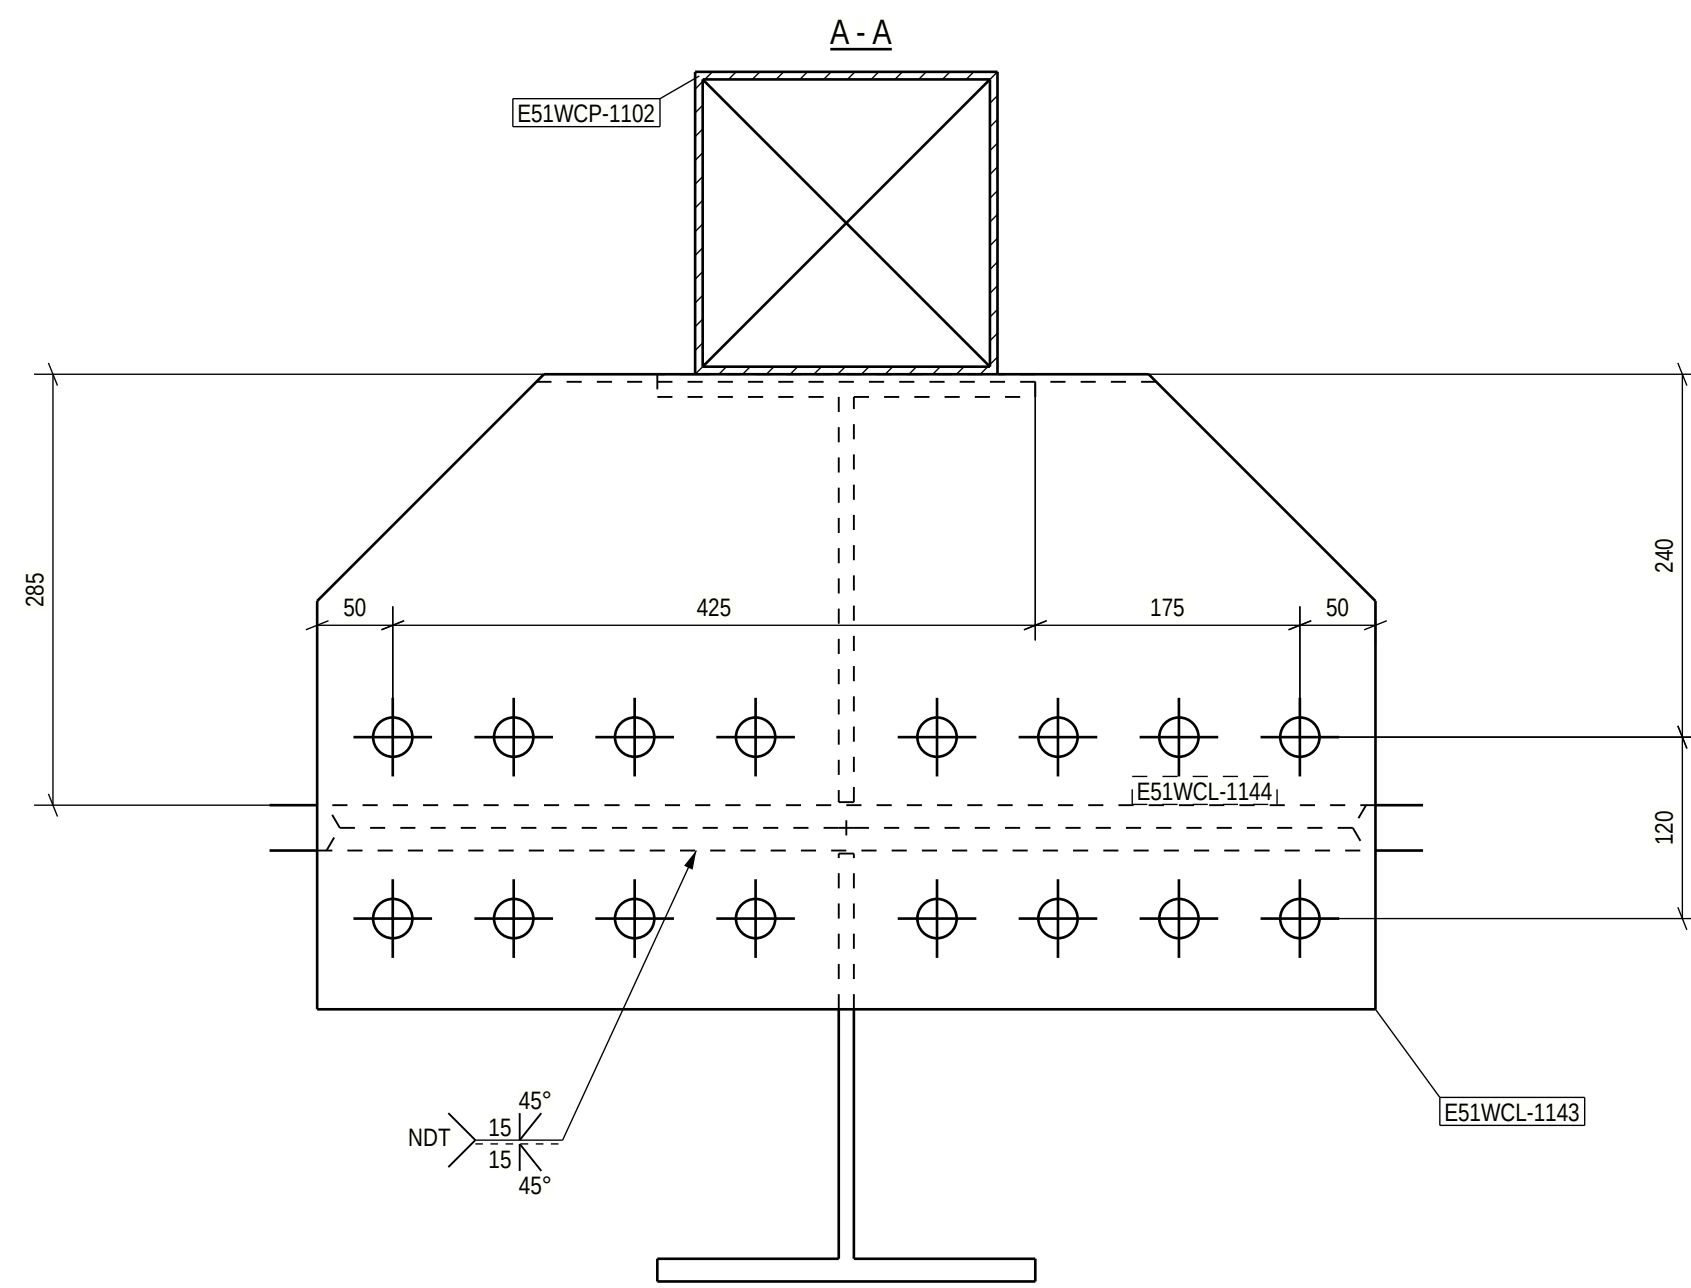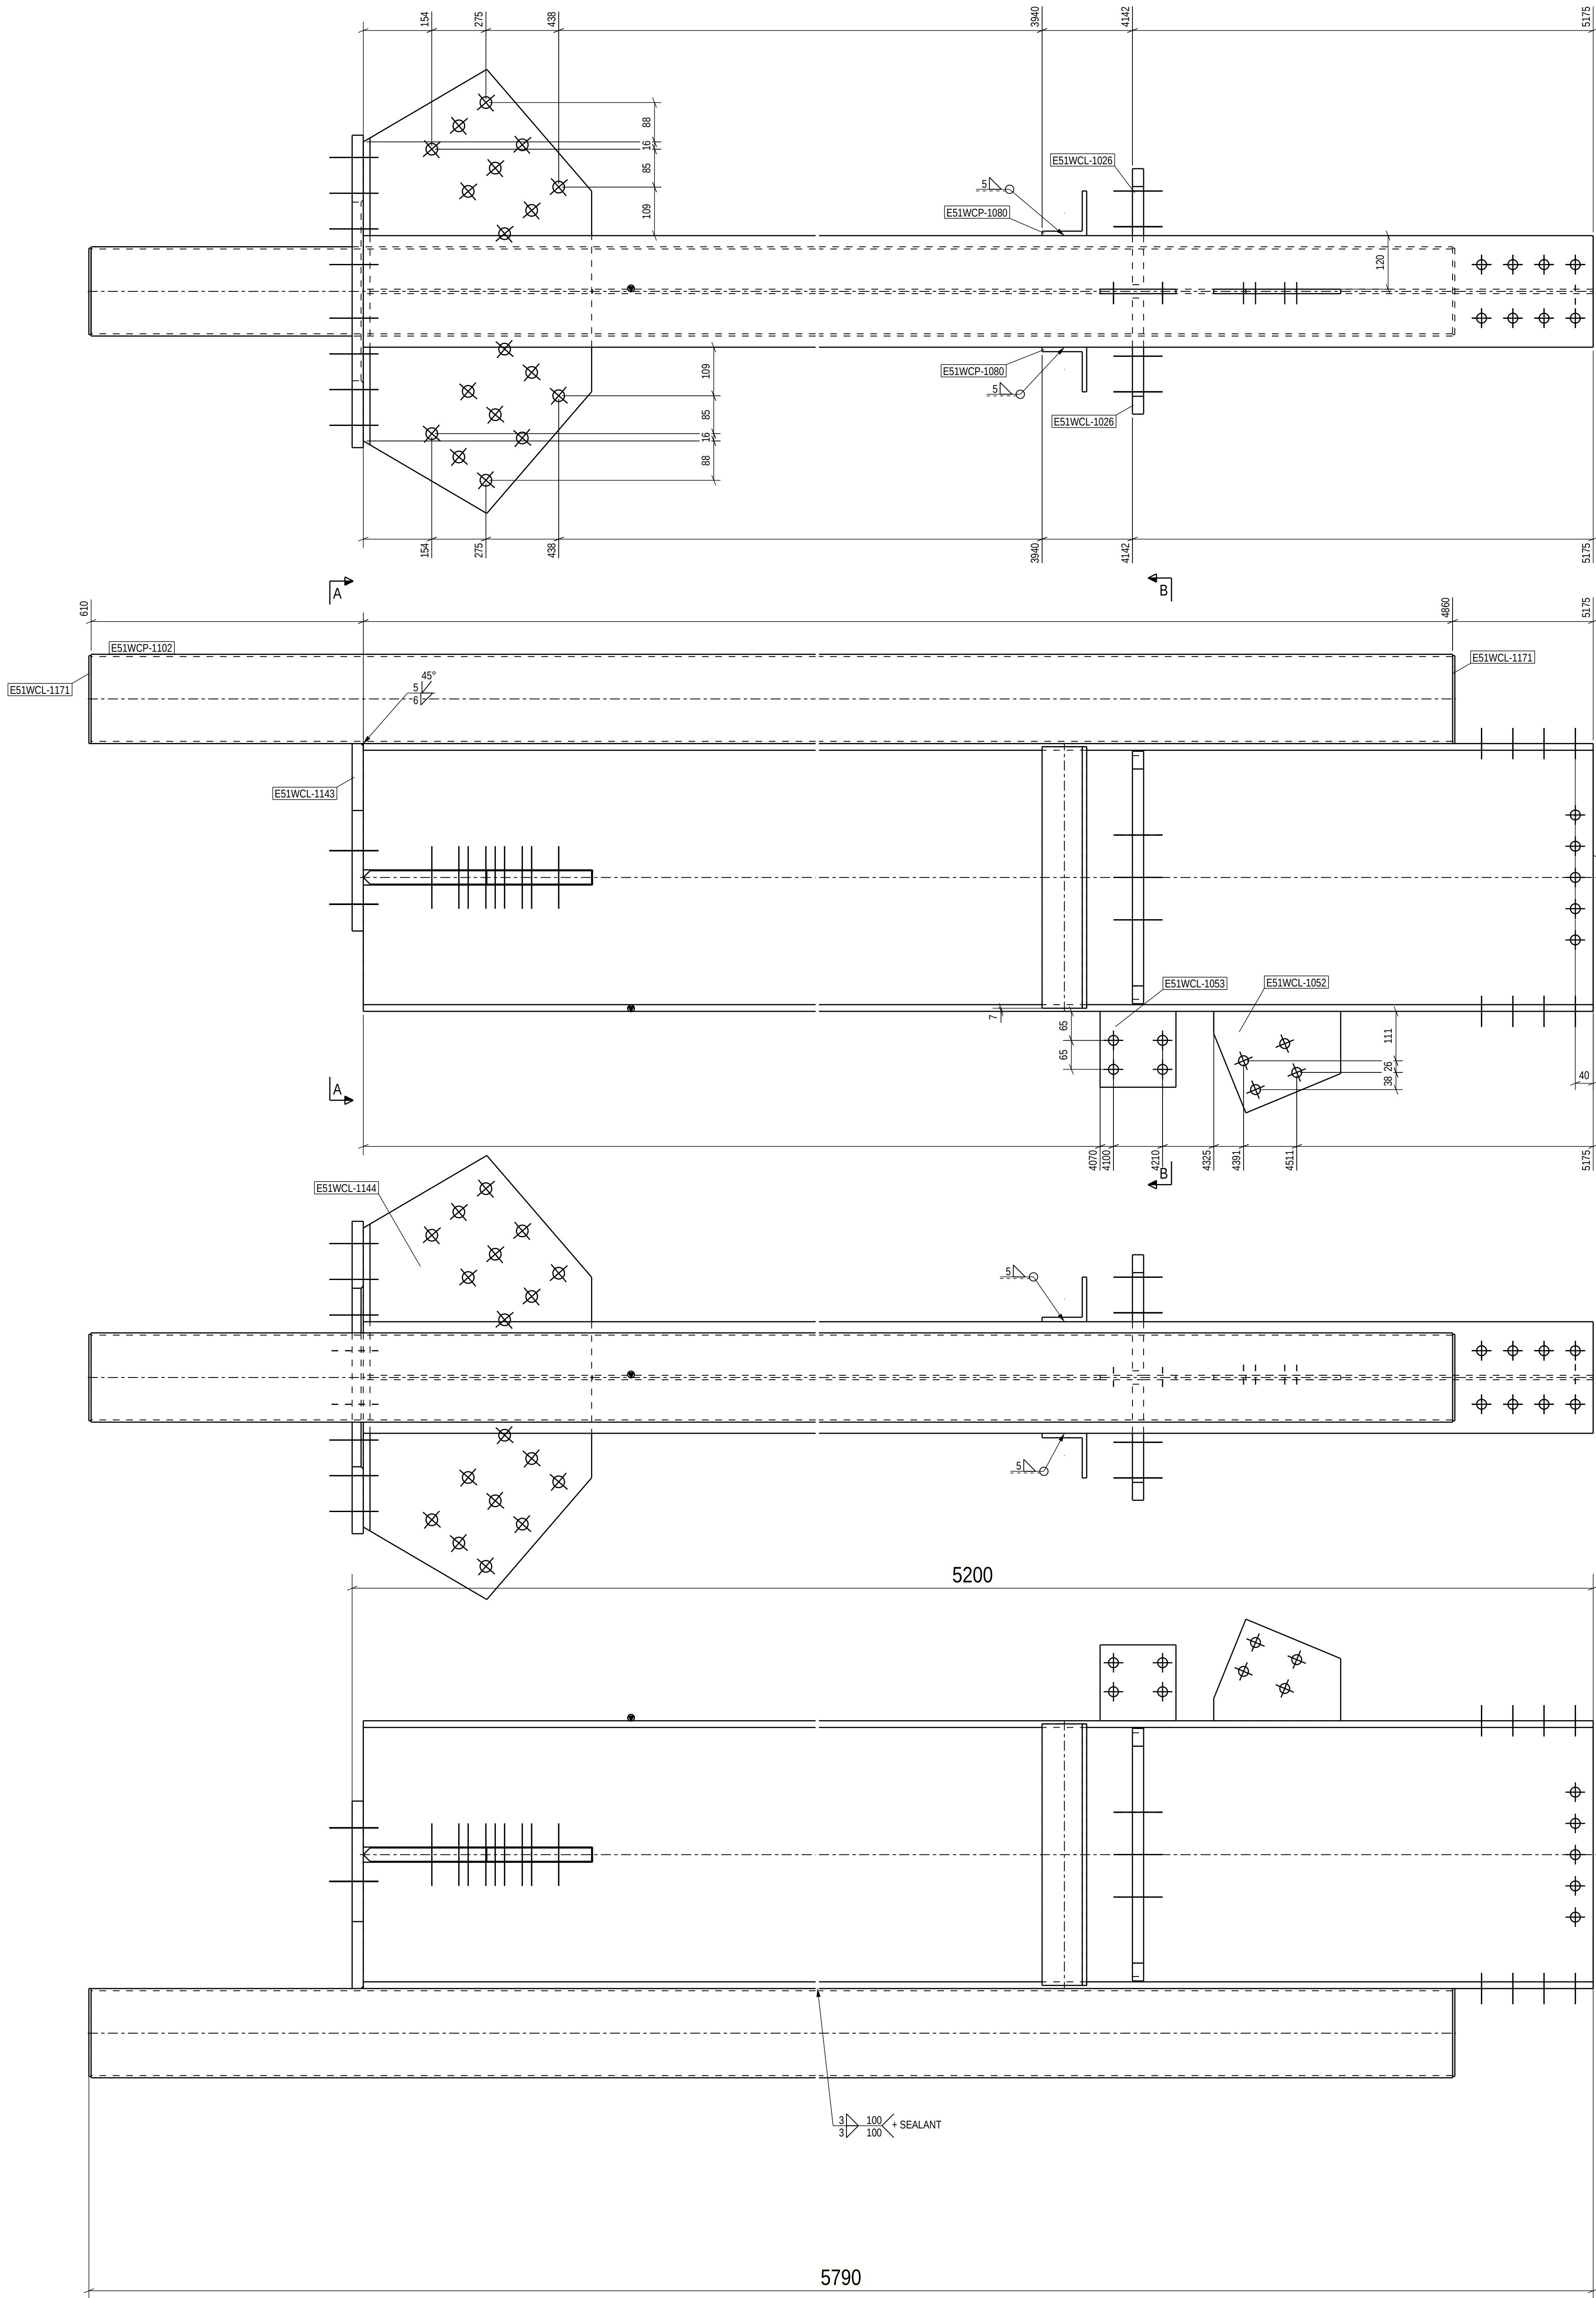

DET 1

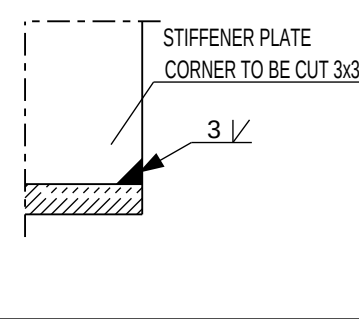

Technical fabrication requirements:			
EN 1090-2, Table A.3, EXC2	EN 1090-2, Appendix B	Project specification shown on drawing	
EN 1090-2, Table A.3, EXC2	EN 1090-2, Table A.3, EXC2	Project specification shown on drawing	
EN 1090-2, Table A.3, EXC2	EN 1090-2, Table A.3, EXC2	Project specification shown on drawing	
EXC2

Approved For Construction



Easpring New Materials Oy
FAIR Phase 1

DATE: 12.06.2026
DRAWING CODE: 25019443
DESIGNER: Jari Kallio
CHECKER: Jari Kallio
APPROVED: Jari Kallio
PROJECT: FAIR Phase 1

DRAWING CONTENT			
ASSEMBLY DRAWING	COLUMN W1	E51WC-1013	
DATE: 12.06.2026	DESIGNER: Jari Kallio	CHECKER: Jari Kallio	APPROVED: Jari Kallio
DRAWING CODE: 25019443	DESIGNER: Jari Kallio	CHECKER: Jari Kallio	APPROVED: Jari Kallio
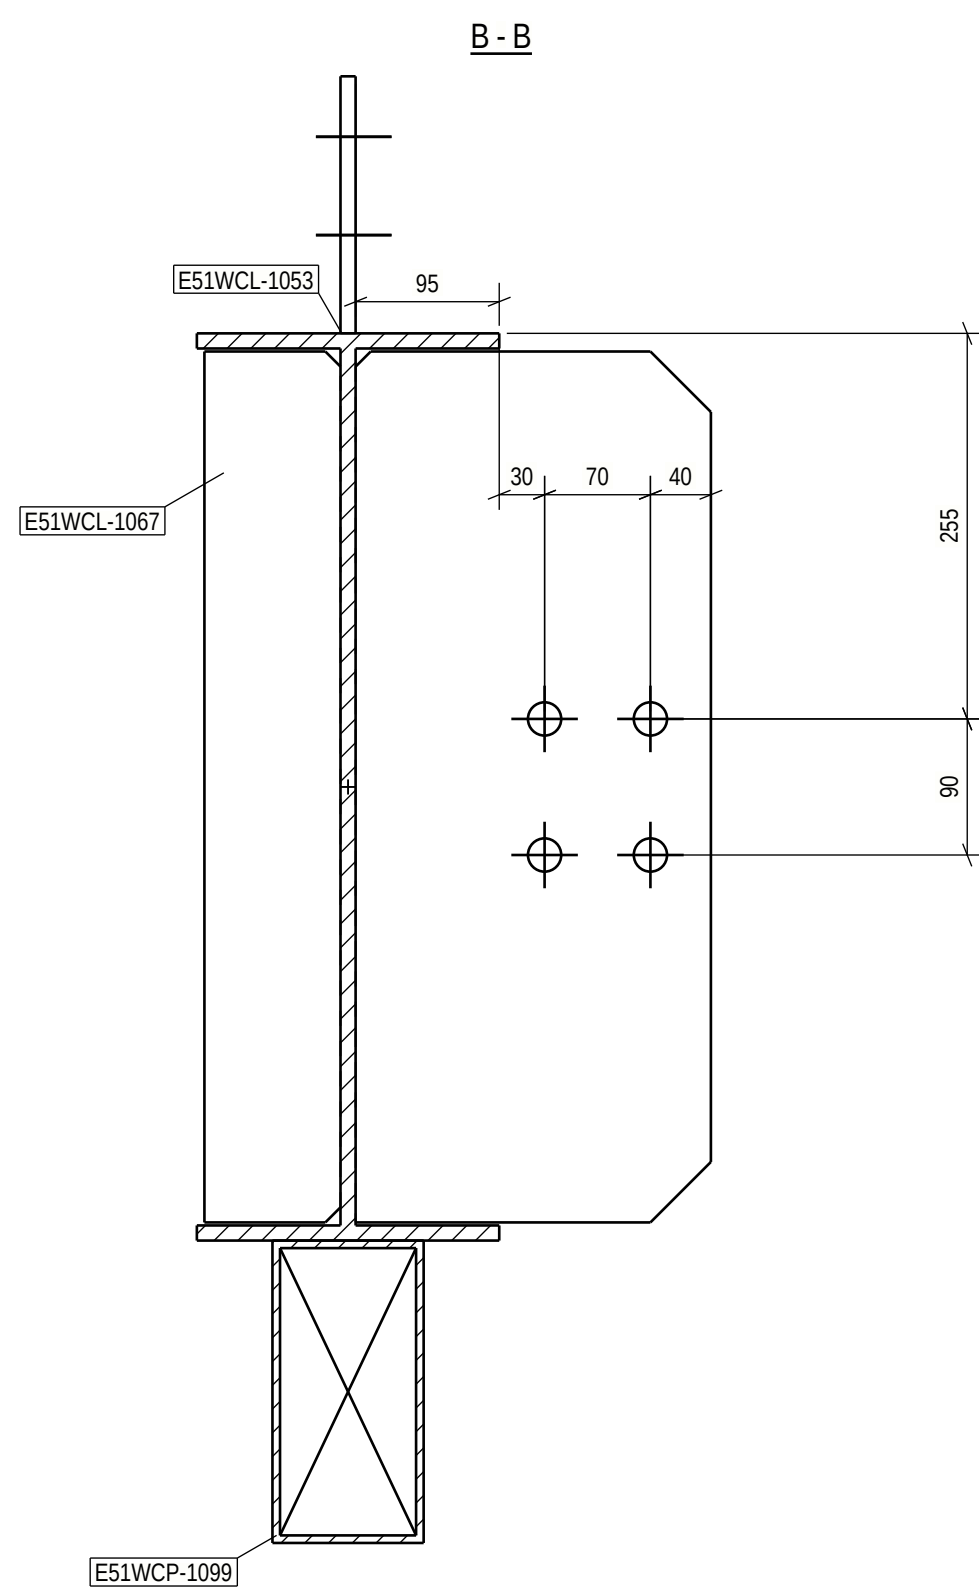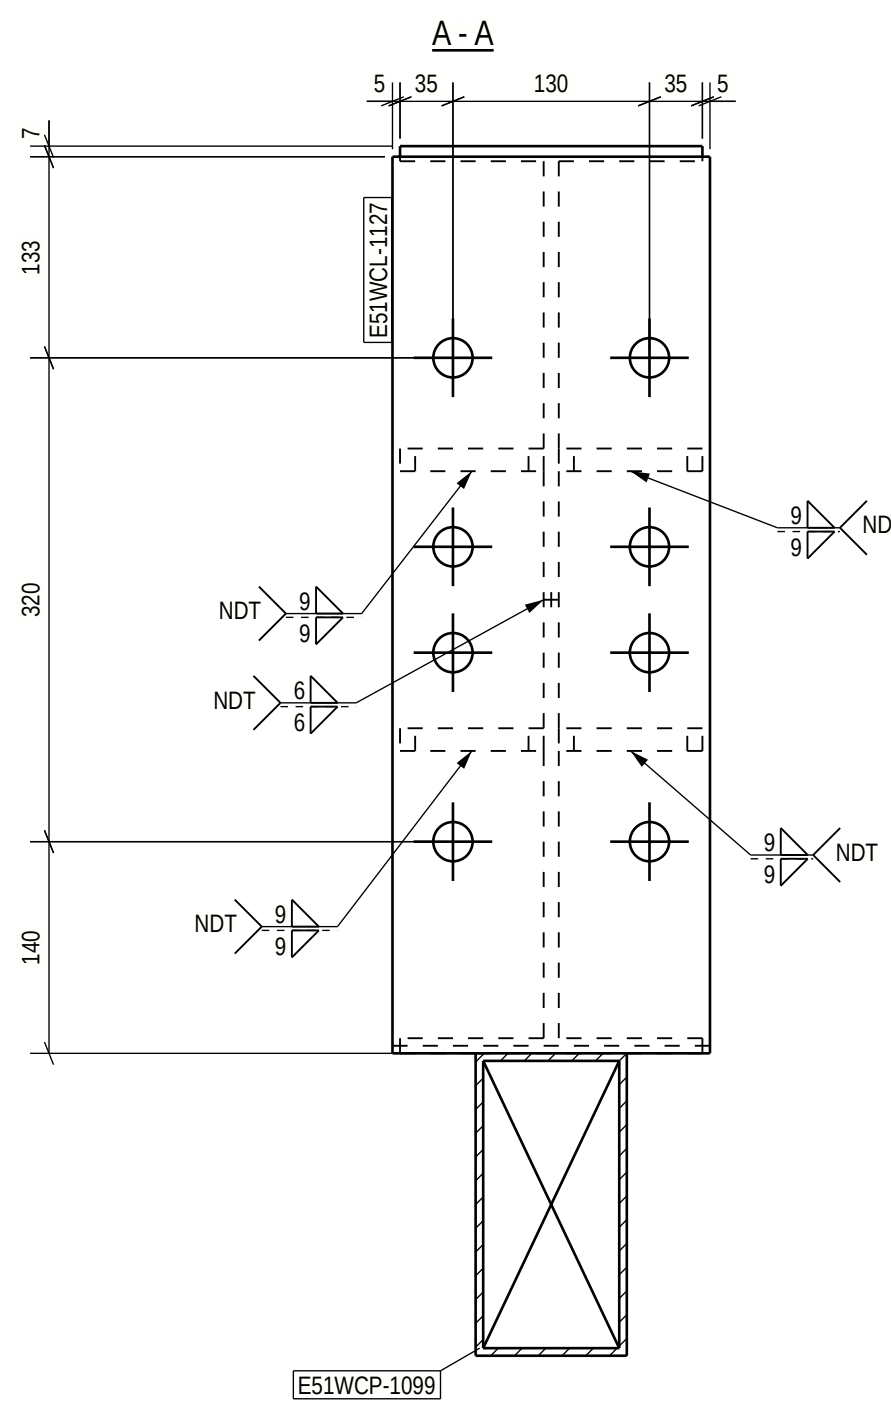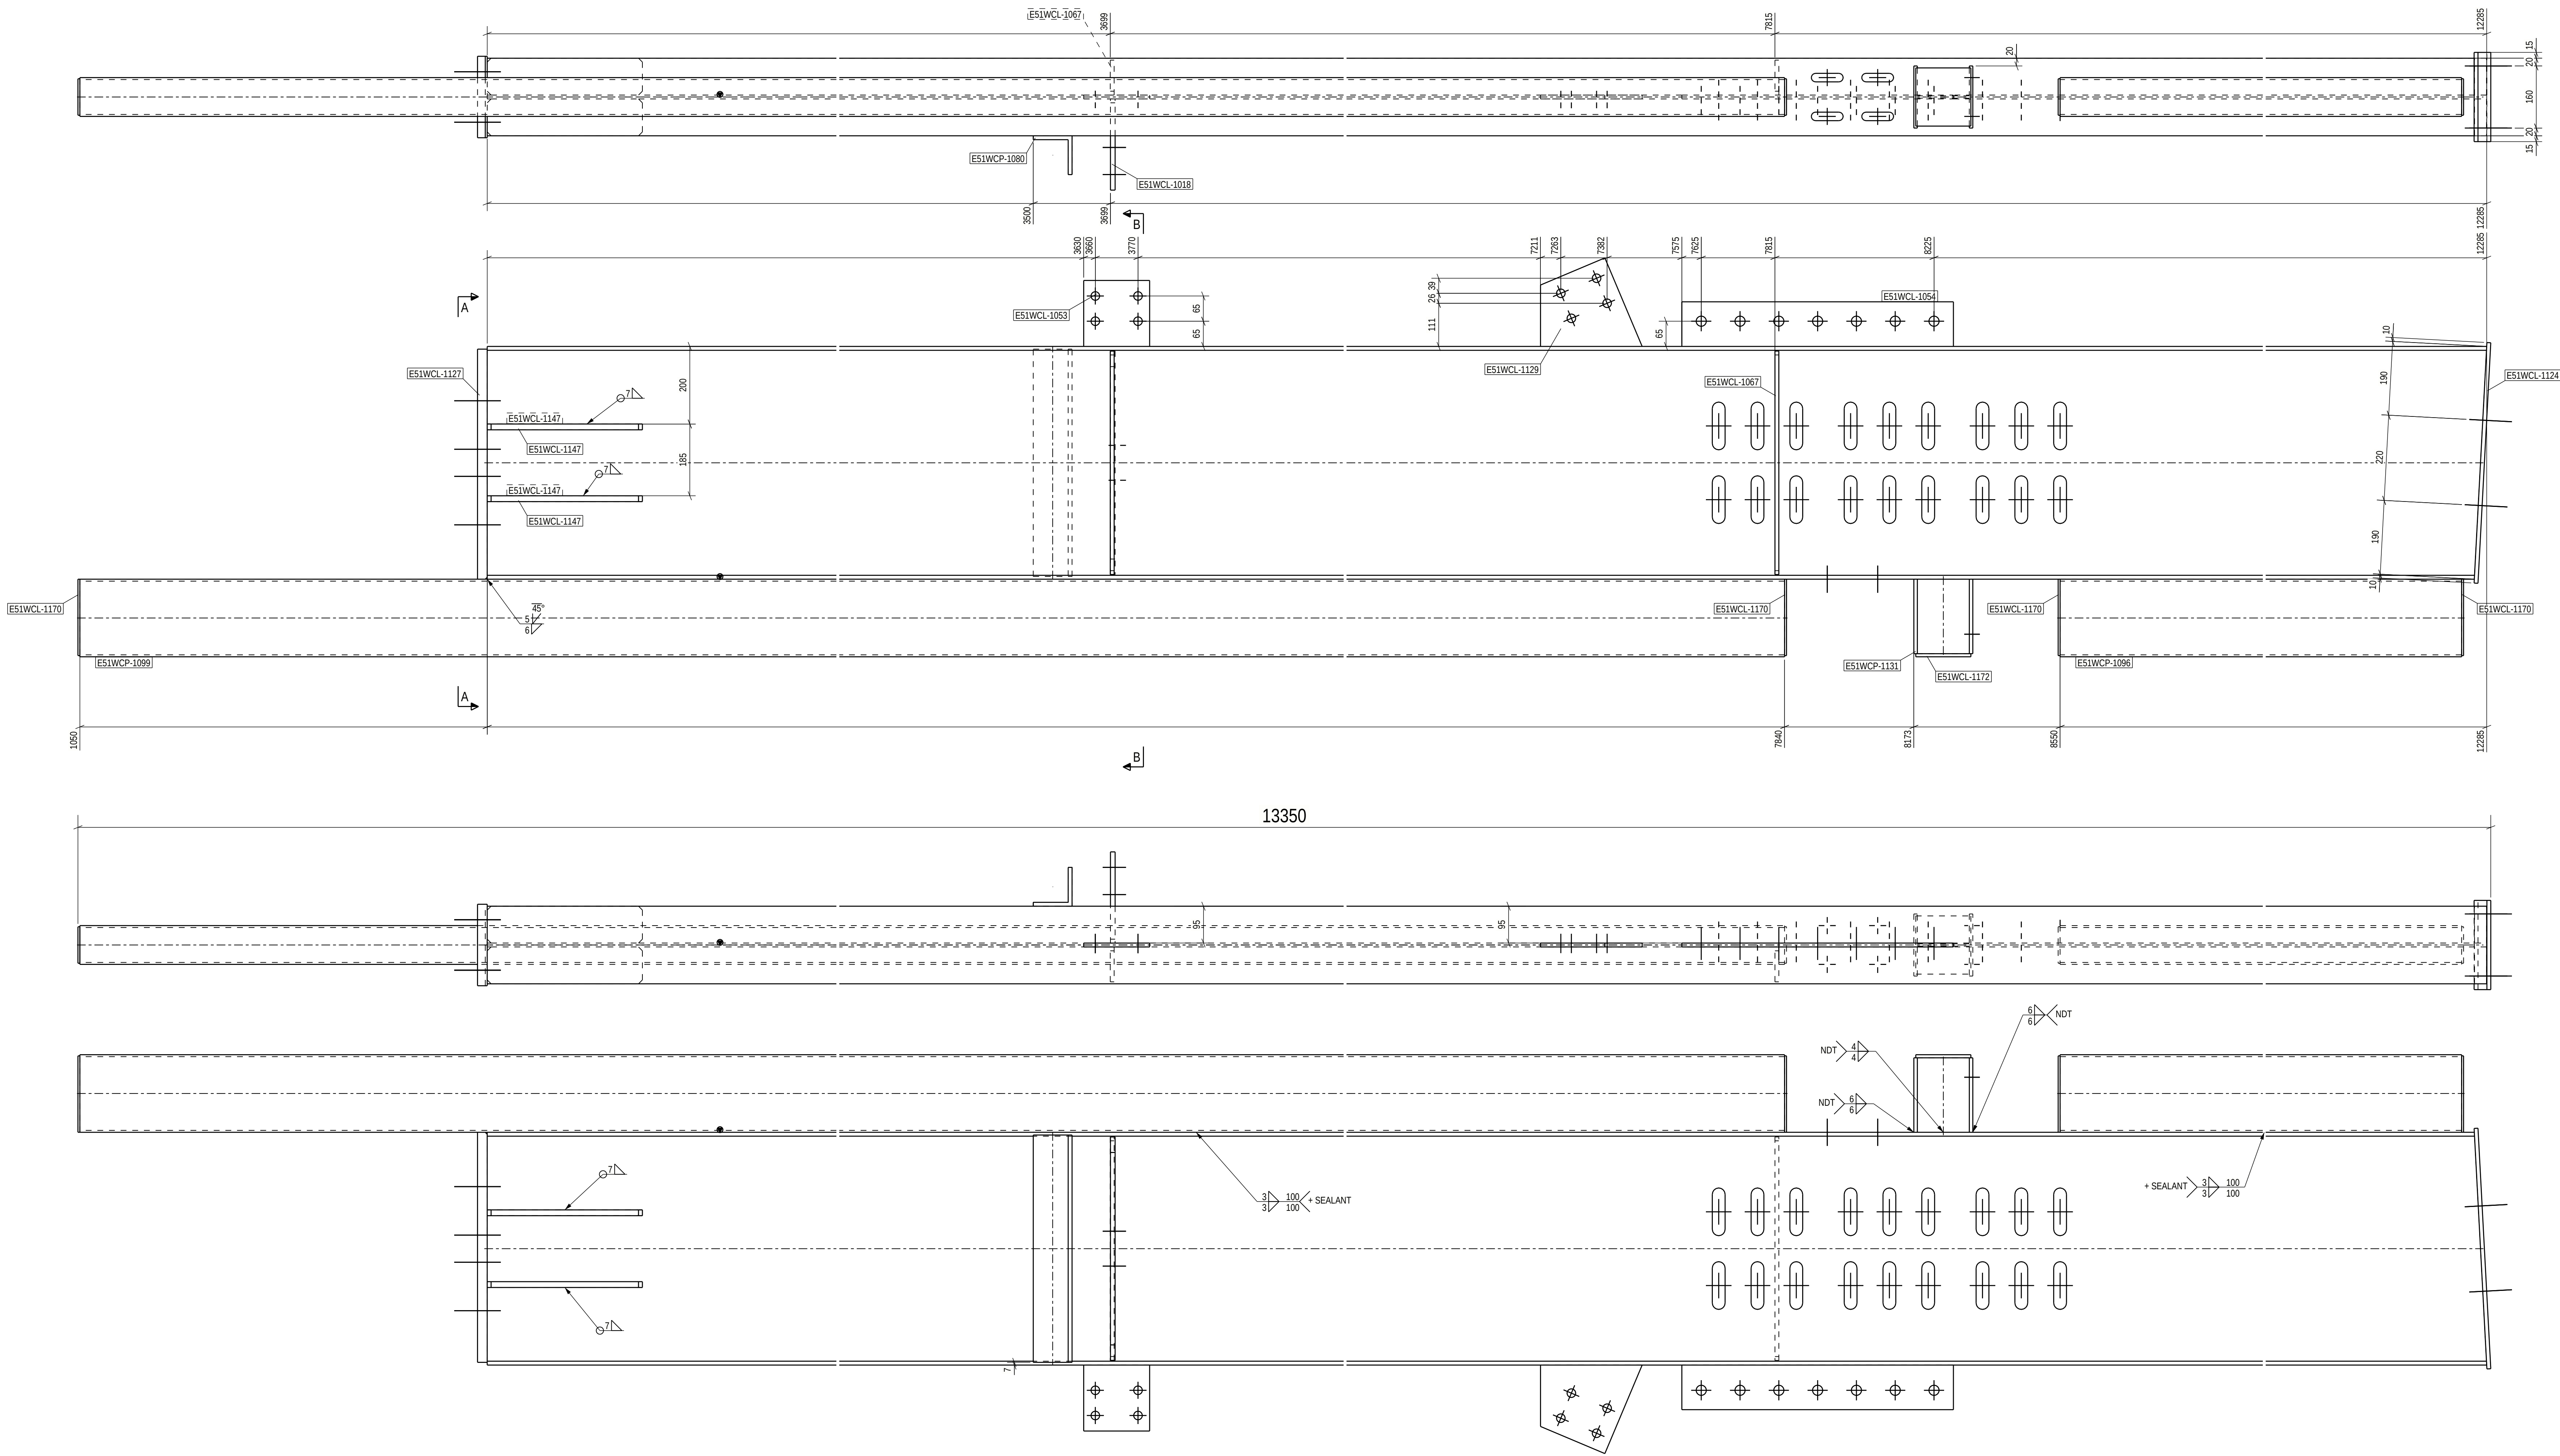

PART LIST FOR ASSEMBLY E51WC-1017. MANUFACTURING AMOUNT 1 PIECES							
PART	PROFILE	MATERIAL	LENGTH [mm]	AREA [m ²]	WEIGHT [kg]	PCS	
ES1WCL-1018	PL12X235	S355J2+N	576	0.29	12.6	1	
ES1WCL-1053	PL10X170	S355J2+N	170	0.06	2.3	1	
ES1WCL-1054	PL10X115	S355J2+N	700	0.18	6.3	1	
ES1WCL-1067	PL10X90	S355J2+N	576	0.23	4.1	2	
ES1WCL-1124	PL10X230	S355J2+N	621	0.30	11.2	1	
ES1WCL-1127	PL25X210	S355J2+N	593	0.29	24.4	1	
ES1WCL-1129	PL10X228	S355J2+N	282	0.09	3.4	1	
ES1WCL-1147	PL15X95	S355J2+N	400	0.36	4.5	4	
ES1WCL-1170	PL5X94	S355J2+N	197	0.16	0.7	4	
ES1WCL-1172	PL8X150	S355J2+N	142	0.05	1.3	1	
ES1WCP-1090	L100X10	S355J2	596	0.23	8.8	1	
ES1WCP-1095	WR600-10-10X200	S355J2	12285	24.31	949.5	1	
ES1WCP-1096	CFRHS200X100X5	S355J2H	3670	2.14	81.7	1	
ES1WCP-1099	CFRHS200X100X5	S355J2H	8890	5.18	197.9	1	
ES1WCP-1131	HEA160	S355J2	192	0.17	5.8	1	
TOTAL:			34.05	334.1			

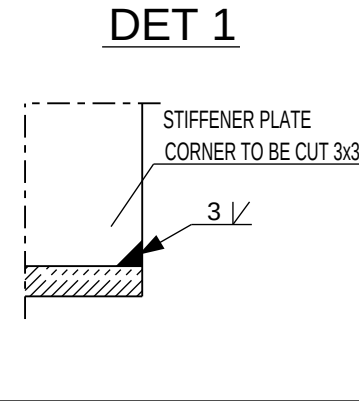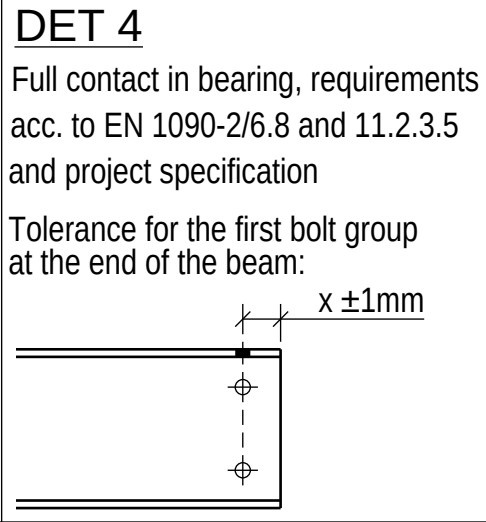


Technical fabrication requirements:			
EN 1090-2, Table A.3, EXC2	EN 1090-2, Appendix B	EN 1090-2, Table 24, 12-15.5	EN 1090-2, Table 24, 12-15.5
EN 1090-2, Table 24, 12-15.5	EN 1090-2, Table 24, 12-15.5	EN 1090-2, Table 24, 12-15.5	EN 1090-2, Table 24, 12-15.5
EN 1090-2, Table 24, 12-15.5	EN 1090-2, Table 24, 12-15.5	EN 1090-2, Table 24, 12-15.5	EN 1090-2, Table 24, 12-15.5
Approved For Construction



Easpring New Materials Oy
FAIR Phase 1

SWECO
SWEVO RAKENNETEKNIIKKA OY
A.M.A. ARKITEHTIT OY
OJANHEIKKILÄ
P.O. BOX 107, FIN-00010
WWW.SWECO.FI

DRAWING CONTENT			
ASSEMBLY DRAWING	COLUMN W/	E51WC-1017	
DATE	12.06.2026	DESIGNED	STR
DRAWN	Alena Semis	CHECKED	STR
APPROVED	Alena Semis	APPROVED	STR
PROJECT CODE	25019443	PROJECT CODE	25019443
PROJECT NAME	E51WC-1017	PROJECT NAME	E51WC-1017




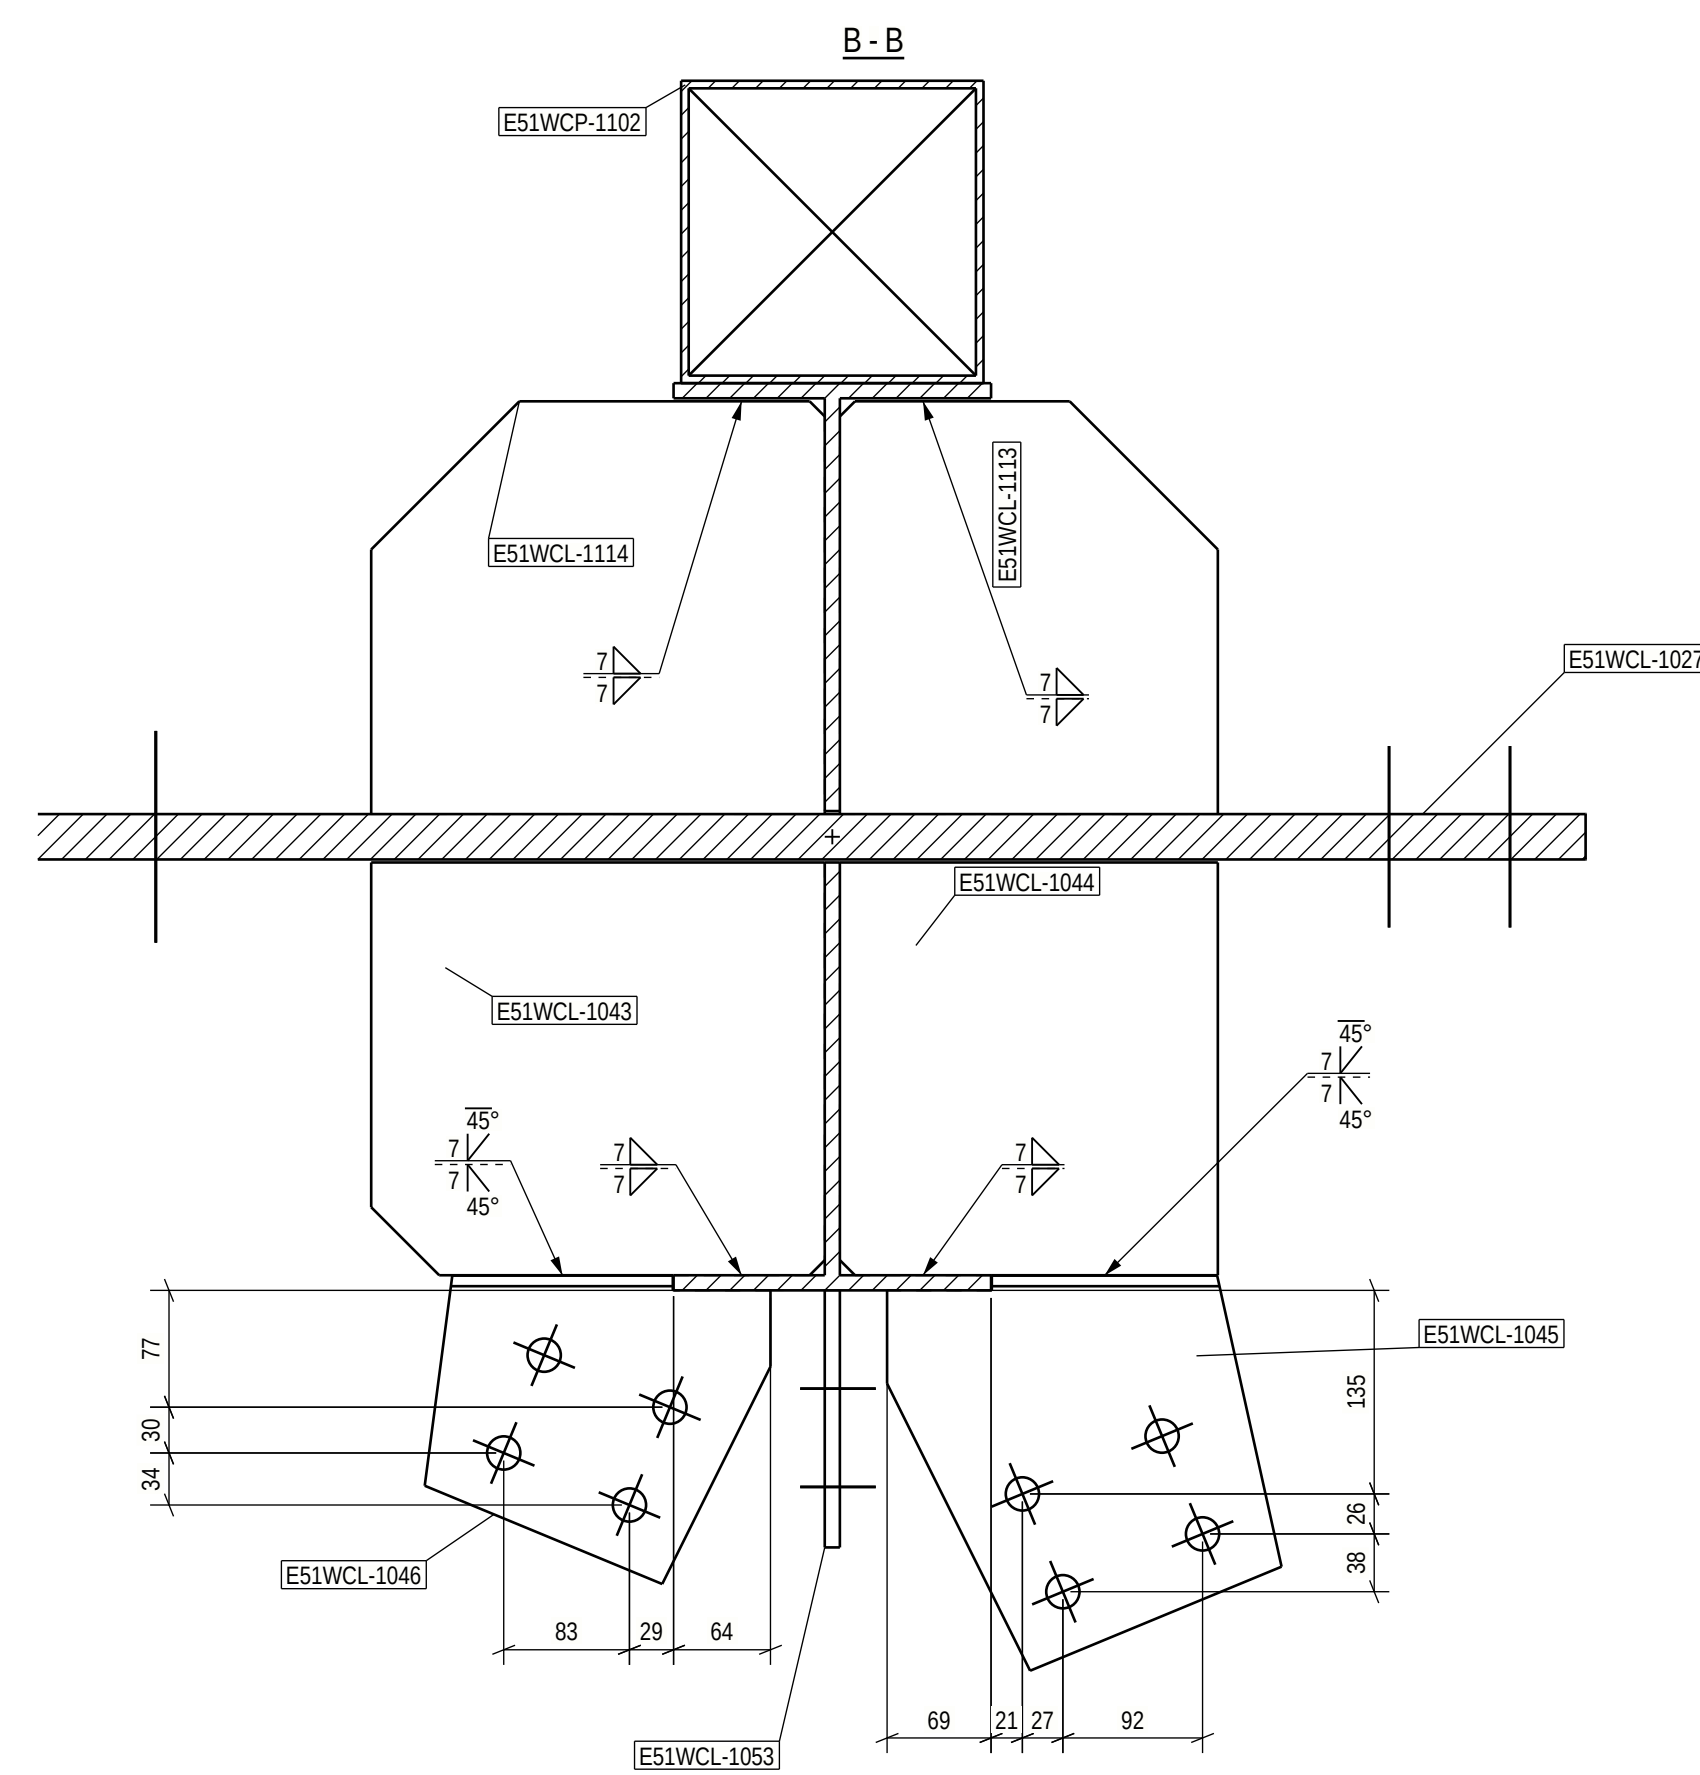


DET 4
Full contact in bearing, requirements
acc. to EN 1090-2/6.8 and 11.2.3.5
and project specification

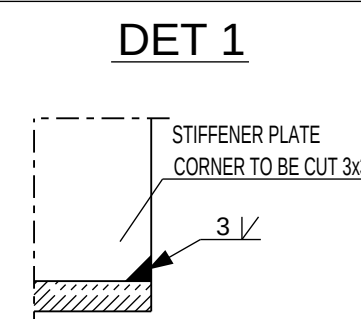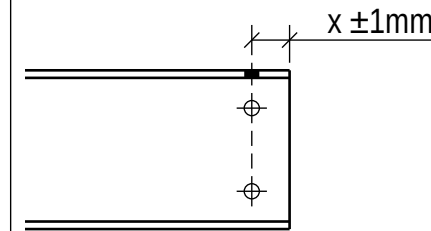


EXC2 Approved For Construction

PROJECT NAME Easpring New Materials Oy FAIR Phase 1				DRAWING CONTENT ASSEMBLY DRAWING COLUMN_VI E51WC-W18	
 SWECO RAKETTIENRAKENTAMINEN OY 6 VALMOKKATIE 12 00210 HELSINKI Puh. +358 207 367 000 www.sweco.fi		DATE 12.05.2025 DRAWN Almy Sanna 25019443		ARCHIVING CODE Designer Almy Sanna 25019443	
PAGE 1		APPROVED Perttu Hämäläinen 25019443		DESIGN GROUP STR Checked Jari Hallanen REVISION	

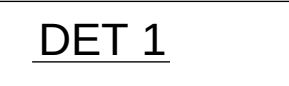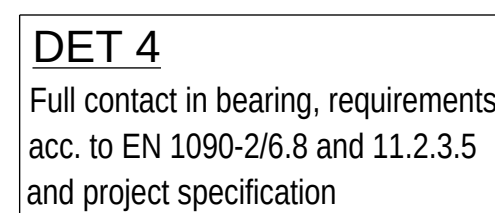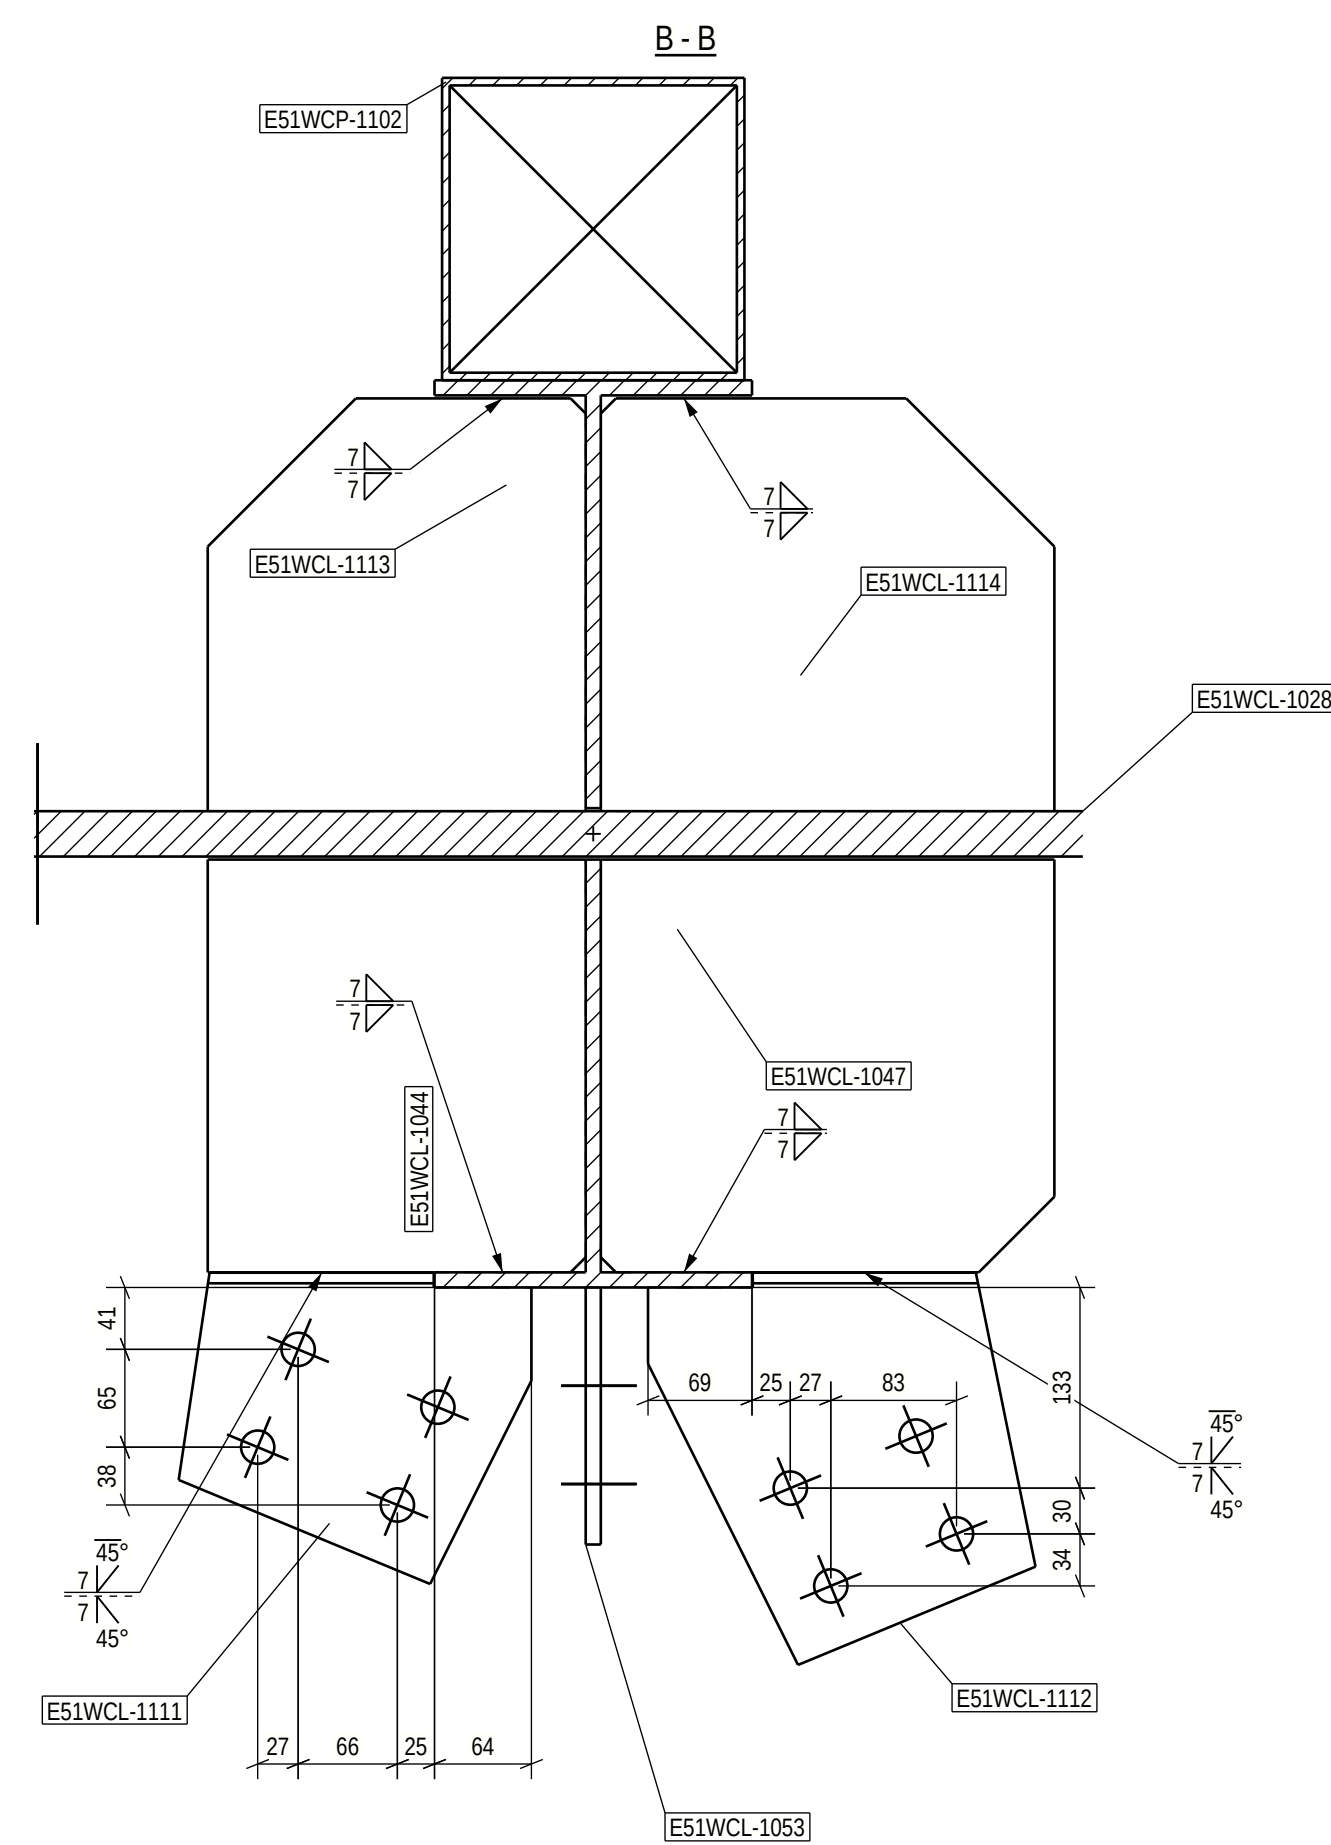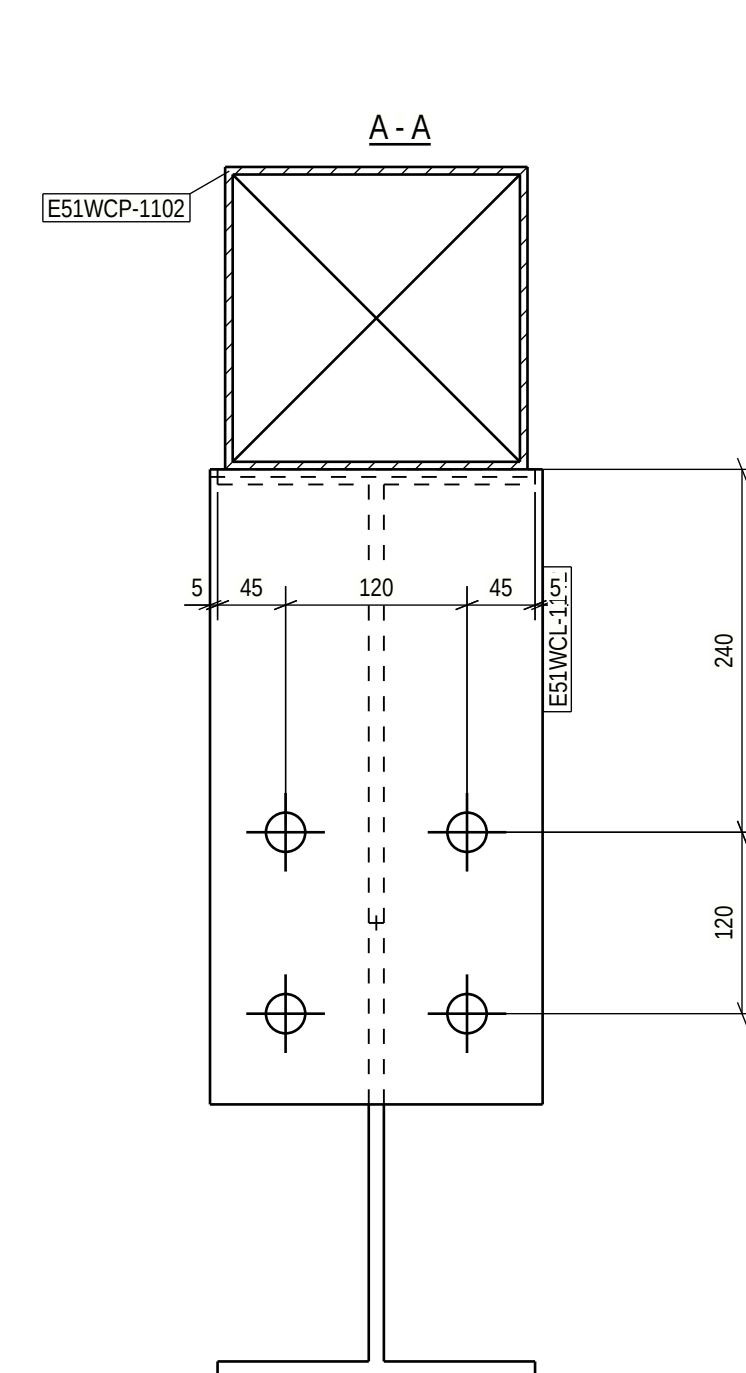[illegible]

Approved For Construction

PROJECT NAME: Easpring New Materials Oy
FAIR Phase 1

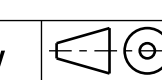


DRAWING CONTENT
ASSEMBLY DRAWING
COLUMN_WI
E51WC-1020



SWECO RAKENNET
ILMALANPORTTI 2
00240 HELSINKI
PUH. +358 207 393 00
www.sweco.fi

DATE 12.06.2026	ARCHIVING CODE	PAGE	DESIGN GROUP ST
DRAWN Alexey Sereus	DESIGNER Alexey Sereus	APPROVED Petr Kovalevskiy	CHECKED Jere Kallaste
PROJECT NUMBER 25019443	DWG. NO. E51WC-1020		

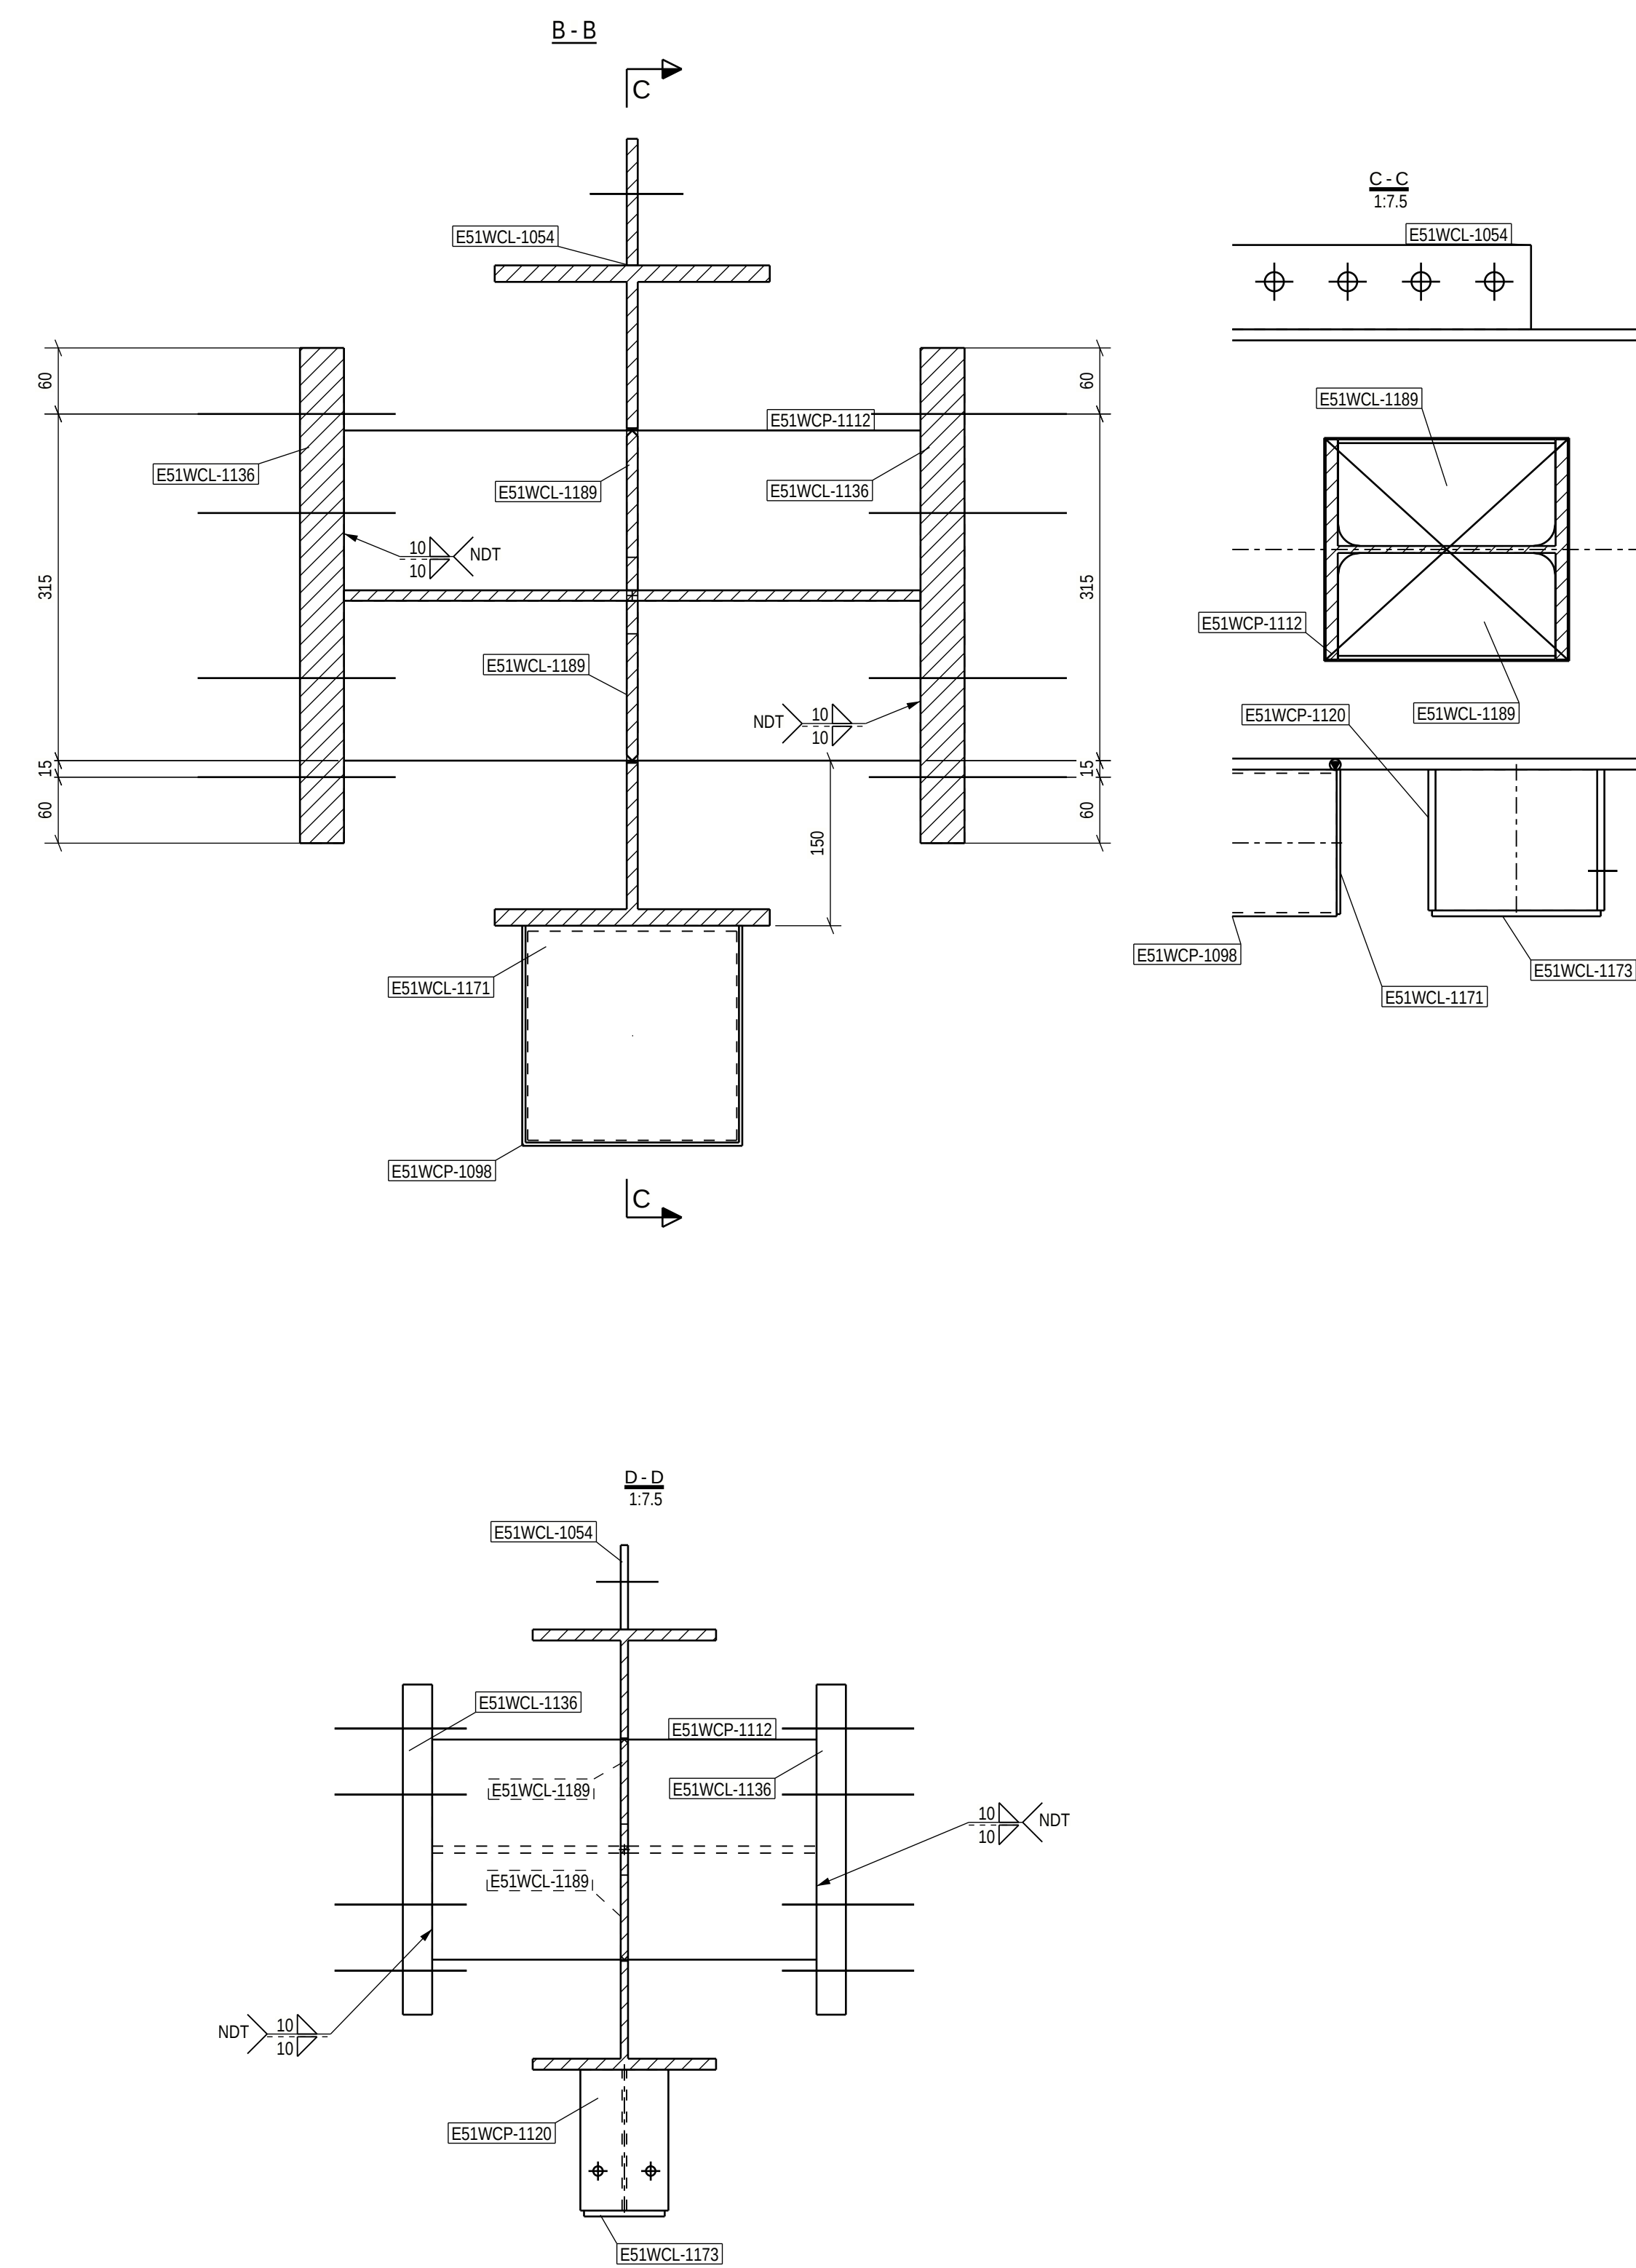


DET 4
Full contact in bearing, requirements acc. to EN 1090-2/6.8 and 11.2.3.5 and project specification

Tolerance for the first bolt group at the end of the beam:

$x \pm 1\text{mm}$





The diagram shows a cross-section of a beam with a vertical web and horizontal flanges. A bolt group is located at the end of the beam, with a dimension line indicating a tolerance of $x \pm 1\text{mm}$ from the end face to the center of the bolt group.

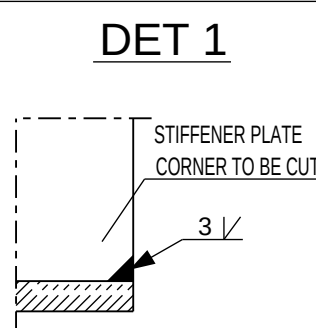


EXC2 own on drag. 0.5 of welds hot welds Additional material inspection Shown on drag.	Approved For Construction PROJECT NAME: Easpring New Materials Oy FAIR Phase 1 SWECO Sustainable engineering and design  SWECO RAKENNE JUMALANPORTTI 2 00240 HELSINKI Puh. +358 207 380 0 www.sweco.fi
---	---

	DRAWING CONTENT			
	ASSEMBLY DRAWING COLUMN_WI E51WC-1025			
NIKKA OY	DATE 12.06.2026	ARCHIVING CODE	PAGE	DESIGN GROUP STR
	DRAWN Alney Serus	DESIGNER Alney Serus	APPROVED Perti Kovanantane	CHECKED Jani Kalliohti
	PROJECT NUMBER 25019443		CUSC NO E51WC-1025	REVISION

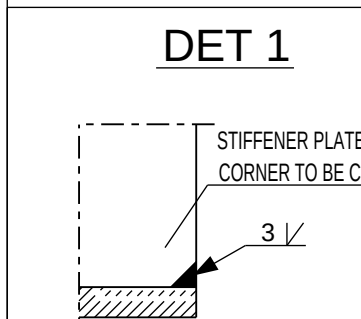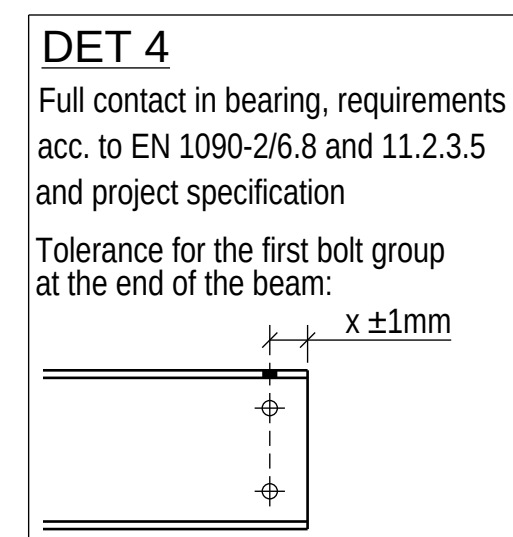[illegible]

EXC2 Approved For Construction

PROJECT NAME: **Easpring New Materials C**
FAIR Phase 1

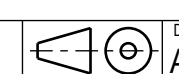


DRAWING CONTENT
ASSEMBLY DRAWING
COLUMN_WI
E51WC-1028



SWECO RAKENNETE
ILMALANPORTTI 2
00240 HELSINKI
Puh. +358 207 393 000
www.sweco.fi

DATE	APPROVED
2.05.2026	
DRAWN	CHECKED
Alexey Seryus	Alexey Seryus
PROJECT NUMBER	
25019443	

PAGE	DESIGN
APPROVED Peri Kovumangho	CHECKED Jere Kallio
DWG. NO. E51WC-1028	

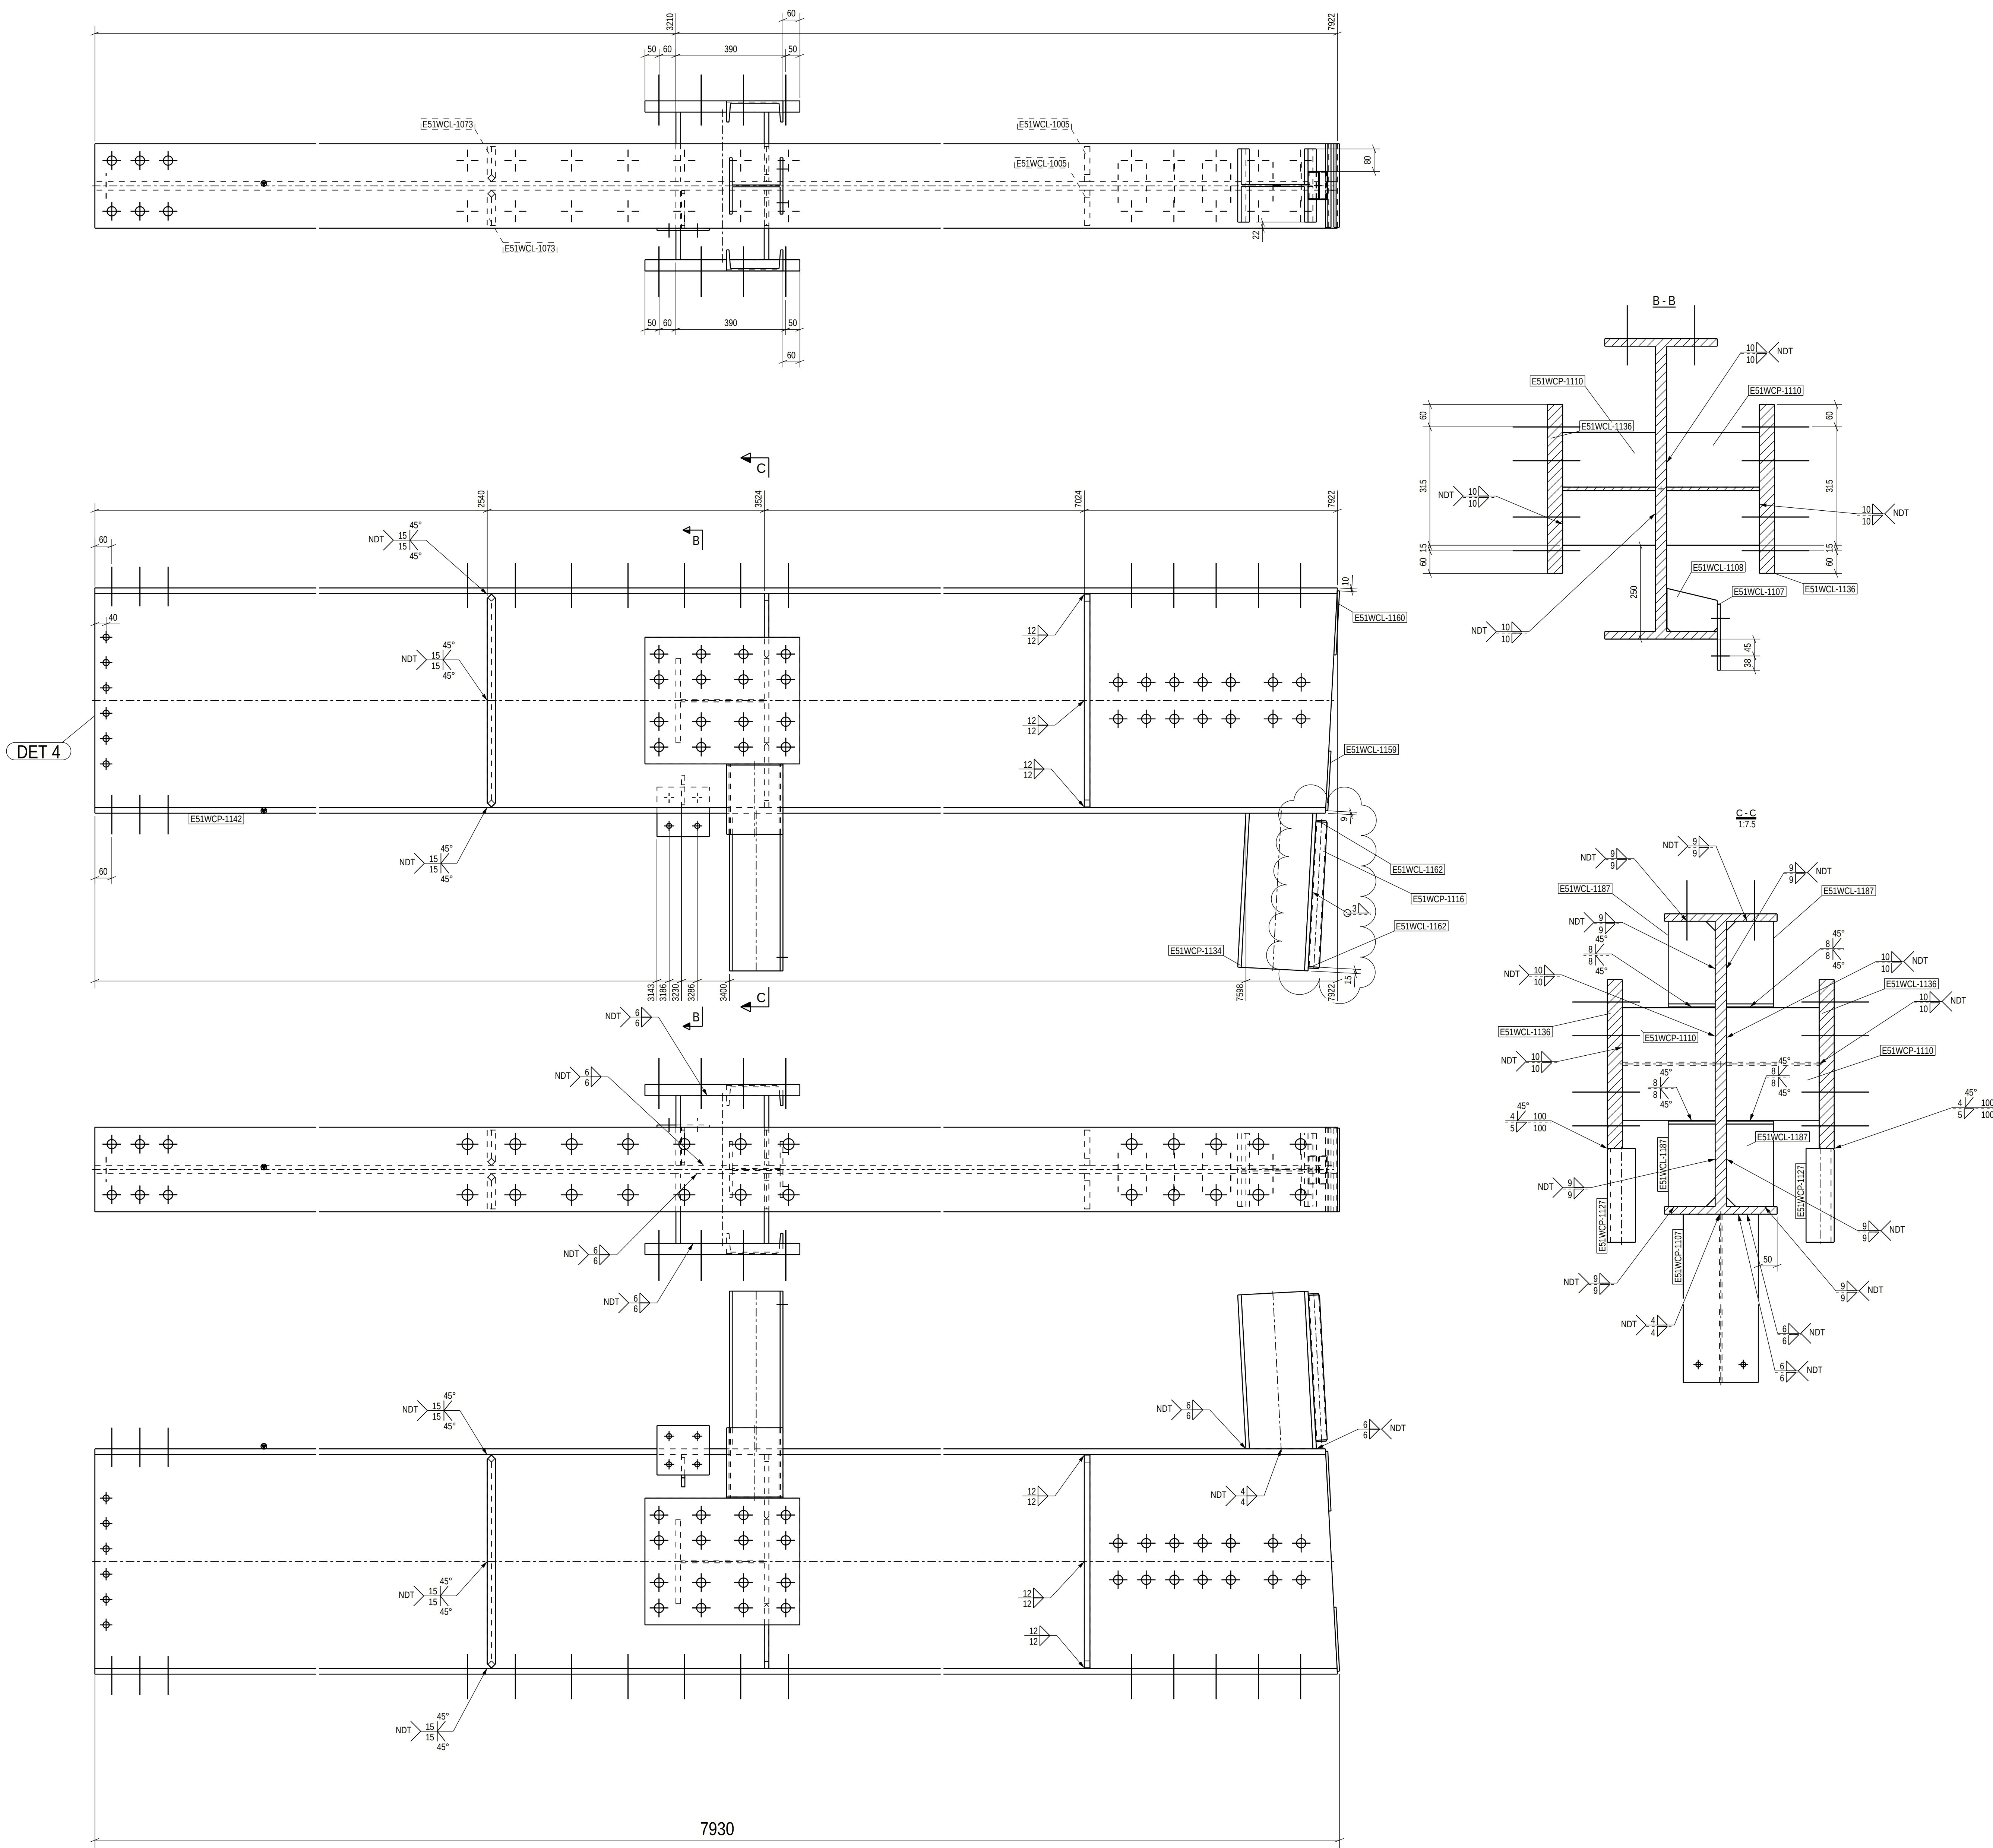

PART LIST FOR ASSEMBLY E51WC-1027. MANUFACTURING AMOUNT 1 PIECES							
PART	PROFILE	MATERIAL	LENGTH [mm]	AREA [m ²]	WEIGHT [kg]	PCS	
E51WCL-1005	PL20X125	S355J2+N	756	0.44	14.7	2	
E51WCL-1073	PL20X125	S355J2+N	756	0.44	20.5	2	
E51WCL-1107	PL8X176	S355J2+N	186	0.07	2.1	1	
E51WCL-1108	PL12X115	S355J2+N	134	0.03	1.2	1	
E51WCL-1136	PL40X450	S355J2+N	550	1.15	77.7	2	
E51WCL-1159	PL6X297	S355J2+N	212	0.13	4.0	1	
E51WCL-1160	PL8X297	S355J2+N	228	0.14	4.2	1	
E51WCL-1162	PL5X37	S355J2+N	94	0.02	0.1	2	
E51WCL-1187	PL16X125	S355J2+N	228	0.26	3.5	4	
E51WCP-1107	HEA200	S355J2	560	0.64	23.7	1	
E51WCP-1110	HEA300	S355J2	247	0.89	29.9	2	
E51WCP-1116	CFRHS100X40X3	S355J2H	515	0.14	3.2	1	
E51WCP-1127	UNP200	S355J2	250	0.33	6.3	2	
E51WCP-1134	HEA260	S355J2	561	0.83	38.2	1	
E51WCP-1142	WB800-30-20X300	S355J2	7922	21.72	2190.0	1	
TOTAL:				22.25	2571.0		

DET 4
Full contact in bearing, requirements acc. to EN 1090-2/6.8 and 11.2.3.5 and project specification
Tolerance for the first bolt group at the end of the beam:
x ±1mm


DET 1

Technical fabrication requirements:		EXC2	
EN 1090-2, Table A.3, EXC2	EN 1090-2, Appendix B	EN 1090-2, Appendix B	EN 1090-2, Appendix B
EN 1090-2, Table A.3, EXC2	EN 1090-2, Appendix B	EN 1090-2, Appendix B	EN 1090-2, Appendix B
Approved For Construction

PROJECT NAME		DRAWING CODE		DATE		CHECKED BY	
Easpring New Materials Oy		25019443		12.06.2026		STR	
FAIR Phase 1		25019443		17.06.2026		STR	
01		Hollow section added		17.06.2026		STR	
EN 1090-2		EN 1090-2		EN 1090-2		EN 1090-2	
EN 1090-2		EN 1090-2		EN 1090-2		EN 1090-2	
SWECO		SWECO RAKENITEKNIIKKA OY		25019443	
SWECO RAKENITEKNIIKKA OY		SWECO RAKENITEKNIIKKA OY		25019443	
SWECO RAKENITEKNIIKKA OY		SWECO RAKENITEKNIIKKA OY		25019443	
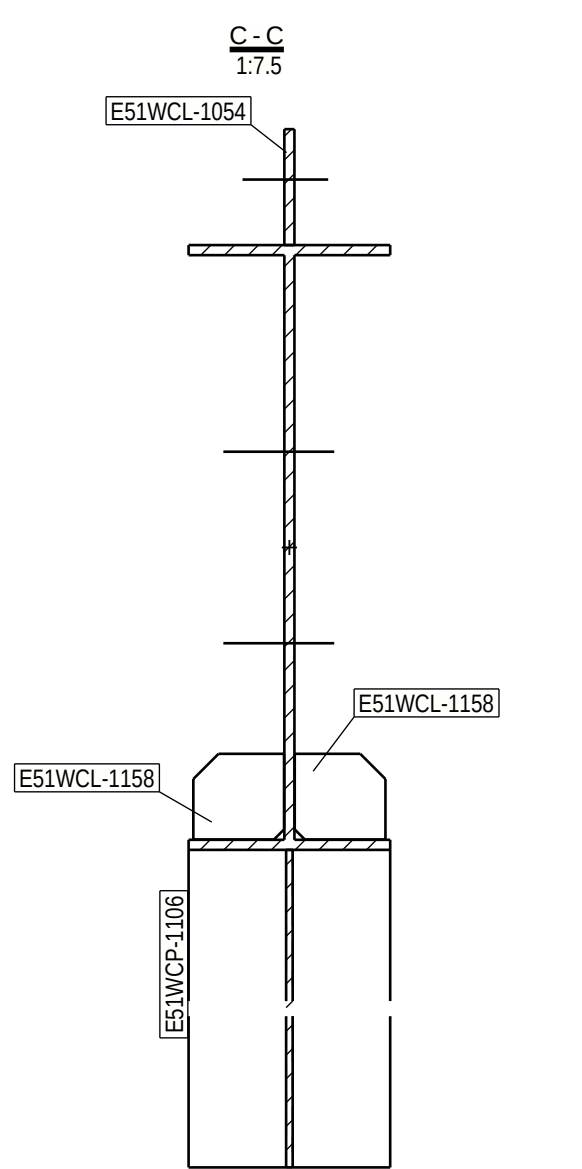

	DRAWING CONTENT			
	ASSEMBLY DRAWING COLUMN_WI E51WC-1063			
ENIKKKA OY 25019443	DATE 12.06.2026	ARCHIVING CODE	PAGE	DESIGN GROUP STR
	DRAWN Ariy Seryus	DESIGNER Ariy Seryus	APPROVED Pertti Kuusmanaho Sari V&S	CHECKED Jari Kalliozalm REVISIO
	25019443		E51WC-1063	

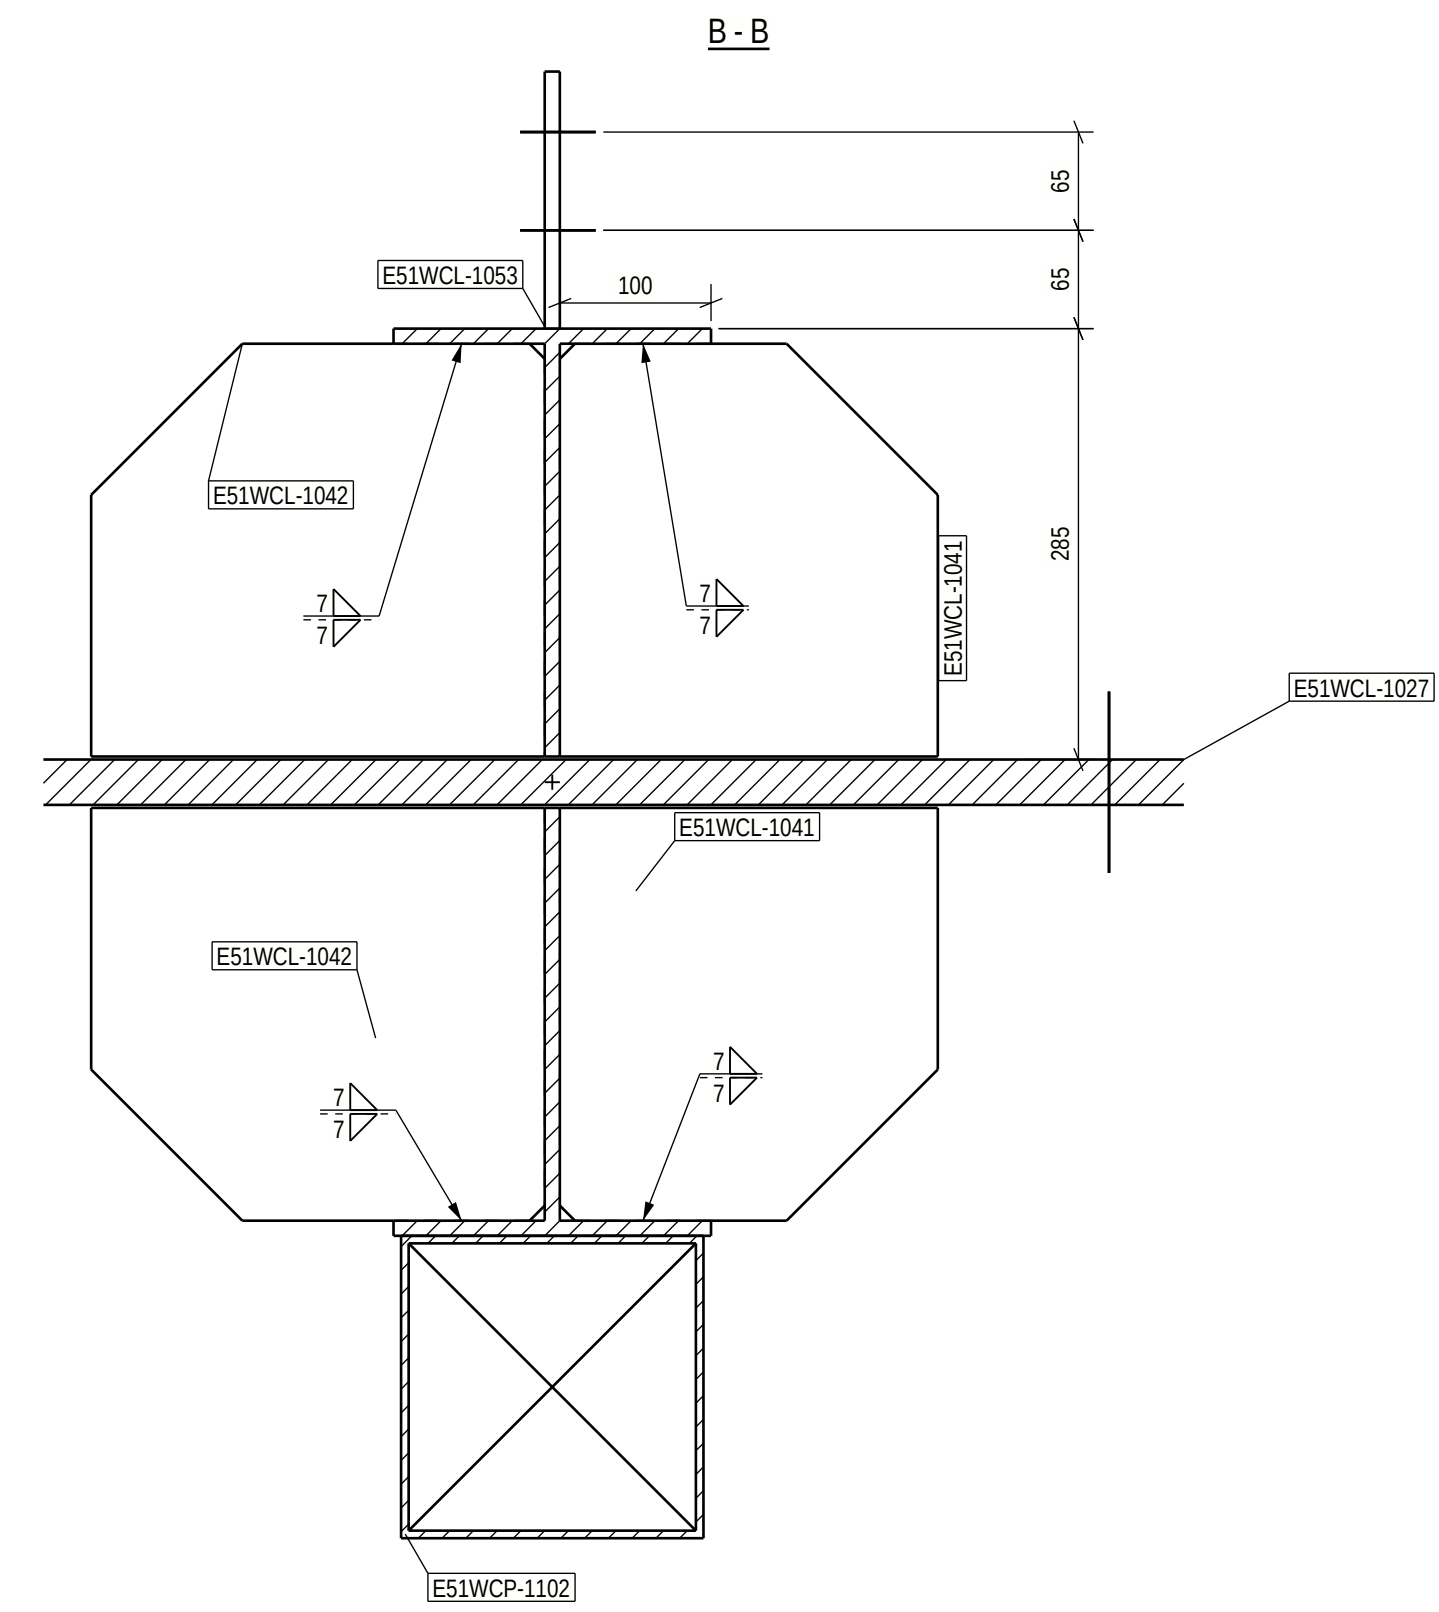


GONIKHA OY	DATE	ARCHIVING CODE	PAGE	DESIGN GROUP
	12.06.2026			STR
	DRAWN	DESIGNER	APPROVED	CHECKED
	Alexy Seros	Alexy Seros	Petr Kovalevskiy	Igor Kalashnikov
	PROJECT NUMBER		DWG. NO.	REVISIONS
	25019443		E51WC-1067	

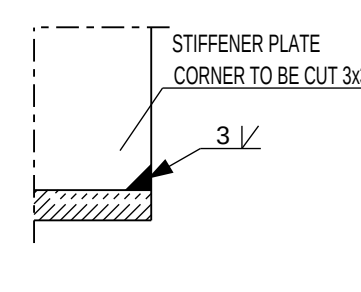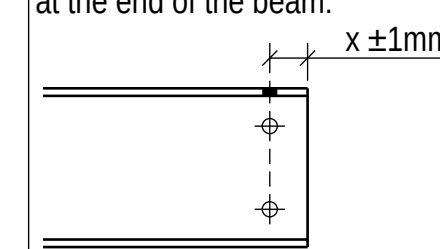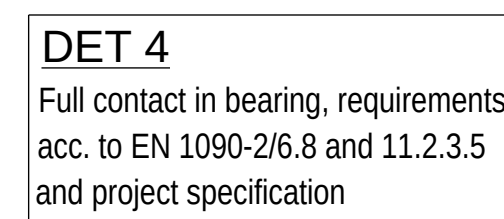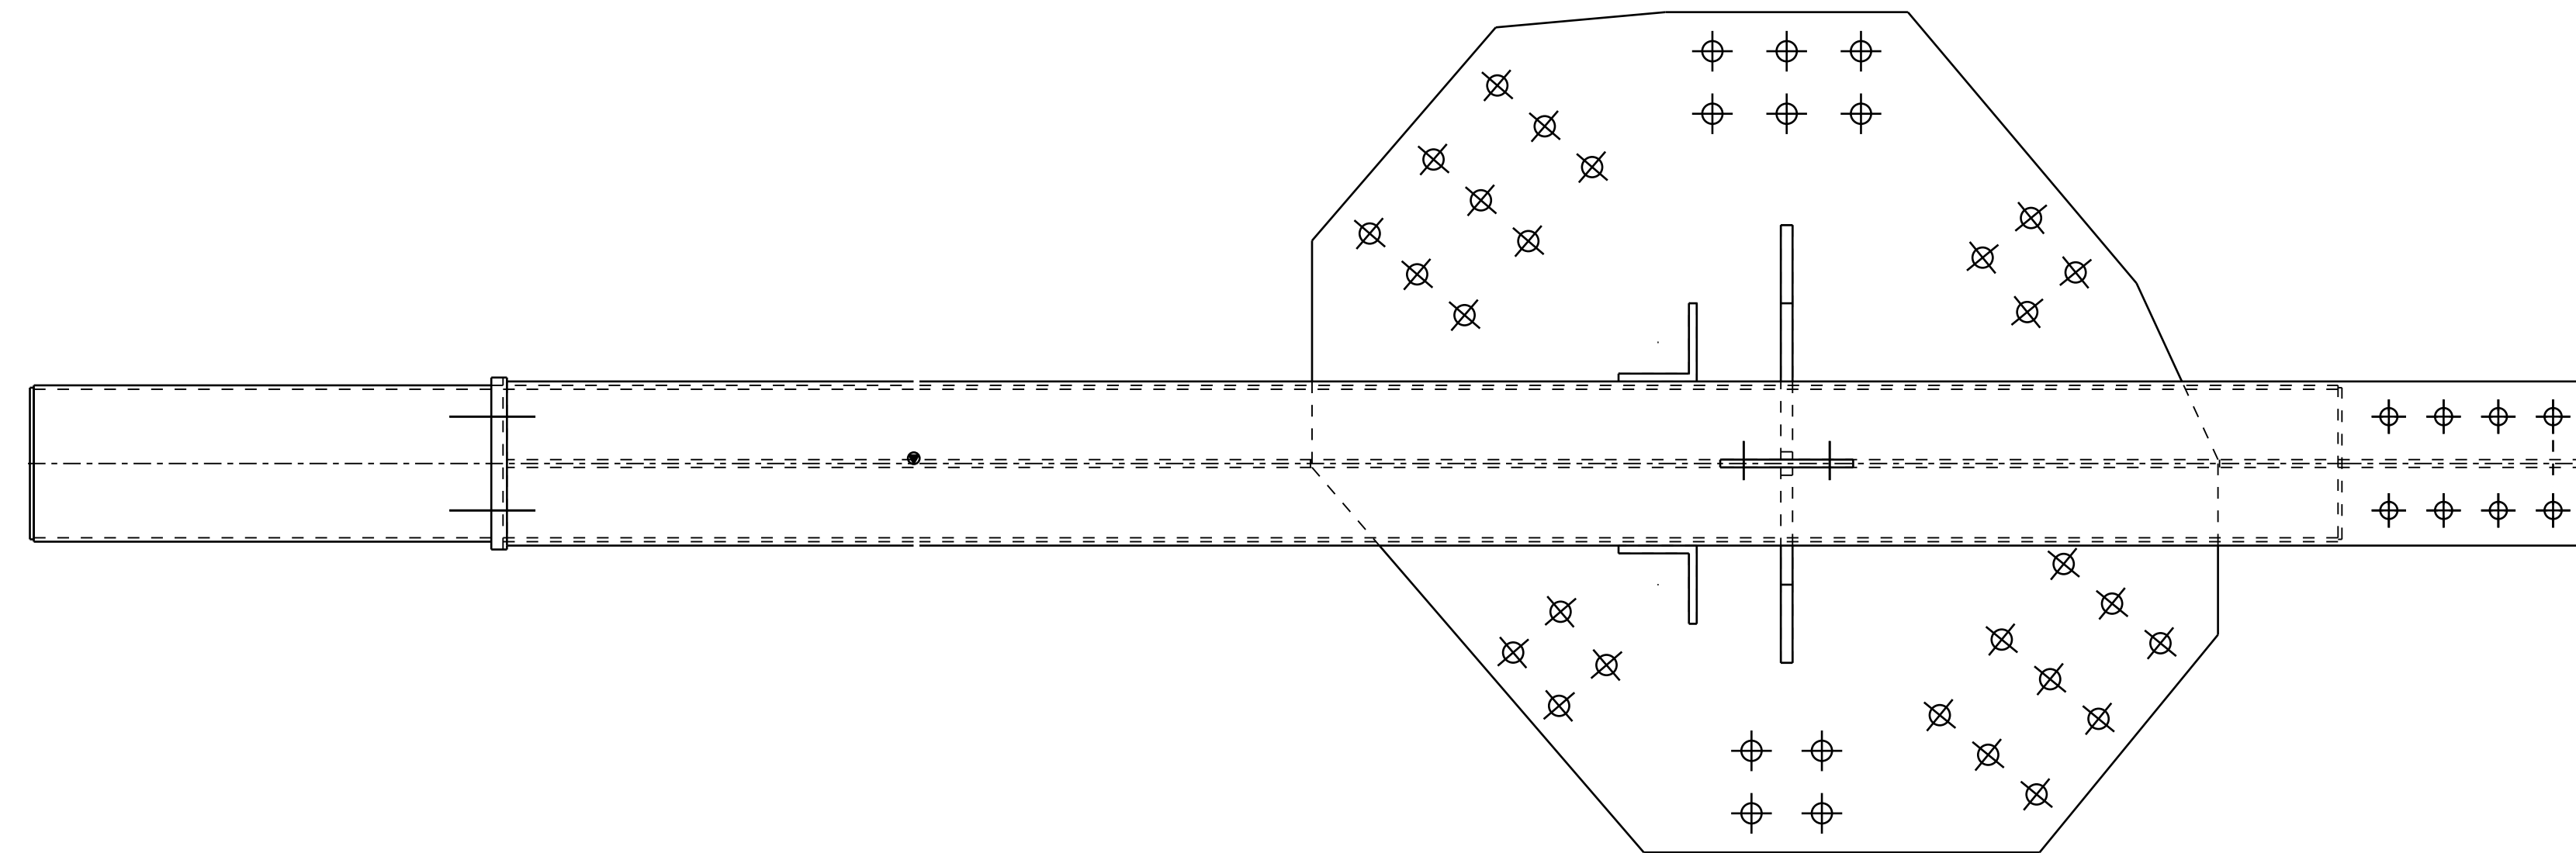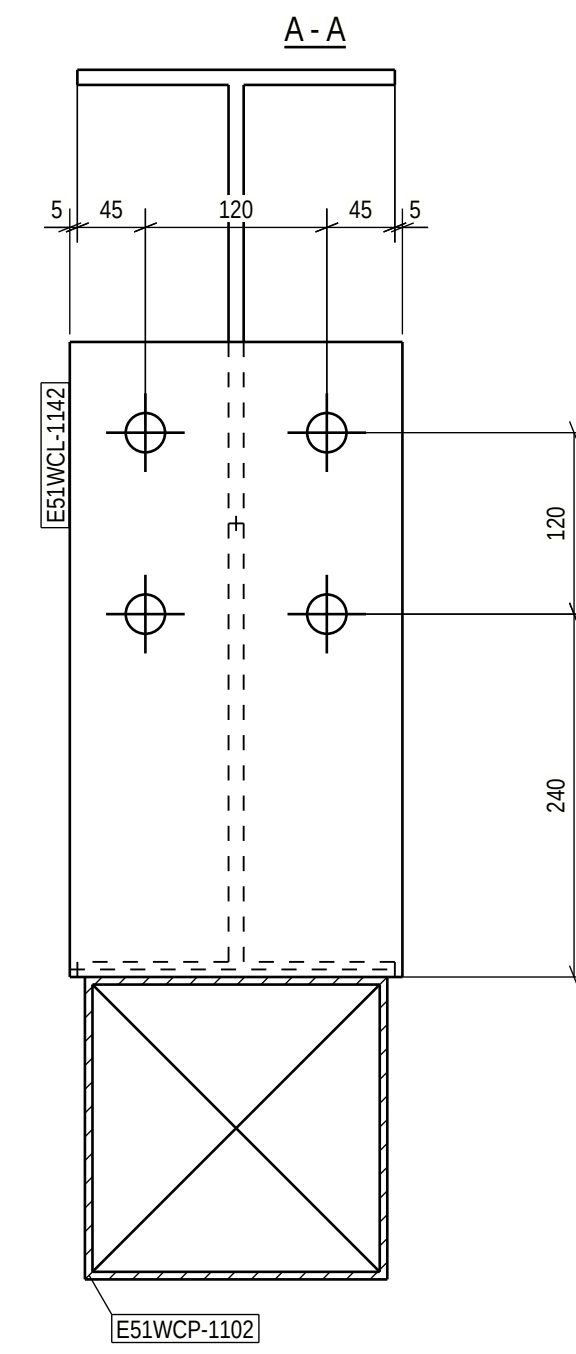

Approved For Construction

PROJECT NAME: **Easpring New Materials Oy**
FAIR Phase 1

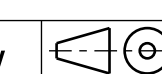

DRAWING CONTENT
ASSEMBLY DRAWING
COLUMN_WI
E51WC-1068



SWECO RAKENNET
ILMALANPORTTI 2
00240 HELSINKI
PUH. +358 207 393 00
WWW.SWECO.FI

TEKNIKKKA OY

DATE	12.01
DRAWN BY	Alexy
PROJECT	25

5.2026
N
Syrus
ECT NUMBER
01944




ARCHIVING CODE
DESIGNER
Alejo José
3

DATE	PAGE
APPROVED	
Per: KAV	
CHG. NO.	
E51	

WC-10

DESIGN GROUP
STR
CHECKED
re Kallosalmi
REVISION
068

PART LIST FOR ASSEMBLY E51WC-1008, MANUFACTURING AMOUNT 1 PIECES						
PART	PROFILE	MATERIAL	LENGTH [mm]	AREA [cm ²]	WEIGHT [kg]	PCS
E51WC-1008	PL20X20	S355J2+N	1158	2,05	228,9	1
E51WC-1008	PL15X50	S355J2+N	273	0,28	7,4	2
E51WC-1008	PL10X73	S355J2+N	300	0,30	4,0	2
E51WC-1008	PL10X73	S355J2+N	120	0,06	2,3	1
E51WC-1142	PL20X20	S355J2+N	420	0,21	14,5	1
E51WC-1171	PL5X14	S355J2+N	197	0,16	1,5	2
E51WC-1010	W600-10-10X210	S355J2	5180	10,43	408,5	1
E51WC-1001	LF10H	S355J2+N	270	0,43	4,2	4
E51WC-1102	CPRM30X200X5	S355J2H	5470	4,28	164,7	1
			200	0,01	12,92	12

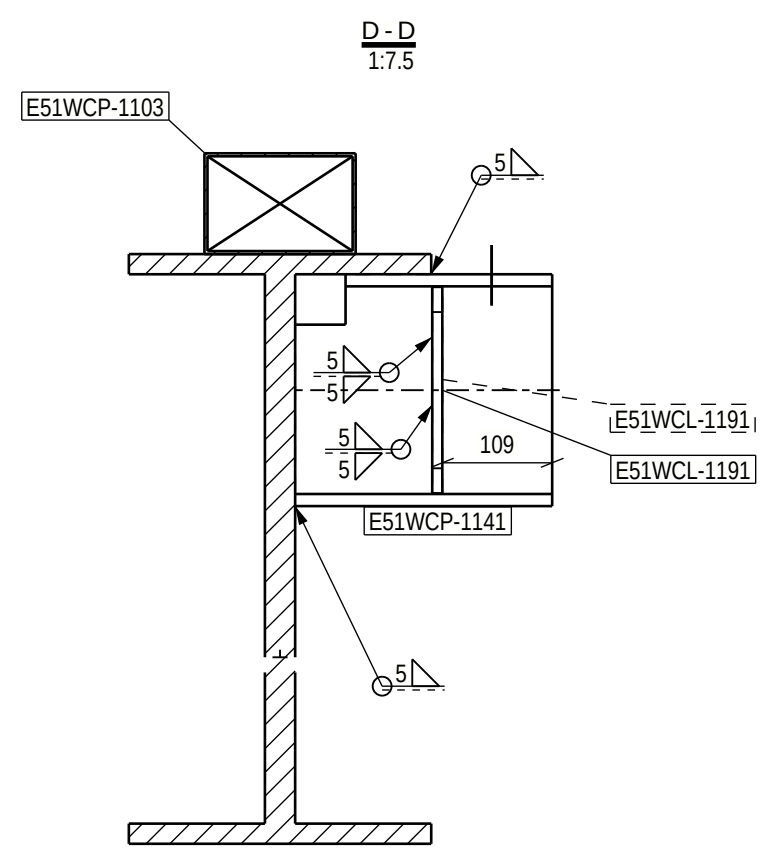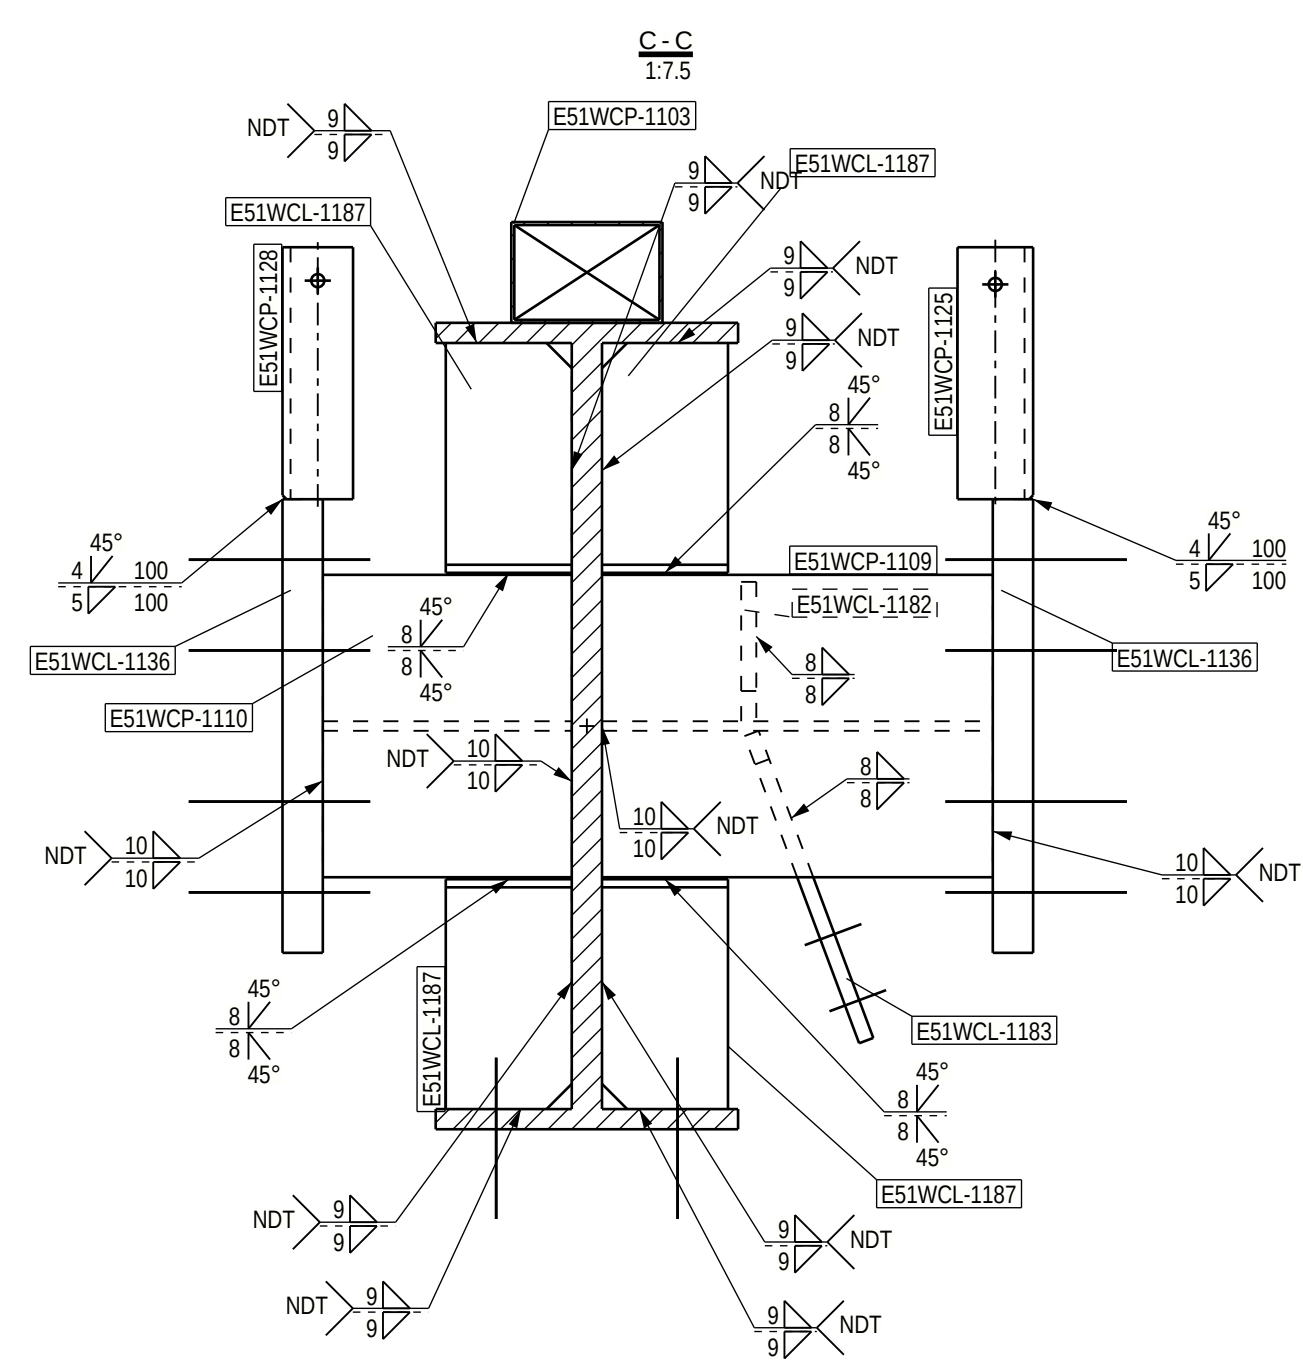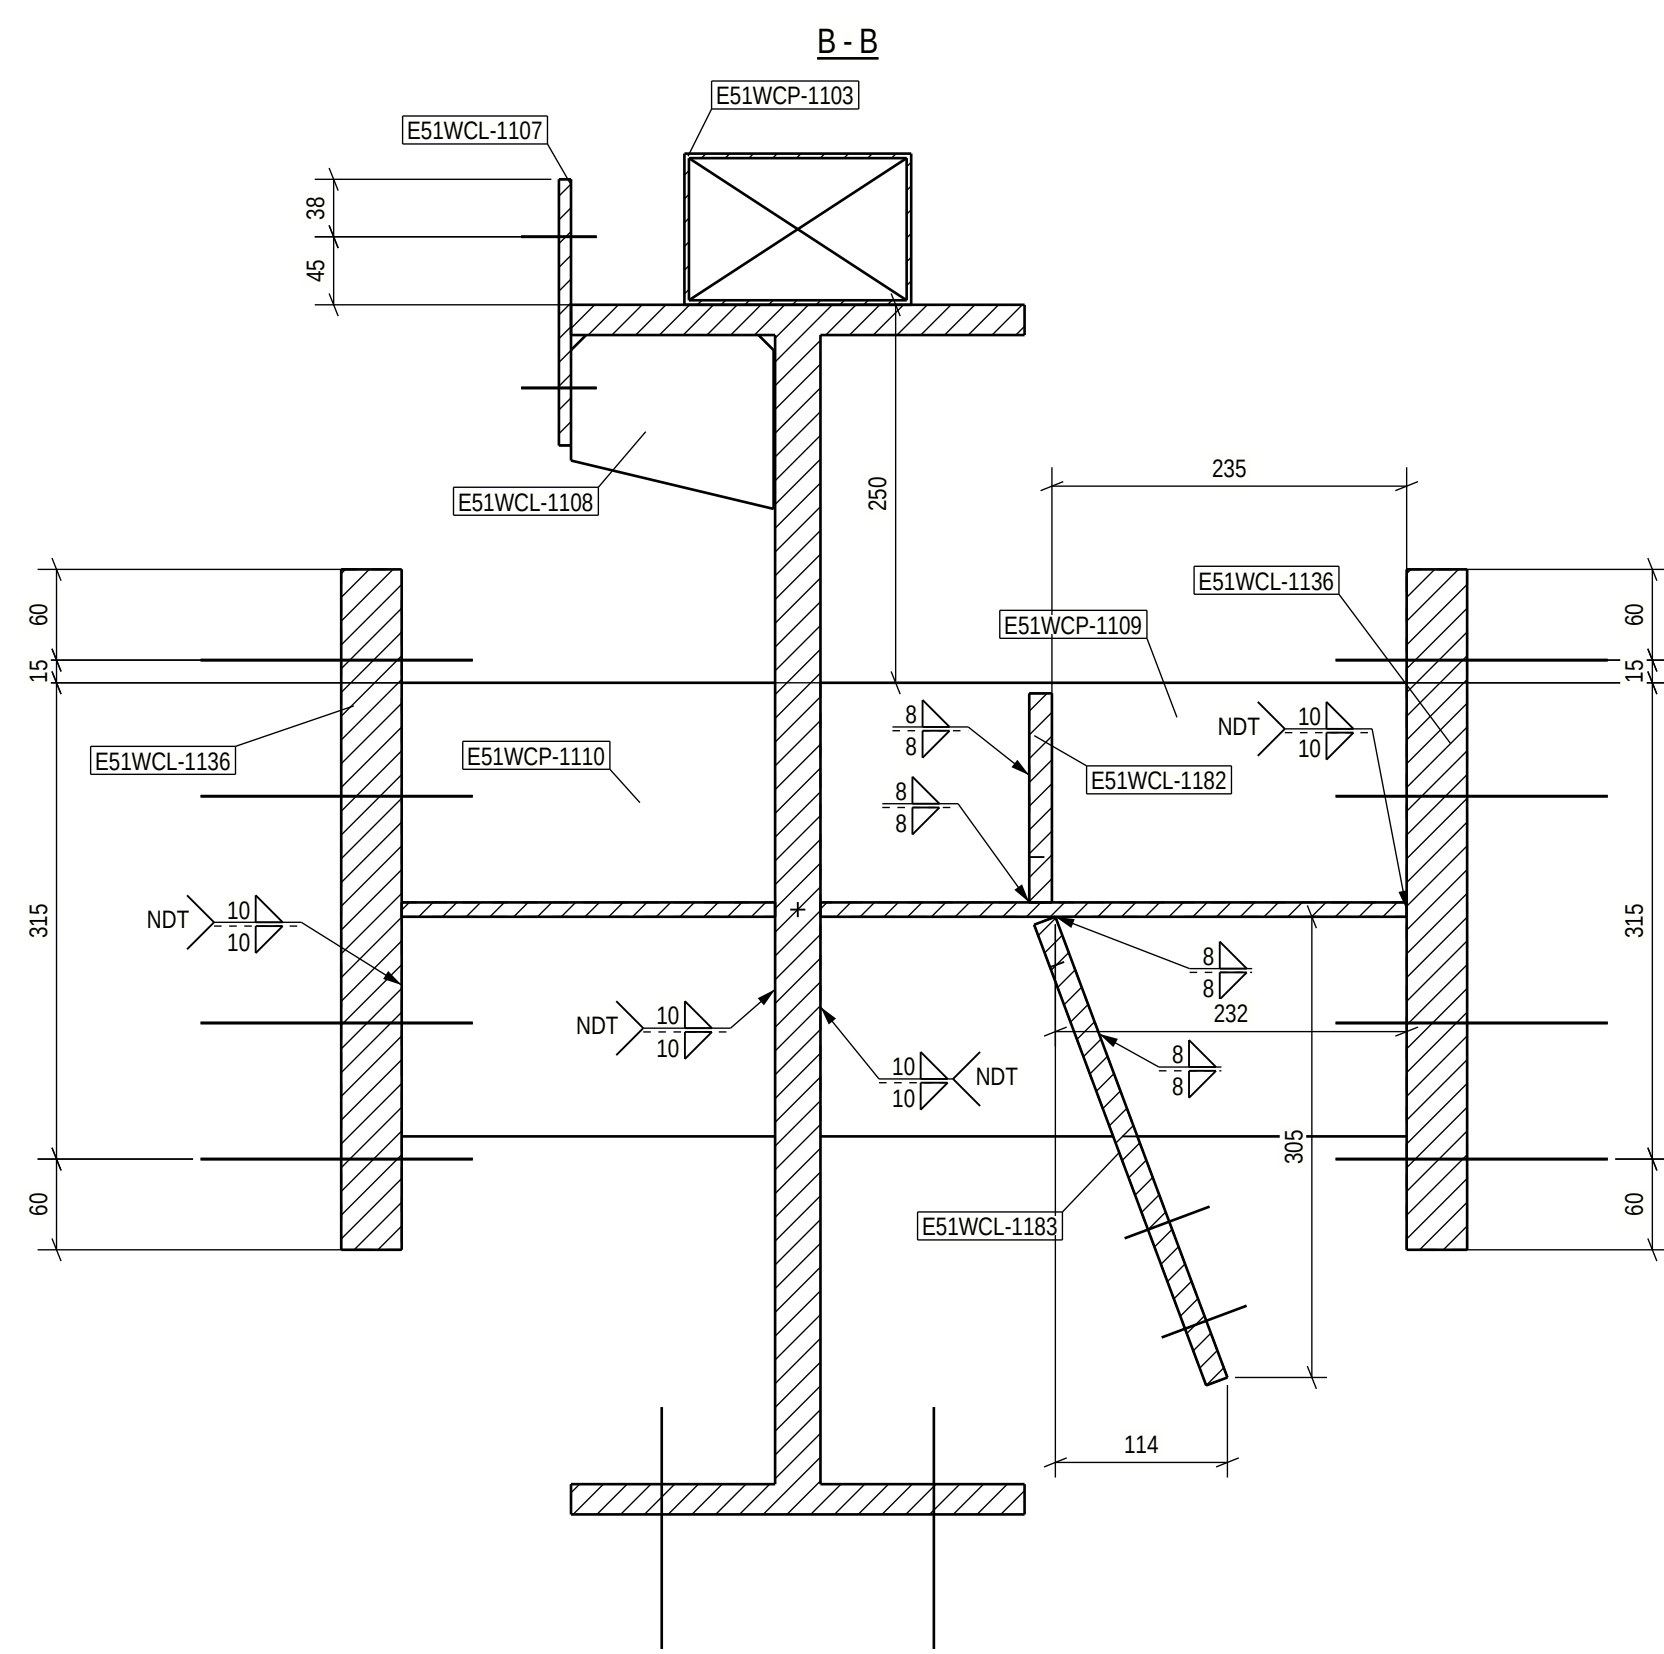

at the end of the beam:



The diagram shows a cross-section of a beam with a vertical line of three bolts. The top bolt is positioned at a distance of $x \pm 1\text{mm}$ from the right edge of the beam.

STIFFENER PLATE
CORNER TO BE CUT 3x

3x

Execution data	EXC2
----------------	------










PROJECT NAME
Easpring New Materials Oy
FAIR Phase 1

SWECO 
Sustainable engineering and design

	C
	E
KNIKKA OY	D
	J
	P
	A


DRAWING CONTENT			
ASSEMBLY DRAWING			
COLUMN_WI			
E51WC-1072			
DATE 2.06.2026	ARCHIVING CODE	PAGE	DESIGN GROUP STR
DRAWN BY Alamy Serus	DESIGNER Alamy Serus	APPROVED Perit Kusumastara	CHECKED Jani Kallioinen
PROJECT NUMBER 25019443	DWG. NO. E51WC-1072		REVISION

PART LIST FOR ASSEMBLY E51WC-1072, MANUFACTURING ANTI 1 PIECES						
PART	PROFILE	MATERIAL	LENGTH [mm]	AREA [cm ²]	Wgt [kg]	PCS
E51WC-1005	L30X125	S355JR	755	2.4	4.4	2
E51WC-1007	L30X125	S355JR	755	0.4	20.5	2
E51WC-1017	PL06X76	S355J2AN	186	0.07	2.1	1
E51WC-1018	L12X125	S355J2AN	134	0.03	1.2	1
E51WC-1106	PL40X40	S355J2AN	550	1.5	77.7	2
E51WC-1108	P40X20	S355J2AN	228	0.14	4.2	1
E51WC-1161	S355J2AN	S355J2AN	281	0.18	5.2	1
E51WC-1169	PL03X44	S355J2AN	97	0.06	0.5	1
E51WC-1181	SL15X138	S355J2AN	296	0.09	4.8	1
E51WC-1182	S355J2AN	S355J2AN	325	0.27	11.3	1
E51WC-1187	PL18X125	S355J2AN	228	0.26	3.5	4
E51WC-1191	SL10X107	S355J2AN	205	0.20	1.7	4
E51WC-1015	W800-30-15	S355J2AN	8385	22.99	2317.9	1
E51WC-1015	W15-15-15-15	S355J2AN	1050	0.62	34.4	1
E51WC-1103	HEX40	S355J2AN	85	0.06	2.1	1
E51WC-1103	CFR45HSX100X3	S355J2AN	7630	3.74	86.1	1
E51WC-1110	HEX40	S355J2AN	70	0.06	1	1
E51WC-1110	S355J2AN	S355J2AN	247	0.44	25.9	1
E51WC-1125	UNP20	S355J2AN	250	0.17	6.3	1
E51WC-1125	HEX40	S355J2AN	250	0.15	5.1	1
E51WC-1141	HEX40	S355J2AN	250	0.70	15.4	2
TOTAL					38.8	3626.1

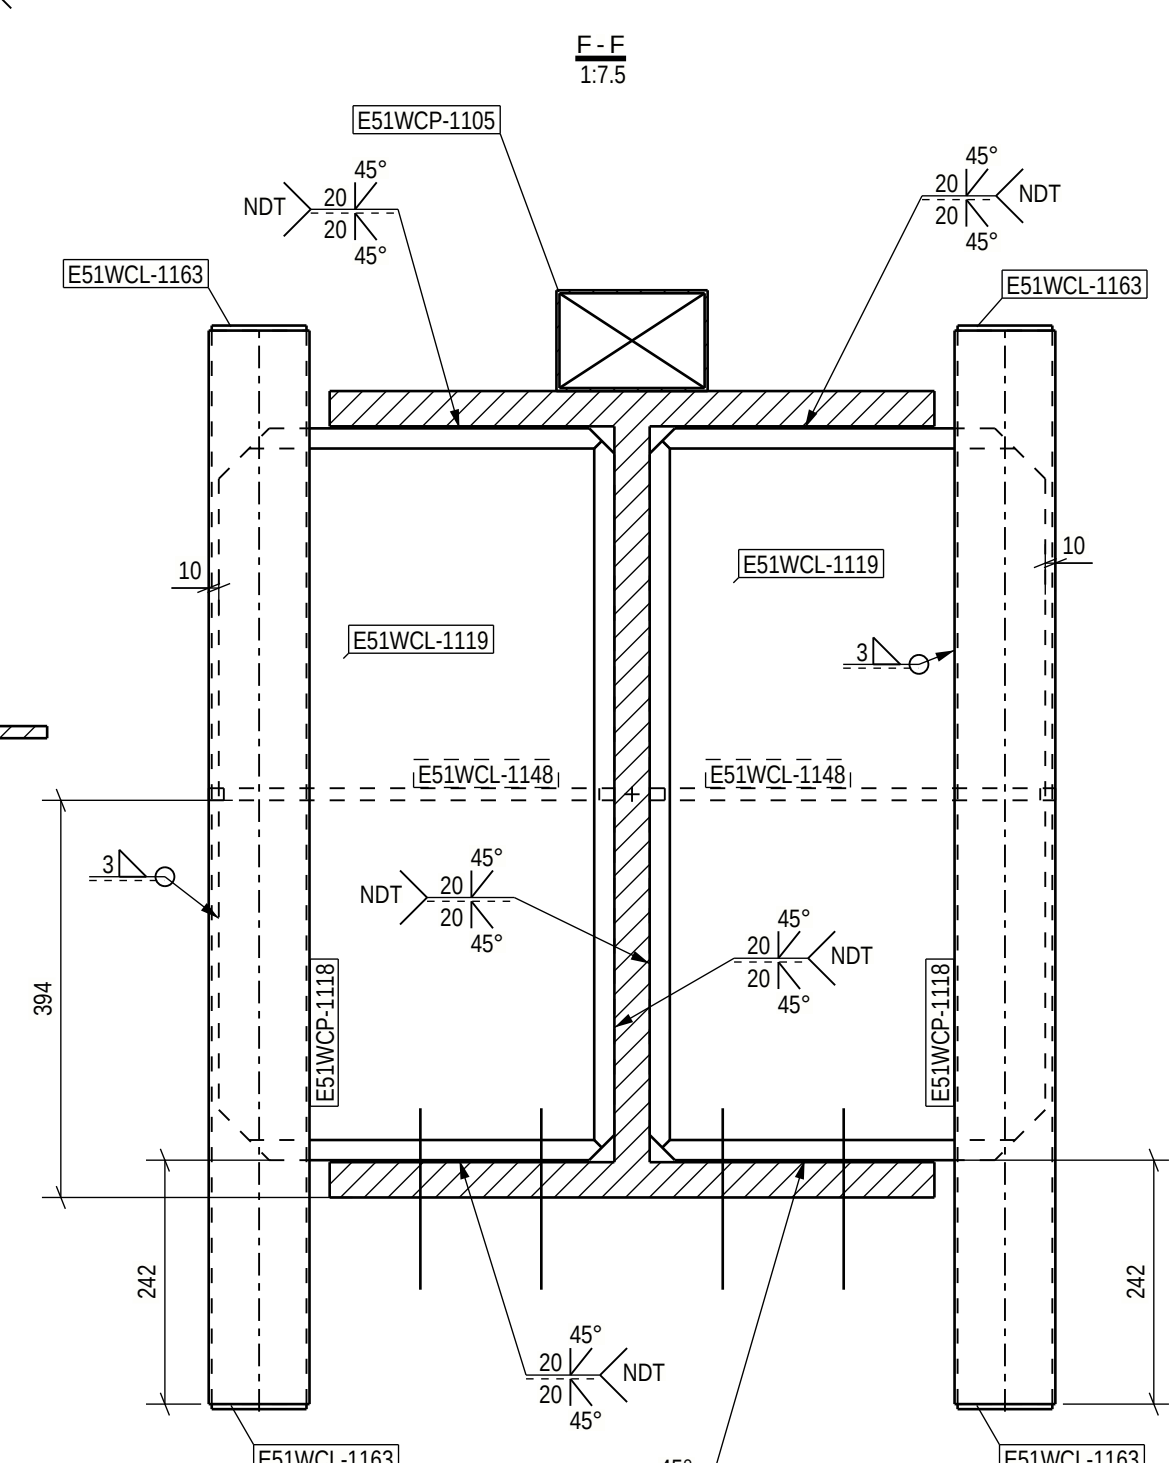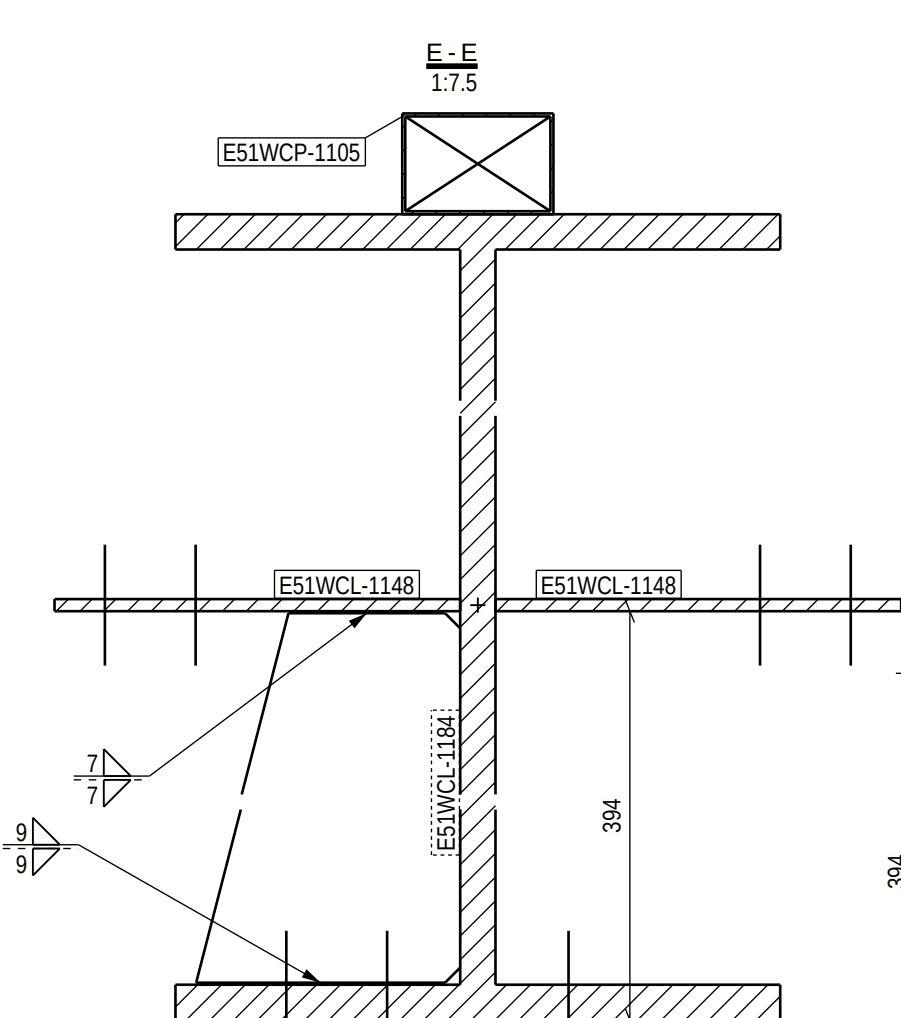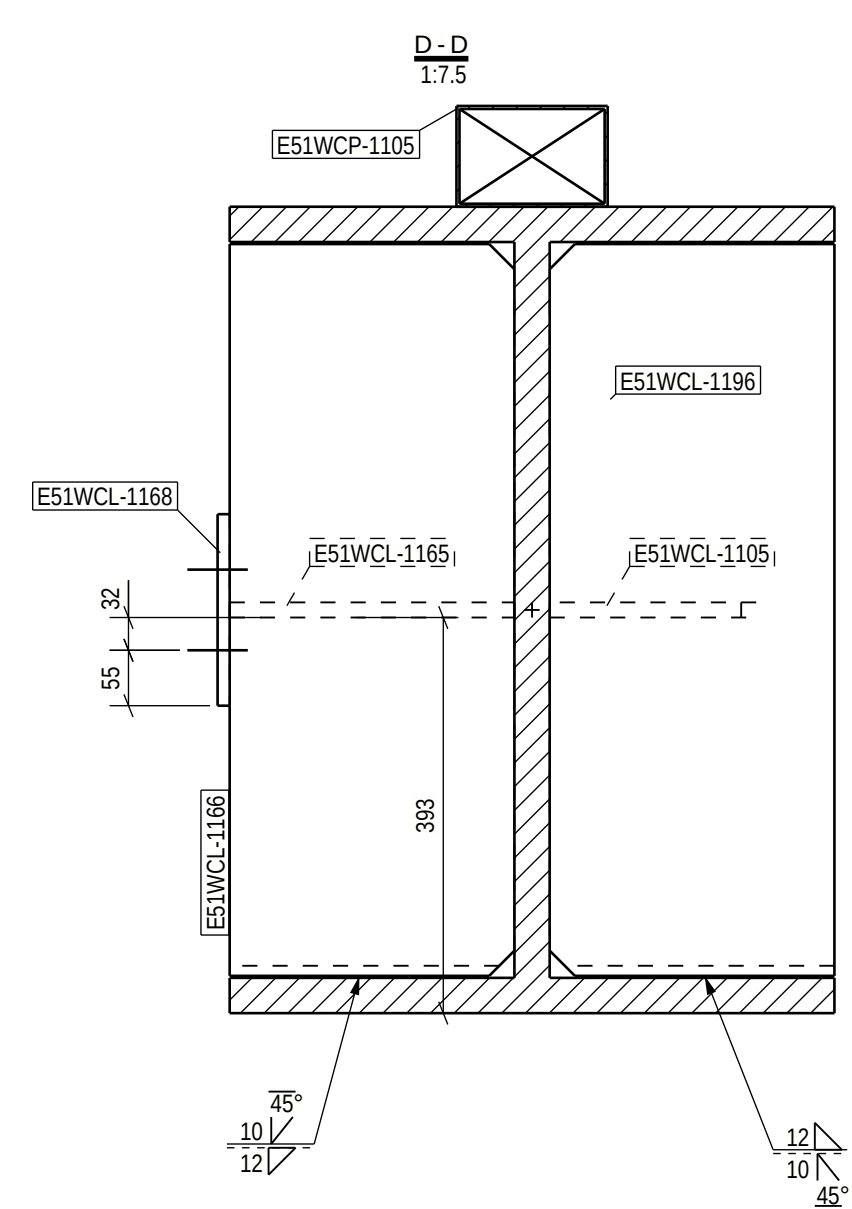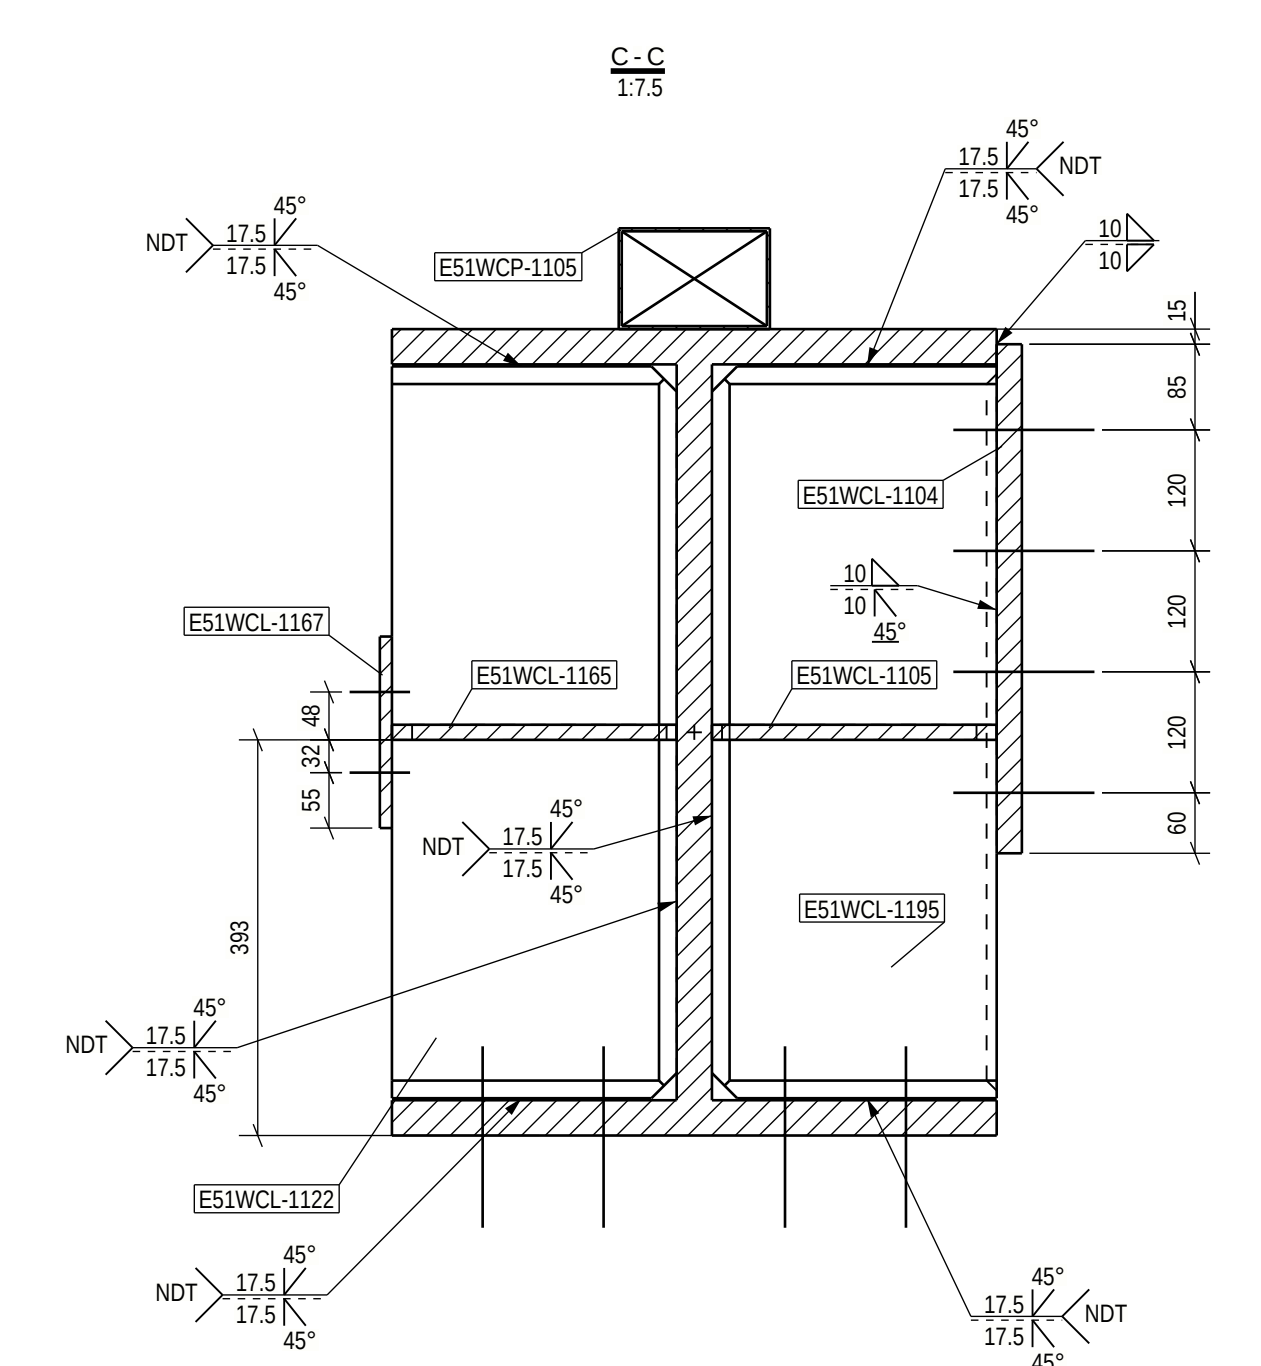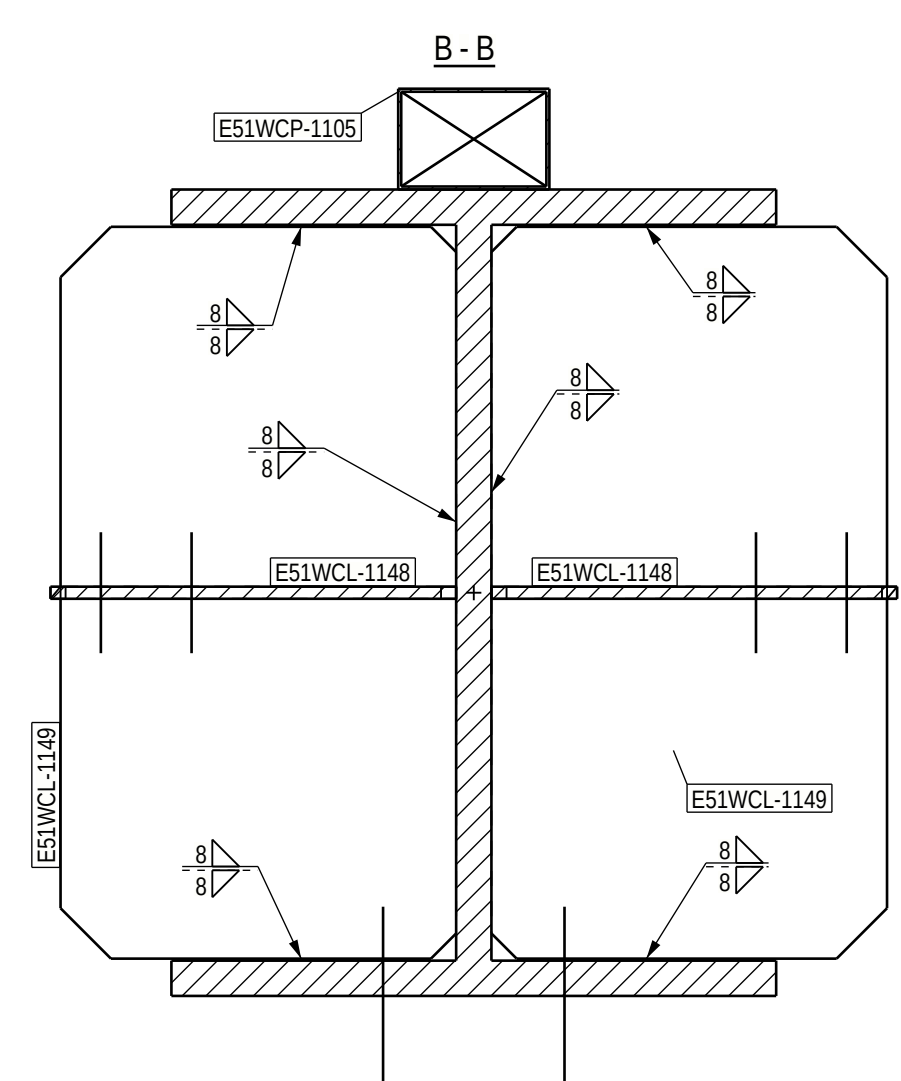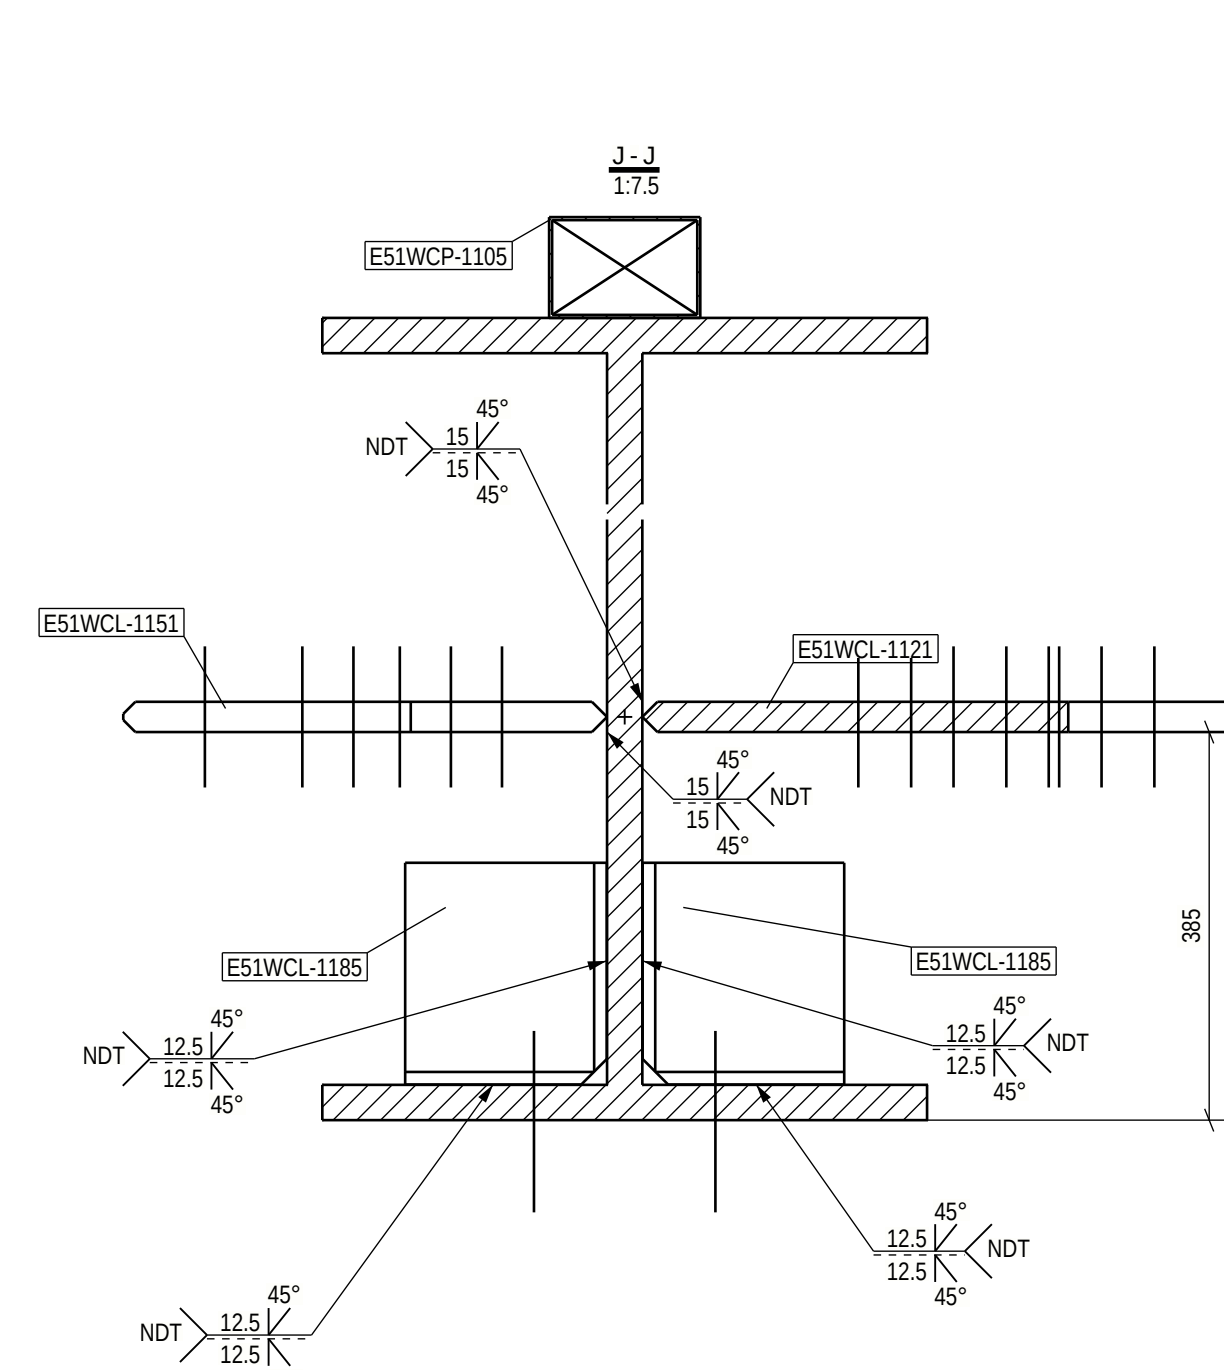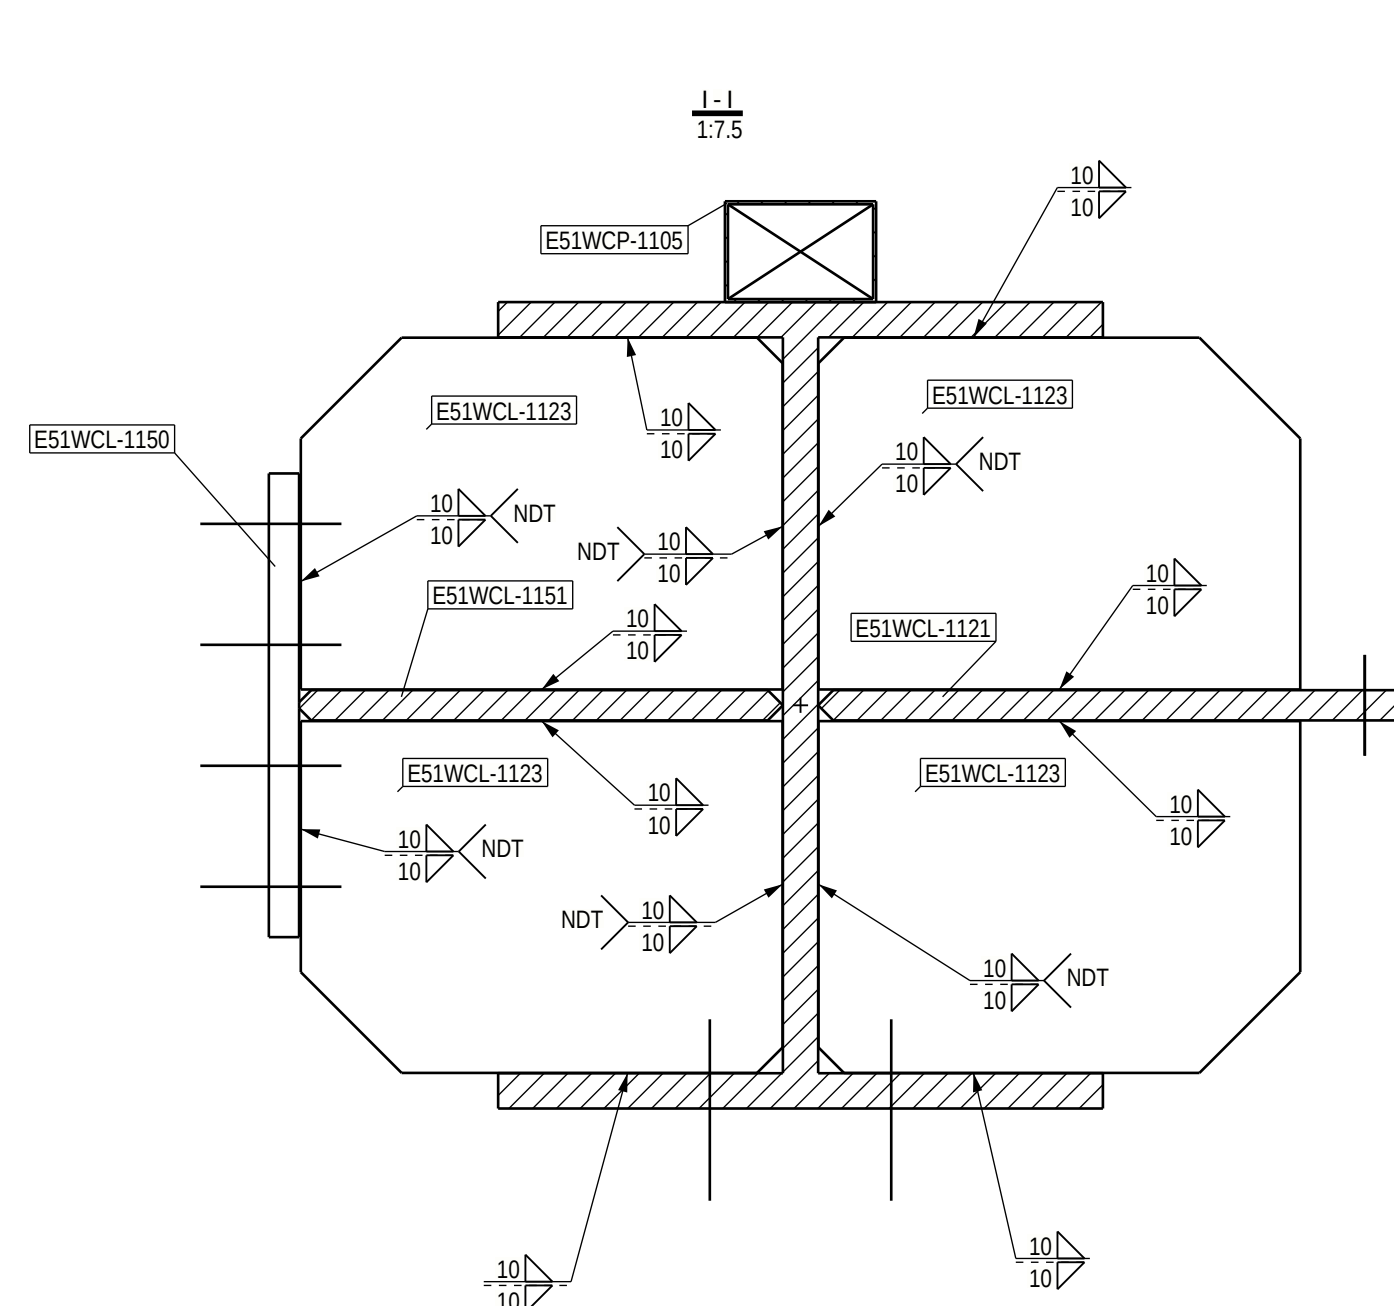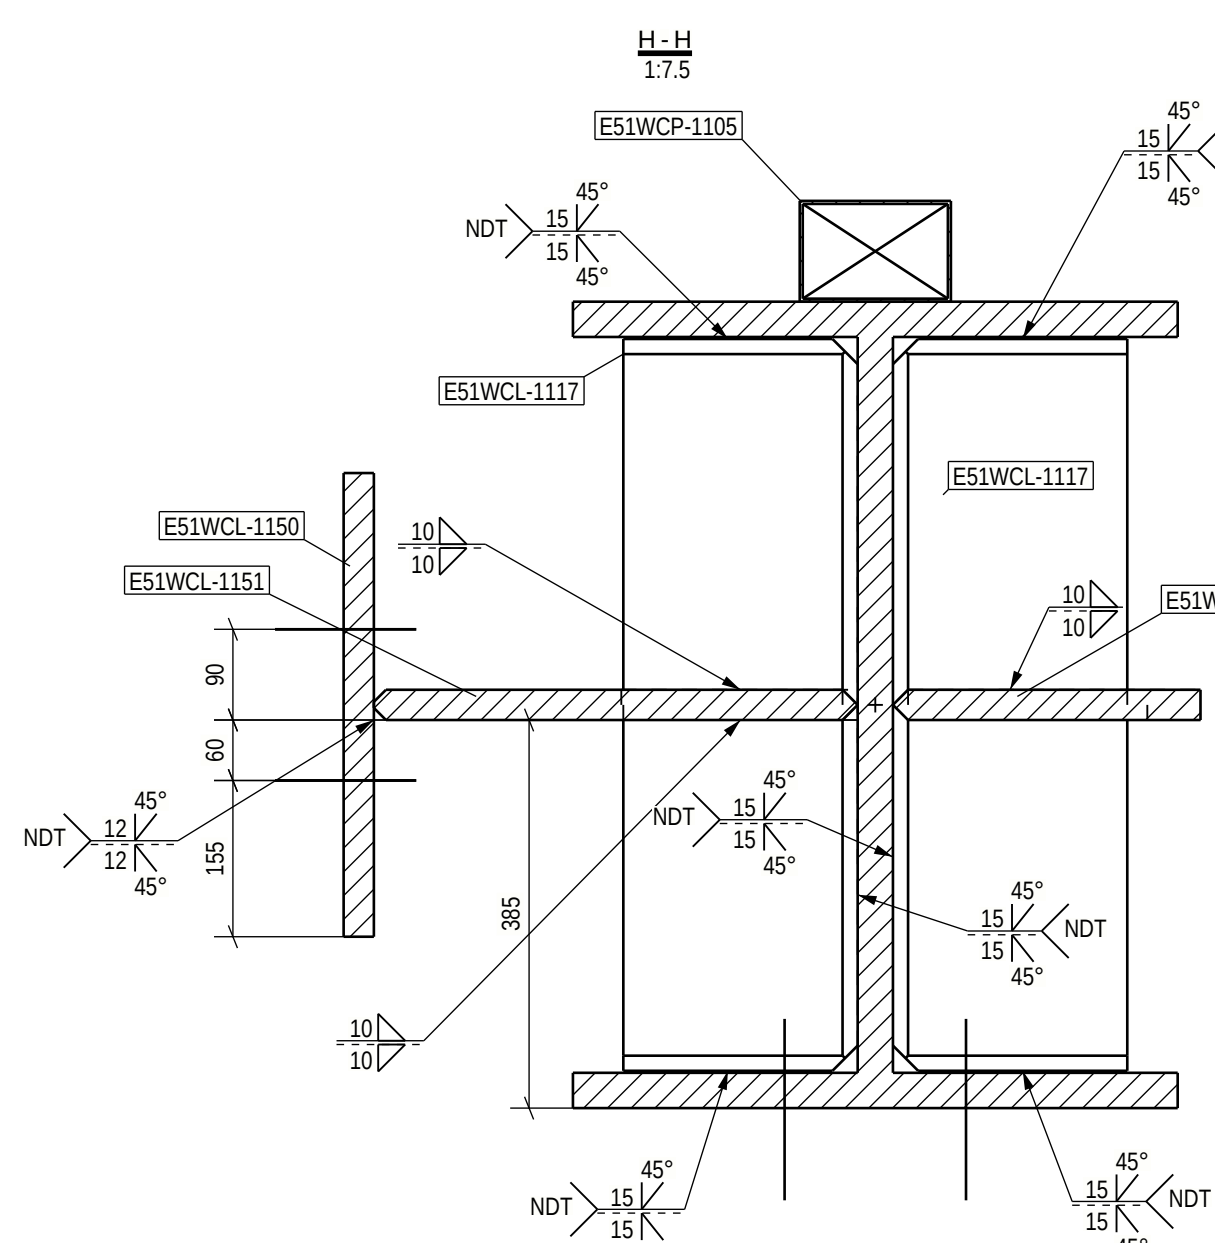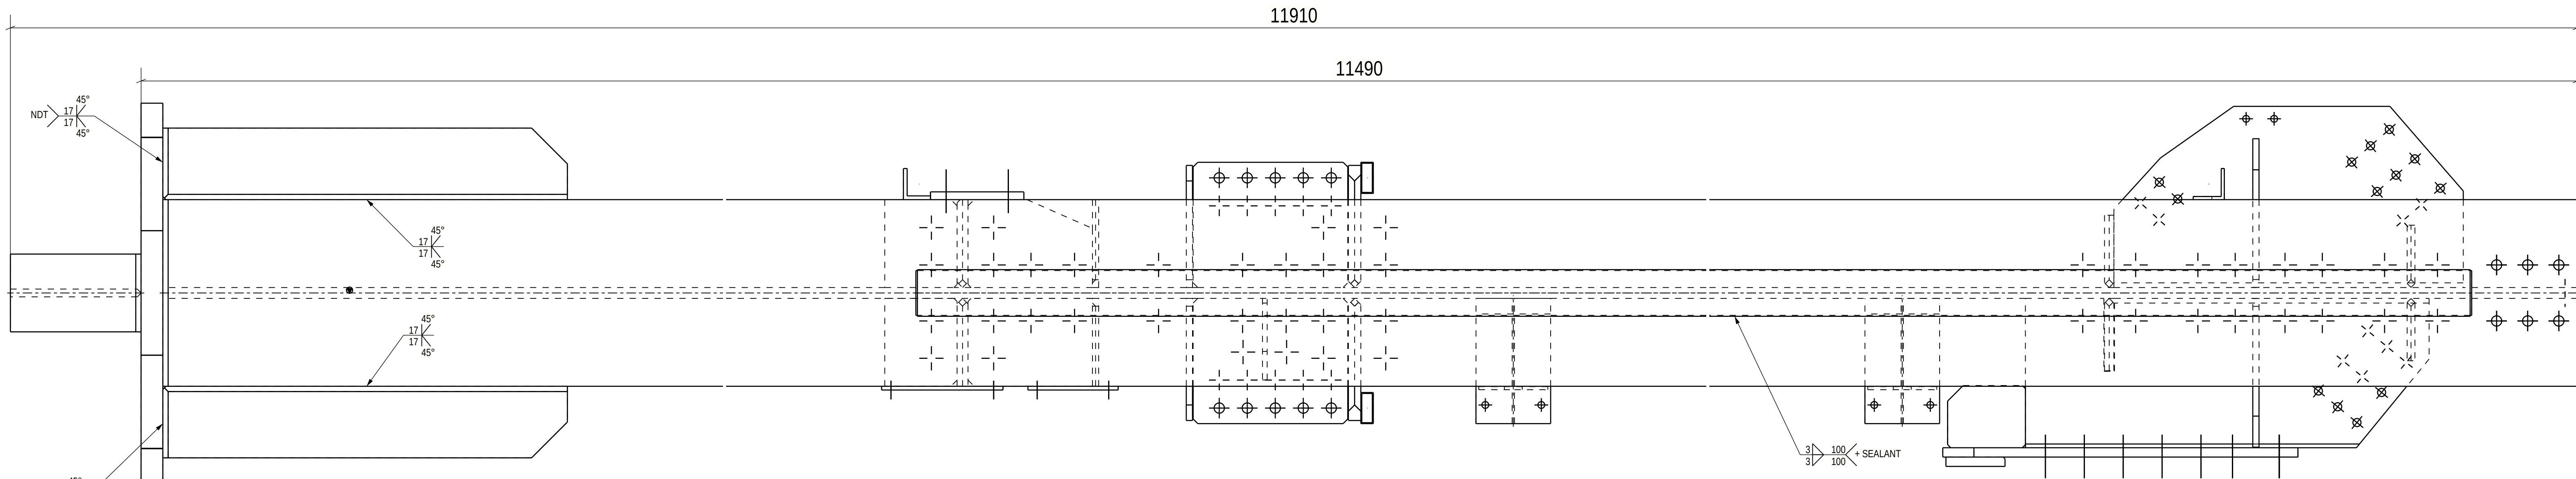


PART LIST FOR ASSEMBLY E5WC-1074 MANUFACTURING ANOMALY #12678						
PART	PROFILE	MATERIAL	LENGTH [mm]	AREA [cm ²]	WEIGHT [kg]	PCS
E5WC-1001	PL70X220	S355NL20	1520	3.56	884.9	1
E5WC-1056	PL36X230	S355NL20	1300	2.63	76.9	4
E5WC-1104	PL25X330	S355NL20	505	0.34	29.7	1
E5WC-1105	PL36X230	S355NL20	400	0.23	22.1	2
E5WC-1116	PL15X232	S355NL20	283	0.29	7.7	7
E5WC-1137	PL30X233	S355NL20	726	0.74	37.6	2
E5WC-1140	PL40X293	S355NL20	726	1.23	84.3	2
E5WC-1141	PL30X233	S355NL20	1123	1.20	52.9	1
E5WC-1122	PL35X293	S355NL20	726	0.45	53.3	1
E5WC-1123	PL30X249	S355NL20	478	1.24	25.4	4
E5WC-1143	PL12X287	S355NL20	403	0.84	18.8	2
E5WC-1148	PL30X293	S355NL20	726	1.12	44.2	2
E5WC-1149	PL30X230	S355NL20	1343	1.12	121.3	1
E5WC-1151	PL30X480	S355NL20	1297	1.25	133.9	1
E5WC-1155	PL35X230	S355NL20	200	0.10	8.9	1
E5WC-1163	PL30X3	S355NL20	84	0.03	0.1	4
E5WC-1164	PL30X232	S355NL20	403	0.25	22.1	2
E5WC-1166	PL20X293	S355NL20	726	0.45	32.0	1
E5WC-1167	PL21X180	S355NL20	390	0.16	7.0	1
E5WC-1168	PL12X190	S355NL20	290	0.12	5.2	1
E5WC-1169	PL30X230	S355NL20	97	0.06	0.5	2
E5WC-1184	PL35X292	S355NL20	250	0.27	9.1	2
E5WC-1185	PL25X200	S355NL20	223	0.20	8.1	2
E5WC-1191	PL10X107	S355NL20	205	0.20	1.7	4
E5WC-1195	PL30X233	S355NL20	726	0.45	53.0	1
E5WC-1202	PL30X230	S355NL20	726	0.45	21.0	1
E5WC-1207	PL20X230	S355NL20	250	0.11	4.6	1
E5WC-1308	W205.25-X5250	S355NL20	420	0.73	81.7	1
E5WC-1301	L10P10	S355L2	378	0.15	5.7	1
E5WC-1302	L10P10	S355L2	375	0.15	5.7	1
E5WC-1303	W300.35-X3000	S355L2	11420	44.99	6106.2	1
E5WC-1110	CFRHS150X100X3	S355L20	6280	3.00	71.0	1
E5WC-1118	CFRHS100X40X3	S355L20	1065	0.58	6.5	2
E5WC-1112	L10P12	S355L2	762	0.30	13.9	1
E5WC-1114	HEX40	S355L2	423	1.10	24.3	1
TOTAL:					79.36	8696.0

DET 4
Full contact in bearing, requirements
acc. to EN 1090-2/6.8 and 11.2.3.5
and project specification

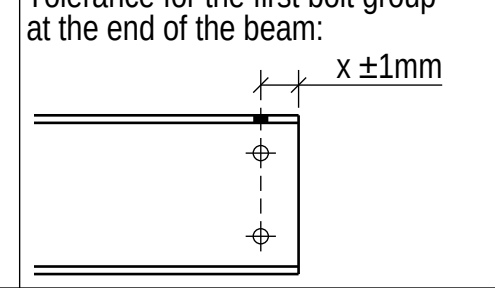

DET 1

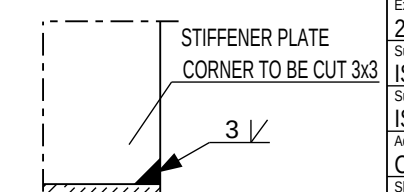

Technical fabrication requirements:		EXC2
Requirements for fabrication, design and construction: EN ISO 9001, EN ISO 14001 Material Specification standard: ISO 9443-4/CIS250-0600-0600-000005 SOS8501-3, grade P2 EN ISO 2344-5 Additional reference for surface treatment: C4/EU-SPD748 2403 RAL 7024 (Graphite Gray) Finishing of surfaces: <u>Appendix I / Project spec.</u> EN 9992-1, EN 9992-2	Fabrication process: EN ISO 9001, Appendix B General fabrication process: <u>Project specification's shown on drawing.</u> EN ISO 2, Table 2A, L+U=5 EN ISO 2020, 20% of welds Level of RT: 100% EN ISO 17640, 100% of welds Level of ET: 100% EN ISO 17649, 100% of welds EN ISO 17649, 100% of welds EN ISO 17649, 100% of welds EN ISO 2 Section 6.6.3 EN C EN ISO 5817 Minimum material inspection Shown on drawing	

For special tolerances of bolt hole location
see specification for steel structures

Tcr=650, Am/V=60





Easpring New Materials Oy

[illegible]

SWECO 
Sustainable engineering and design

SWECO RAKENNETE
ILMALANPORTTI 2
00240 HELSINKI
Puh. +358 207 393 000
www.sweco.fi


	DRAWING CONTENT			
	ASSEMBLY DRAWING COLUMN_WI E51WC-1074			
	DATE	ARCHIVING CODE	PAGE	DESIGN GROUP
	12.06.2026			STR
ENKIKKA OY DRAWN Alloy Senua PROJECT NUMBER 25019443	DESIGNER	APPROVED	CHECKED	REVISIO
	Alloy Senua	Pertti Kouvanmaki Sivu: 1/5	Jani Kallioalmi	
	E51WC-1074			

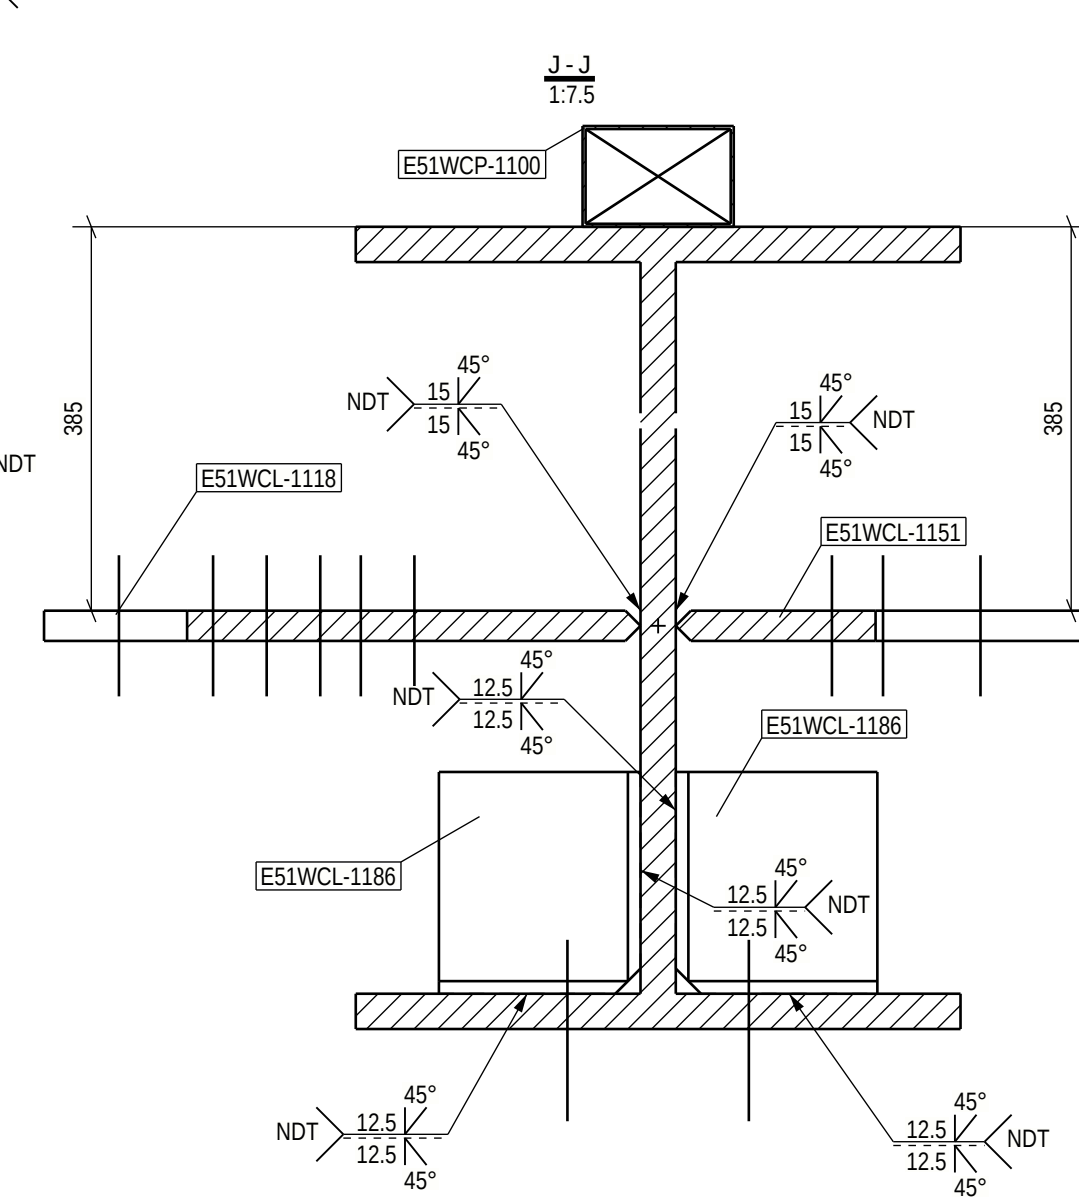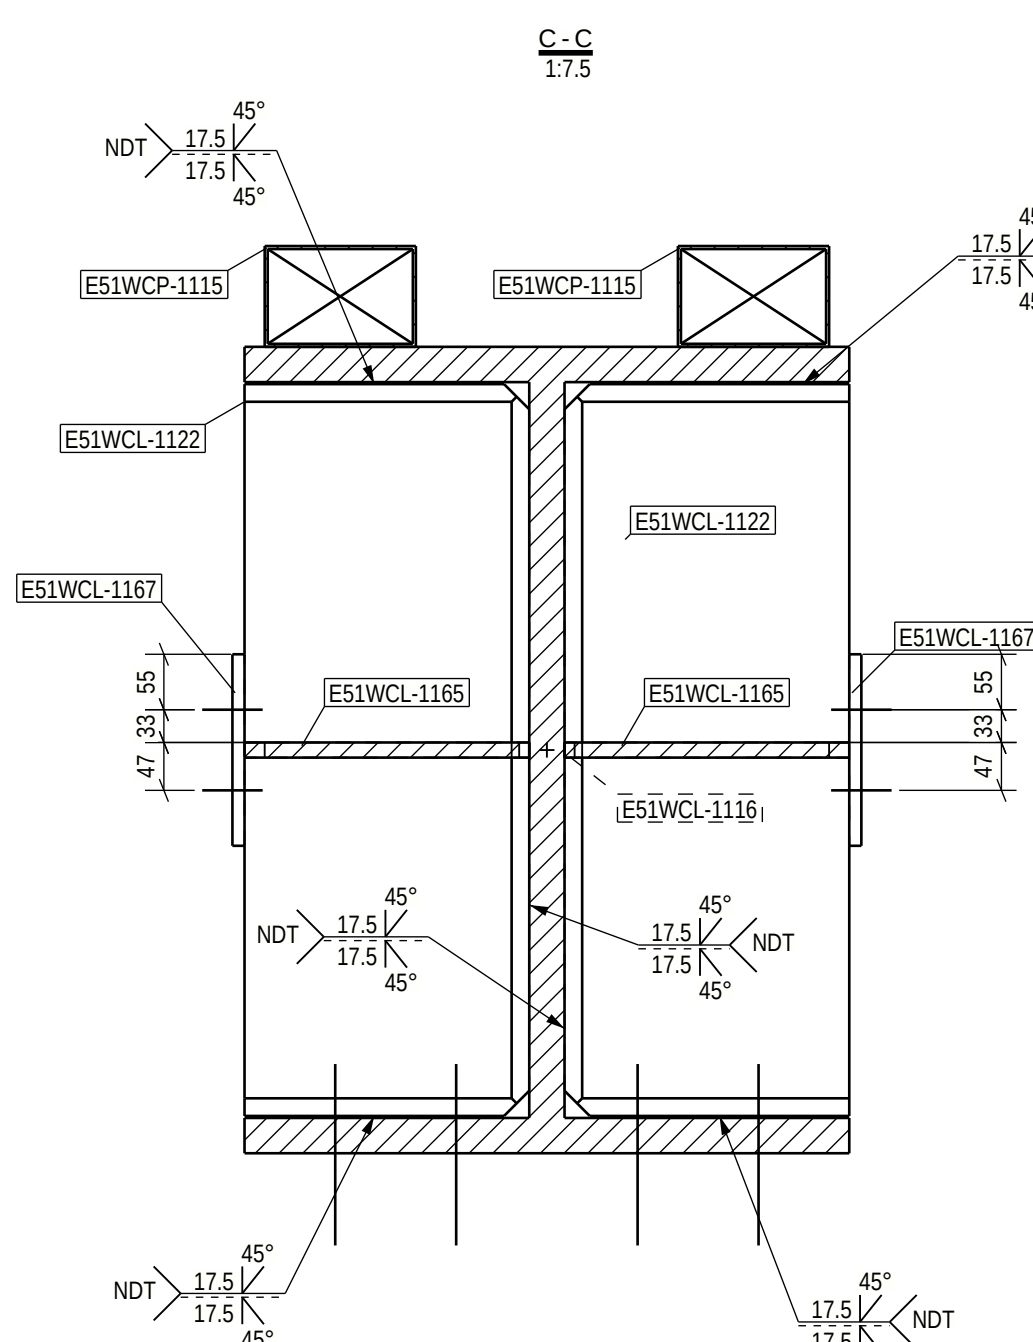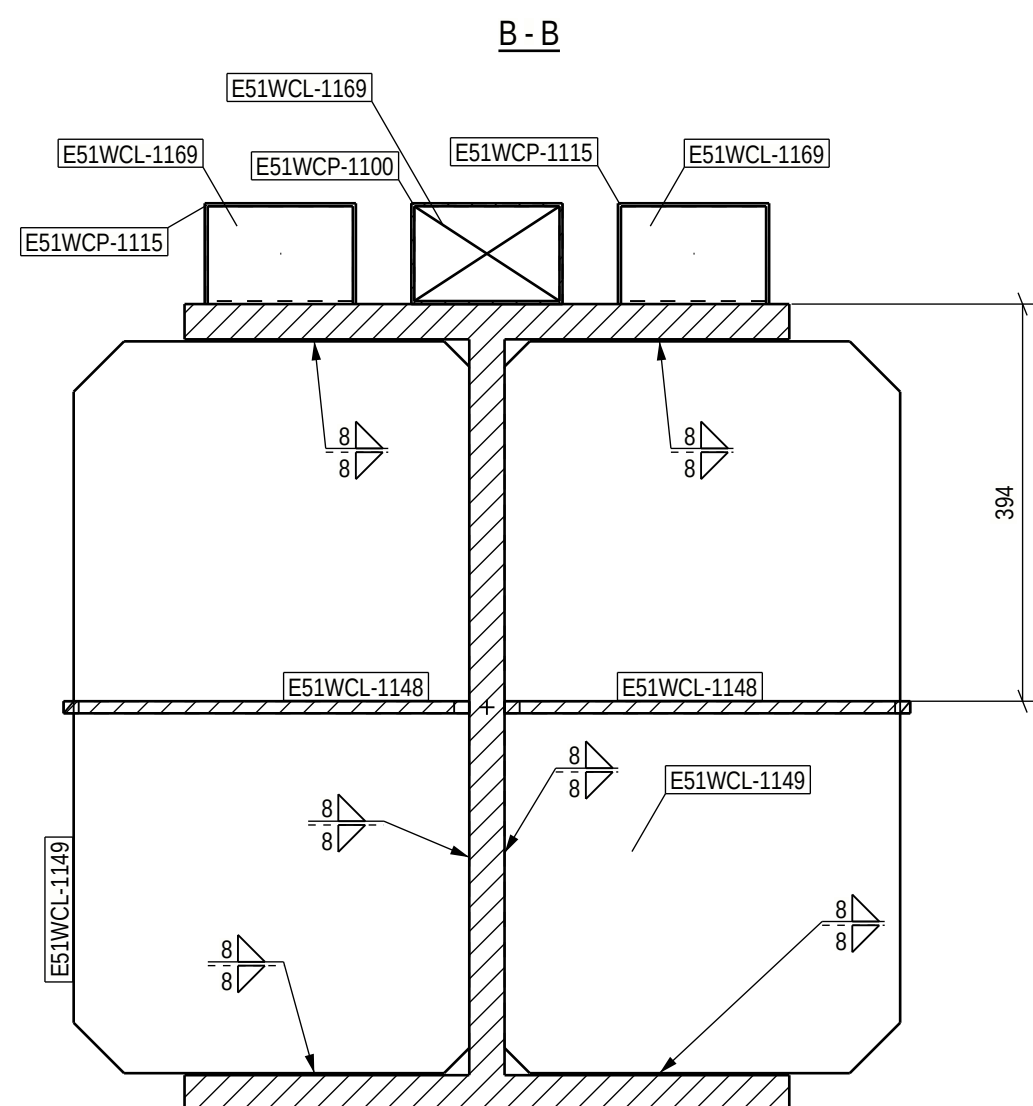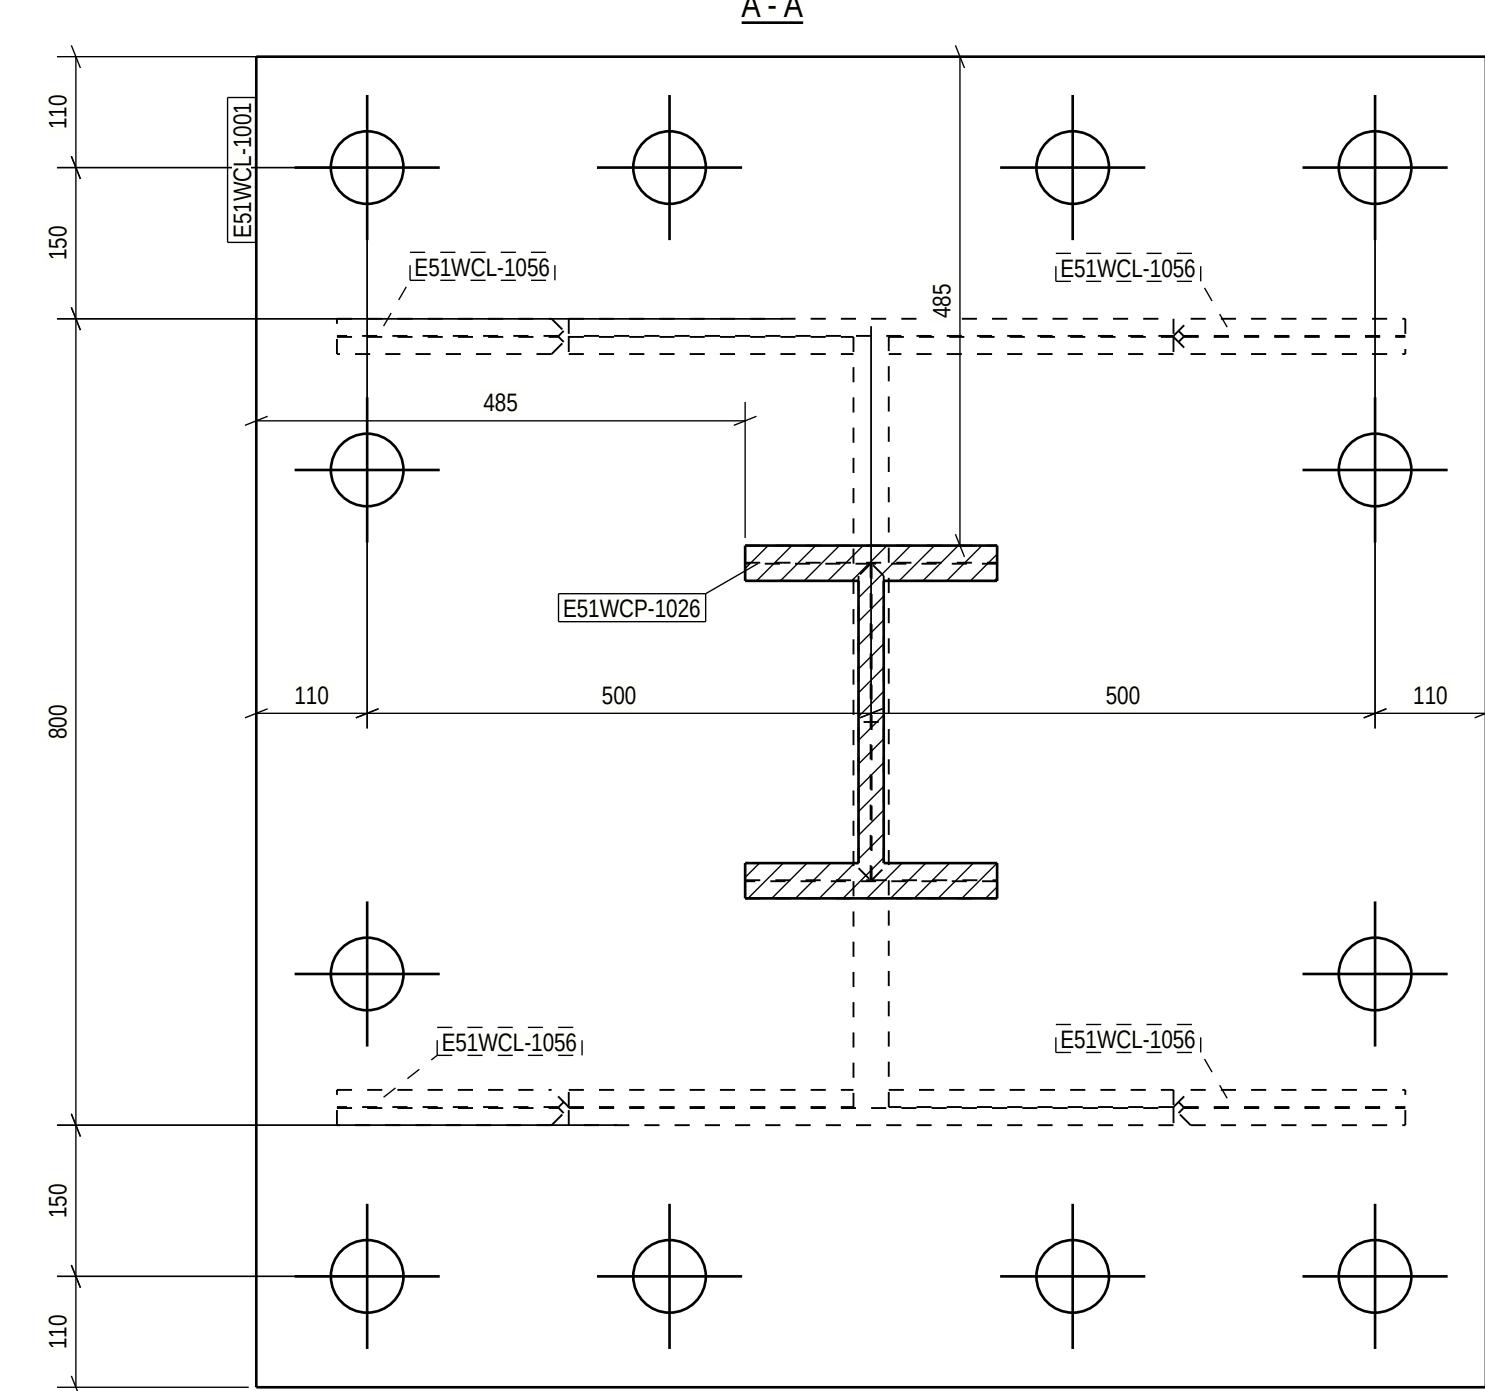

DET 4
Full contact in bearing, requirements acc. to EN 1090-2/6.8 and 11.2.3.5 and project specification
Tolerance for the first bolt group at the end of the beam:




The diagram shows a cross-section of a beam with a bolt group at the end. The bolt group is represented by two circles with a cross inside. A dimension line with arrows indicates the distance from the end of the beam to the center of the bolt group, labeled as $x \pm 1\text{mm}$.

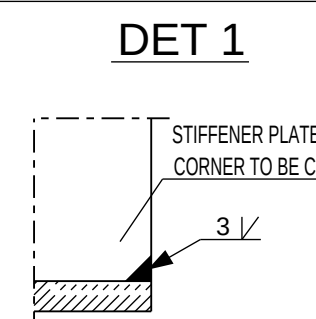[illegible]

For special tolerances of bolt hole location
see specification for steel structures
Approved For Construction

Tcr=650, Am/V=60

PROJECT NAME: Easpring New Materials Oy
FAIR Phase 1

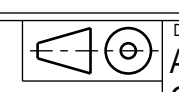

DRAWING CONTENT
ASSEMBLY DRAWING
COLUMN_WI
E51WC-1075

SWECO 
Sustainable engineering and design




SWECO RAKENNETT
ILMALANPORTTI 2
00240 HELSINKI
PUH. +358 207 393 000
www.sweco.fi

KNIKKKA OY	D J D F A
------------	-----------------------

DATE 2.06.2026	ARCHIVING CODE
DRAWN Alexey Seryus	DESIGNER Alexey Seryus
PROJECT NUMBER 25019443	

PAGE	DESIGN
APPROVED Peri Kovummaanohe	CHECKED Jere Kallio
DWG. NO.	REV.

E51WC-1075

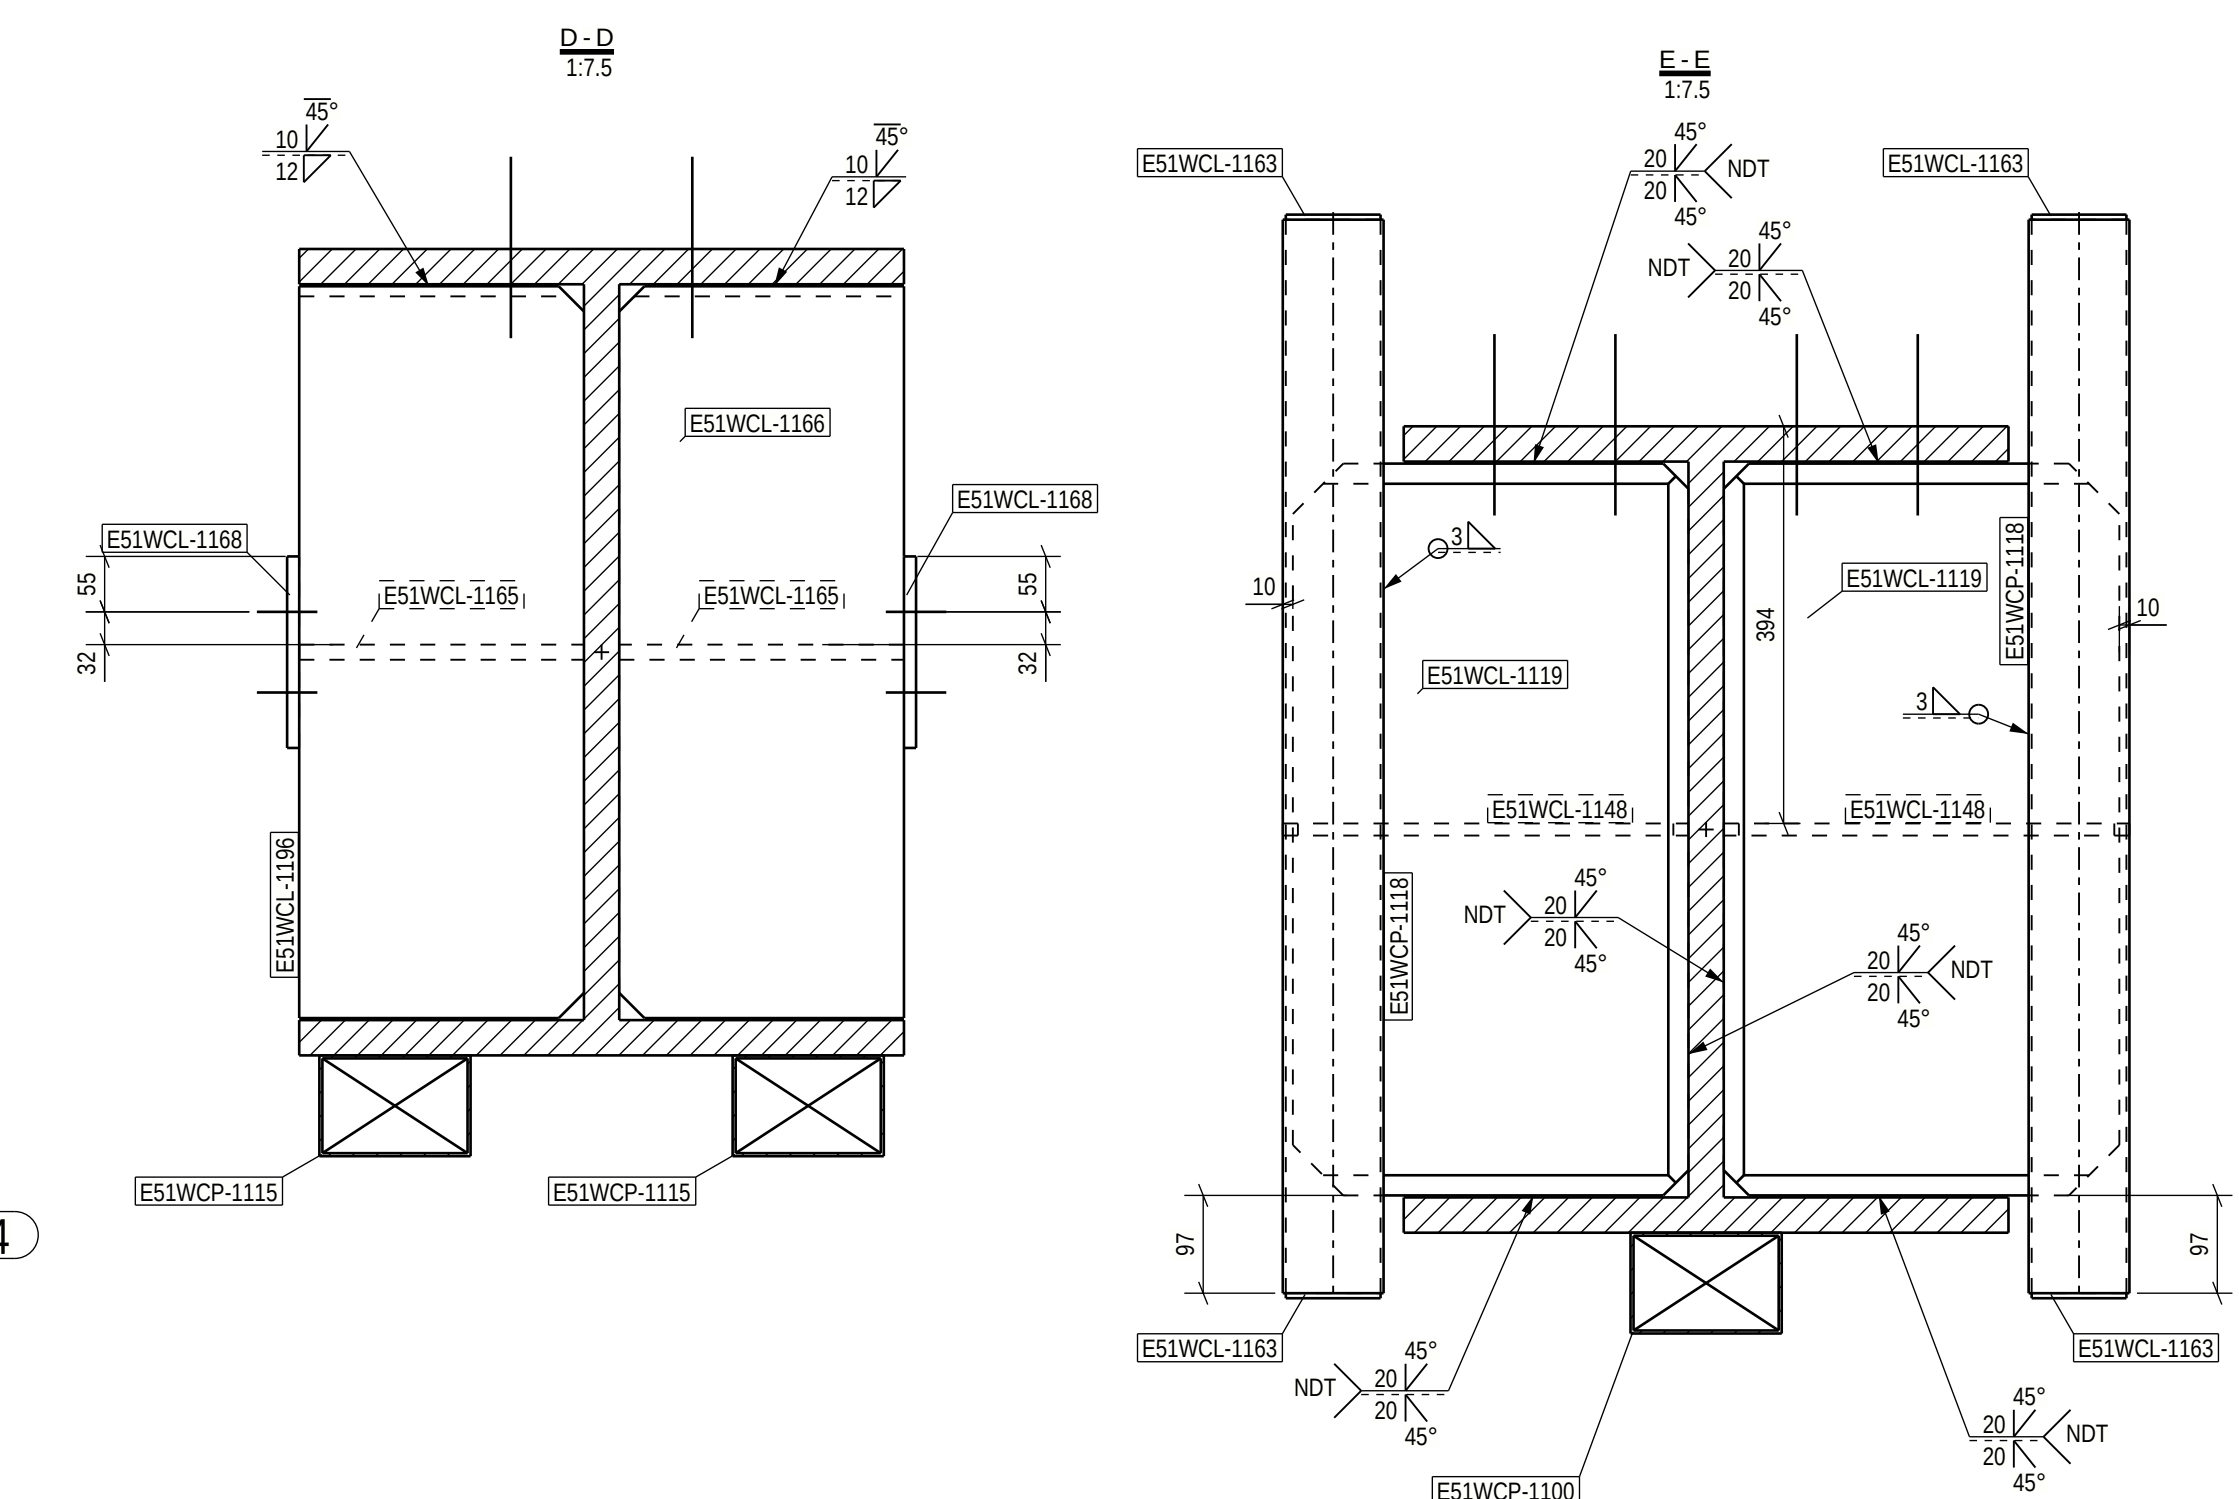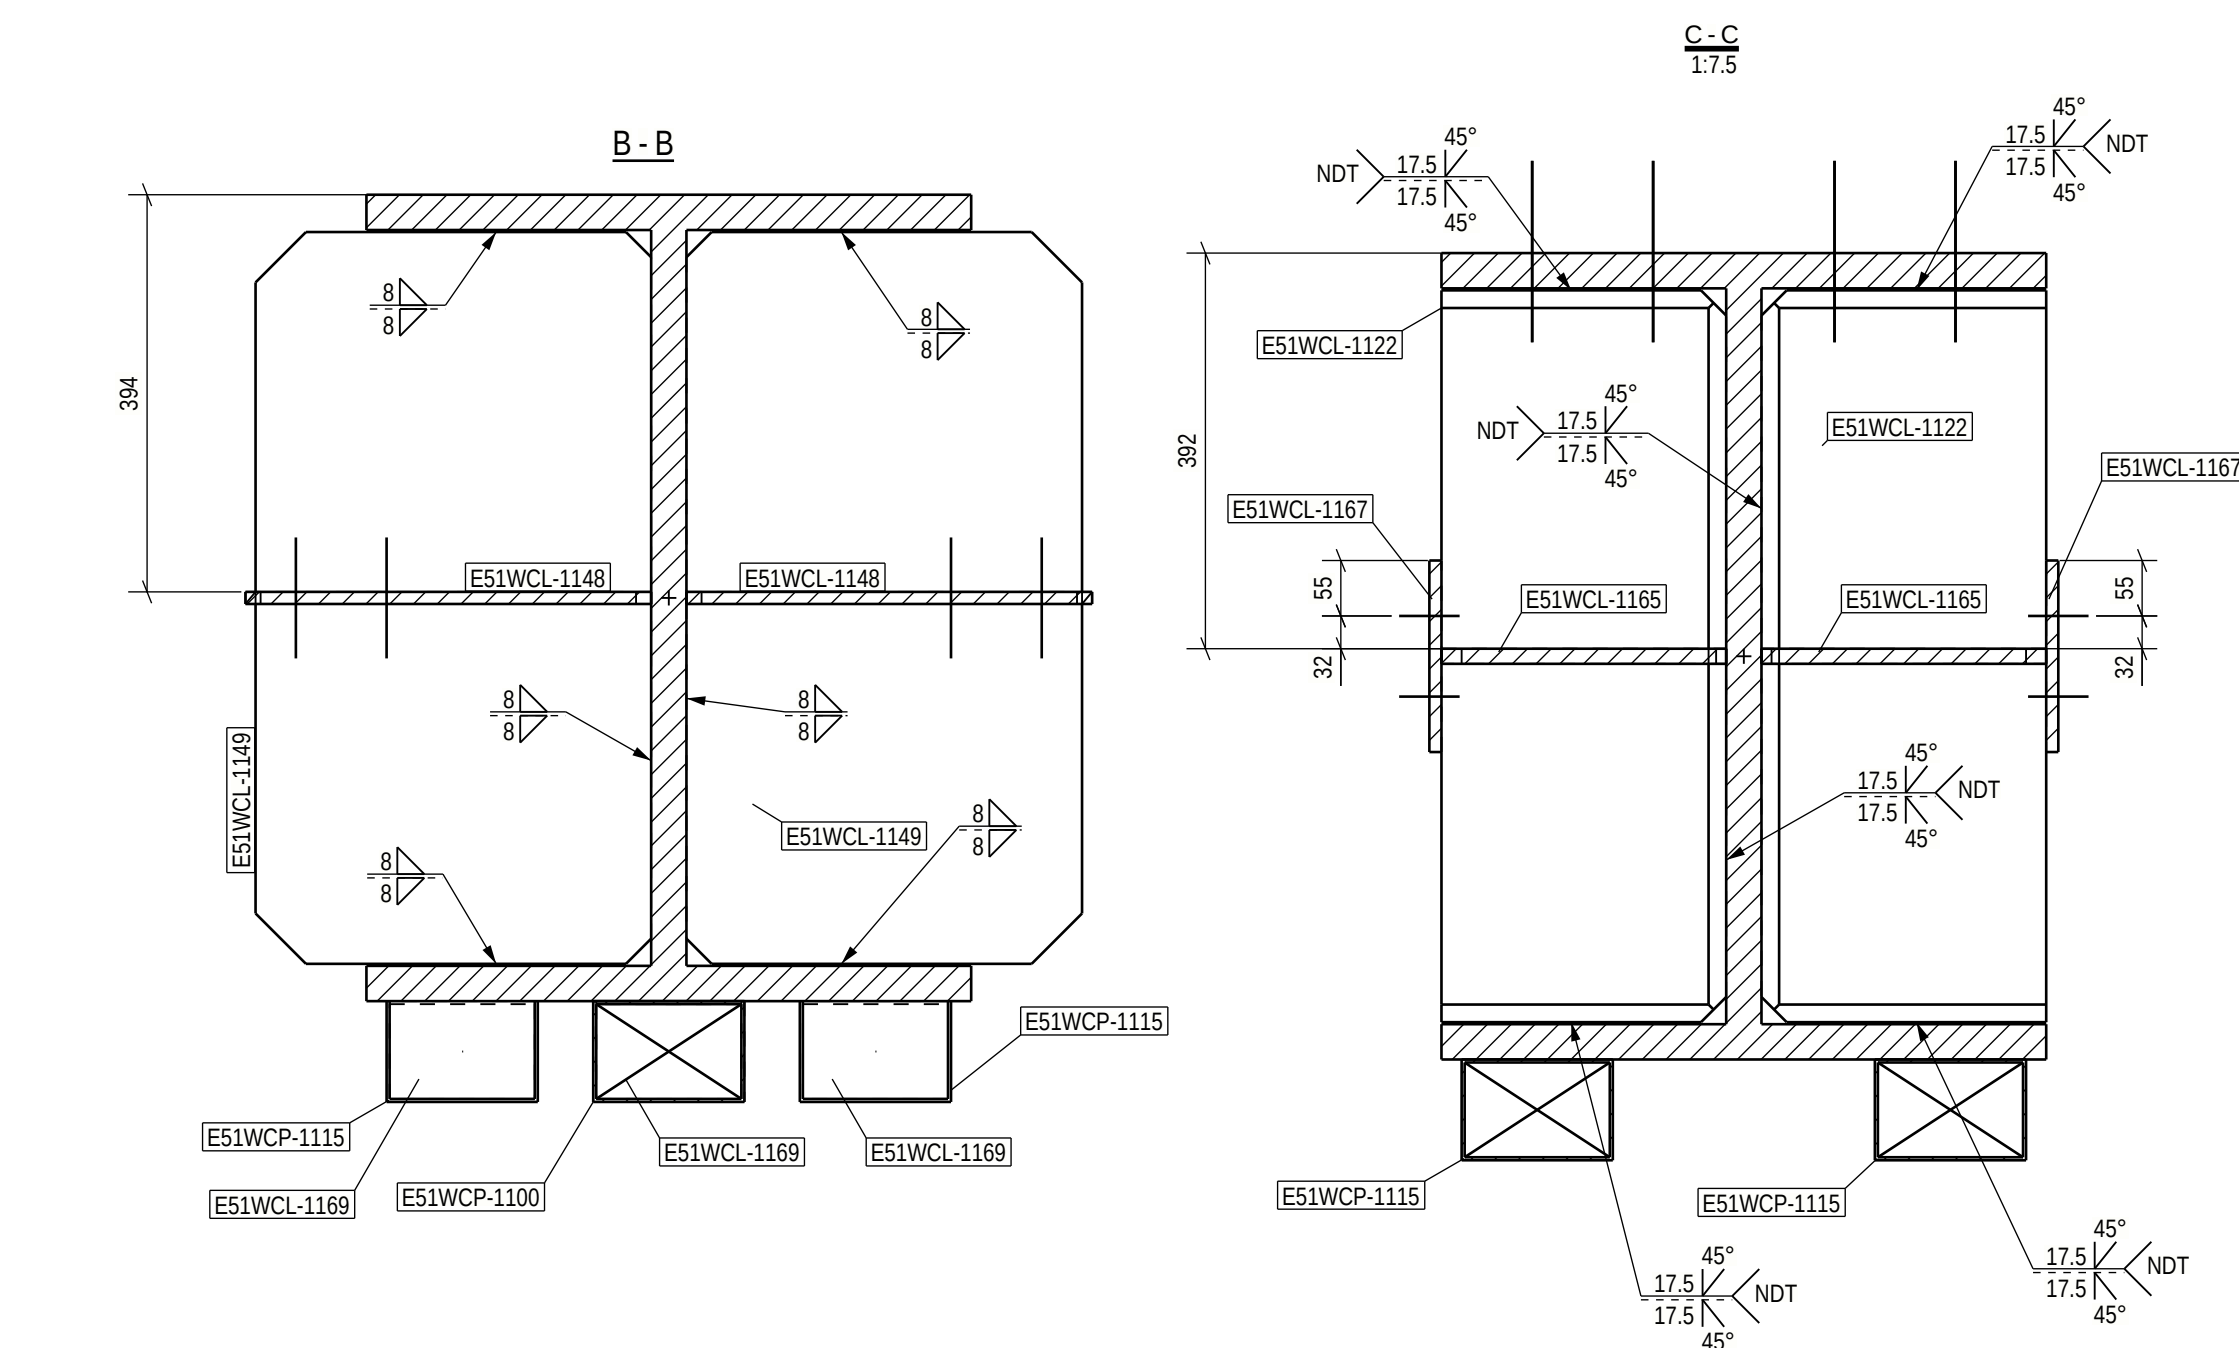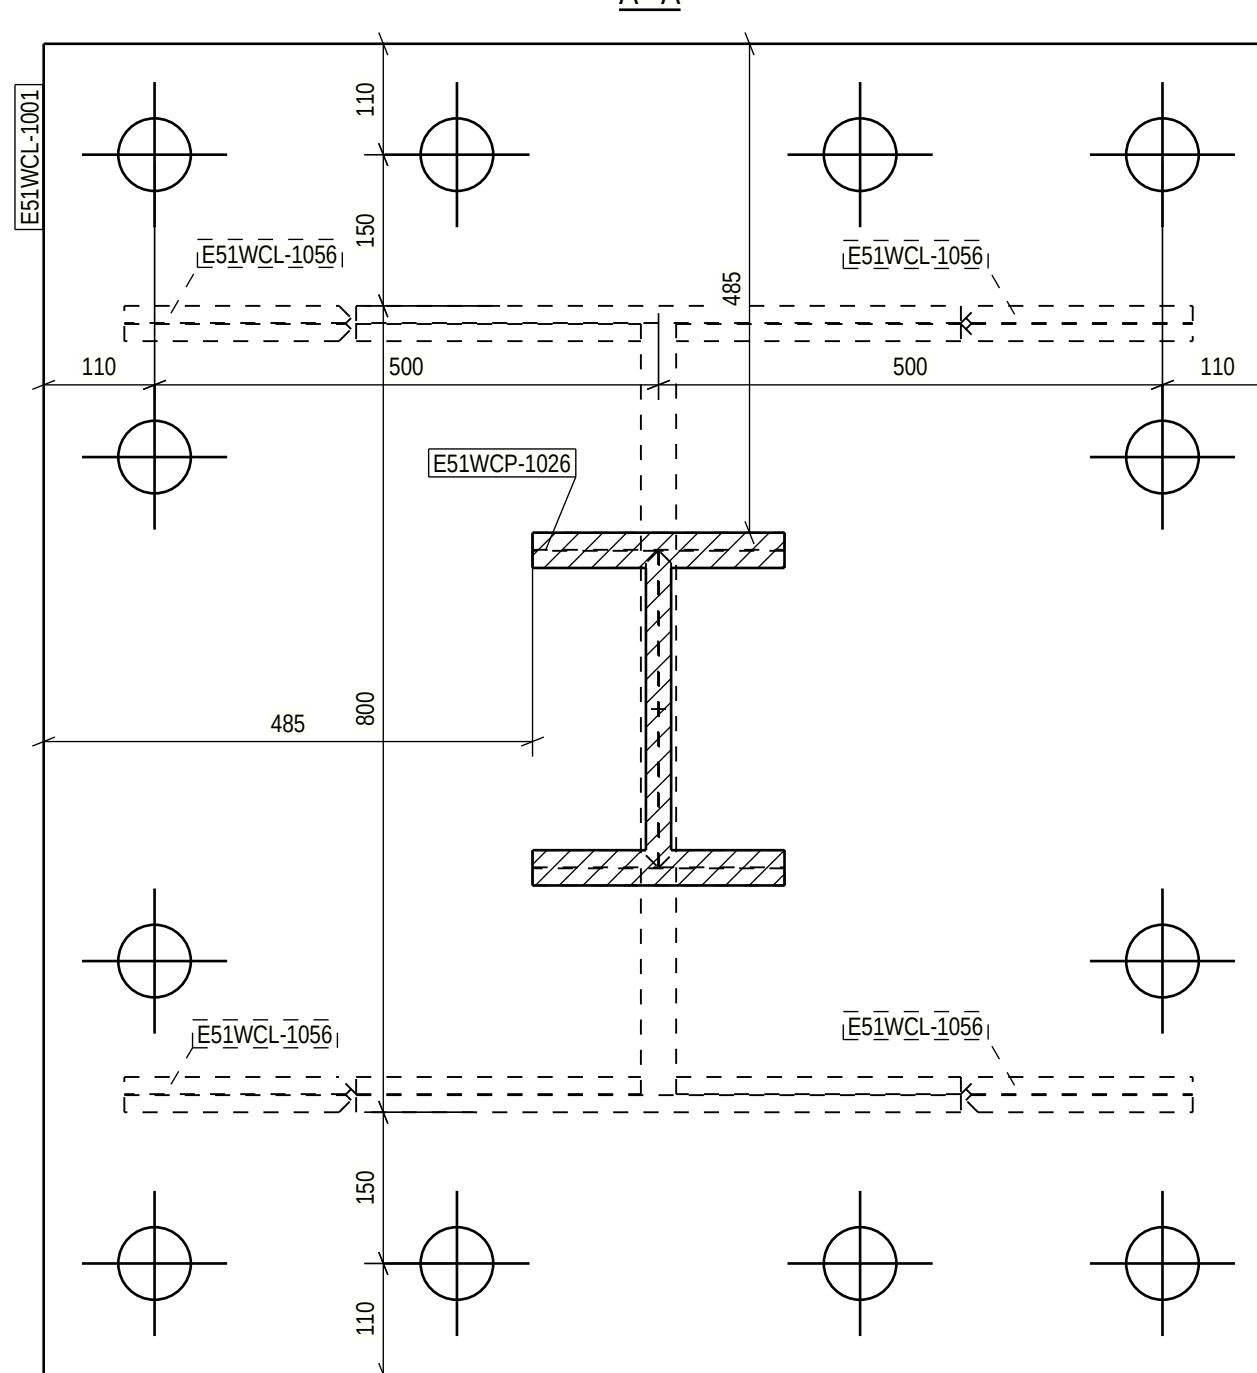

DET 1

Technical fabrication requirements:

EXC2

For special tolerances of bolt hole location
see specification for steel structures
Approved For Construction

PROJECT NAME: **Engineering New Materials Ov**

PROJECT NAME: Easpring New Materials Oy
FAIR Phase 1

	DRAWING CONTENT ASSEMBLY DRAWING COLUMN_WI E51WC-1076
---	--

DRAWING CONTENT	ASSEMBLY DRAWING COLUMN WITH
-----------------	---------------------------------

E51WC-1076

DATE	40- WING CODE
------	---------------


12.05.2026	ATTENDING CODE
DEMAN	DECEASED

Alamy Syrus	Alamy Syrus
-------------	-------------


25019443

E51WC-1076

PART LIST FOR ASSEMBLY E51WC-1077, MANUFACTURING AMOUNT 1 PIECES						
PART	PROFILE	MATERIAL	LENGTH [mm]	AREA [m2]	WEIGHT [kg]	PCS
E51WCL-1011	PL20X170	S355J2+N	576	0.22	15.1	1
E51WCL-1092	PL10X228	S355J2+N	284	0.11	3.8	1
E51WCL-1053	PL10X170	S355J2+N	170	0.06	2.3	1
E51WCL-1143	PL25X700	S355J2+N	420	0.96	53.2	1
E51WCL-1152	PL20X250	S355J2+N	582	0.32	22.8	1
E51WCL-1154	PL20X99	S355J2+N	576	0.14	8.9	1
E51WCL-1157	PL15X385	S355J2+N	683	0.47	25.9	1
E51WCL-1171	PL5X194	S355J2+N	197	0.32	1.5	4
E51WCL-1190	PL5X194	S355J2+N	194	0.08	1.5	1
E51WCL-1192	PL5X194	S355J2+N	197	0.08	2.4	1
E51WCL-1193	PL10X91	S355J2+N	150	0.06	1.0	2
E51WCL-1194	PL30X300	S355J2+N	576	0.40	40.7	1
E51WCP-1004	W800-10-10X210	S355J2	5175	10.12	408.1	1
E51WCP-1080	L100*10	S355J2	586	0.23	8.8	1
E51WCP-1101	CFRHS200X200X5	S355J2H	1690	1.32	50.9	1
E51WCP-1135	CFRHS200X200X5	S355J2H	907	0.71	27.3	1
E51WCP-1136	CFRHS200X200X5	S355J2H	2210	1.73	68.5	1
TOTAL:			16.98	746.4		

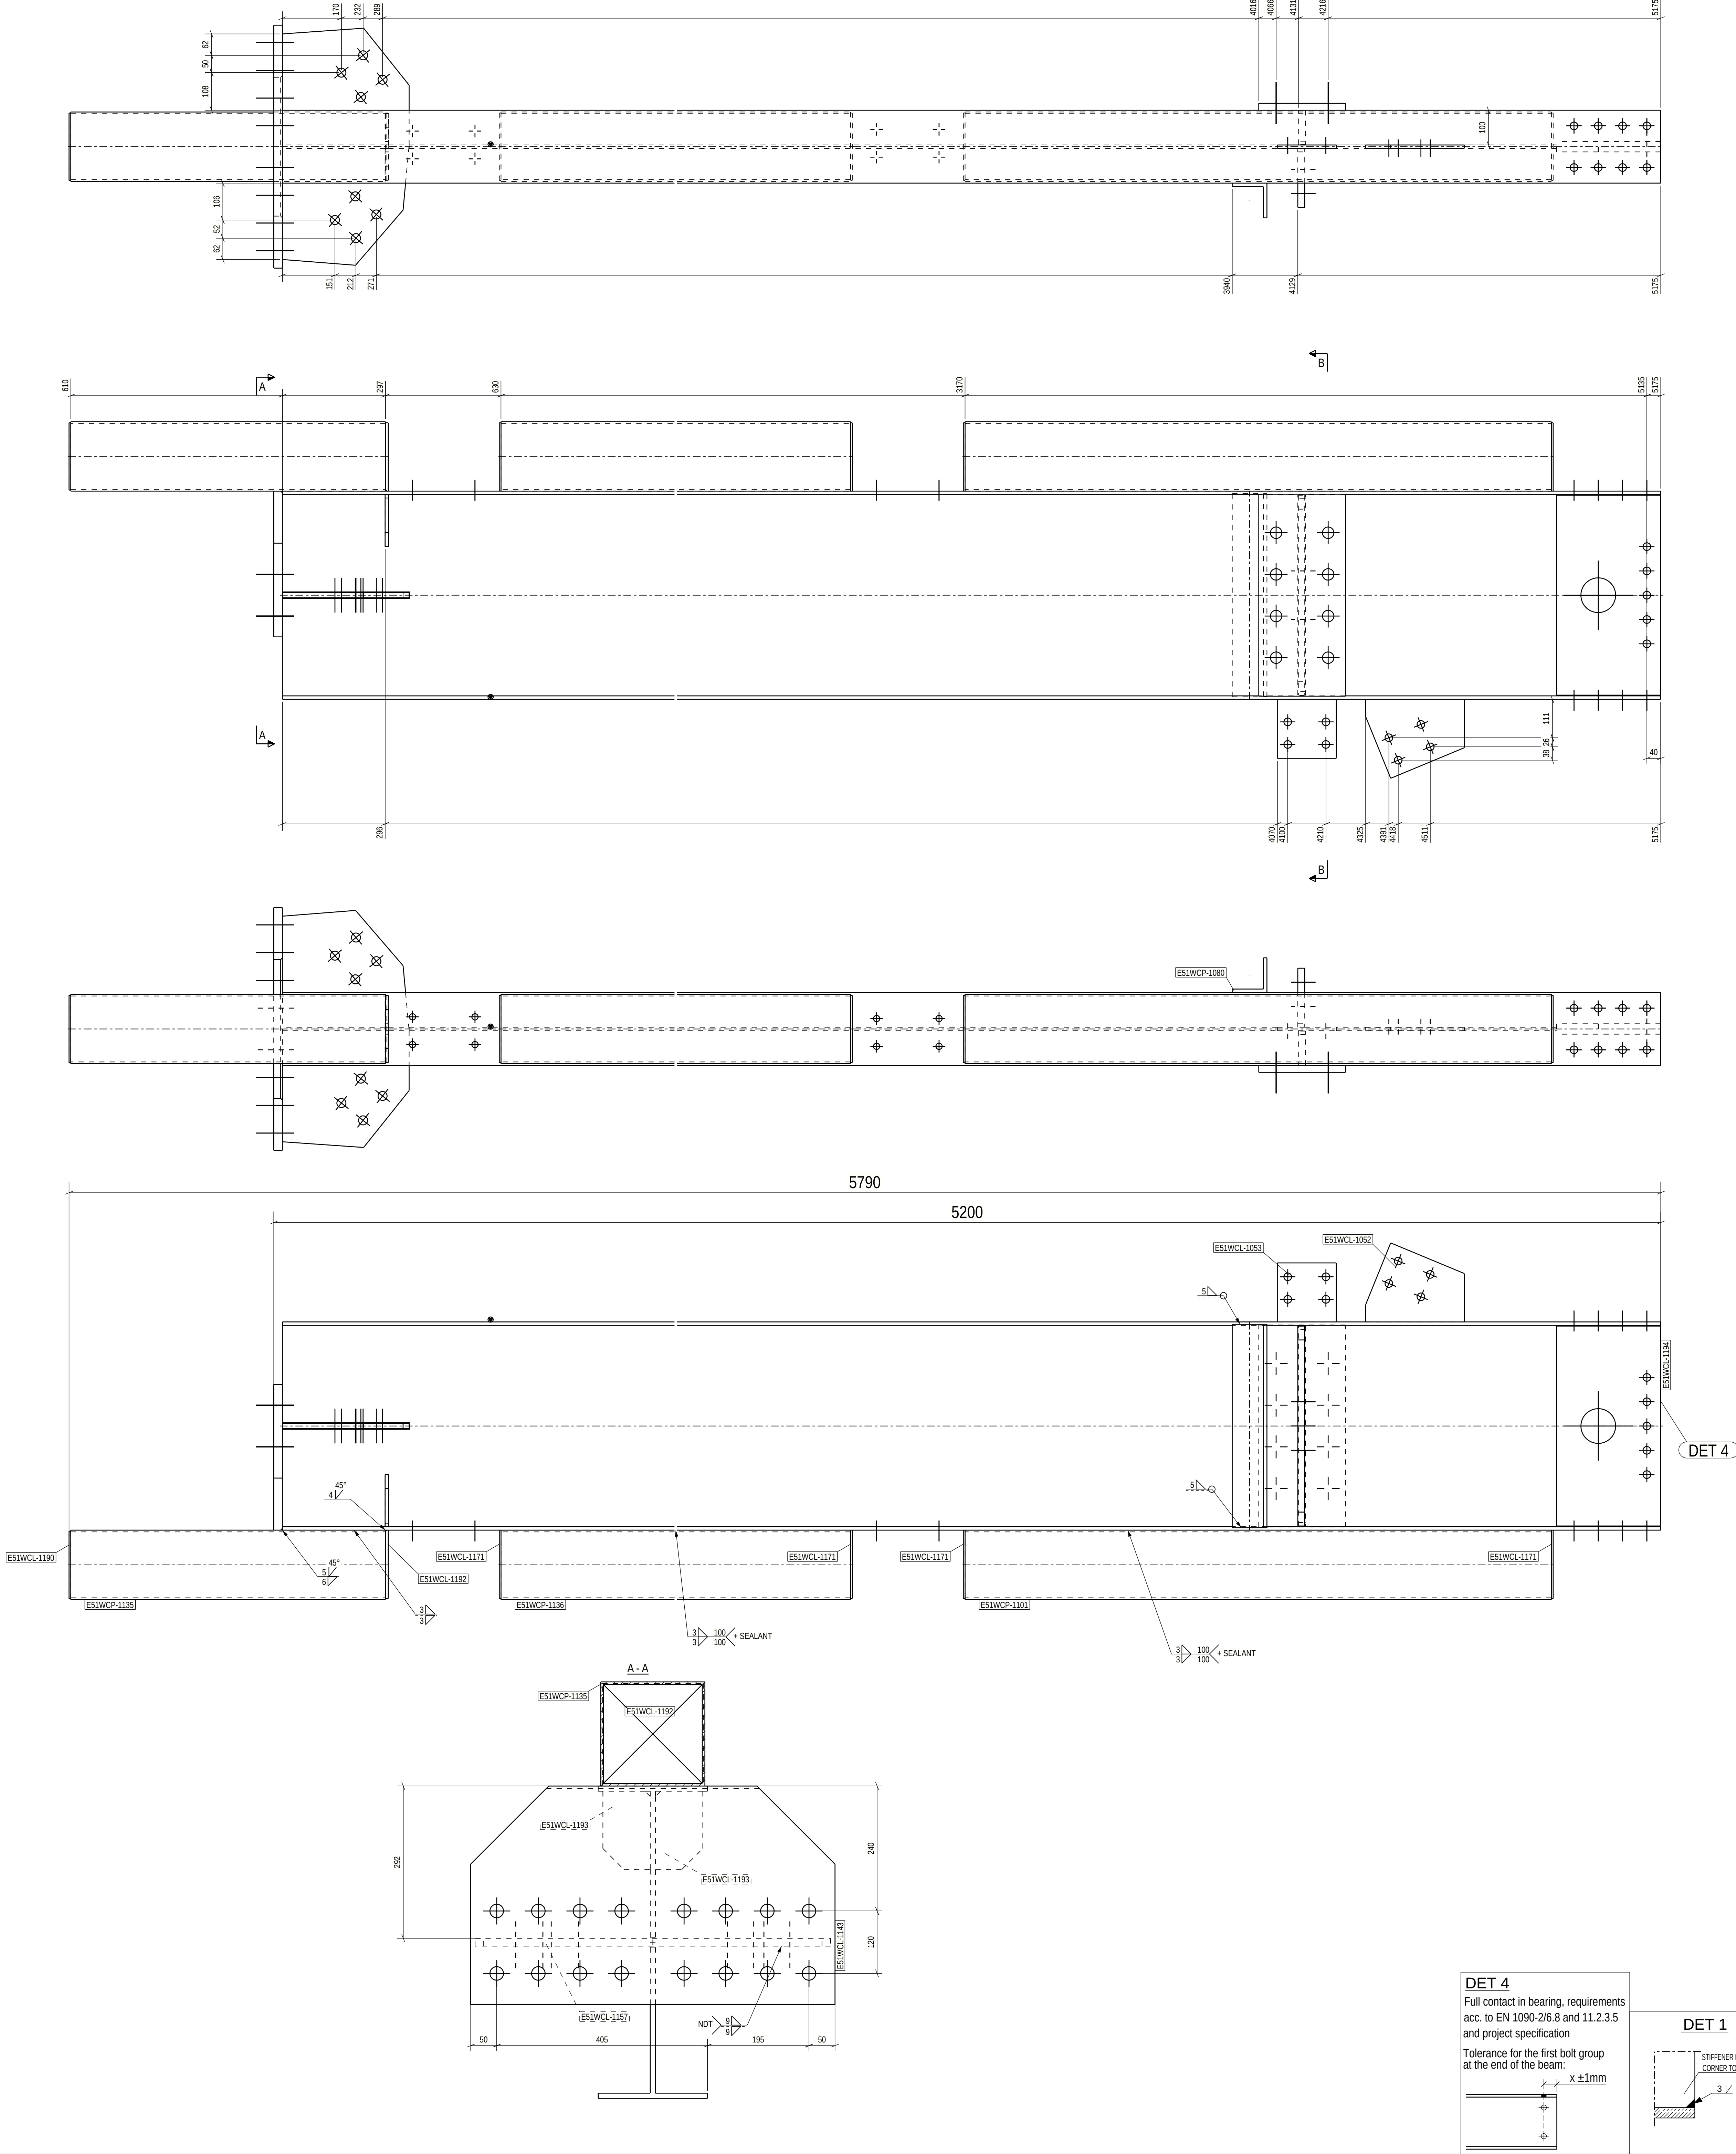


DET 4
Full contact in bearing, requirements acc. to EN 1090-2/6.8 and 11.2.3.5 and project specification
Tolerance for the first bolt group at the end of the beam:
x ±1mm

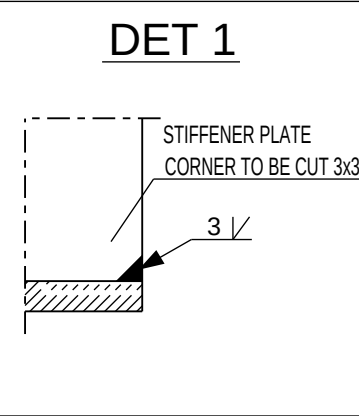


Technical fabrication requirements:		EXC2	
EN 1090-2, Table A.3, EXC2	EN 1090-2, Appendix B	Approved For Construction	
25019443-CC250-0600-0660-000006	Project specification shown on drawing	Easpring New Materials Oy	
EN 1090-2, Table 24, 12-5.5	EN 1090-2, Table 24, 12-5.5	FAIR Phase 1	
ISO 1944-6	WT: EN 1090-2, 20% of weight	SWECO	
C307, EP50UR 2402	WT: EN 1090-2, 20% of weight	SWECO RAKENNETEKNIKKA OY	
RAL 7024 (Graphite Gray)	WT: EN 1090-2, 20% of weight	A.M. RAKENNETE 1.0	
Appendix 1 / Project Spec.	EN 1090-2 Section 6.6.3	00240-HEL-SIKI	
EN 1092-1, EN 1092-2	C, EN ISO 5817	Aluminum material specified	
Shown on drawing		Suomenkabin engineering and design	

PROJECT NAME		Approved For Construction	
Easpring New Materials Oy		DRAWING CONTENT	
FAIR Phase 1		ASSEMBLY DRAWING	
		COLUMN W/	
		E51WC-1077	
DATE		12.06.2026	PROJECT CODE
DRAWN		Antti Sironen	PROJECT CODE
CHECKED		Antti Sironen	PROJECT CODE
APPROVED		Antti Sironen	PROJECT CODE
25019443		25019443	25019443
E51WC-1077		E51WC-1077	E51WC-1077

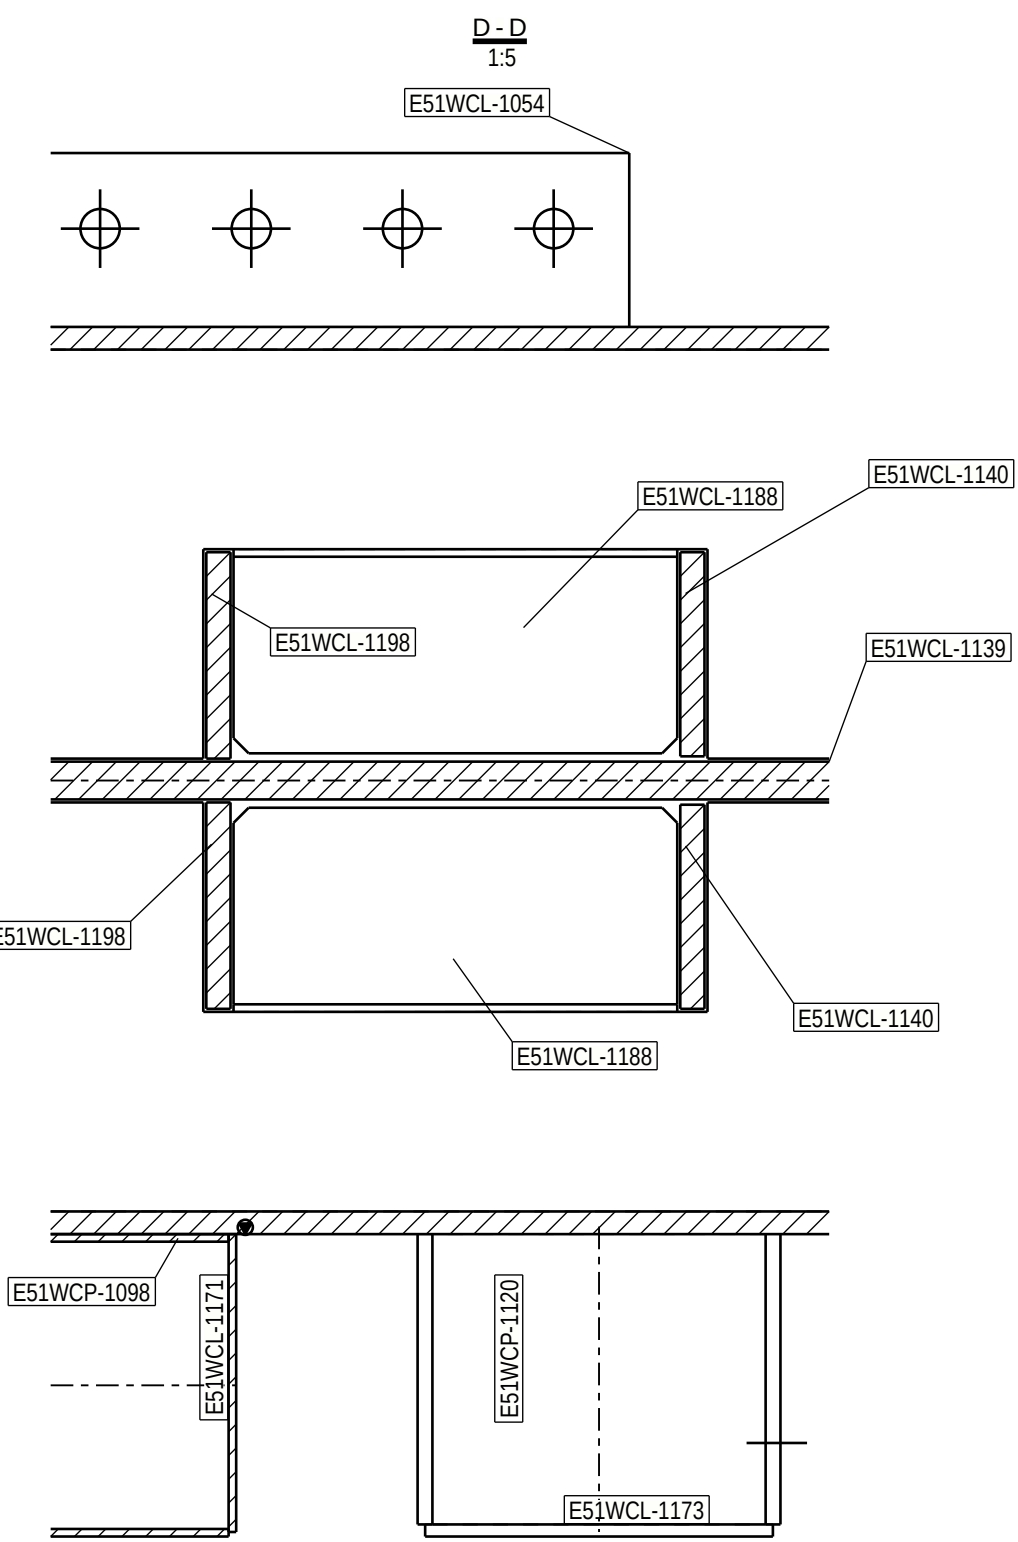

	DRAWING CONTENT			
	ASSEMBLY DRAWING			
	COLUMN_WI E51WC-1080			
ETEKONINKA OY	DATE 12.06.2026	ARCHIVING CODE	PAGE	DESIGN GROUP STR
	DRAWING Alteryk Surov	DESIGNER Alteryk Surov	APPROVED Pirkko Kovanenaho	CHECKED Jenni Kallanmaki
	PROJECT NUMBER 25019445	QUICK NO.	REVISION	
			E51WC-1080	

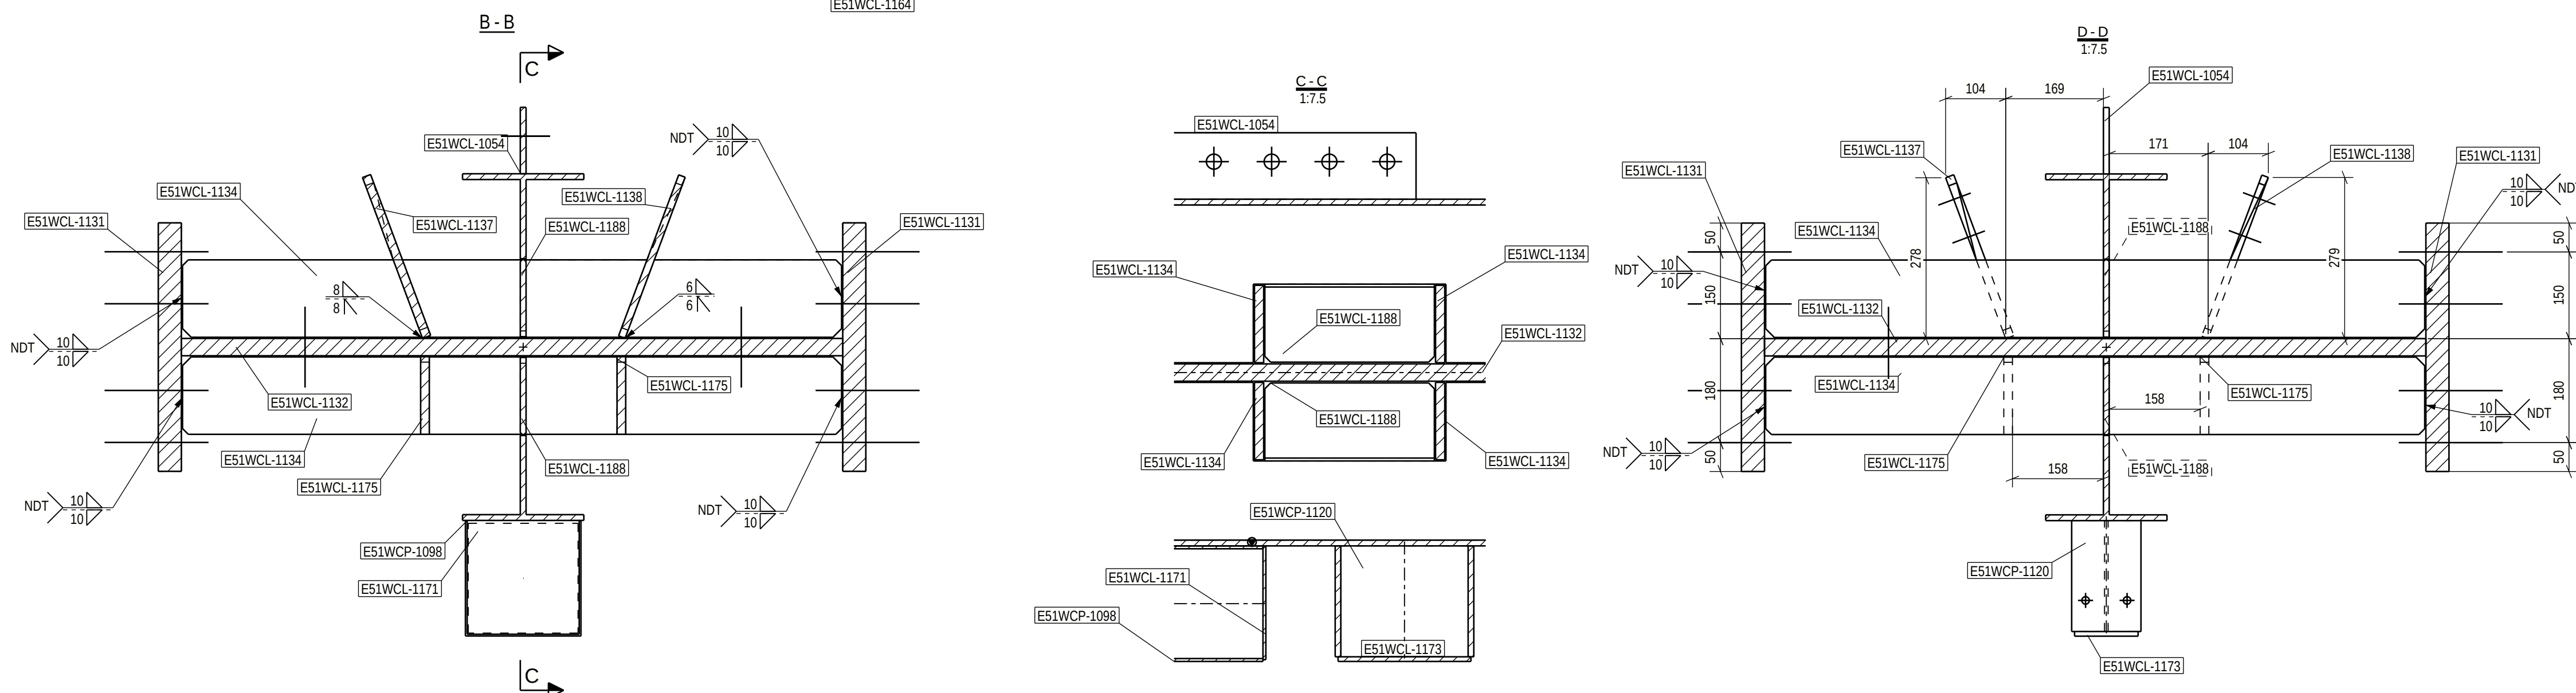


DET 4

Full contact in bearing, requirements acc. to EN 1090-2/6.8 and 11.2.3.5 and project specification

Tolerance for the first bolt group at the end of the beam:




The diagram shows a cross-section of a beam with a vertical web and horizontal flanges. Two bolt groups are shown: one at the end of the beam and another further along. A dimension line with arrows indicates the distance from the end of the beam to the center of the first bolt group, labeled as $x \pm 1\text{mm}$.


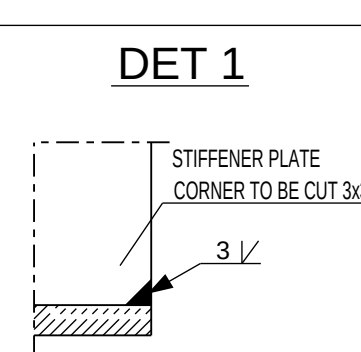
[illegible]

Approved For Construction

PROJECT NAME
Easpring New Materials Oy
FAIR Phase 1

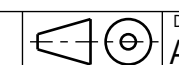


DRAWING CONTENT				
ASSEMBLY DRAWING				
COLUMN_WI				
E51WC-1081				
DATE	ARCHIVING CODE	PAGE	DESIGN GROUP	
2.06.2026			STR	
DESIGNER	APPROVED	CHECKED		REVISION
Aleky Serus	Peri Kowmanah	Jeri Kallipalmi		
E51WC-1081				

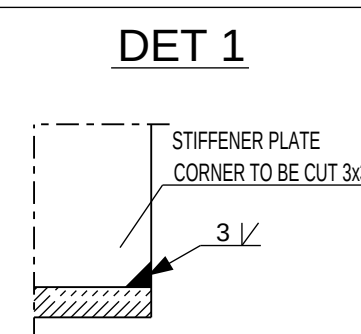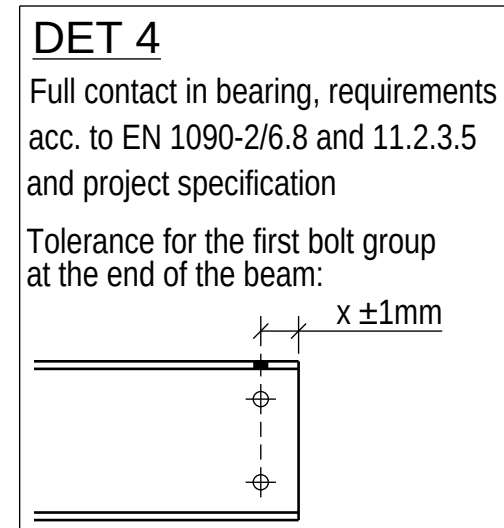[illegible]

Approved For Construction

PROJECT NAME
Easpring New Materials O
FAIR Phase 1

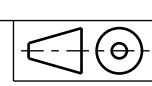

DRAWING CONTENT
ASSEMBLY DRAWING
COLUMN_WI
E51WC-1082




SWECO RAKENNI
ILMALANPORTTI 2
00240 HELSINKI
PUH. +358 207 390
www.sweco.fi

DATE
12.06.2026
DRAWN
Alexy Serrus
PROJECT NUMBER
2501944

PAGE	DESIGN
APPROVED Peri Kivimaa DWG. NO.	CHECKED Jere Kallio

E51WC-1082

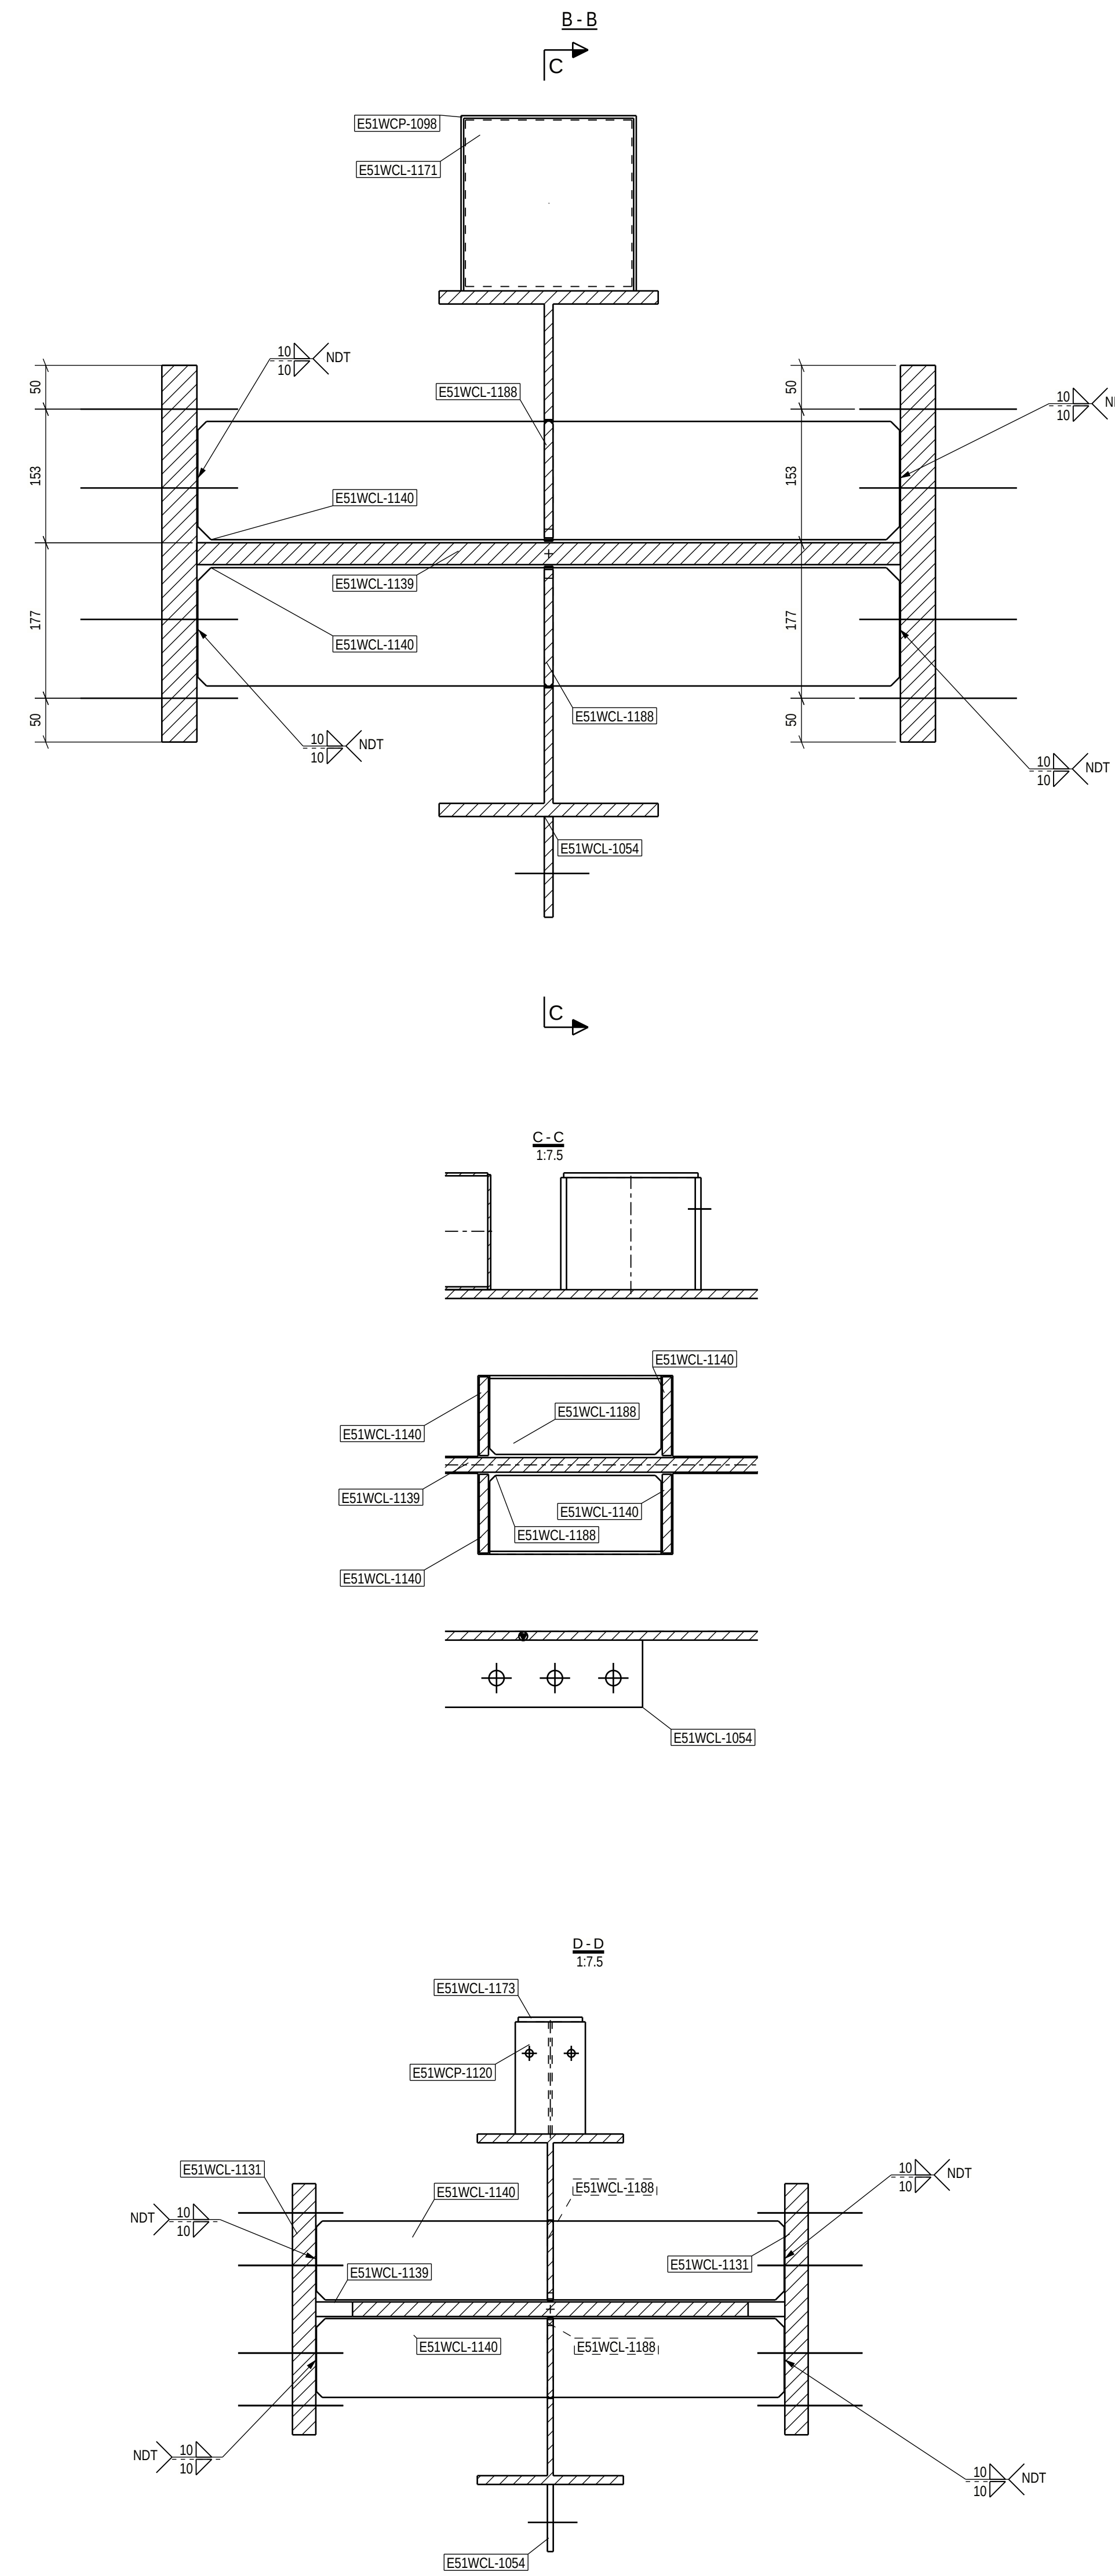


DET 4

Full contact in bearing, requirements acc. to EN 1090-2/6.8 and 11.2.3.5 and project specification

Tolerance for the first bolt group at the end of the beam:



The diagram shows a cross-section of a beam with a vertical web and horizontal flanges. Two bolt groups are shown: one at the end of the beam and another further along. A dimension line with arrows indicates a tolerance zone of width $x \pm 1mm$ for the first bolt group at the end of the beam.

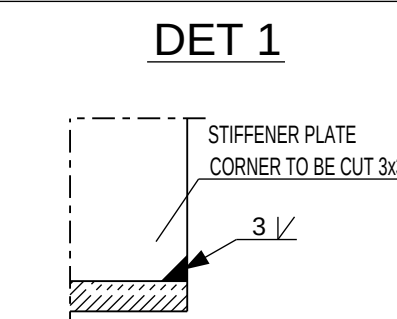

EXC2 Approved For Construction

PROJECT NAME Easpring New Materials Oy FAIR Phase 1				DRAWING CONTENT ASSEMBLY DRAWING COLUMN_WI E51WC-1083	
SWECO RAKENNETEKNIIKKA OY SUOMENRAKENNUSALUE P.O. BOX 72 FIN-00070 HELSINKI PUH +358 907 365 000 WWW.SWECO.FI Sustainable engineering and design		DATE 12.06.2026 DESIGNER Jukka Seppälä CHECKED Aleksi Sassi PROJECT NUMBER 25019443		ARCHIVING CODE PAGE DESIGNED APPROVED Approved by Kouvola Checked by Järvelin E51WC-1083	

