
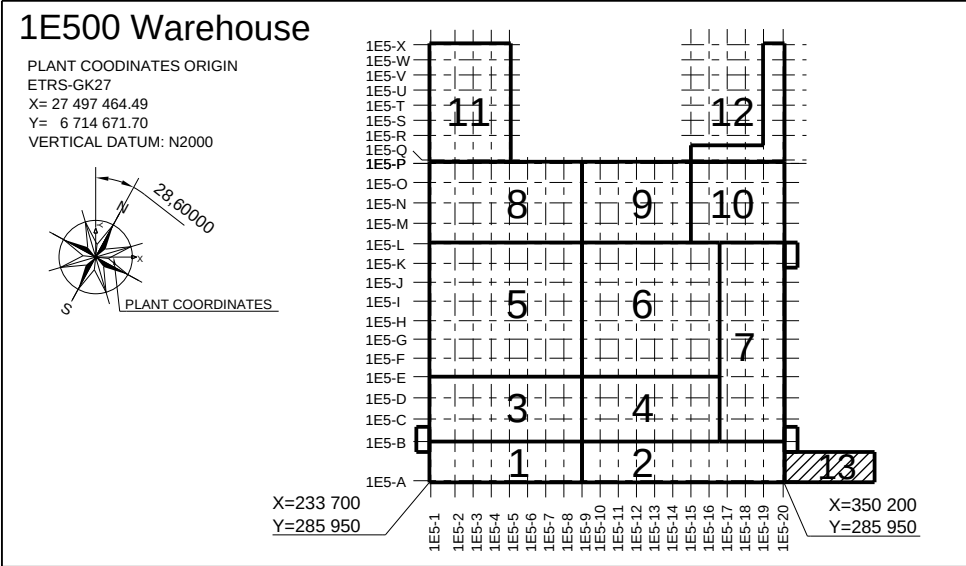


APPROVED FOR CONSTRUCTION 12.06.2026

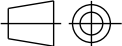

01	E51EX-1029 and 1088 quantity decreased, 1090 and 1091 added. Lists upd				FIALES	18.06.2026	FIKJER
REV.		REVISION			CHANGED BY	DATE	CHECKED BY
Date	Designed	Checked	Approved	Status			
05.06.2026	FIALES	FIKJER	FIKOPE	AFC			
Document ID		Area	Relates		Scale	Size	
25019443-ICC250-0600-0660-001337		1E500				A4	
Project ID		Sub area	Position ID		Discipline		
25019443					CIVIL		
		Title Easpring New Materials Oy FAIR phase 1 Warehouse, Steel Structures, Access bridge between 1A100-1E500, Installation Parts, Assembly Drawings					
Drawing number					Revision	Page/Pages	
25019443-ICC250-0600-0660-001337					01	1/1	

ASSEMBLY PART LIST


Project Number		25019443					Content	Access bridge between 1A100-1E500, Installation Parts							
Project Name		Easpring New Materials Oy					Document	25019443-ICC250-0600-0660-001337							
Project Address		FAIR Phase 1					Status	AFC					Revisio	01	
Author	FIALES	Inspector	FIKJER	Approver	FIPEKO		Rev. Comment:		EX-1029 and 1088 quantity decreased, 1090 and 1091 added					Date	18.06.2026
Phase	Position	Main part name	Main part profile	Exec. Class	Shade (assembly) / Material (part)	Pcs.	Length [mm]	Width [mm]	Height [mm]	Paino [kg]	Weight sum [kg]	Area [m²]	Date	Rev.	Rev. Date
9000	E51EX-1008	PLATE		EXC2	RAL 7024 (Graphite Gray)	16	375	8	210	4.9	79.1	0.17	12.06.2026		
9000	E51EXL-1017		PL8X210		S355J2+N	16	375	210	8	4.9	79.1		12.06.2026		
9000	E51EX-1009	PLATE		EXC2	RAL 7024 (Graphite Gray)	22	535	15	360	22.7	498.9	0.41	12.06.2026		
9000	E51EXL-1018		PL15X360		S355J2+N	22	535	360	15	22.7	498.9		12.06.2026		
9000	E51EX-1010	PLATE		EXC2	RAL 7024 (Graphite Gray)	8	375	15	210	9.3	74.2	0.18	12.06.2026		
9000	E51EXL-1020		PL15X210		S355J2+N	8	375	210	15	9.3	74.2		12.06.2026		
9000	E51EX-1013	PLATE		EXC2	RAL 7024 (Graphite Gray)	8	1280	5	300	15.1	120.6	0.78	12.06.2026		
9000	E51EXL-1004		PL5X300		S355J2+N	8	1280	300	5	15.1	120.6		12.06.2026		
9000	E51EX-1014	PLATE		EXC2	RAL 7024 (Graphite Gray)	8	375	15	310	13.7	109.5	0.25	12.06.2026		
9000	E51EXL-1021		PL15X310		S355J2+N	8	375	310	15	13.7	109.5		12.06.2026		
9000	E51EX-1015	PLATE		EXC2	RAL 7024 (Graphite Gray)	8	375	12	310	11.0	87.6	0.25	12.06.2026		
9000	E51EXL-1019		PL12X310		S355J2+N	8	375	310	12	11.0	87.6		12.06.2026		
9000	E51EX-1016	PLATE		EXC2	RAL 7024 (Graphite Gray)	8	375	8	290	6.8	54.6	0.23	12.06.2026		
9000	E51EXL-1025		PL8X290		S355J2+N	8	375	290	8	6.8	54.6		12.06.2026		
9000	E51EX-1020	PLATE		EXC2	RAL 7024 (Graphite Gray)	12	160	8	360	3.6	43.4	0.12	12.06.2026		
9000	E51EXL-1032		PL8X360		S355J2+N	12	160	360	8	3.6	43.4		12.06.2026		
9000	E51EX-1021	PLATE		EXC2	RAL 7024 (Graphite Gray)	10	580	200	200	28.6	285.6	0.65	12.06.2026		
9000	E51EXL-1033		PL15X200		S355J2+N	10	580	200	15	13.7	136.6		12.06.2026		
9000	E51EXP-1001		T185-10-10-150		S355J2+N	10	580	0	0	14.9	149.0		12.06.2026		
9000	E51EX-1022	PLATE		EXC2	RAL 7024 (Graphite Gray)	6	580	15	200	13.7	82.0	0.26	12.06.2026		
9000	E51EXL-1033		PL15X200		S355J2+N	6	580	200	15	13.7	82.0		12.06.2026		
9000	E51EX-1024	PLATE		EXC2	RAL 7024 (Graphite Gray)	16	435	2	220	1.2	19.2	0.16	12.06.2026		
9000	E51EXL-1027		PL2X220		S355J2+N	16	435	220	2	1.2	19.2		12.06.2026		
9000	E51EX-1027	PLATE		EXC2	RAL 7024 (Graphite Gray)	8	801	5	300	9.4	75.5	0.49	12.06.2026		
9000	E51EXL-1003		PL5X300		S355J2+N	8	801	300	5	9.4	75.5		12.06.2026		

9000	E51EX-1028	PLATE		EXC2	RAL 7024 (Graphite Gray)	6	260	2	200	0.7	4.1	0.09	12.06.2026		
9000	E51EXL-1002		PL2X200		S355J2+N	6	260	200	2	0.7	4.1		12.06.2026		
9000	E51EX-1029	PLATE		EXC2	RAL 7024 (Graphite Gray)	6	240	2	180	0.5	3.2	0.07	12.06.2026	01	18.06.2026
9000	E51EXL-1001		PL2X180		S355J2+N	6	240	180	2	0.5	3.2		12.06.2026	01	18.06.2026
9000	E51EX-1033	PLATE		EXC2	RAL 7024 (Graphite Gray)	1	1040	235	300	65.0	65.0	1.00	12.06.2026		
9000	E51EXL-1035		PL20X300		S355J2+N	1	950	300	20	44.7	44.7		12.06.2026		
9000	E51EXL-1036		PL15X215		S355J2+N	1	1030	215	15	20.3	20.3		12.06.2026		
9000	E51EX-1045	PLATE		EXC2	RAL 7024 (Graphite Gray)	8	505	5	300	4.6	36.7	0.25	12.06.2026		
9000	E51EXL-1085		PL5X300		S355J2+N	8	505	300	5	4.6	36.7		12.06.2026		
9000	E51EX-1046	PLATE		EXC2	RAL 7024 (Graphite Gray)	4	375	10	260	7.7	30.6	0.21	12.06.2026		
9000	E51EXL-1062		PL10X260		S355J2+N	4	375	260	10	7.7	30.6		12.06.2026		
9000	E51EX-1047	PLATE		EXC2	RAL 7024 (Graphite Gray)	5	900	5	300	8.5	42.5	0.46	12.06.2026		
9000	E51EXL-1086		PL5X300		S355J2+N	5	900	300	5	8.5	42.5		12.06.2026		
9000	E51EX-1048	PLATE		EXC2	RAL 7024 (Graphite Gray)	1	900	359	405	88.0	88.0	1.44	12.06.2026		
9000	E51EXL-1060		PL20X305		S355J2+N	1	900	305	20	43.1	43.1		12.06.2026		
9000	E51EXL-1061		PL16X339		S355J2+N	1	775	339	16	28.8	28.8		12.06.2026		
9000	E51EXL-1081		L100*12		S355J2	1	900	0	0	16.0	16.0		12.06.2026		
9000	E51EX-1049	PLATE		EXC2	RAL 7024 (Graphite Gray)	4	1600	5	600	37.7	150.7	1.94	12.06.2026		
9000	E51EXL-1069		PL5X600		S355J2+N	4	1600	600	5	37.7	150.7		12.06.2026		
9000	E51EX-1050	PLATE		EXC2	RAL 7024 (Graphite Gray)	4	1600	5	600	37.7	150.7	1.94	12.06.2026		
9000	E51EXL-1065		PL5X600		S355J2+N	4	1600	600	5	37.7	150.7		12.06.2026		
9000	E51EX-1051	PLATE		EXC2	RAL 7024 (Graphite Gray)	1	300	235	950	78.2	78.2	1.11	12.06.2026		
9000	E51EXL-1035		PL20X300		S355J2+N	1	950	300	20	44.7	44.7		12.06.2026		
9000	E51EXL-1070		PL20X215		S355J2+N	1	930	215	20	30.6	30.6		12.06.2026		
9000	E51EXL-1071		PL15X130		S355J2+N	1	195	130	15	2.8	2.8		12.06.2026		
9000	E51EX-1052	PLATE		EXC2	RAL 7024 (Graphite Gray)	1	950	235	300	70.5	73.4	1.16	12.06.2026		
9000	E51EXL-1035		PL20X300		S355J2+N	1	950	300	20	44.7	44.7		12.06.2026		
9000	E51EXL-1071		PL15X130		S355J2+N	2	195	130	15	2.8	5.6		12.06.2026		
9000	E51EXL-1078		PL15X215		S355J2+N	1	930	215	15	23.0	23.0		12.06.2026		
9000	E51EX-1053	PLATE		EXC2	RAL 7024 (Graphite Gray)	2	925	5	625	18.7	37.4	0.97	12.06.2026		
9000	E51EXL-1091		PL5X625		S355J2+N	2	925	625	5	18.7	37.4		12.06.2026		
9000	E51EX-1054	PLATE		EXC2	RAL 7024 (Graphite Gray)	2	940	5	625	19.0	38.0	0.98	12.06.2026		
9000	E51EXL-1090		PL5X625		S355J2+N	2	940	625	5	19.0	38.0		12.06.2026		

9000	E51EX-1055	PLATE		EXC2	RAL 7024 (Graphite Gray)	1	935	223	690	155.5	155.5	2.14	12.06.2026		
9000	E51EXL-1058		PL20X625		S355J2+N	1	925	625	20	74.8	74.8		12.06.2026		
9000	E51EXL-1073		PL20X220		S355J2+N	1	670	220	20	23.1	23.1		12.06.2026		
9000	E51EXL-1083		PL10X76		S355J2+N	1	245	76	10	1.5	1.5		12.06.2026		
9000	E51EXL-1087		PL30X181		S355J2+N	1	844	181	30	33.0	33.0		12.06.2026		
9000	E51EXL-1088		PL15X181		S355J2+N	1	190	181	15	3.9	3.9		12.06.2026		
9000	E51EXP-1004		IPE550		S355J2	1	183	0	0	19.2	19.2		12.06.2026		
9000	E51EX-1056	PLATE		EXC2	RAL 7024 (Graphite Gray)	1	940	223	700	155.4	155.4	2.11	12.06.2026		
9000	E51EXL-1059		PL20X625		S355J2+N	1	940	625	20	75.9	75.9		12.06.2026		
9000	E51EXL-1077		PL20X220		S355J2+N	1	680	220	20	23.4	23.4		12.06.2026		
9000	E51EXL-1087		PL30X181		S355J2+N	1	844	181	30	33.0	33.0		12.06.2026		
9000	E51EXL-1088		PL15X181		S355J2+N	1	190	181	15	3.9	3.9		12.06.2026		
9000	E51EXP-1004		IPE550		S355J2	1	183	0	0	19.2	19.2		12.06.2026		
9000	E51EX-1057	PLATE		EXC2	RAL 7024 (Graphite Gray)	2	550	2	210	1.8	3.6	0.23	12.06.2026		
9000	E51EXL-1082		PL2X210		S355J2+N	2	550	210	2	1.8	3.6		12.06.2026		
9000	E51EX-1058	PLATE		EXC2	RAL 7024 (Graphite Gray)	48	530	2	220	1.5	71.6	0.20	12.06.2026		
9000	E51EXL-1050		PL2X220		S355J2+N	48	530	220	2	1.5	71.6		12.06.2026		
9000	E51EX-1059	PLATE		EXC2	RAL 7024 (Graphite Gray)	2	530	2	220	1.5	2.9	0.19	12.06.2026		
9000	E51EXL-1052		PL2X220		S355J2+N	2	530	220	2	1.5	2.9		12.06.2026		
9000	E51EX-1060	PLATE		EXC2	RAL 7024 (Graphite Gray)	16	440	12	390	16.2	258.6	0.36	12.06.2026		
9000	E51EXL-1079		PL12X390		S355J2+N	16	440	390	12	16.2	258.6		12.06.2026		
9000	E51EX-1061	Beam		EXC2	RAL 7024 (Graphite Gray)	2	229	300	390	43.7	87.3	0.65	12.06.2026		
9000	E51EXL-1072		PL20X290		S355J2+N	2	390	290	20	17.6	35.3		12.06.2026		
9000	E51EXP-1003		HEA400		S355J2	2	209	0	0	26.0	52.0		12.06.2026		
9000	E51EX-1062	PLATE		EXC2	RAL 7024 (Graphite Gray)	2	495	2	200	1.2	2.5	0.16	12.06.2026		
9000	E51EXL-1051		PL2X200		S355J2+N	2	495	200	2	1.2	2.5		12.06.2026		
9000	E51EX-1063	PLATE		EXC2	RAL 7024 (Graphite Gray)	8	605	55	105	2.7	21.4	0.14	12.06.2026		
9000	E51EXL-1084		PL5X105		S355J2+N	8	646	105	5	2.7	21.4		12.06.2026		
9000	E51EX-1064	PLATE		EXC2	RAL 7024 (Graphite Gray)	32	375	8	210	4.9	158.3	0.17	12.06.2026		
9000	E51EXL-1017		PL8X210		S355J2+N	32	375	210	8	4.9	158.3		12.06.2026		
9000	E51EX-1065	PLATE		EXC2	RAL 7024 (Graphite Gray)	58	535	15	360	22.7	1315.4	0.41	12.06.2026		
9000	E51EXL-1018		PL15X360		S355J2+N	58	535	360	15	22.7	1315.4		12.06.2026		
9000	E51EX-1066	PLATE		EXC2	RAL 7024 (Graphite Gray)	8	375	15	210	9.3	74.2	0.18	12.06.2026		
9000	E51EXL-1020		PL15X210		S355J2+N	8	375	210	15	9.3	74.2		12.06.2026		
9000	E51EX-1067	PLATE		EXC2	RAL 7024 (Graphite Gray)	8	460	5	930	16.4	131.2	0.85	12.06.2026		

9000	E51EXL-1080		PL5X930		S355J2+N	8	460	930	5	16.4	131.2		12.06.2026		
9000	E51EX-1068	PLATE		EXC2	RAL 7024 (Graphite Gray)	8	175	15	170	3.5	28.0	0.07	12.06.2026		
9000	E51EXL-1064		PL15X170		S355J2+N	8	175	170	15	3.5	28.0		12.06.2026		
9000	E51EX-1069	PLATE		EXC2	RAL 7024 (Graphite Gray)	8	1280	5	300	15.1	120.6	0.78	12.06.2026		
9000	E51EXL-1063		PL5X300		S355J2+N	8	1280	300	5	15.1	120.6		12.06.2026		
9000	E51EX-1071	PLATE		EXC2	RAL 7024 (Graphite Gray)	5	300	30	640	45.2	226.1	0.44	12.06.2026		
9000	E51EXL-1067		PL30X300		S355J2+N	5	640	300	30	45.2	226.1		12.06.2026		
9000	E51EX-1072	PLATE		EXC2	RAL 7024 (Graphite Gray)	8	530	10	160	6.7	53.3	0.18	12.06.2026		
9000	E51EXL-1068		PL10X160		S355J2+N	8	530	160	10	6.7	53.3		12.06.2026		
9000	E51EX-1074	PLATE		EXC2	RAL 7024 (Graphite Gray)	4	580	185	200	18.1	72.3	0.34	12.06.2026		
9000	E51EXL-1033		PL15X200		S355J2+N	4	580	200	15	13.7	54.6		12.06.2026		
9000	E51VEXL-1017		PL15X170		S355J2+N	4	220	170	15	4.4	17.6		12.06.2026		
9000	E51EX-1075	PLATE		EXC2	RAL 7024 (Graphite Gray)	8	180	10	360	5.1	40.7	0.14	12.06.2026		
9000	E51EXL-1049		PL10X360		S355J2+N	8	180	360	10	5.1	40.7		12.06.2026		
9000	E51EX-1076	PLATE		EXC2	RAL 7024 (Graphite Gray)	8	530	3	80	0.8	6.7	0.09	12.06.2026		
9000	E51EXL-1066		PL2.5X80		S355J2+N	8	530	80	3	0.8	6.7		12.06.2026		
9000	E51EX-1077	PLATE		EXC2	RAL 7024 (Graphite Gray)	8	100	10	360	2.8	22.6	0.08	12.06.2026		
9000	E51EXL-1089		PL10X360		S355J2+N	8	100	360	10	2.8	22.6		12.06.2026		
9000	E51EX-1078	PLATE		EXC2	RAL 7024 (Graphite Gray)	8	375	10	210	6.2	49.5	0.17	12.06.2026		
9000	E51EXL-1076		PL10X210		S355J2+N	8	375	210	10	6.2	49.5		12.06.2026		
9000	E51EX-1079	PLATE		EXC2	RAL 7024 (Graphite Gray)	1	940	235	300	61.1	61.1	0.94	12.06.2026		
9000	E51EXL-1053		PL20X300		S355J2+N	1	900	300	20	42.4	42.4		12.06.2026		
9000	E51EXL-1055		PL15X215		S355J2+N	1	940	215	15	18.8	18.8		12.06.2026		
9000	E51EX-1080	PLATE		EXC2	RAL 7024 (Graphite Gray)	1	960	235	300	63.4	63.4	0.97	12.06.2026		
9000	E51EXL-1054		PL20X300		S355J2+N	1	940	300	20	44.3	44.3		12.06.2026		
9000	E51EXL-1056		PL15X215		S355J2+N	1	960	215	15	19.1	19.1		12.06.2026		
9000	E51EX-1081	PLATE		EXC2	RAL 7024 (Graphite Gray)	1	950	235	300	63.1	63.1	0.97	12.06.2026		
9000	E51EXL-1035		PL20X300		S355J2+N	1	950	300	20	44.7	44.7		12.06.2026		
9000	E51EXL-1057		PL15X215		S355J2+N	1	930	215	15	18.4	18.4		12.06.2026		
9000	E51EX-1082	PLATE		EXC2	RAL 7024 (Graphite Gray)	16	435	2	220	1.2	19.2	0.16	12.06.2026		
9000	E51EXL-1027		PL2X220		S355J2+N	16	435	220	2	1.2	19.2		12.06.2026		
9000	E51EX-1083	PLATE		EXC2	RAL 7024 (Graphite Gray)	32	550	5	450	9.7	310.9	0.51	12.06.2026		
9000	E51EXL-1075		PL5X450		S355J2+N	32	550	450	5	9.7	310.9		12.06.2026		

9000	E51EX-1084	PLATE		EXC2	RAL 7024 (Graphite Gray)	24	550	5	430	9.3	222.8	0.48	12.06.2026		
9000	E51EXL-1074		PL5X430		S355J2+N	24	550	430	5	9.3	222.8		12.06.2026		
9000	E51EX-1085	PLATE		EXC2	RAL 7024 (Graphite Gray)	34	260	2	200	0.7	23.4	0.09	12.06.2026		
9000	E51EXL-1002		PL2X200		S355J2+N	34	260	200	2	0.7	23.4		12.06.2026		
9000	E51EX-1086	PLATE		EXC2	RAL 7024 (Graphite Gray)	4	236	2	200	0.6	2.4	0.08	12.06.2026		
9000	E51EXL-1048		PL2X200		S355J2+N	4	236	200	2	0.6	2.4		12.06.2026		
9000	E51EX-1087	PLATE		EXC2	RAL 7024 (Graphite Gray)	4	236	2	200	0.6	2.4	0.08	12.06.2026		
9000	E51EXL-1048		PL2X200		S355J2+N	4	236	200	2	0.6	2.4		12.06.2026		
9000	E51EX-1088	PLATE		EXC2	RAL 7024 (Graphite Gray)	8	240	2	180	0.5	4.3	0.07	12.06.2026	01	18.06.2026
9000	E51EXL-1001		PL2X180		S355J2+N	8	240	180	2	0.5	4.3		12.06.2026	01	18.06.2026
9000	E51EX-1089	PLATE		EXC2	RAL 7024 (Graphite Gray)	3	300	100	640	54.4	163.1	0.69	12.06.2026		
9000	E51EXL-1067		PL30X300		S355J2+N	3	640	300	30	45.2	135.6		12.06.2026		
9000	E51EXP-1002		T70-10-10-120		S355J2+N	3	640	0	0	9.2	27.5		12.06.2026		
9000	E51EX-1090	PLATE		EXC2	RAL 7024 (Graphite Gray)	2	240	2	180	0.5	1.0	0.07	18.06.2026		
9000	E51EXL-1092		PL2X180		S355J2+N	2	240	180	2	0.5	1.0		18.06.2026		
9000	E51EX-1091	PLATE		EXC2	RAL 7024 (Graphite Gray)	48	165	10	165	2.1	102.6	0.06	18.06.2026		
9000	E51EXL-1031		PL10X165		S355J2+N	48	165	165	10	2.1	102.6		18.06.2026		

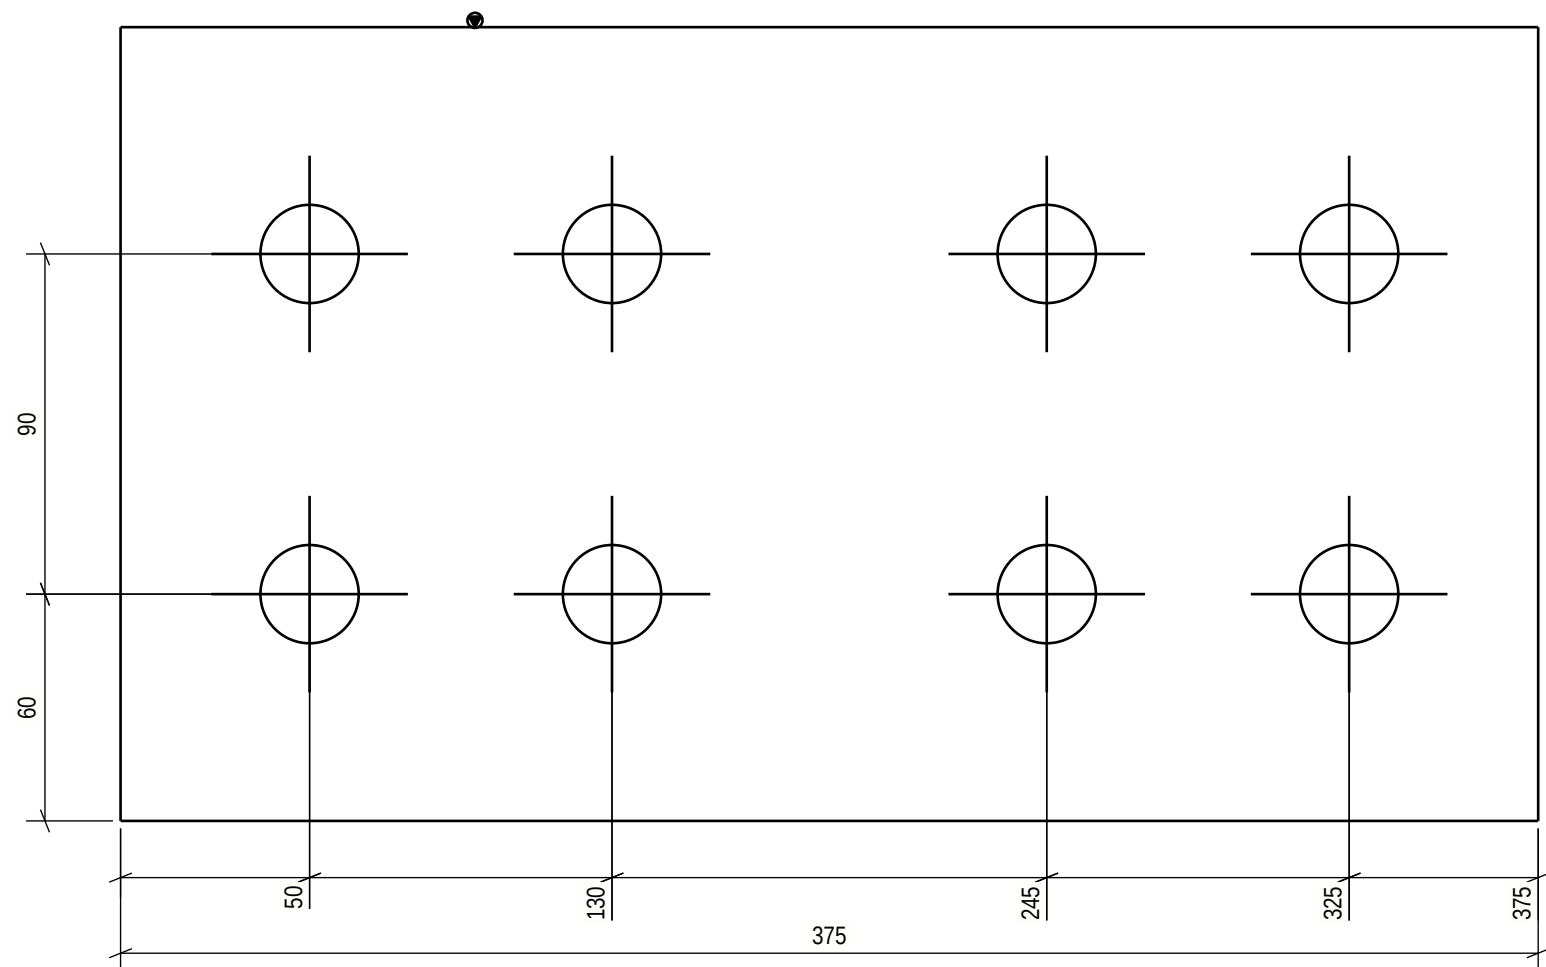


For special tolerances of bolt hole location
see specification for steel structures
Approved For Construction

PART LIST FOR ASSEMBLY E51EX-1008, MANUFACTURING AMOUNT 16 PIECES						
PART	PROFILE	MATERIAL	LENGTH [mm]	AREA [m2]	WEIGHT [kg]	PCS
E51EXL-1017	PL8X210	S355J2+N	375	0.17	4.9	1
TOTAL:				0.17	4.9	

Technical fabrication requirements:		Execution class
EXC2		
Requirements for fabrication, standard	Fabrication tolerances	
EN1090-2, table A.3 : EXC2	EN 1090-2, Appendix B	
Execution Specification document nr	Special fabrication tolerances	
25019443-ICC250-0600-0660-000005	Project specification/ shown on drwg.	
Surface preparation grade	Weld inspection, requirements	
ISO8501-3, grade P2	EN 1090-2,Table 24, U>0.5	
Surface treatment	Extent of NDT, fillet welds	
ISO12944-5	MT-EN1290,20% of welds	
Additional requirements on surface treatment	Extent of NDT, butt welds	
C3.07, EPPUR 240/2	UT, EN-ISO17640, 20% of welds	
Shade	Extent of NDT for splices not shown on drawing	
RAL 7024 (Graphite Gray)	UT, EN-ISO17640, 100%of welds	
Welding of built up steel section	Requirements on holing	
Appendix 1 / Project spec.	EN1090-2 Section 6.6.3	
Welds, if not specified otherwise	Weld class	
EN 9692-1, EN 9692-2	C, EN ISO 5817	
Additional material inspection		Shown on drwg.

FIRE PROTECTION: SAME AS FOR E51V-1012

PROJECT NAME
Easpring New Materials Oy
FAIR Phase 1

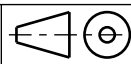


DRAWING CONTENT
ASSEMBLY DRAWING
PLATE
E51EX-1008



SWECO RAKENNTEKNIikka OY
ILMALANPORTTI 2
00240 HELSINKI
PUH. +358 207 393 000
www.sweco.fi

DATE	ARCHIVING CODE	PAGE	DESIGN GROUP
12.06.2026			STR
DRAWN	DESIGNER	APPROVED	CHECKED
Alexey Serous	Alexey Serous	Pertti Koivumaaanaho	Jere Kallosalmi
PROJECT NUMBER	DWG. NO.	REVISION	
25019443	E51EX-1008		

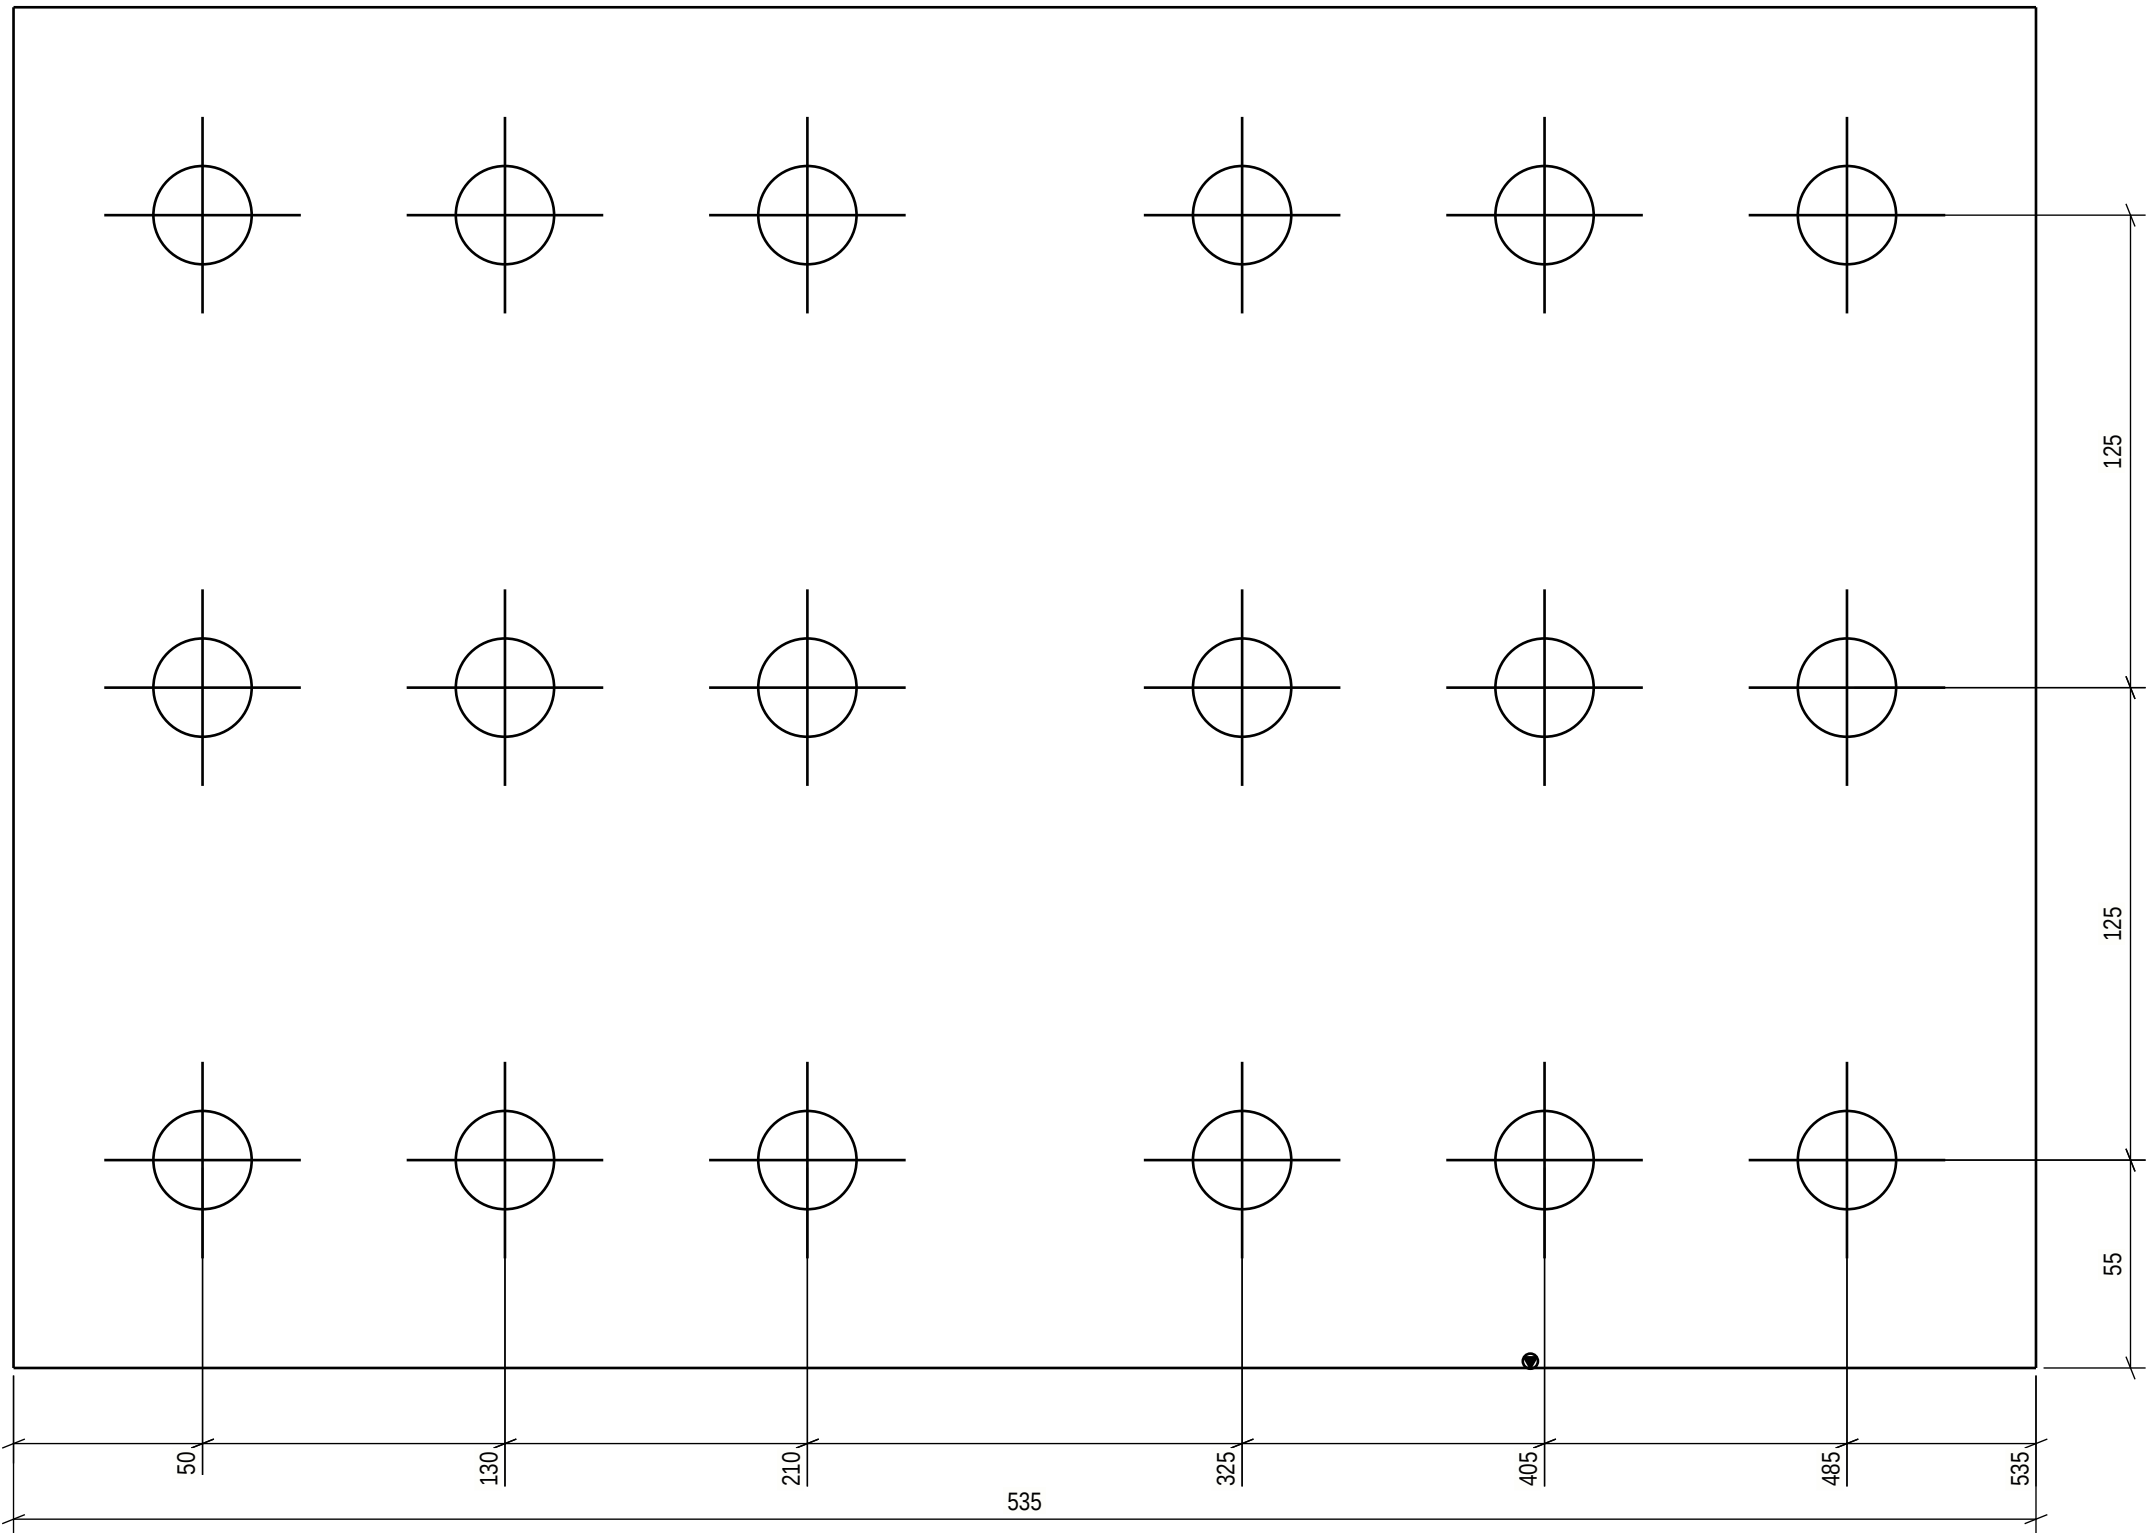


For special tolerances of bolt hole location
see specification for steel structures
Approved For Construction

PART LIST FOR ASSEMBLY E51EX-1009, MANUFACTURING AMOUNT 22 PIECES						
PART	PROFILE	MATERIAL	LENGTH [mm]	AREA [m2]	WEIGHT [kg]	PCS
E51EXL-1018	PL15X360	S355J2+N	535	0.41	22.7	1
TOTAL:				0.41	22.7	

Technical fabrication requirements:		Execution class
Requirements for fabrication, standard EN1090-2, table A.3 : EXC2		EXC2
Execution Specification document nr 25019443-ICC250-0600-0660-000005	Fabrication tolerances EN 1090-2, Appendix B Special fabrication tolerances Project specification/ shown on drwg.	
Surface preparation grade ISO8501-3, grade P2	Weld inspection, requirements EN 1090-2,Table 24, U>0.5	
Surface treatment ISO12944-5	Extent of NDT, fillet welds MT-EN1290,20% of welds	
Additional requirements on surface treatment C3.07, EPPUR 240/2	Extent of NDT, butt welds UT, EN-ISO17640, 20% of welds	
Shade RAL 7024 (Graphite Gray)	Extent of NDT for splices not shown on drawing UT, EN-ISO17640, 100%of welds	
Welding of built up steel section Appendix 1 / Project spec.	Requirements on holing EN1090-2 Section 6.6.3	
Welds, if not specified otherwise EN 9692-1, EN 9692-2	Weld class C, EN ISO 5817	Additional material inspection Shown on drwg.

FIRE PROTECTION: SAME AS FOR E51V-1012

PROJECT NAME
Easpring New Materials Oy
FAIR Phase 1

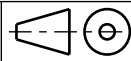


DRAWING CONTENT
ASSEMBLY DRAWING
PLATE
E51EX-1009



SWECO RAKENNETEKNIikka OY
ILMALANPORTTI 2
00240 HELSINKI
PUH. +358 207 393 000
www.sweco.fi

DATE	ARCHIVING CODE	PAGE	DESIGN GROUP
12.06.2026			STR
DRAWN	DESIGNER	APPROVED	CHECKED
Alexey Serous	Alexey Serous	Pertti Koivumaa	Jere Kallosalmi
PROJECT NUMBER	DWG. NO.	REVISION	
25019443	E51EX-1009		

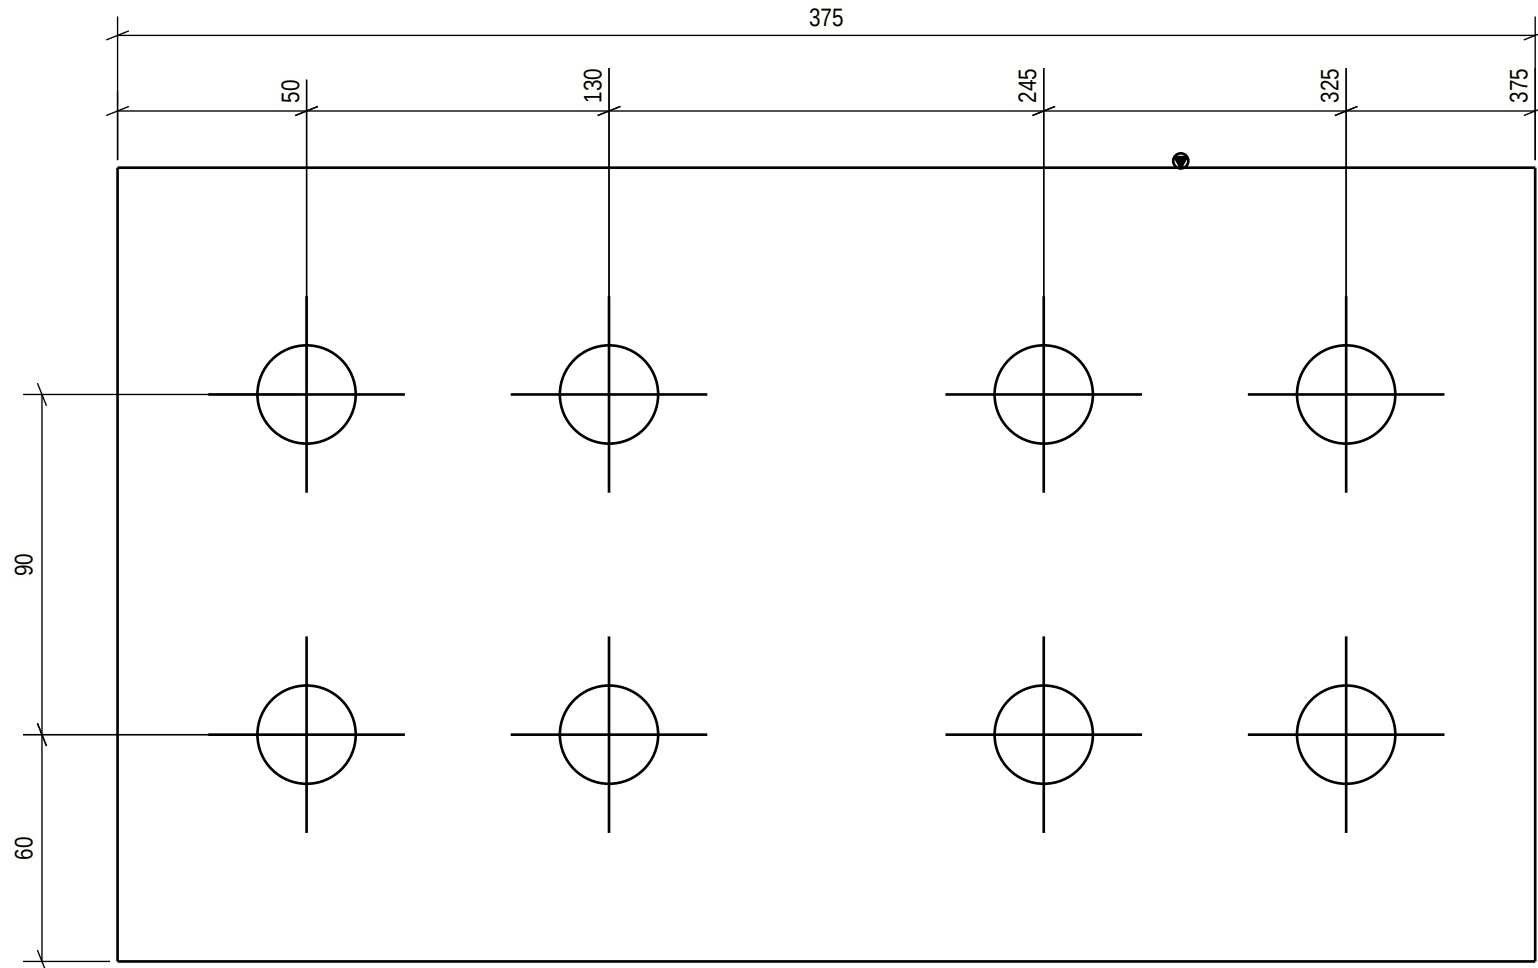


For special tolerances of bolt hole location
see specification for steel structures
Approved For Construction

PART LIST FOR ASSEMBLY E51EX-1010, MANUFACTURING AMOUNT 8 PIECES						
PART	PROFILE	MATERIAL	LENGTH [mm]	AREA [m2]	WEIGHT [kg]	PCS
E51EXL-1020	PL15X210	S355J2+N	375	0.18	9.3	1
TOTAL:				0.18	9.3	

Technical fabrication requirements:		Execution class
EXC2		
Requirements for fabrication, standard	Fabrication tolerances	
EN1090-2, table A.3 : EXC2	EN 1090-2, Appendix B	
Execution Specification document nr	Special fabrication tolerances	
25019443-ICC250-0600-0660-000005	Project specification/ shown on drwg.	
Surface preparation grade	Weld inspection, requirements	
ISO8501-3, grade P2	EN 1090-2,Table 24, U>0.5	
Surface treatment	Extent of NDT, filled welds	
ISO12944-5	MT-EN1290,20% of welds	
Additional requirements on surface treatment	Extent of NDT, butt welds	
C3.07, EPPUR 240/2	UT, EN-ISO17640, 20% of welds	
Shade	Extent of NDT for splices not shown on drawing	
RAL 7024 (Graphite Gray)	UT, EN-ISO17640, 100%of welds	
Welding of built up steel section	Requirements on holing	
Appendix 1 / Project spec.	EN1090-2 Section 6.6.3	
Welds, if not specified otherwise	Weld class	
EN 9692-1, EN 9692-2	C, EN ISO 5817	
Additional material inspection		Shown on drwg.

FIRE PROTECTION: SAME AS FOR E51V-1012

PROJECT NAME
Easpring New Materials Oy
FAIR Phase 1

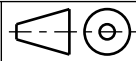


DRAWING CONTENT
ASSEMBLY DRAWING
PLATE
E51EX-1010



SWECO RAKENNETEKNIikka OY
ILMALANPORTTI 2
00240 HELSINKI
PUH. +358 207 393 000
www.sweco.fi

DATE	ARCHIVING CODE	PAGE	DESIGN GROUP
12.06.2026			STR
DRAWN	DESIGNER	APPROVED	CHECKED
Alexey Serous	Alexey Serous	Pertti Koivumaaanaho	Jere Kallosalmi
PROJECT NUMBER	DWG. NO.	REVISION	
25019443	E51EX-1010		

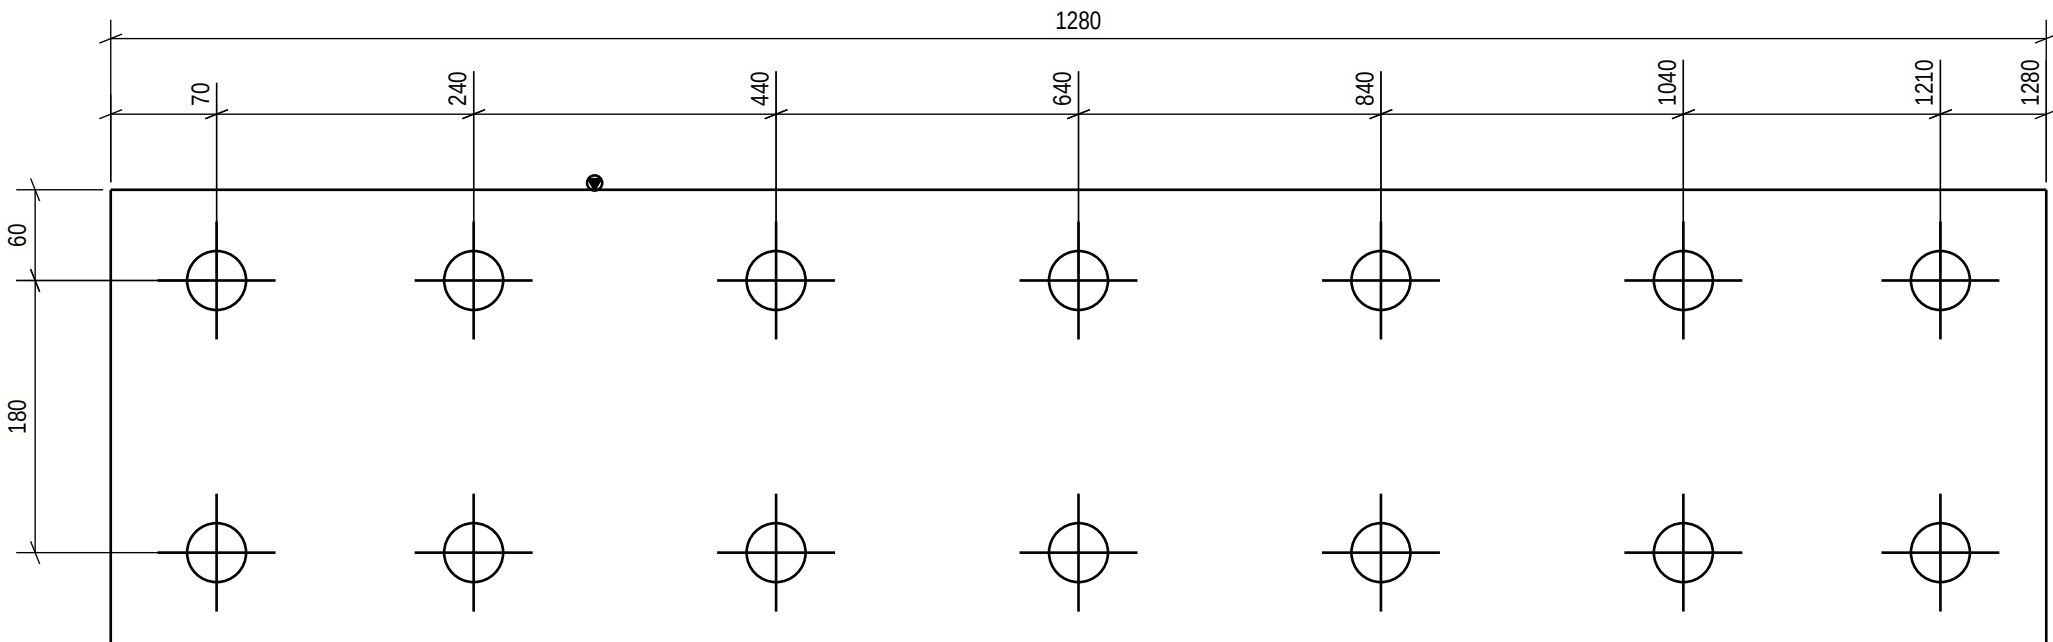



For special tolerances of bolt hole location
see specification for steel structures
Approved For Construction

PART LIST FOR ASSEMBLY E51EX-1013, MANUFACTURING AMOUNT 8 PIECES						
PART	PROFILE	MATERIAL	LENGTH [mm]	AREA [m2]	WEIGHT [kg]	PCS
E51EXL-1004	PL5X300	S355J2+N	1280	0.78	15.1	1
TOTAL:				0.78	15.1	

Technical fabrication requirements:		Execution class
EXC2		
Requirements for fabrication, standard	Fabrication tolerances	
EN1090-2, table A.3 : EXC2	EN 1090-2, Appendix B	
Execution Specification document nr	Special fabrication tolerances	
25019443-ICC250-0600-0660-000005	Project specification/ shown on drwg.	
Surface preparation grade	Weld inspection, requirements	
ISO8501-3, grade P2	EN 1090-2,Table 24, U>0.5	
Surface treatment	Extent of NDT, fillet welds	
ISO12944-5	MT-EN1290,20% of welds	
Additional requirements on surface treatment	Extent of NDT, butt welds	
C3.07, EPPUR 240/2	UT, EN-ISO17640, 20% of welds	
Shade	Extent of NDT for splices not shown on drawing	
RAL 7024 (Graphite Gray)	UT, EN-ISO17640, 100%of welds	
Welding of built up steel section	Requirements on holing	
Appendix 1 / Project spec.	EN1090-2 Section 6.6.3	
Welds, if not specified otherwise	Weld class	Additional material inspection
EN 9692-1, EN 9692-2	C, EN ISO 5817	Shown on drwg.

FIRE PROTECTION SAME AS FOR E51WC-1031

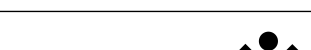PROJECT NAME		DRAWING CONTENT			
Easpring New Materials Oy FAIR Phase 1		ASSEMBLY DRAWING			
		PLATE			
		E51EX-1013			
 Sustainable engineering and design	SWECO RAKENNETEKNIikka OY ILMALANPORTTI 2 00240 HELSINKI PUH. +358 207 393 000 www.sweco.fi	DATE	ARCHIVING CODE	PAGE	DESIGN GROUP
		12.06.2026			STR
		DRAWN	DESIGNER	APPROVED	CHECKED
		Alexey Serous	Alexey Serous	Pertti Koivumaaanaho	Jere Kalliosalmi
		PROJECT NUMBER		DWG. NO.	
		25019443		E51EX-1013	

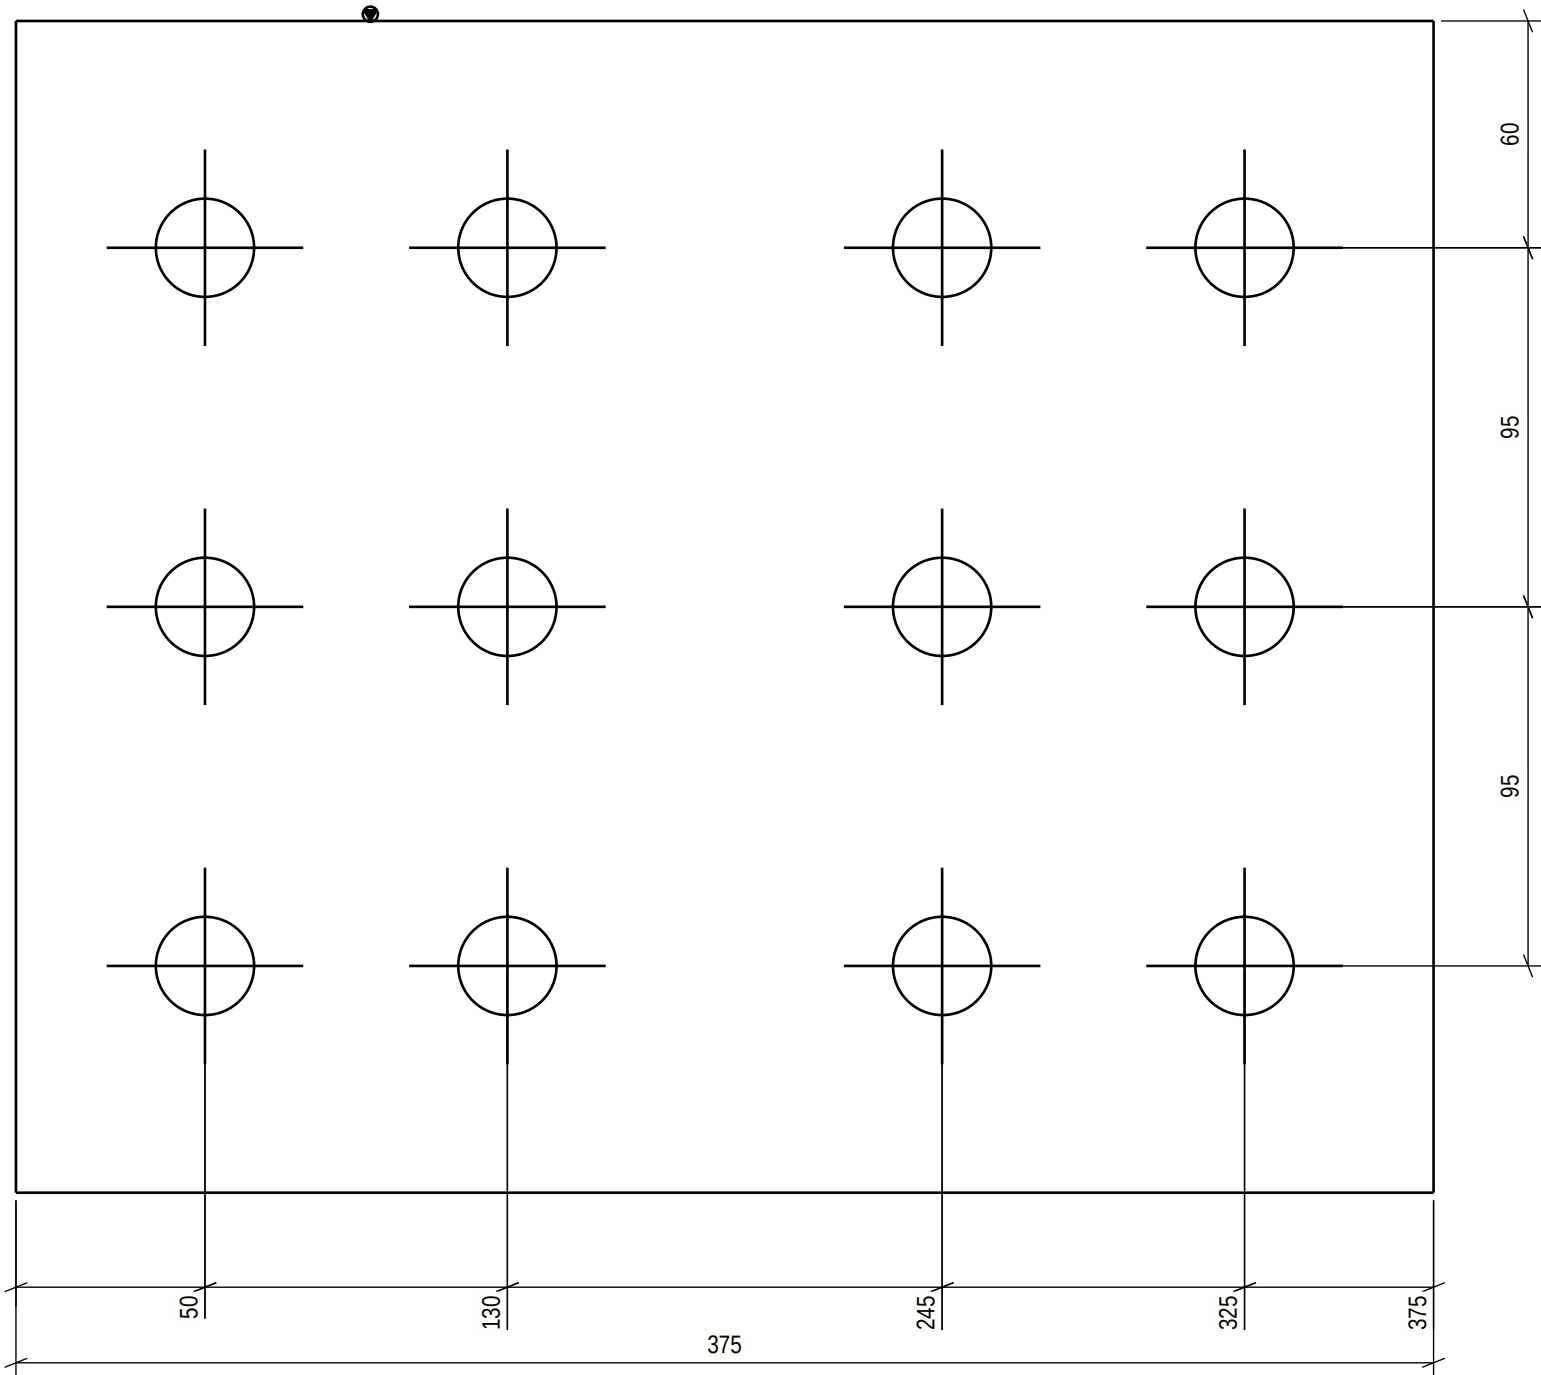


For special tolerances of bolt hole location
see specification for steel structures
Approved For Construction

PART LIST FOR ASSEMBLY E51EX-1014, MANUFACTURING AMOUNT 8 PIECES						
PART	PROFILE	MATERIAL	LENGTH [mm]	AREA [m2]	WEIGHT [kg]	PCS
E51EXL-1021	PL15X310	S355J2+N	375	0.25	13.7	1
TOTAL:				0.25	13.7	

Technical fabrication requirements:		Execution class
EXC2		
Requirements for fabrication, standard	Fabrication tolerances	
EN1090-2, table A.3 : EXC2	EN 1090-2, Appendix B	
Execution Specification document nr	Special fabrication tolerances	
25019443-ICC250-0600-0660-000005	Project specification/ shown on drwg.	
Surface preparation grade	Weld inspection, requirements	
ISO8501-3, grade P2	EN 1090-2,Table 24, U>0.5	
Surface treatment	Extent of NDT, fillet welds	
ISO12944-5	MT-EN1290,20% of welds	
Additional requirements on surface treatment	Extent of NDT, butt welds	
C3.07, EPPUR 240/2	UT, EN-ISO17640, 20% of welds	
Shade	Extent of NDT for splices not shown on drawing	
RAL 7024 (Graphite Gray)	UT, EN-ISO17640, 100%of welds	
Welding of built up steel section	Requirements on holing	
Appendix 1 / Project spec.	EN1090-2 Section 6.6.3	
Welds, if not specified otherwise	Weld class	Additional material inspection
EN 9692-1, EN 9692-2	C, EN ISO 5817	Shown on drwg.

FIRE PROTECTION: SAME AS FOR E51V-1012

PROJECT NAME
Easpring New Materials Oy
FAIR Phase 1

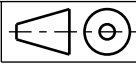


DRAWING CONTENT
ASSEMBLY DRAWING
PLATE
E51EX-1014



SWECO RAKENNTEKNIikka OY
ILMALANPORTTI 2
00240 HELSINKI
PUH. +358 207 393 000
www.sweco.fi

DATE	ARCHIVING CODE	PAGE	DESIGN GROUP
12.06.2026			STR
DRAWN	DESIGNER	APPROVED	CHECKED
Alexey Serous	Alexey Serous	Pertti Koivumaaanaho	Jere Kallosalmi
PROJECT NUMBER	DWG. NO.	REVISION	
25019443	E51EX-1014		

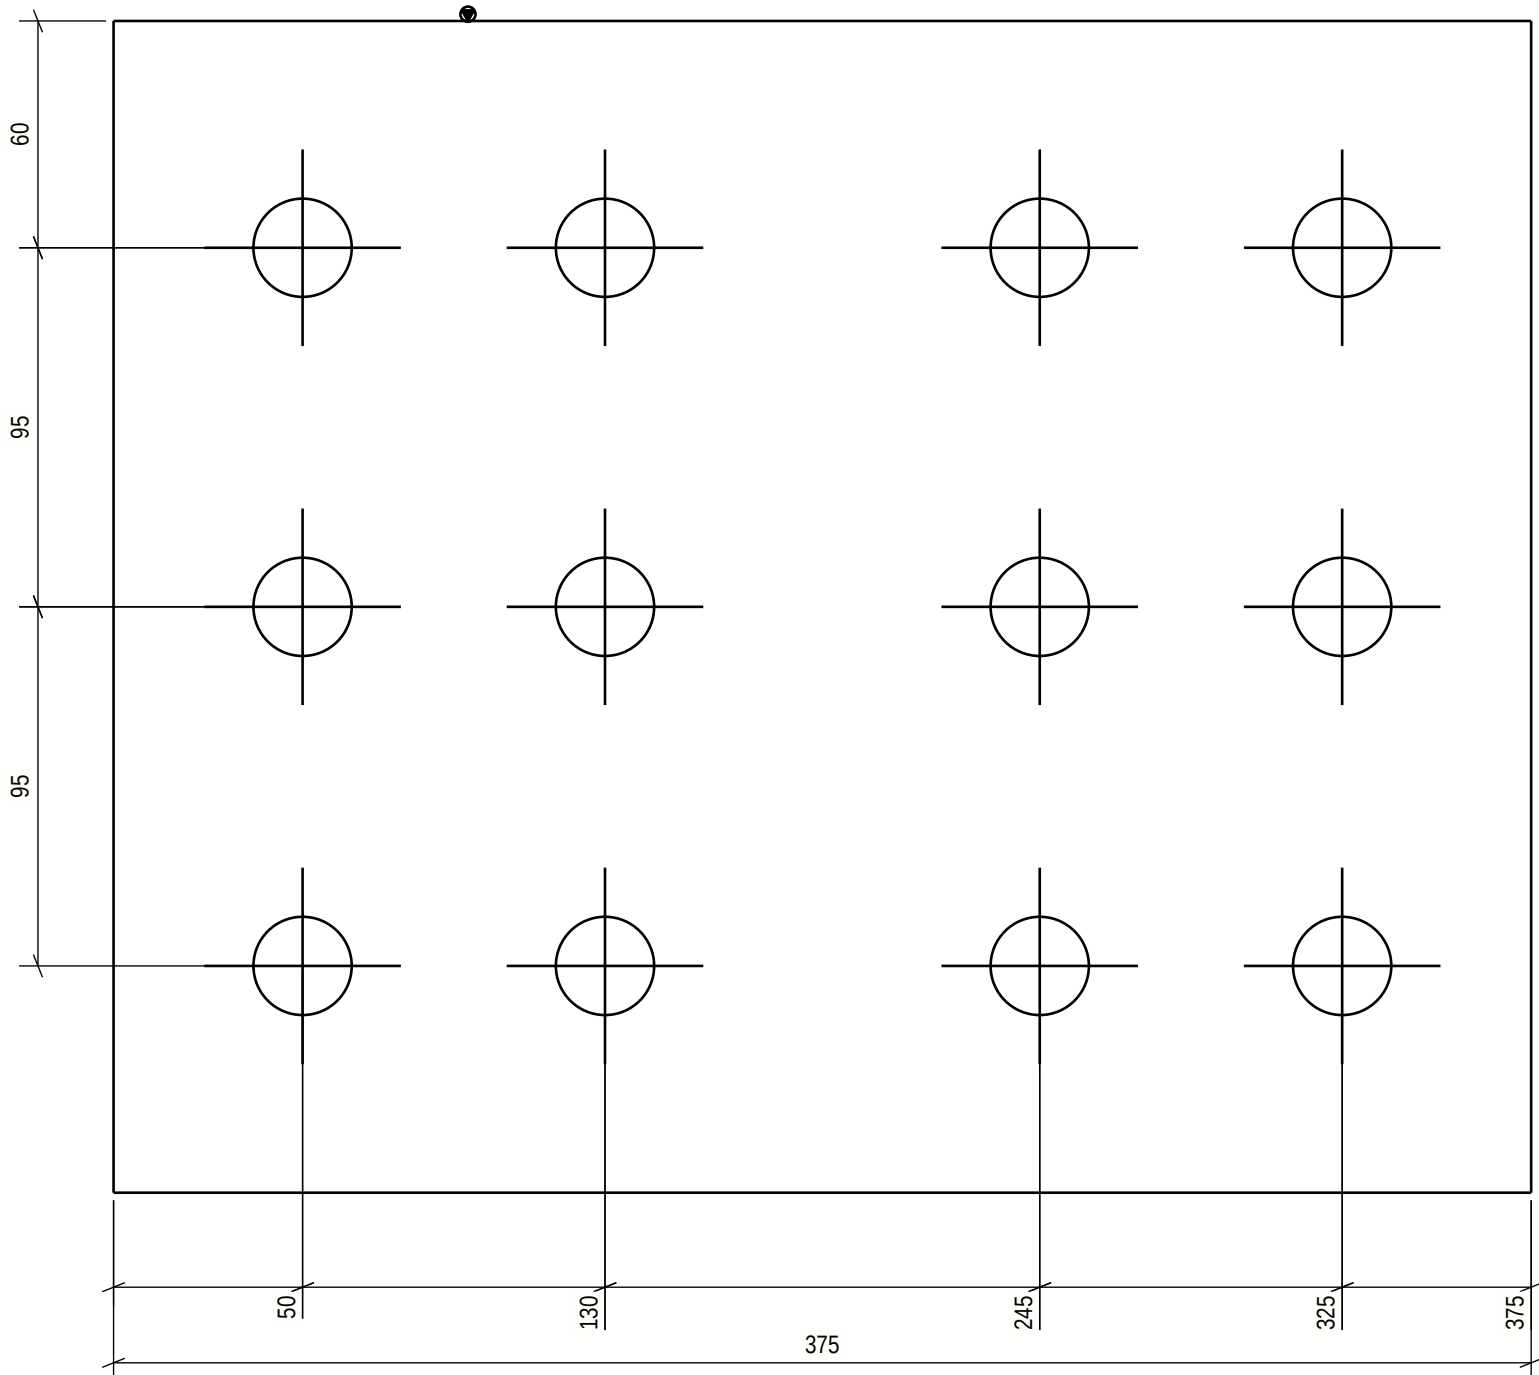


For special tolerances of bolt hole location
see specification for steel structures
Approved For Construction

PART LIST FOR ASSEMBLY E51EX-1015, MANUFACTURING AMOUNT 8 PIECES						
PART	PROFILE	MATERIAL	LENGTH [mm]	AREA [m2]	WEIGHT [kg]	PCS
E51EXL-1019	PL12X310	S355J2+N	375	0.25	11.0	1
TOTAL:				0.25	11.0	

Technical fabrication requirements:		Execution class
EXC2		
Requirements for fabrication, standard	Fabrication tolerances	
EN1090-2, table A.3 : EXC2	EN 1090-2, Appendix B	
Execution Specification document nr	Special fabrication tolerances	
25019443-ICC250-0600-0660-000005	Project specification/ shown on drwg.	
Surface preparation grade	Weld inspection, requirements	
ISO8501-3, grade P2	EN 1090-2,Table 24, U>0.5	
Surface treatment	Extent of NDT, filled welds	
ISO12944-5	MT-EN1290,20% of welds	
Additional requirements on surface treatment	Extent of NDT, butt welds	
C3.07, EPPUR 240/2	UT, EN-ISO17640, 20% of welds	
Shade	Extent of NDT for splices not shown on drawing	
RAL 7024 (Graphite Gray)	UT, EN-ISO17640, 100%of welds	
Welding of built up steel section	Requirements on holing	
Appendix 1 / Project spec.	EN1090-2 Section 6.6.3	
Welds, if not specified otherwise	Weld class	
EN 9692-1, EN 9692-2	C, EN ISO 5817	
Additional material inspection		Shown on drwg.

FIRE PROTECTION: SAME AS FOR E51V-1012

PROJECT NAME
Easpring New Materials Oy
FAIR Phase 1

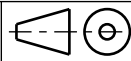


DRAWING CONTENT
ASSEMBLY DRAWING
PLATE
E51EX-1015



SWECO RAKENNETEKNIikka OY
ILMALANPORTTI 2
00240 HELSINKI
PUH. +358 207 393 000
www.sweco.fi

DATE	ARCHIVING CODE	PAGE	DESIGN GROUP
12.06.2026			STR
DRAWN	DESIGNER	APPROVED	CHECKED
Alexey Serous	Alexey Serous	Pertti Koivumaaanaho	Jere Kallosalmi
PROJECT NUMBER	DWG. NO.	REVISION	
25019443	E51EX-1015		

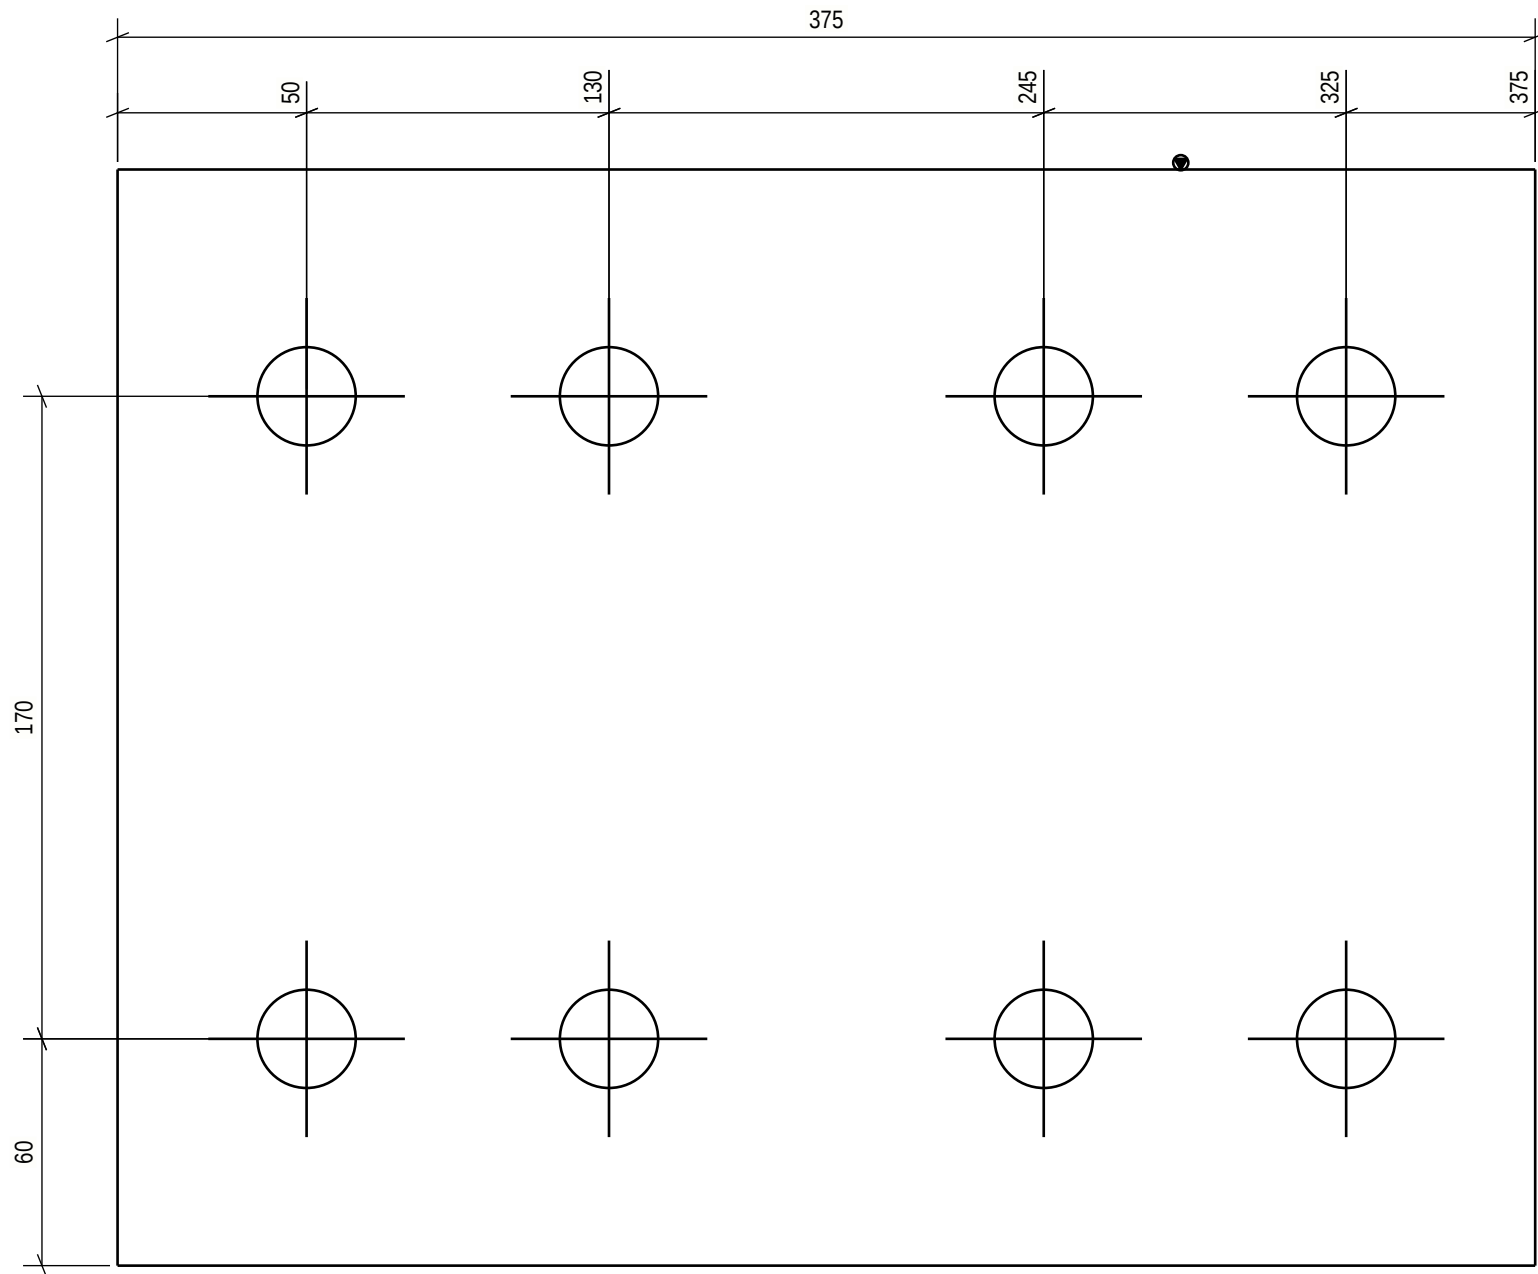


For special tolerances of bolt hole location
see specification for steel structures
Approved For Construction


PART LIST FOR ASSEMBLY E51EX-1016, MANUFACTURING AMOUNT 8 PIECES						
PART	PROFILE	MATERIAL	LENGTH [mm]	AREA [m2]	WEIGHT [kg]	PCS
E51EXL-1025	PL8X290	S355J2+N	375	0.23	6.8	1
TOTAL:				0.23	6.8	

Technical fabrication requirements:		Execution class
EXC2		
Requirements for fabrication, standard EN1090-2, table A.3 : EXC2	Fabrication tolerances EN 1090-2, Appendix B	
Execution Specification document nr 25019443-ICC250-0600-0660-000005	Special fabrication tolerances Project specification/ shown on drwg.	
Surface preparation grade ISO8501-3, grade P2	Weld inspection, requirements EN 1090-2,Table 24, U>0.5	
Surface treatment ISO12944-5	Extent of NDT, fillet welds MT-EN1290,20% of welds	
Additional requirements on surface treatment C3.07, EPPUR 240/2	Extent of NDT, butt welds UT, EN-ISO17640, 20% of welds	
Shade RAL 7024 (Graphite Gray)	Extent of NDT for splices not shown on drawing UT, EN-ISO17640, 100%of welds	
Welding of built up steel section Appendix 1 / Project spec.	Requirements on holing EN1090-2 Section 6.6.3	
Welds, if not specified otherwise EN 9692-1, EN 9692-2	Weld class C, EN ISO 5817	Additional material inspection Shown on drwg.

FIRE PROTECTION: SAME AS FOR E51V-1012

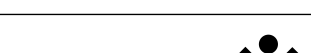PROJECT NAME Easpring New Materials Oy FAIR Phase 1				DRAWING CONTENT ASSEMBLY DRAWING PLATE E51EX-1016			
 Sustainable engineering and design		SWECO RAKENNETEKNIikka OY ILMALANPORTTI 2 00240 HELSINKI		DATE 12.06.2026	ARCHIVING CODE	PAGE	DESIGN GROUP STR
		PUH. +358 207 393 000 www.sweco.fi		DRAWN Alexey Serous	DESIGNER Alexey Serous	APPROVED Pertti Koivumaaanaho	CHECKED Jere Kallosalmi
				PROJECT NUMBER 25019443	DWG. NO. E51EX-1016		REVISION


PART LIST FOR ASSEMBLY E51EX-1020, MANUFACTURING AMOUNT 12 PIECES						
PART	PROFILE	MATERIAL	LENGTH [mm]	AREA [m2]	WEIGHT [kg]	PCS
E51EXL-1032	PL8X360	S355J2+N	160	0.12	3.6	1
TOTAL:				0.12	3.6	

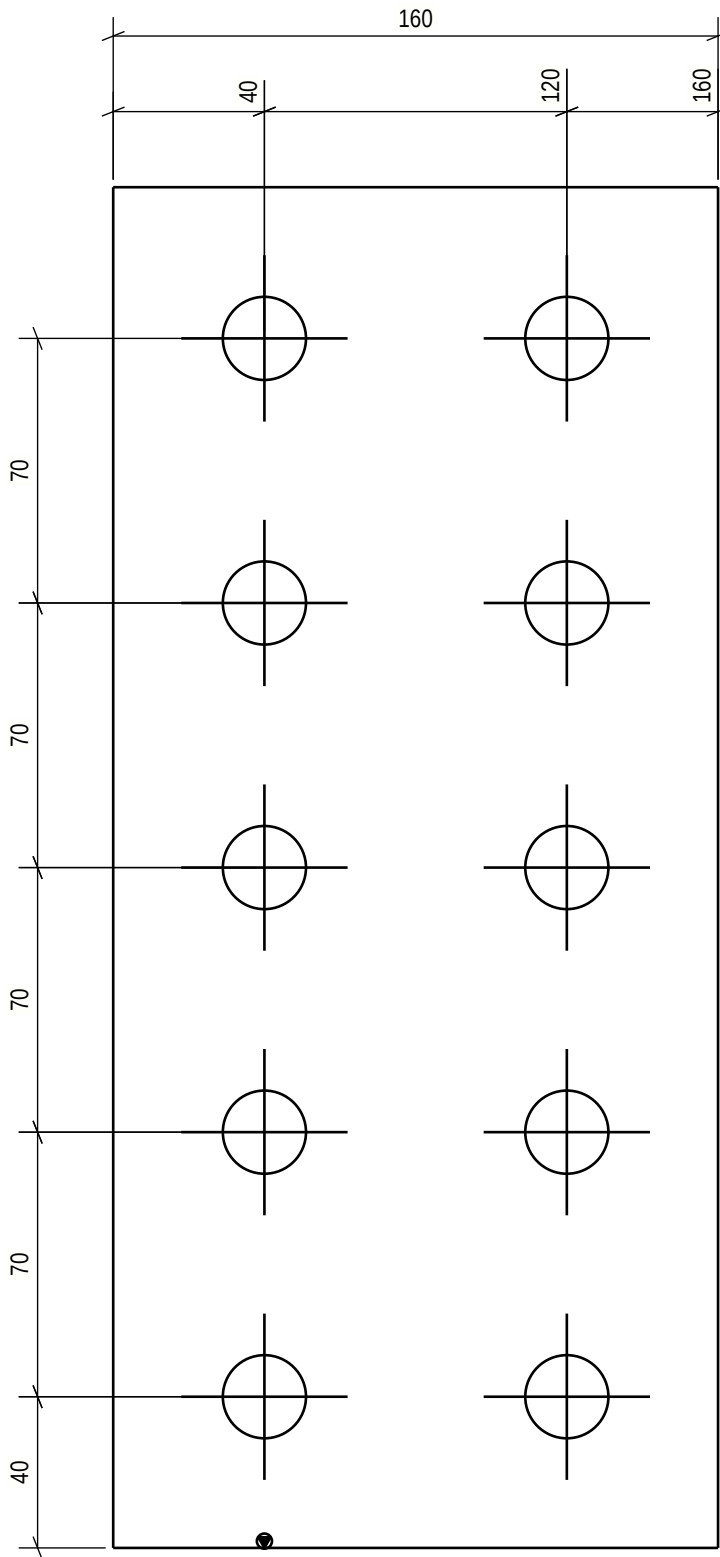


For special tolerances of bolt hole location
see specification for steel structures
Approved For Construction

Technical fabrication requirements:		Execution class
Requirements for fabrication, standard EN1090-2, table A.3 : EXC2		EXC2
Execution Specification document nr 25019443-ICC250-0600-0660-000005	Fabrication tolerances EN 1090-2, Appendix B Special fabrication tolerances Project specification/ shown on drwg.	
Surface preparation grade ISO8501-3, grade P2	Weld inspection, requirements EN 1090-2,Table 24, U>0.5	
Surface treatment ISO12944-5	Extent of NDT, fillet welds MT-EN1290,20% of welds	
Additional requirements on surface treatment C3.07, EPPUR 240/2	Extent of NDT, butt welds UT, EN-ISO17640, 20% of welds	
Shade RAL 7024 (Graphite Gray)	Extent of NDT for splices not shown on drawing UT, EN-ISO17640, 100%of welds	
Welding of built up steel section Appendix 1 / Project spec.	Requirements on holing EN1090-2 Section 6.6.3	
Welds, if not specified otherwise EN 9692-1, EN 9692-2	Weld class C, EN ISO 5817	Additional material inspection Shown on drwg.

FIRE PROTECTION SAME AS FOR E51WC-1031

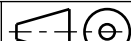PROJECT NAME Easpring New Materials Oy FAIR Phase 1				DRAWING CONTENT ASSEMBLY DRAWING PLATE E51EX-1020					
		DATE 12.06.2026		ARCHIVING CODE		PAGE		DESIGN GROUP STR	
		DRAWN Alexey Serous		DESIGNER Alexey Serous		APPROVED Pertti Koivumaaaho		CHECKED Jere Kalliosalmi	
		PROJECT NUMBER 25019443		DWG. NO. E51EX-1020		REVISION			
SWECO RAKENNETEKNIikka OY ILMALANPORTTI 2 00240 HELSINKI PUH. +358 207 393 000 www.sweco.fi									

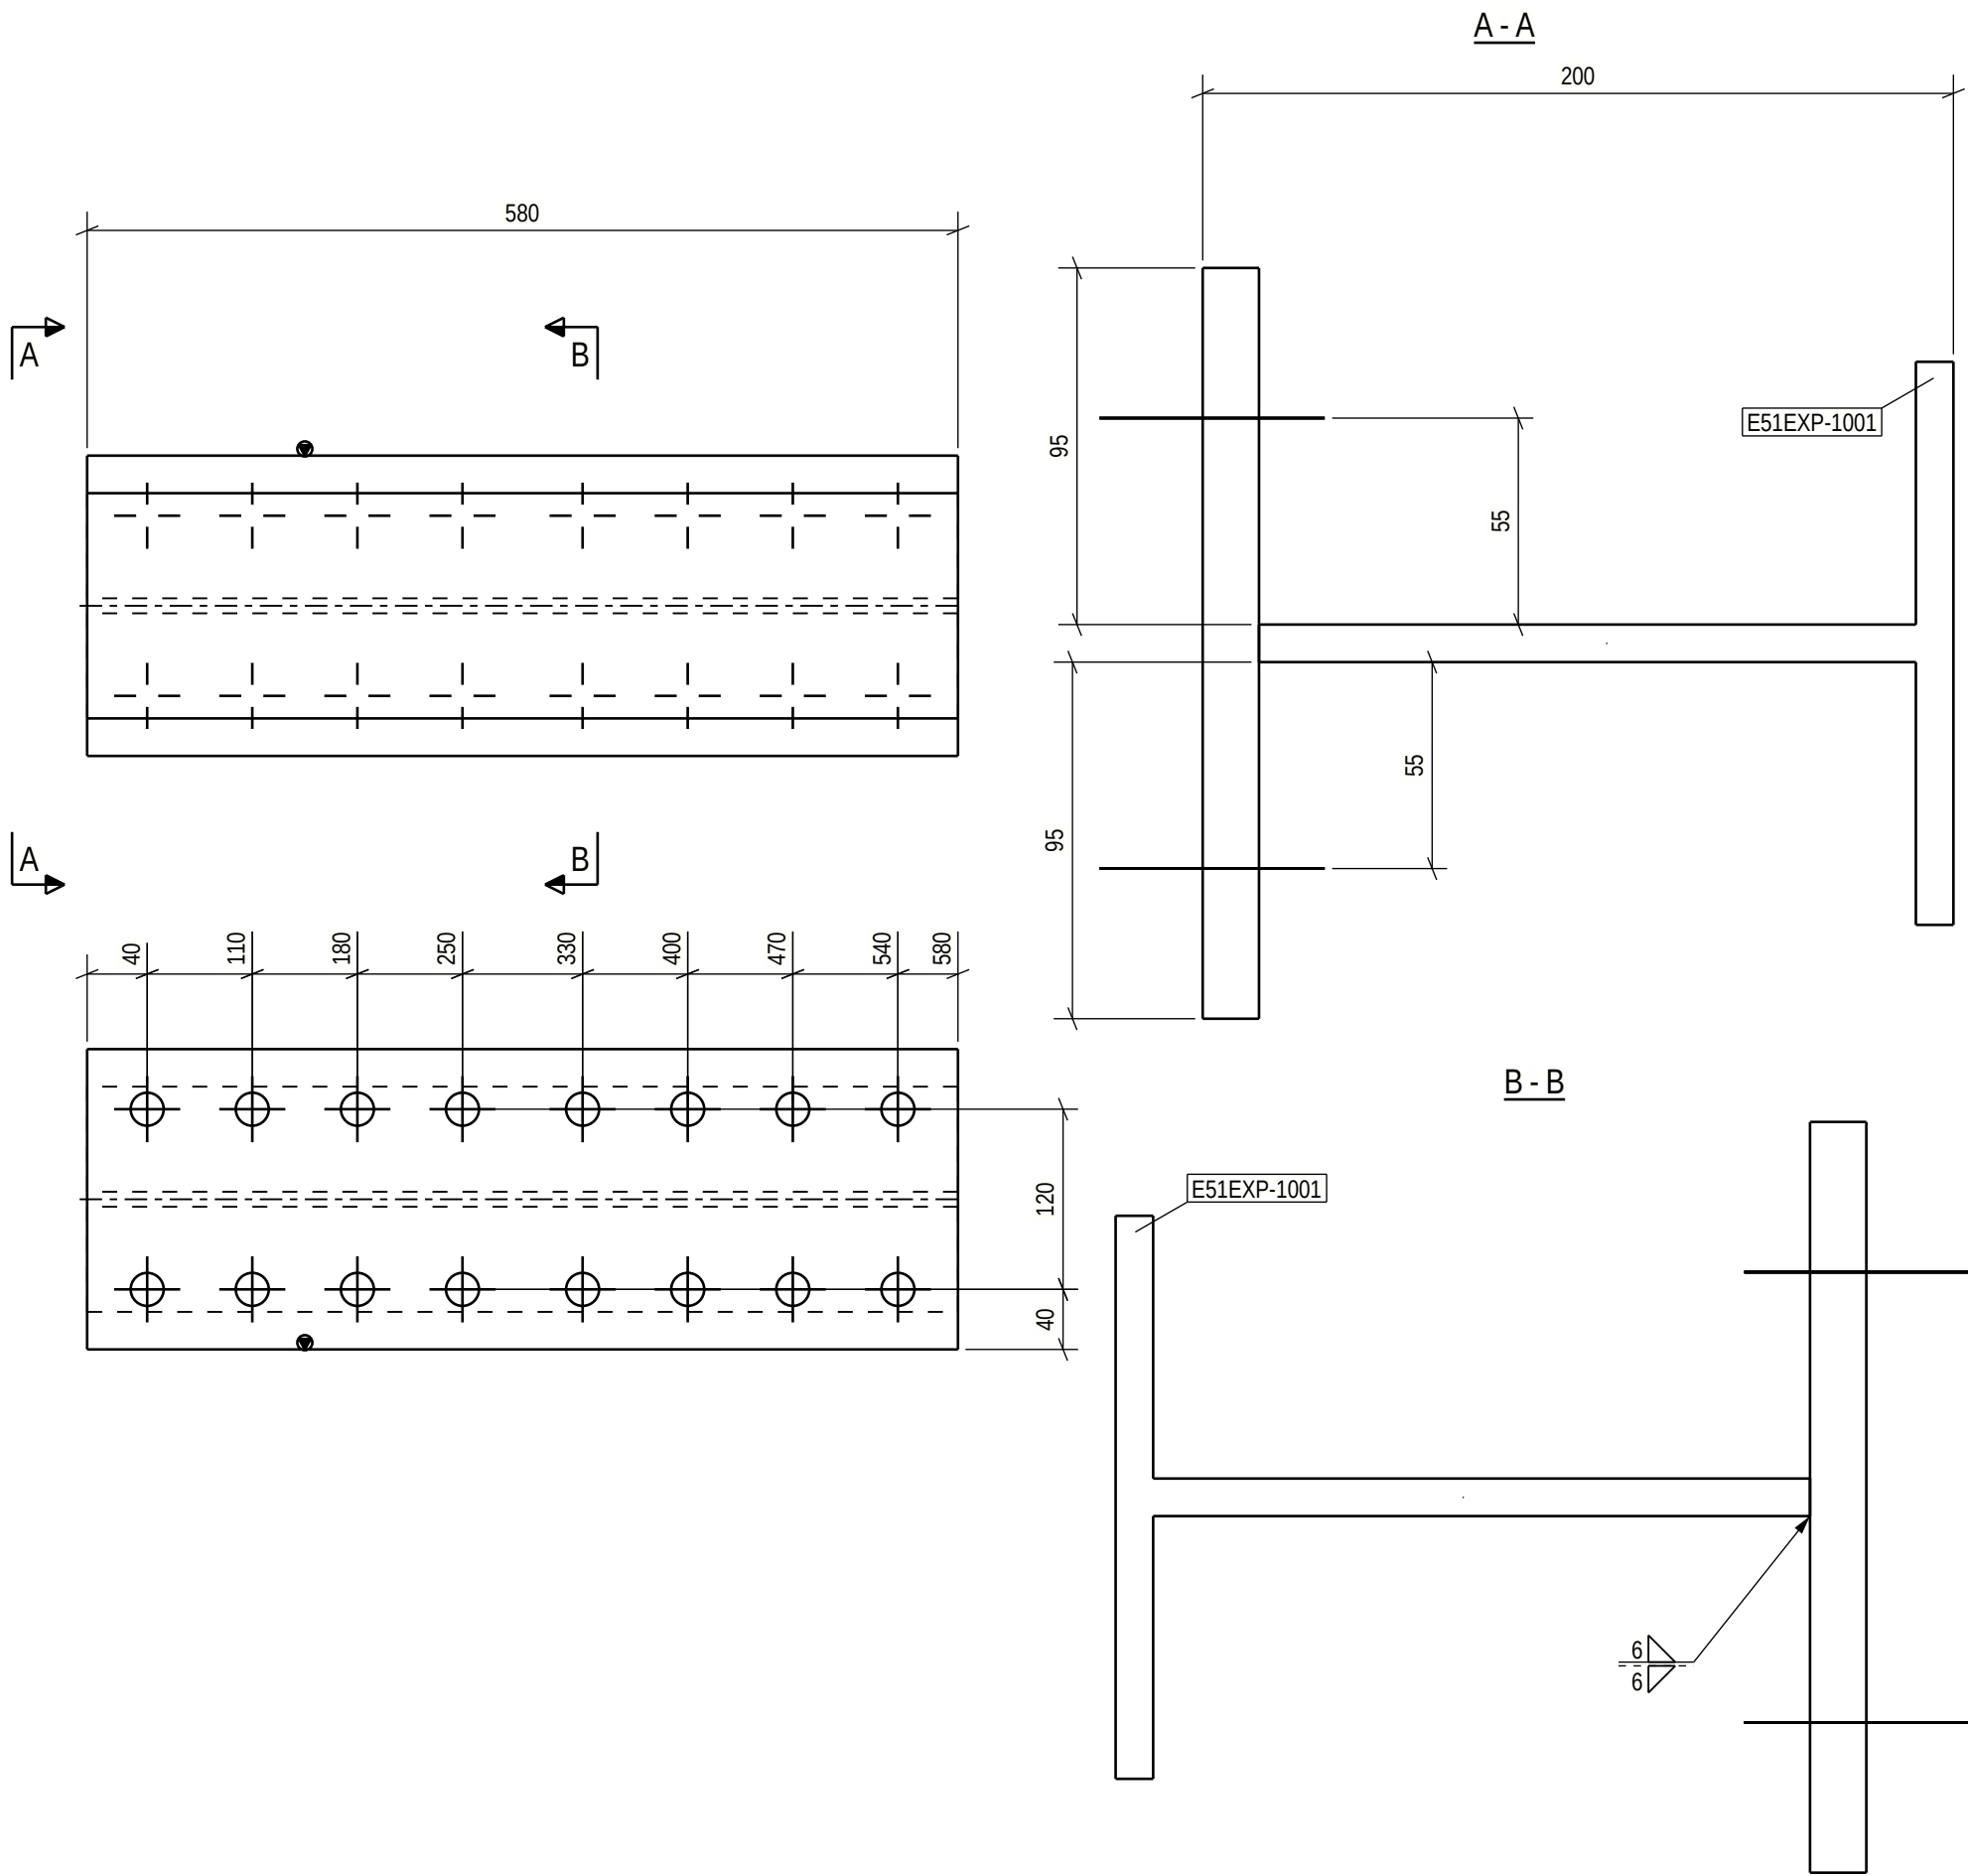


For special tolerances of bolt hole location
see specification for steel structures
Approved For Construction

PART LIST FOR ASSEMBLY E51EX-1021, MANUFACTURING AMOUNT 10 PIECES						
PART	PROFILE	MATERIAL	LENGTH [mm]	AREA [m2]	WEIGHT [kg]	PCS
E51EXL-1033	PL15X200	S355J2+N	580	0.26	13.7	1
E51EXP-1001	T185-10-10-150	S355J2+N	580	0.40	14.9	1
TOTAL:				0.65	28.6	

Technical fabrication requirements:		Execution class
Requirements for fabrication, standard EN1090-2, table A.3 : EXC2		EXC2
Execution Specification document nr 25019443-ICC250-0600-0660-000005	Fabrication tolerances EN 1090-2, Appendix B Special fabrication tolerances Project specification/ shown on drwg.	
Surface preparation grade ISO8501-3, grade P2	Weld inspection, requirements EN 1090-2,Table 24, U>0.5	
Surface treatment ISO12944-5	Extent of NDT, fillet welds MT-EN1290,20% of welds	
Additional requirements on surface treatment C3.07, EPPUR 240/2	Extent of NDT, butt welds UT, EN-ISO17640, 20% of welds	
Shade RAL 7024 (Graphite Gray)	Extent of NDT for splices not shown on drawing UT, EN-ISO17640, 100%of welds	
Welding of built up steel section Appendix 1 / Project spec.	Requirements on holing EN1090-2 Section 6.6.3	
Welds, if not specified otherwise EN 9692-1, EN 9692-2	Weld class C, EN ISO 5817	Additional material inspection Shown on drwg.

FIRE PROTECTION SAME AS FOR E51WC-1031

PROJECT NAME
Easpring New Materials Oy
FAIR Phase 1

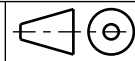


DRAWING CONTENT
ASSEMBLY DRAWING
PLATE
E51EX-1021



SWECO RAKENNETEKNIikka OY
ILMALANPORTTI 2
00240 HELSINKI
PUH. +358 207 393 000
www.sweco.fi

DATE	ARCHIVING CODE	PAGE	DESIGN GROUP
12.06.2026			STR
DRAWN	DESIGNER	APPROVED	CHECKED
Alexey Serous	Alexey Serous	Pertti Koivumaaanaho	Jere Kallosalmi
PROJECT NUMBER	DWG. NO.	REVISION	
25019443	E51EX-1021		

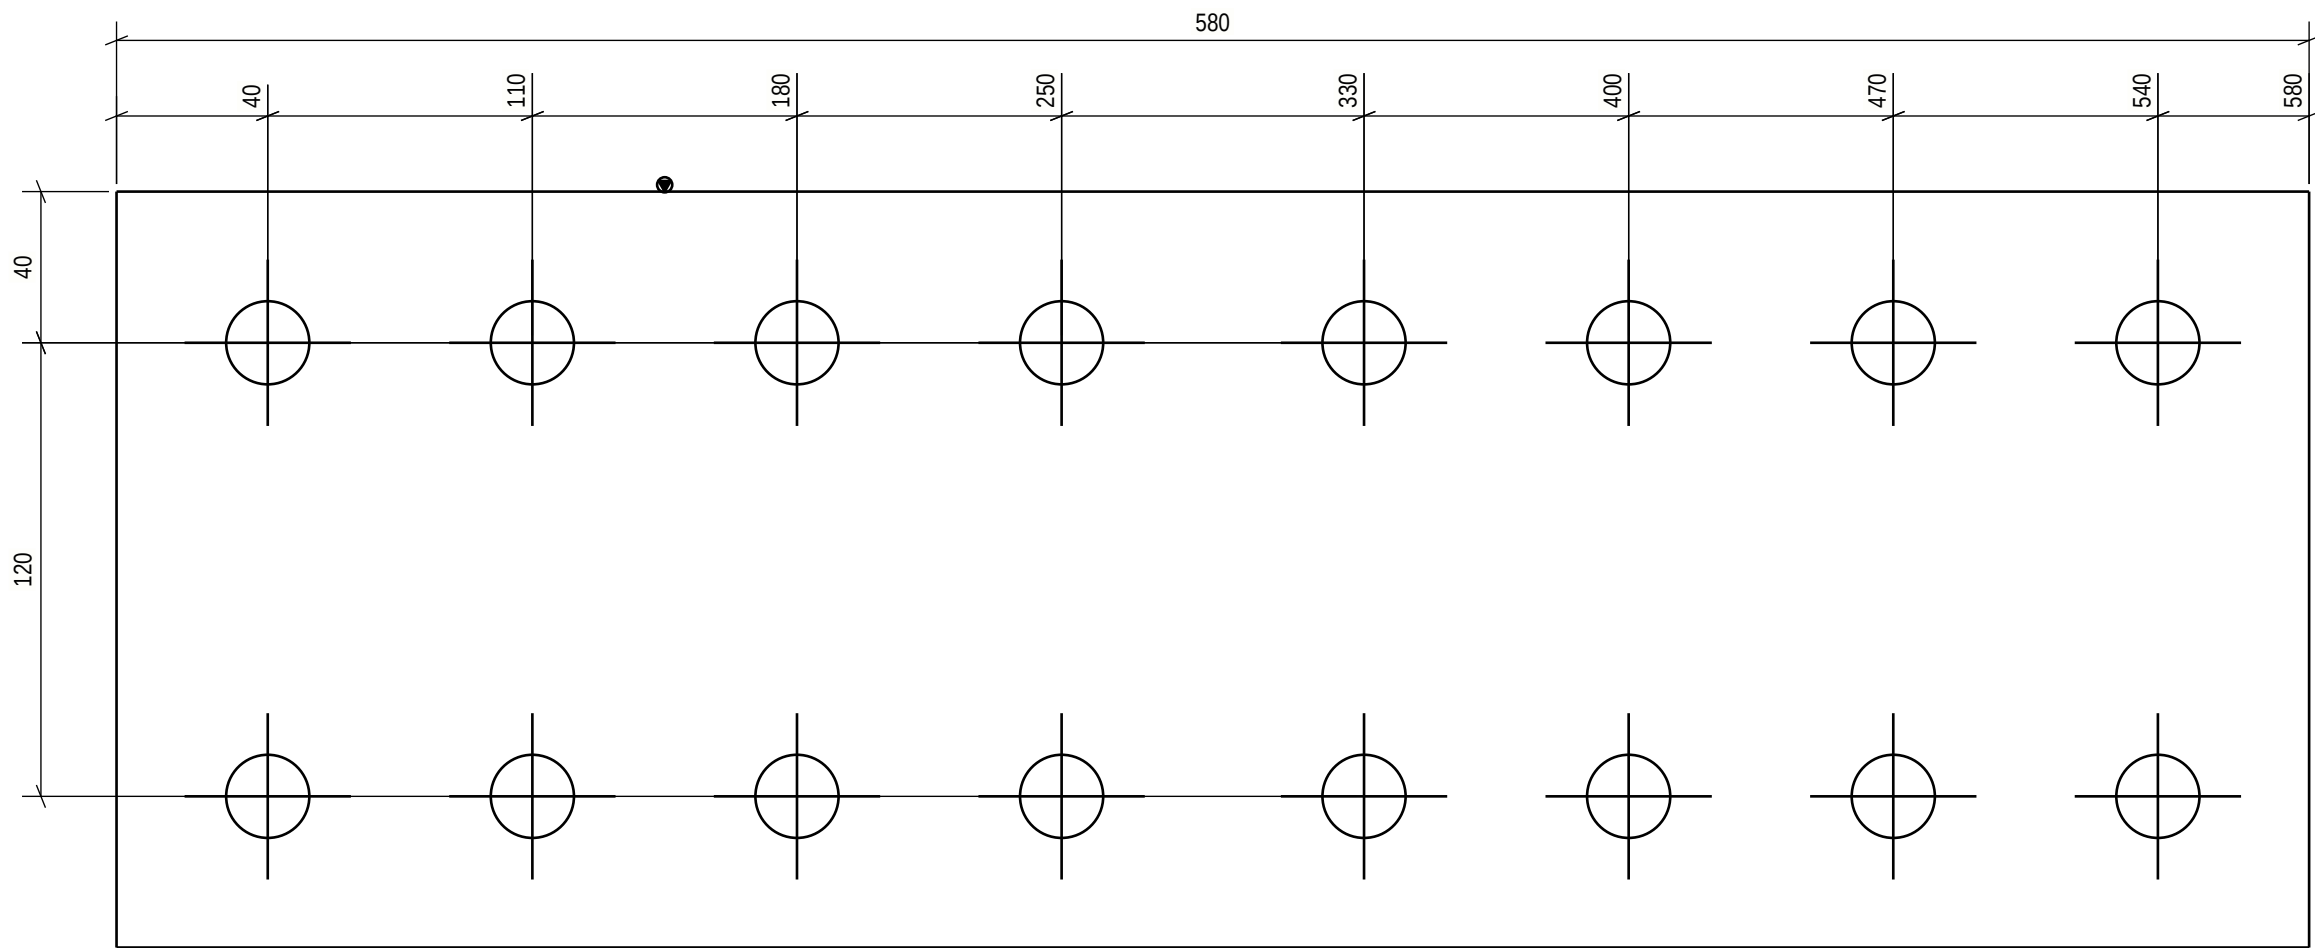


For special tolerances of bolt hole location
see specification for steel structures
Approved For Construction

PART LIST FOR ASSEMBLY E51EX-1022, MANUFACTURING AMOUNT 6 PIECES						
PART	PROFILE	MATERIAL	LENGTH [mm]	AREA [m2]	WEIGHT [kg]	PCS
E51EXL-1033	PL15X200	S355J2+N	580	0.26	13.7	1
TOTAL:				0.26	13.7	

Technical fabrication requirements:		Execution class
EXC2		
Requirements for fabrication, standard	Fabrication tolerances	
EN1090-2, table A.3 : EXC2	EN 1090-2, Appendix B	
Execution Specification document nr	Special fabrication tolerances	
25019443-ICC250-0600-0660-000005	Project specification/ shown on drwg.	
Surface preparation grade	Weld inspection, requirements	
ISO8501-3, grade P2	EN 1090-2,Table 24, U>0.5	
Surface treatment	Extent of NDT, fillet welds	
ISO12944-5	MT-EN1290,20% of welds	
Additional requirements on surface treatment	Extent of NDT, butt welds	
C3.07, EPPUR 240/2	UT, EN-ISO17640, 20% of welds	
Shade	Extent of NDT for splices not shown on drawing	
RAL 7024 (Graphite Gray)	UT, EN-ISO17640, 100%of welds	
Welding of built up steel section	Requirements on holing	
Appendix 1 / Project spec.	EN1090-2 Section 6.6.3	
Welds, if not specified otherwise	Weld class	Additional material inspection
EN 9692-1, EN 9692-2	C, EN ISO 5817	Shown on drwg.

FIRE PROTECTION SAME AS FOR E51WC-1031

PROJECT NAME
Easpring New Materials Oy
FAIR Phase 1

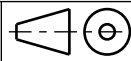

DRAWING CONTENT
ASSEMBLY DRAWING
PLATE
E51EX-1022



SWECO RAKENNETEKNIikka OY
ILMALANPORTTI 2
00240 HELSINKI
PUH. +358 207 393 000
www.sweco.fi

DATE	ARCHIVING CODE	PAGE	DESIGN GROUP
12.06.2026			STR
DRAWN	DESIGNER	APPROVED	CHECKED
Alexey Serous	Alexey Serous	Pertti Koivumaaanaho	Jere Kallosalmi
PROJECT NUMBER	DWG. NO.	REVISION	
25019443	E51EX-1022		


PART LIST FOR ASSEMBLY E51EX-1024, MANUFACTURING AMOUNT 16 PIECES						
PART	PROFILE	MATERIAL	LENGTH [mm]	AREA [m ²]	WEIGHT [kg]	PCS
E51EXL-1027	PL2X220	S355J2+N	435	0.16	1.2	1
			TOTAL:	0.16	1.2	

		Execution class	
Technical fabrication requirements:		EXC2	
Requirements for fabrication, standard EN1090-2, table A.3 : EXC2 Execution Specification document nr. 25019443-ICC250-0600-0660-000005 Surface preparation grade ISO8501-3, grade P2 Surface treatment ISO12944-5 Additional requirements on surface treatment C3.07, EPPUR 240/2 Shade RAL 7024 (Graphite Gray) Welding of built up steel section Appendix 1 / Project spec. Welds, if not specified otherwise EN 9692-1, EN 9692-2		Fabrication tolerances EN 1090-2, Appendix B Special fabrication tolerances Project specification/ shown on drwg. Weld inspection, requirements EN 1090-2, Table 24, U>0.5 Extent of NDT, fillet welds MT-EN1290, 20% of welds Extent of NDT, butt welds UT, EN-ISO17640, 20% of welds Extent of NDT for splices not shown on drawing UT-EN-ISO17640, 100% of welds Requirements on holding EN1090-2 Section 6.6.3 Weld class EN ISO 5817	
Additional material inspection Shown on drwg.			

PROJECT NAME Easpring New Materials Oy FAIR Phase 1				DRAWING CONTENT ASSEMBLY DRAWING PLATE E51EX-1024	
		SWECO RAKENNETEKNIikka OY ILMALANPORTTI 2 00240 HELSINKI PUH. +358 207 393 000 www.sweco.fi		DATE 12.06.2026	ARCHIVING CODE
		DRAWN Alexey Serous	DESIGNER Alexey Serous	APPROVED Pertti Koivumaaanaho	DESIGN GROUP STR CHECKED Jere Kalliosaalmi
		PROJECT NUMBER 25019443	DWG. NO. E51EX-1024		
		REVISION			

For special tolerances of bolt hole location
see specification for steel structures

Approved For Construction

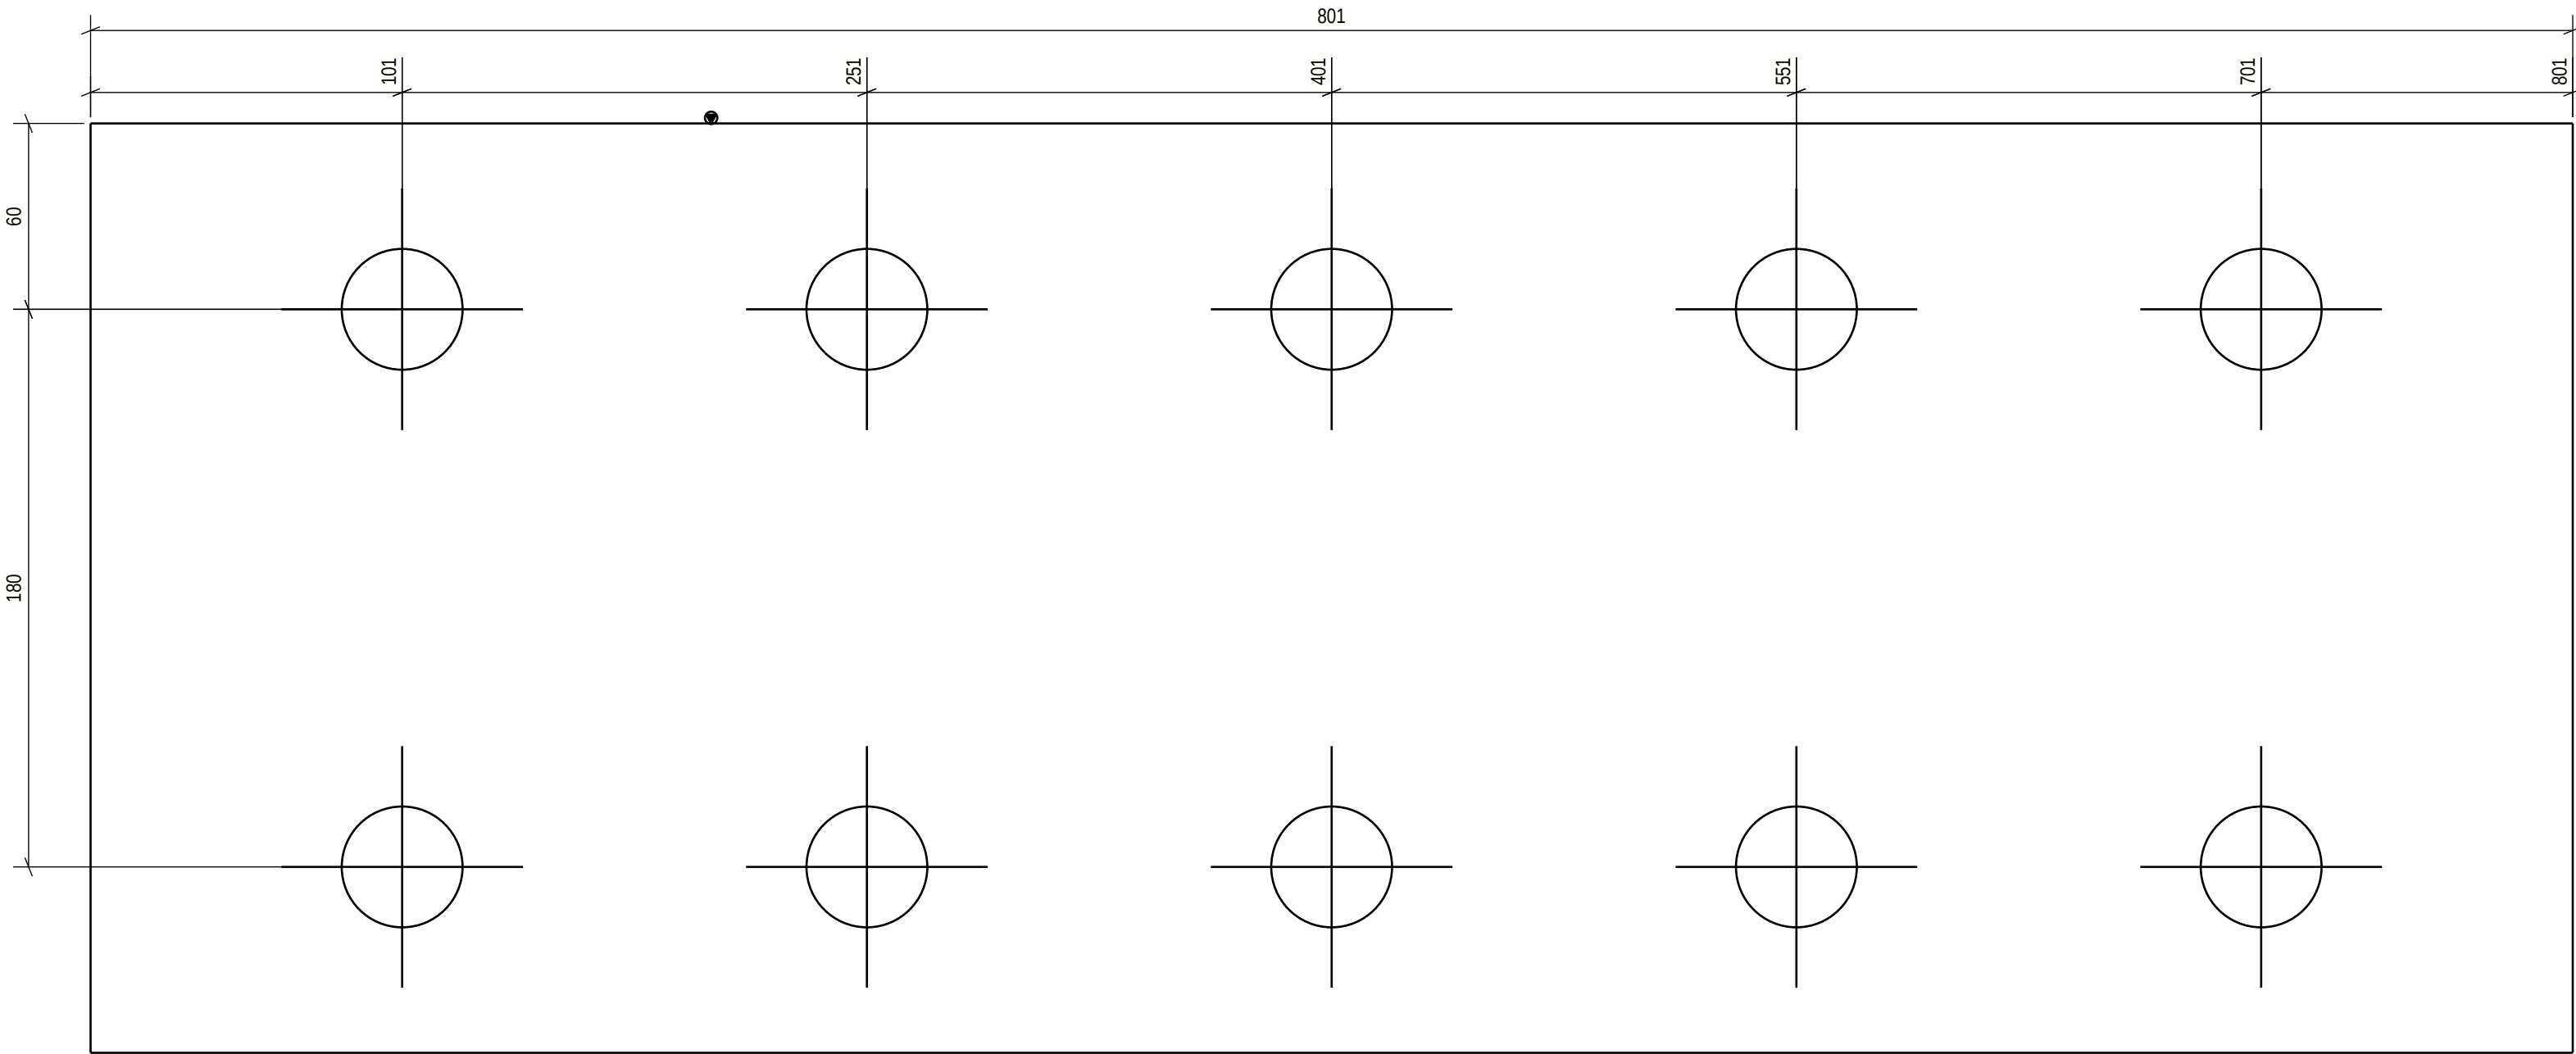


For special tolerances of bolt hole location
see specification for steel structures
Approved For Construction

PART LIST FOR ASSEMBLY E51EX-1027, MANUFACTURING AMOUNT 8 PIECES						
PART	PROFILE	MATERIAL	LENGTH [mm]	AREA [m2]	WEIGHT [kg]	PCS
E51EXL-1003	PL5X300	S355J2+N	801	0.49	9.4	1
TOTAL:				0.49	9.4	

Technical fabrication requirements:		Execution class
EXC2		
Requirements for fabrication, standard	Fabrication tolerances	
EN1090-2, table A.3 : EXC2	EN 1090-2, Appendix B	
Execution Specification document nr	Special fabrication tolerances	
25019443-ICC250-0600-0660-000005	Project specification/ shown on drwg.	
Surface preparation grade	Weld inspection, requirements	
ISO8501-3, grade P2	EN 1090-2,Table 24, U>0.5	
Surface treatment	Extent of NDT, fillet welds	
ISO12944-5	MT-EN1290,20% of welds	
Additional requirements on surface treatment	Extent of NDT, butt welds	
C3.07, EPPUR 240/2	UT, EN-ISO17640, 20% of welds	
Shade	Extent of NDT for splices not shown on drawing	
RAL 7024 (Graphite Gray)	UT, EN-ISO17640, 100%of welds	
Welding of built up steel section	Requirements on holing	
Appendix 1 / Project spec.	EN1090-2 Section 6.6.3	
Welds, if not specified otherwise	Weld class	Additional material inspection
EN 9692-1, EN 9692-2	C, EN ISO 5817	Shown on drwg.

FIRE PROTECTION SAME AS FOR E51WC-1031

PROJECT NAME
Easpring New Materials Oy
FAIR Phase 1

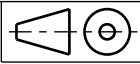


DRAWING CONTENT
ASSEMBLY DRAWING
PLATE
E51EX-1027



SWECO RAKENNETEKNIikka OY
ILMALANPORTTI 2
00240 HELSINKI
PUH. +358 207 393 000
www.sweco.fi

DATE	ARCHIVING CODE	PAGE	DESIGN GROUP
12.06.2026			STR
DRAWN	DESIGNER	APPROVED	CHECKED
Alexey Serous	Alexey Serous	Pertti Koivumaaanaho	Jere Kalilosalmi
PROJECT NUMBER	DWG. NO.	REVISION	
25019443	E51EX-1027		

PART LIST FOR ASSEMBLY E51EX-1028, MANUFACTURING AMOUNT 6 PIECES						
PART	PROFILE	MATERIAL	LENGTH [mm]	AREA [m2]	WEIGHT [kg]	PCS
E51EXL-1002	PL2X200	S355J2+N	260	0.09	0.7	1
TOTAL:				0.09	0.7	

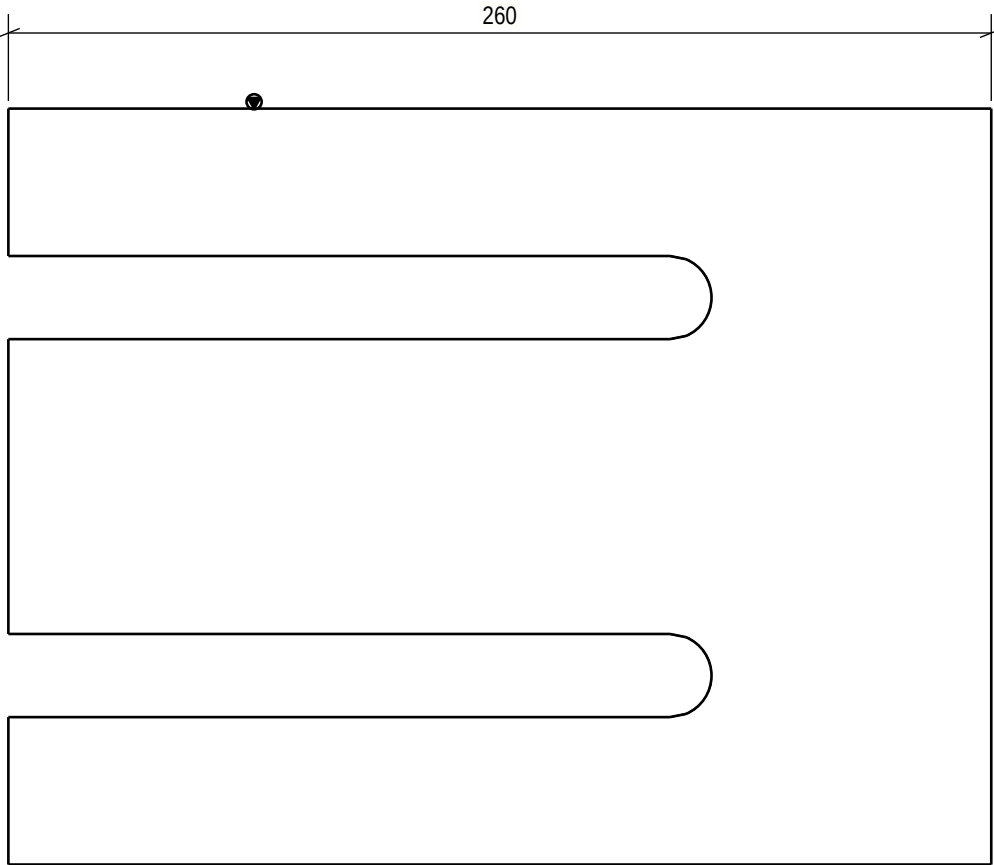

For special tolerances of bolt hole location
see specification for steel structures
Approved For Construction


Technical fabrication requirements:		Execution class	
		EXC2	
Requirements for fabrication, standard		Fabrication tolerances	
EN1090-2, table A.3 : EXC2		EN 1090-2, Appendix B	
Execution Specification document nr		Special fabrication tolerances	
25019443-ICC250-0600-0660-000005		Project specification/ shown on drwg.	
Surface preparation grade		Weld inspection, requirements	
ISO8501-3, grade P2		EN 1090-2,Table 24, U>0.5	
Surface treatment		Extent of NDT, fillet welds	
ISO12944-5		MT-EN1290,20% of welds	
Additional requirements on surface treatment		Extent of NDT, butt welds	
C3.07, EPPUR 240/2		UT, EN-ISO17640, 20% of welds	
Shade		Extent of NDT for splices not shown on drawing	
RAL 7024 (Graphite Gray)		UT, EN-ISO17640, 100%of welds	
Welding of built up steel section		Requirements on holing	
Appendix 1 / Project spec.		EN1090-2 Section 6.6.3	
Welds, if not specified otherwise		Weld class	
EN 9692-1, EN 9692-2		C, EN ISO 5817	
		Additional material inspection	
		Shown on drwg.	

Approved For Construction

PROJECT NAME				DRAWING CONTENT	
Easpring New Materials Oy		FAIR Phase 1		ASSEMBLY DRAWING	
				PLATE	
				E51EX-1028	

 Sustainable engineering and design	SWECO RAKENNETEKNIikka OY ILMALANPORTTI 2 00240 HELSINKI PUH. +358 207 393 000 www.sweco.fi	DATE	ARCHIVING CODE	PAGE	DESIGN GROUP		
		12.06.2026			STR		
		DRAWN	DESIGNER	APPROVED	CHECKED		
		Alexey Serous	Alexey Serous	Pertti Koivumaaanaho	Jere Kallosalmi		
		PROJECT NUMBER		DWG. NO.		REVISION	
		25019443		E51EX-1028			

PART LIST FOR ASSEMBLY E51EX-1029, MANUFACTURING AMOUNT 6 PIECES						
PART	PROFILE	MATERIAL	LENGTH [mm]	AREA [m2]	WEIGHT [kg]	PCS
E51EXL-1001	PL2X180	S355J2+N	240	0.07	0.5	1
TOTAL:				0.07	0.5	

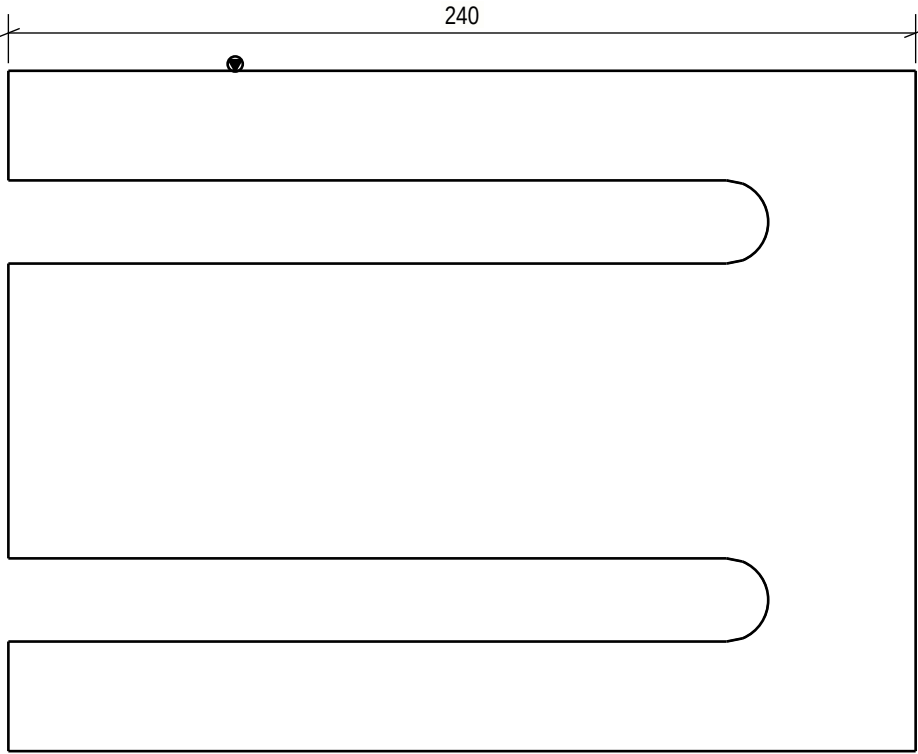

For special tolerances of bolt hole location
see specification for steel structures
Approved For Construction

Technical fabrication requirements:		Execution class EXC2	
Requirements for fabrication, standard EN1090-2, table A.3 : EXC2		Fabrication tolerances EN 1090-2, Appendix B	
Execution Specification document nr 25019443-ICC250-0600-0660-000005		Special fabrication tolerances Project specification/ shown on drwg.	
Surface preparation grade ISO8501-3, grade P2		Weld inspection, requirements EN 1090-2, Table 24, U>0.5	
Surface treatment ISO12944-5		Extent of NDT, fillet welds MT-EN1290, 20% of welds	
Additional requirements on surface treatment C3.07, EPPUR 240/2		Extent of NDT, butt welds UT, EN-ISO17640, 20% of welds	
Shade RAL 7024 (Graphite Gray)		Extent of NDT for splices not shown on drawing UT, EN-ISO17640, 100% of welds	
Welding of built up steel section Appendix 1 / Project spec.		Requirements on holing EN1090-2 Section 6.6.3	
Welds, if not specified otherwise EN 9692-1, EN 9692-2		Weld class C, EN ISO 5817	
		Additional material inspection Shown on drwg.	

01	Quantity decreased	FIALES	18.06.2026	FIKJER
REV.	REVISION	CHANGED BY	DATE	CHECKED BY

PROJECT NAME

Easpring New Materials Oy

FAIR Phase 1

DRAWING CONTENT


ASSEMBLY DRAWING

PLATE

E51EX-1029

	SWECO RAKENNETEKNIikka OY ILMALANPORTTI 2 00240 HELSINKI PUH. +358 207 393 000 www.sweco.fi	DATE 12.06.2026	ARCHIVING CODE	PAGE	DESIGN GROUP STR
		DRAWN Alexey Serous	DESIGNER Alexey Serous	APPROVED Pertti Koivumaaanaho	CHECKED Jere Kallosalmi
		PROJECT NUMBER 25019443	REVISION E51EX-1029 01		

25019443_Fair_E500

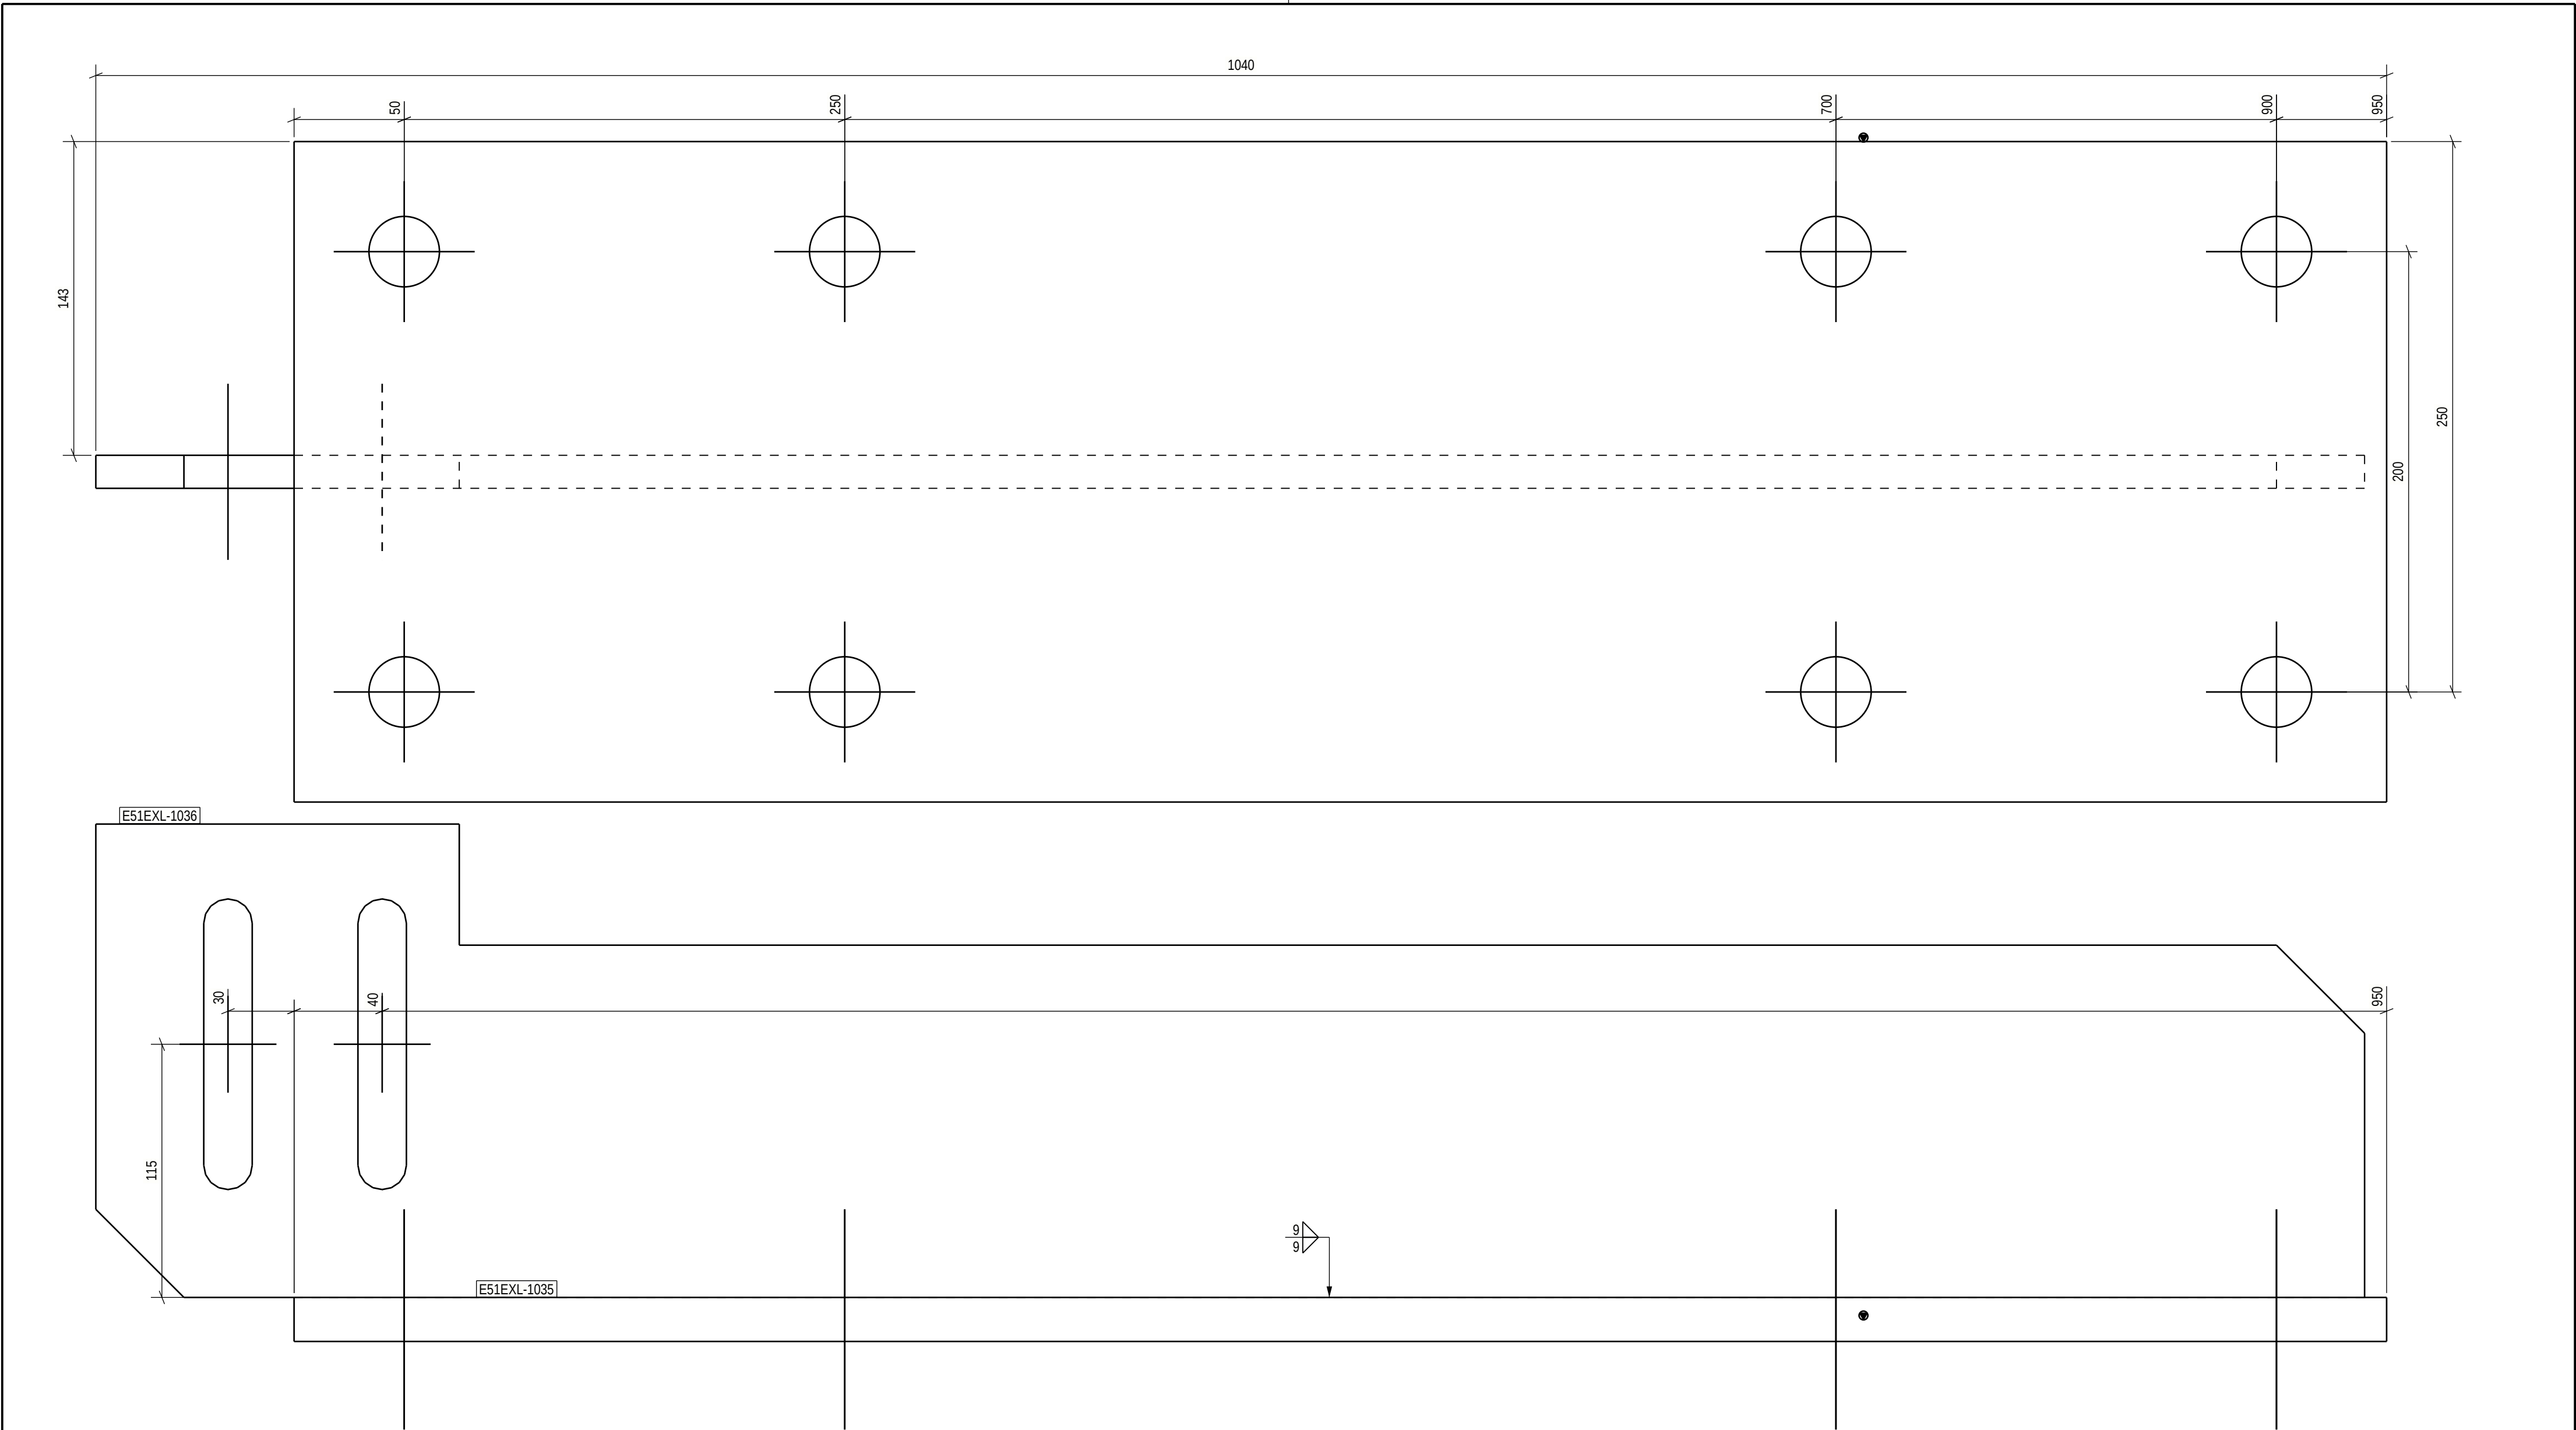

PART LIST FOR ASSEMBLY E51EX-1033, MANUFACTURING AMOUNT 1 PIECES						
PART	PROFILE	MATERIAL	LENGTH [mm]	AREA [m2]	WEIGHT [kg]	PCS
E51EXL-1035	PL20X300	S355J2+N	950	0.62	44.7	1
E51EXL-1036	PL15X215	S355J2+N	1030	0.38	20.3	1
TOTAL:				1.00	65.0	

Technical fabrication requirements:

Execution class

EXC2

Requirements for fabrication, standard
EN1090-2, table A.3 : EXC2

Execution Specification document nr
25019443-ICC250-0600-0660-000005

Surface preparation grade
ISO8501-3, grade P2

Surface treatment
ISO12944-5

Additional requirements on surface treatment
C3.07, EPPUR 240/2

Shade
RAL 7024 (Graphite Gray)

Welding of built up steel section
Appendix 1 / Project spec.

Welds, if not specified otherwise
EN 9692-1, EN 9692-2

Fabrication tolerances
EN 1090-2, Appendix B

Special fabrication tolerances
Project specification/ shown on drwg.

Weld inspection, requirements
EN 1090-2,Table 24, U>0.5

Extent of NDT, filled welds
MT-EN1290,20% of welds

Extent of NDT for splices not shown on drawing
UT, EN-ISO17640, 100%of welds

Requirements on holing
EN1090-2 Section 6.6.3

Weld class
C, EN ISO 5817

Additional material inspection
Shown on drwg.

PROJECT NAME
Easpring New Materials Oy
FAIR Phase 1




SWECO RAKENNETEKNIikka OY
ILMALANPORTTI 2
00240 HELSINKI
PUH. +358 207 393 000
www.sweco.fi

DRAWING CONTENT
ASSEMBLY DRAWING
PLATE
E51EX-1033

DATE 12.06.2026	ARCHIVING CODE	PAGE	DESIGN GROUP STR
DRAWN Alexey Serous	DESIGNER Alexey Serous	APPROVED Pertti Koivumaaanaho	CHECKED Jere Kalilosalmi
PROJECT NUMBER 25019443	REVISION E51EX-1033		

For special tolerances of bolt hole location
see specification for steel structures
Approved For Construction

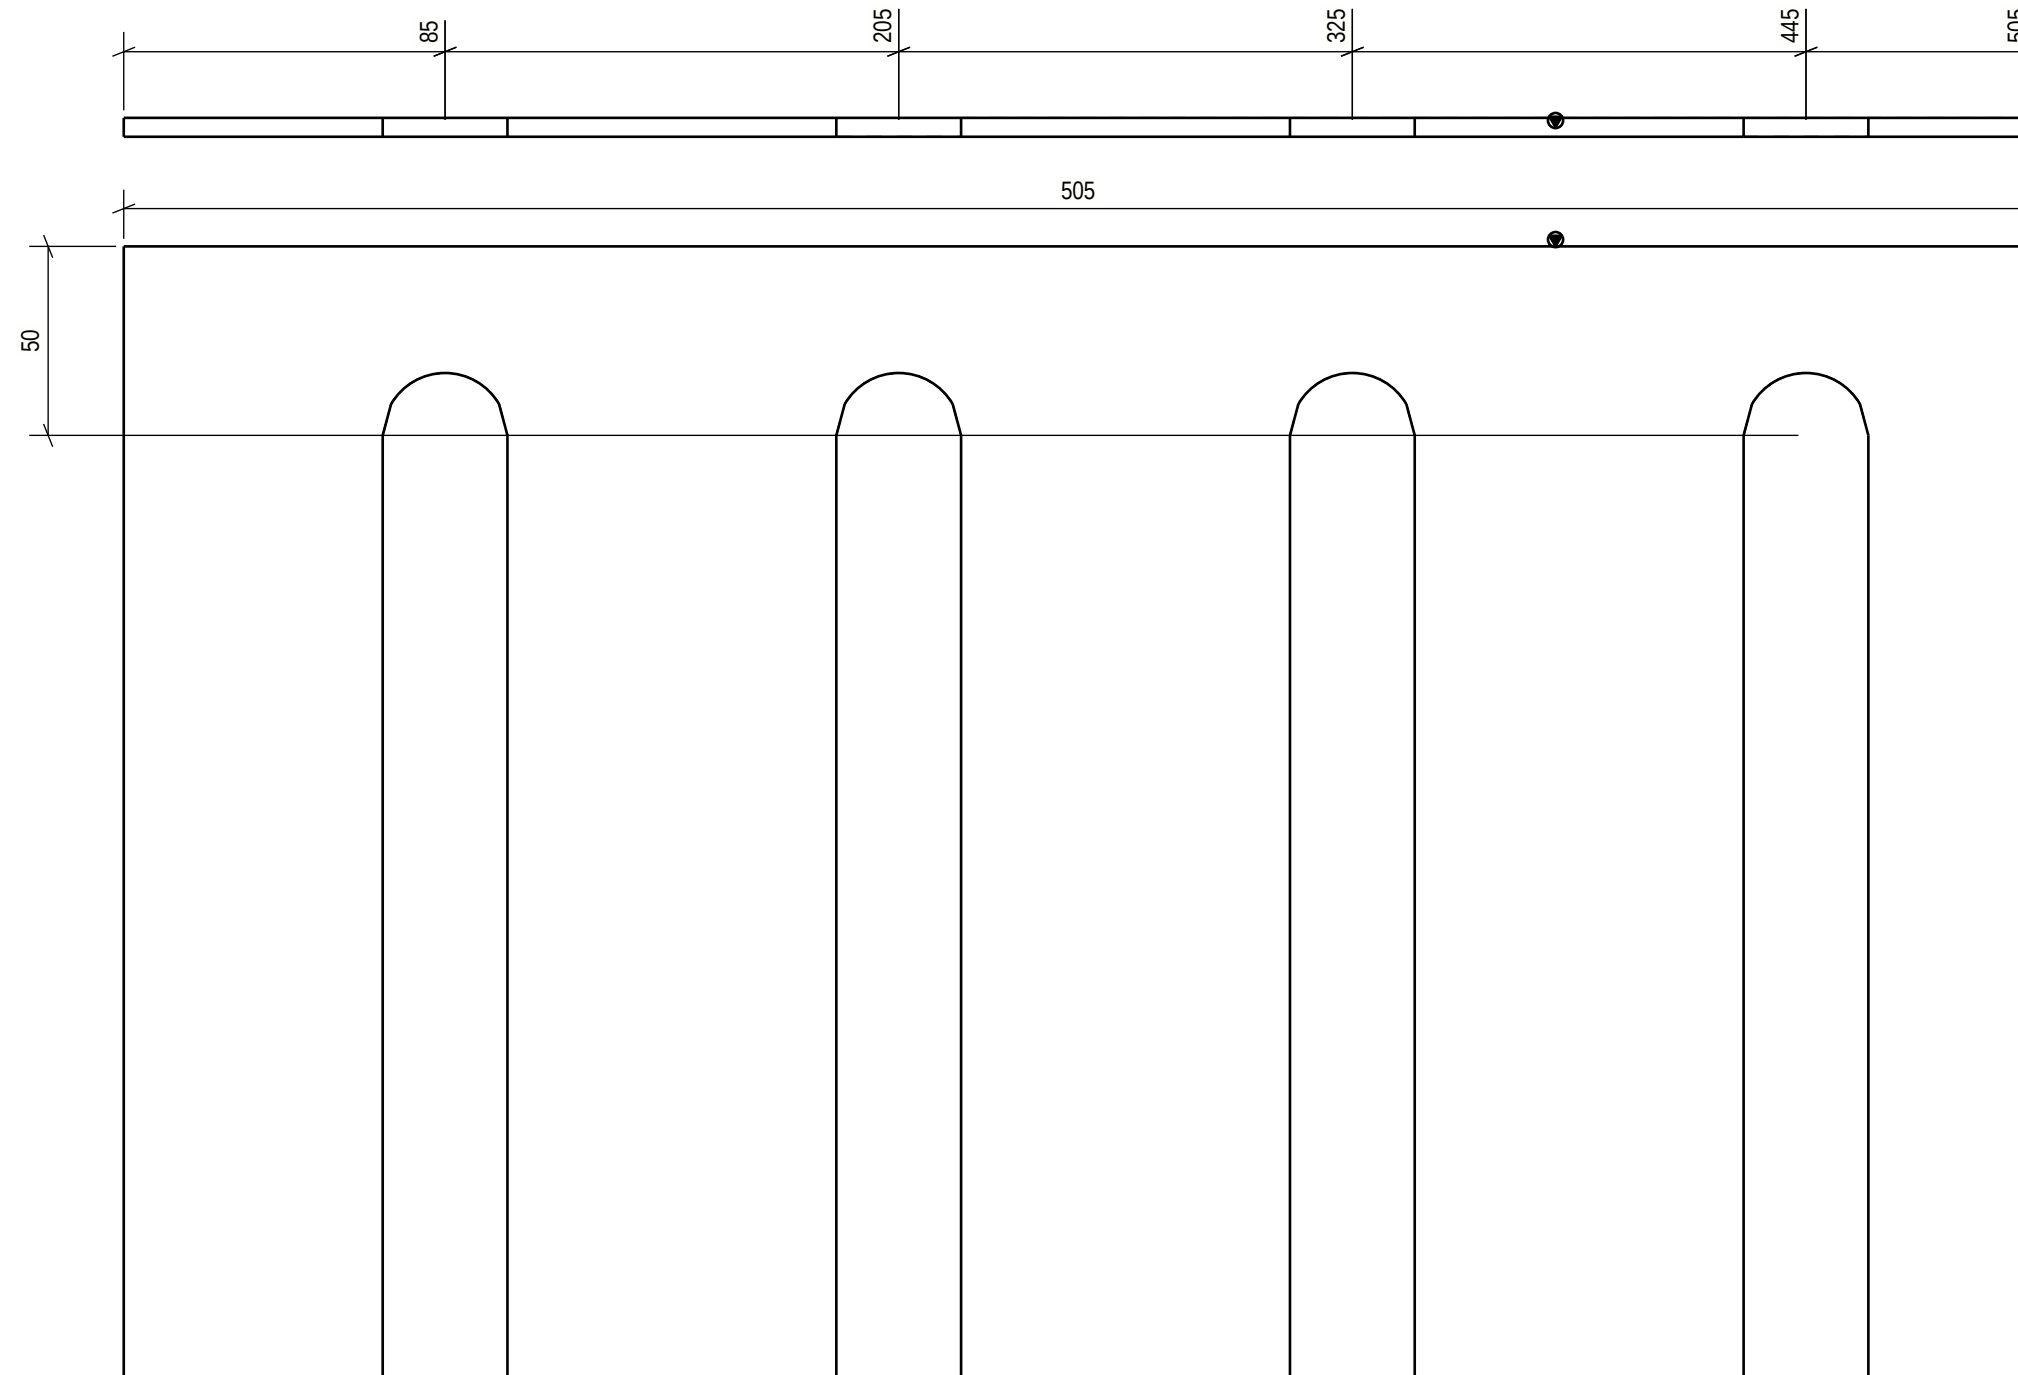


PART LIST FOR ASSEMBLY E51EX-1045, MANUFACTURING AMOUNT 8 PIECES						
PART	PROFILE	MATERIAL	LENGTH [mm]	AREA [m2]	WEIGHT [kg]	PCS
E51EXL-1085	PL5X300	S355J2+N	505	0.25	4.6	1
			TOTAL:	0.25	4.6	

Technical fabrication requirements: Execution class EXC2 Requirements for fabrication, standard EN1090-2, table A.3 : EXC2 Execution Specification document nr 25019443-ICC250-0600-0660-000005 Surface preparation grade ISO8501-3, grade P2 Surface treatment ISO12944-5 Additional requirements on surface treatment C3.07, EPPUR 240/2 Shade RAL 7024 (Graphite Gray) Welding of built up steel section Appendix 1 / Project spec. Welds, if not specified otherwise EN 9692-2 Fabrication tolerances EN 1090-2, Appendix B Special fabrication tolerances Project specification/ shown on drwg. Weld inspection, requirements EN 1090-2, Table 24, U>0.5 Extent of NDT, fillet welds MT-EN1290, 20% of welds Extent of NDT, butt welds UT, EN-ISO17640, 20% of welds Extent of NDT for splices not shown on drawing UT, EN-ISO17640, 100% of welds Requirements on holding EN1090-2 Section 6.6.3 Weld class C, EN ISO 5817 Additional material inspection Shown on drwg.		See specification for steel structures Approved For Construction PROJECT NAME Easpring New Materials Oy FAIR Phase 1 SWECO Sustainable engineering and design  SWECO RAKENNETEKNIikka OY ILMALANPORTTI 2 00240 HELSINKI PUH. +358 207 393 000 www.sweco.fi		DRAWING CONTENT ASSEMBLY DRAWING PLATE E51EX-1045 DATE 12.06.2026 ARCHIVING CODE PAGE DESIGN GROUP STR DRAWN Alexey Serous DESIGNER Alexey Serous APPROVED Pertti Koivumaaanaho CHECKED Jere Kalliosalmi PROJECT NUMBER 25019443 DWG. NO. E51EX-1045 REVISION			
---	--	--	--	---	--	--	--

For special tolerances of bolt hole location
see specification for steel structures

Approved For Construction

PART LIST FOR ASSEMBLY E51EX-1046, MANUFACTURING AMOUNT 4 PIECES						
PART	PROFILE	MATERIAL	LENGTH [mm]	AREA [m2]	WEIGHT [kg]	PCS
E51EXL-1062	PL10X260	S355J2+N	375	0.21	7.7	1
TOTAL:				0.21	7.7	

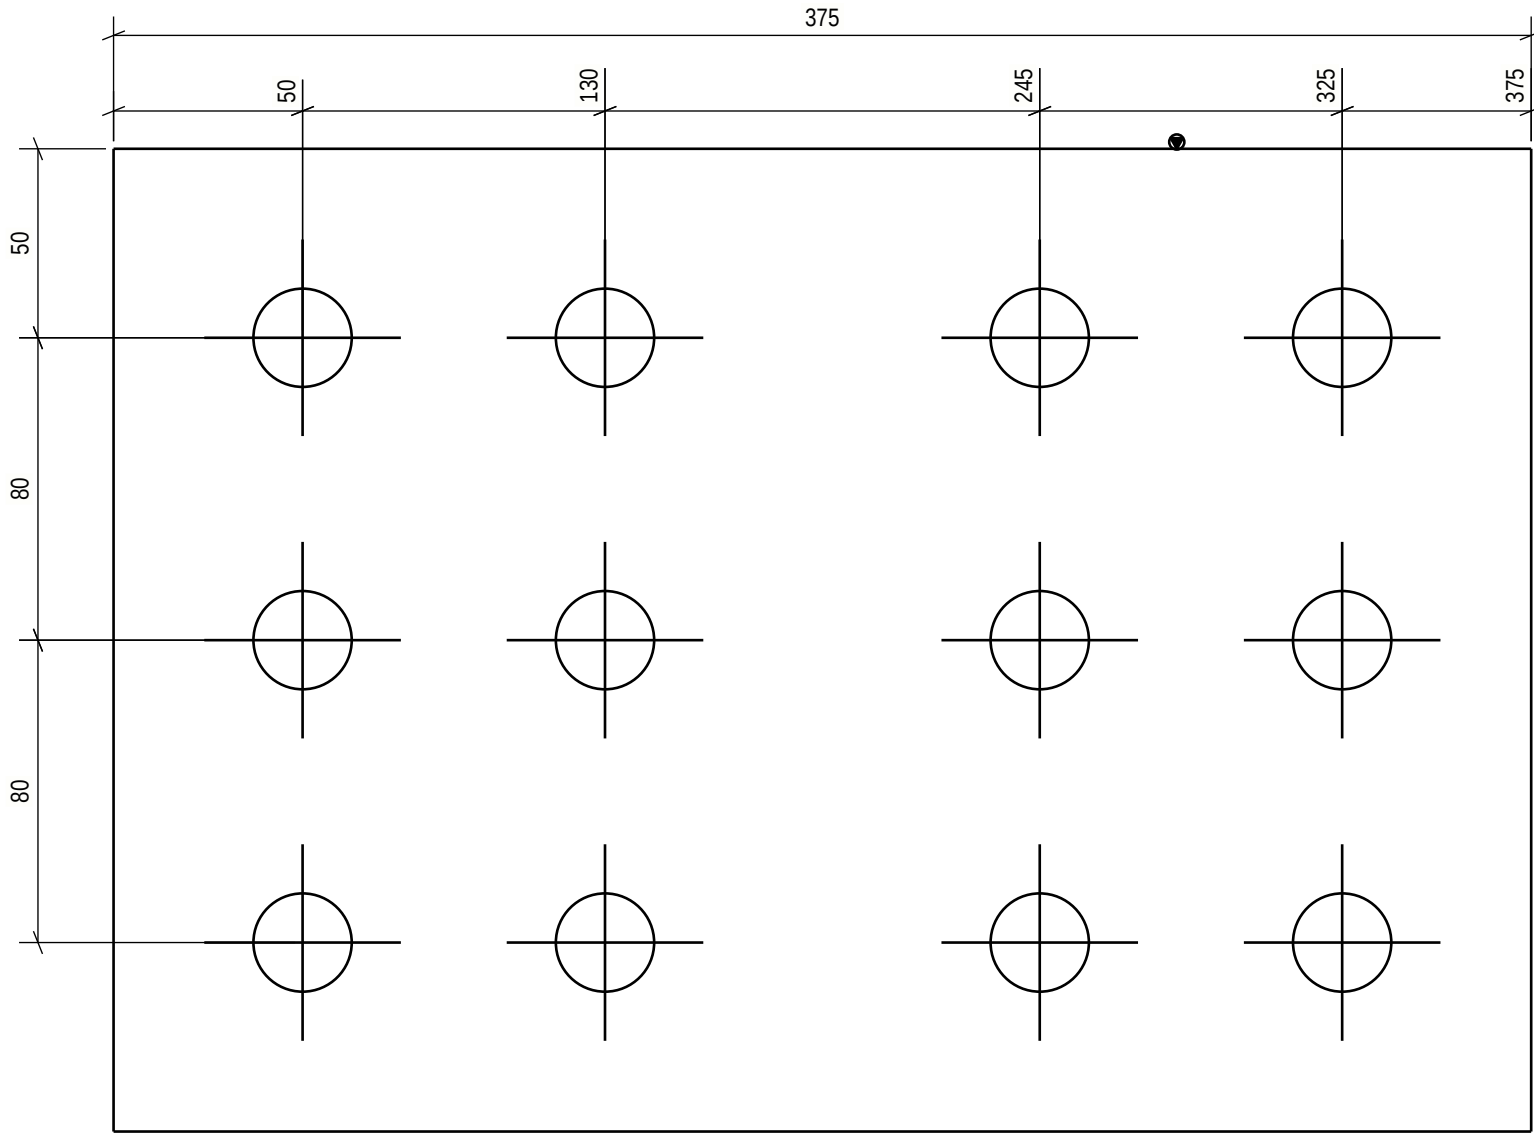


For special tolerances of bolt hole location
see specification for steel structures
Approved For Construction

Technical fabrication requirements:		Execution class	
		EXC2	
Requirements for fabrication, standard	Fabrication tolerances		
EN1090-2, table A.3 : EXC2	EN 1090-2, Appendix B		
Execution Specification document nr	Special fabrication tolerances		
25019443-ICC250-0600-0660-000005	Project specification/ shown on drwg.		
Surface preparation grade	Weld inspection, requirements		
ISO8501-3, grade P2	EN 1090-2,Table 24, U>0.5		
Surface treatment	Extent of NDT, filled welds		
ISO12944-5	MT-EN1290,20% of welds		
Additional requirements on surface treatment	Extent of NDT, butt welds		
C3.07, EPPUR 240/2	UT, EN-ISO17640, 20% of welds		
Shade	Extent of NDT for splices not shown on drawing		
RAL 7024 (Graphite Gray)	UT, EN-ISO17640, 100%of welds		
Welding of built up steel section	Requirements on holing		
Appendix 1 / Project spec.	EN1090-2 Section 6.6.3		
Welds, if not specified otherwise	Weld class	Additional material inspection	
EN 9692-1, EN 9692-2	C, EN ISO 5817	Shown on drwg.	

PROJECT NAME		DRAWING CONTENT	
Easpring New Materials Oy		ASSEMBLY DRAWING	
FAIR Phase 1		PLATE	
		E51EX-1046	

 Sustainable engineering and design	SWECO RAKENNETEKNIikka OY ILMALANPORTTI 2 00240 HELSINKI		DATE 12.06.2026	ARCHIVING CODE	PAGE	DESIGN GROUP STR
	PUH. +358 207 393 000 www.sweco.fi		DRAWN Alexey Serous	DESIGNER Alexey Serous	APPROVED Pertti Koivumaaanaho	CHECKED Jere Kallosalmi
			PROJECT NUMBER 25019443	REVISION E51EX-1046		

PART LIST FOR ASSEMBLY E51EX-1047, MANUFACTURING AMOUNT 5 PIECES						
PART	PROFILE	MATERIAL	LENGTH [mm]	AREA [m2]	WEIGHT [kg]	PCS
E51EXL-1086	PL5X300	S355J2+N	900	0.46	8.5	1
TOTAL:				0.46	8.5	

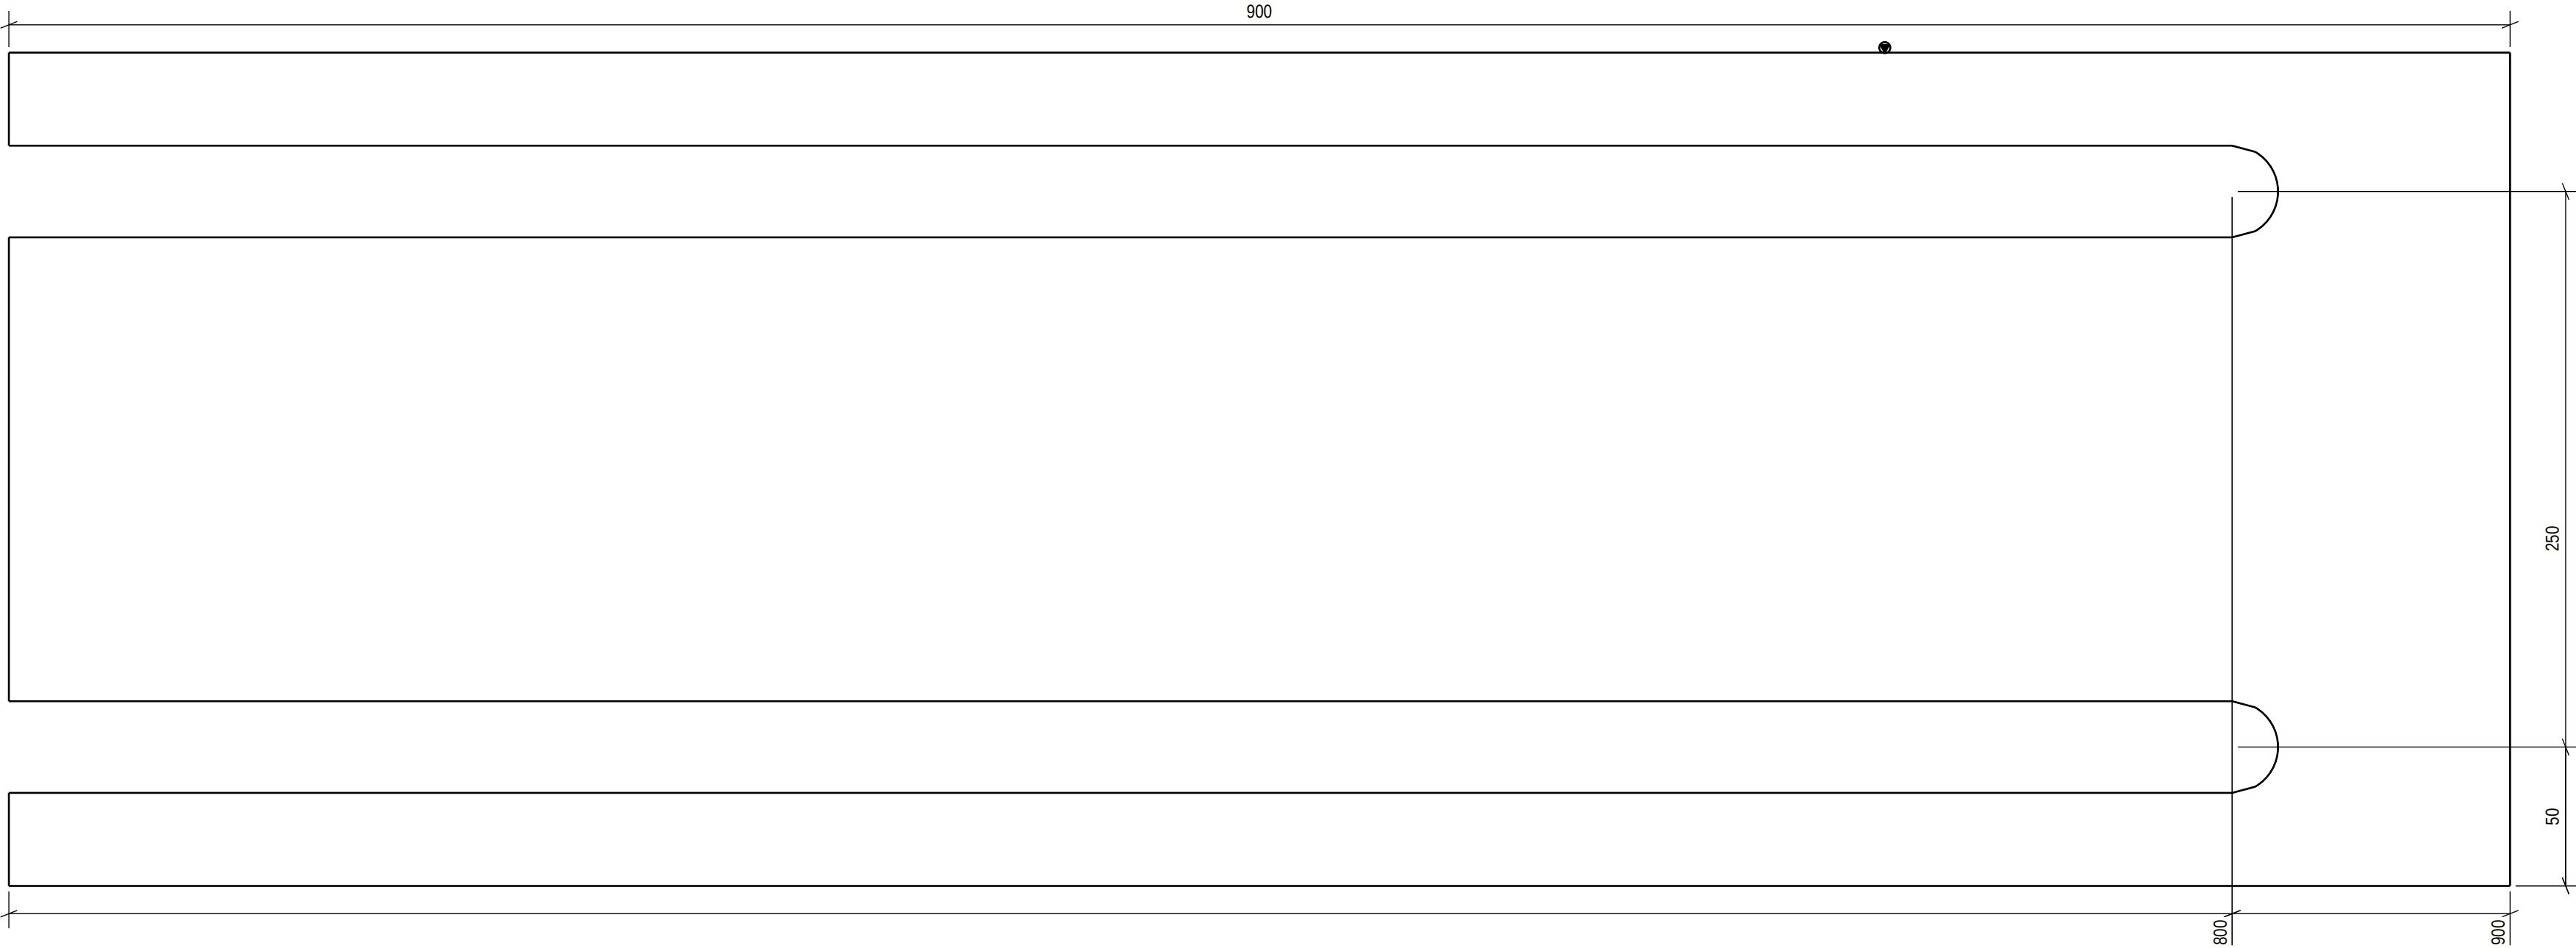

Technical fabrication requirements:

Execution class

EXC2

Requirements for fabrication, standard

EN1090-2, table A.3 : EXC2

Execution Specification document nr

25019443-ICC250-0600-0660-000005

Surface preparation grade

ISO8501-3, grade P2

Surface treatment

ISO12944-5

Additional requirements on surface treatment

C3.07, EPPUR 240/2

Shade

RAL 7024 (Graphite Gray)

Welding of built up steel section

Appendix 1 / Project spec.

Welds, if not specified otherwise

EN 9692-1, EN 9692-2

Fabrication tolerances

EN 1090-2, Appendix B

Special fabrication tolerances

Project specification/ shown on drwg.

Weld inspection, requirements

EN 1090-2,Table 24, U>0.5

Extent of NDT, fillet welds

MT-EN1290,20% of welds

Extent of NDT, butt welds

UT, EN-ISO17640, 20% of welds

Extent of NDT for splices not shown on drawing

UT, EN-ISO17640, 100%of welds

Requirements on holing

EN1090-2 Section 6.6.3

Weld class

C, EN ISO 5817

Additional material inspection

Shown on drwg.

PROJECT NAME

Easpring New Materials Oy

FAIR Phase 1



SWECO RAKENNETEKNIikka OY

ILMALANPORTTI 2

00240 HELSINKI

PUH. +358 207 393 000

www.sweco.fi

DRAWING CONTENT

ASSEMBLY DRAWING

PLATE

E51EX-1047

DATE

12.06.2026

ARCHIVING CODE

PAGE

DESIGN GROUP

STR

DRAWN

Alexey Serous

DESIGNER

Alexey Serous

APPROVED

Pertti Koivumaaanaho

CHECKED

Jere Kalilosalmi

PROJECT NUMBER


25019443

DWG. NO.

E51EX-1047


REVISION

For special tolerances of bolt hole location
see specification for steel structures
Approved For Construction

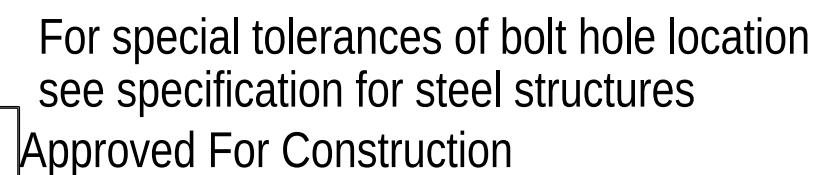

		Execution class
Technical fabrication requirements:		EXC2
Requirements for fabrication, standard EN1090-2, table A.3 : EXC2 Execution Specification document nr 25019443-ICC250-0600-0660-000005 Surface preparation grade ISO8501-3, grade P2 Surface treatment ISO12944-5 Additional requirements on surface treatment C3.07, EPPUR 240/2 Shade RAL 7024 (Graphite Gray) Welding of built up steel section Appendix 1 / Project spec. Welds, if not specified otherwise EN 9692-1, EN 9692-2	Fabrication tolerances EN 1090-2, Appendix B Special fabrication tolerances Project specification/ shown on drwg. Weld inspection, requirements EN 1090-2, Table 24, U>0.5 Extent of NDT, fillet welds MT-EN1290, 20% of welds Extent of NDT, butt welds UT, EN-ISO17640, 20% of welds Extent of NDT for splices not shown on drawing UT, EN-ISO17640, 100% of welds Requirements on healing EN1090-2 Section 6.6.3 Weld class EN ISO 5817	
		Additional material inspection Shown on drwg.

25019443 Fair E500

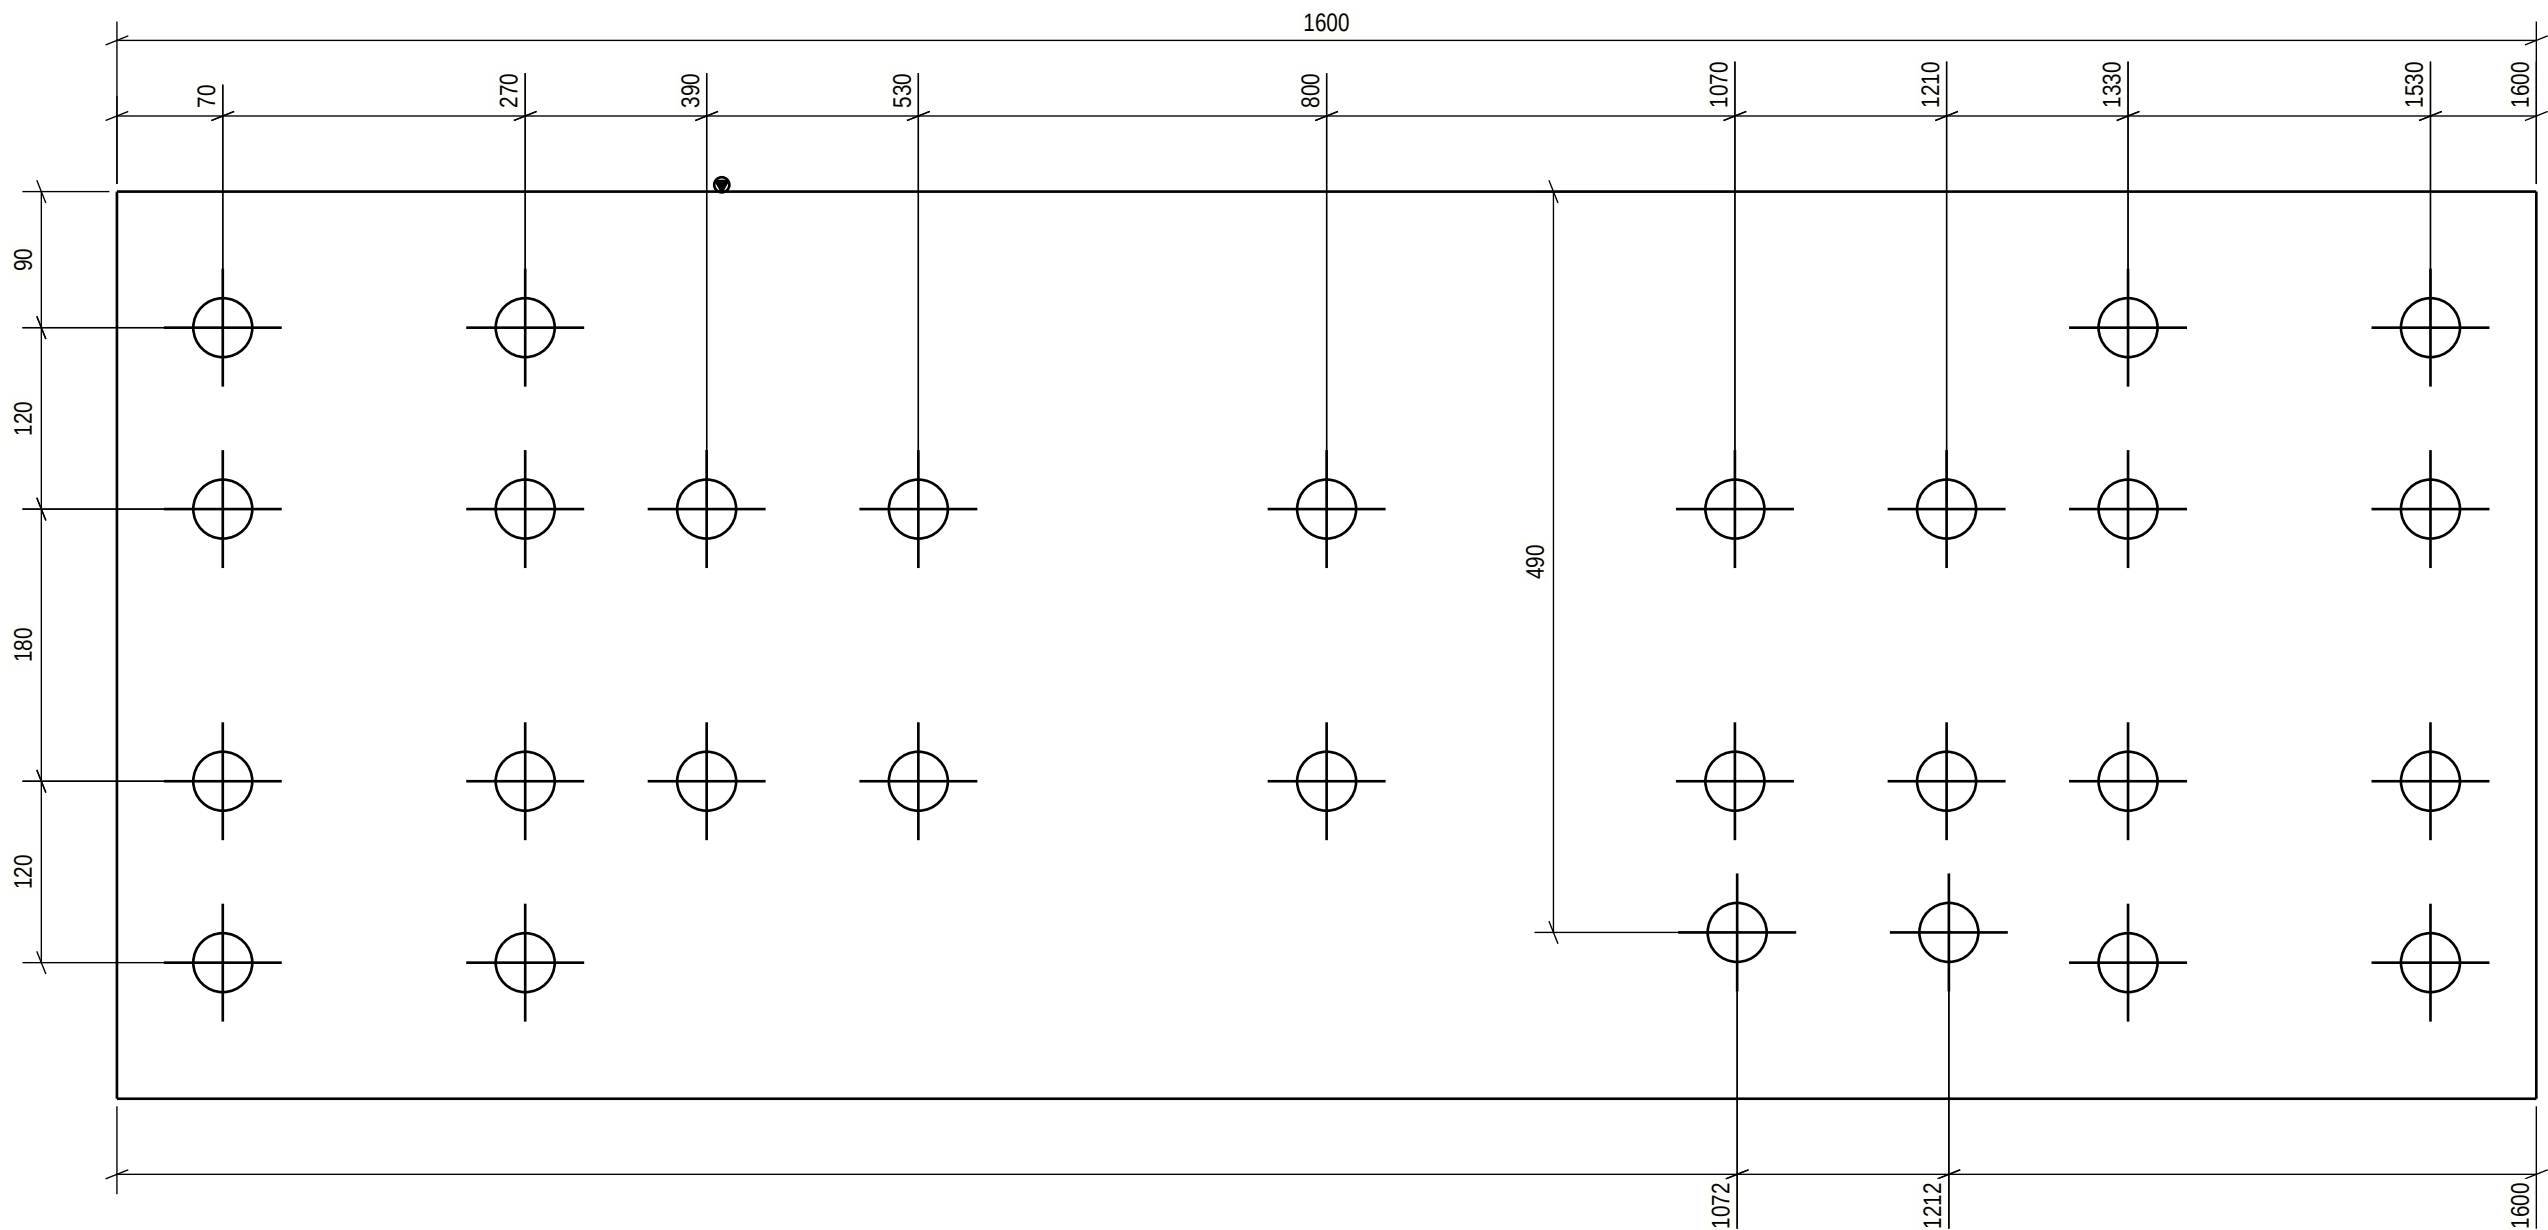

PART LIST FOR ASSEMBLY E51EX-1049, MANUFACTURING AMOUNT 4 PIECES						
PART	PROFILE	MATERIAL	LENGTH [mm]	AREA [m2]	WEIGHT [kg]	PCS
E51EXL-1069	PL5X600	S355J2+N	1600	1.94	37.7	1
TOTAL:				1.94	37.7	


Technical fabrication requirements:		Execution class
Requirements for fabrication, standard	Fabrication tolerances	EXC2
EN1090-2, table A.3 : EXC2	EN 1090-2, Appendix B	
Execution Specification document nr	Special fabrication tolerances	
25019443-ICC250-0600-0660-000005	Project specification/ shown on drwg.	
Surface preparation grade	Weld inspection, requirements	
ISO8501-3, grade P2	EN 1090-2,Table 24, U>0.5	
Surface treatment	Extent of NDT, fillet welds	
ISO12944-5	MT-EN1290,20% of welds	
Additional requirements on surface treatment	Extent of NDT, butt welds	
C3.07, EPPUR 240/2	UT, EN-ISO17640, 20% of welds	
Shade	Extent of NDT for splices not shown on drawing	a 5 / 5 a
RAL 7024 (Graphite Gray)	UT, EN-ISO17640, 100% of welds	
Welding of built up steel section	Requirements on holing	
Appendix 1 / Project spec.	EN1090-2 Section 6.6.3	
Welds, if not specified otherwise	Weld class	
EN 9692-1, EN 9692-2	C, EN ISO 5817	Additional material inspection Shown on drwg.

Approved For Construction

PROJECT NAME
Easpring New Materials Oy
FAIR Phase 1




SWECO RAKENNETEKNIikka OY
ILMALANPORTTI 2
00240 HELSINKI
PUH. +358 207 393 000
www.sweco.fi

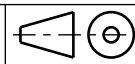

DRAWING CONTENT
ASSEMBLY DRAWING
PLATE
E51EX-1049

DATE	ARCHIVING CODE	PAGE	DESIGN GROUP
12.06.2026			STR
DRAWN	DESIGNER	APPROVED	CHECKED
Alexey Serous	Alexey Serous	Pertti Koivumaaanaho	Jere Kallosalmi
PROJECT NUMBER	DWG. NO.	REVISION	
25019443	E51EX-1049		

PART LIST FOR ASSEMBLY E51EX-1050, MANUFACTURING AMOUNT 4 PIECES						
PART	PROFILE	MATERIAL	LENGTH [mm]	AREA [m2]	WEIGHT [kg]	PCS
E51EXL-1065	PL5X600	S355J2+N	1600	1.94	37.7	1
TOTAL:				1.94	37.7	

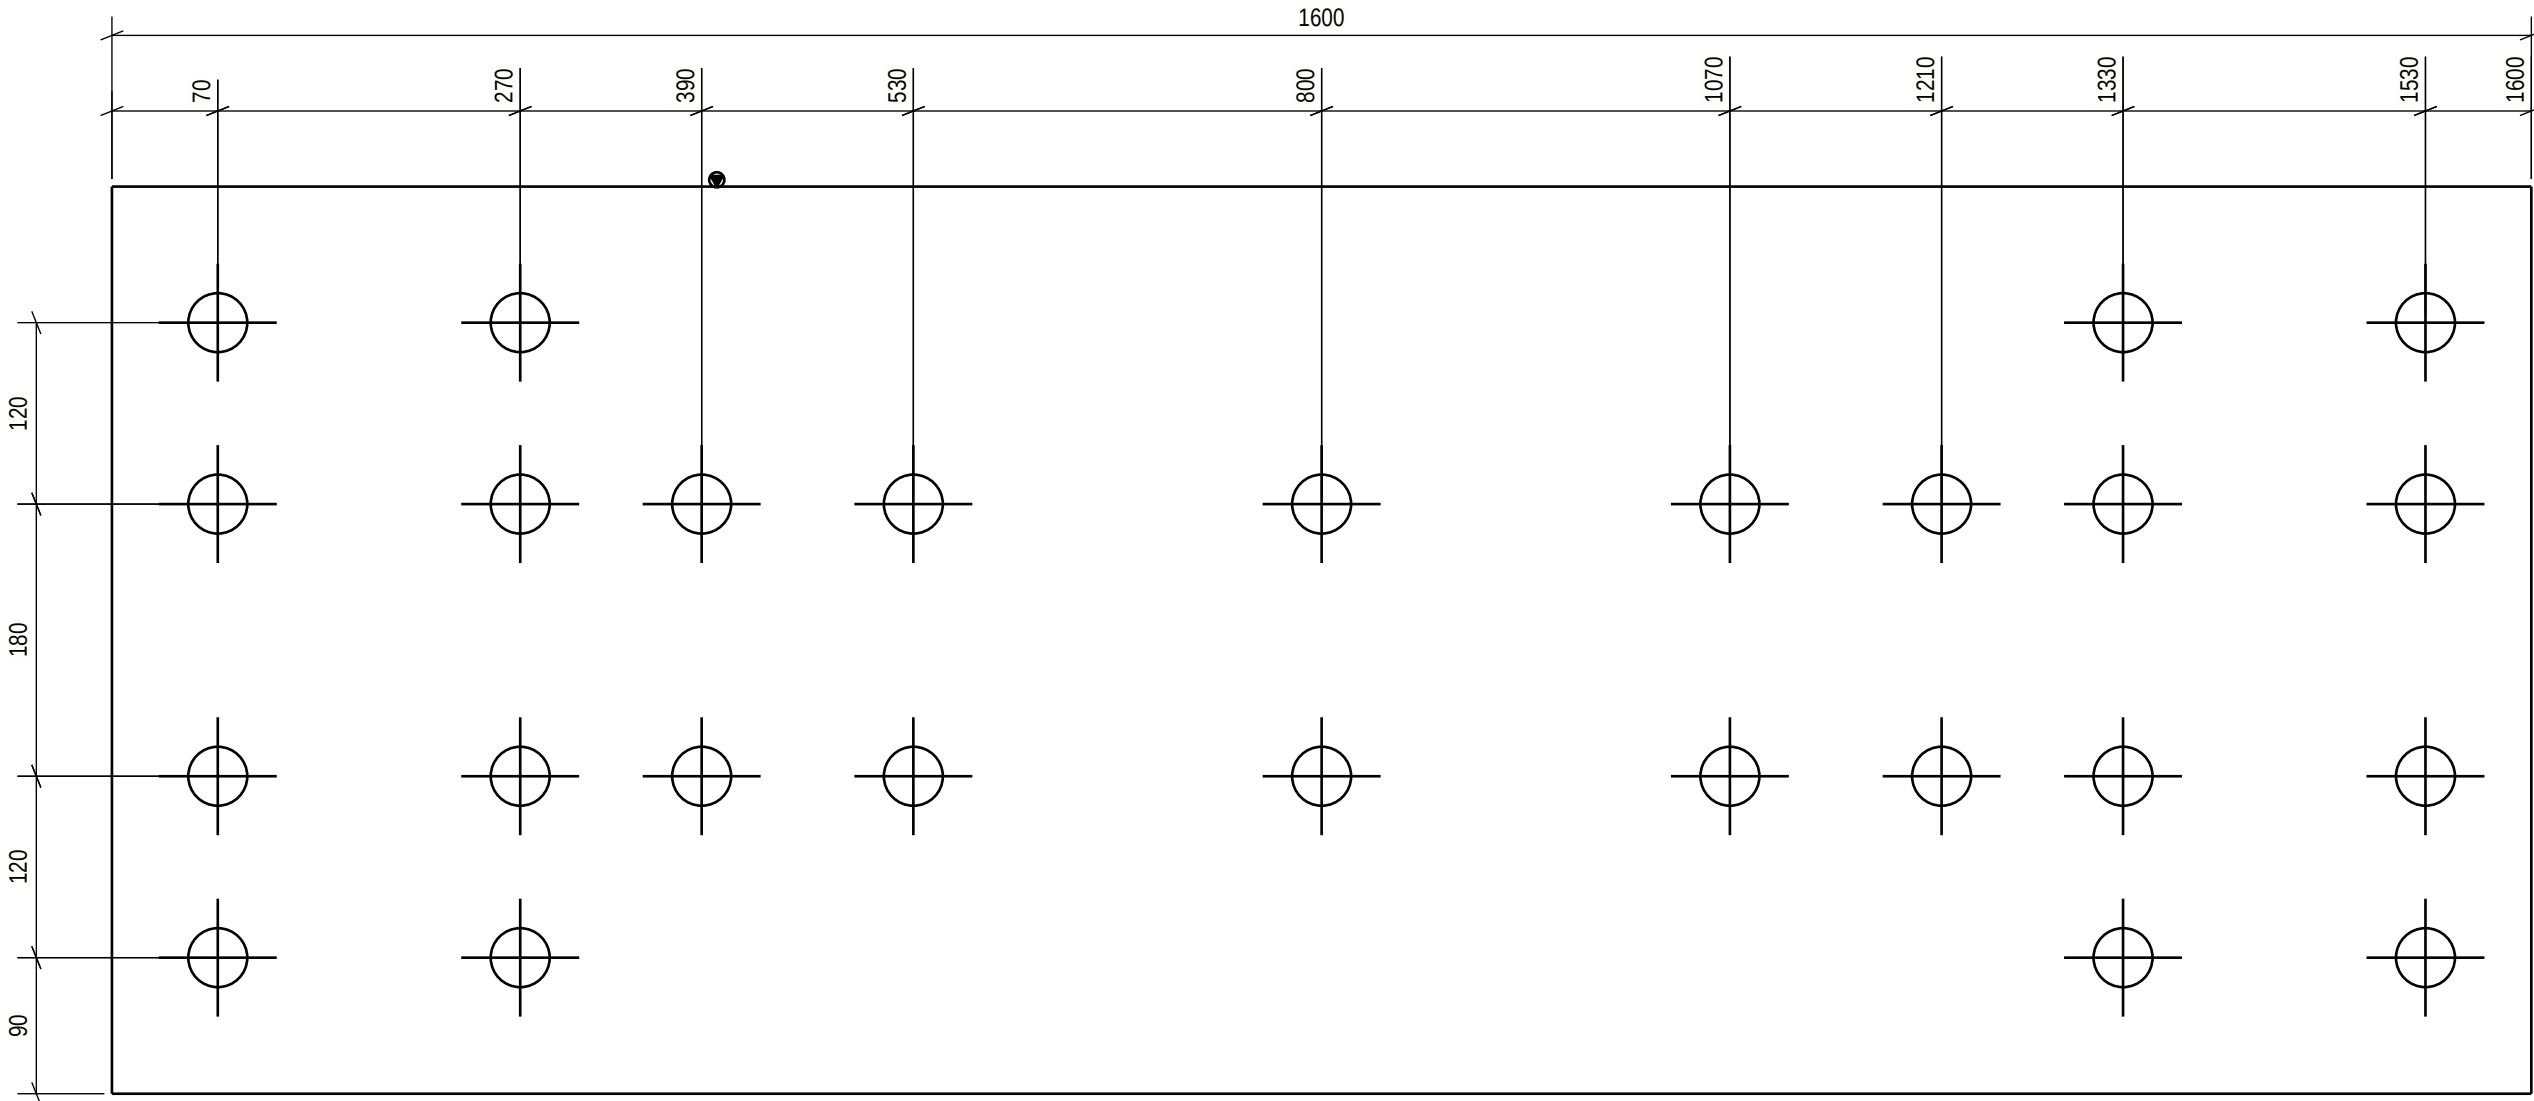


Technical fabrication requirements:		Execution class
Requirements for fabrication, standard	Fabrication tolerances	EXC2
EN1090-2, table A.3 : EXC2	EN 1090-2, Appendix B	
Execution Specification document nr	Special fabrication tolerances	
25019443-ICC250-0600-0660-000005	Project specification/ shown on drwg.	
Surface preparation grade	Weld inspection, requirements	
ISO8501-3, grade P2	EN 1090-2,Table 24, U>0.5	
Surface treatment	Extent of NDT, fillet welds	
ISO12944-5	MT-EN1290,20% of welds	
Additional requirements on surface treatment	Extent of NDT, butt welds	
C3.07, EPPUR 240/2	UT, EN-ISO17640, 20% of welds	
Shade	Extent of NDT for splices not shown on drawing	a 5 \ 5/ a
RAL 7024 (Graphite Gray)	UT, EN-ISO17640, 100%of welds	
Welding of built up steel section	Requirements on holing	
Appendix 1 / Project spec.	EN1090-2 Section 6.6.3	
Welds, if not specified otherwise	Weld class	
EN 9692-1, EN 9692-2	C, EN ISO 5817	Additional material inspection Shown on drwg.

Approved For Construction

PROJECT NAME
Easpring New Materials Oy
FAIR Phase 1






SWECO RAKENNETEKNIikka OY
ILMALANPORTTI 2
00240 HELSINKI
PUH. +358 207 393 000
www.sweco.fi

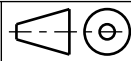

DRAWING CONTENT
ASSEMBLY DRAWING
PLATE
E51EX-1050

DATE	ARCHIVING CODE	PAGE	DESIGN GROUP
12.06.2026			STR
DRAWN	DESIGNER	APPROVED	CHECKED
Alexey Serous	Alexey Serous	Pertti Koivumaaanaho	Jere Kallosalmi
PROJECT NUMBER	DWG. NO.	REVISION	
25019443	E51EX-1050		

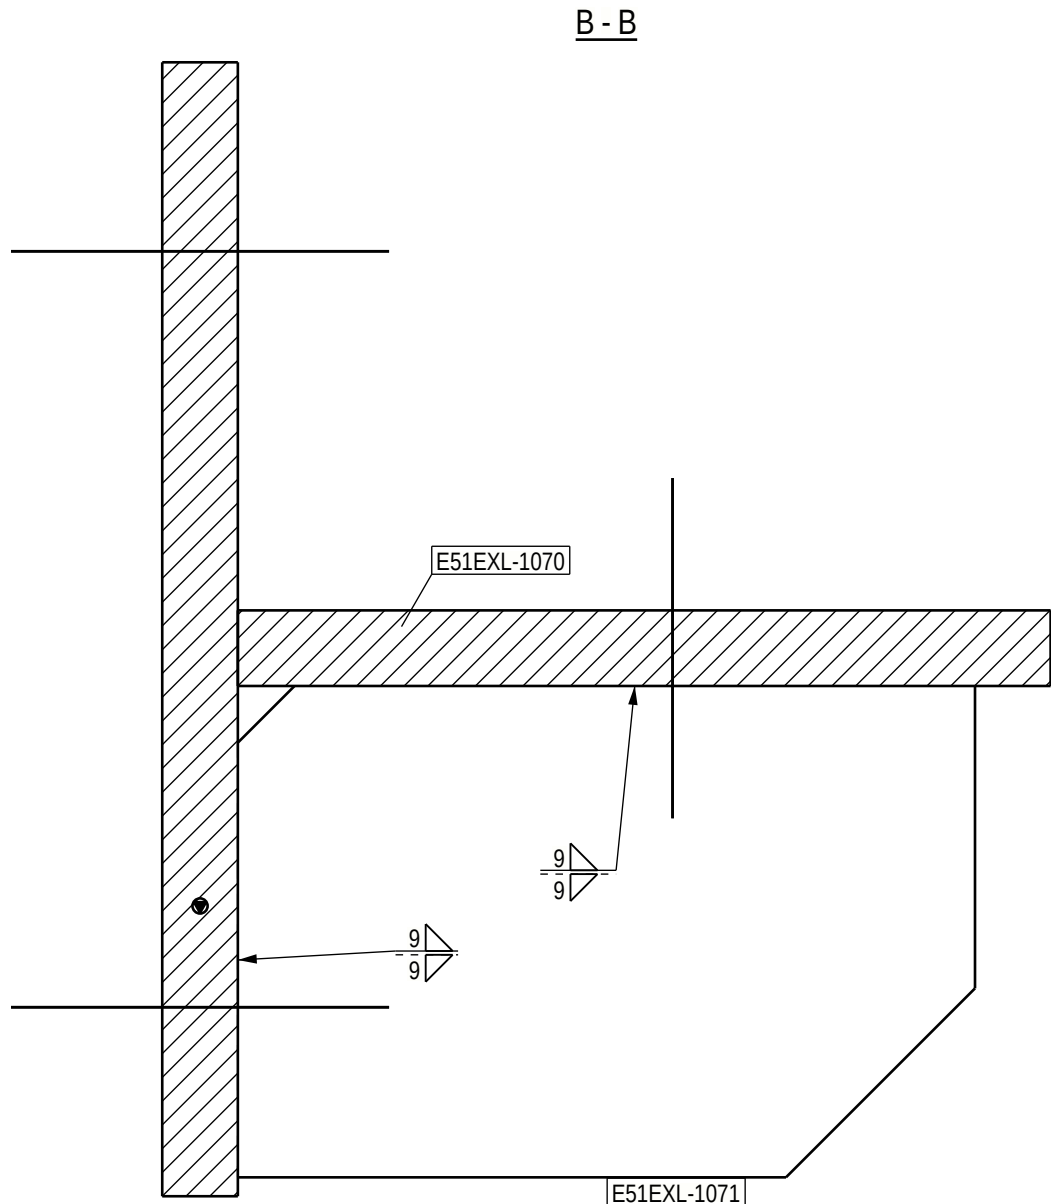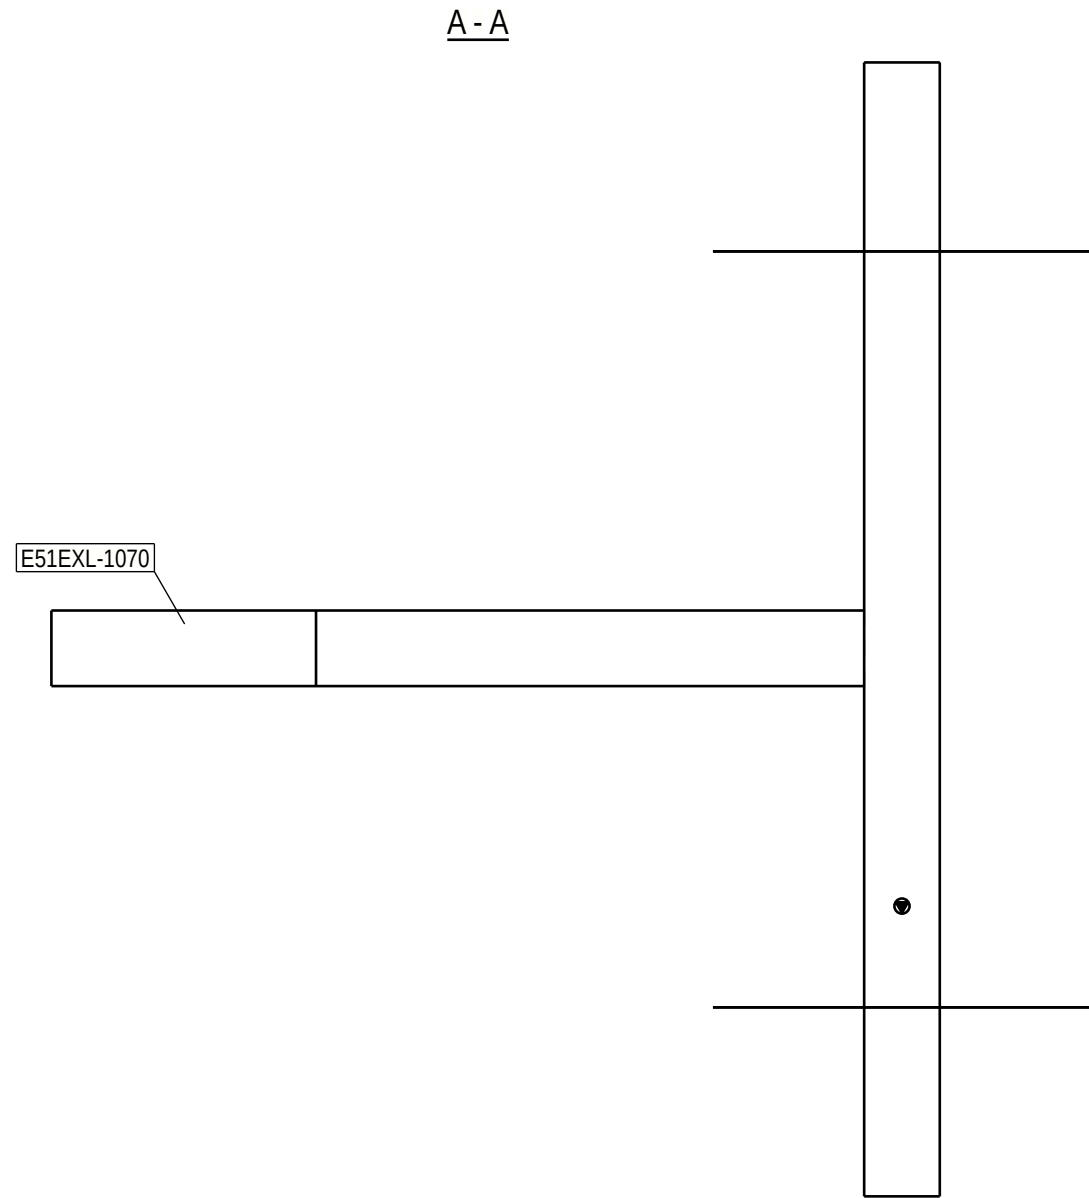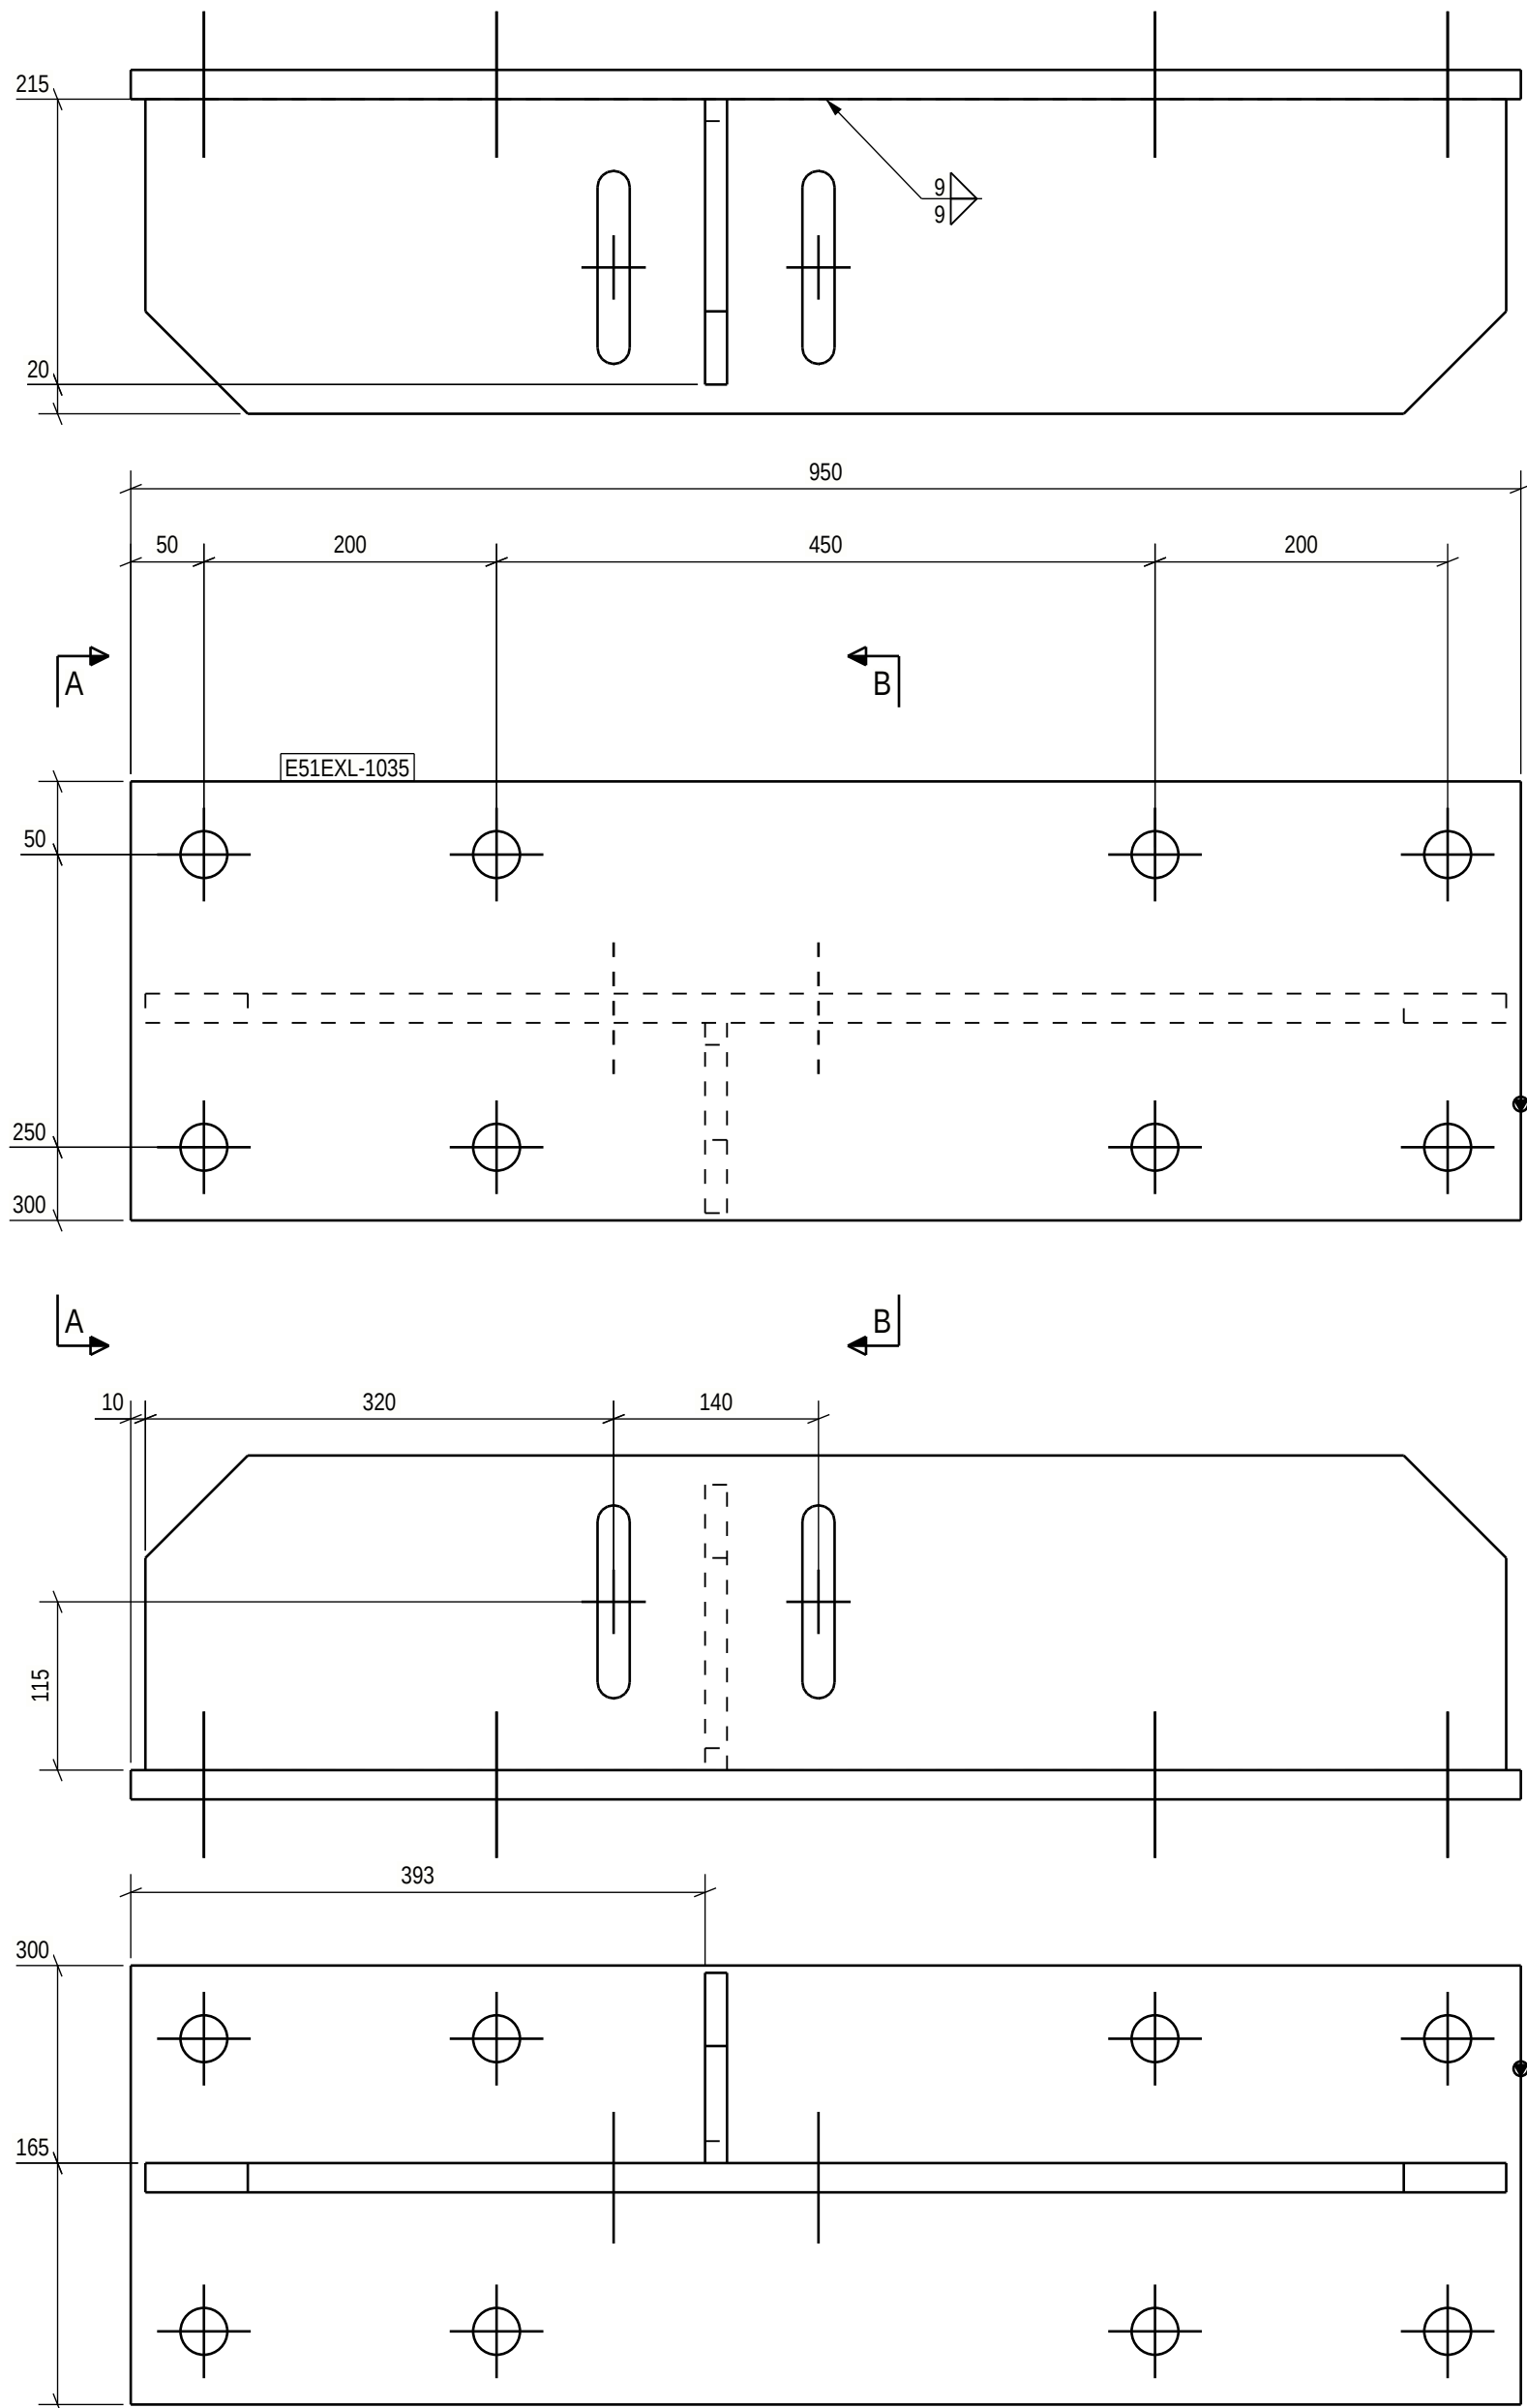

PART LIST FOR ASSEMBLY E51EX-1051, MANUFACTURING AMOUNT 1 PIECES						
PART	PROFILE	MATERIAL	LENGTH [mm]	AREA [m2]	WEIGHT [kg]	PCS
E51EXL-1035	PL20X300	S355J2+N	950	0.62	44.7	1
E51EXL-1070	PL20X215	S355J2+N	930	0.43	30.6	1
E51EXL-1071	PL15X130	S355J2+N	195	0.06	2.8	1
TOTAL:				1.11	78.2	


Technical fabrication requirements:		Execution class
Requirements for fabrication, standard	Fabrication tolerances	EXC2
EN1090-2, table A.3 : EXC2	EN 1090-2, Appendix B	
Execution Specification document nr	Special fabrication tolerances	
25019443-ICC250-0600-0660-000005	Project specification/ shown on drwg.	
Surface preparation grade	Weld inspection, requirements	
ISO8501-3, grade P2	EN 1090-2, Table 24, U>0.5	
Surface treatment	Extent of NDT, fillet welds	
ISO12944-5	MT-EN1290, 20% of welds	
Additional requirements on surface treatment	Extent of NDT, butt welds	
C3.07, EPPUR 240/2	UT, EN-ISO17640, 20% of welds	
Shade	Extent of NDT for splices not shown on drawing	a 5 / 5 a
RAL 7024 (Graphite Gray)	UT, EN-ISO17640, 100% of welds	
Welding of built up steel section	Requirements on holing	
Appendix 1 / Project spec.	EN1090-2 Section 6.6.3	
Welds, if not specified otherwise	Weld class	
EN 9692-1, EN 9692-2	C, EN ISO 5817	Additional material inspection Shown on drwg.

Approved For Construction

PROJECT NAME
Easpring New Materials Oy
FAIR Phase 1





SWECO RAKENNETEKNIikka OY
ILMALANPORTTI 2
00240 HELSINKI
PUH. +358 207 393 000
www.sweco.fi

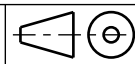

DRAWING CONTENT
ASSEMBLY DRAWING
PLATE
E51EX-1051

DATE	ARCHIVING CODE	PAGE	DESIGN GROUP
12.06.2026			STR
DRAWN	DESIGNER	APPROVED	CHECKED
Alexey Serous	Alexey Serous	Pertti Koivumaa	Jere Kallosalmi
PROJECT NUMBER	DWG. NO.	REVISION	
25019443	E51EX-1051		

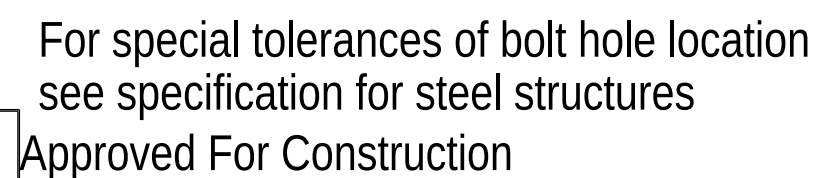

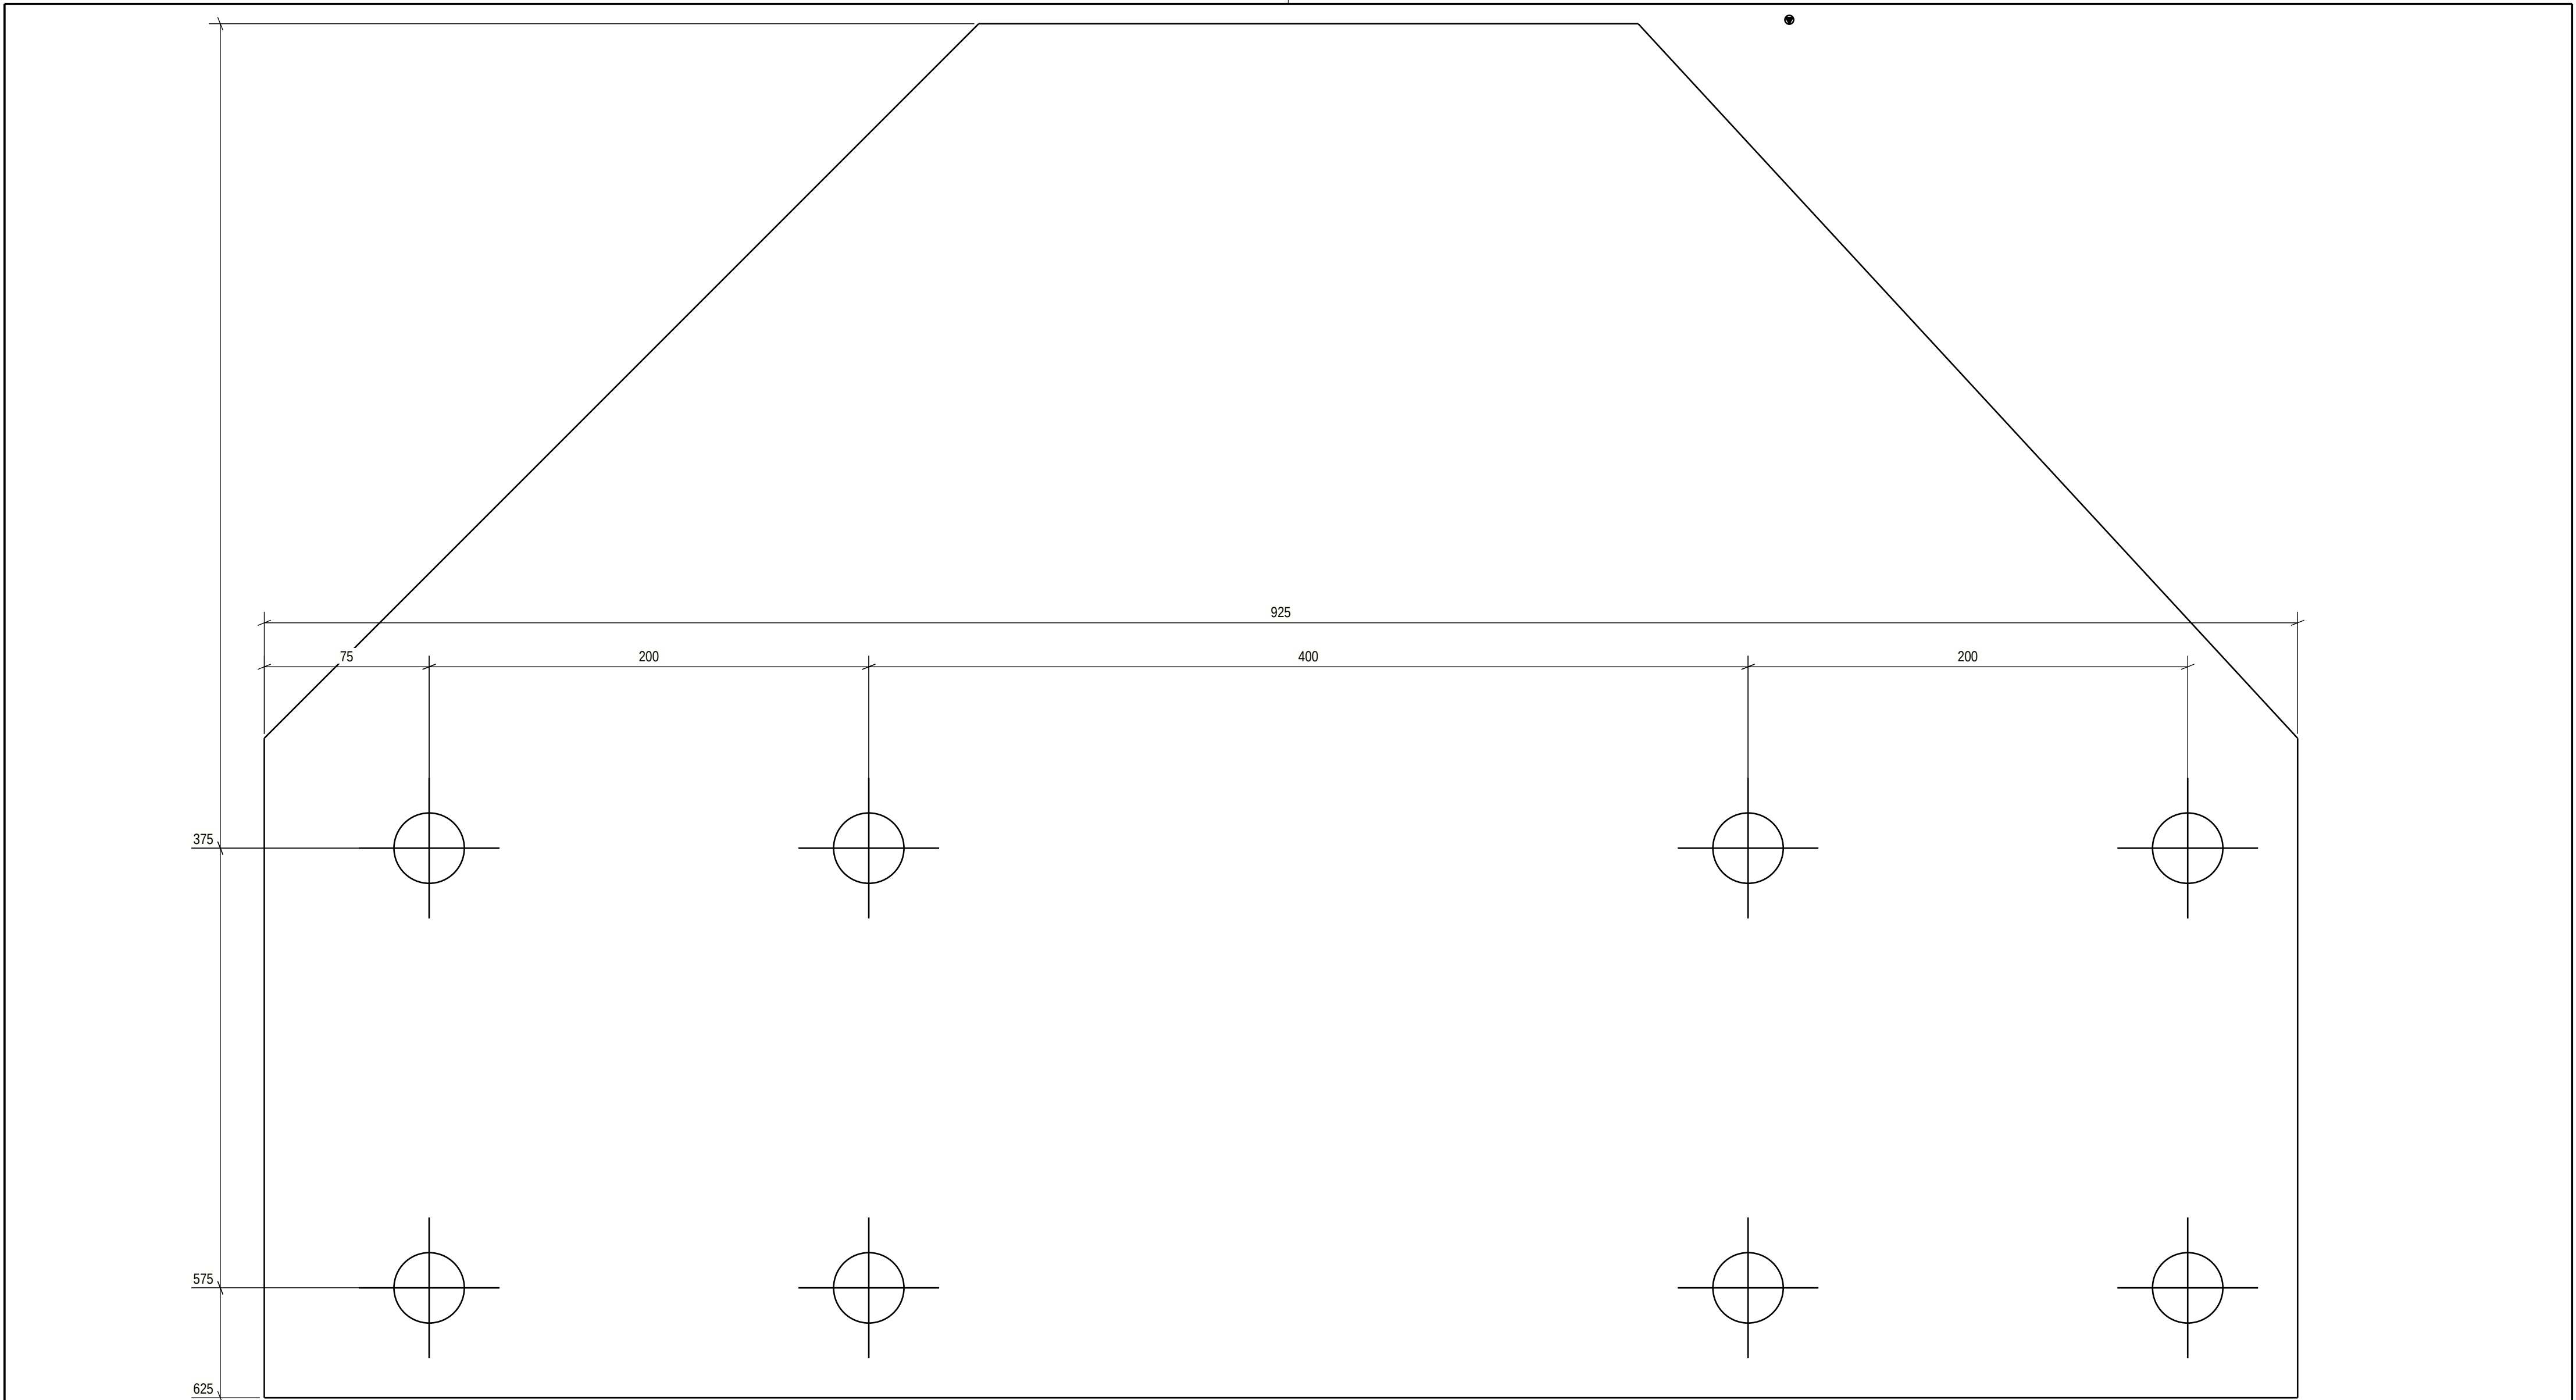

PART LIST FOR ASSEMBLY E51EX-1053, MANUFACTURING AMOUNT 2 PIECES						
PART	PROFILE	MATERIAL	LENGTH [mm]	AREA [m2]	WEIGHT [kg]	PCS
E51EXL-1091	PL5X625	S355J2+N	925	0.97	18.7	1
TOTAL:				0.97	18.7	

Technical fabrication requirements:		Execution class EXC2	
Requirements for fabrication, standard EN1090-2, table A.3 : EXC2		Fabrication tolerances EN 1090-2, Appendix B	
Execution Specification document nr 25019443-ICC250-0600-0660-000005		Special fabrication tolerances Project specification/ shown on drwg.	
Surface preparation grade ISO8501-3, grade P2		Weld inspection, requirements EN 1090-2, Table 24, U>0.5	
Surface treatment ISO12944-5		Extent of NDT, fillet welds MT-EN1290, 20% of welds	
Additional requirements on surface treatment C3.07, EPPUR 240/2		Extent of NDT, butt welds UT, EN-ISO17640, 20% of welds	
Shade RAL 7024 (Graphite Gray)		Extent of NDT for splices not shown on drawing UT, EN-ISO17640, 100% of welds	
Welding of built up steel section Appendix 1 / Project spec.		Requirements on holing EN1090-2 Section 6.6.3	
Welds, if not specified otherwise EN 9692-1, EN 9692-2		Weld class C, EN ISO 5817	
Additional material inspection Shown on drwg.			

For special tolerances of bolt hole location
see specification for steel structures
Approved For Construction

PROJECT NAME
Easpring New Materials Oy
FAIR Phase 1

SWECO 
Sustainable engineering and design

SWECO RAKENNETEKNIikka OY
ILMALANPORTTI 2
00240 HELSINKI

PUH. +358 207 393 000
www.sweco.fi

DATE
12.06.2026

DRAWN
Alexey Serous

PROJECT NUMBER
25019443

ARCHIVING CODE

DESIGNER
Alexey Serous

DWG. NO.
E51EX-1053


PAGE

APPROVED
Pertti Koivumaa

CHECKED
Jere Kallosalmi

DESIGN GROUP
STR

REVISION

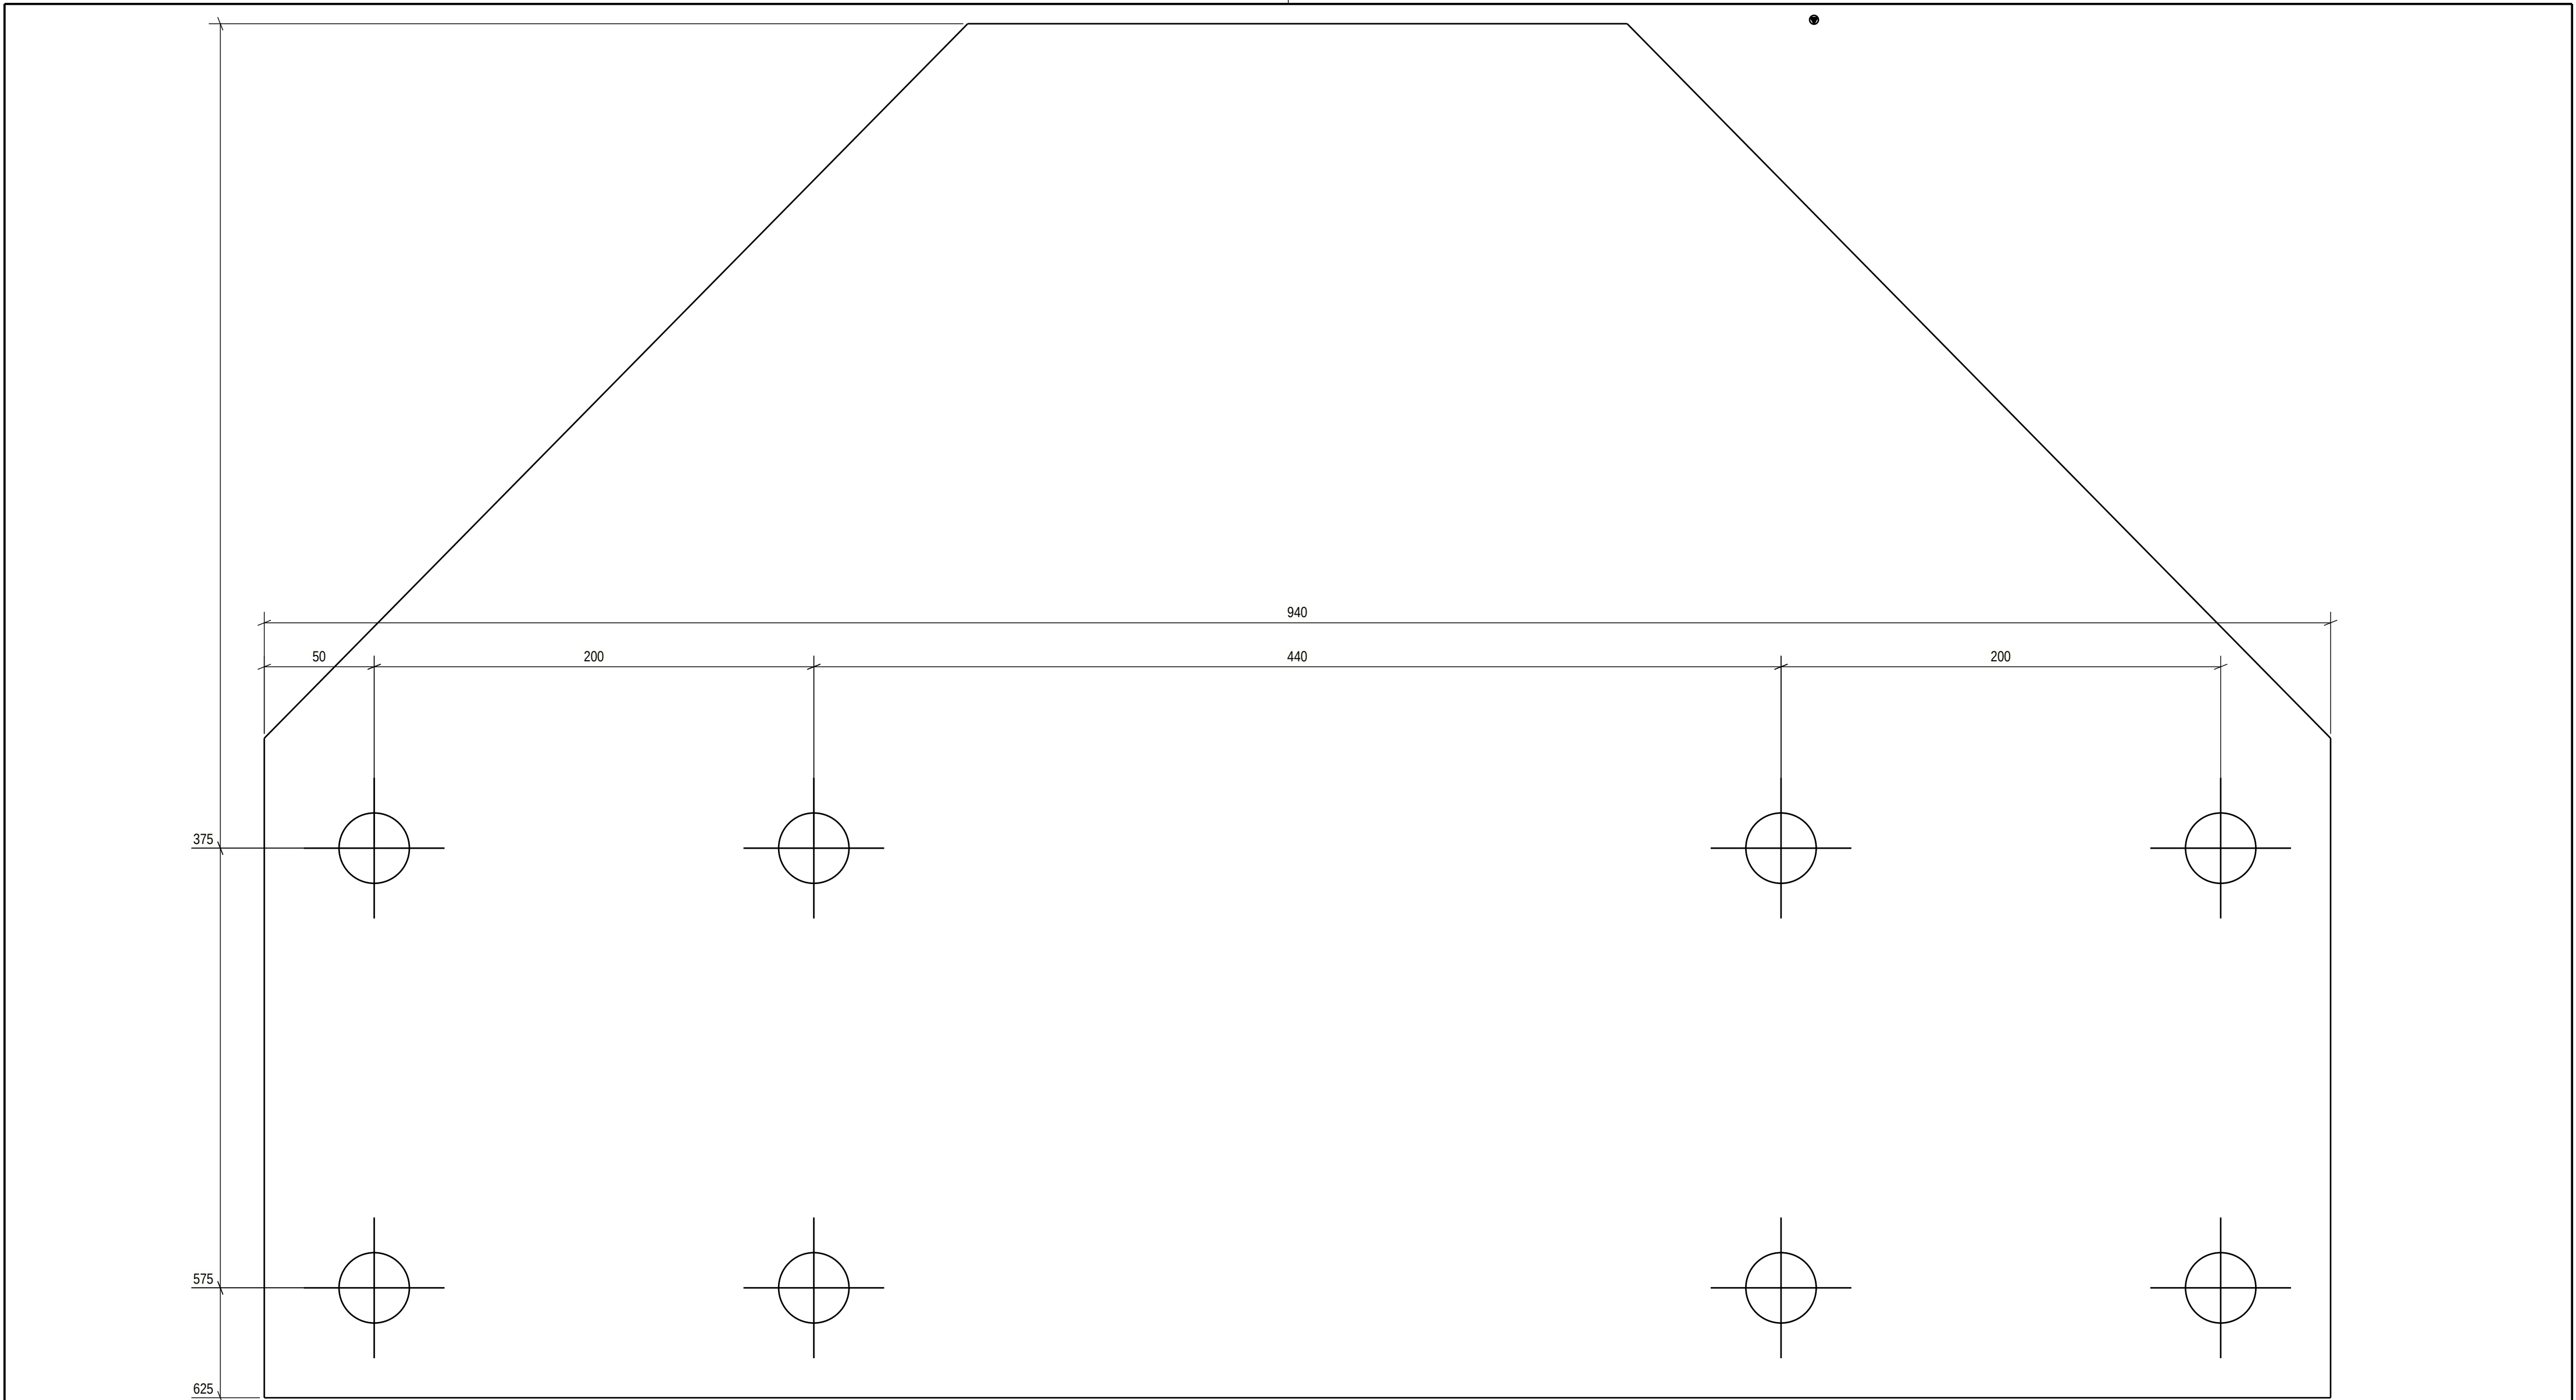

PART LIST FOR ASSEMBLY E51EX-1054, MANUFACTURING AMOUNT 2 PIECES						
PART	PROFILE	MATERIAL	LENGTH [mm]	AREA [m2]	WEIGHT [kg]	PCS
E51EXL-1090	PL5X625	S355J2+N	940	0.98	19.0	1
TOTAL:				0.98	19.0	

Technical fabrication requirements:		Execution class EXC2	
Requirements for fabrication, standard EN1090-2, table A.3 : EXC2		Fabrication tolerances EN 1090-2, Appendix B	
Execution Specification document nr 25019443-ICC250-0600-0660-000005		Special fabrication tolerances Project specification/ shown on drwg.	
Surface preparation grade ISO8501-3, grade P2		Weld inspection, requirements EN 1090-2, Table 24, U>0.5	
Surface treatment ISO12944-5		Extent of NDT, fillet welds MT-EN1290, 20% of welds	
Additional requirements on surface treatment C3.07, EPPUR 240/2		Extent of NDT, butt welds UT, EN-ISO17640, 20% of welds	
Shade RAL 7024 (Graphite Gray)		Extent of NDT for splices not shown on drawing UT, EN-ISO17640, 100% of welds	
Welding of built up steel section Appendix 1 / Project spec.		Requirements on holing EN1090-2 Section 6.6.3	
Welds, if not specified otherwise EN 9692-1, EN 9692-2		Weld class C, EN ISO 5817	
Additional material inspection Shown on drwg.			

PROJECT NAME

Easpring New Materials Oy

FAIR Phase 1




SWECO RAKENNETEKNIikka OY
ILMALANPORTTI 2
00240 HELSINKI





PUH. +358 207 393 000
www.sweco.fi

DRAWING CONTENT		DATE 12.06.2026		ARCHIVING CODE	PAGE	DESIGN GROUP STR
ASSEMBLY DRAWING		DRAWN Alexey Serous		DESIGNER Alexey Serous	APPROVED Pertti Koivumaa	CHECKED Jere Kallosalmi
E51EX-1054		PROJECT NUMBER 25019443		DWG. NO.		REVISION
				E51EX-1054		

For special tolerances of bolt hole location
see specification for steel structures

Approved For Construction

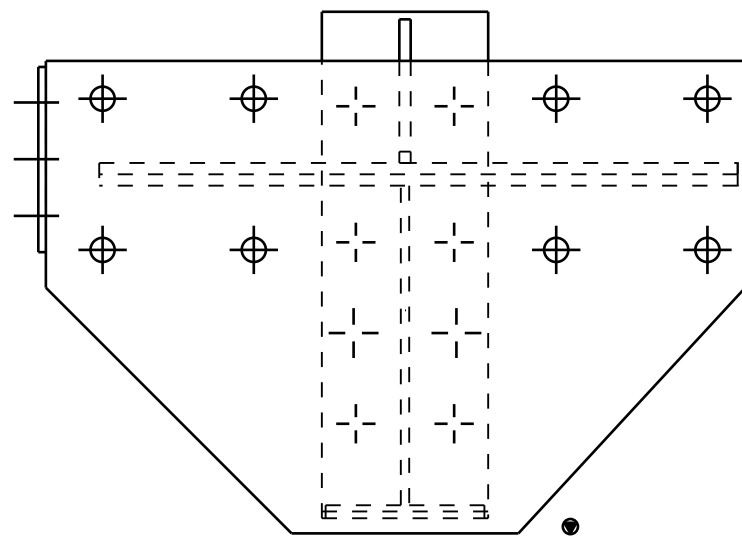

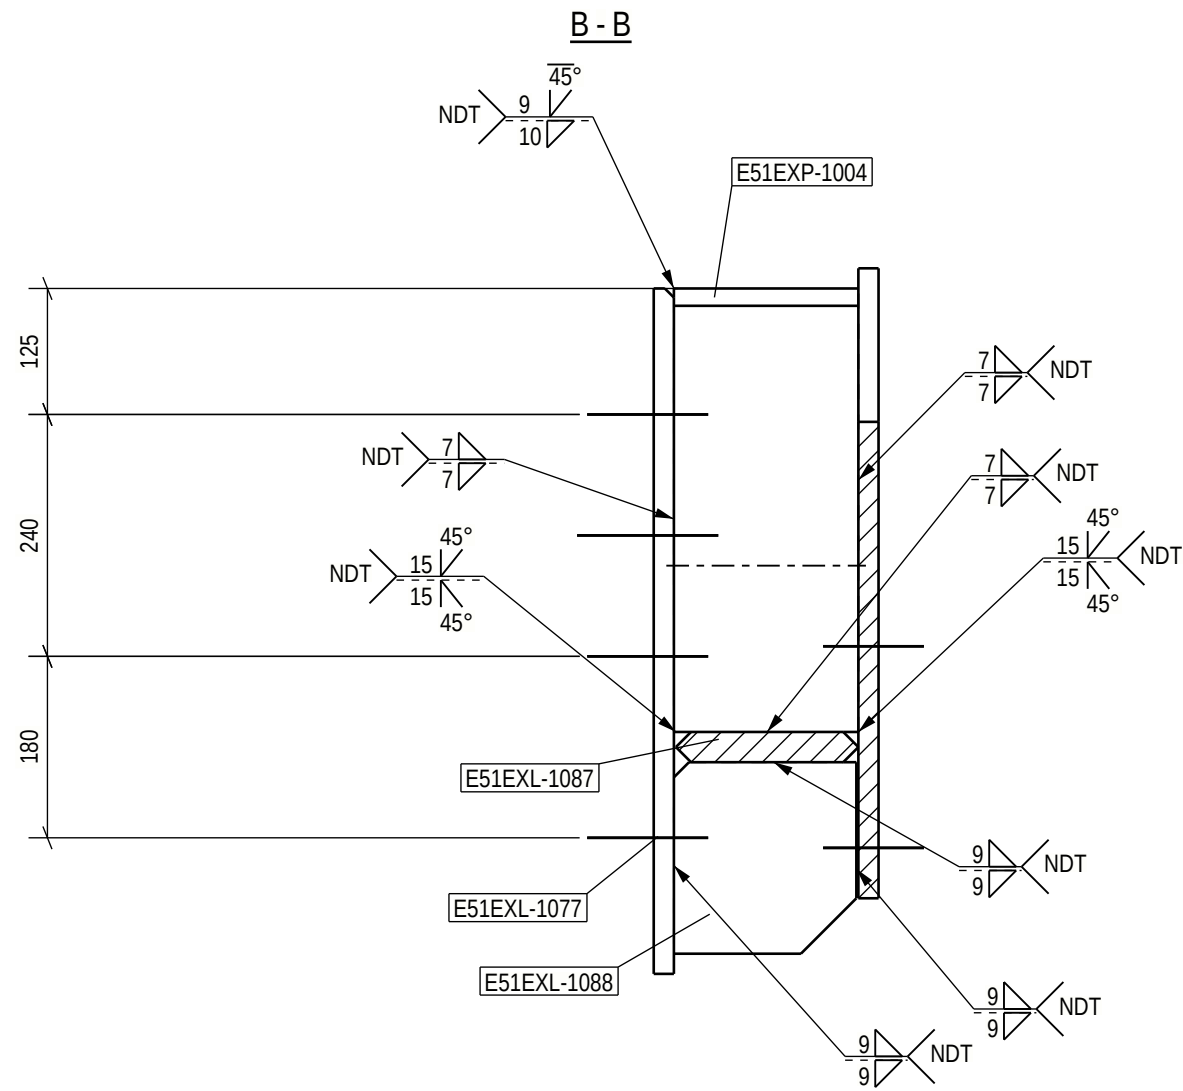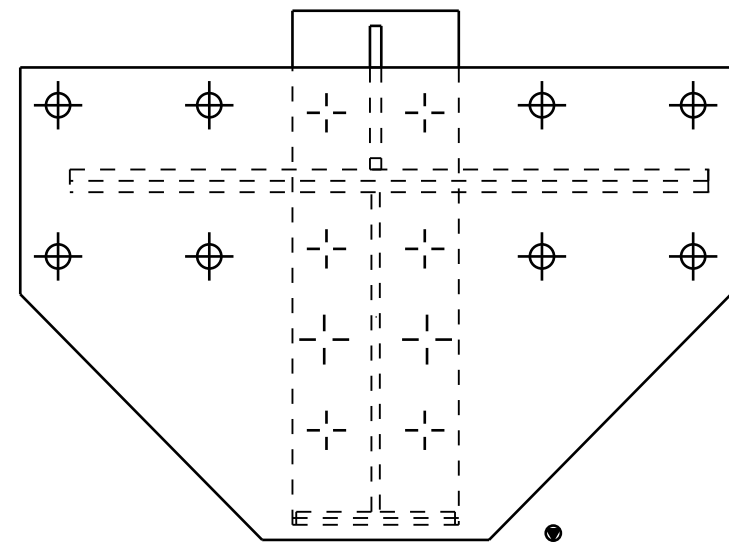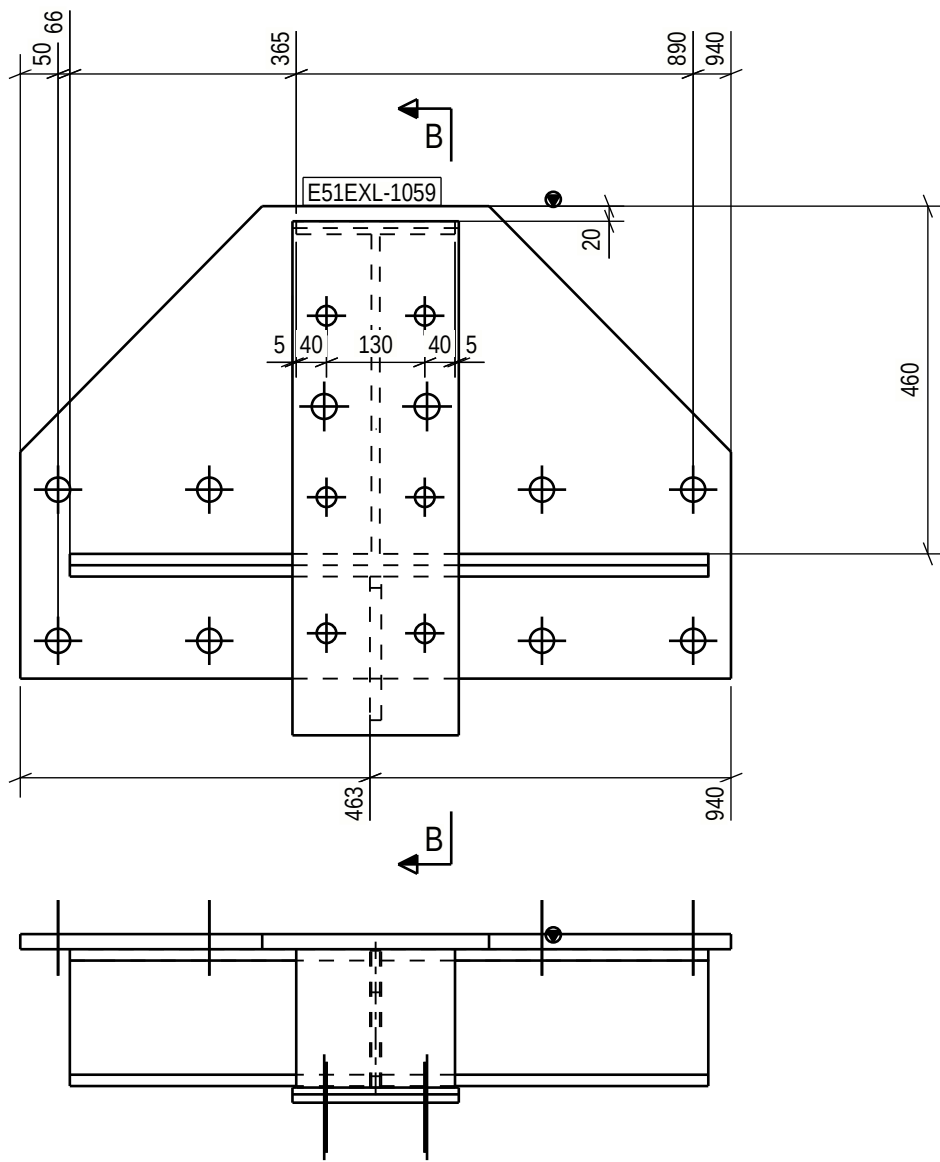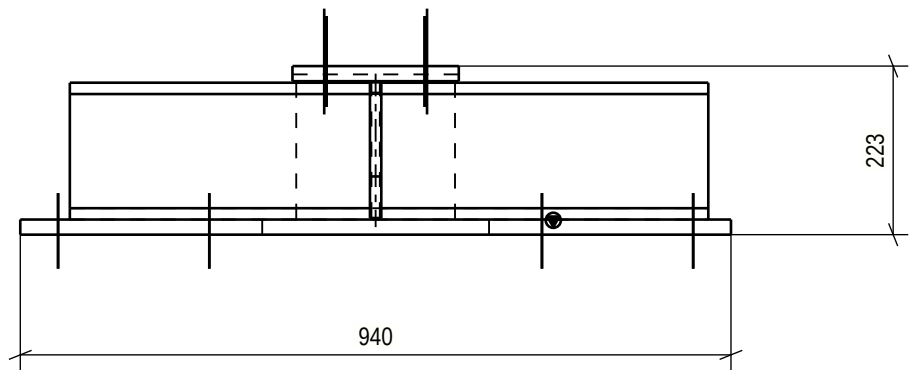

PART LIST FOR ASSEMBLY E51EX-1056, MANUFACTURING AMOUNT 1 PIECES						
PART	PROFILE	MATERIAL	LENGTH [mm]	AREA [m2]	WEIGHT [kg]	PCS
E51EXL-1059	PL20X625	S355J2+N	940	1.02	75.9	1
E51EXL-1077	PL20X220	S355J2+N	680	0.33	23.4	1
E51EXL-1087	PL30X181	S355J2+N	844	0.34	33.0	1
E51EXL-1088	PL15X181	S355J2+N	190	0.08	3.9	1
E51EXP-1004	IPE550	S355J2	183	0.34	19.2	1
TOTAL:				2.11	155.4	


Technical fabrication requirements:		Execution class
Requirements for fabrication, standard EN1090-2, table A.3 : EXC2		EXC2
Execution Specification document nr 25019443-ICC250-0600-0660-000005		Fabrication tolerances EN 1090-2, Appendix B
Surface preparation grade ISO8501-3, grade P2		Special fabrication tolerances Project specification/ shown on drwg.
Surface treatment ISO12944-5		Weld inspection, requirements EN 1090-2, Table 24, U>0.5
Additional requirements on surface treatment C3.07, EPPUR 240/2		Extent of NDT, fillet welds MT-EN1290, 20% of welds
Shade RAL 7024 (Graphite Gray)		Extent of NDT, butt welds UT, EN-ISO17640, 20% of welds
Welding of built up steel section Appendix 1 / Project spec.		Extent of NDT for splices not shown on drawing UT, EN-ISO17640, 100% of welds
Welds, if not specified otherwise EN 9692-1, EN 9692-2		Requirements on holing EN1090-2 Section 6.6.3
		Weld class C, EN ISO 5817
		Additional material inspection Shown on drwg.

Approved For Construction

PROJECT NAME
Easpring New Materials Oy
FAIR Phase 1




SWECO RAKENNETEKNIikka OY
ILMALANPORTTI 2
00240 HELSINKI
PUH. +358 207 393 000
www.sweco.fi

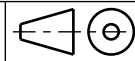


DRAWING CONTENT
ASSEMBLY DRAWING
PLATE
E51EX-1056

DATE	ARCHIVING CODE	PAGE	DESIGN GROUP
12.06.2026			STR
DRAWN	DESIGNER	APPROVED	CHECKED
Alexey Serous	Alexey Serous	Pertti Koivumaa	Jere Kallosalmi
PROJECT NUMBER	DWG. NO.	REVISION	
25019443	E51EX-1056		

PART LIST FOR ASSEMBLY E51EX-1058, MANUFACTURING AMOUNT 48 PIECES						
PART	PROFILE	MATERIAL	LENGTH [mm]	AREA [m2]	WEIGHT [kg]	PCS
E51EXL-1050	PL2X220	S355J2+N	530	0.20	1.5	1
TOTAL:				0.20	1.5	

 

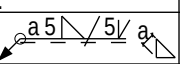
Technical fabrication requirements:		Execution class
Requirements for fabrication, standard	Fabrication tolerances	EXC2
EN1090-2, table A.3 : EXC2	EN 1090-2, Appendix B	
Execution Specification document nr	Special fabrication tolerances	
25019443-ICC250-0600-0660-000005	Project specification/ shown on drwg.	
Surface preparation grade	Weld inspection, requirements	
ISO8501-3, grade P2	EN 1090-2,Table 24, U>0.5	
Surface treatment	Extent of NDT, filled welds	
ISO12944-5	MT-EN1290,20% of welds	
Additional requirements on surface treatment	Extent of NDT, butt welds	
C3.07, EPPUR 240/2	UT, EN-ISO17640, 20% of welds	
Shade	Extent of NDT for splices not shown on drawing	
RAL 7024 (Graphite Gray)	UT, EN-ISO17640, 100%of welds	
Welding of built up steel section	Requirements on holing	
Appendix 1 / Project spec.	EN1090-2 Section 6.6.3	
Welds, if not specified otherwise	Weld class	
EN 9692-1, EN 9692-2	C, EN ISO 5817	Additional material inspection Shown on drwg.

Approved For Construction

Easpring New Materials Oy
FAIR Phase 1




SWECO RAKENNETEKNIikka OY
ILMALANPORTTI 2
00240 HELSINKI
PUH. +358 207 393 000
www.sweco.fi

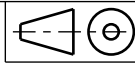

DRAWING CONTENT			
ASSEMBLY DRAWING			
PLATE			
E51EX-1058			
DATE	ARCHIVING CODE	PAGE	DESIGN GROUP
12.06.2026			STR
DRAWN	DESIGNER	APPROVED	CHECKED
Alexey Serous	Alexey Serous	Pertti Koivumaaanaho	Jere Kallosalmi
PROJECT NUMBER	DWG. NO.	REVISION	
25019443	E51EX-1058		

PART LIST FOR ASSEMBLY E51EX-1059, MANUFACTURING AMOUNT 2 PIECES						
PART	PROFILE	MATERIAL	LENGTH [mm]	AREA [m2]	WEIGHT [kg]	PCS
E51EXL-1052	PL2X220	S355J2+N	530	0.19	1.5	1
TOTAL:				0.19	1.5	

 


Technical fabrication requirements:		Execution class
Requirements for fabrication, standard	Fabrication tolerances	EXC2
EN1090-2, table A.3 : EXC2	EN 1090-2, Appendix B	
Execution Specification document nr	Special fabrication tolerances	
25019443-ICC250-0600-0660-000005	Project specification/ shown on drwg.	
Surface preparation grade	Weld inspection, requirements	
ISO8501-3, grade P2	EN 1090-2,Table 24, U>0.5	
Surface treatment	Extent of NDT, fillet welds	
ISO12944-5	MT-EN1290,20% of welds	
Additional requirements on surface treatment	Extent of NDT, butt welds	
C3.07, EPPUR 240/2	UT, EN-ISO17640, 20% of welds	
Shade	Extent of NDT for splices not shown on drawing	
RAL 7024 (Graphite Gray)	UT, EN-ISO17640, 100%of welds	
Welding of built up steel section	Requirements on holing	
Appendix 1 / Project spec.	EN1090-2 Section 6.6.3	
Welds, if not specified otherwise	Weld class	
EN 9692-1, EN 9692-2	C, EN ISO 5817	Additional material inspection Shown on drwg.

Approved For Construction

Easpring New Materials Oy
FAIR Phase 1




SWECO RAKENNETEKNIikka OY
ILMALANPORTTI 2
00240 HELSINKI
PUH. +358 207 393 000
www.sweco.fi

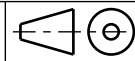

DRAWING CONTENT			
ASSEMBLY DRAWING			
PLATE			
E51EX-1059			
DATE	ARCHIVING CODE	PAGE	DESIGN GROUP
12.06.2026			STR
DRAWN	DESIGNER	APPROVED	CHECKED
Alexey Serous	Alexey Serous	Pertti Koivumaaanaho	Jere Kallosalmi
PROJECT NUMBER	DWG. NO.	REVISION	
25019443	E51EX-1059		

PART LIST FOR ASSEMBLY E51EX-1060, MANUFACTURING AMOUNT 16 PIECES						
PART	PROFILE	MATERIAL	LENGTH [mm]	AREA [m2]	WEIGHT [kg]	PCS
E51EXL-1079	PL12X390	S355J2+N	440	0.36	16.2	1
TOTAL:				0.36	16.2	

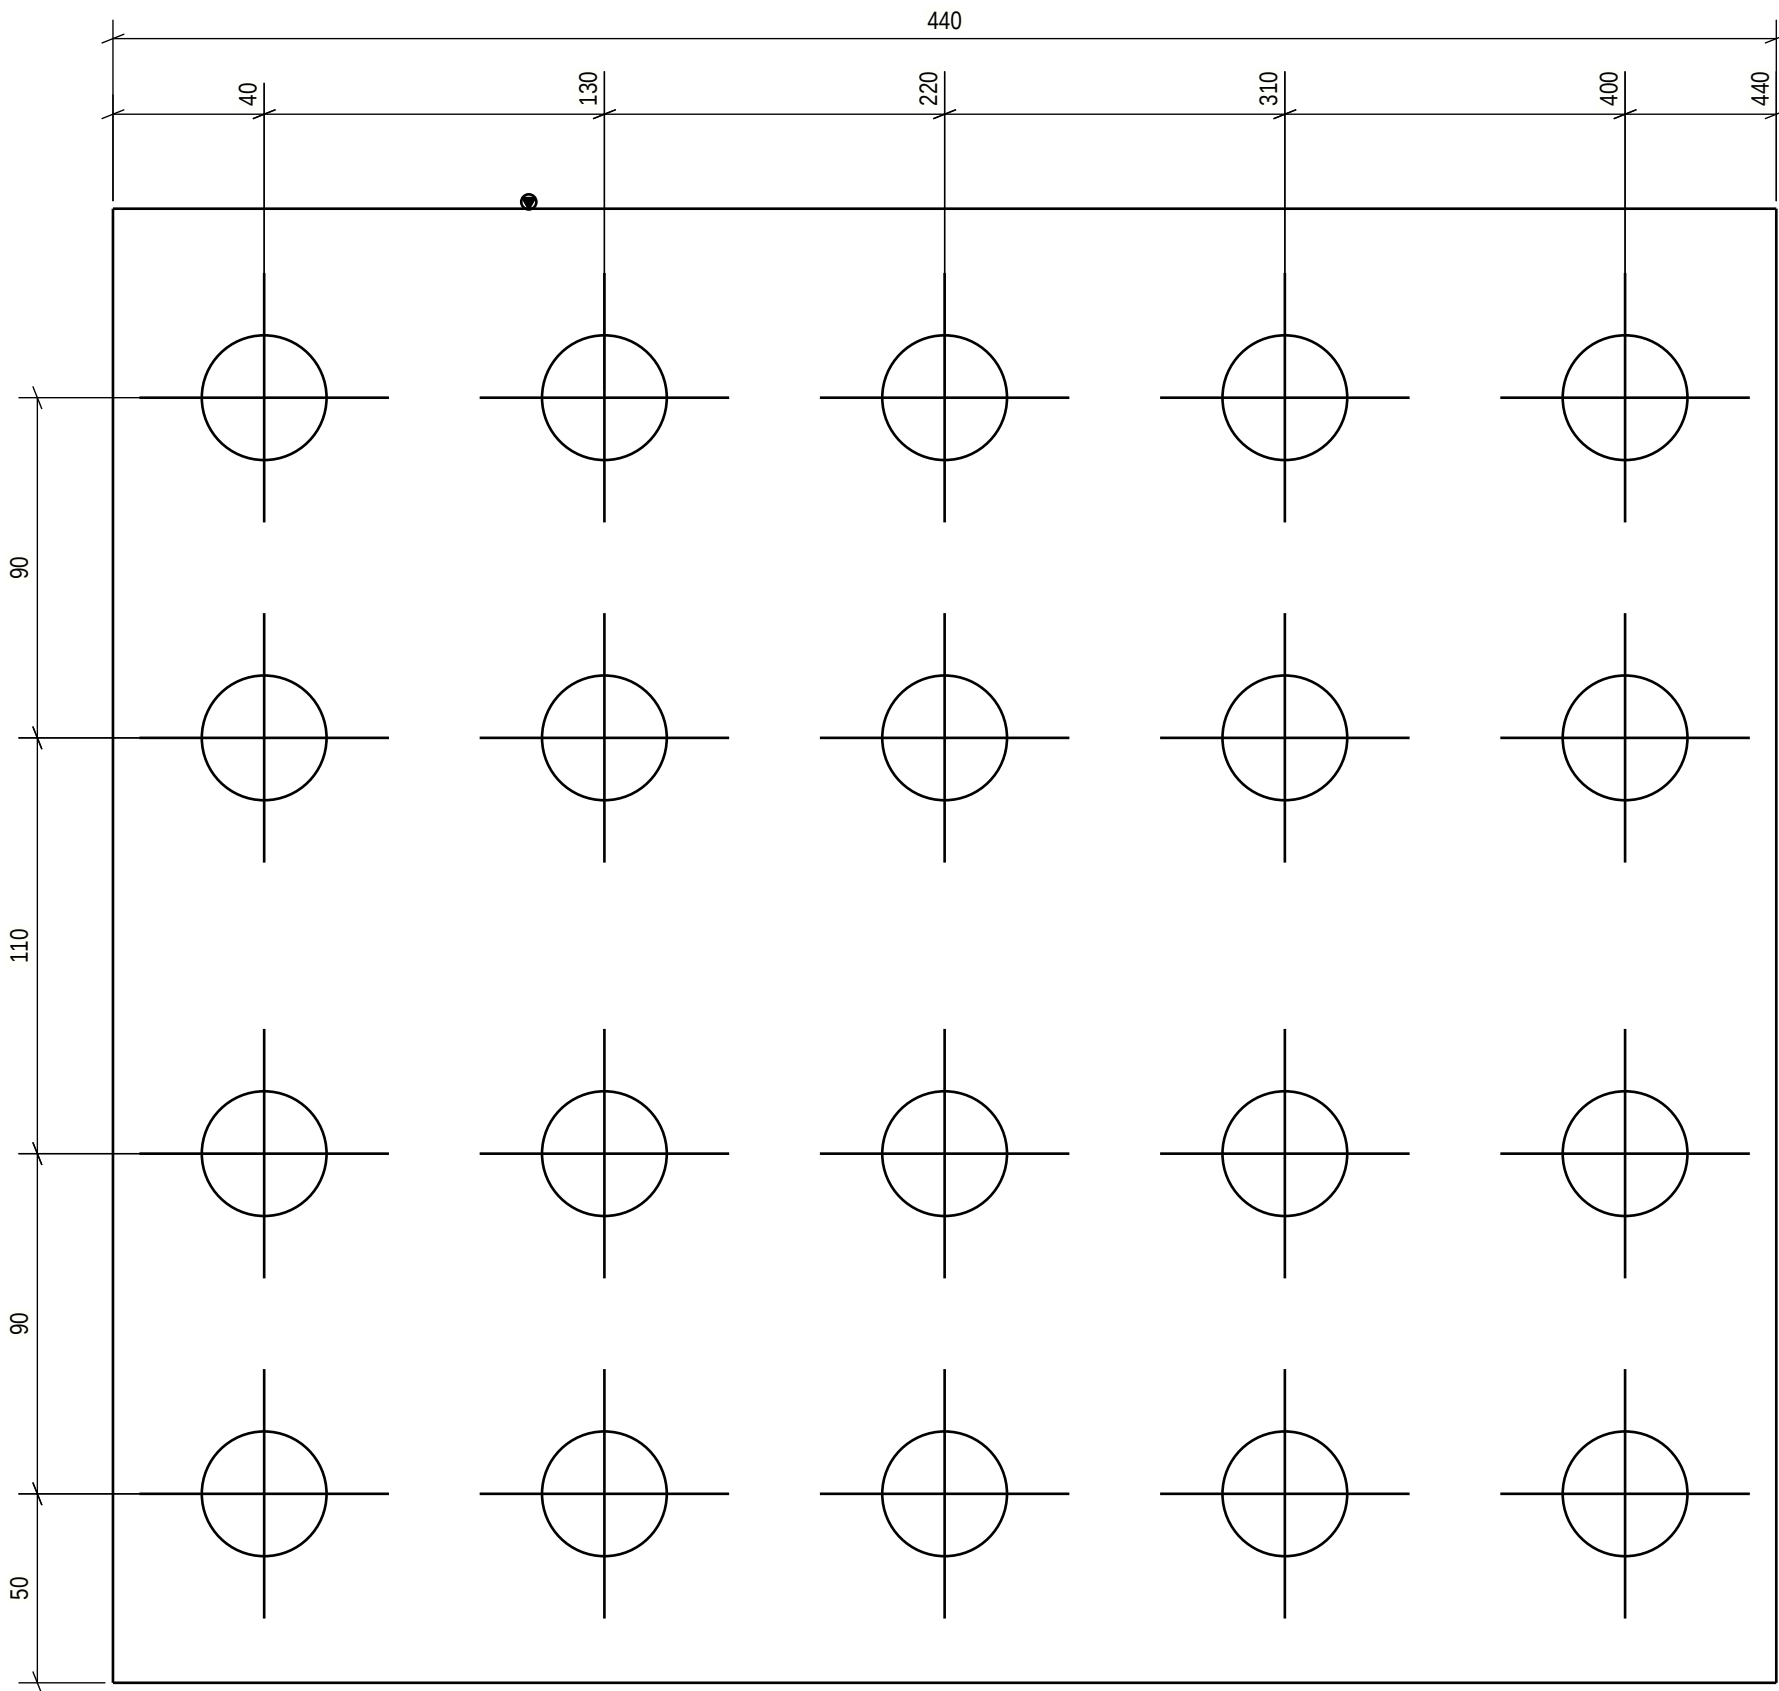


Technical fabrication requirements:		Execution class	
Requirements for fabrication, standard EN1090-2, table A.3 : EXC2		EXC2	
Execution Specification document nr 25019443-ICC250-0600-0660-000005		Fabrication tolerances EN 1090-2, Appendix B	
Surface preparation grade ISO8501-3, grade P2		Special fabrication tolerances Project specification/ shown on drwg.	
Surface treatment ISO12944-5		Weld inspection, requirements EN 1090-2,Table 24, U>0.5	
Additional requirements on surface treatment C3.07, EPPUR 240/2		Extent of NDT, fillet welds MT-EN1290,20% of welds	
Shade RAL 7024 (Graphite Gray)		Extent of NDT, butt welds UT, EN-ISO17640, 20% of welds	
Welding of built up steel section Appendix 1 / Project spec.		Extent of NDT for splices not shown on drawing UT, EN-ISO17640, 100%of welds	
Welds, if not specified otherwise EN 9692-1, EN 9692-2		Requirements on holing EN1090-2 Section 6.6.3	
		Weld class C, EN ISO 5817	
		Additional material inspection Shown on drwg.	

Approved For Construction


Easpring New Materials Oy
FAIR Phase 1



SWECO RAKENNETEKNIikka OY
ILMALANPORTTI 2
00240 HELSINKI
PUH. +358 207 393 000
www.sweco.fi

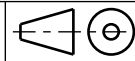

DRAWING CONTENT			
ASSEMBLY DRAWING			
PLATE			
E51EX-1060			
DATE 12.06.2026	ARCHIVING CODE	PAGE	DESIGN GROUP STR
DRAWN Alexey Serous	DESIGNER Alexey Serous	APPROVED Pertti Koivumaaaho	CHECKED Jere Kallosalmi
PROJECT NUMBER 25019443	DWG. NO.	REVISION	E51EX-1060

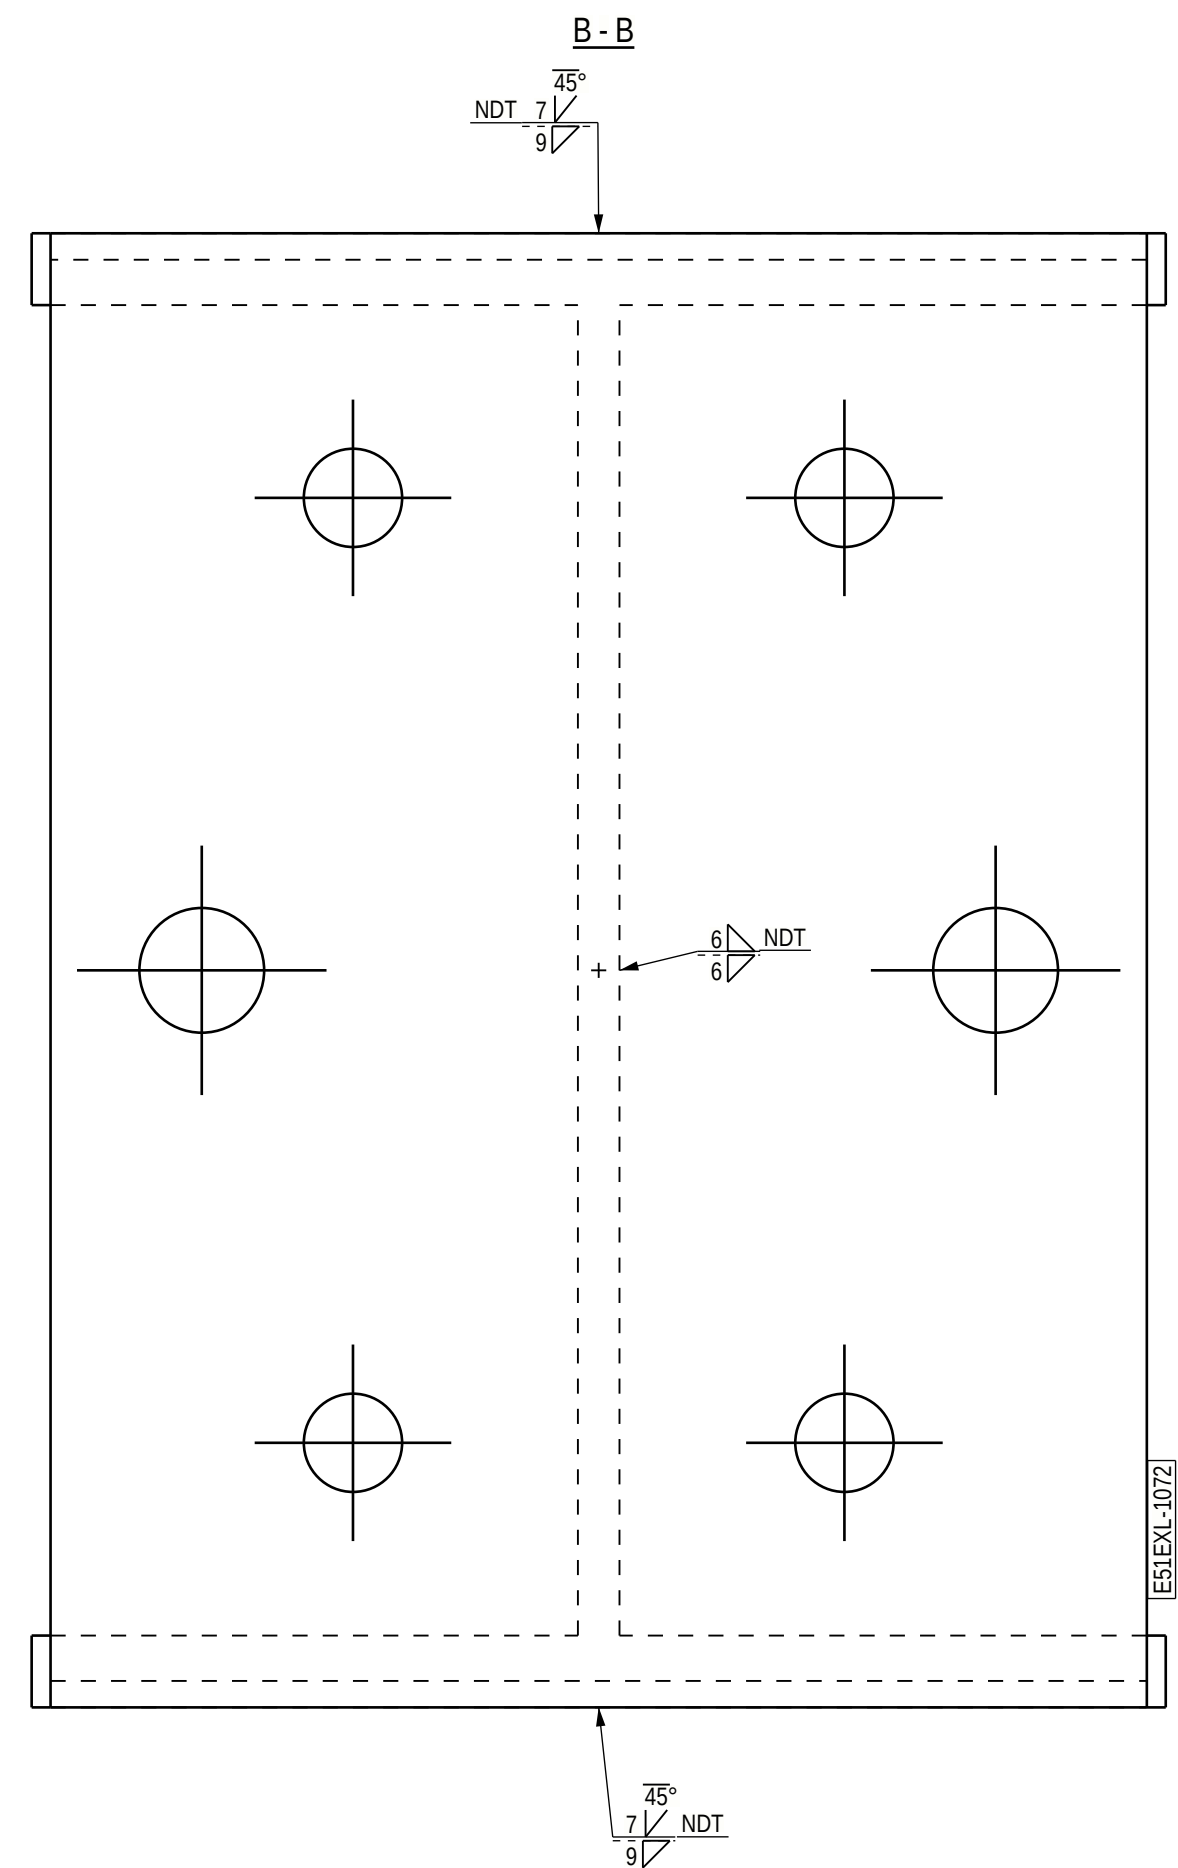

Technical fabrication requirements:		Execution class	
		EXC2	
Approved For Construction			
Requirements for fabrication, standard EN1090-2, table A.3 : EXC2		Fabrication tolerances EN 1090-2, Appendix B	
Execution Specification document nr 25019443-ICC250-0600-0660-000005		Special fabrication tolerances Project specification/ shown on drwg.	
Surface preparation grade ISO8501-3, grade P2		Weld inspection, requirements EN 1090-2, Table 24, U>0.5	
Surface treatment ISO12944-5		Extent of NDT, fillet welds MT-EN1290, 20% of welds	
Additional requirements on surface treatment C3.07, EPPUR 240/2		Extent of NDT, butt welds UT, EN-ISO17640, 20% of welds	
Shade RAL 7024 (Graphite Gray)		Extent of NDT for splices not shown on drawing UT, EN-ISO17640, 100% of welds	
Welding of built up steel section Appendix 1 / Project spec.		Requirements on holding EN1090-2 Section 6.6.3	
Welds, if not specified otherwise EN 9692-1, C, EN 9692-2		Weld class C, EN ISO 5817	
a 5 / 5 / a		Additional material inspection Shown on drwg.	
PROJECT NAME Easpring New Materials Oy FAIR Phase 1		DRAWING CONTENT ASSEMBLY DRAWING Beam E51EX-1061	
DATE 12.06.2026		ARCHIVING CODE PAGE	
DRAWN Aleyex Serous		DESIGNER Aleyex Serous	
PROJECT NUMBER 25019443		DESIGN GROUP STR	
PUH. : +358 207 393 000 www.sweco.fi		APPROVED Pertti Koivumäenaho	
SWECO Sustainable engineering and design		CHECKED Jere Kalliosalmi	
SWECO Sustainable engineering and design		REVISION E51EX-1061	

For special tolerances of bolt hole location
see specification for steel structures


Approved For Construction

PART LIST FOR ASSEMBLY E51EX-1062, MANUFACTURING AMOUNT 2 PIECES						
PART	PROFILE	MATERIAL	LENGTH [mm]	AREA [m2]	WEIGHT [kg]	PCS
E51EXL-1051	PL2X200	S355J2+N	495	0.16	1.2	1
			TOTAL:	0.16	1.2	

		Execution class	
Technical fabrication requirements:		EXC2	
Requirements for fabrication, standard EN1090-2, table A.3 : EXC2 Execution Specification document nr. 25019443-ICC250-0600-0660-000005 Surface preparation grade ISO8501-3, grade P2 Surface treatment ISO12944-5 Additional requirements on surface treatment C3.07, EPPUR 240/2 Shade RAL 7024 (Graphite Gray) Welding of built up steel section Appendix 1 / Project spec. Welds, if not specified otherwise EN 9692-1, EN 9692-2		Fabrication tolerances EN 1090-2, Appendix B Special fabrication tolerances Project specification/ shown on drwg. Weld inspection, requirements EN 1090-2, Table 24, U>0.5 Extent of NDT, fillet welds MT-EN1290, 20% of welds Extent of NDT, butt welds UT, EN-ISO17640, 20% of welds Extent of NDT for splices not shown on drawing UT-EN-ISO17640, 100% of welds Requirements on healing EN1090-2 Section 6.6.3 Weld class EN ISO 5817	
Additional material inspection Shown on drwg.			

Approved For Construction

PROJECT NAME
Easpring New Materials Oy
FAIR Phase 1

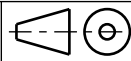


DRAWING CONTENT

ASSEMBLY DRAWING
PLATE
E51EX-1062

 SWECO Sustainable engineering and design	SWECO RAKENNETEKNIIKKA OY ILMALANPORTTI 2 00240 HELSINKI PUH. +358 207 393 000 www.sweco.fi	DATE 12.06.2026	ARCHIVING CODE	PAGE	DESIGN GROUP STR
	DRAWN Alexey Serous	DESIGNER Alexey Serous	APPROVED Pertti Koivumäenaho	CHECKED Jere Kalliosalmi	
PROJECT NUMBER 25019443		DWG. NO. E51EX-1062			
		REVISION			

PART LIST FOR ASSEMBLY E51EX-1063, MANUFACTURING AMOUNT 8 PIECES						
PART	PROFILE	MATERIAL	LENGTH [mm]	AREA [m2]	WEIGHT [kg]	PCS
E51EXL-1084	PL5X105	S355J2+N	646	0.14	2.7	1
TOTAL:				0.14	2.7	

 


Technical fabrication requirements:		Execution class
Requirements for fabrication, standard	Fabrication tolerances	EXC2
EN1090-2, table A.3 : EXC2	EN 1090-2, Appendix B	
Execution Specification document nr	Special fabrication tolerances	
25019443-ICC250-0600-0660-000005	Project specification/ shown on drwg.	
Surface preparation grade	Weld inspection, requirements	
ISO8501-3, grade P2	EN 1090-2,Table 24, U>0.5	
Surface treatment	Extent of NDT, fillet welds	
ISO12944-5	MT-EN1290,20% of welds	
Additional requirements on surface treatment	Extent of NDT, butt welds	
C3.07, EPPUR 240/2	UT, EN-ISO17640, 20% of welds	
Shade	Extent of NDT for splices not shown on drawing	
RAL 7024 (Graphite Gray)	UT, EN-ISO17640, 100%of welds	
Welding of built up steel section	Requirements on holing	
Appendix 1 / Project spec.	EN1090-2 Section 6.6.3	
Welds, if not specified otherwise	Weld class	
EN 9692-1, EN 9692-2	C, EN ISO 5817	Additional material inspection Shown on drwg.

For special tolerances of bolt hole location
see specification for steel structures
Approved For Construction

PROJECT NAME			DRAWING CONTENT			
Easpring New Materials Oy			ASSEMBLY DRAWING			
FAIR Phase 1			PLATE			
			E51EX-1063			
 SWECO Sustainable engineering and design		SWECO RAKENNETEKNIikka OY ILMALANPORTTI 2 00240 HELSINKI PUH. +358 207 393 000 www.sweco.fi	DATE	ARCHIVING CODE	PAGE	DESIGN GROUP
			12.06.2026			STR
			DRAWN	DESIGNER	APPROVED	CHECKED
			Alexey Serous	Alexey Serous	Pertti Koivumaaanaho	Jere Kalliosalmi
			PROJECT NUMBER	DWG. NO.	REVISION	
			25019443	E51EX-1063		

PART LIST FOR ASSEMBLY E51EX-1064, MANUFACTURING AMOUNT 32 PIECES						
PART	PROFILE	MATERIAL	LENGTH [mm]	AREA [m2]	WEIGHT [kg]	PCS
E51EXL-1017	PL8X210	S355J2+N	375	0.17	4.9	1
TOTAL:				0.17	4.9	

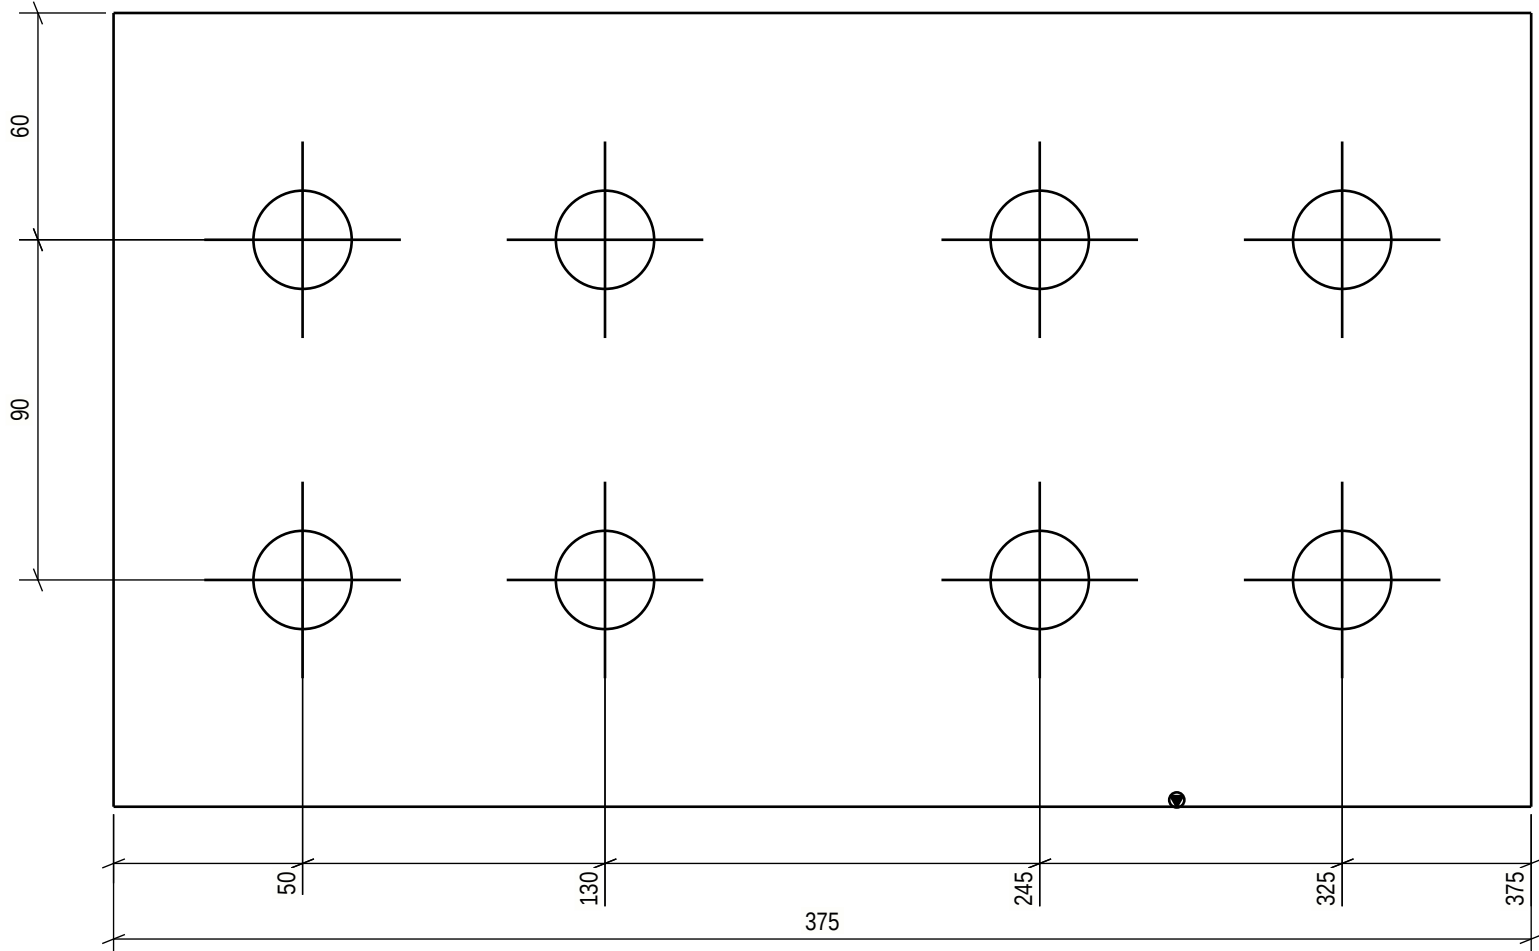


Technical fabrication requirements:		Execution class	
Requirements for fabrication, standard		EN 1090-2, Appendix B	
EN1090-2, table A.3 : EXC2		Special fabrication tolerances	
Execution Specification document nr		Project specification/ shown on drwg.	
25019443-ICC250-0600-0660-000005		Weld inspection, requirements	
Surface preparation grade		EN 1090-2,Table 24, U>0.5	
ISO8501-3, grade P2		Extent of NDT, fillet welds	
Surface treatment		MT-EN1290,20% of welds	
ISO12944-5		Extent of NDT, butt welds	
Additional requirements on surface treatment		UT, EN-ISO17640, 20% of welds	
C3.07, EPPUR 240/2		UT, EN-ISO17640, 100%of welds	
Shade		Requirements on holing	
RAL 7024 (Graphite Gray)		EN1090-2 Section 6.6.3	
Welding of built up steel section		Weld class	
Appendix 1 / Project spec.		C, EN ISO 5817	
Welds, if not specified otherwise		Additional material inspection	
EN 9692-1, EN 9692-2		Shown on drwg.	

Approved For Construction

Easpring New Materials Oy
FAIR Phase 1




SWECO RAKENNETEKNIikka OY
ILMALANPORTTI 2
00240 HELSINKI
PUH. +358 207 393 000
www.sweco.fi

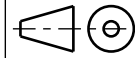

DRAWING CONTENT
ASSEMBLY DRAWING
PLATE
E51EX-1064

DATE	ARCHIVING CODE	PAGE	DESIGN GROUP
12.06.2026			STR
DRAWN	DESIGNER	APPROVED	CHECKED
Alexey Serous	Alexey Serous	Pertti Koivumaaanaho	Jere Kallosalmi
PROJECT NUMBER	DWG. NO.	REVISION	
25019443	E51EX-1064		

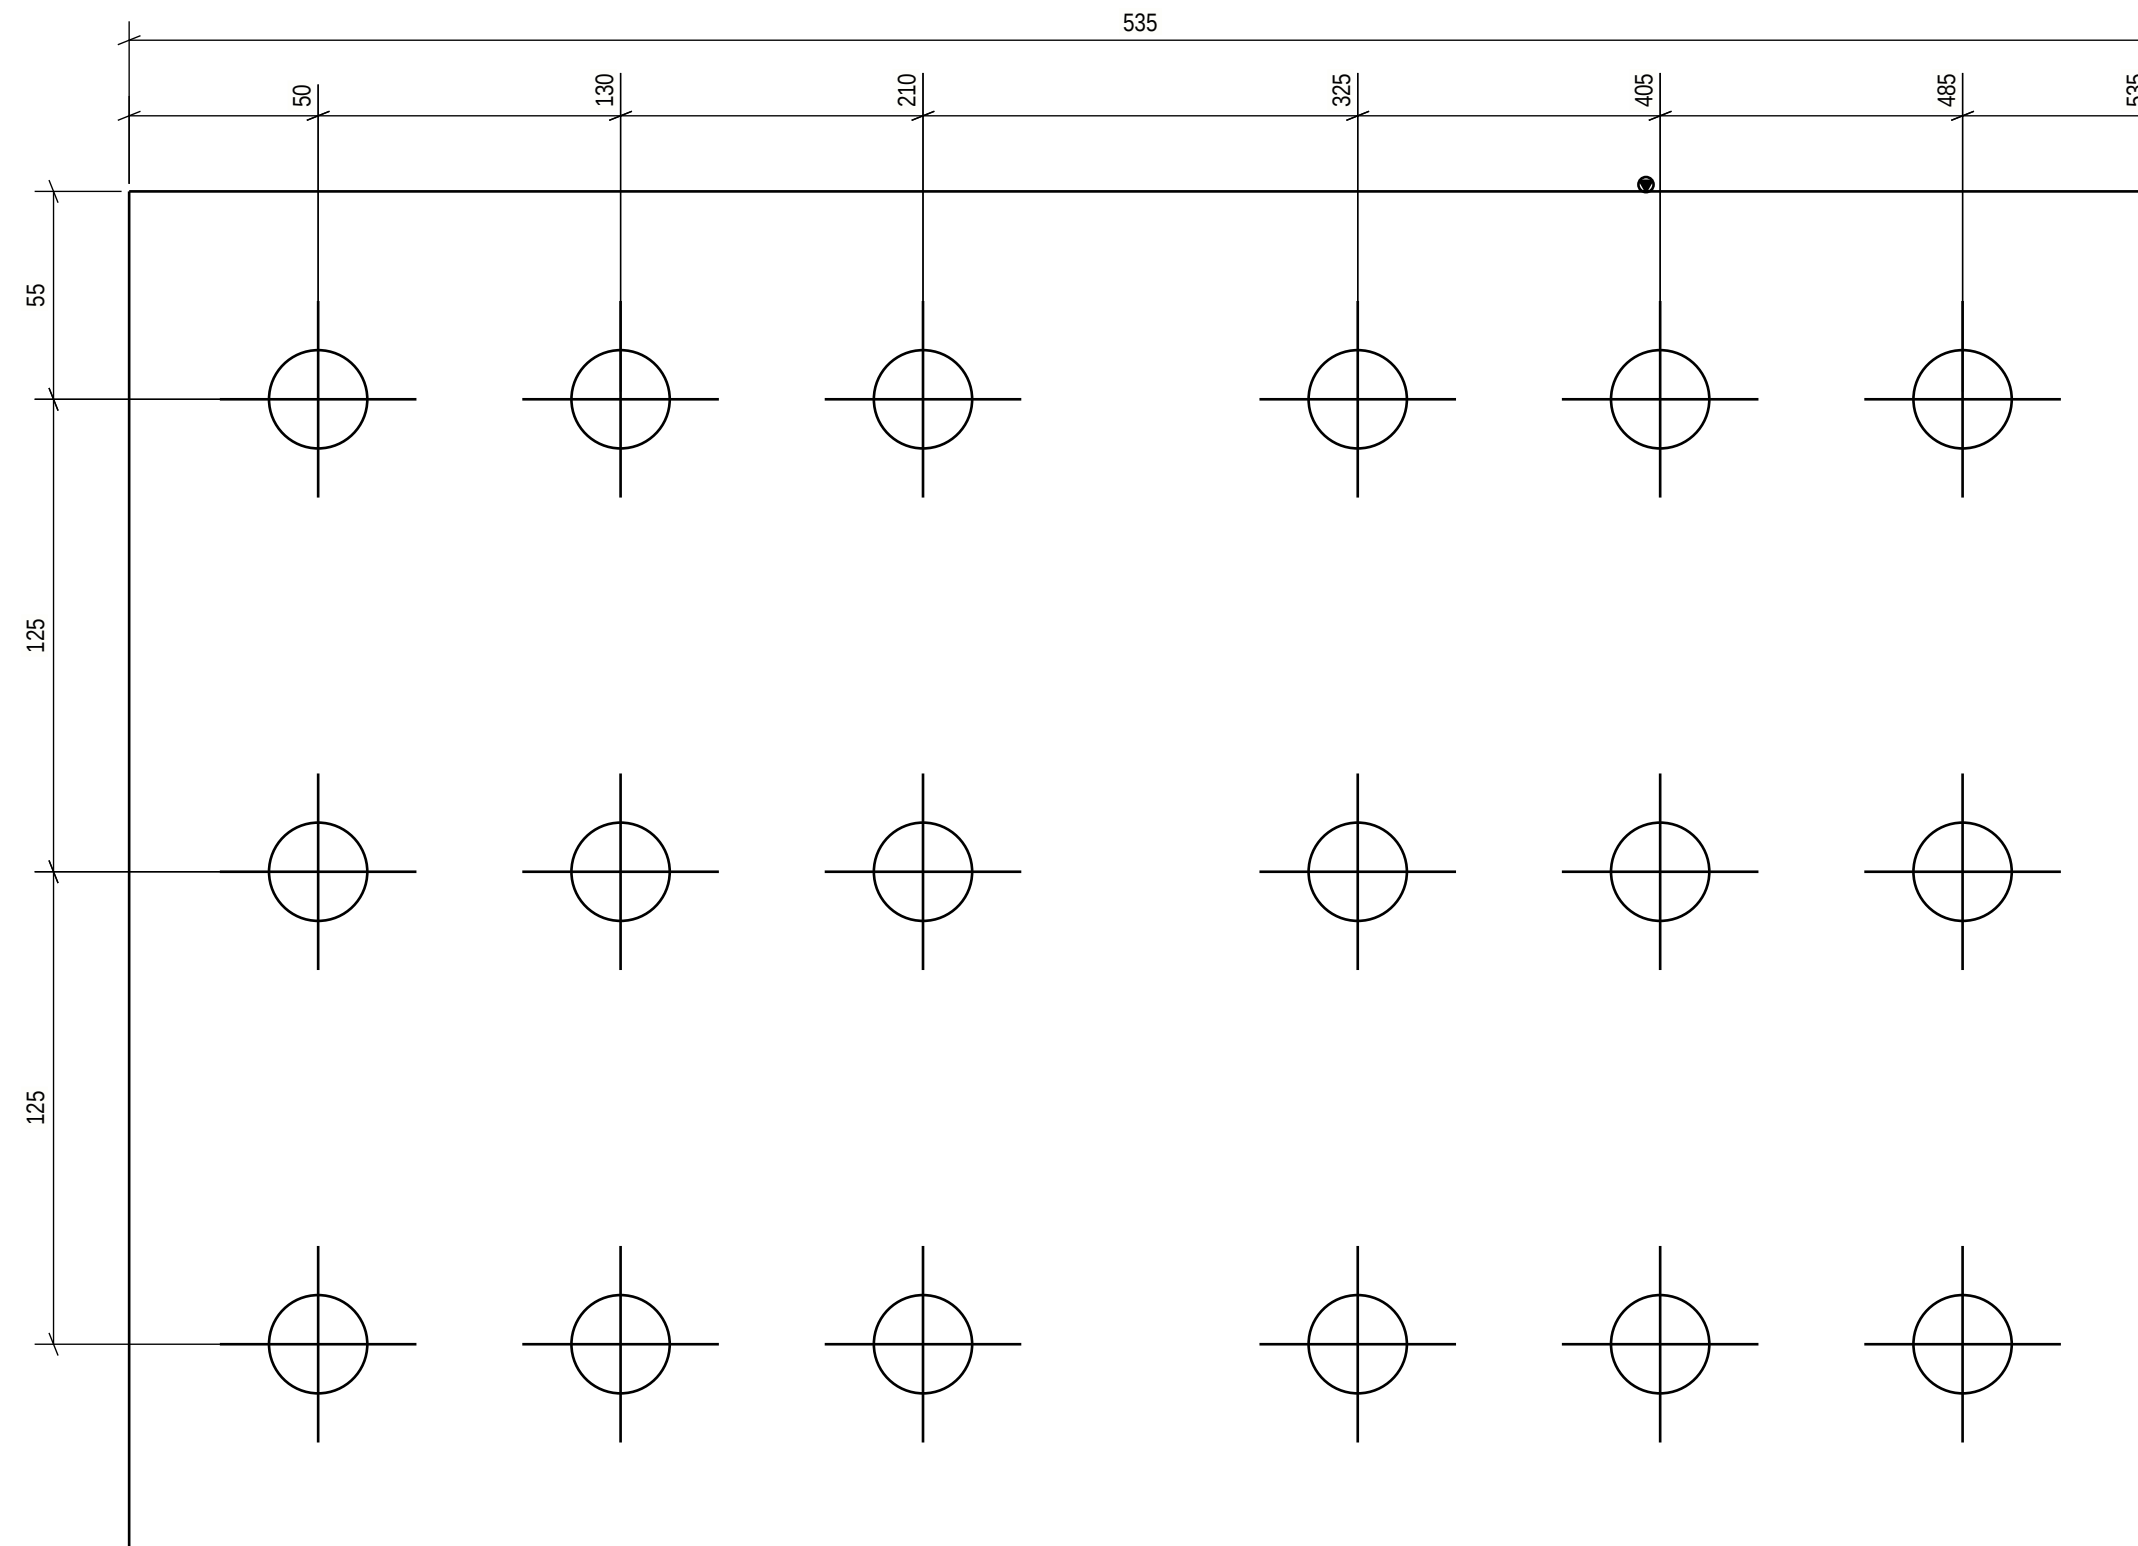


PART LIST FOR ASSEMBLY E51EX-1065, MANUFACTURING AMOUNT 58 PIECES						
PART	PROFILE	MATERIAL	LENGTH [mm]	AREA [m2]	WEIGHT [kg]	PCS
E51EXL-1018	PL15X360	S355J2+N	535	0.41	22.7	1
			TOTAL:	0.41	22.7	

		Execution class	
Technical fabrication requirements:		EXC2	
Requirements for fabrication, standard EN1090-2, table A.3 : EXC2		Fabrication tolerances	
Execution Specification document nr 25019443-ICC250-0600-0660-000005		EN 1090-2, Appendix B	
Surface preparation grade ISO8501-3, grade P2		Special fabrication tolerances	
Surface treatment ISO12944-5		Project specification/ shown on drwg.	
Additional requirements on surface treatment C3.07, EPPUR 240/2		Weld inspection, requirements	
Shade RAL 7024 (Graphite Gray)		EN 1090-2, Table 24, U>0.5	
Welding of built up steel section Appendix 1 / Project spec.		Extent of NDT, fillet welds	
Welds, if not specified otherwise EN 9692-1, EN 9692-2		MT-EN1290, 20% of welds	
		Extent of NDT, butt welds	
		UT, EN-ISO17640, 20% of welds	
		Extent of NDT for splices not shown on drawing	
		UT, EN-ISO17640, 100% of welds	
		Requirements on holding	
		EN1090-2 Section 6.6.3	
		Weld class	
		C, EN ISO 5817	
		Additional material inspection	
		Shown on drwg.	

Approved For Construction


PROJECT NAME
Easpring New Materials Oy
FAIR Phase 1

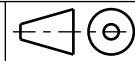

DRAWING CONTENT
ASSEMBLY DRAWING
PLATE
E51EX-1065

 SWECO Sustainable engineering and design	SWECO RAKENNETEKNIikka OY ILMALANPORTTI 2 00240 HELSINKI PUH. +358 207 393 000 www.sweco.fi	DATE	ARCHIVING CODE	PAGE	DESIGN GROUP
		12.06.2026			STR
		DRAWN	DESIGNER	APPROVED	CHECKED
		Alexey Serous	Alexey Serous	Pertti Koivumäenaho	Jere Kalliosalmi
		PROJECT NUMBER	DWG. NO.	REVISION	
		25019443	E51EX-1065		

PART LIST FOR ASSEMBLY E51EX-1066, MANUFACTURING AMOUNT 8 PIECES						
PART	PROFILE	MATERIAL	LENGTH [mm]	AREA [m2]	WEIGHT [kg]	PCS
E51EXL-1020	PL15X210	S355J2+N	375	0.18	9.3	1
TOTAL:				0.18	9.3	

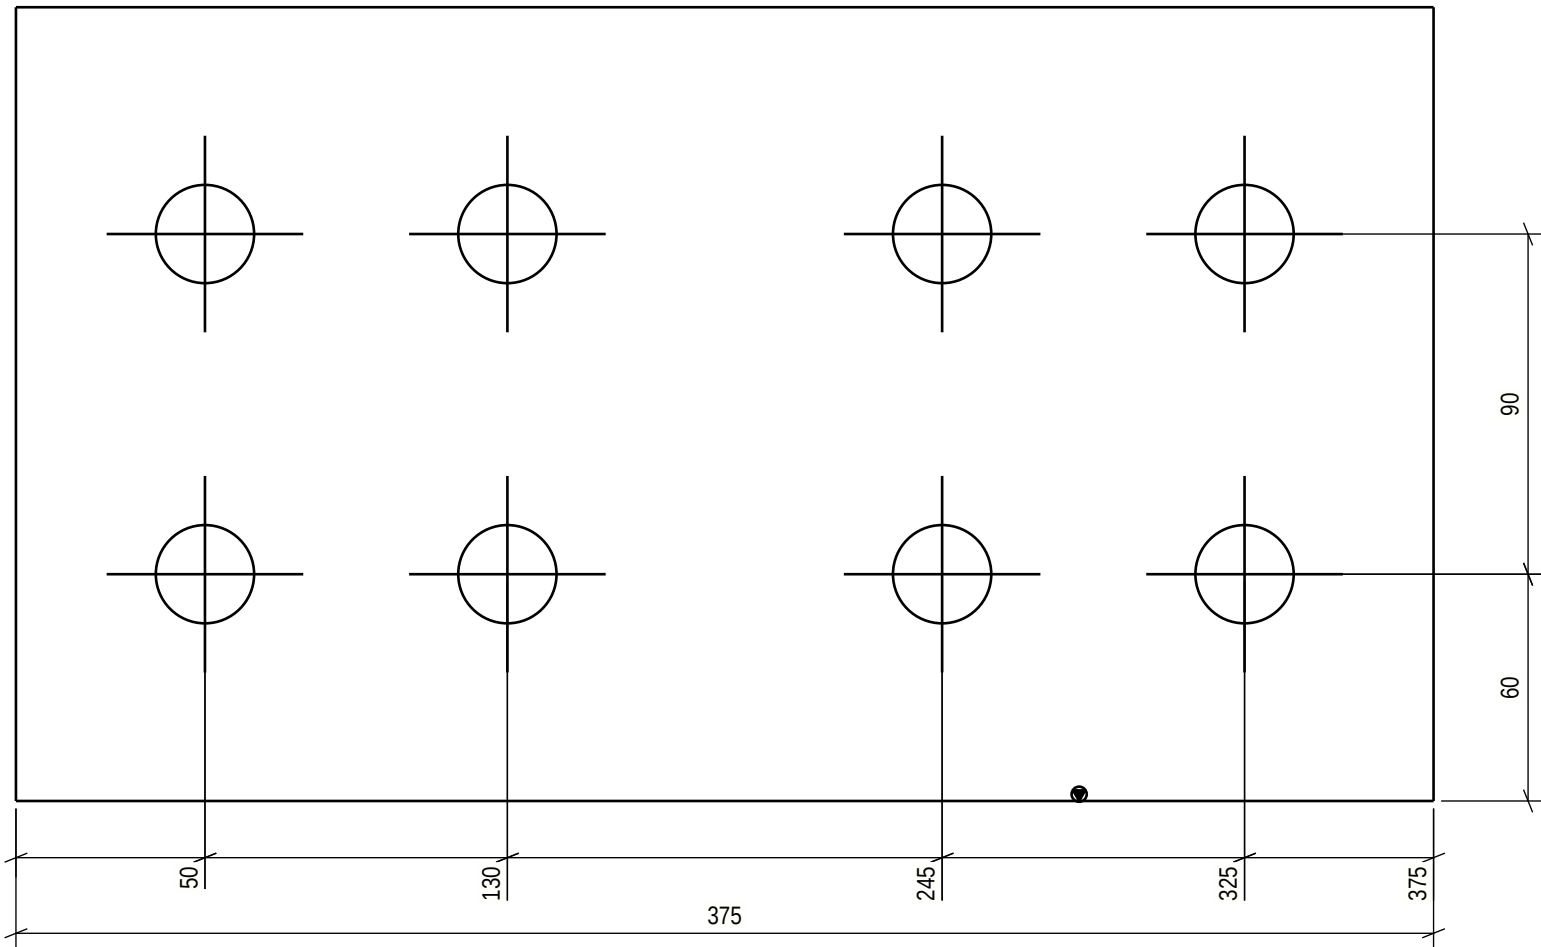


Technical fabrication requirements:		Execution class	
Requirements for fabrication, standard		EN 1090-2, Appendix B	
EN1090-2, table A.3 : EXC2		EN 1090-2, Appendix B	
Execution Specification document nr		Special fabrication tolerances	
25019443-ICC250-0600-0660-000005		Project specification/ shown on drwg.	
Surface preparation grade		Weld inspection, requirements	
ISO8501-3, grade P2		EN 1090-2, Table 24, U>0.5	
Surface treatment		Extent of NDT, filled welds	
ISO12944-5		MT-EN1290, 20% of welds	
Additional requirements on surface treatment		Extent of NDT, butt welds	
C3.07, EPPUR 240/2		UT, EN-ISO17640, 20% of welds	
Shade		Extent of NDT for splices not shown on drawing	
RAL 7024 (Graphite Gray)		UT, EN-ISO17640, 100% of welds	
Welding of built up steel section		Requirements on holing	
Appendix 1 / Project spec.		EN1090-2 Section 6.6.3	
Welds, if not specified otherwise		Weld class	
EN 9692-1, EN 9692-2		C, EN ISO 5817	
		Additional material inspection	
		Shown on drwg.	

Approved For Construction

Easpring New Materials Oy
FAIR Phase 1




SWECO RAKENNETEKNIikka OY
ILMALANPORTTI 2
00240 HELSINKI
PUH. +358 207 393 000
www.sweco.fi

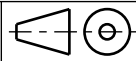

DRAWING CONTENT
ASSEMBLY DRAWING
PLATE
E51EX-1066

DATE	ARCHIVING CODE	PAGE	DESIGN GROUP
12.06.2026			STR
DRAWN	DESIGNER	APPROVED	CHECKED
Alexey Serous	Alexey Serous	Pertti Koivumaaanaho	Jere Kallosalmi
PROJECT NUMBER	DWG. NO.	REVISION	
25019443	E51EX-1066		

PART LIST FOR ASSEMBLY E51EX-1067, MANUFACTURING AMOUNT 8 PIECES						
PART	PROFILE	MATERIAL	LENGTH [mm]	AREA [m2]	WEIGHT [kg]	PCS
E51EXL-1080	PL5X930	S355J2+N	460	0.85	16.4	1
TOTAL:				0.85	16.4	

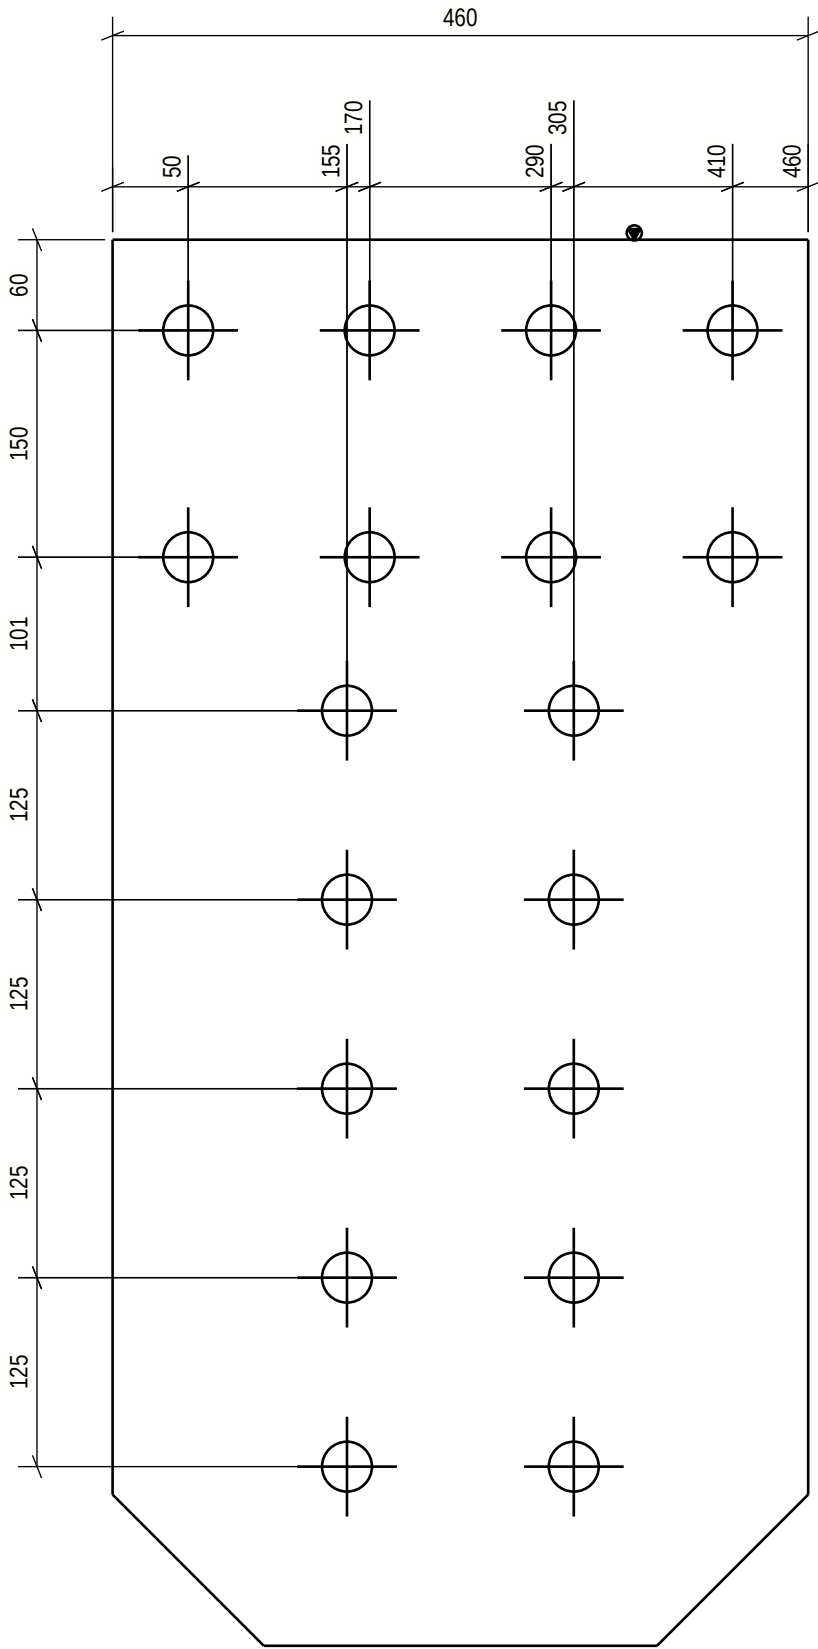


Technical fabrication requirements:		Execution class
Requirements for fabrication, standard	Fabrication tolerances	EXC2
EN1090-2, table A.3 : EXC2	EN 1090-2, Appendix B	
Execution Specification document nr	Special fabrication tolerances	
25019443-ICC250-0600-0660-000005	Project specification/ shown on drwg.	
Surface preparation grade	Weld inspection, requirements	
ISO8501-3, grade P2	EN 1090-2,Table 24, U>0.5	
Surface treatment	Extent of NDT, filled welds	
ISO12944-5	MT-EN1290,20% of welds	
Additional requirements on surface treatment	Extent of NDT, butt welds	
C3.07, EPPUR 240/2	UT, EN-ISO17640, 20% of welds	
Shade	Extent of NDT for splices not shown on drawing	
RAL 7024 (Graphite Gray)	UT, EN-ISO17640, 100%of welds	
Welding of built up steel section	Requirements on holing	
Appendix 1 / Project spec.	EN1090-2 Section 6.6.3	
Welds, if not specified otherwise	Weld class	
EN 9692-1, EN 9692-2	C, EN ISO 5817	Additional material inspection Shown on drwg.

Approved For Construction

Easpring New Materials Oy
FAIR Phase 1




SWECO RAKENNETEKNIikka OY
ILMALANPORTTI 2
00240 HELSINKI
PUH. +358 207 393 000
www.sweco.fi

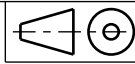

DRAWING CONTENT
ASSEMBLY DRAWING
PLATE
E51EX-1067

DATE	ARCHIVING CODE	PAGE	DESIGN GROUP
12.06.2026			STR
DRAWN	DESIGNER	APPROVED	CHECKED
Alexey Serous	Alexey Serous	Pertti Koivumaaanaho	Jere Kallosalmi
PROJECT NUMBER	DWG. NO.	REVISION	
25019443	E51EX-1067		

PART LIST FOR ASSEMBLY E51EX-1068, MANUFACTURING AMOUNT 8 PIECES						
PART	PROFILE	MATERIAL	LENGTH [mm]	AREA [m2]	WEIGHT [kg]	PCS
E51EXL-1064	PL15X170	S355J2+N	175	0.07	3.5	1
TOTAL:				0.07	3.5	

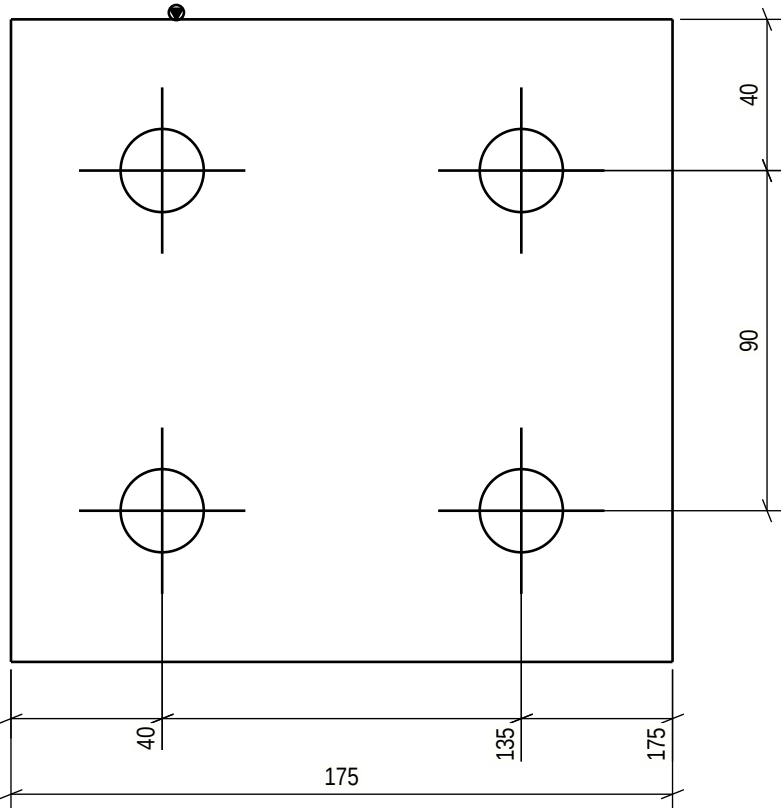


Technical fabrication requirements:		Execution class	
Requirements for fabrication, standard EN1090-2, table A.3 : EXC2		EXC2	
Execution Specification document nr 25019443-ICC250-0600-0660-000005		Fabrication tolerances EN 1090-2, Appendix B	
Surface preparation grade ISO8501-3, grade P2		Special fabrication tolerances Project specification/ shown on drwg.	
Surface treatment ISO12944-5		Weld inspection, requirements EN 1090-2,Table 24, U>0.5	
Additional requirements on surface treatment C3.07, EPPUR 240/2		Extent of NDT, fillet welds MT-EN1290,20% of welds	
Shade RAL 7024 (Graphite Gray)		Extent of NDT, butt welds UT, EN-ISO17640, 20% of welds	
Welding of built up steel section Appendix 1 / Project spec.		Extent of NDT for splices not shown on drawing UT, EN-ISO17640, 100%of welds	
Welds, if not specified otherwise EN 9692-1, EN 9692-2		Requirements on bolting EN1090-2 Section 6.6.3	
		Weld class C, EN ISO 5817	
		Additional material inspection Shown on drwg.	

Approved For Construction

Easpring New Materials Oy
FAIR Phase 1




SWECO RAKENNETEKNIikka OY
ILMALANPORTTI 2
00240 HELSINKI
PUH. +358 207 393 000
www.sweco.fi

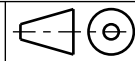


DRAWING CONTENT			
ASSEMBLY DRAWING PLATE E51EX-1068			
DATE 12.06.2026	ARCHIVING CODE	PAGE	DESIGN GROUP STR
DRAWN Alexey Serous	DESIGNER Alexey Serous	APPROVED Pertti Koivumaaanaho	CHECKED Jere Kallosalmi
PROJECT NUMBER 25019443	DWG. NO.	REVISION	E51EX-1068

PART LIST FOR ASSEMBLY E51EX-1069, MANUFACTURING AMOUNT 8 PIECES						
PART	PROFILE	MATERIAL	LENGTH [mm]	AREA [m2]	WEIGHT [kg]	PCS
E51EXL-1063	PL5X300	S355J2+N	1280	0.78	15.1	1
TOTAL:				0.78	15.1	

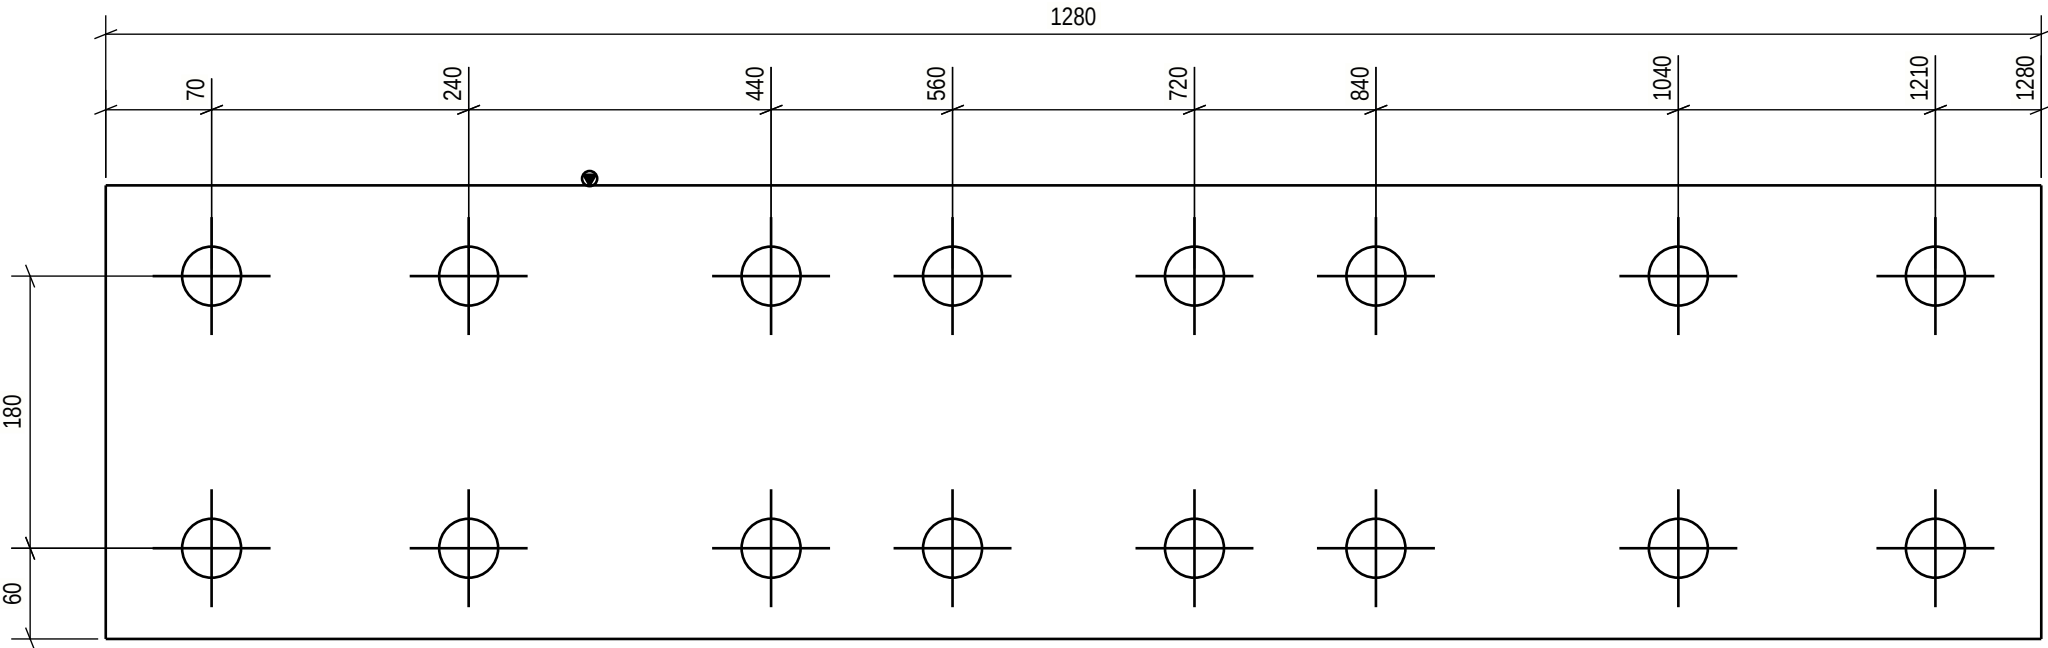

Technical fabrication requirements:		Execution class EXC2	
Requirements for fabrication, standard EN1090-2, table A.3 : EXC2		Fabrication tolerances EN 1090-2, Appendix B	
Execution Specification document nr 25019443-ICC250-0600-0660-000005		Special fabrication tolerances Project specification/ shown on drwg.	
Surface preparation grade ISO8501-3, grade P2		Weld inspection, requirements EN 1090-2,Table 24, U>0.5	
Surface treatment ISO12944-5		Extent of NDT, fillet welds MT-EN1290,20% of welds	
Additional requirements on surface treatment C3.07, EPPUR 240/2		Extent of NDT, butt welds UT, EN-ISO17640, 20% of welds	
Shade RAL 7024 (Graphite Gray)		Extent of NDT for splices not shown on drawing UT, EN-ISO17640, 100%of welds	
Welding of built up steel section Appendix 1 / Project spec.		Requirements on holing EN1090-2 Section 6.6.3	
Welds, if not specified otherwise EN 9692-1, EN 9692-2		Weld class C, EN ISO 5817	
		Additional material inspection Shown on drwg.	
PROJECT NAME Easpring New Materials Oy FAIR Phase 1			
		DRAWING CONTENT ASSEMBLY DRAWING PLATE E51EX-1069	
SWECO RAKENNETEKNIikka OY ILMALANPORTTI 2 00240 HELSINKI		DATE 12.06.2026	
PUH. +358 207 393 000 www.sweco.fi		ARCHIVING CODE	
		PAGE	
		DESIGN GROUP STR	
DRAWN Alexey Serous		DESIGNER Alexey Serous	
PROJECT NUMBER 25019443		APPROVED Pertti Koivumaaanaho	
		CHECKED Jere Kallosalmi	
		DWG. NO. E51EX-1069	
		REVISION	

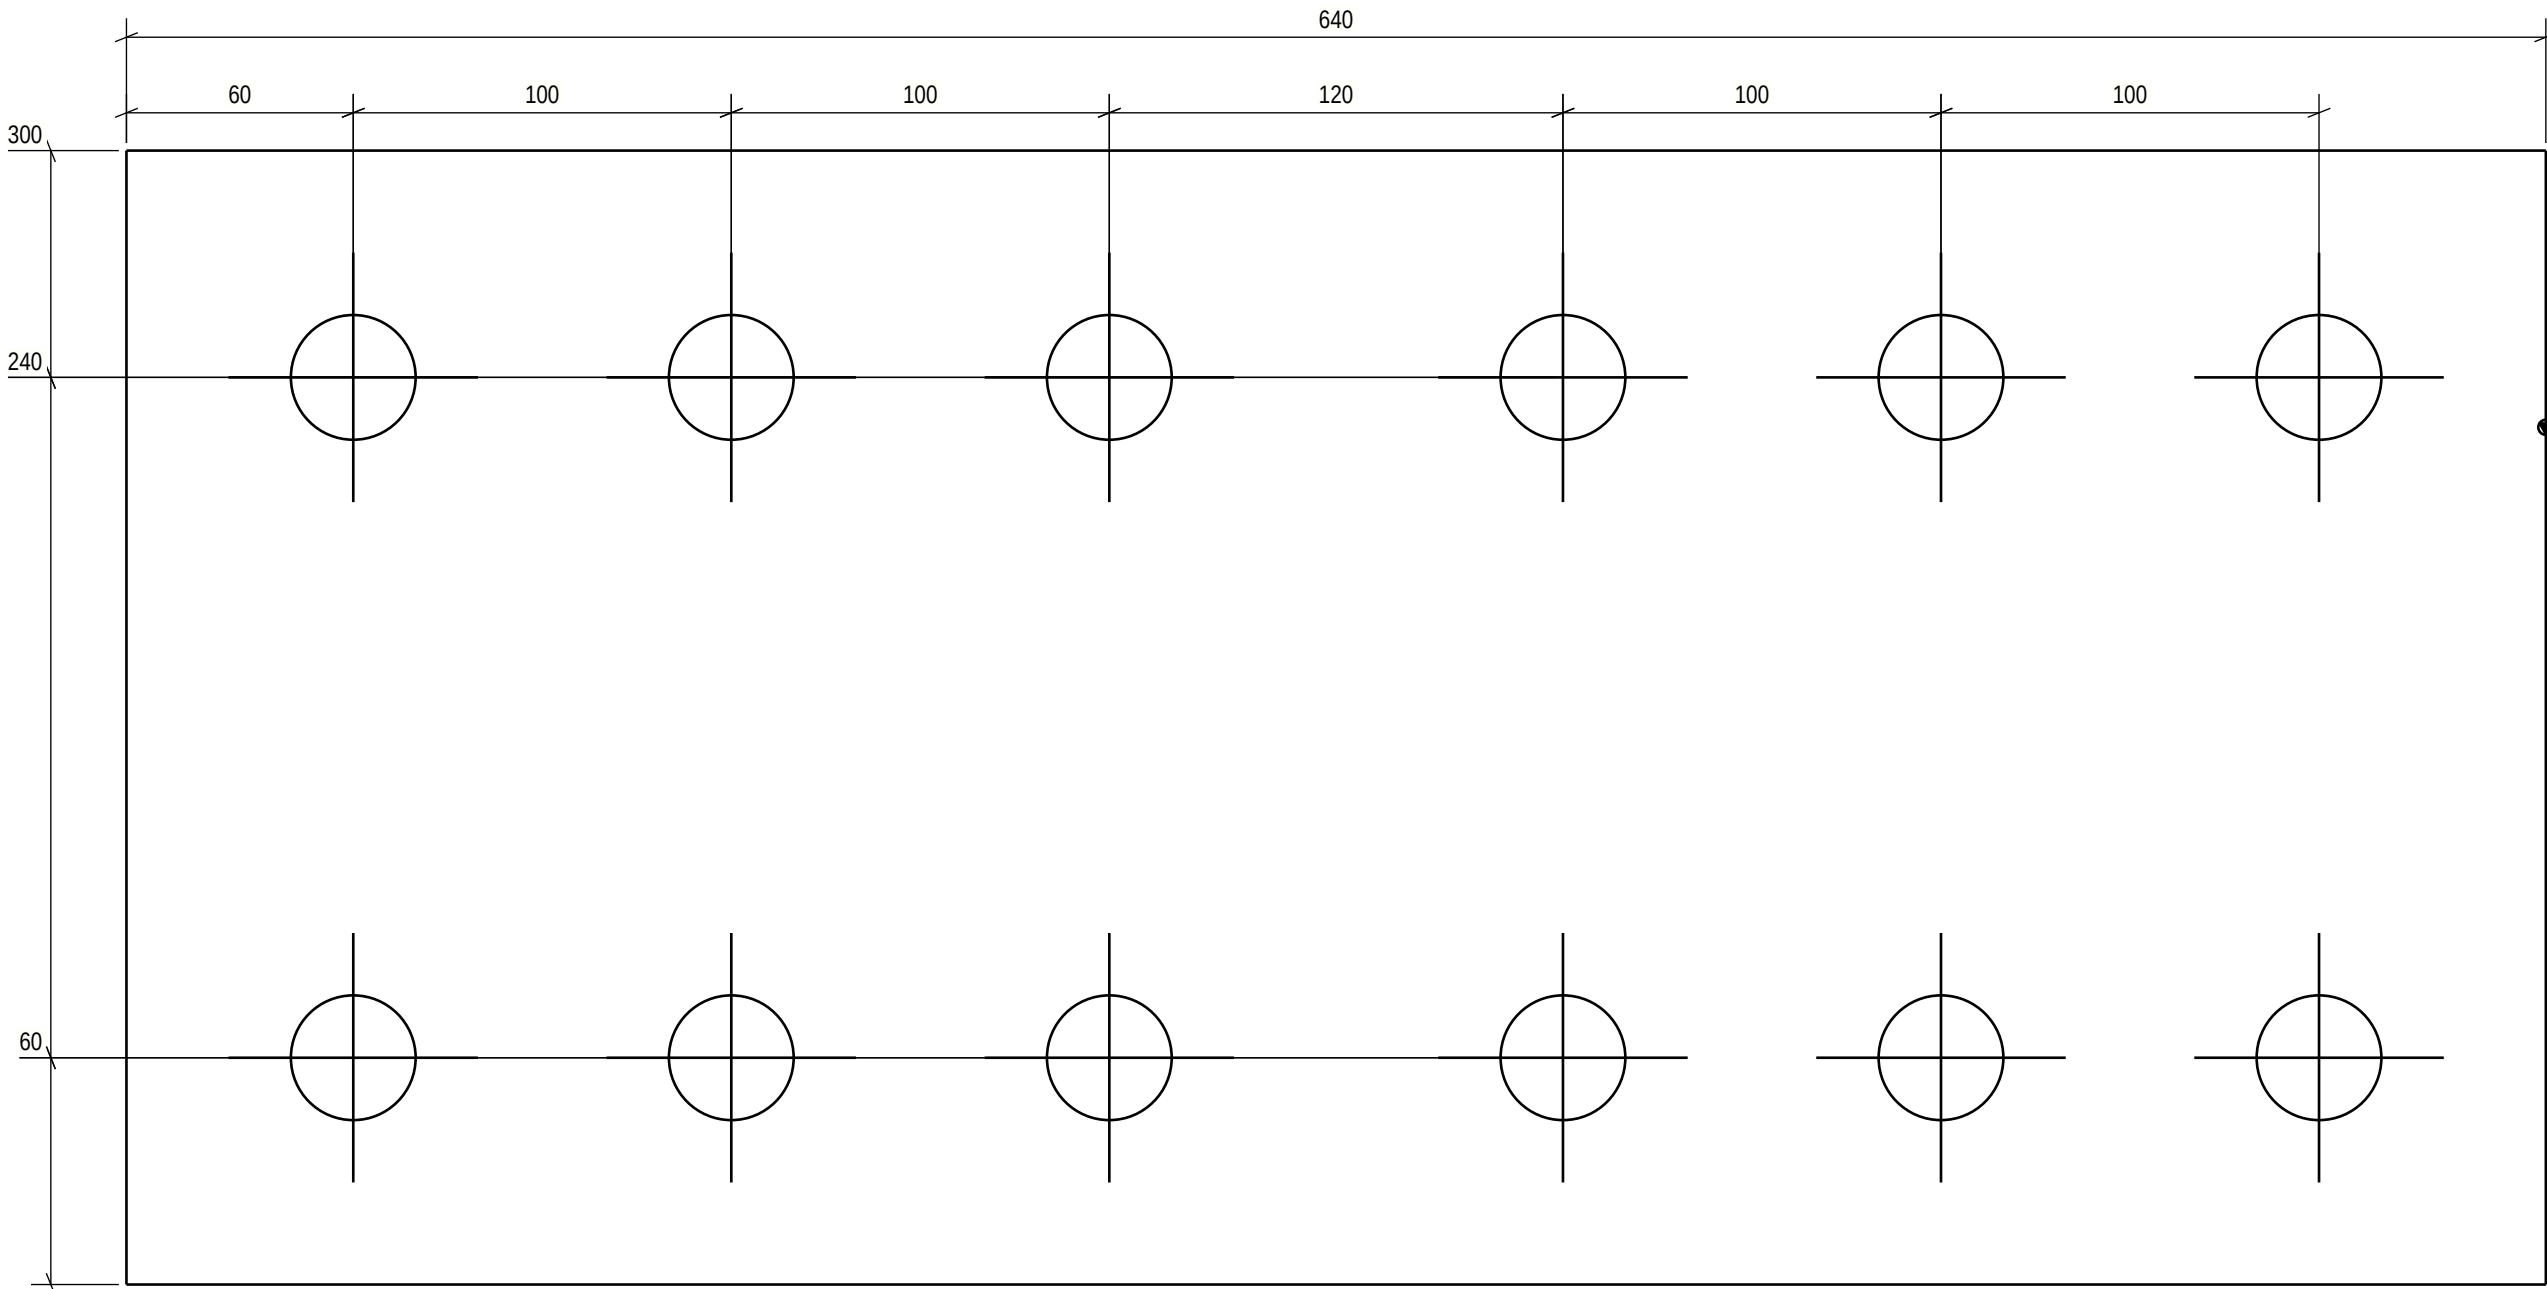


For special tolerances of bolt hole location
see specification for steel structures
Approved For Construction

PART LIST FOR ASSEMBLY E51EX-1071, MANUFACTURING AMOUNT 5 PIECES						
PART	PROFILE	MATERIAL	LENGTH [mm]	AREA [m2]	WEIGHT [kg]	PCS
E51EXL-1067	PL30X300	S355J2+N	640	0.44	45.2	1
TOTAL:				0.44	45.2	

Technical fabrication requirements:		Execution class
EXC2		
Requirements for fabrication, standard	Fabrication tolerances	
EN1090-2, table A.3 : EXC2	EN 1090-2, Appendix B	
Execution Specification document nr	Special fabrication tolerances	
25019443-ICC250-0600-0660-000005	Project specification/ shown on drwg.	
Surface preparation grade	Weld inspection, requirements	
ISO8501-3, grade P2	EN 1090-2,Table 24, U>0.5	
Surface treatment	Extent of NDT, fillet welds	
ISO12944-5	MT-EN1290,20% of welds	
Additional requirements on surface treatment	Extent of NDT, butt welds	
C3.07, EPPUR 240/2	UT, EN-ISO17640, 20% of welds	
Shade	Extent of NDT for splices not shown on drawing	
RAL 7024 (Graphite Gray)	UT, EN-ISO17640, 100%of welds	
Welding of built up steel section	Requirements on holing	
Appendix 1 / Project spec.	EN1090-2 Section 6.6.3	
Welds, if not specified otherwise	Weld class	Additional material inspection
EN 9692-1, EN 9692-2	C, EN ISO 5817	Shown on drwg.

FIRE PROTECTION SAME AS FOR E51WC-1031

PROJECT NAME
Easpring New Materials Oy
FAIR Phase 1

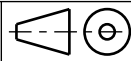


DRAWING CONTENT
ASSEMBLY DRAWING
PLATE
E51EX-1071



SWECO RAKENNTEKNIikka OY
ILMALANPORTTI 2
00240 HELSINKI
PUH. +358 207 393 000
www.sweco.fi

DATE	ARCHIVING CODE	PAGE	DESIGN GROUP
12.06.2026			STR
DRAWN	DESIGNER	APPROVED	CHECKED
Alexey Serous	Alexey Serous	Pertti Koivumaaanaho	Jere Kallosalmi
PROJECT NUMBER	DWG. NO.	REVISION	
25019443	E51EX-1071		

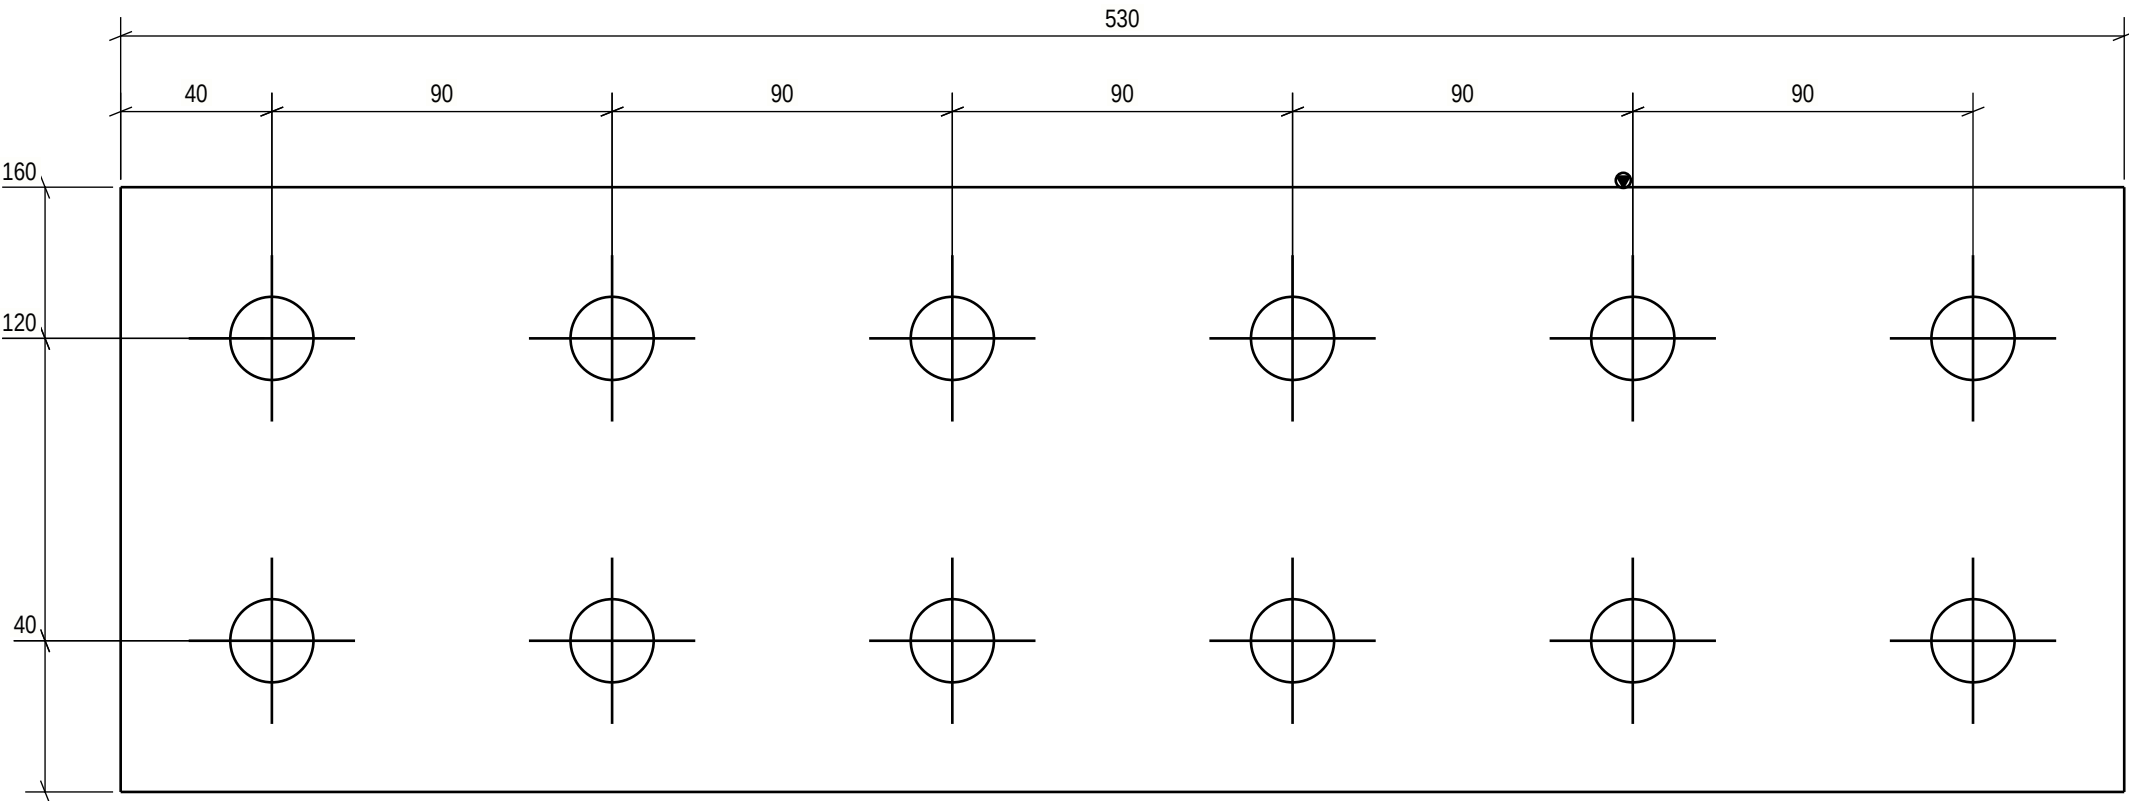


For special tolerances of bolt hole location
see specification for steel structures
Approved For Construction

PART LIST FOR ASSEMBLY E51EX-1072, MANUFACTURING AMOUNT 8 PIECES						
PART	PROFILE	MATERIAL	LENGTH [mm]	AREA [m2]	WEIGHT [kg]	PCS
E51EXL-1068	PL10X160	S355J2+N	530	0.18	6.7	1
TOTAL:				0.18	6.7	

Technical fabrication requirements:		Execution class
EXC2		
Requirements for fabrication, standard	Fabrication tolerances	
EN1090-2, table A.3 : EXC2	EN 1090-2, Appendix B	
Execution Specification document nr	Special fabrication tolerances	
25019443-ICC250-0600-0660-000005	Project specification/ shown on drwg.	
Surface preparation grade	Weld inspection, requirements	
ISO8501-3, grade P2	EN 1090-2,Table 24, U>0.5	
Surface treatment	Extent of NDT, fillet welds	
ISO12944-5	MT-EN1290,20% of welds	
Additional requirements on surface treatment	Extent of NDT, butt welds	
C3.07, EPPUR 240/2	UT, EN-ISO17640, 20% of welds	
Shade	Extent of NDT for splices not shown on drawing	
RAL 7024 (Graphite Gray)	UT, EN-ISO17640, 100%of welds	
Welding of built up steel section	Requirements on holing	
Appendix 1 / Project spec.	EN1090-2 Section 6.6.3	
Welds, if not specified otherwise	Weld class	Additional material inspection
EN 9692-1, EN 9692-2	C, EN ISO 5817	Shown on drwg.

FIRE PROTECTION SAME AS FOR E51WC-1031

PROJECT NAME
Easpring New Materials Oy
FAIR Phase 1

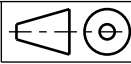


DRAWING CONTENT
ASSEMBLY DRAWING
PLATE
E51EX-1072



SWECO RAKENNETEKNIikka OY
ILMALANPORTTI 2
00240 HELSINKI
PUH. +358 207 393 000
www.sweco.fi

DATE	ARCHIVING CODE	PAGE	DESIGN GROUP
12.06.2026			STR
DRAWN	DESIGNER	APPROVED	CHECKED
Alexey Serous	Alexey Serous	Pertti Koivumaaanaho	Jere Kallosalmi
PROJECT NUMBER	DWG. NO.	REVISION	
25019443	E51EX-1072		


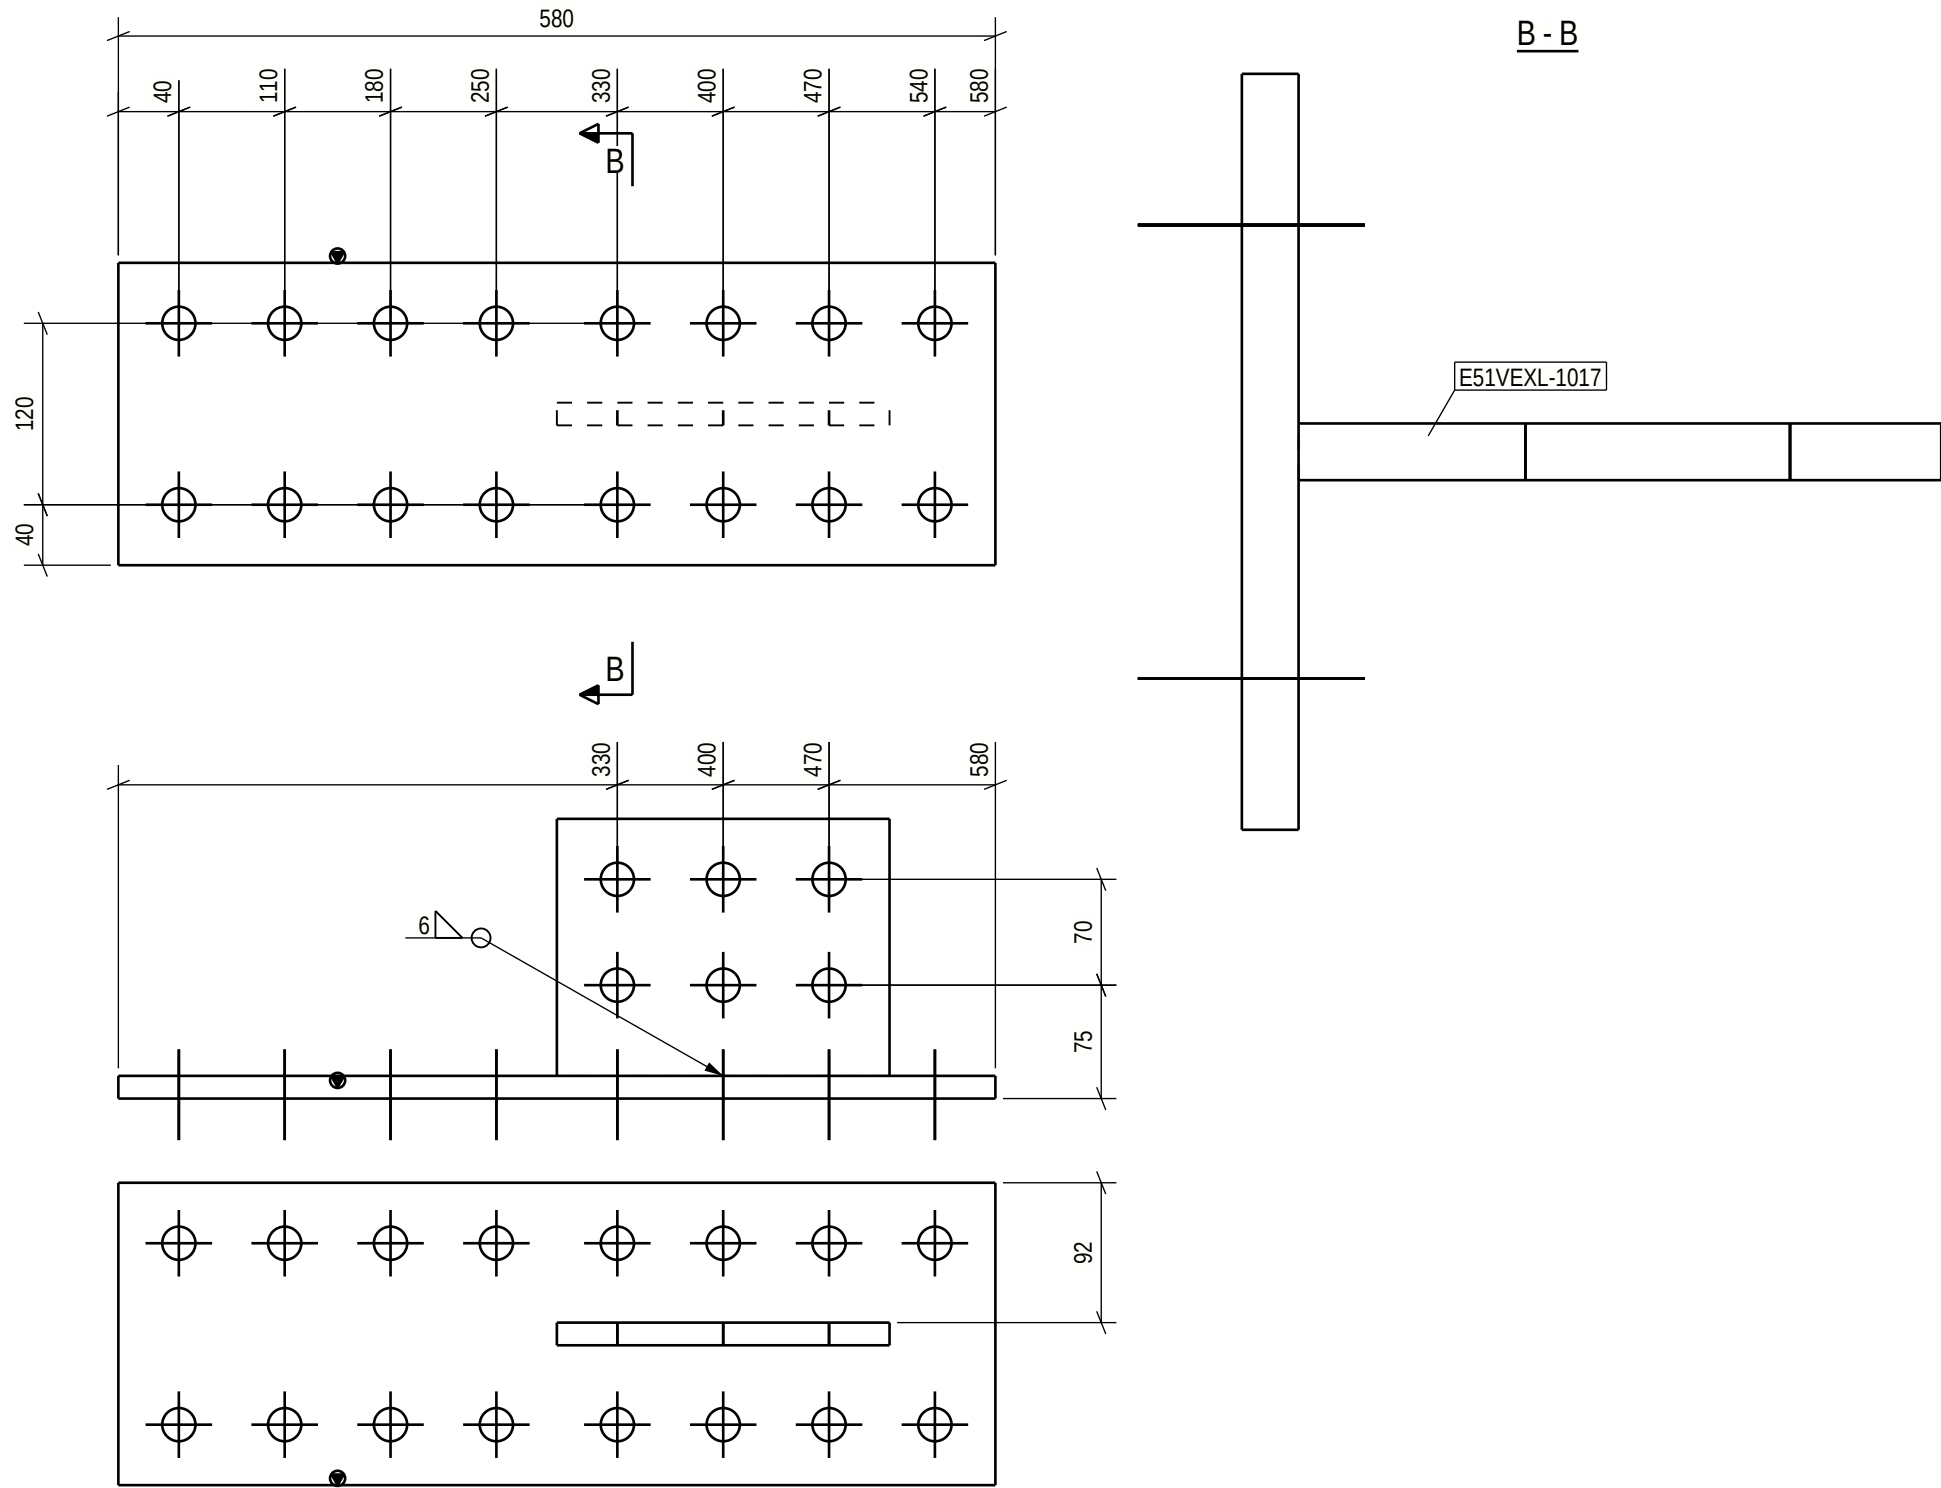


For special tolerances of bolt hole location
see specification for steel structures
Approved For Construction


PART LIST FOR ASSEMBLY E51EX-1074, MANUFACTURING AMOUNT 4 PIECES						
PART	PROFILE	MATERIAL	LENGTH [mm]	AREA [m2]	WEIGHT [kg]	PCS
E51EXL-1033	PL15X200	S355J2+N	580	0.26	13.7	1
E51VEXL-1017	PL15X170	S355J2+N	220	0.09	4.4	1
TOTAL:				0.34	18.1	

Technical fabrication requirements:		Execution class
Requirements for fabrication, standard EN1090-2, table A.3 : EXC2		EXC2
Execution Specification document nr 25019443-ICC250-0600-0660-000005	Fabrication tolerances EN 1090-2, Appendix B Special fabrication tolerances Project specification/ shown on drwg.	
Surface preparation grade ISO8501-3, grade P2	Weld inspection, requirements EN 1090-2,Table 24, U>0.5	
Surface treatment ISO12944-5	Extent of NDT, fillet welds MT-EN1290,20% of welds	
Additional requirements on surface treatment C3.07, EPPUR 240/2	Extent of NDT, butt welds UT, EN-ISO17640, 20% of welds	
Shade RAL 7024 (Graphite Gray)	Extent of NDT for splices not shown on drawing UT, EN-ISO17640, 100%of welds	
Welding of built up steel section Appendix 1 / Project spec.	Requirements on holing EN1090-2 Section 6.6.3	
Welds, if not specified otherwise EN 9692-1, EN 9692-2	Weld class C, EN ISO 5817	Additional material inspection Shown on drwg.

FIRE PROTECTION SAME AS FOR E51WC-1031

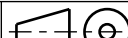 PROJECT NAME Easpring New Materials Oy FAIR Phase 1				DRAWING CONTENT ASSEMBLY DRAWING PLATE E51EX-1074	
 Sustainable engineering and design	SWECO RAKENNETEKNIikka OY ILMALANPORTTI 2 00240 HELSINKI PUH. +358 207 393 000 www.sweco.fi	DATE 12.06.2026	ARCHIVING CODE	PAGE	DESIGN GROUP STR
		DRAWN Alexey Serous	DESIGNER Alexey Serous	APPROVED Pertti Koivumaaanaho	CHECKED Jere Kalliosalmi
		PROJECT NUMBER 25019443		REVISION	
		DWG. NO. E51EX-1074			


PART LIST FOR ASSEMBLY E51EX-1075, MANUFACTURING AMOUNT 8 PIECES						
PART	PROFILE	MATERIAL	LENGTH [mm]	AREA [m2]	WEIGHT [kg]	PCS
E51EXL-1049	PL10X360	S355J2+N	180	0.14	5.1	1
TOTAL:				0.14	5.1	

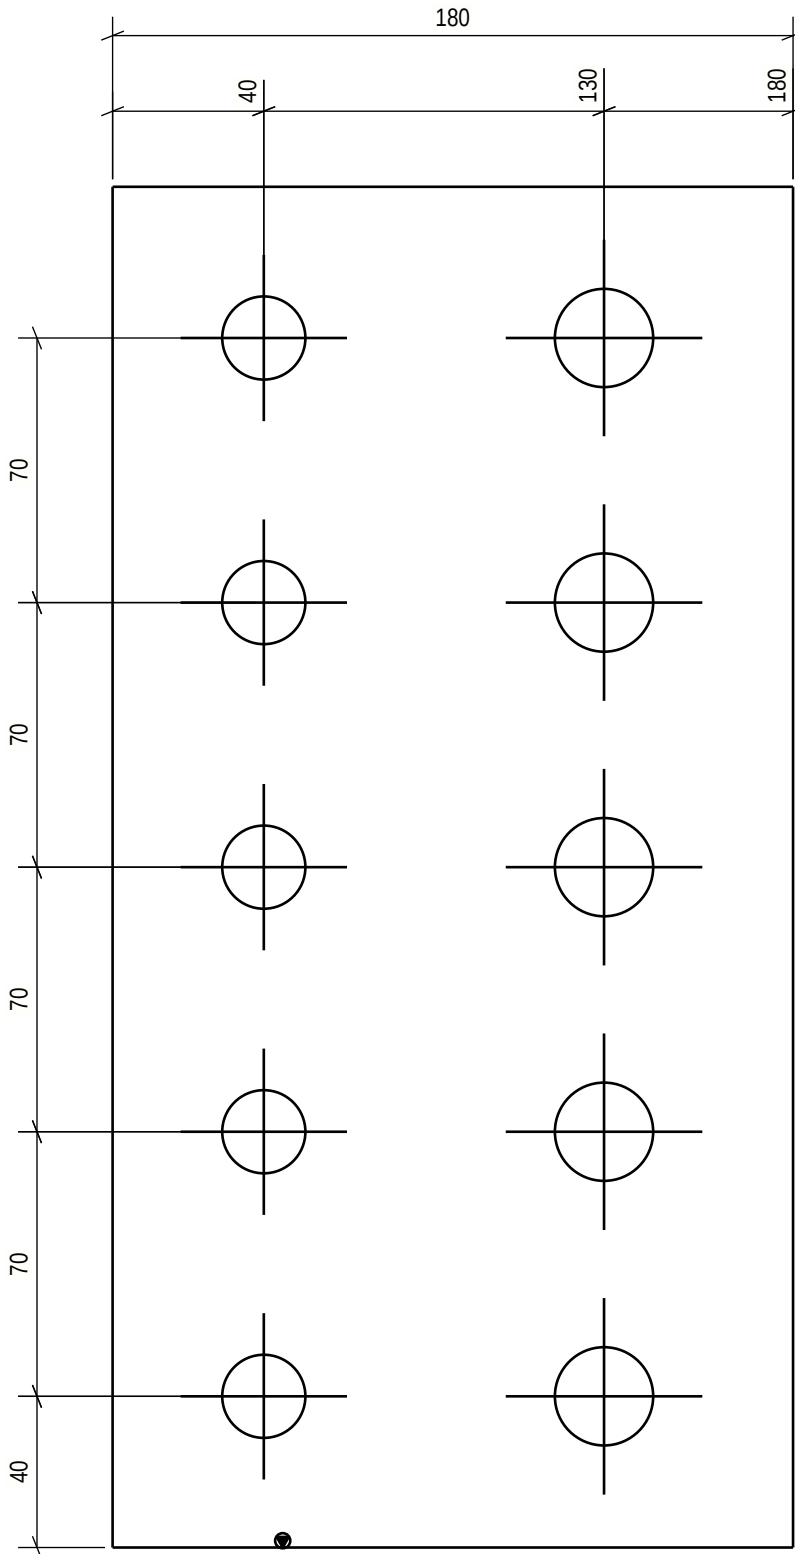

Technical fabrication requirements:		Execution class
Requirements for fabrication, standard		EXC2
EN1090-2, table A.3 : EXC2	Fabrication tolerances	EN 1090-2, Appendix B
Execution Specification document nr	Special fabrication tolerances	
25019443-ICC250-0600-0660-000005	Project specification/ shown on drwg.	
Surface preparation grade	Weld inspection, requirements	
ISO8501-3, grade P2	EN 1090-2,Table 24, U>0.5	
Surface treatment	Extent of NDT, fillet welds	
ISO12944-5	MT-EN1290,20% of welds	
Additional requirements on surface treatment	Extent of NDT, butt welds	
C3.07, EPPUR 240/2	UT, EN-ISO17640, 20% of welds	
Shade	Extent of NDT for splices not shown on drawing	
RAL 7024 (Graphite Gray)	UT, EN-ISO17640, 100%of welds	
Welding of built up steel section	Requirements on holing	
Appendix 1 / Project spec.	EN1090-2 Section 6.6.3	
Welds, if not specified otherwise	Weld class	Additional material inspection
EN 9692-1, EN 9692-2	C, EN ISO 5817	Shown on drwg.

For special tolerances of bolt hole location
see specification for steel structures
Approved For Construction


PROJECT NAME		DRAWING CONTENT	
Easpring New Materials Oy		ASSEMBLY DRAWING	
FAIR Phase 1		PLATE	
		E51EX-1075	
 SWECO RAKENNETEKNIikka OY ILMALANPORTTI 2 00240 HELSINKI PUH. +358 207 393 000 www.sweco.fi	DATE	ARCHIVING CODE	PAGE
	12.06.2026		
	DRAWN	DESIGNER	APPROVED
	Alexey Serous	Alexey Serous	Pertti Koivumaaanaho
PROJECT NUMBER		DWG. NO.	REVISION
25019443		E51EX-1075	

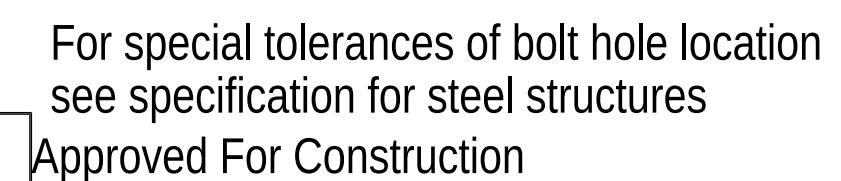

Technical fabrication requirements:		Execution class EXC2	
Requirements for fabrication, standard EN1090-2, table A.3 : EXC2 Execution Specification document nr 25019443-ICC250-0600-0660-000005 Surface preparation grade ISO8501-3, grade P2 Surface treatment ISO12944-5 Additional requirements on surface treatment C3.07, EPPUR 240/2 Shade RAL 7024 (Graphite Gray) Welding of built up steel section Appendix 1 / Project spec. Welds, if not specified otherwise EN 9692-1, EN 9692-2		Fabrication tolerances EN 1090-2, Appendix B Special fabrication tolerances Project specification/ shown on drwg. Weld inspection, requirements EN 1090-2, Table 24, U>0.5 Extent of NDT, fillet welds MT-EN1290, 20% of welds Extent of NDT, butt welds UT, EN-ISO17640, 20% of welds Extent of NDT for splices not shown on drawing UT, EN-ISO17640, 100%of welds Requirements on holding EN1090-2 Section 6.6.3 Weld class C, EN ISO 5817 Additional material inspection Shown on drwg	

25019443 Fair E500

PART LIST FOR ASSEMBLY E51EX-1078, MANUFACTURING AMOUNT 8 PIECES						
PART	PROFILE	MATERIAL	LENGTH [mm]	AREA [m2]	WEIGHT [kg]	PCS
E51EXL-1076	PL10X210	S355J2+N	375	0.17	6.2	1
TOTAL:				0.17	6.2	

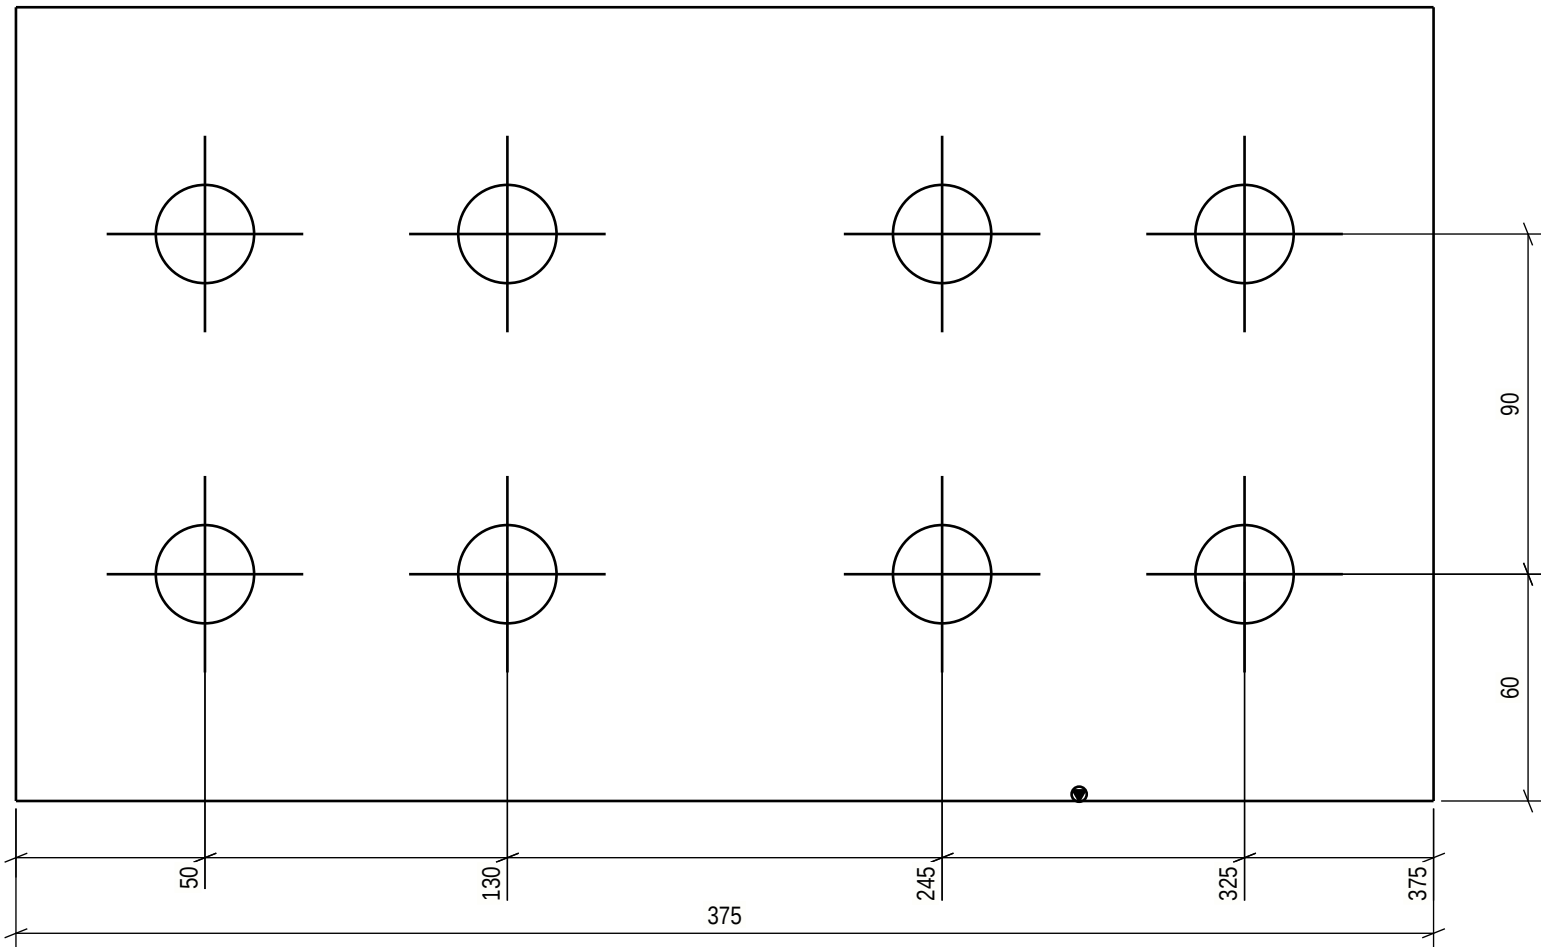


Technical fabrication requirements:		Execution class
Requirements for fabrication, standard	Fabrication tolerances	EXC2
EN1090-2, table A.3 : EXC2	EN 1090-2, Appendix B	
Execution Specification document nr	Special fabrication tolerances	
25019443-ICC250-0600-0660-000005	Project specification/ shown on drwg.	
Surface preparation grade	Weld inspection, requirements	
ISO8501-3, grade P2	EN 1090-2,Table 24, U>0.5	
Surface treatment	Extent of NDT, fillet welds	
ISO12944-5	MT-EN1290,20% of welds	
Additional requirements on surface treatment	Extent of NDT, butt welds	
C3.07, EPPUR 240/2	UT, EN-ISO17640, 20% of welds	
Shade	Extent of NDT for splices not shown on drawing	
RAL 7024 (Graphite Gray)	UT, EN-ISO17640, 100%of welds	
Welding of built up steel section	Requirements on holing	
Appendix 1 / Project spec.	EN1090-2 Section 6.6.3	
Welds, if not specified otherwise	Weld class	
EN 9692-1, EN 9692-2	C, EN ISO 5817	Additional material inspection Shown on drwg.

Approved For Construction

Easpring New Materials Oy
FAIR Phase 1




SWECO RAKENNETEKNIikka OY
ILMALANPORTTI 2
00240 HELSINKI
PUH. +358 207 393 000
www.sweco.fi

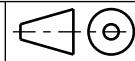

DRAWING CONTENT
ASSEMBLY DRAWING
PLATE
E51EX-1078

DATE	ARCHIVING CODE	PAGE	DESIGN GROUP
12.06.2026			STR
DRAWN	DESIGNER	APPROVED	CHECKED
Alexey Serous	Alexey Serous	Pertti Koivumaaanaho	Jere Kallosalmi
PROJECT NUMBER	DWG. NO.	REVISION	
25019443	E51EX-1078		

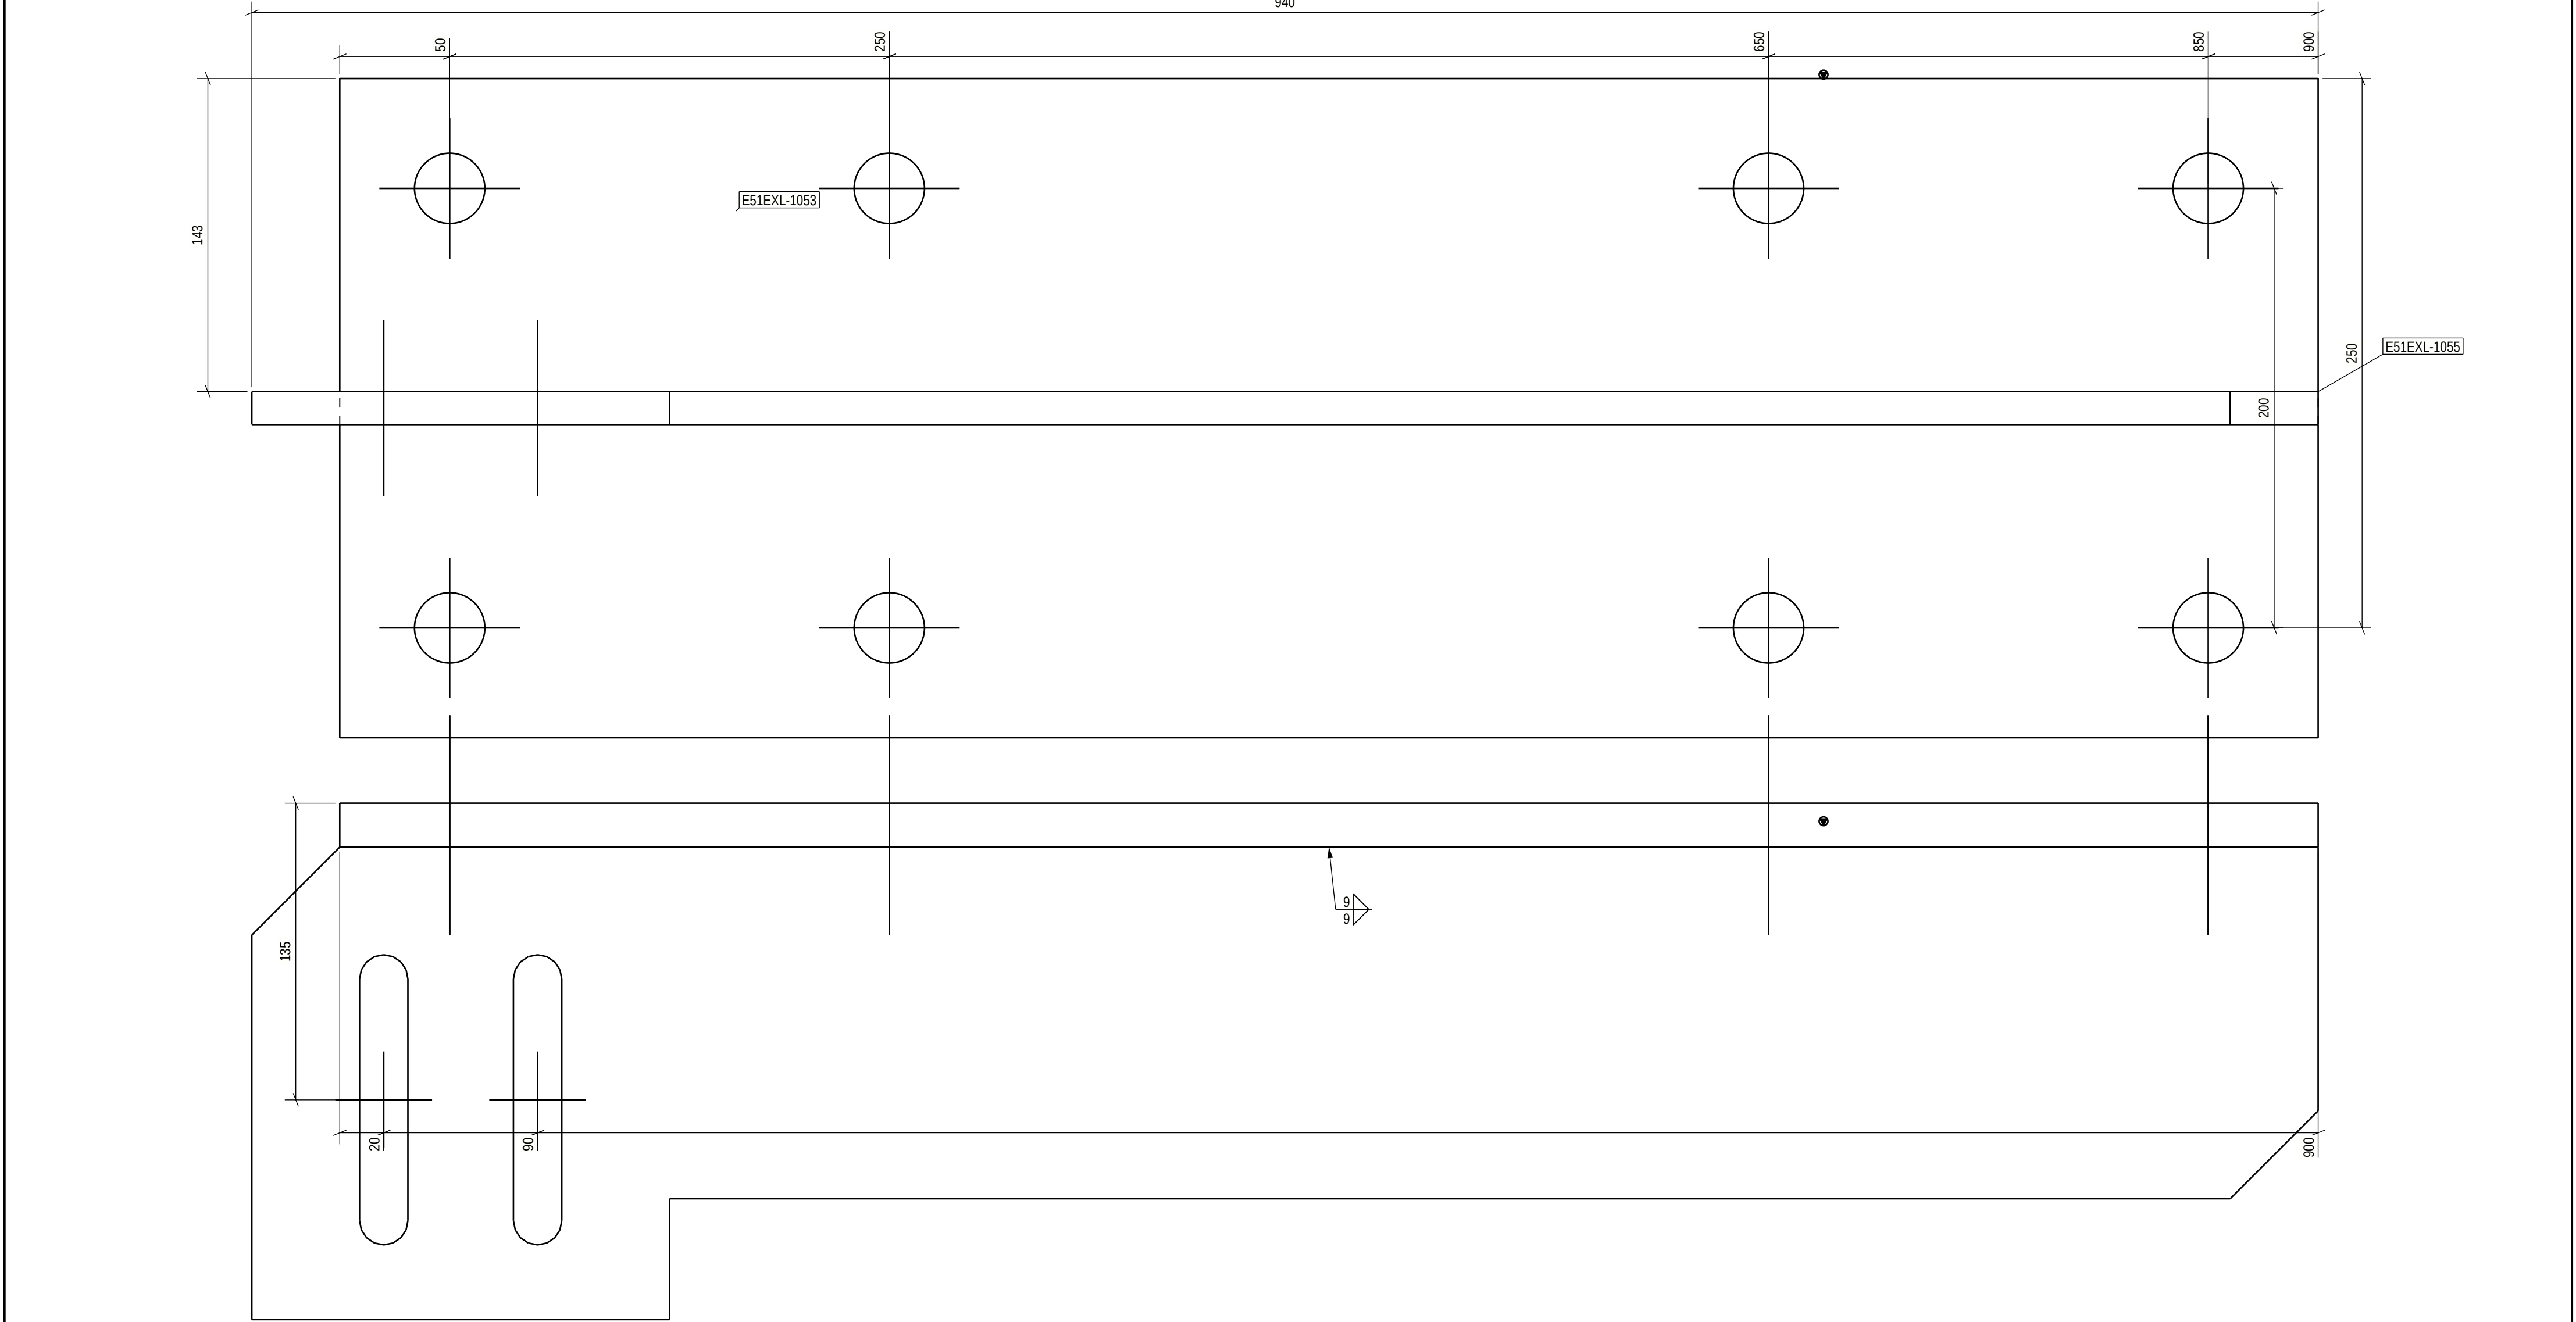

PART LIST FOR ASSEMBLY E51EX-1079, MANUFACTURING AMOUNT 1 PIECES						
PART	PROFILE	MATERIAL	LENGTH [mm]	AREA [m2]	WEIGHT [kg]	PCS
E51EXL-1053	PL20X300	S355J2+N	900	0.59	42.4	1
E51EXL-1055	PL15X215	S355J2+N	940	0.35	18.8	1
TOTAL:				0.94	61.1	

Technical fabrication requirements:

Execution class

EXC2

Requirements for fabrication, standard

EN1090-2, table A.3 : EXC2

Execution Specification document nr

25019443-ICC250-0600-0660-000005

Surface preparation grade

ISO8501-3, grade P2

Surface treatment

ISO12944-5

Additional requirements on surface treatment

C3.07, EPPUR 240/2

Shade

RAL 7024 (Graphite Gray)

Welding of built up steel section

Appendix 1 / Project spec.

Welds, if not specified otherwise

EN 9692-1, EN 9692-2

Fabrication tolerances

EN 1090-2, Appendix B

Special fabrication tolerances

Project specification/ shown on drwg.

Weld inspection, requirements

EN 1090-2,Table 24, U>0.5

Extent of NDT, fillet welds

MT-EN1290,20% of welds

Extent of NDT, butt welds

UT, EN-ISO17640, 20% of welds

Extent of NDT for splices not shown on drawing

UT, EN-ISO17640, 100%of welds

Requirements on holing

EN1090-2 Section 6.6.3

Weld class

C, EN ISO 5817

Additional material inspection

Shown on drwg.

PROJECT NAME

Easpring New Materials Oy

FAIR Phase 1

SWECO



Sustainable engineering and design

SWECO RAKENNETEKNIikka OY

ILMALANPORTTI 2

00240 HELSINKI

PUH. +358 207 393 000

www.sweco.fi

DRAWING CONTENT

ASSEMBLY DRAWING

PLATE

E51EX-1079

DATE

12.06.2026

ARCHIVING CODE

PAGE

DESIGN GROUP

STR

DRAWN

Alexey Serous

DESIGNER

Alexey Serous

APPROVED

Pertti Koivumaaanaho

CHECKED

Jere Kallosalmi

PROJECT NUMBER


25019443

DWG. NO.

REVISION

E51EX-1079

For special tolerances of bolt hole location
see specification for steel structures
Approved For Construction

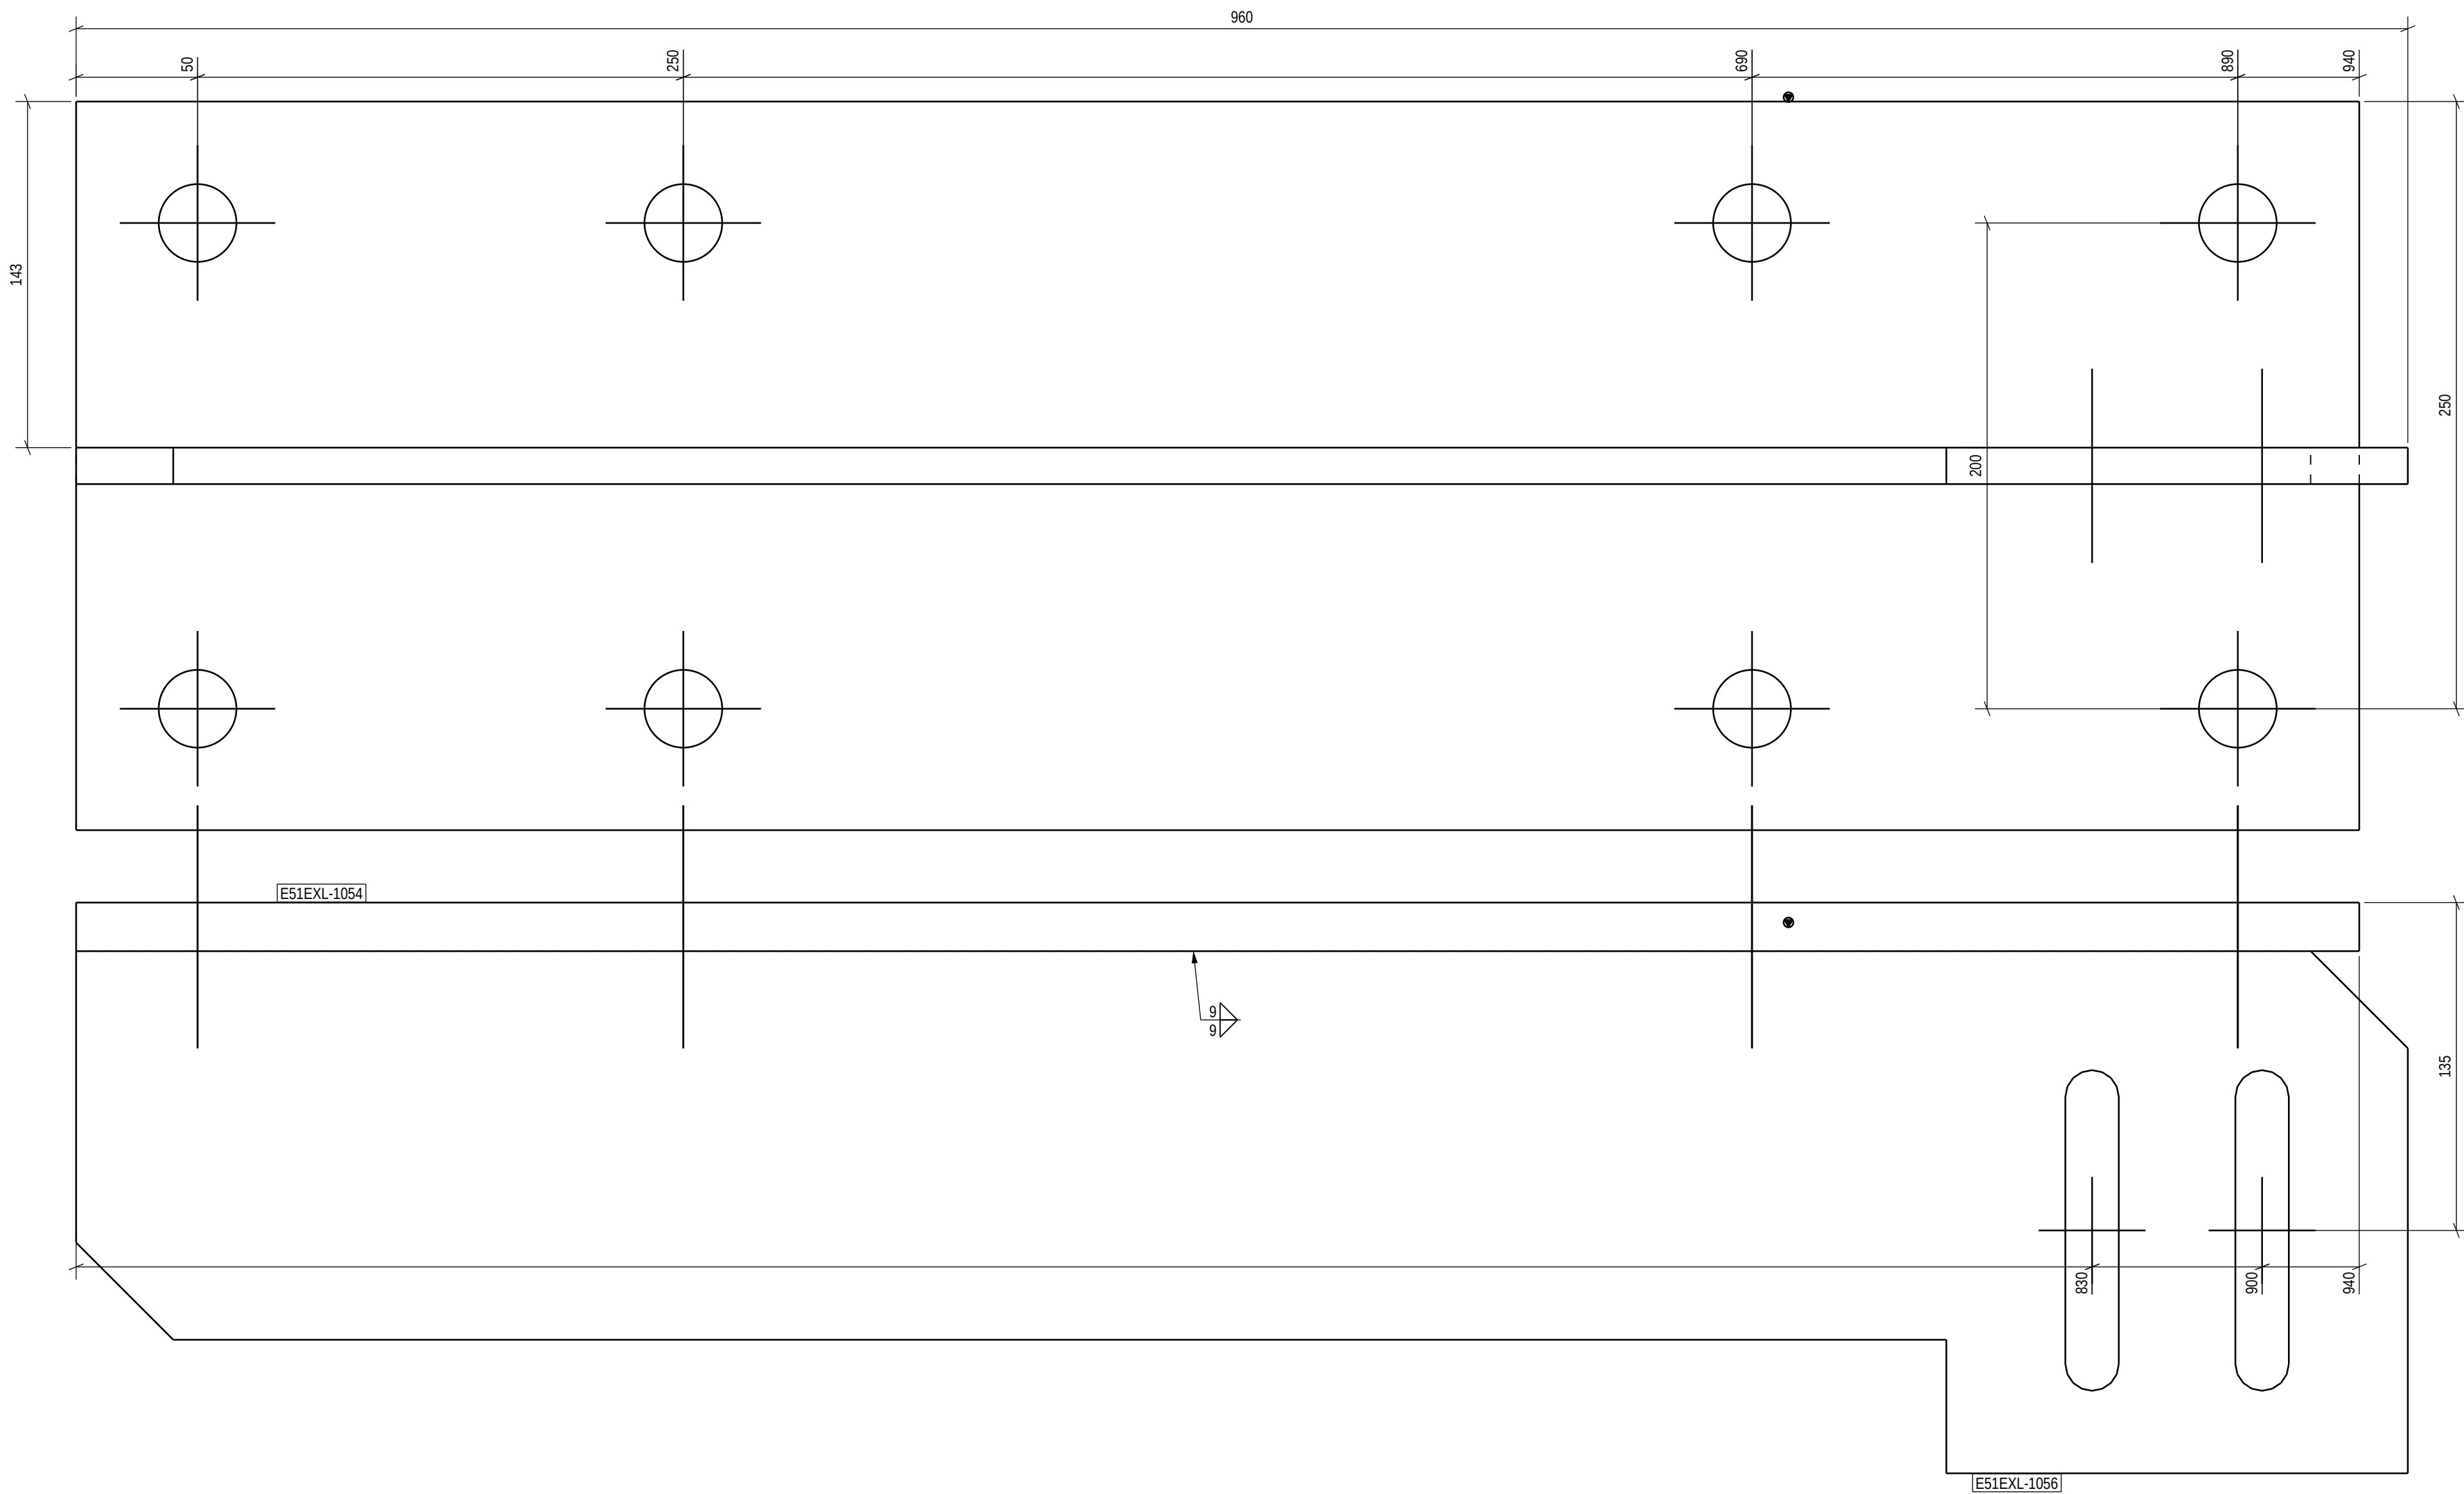


PART LIST FOR ASSEMBLY E51EX-1080, MANUFACTURING AMOUNT 1 PIECES						
PART	PROFILE	MATERIAL	LENGTH [mm]	AREA [m2]	WEIGHT [kg]	PCS
E51EXL-1054	PL20X300	S355J2+N	940	0.61	44.3	1
E51EXL-1056	PL15X215	S355J2+N	960	0.36	19.1	1
			TOTAL:	0.97	63.4	

Technical fabrication requirements:		Execution class EXC2		Approved For Construction			
Requirements for fabrication, standard EN1090-2, table A.3 : EXC2 Execution Specification document nr 25019443-ICC250-0600-0660-000005 Surface preparation grade ISO8501-3, grade P2 Surface treatment ISO12944-5 Additional requirements on surface treatment C3.07, EPPUR 240/2 Shade RAL 7024 (Graphite Gray) Welding of built up steel section Appendix 1 / Project spec. Welds, if not specified otherwise EN 9692-1, EN 9692-2		Fabrication tolerances EN 1090-2, Appendix B Special fabrication tolerances Project specification/ shown on drwg. Weld inspection, requirements EN 1090-2, Table 24, U>0.5 Extent of NDT, fillet welds MT-EN1290, 20% of welds Extent of NDT, butt welds UT, EN-ISO17640, 20% of welds Extent of NDT for splices not shown on drawing UT, EN-ISO17640, 100% of welds Requirements on holding EN1090-2 Section 6.6.3 Weld class C, EN ISO 5817 Additional inspection Shown on drwg.		PROJECT NAME Easpring New Materials Oy FAIR Phase 1			
		 SWECO Sustainable engineering and design		SWECO RAKENNETEKNIikka OY ILMALANPORTTI 2 00240 HELSINKI PUH. +358 207 393 000 www.sweco.fi		DRAWING CONTENT ASSEMBLY DRAWING PLATE E51EX-1080	
				DATE 12.06.2026 DRAWN Alexey Serous PROJECT NUMBER 25019443		ARCHIVING CODE DESIGNER Alexey Serous DWG. NO. E51EX-1080	
				PAGE APPROVED Pertti Koivumaaanaho DESIGN GROUP STR CHECKED Jere Kalliosalmi REVISION			

For special tolerances of bolt hole location
see specification for steel structures

Approved For Construction

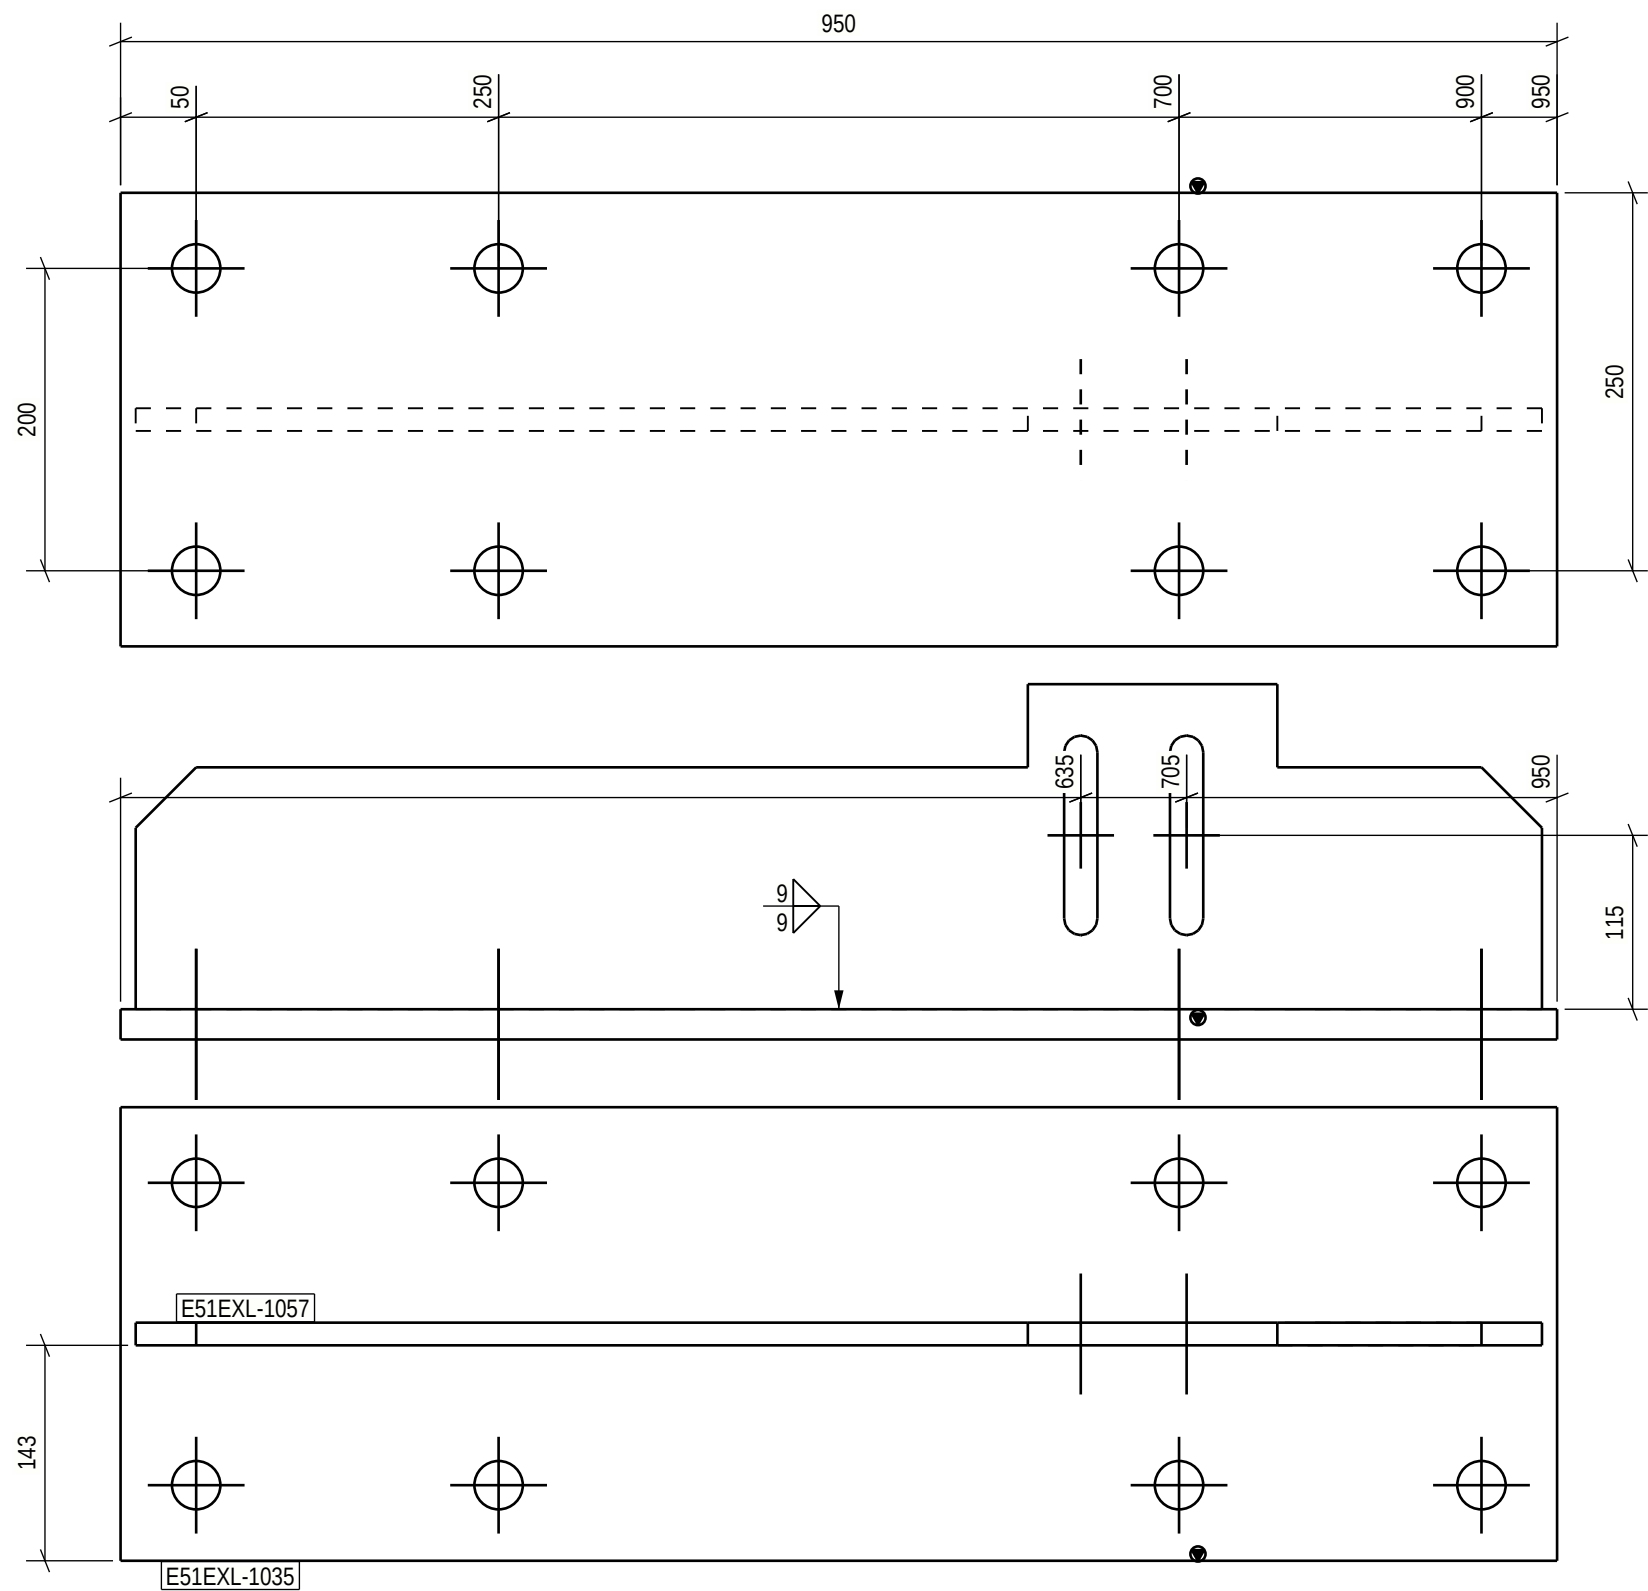


For special tolerances of bolt hole location
see specification for steel structures
Approved For Construction

PART LIST FOR ASSEMBLY E51EX-1081, MANUFACTURING AMOUNT 1 PIECES						
PART	PROFILE	MATERIAL	LENGTH [mm]	AREA [m2]	WEIGHT [kg]	PCS
E51EXL-1035	PL20X300	S355J2+N	950	0.62	44.7	1
E51EXL-1057	PL15X215	S355J2+N	930	0.35	18.4	1
TOTAL:				0.97	63.1	

Technical fabrication requirements:		Execution class
EXC2		
Requirements for fabrication, standard	Fabrication tolerances	
EN1090-2, table A.3 : EXC2	EN 1090-2, Appendix B	
Execution Specification document nr	Special fabrication tolerances	
25019443-ICC250-0600-0660-000005	Project specification/ shown on drwg.	
Surface preparation grade	Weld inspection, requirements	
ISO8501-3, grade P2	EN 1090-2,Table 24, U>0.5	
Surface treatment	Extent of NDT, fillet welds	
ISO12944-5	MT-EN1290,20% of welds	
Additional requirements on surface treatment	Extent of NDT, butt welds	
C3.07, EPPUR 240/2	UT, EN-ISO17640, 20% of welds	
Shade	Extent of NDT for splices not shown on drawing	
RAL 7024 (Graphite Gray)	UT, EN-ISO17640, 100%of welds	
Welding of built up steel section	Requirements on holing	
Appendix 1 / Project spec.	EN1090-2 Section 6.6.3	
Welds, if not specified otherwise	Weld class	Additional material inspection
EN 9692-1, EN 9692-2	C, EN ISO 5817	Shown on drwg.

PROJECT NAME
Easpring New Materials Oy
FAIR Phase 1

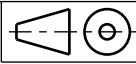


DRAWING CONTENT
ASSEMBLY DRAWING
PLATE
E51EX-1081




SWECO RAKENNETEKNIikka OY
ILMALANPORTTI 2
00240 HELSINKI
PUH. +358 207 393 000
www.sweco.fi

DATE	ARCHIVING CODE	PAGE	DESIGN GROUP
12.06.2026			STR
DRAWN	DESIGNER	APPROVED	CHECKED
Alexey Serous	Alexey Serous	Pertti Koivumaa	Jere Kallosalmi
PROJECT NUMBER	DWG. NO.	REVISION	
25019443	E51EX-1081		

PART LIST FOR ASSEMBLY E51EX-1082, MANUFACTURING AMOUNT 16 PIECES						
PART	PROFILE	MATERIAL	LENGTH [mm]	AREA [m2]	WEIGHT [kg]	PCS
E51EXL-1027	PL2X220	S355J2+N	435	0.16	1.2	1
TOTAL:				0.16	1.2	

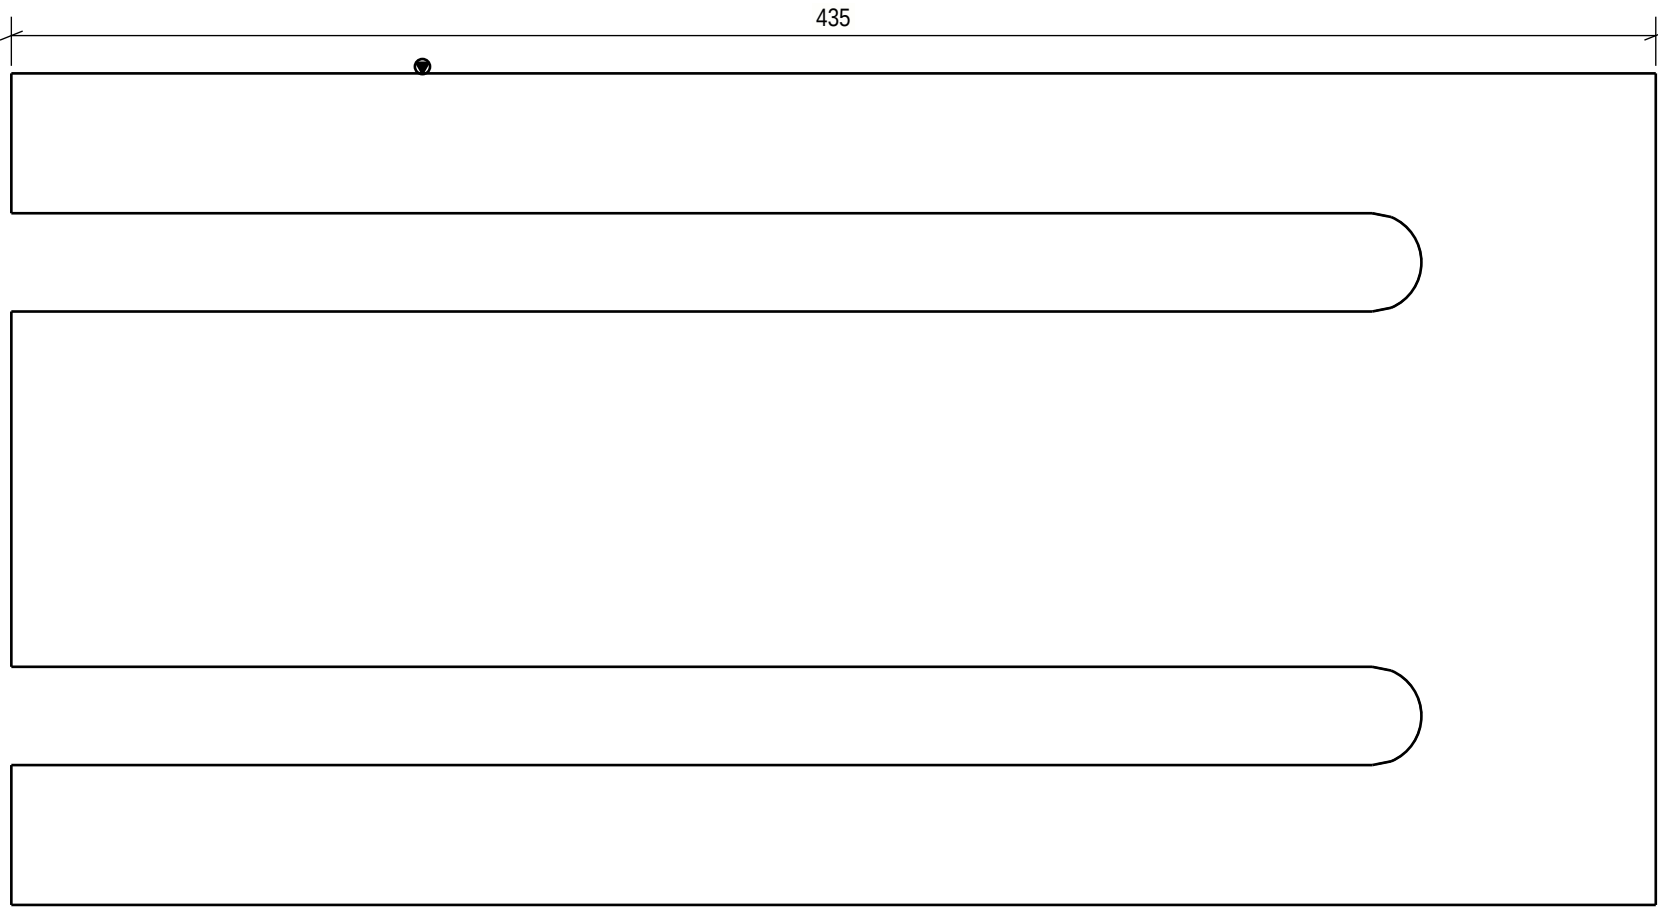

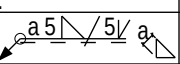
Technical fabrication requirements:		Execution class
Requirements for fabrication, standard	Fabrication tolerances	EXC2
EN1090-2, table A.3 : EXC2	EN 1090-2, Appendix B	
Execution Specification document nr	Special fabrication tolerances	
25019443-ICC250-0600-0660-000005	Project specification/ shown on drwg.	
Surface preparation grade	Weld inspection, requirements	
ISO8501-3, grade P2	EN 1090-2,Table 24, U>0.5	
Surface treatment	Extent of NDT, filled welds	
ISO12944-5	MT-EN1290,20% of welds	
Additional requirements on surface treatment	Extent of NDT, butt welds	
C3.07, EPPUR 240/2	UT, EN-ISO17640, 20% of welds	
Shade	Extent of NDT for splices not shown on drawing	
RAL 7024 (Graphite Gray)	UT, EN-ISO17640, 100%of welds	
Welding of built up steel section	Requirements on holing	
Appendix 1 / Project spec.	EN1090-2 Section 6.6.3	
Welds, if not specified otherwise	Weld class	
EN 9692-1, EN 9692-2	C, EN ISO 5817	Additional material inspection Shown on drwg.

Approved For Construction

Easpring New Materials Oy
FAIR Phase 1





SWECO RAKENNETEKNIikka OY
ILMALANPORTTI 2
00240 HELSINKI
PUH. +358 207 393 000
www.sweco.fi

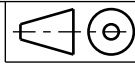

DRAWING CONTENT			
ASSEMBLY DRAWING			
PLATE			
E51EX-1082			
DATE	ARCHIVING CODE	PAGE	DESIGN GROUP
12.06.2026			STR
DRAWN	DESIGNER	APPROVED	CHECKED
Alexey Serous	Alexey Serous	Pertti Koivumaaanaho	Jere Kallosalmi
PROJECT NUMBER	DWG. NO.	REVISION	
25019443	E51EX-1082		

PART LIST FOR ASSEMBLY E51EX-1083, MANUFACTURING AMOUNT 32 PIECES						
PART	PROFILE	MATERIAL	LENGTH [mm]	AREA [m2]	WEIGHT [kg]	PCS
E51EXL-1075	PL5X450	S355J2+N	550	0.51	9.7	1
TOTAL:				0.51	9.7	

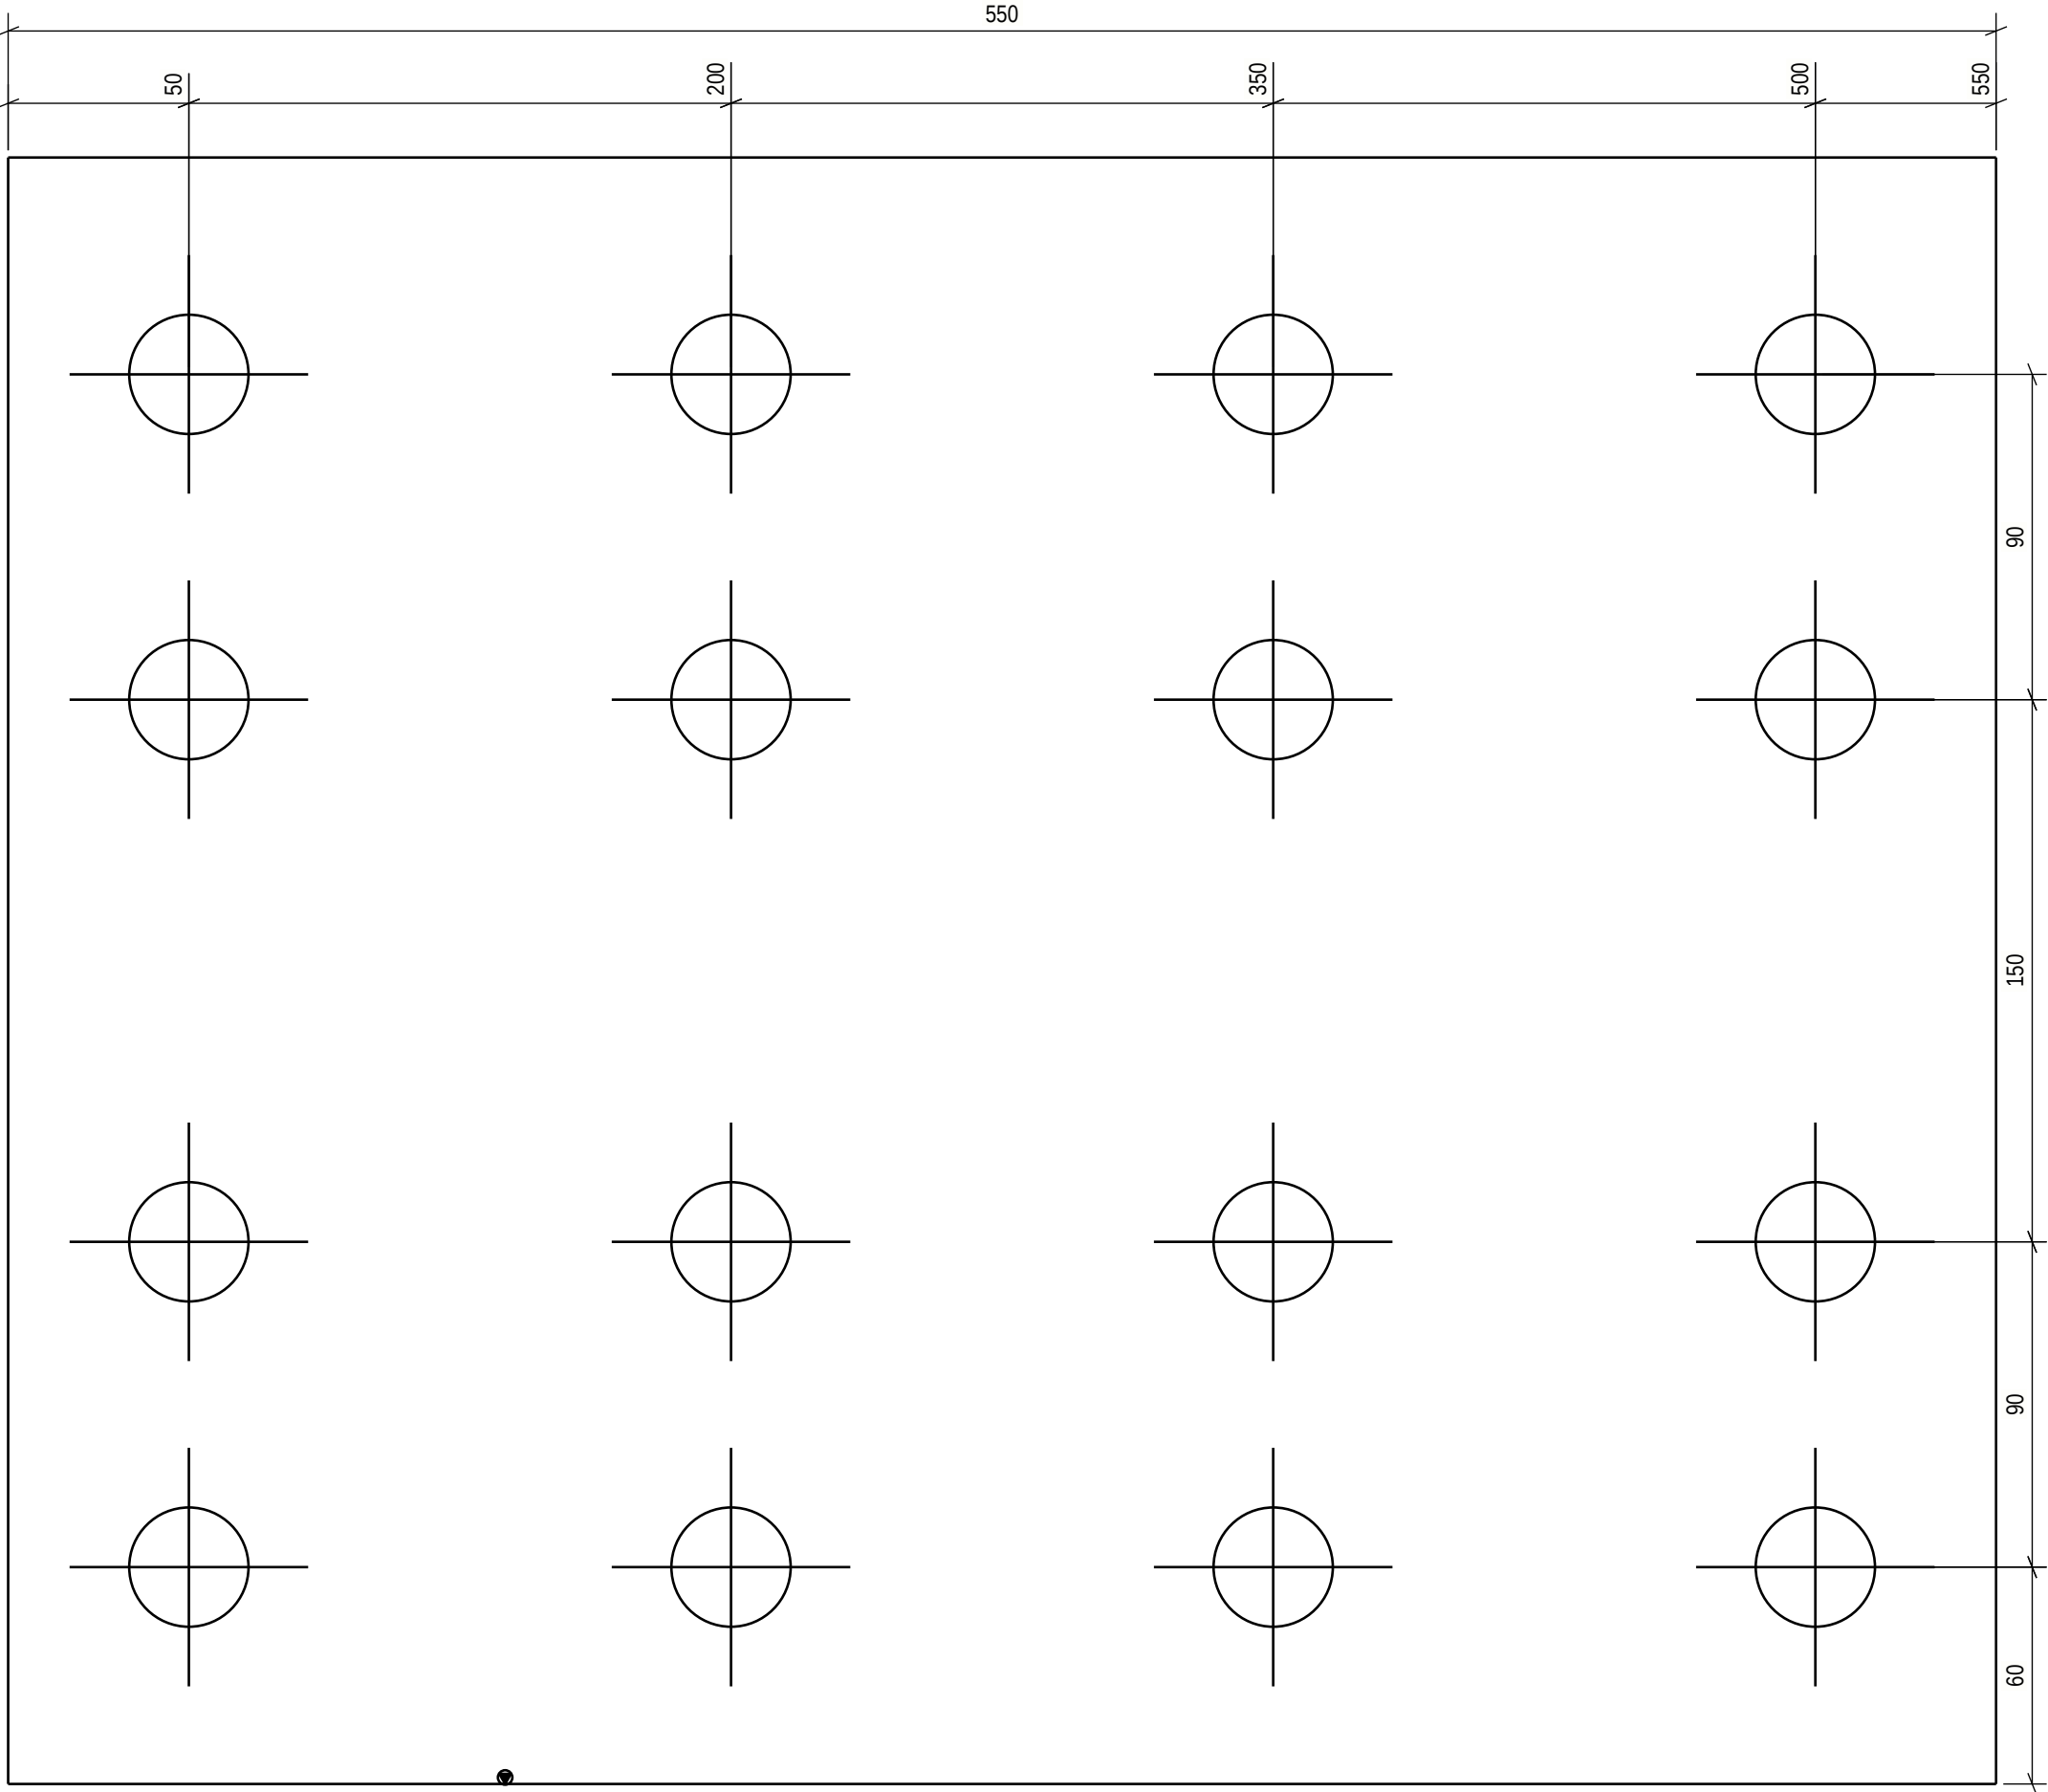

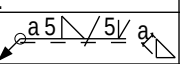
Technical fabrication requirements:		Execution class
Requirements for fabrication, standard	Fabrication tolerances	EXC2
EN1090-2, table A.3 : EXC2	EN 1090-2, Appendix B	
Execution Specification document nr	Special fabrication tolerances	
25019443-ICC250-0600-0660-000005	Project specification/ shown on drwg.	
Surface preparation grade	Weld inspection, requirements	
ISO8501-3, grade P2	EN 1090-2,Table 24, U>0.5	
Surface treatment	Extent of NDT, filled welds	
ISO12944-5	MT-EN1290,20% of welds	
Additional requirements on surface treatment	Extent of NDT, butt welds	
C3.07, EPPUR 240/2	UT, EN-ISO17640, 20% of welds	
Shade	Extent of NDT for splices not shown on drawing	
RAL 7024 (Graphite Gray)	UT, EN-ISO17640, 100%of welds	
Welding of built up steel section	Requirements on holing	
Appendix 1 / Project spec.	EN1090-2 Section 6.6.3	
Welds, if not specified otherwise	Weld class	
EN 9692-1, EN 9692-2	C, EN ISO 5817	Additional material inspection Shown on drwg.

Approved For Construction

Easpring New Materials Oy
FAIR Phase 1




SWECO RAKENNETEKNIikka OY
ILMALANPORTTI 2
00240 HELSINKI
PUH. +358 207 393 000
www.sweco.fi

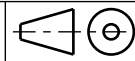

DRAWING CONTENT
ASSEMBLY DRAWING
PLATE
E51EX-1083

DATE	ARCHIVING CODE	PAGE	DESIGN GROUP
12.06.2026			STR
DRAWN	DESIGNER	APPROVED	CHECKED
Alexey Serous	Alexey Serous	Pertti Koivumaaanaho	Jere Kallosalmi
PROJECT NUMBER	DWG. NO.	REVISION	
25019443	E51EX-1083		

PART LIST FOR ASSEMBLY E51EX-1084, MANUFACTURING AMOUNT 24 PIECES						
PART	PROFILE	MATERIAL	LENGTH [mm]	AREA [m2]	WEIGHT [kg]	PCS
E51EXL-1074	PL5X430	S355J2+N	550	0.48	9.3	1
TOTAL:				0.48	9.3	

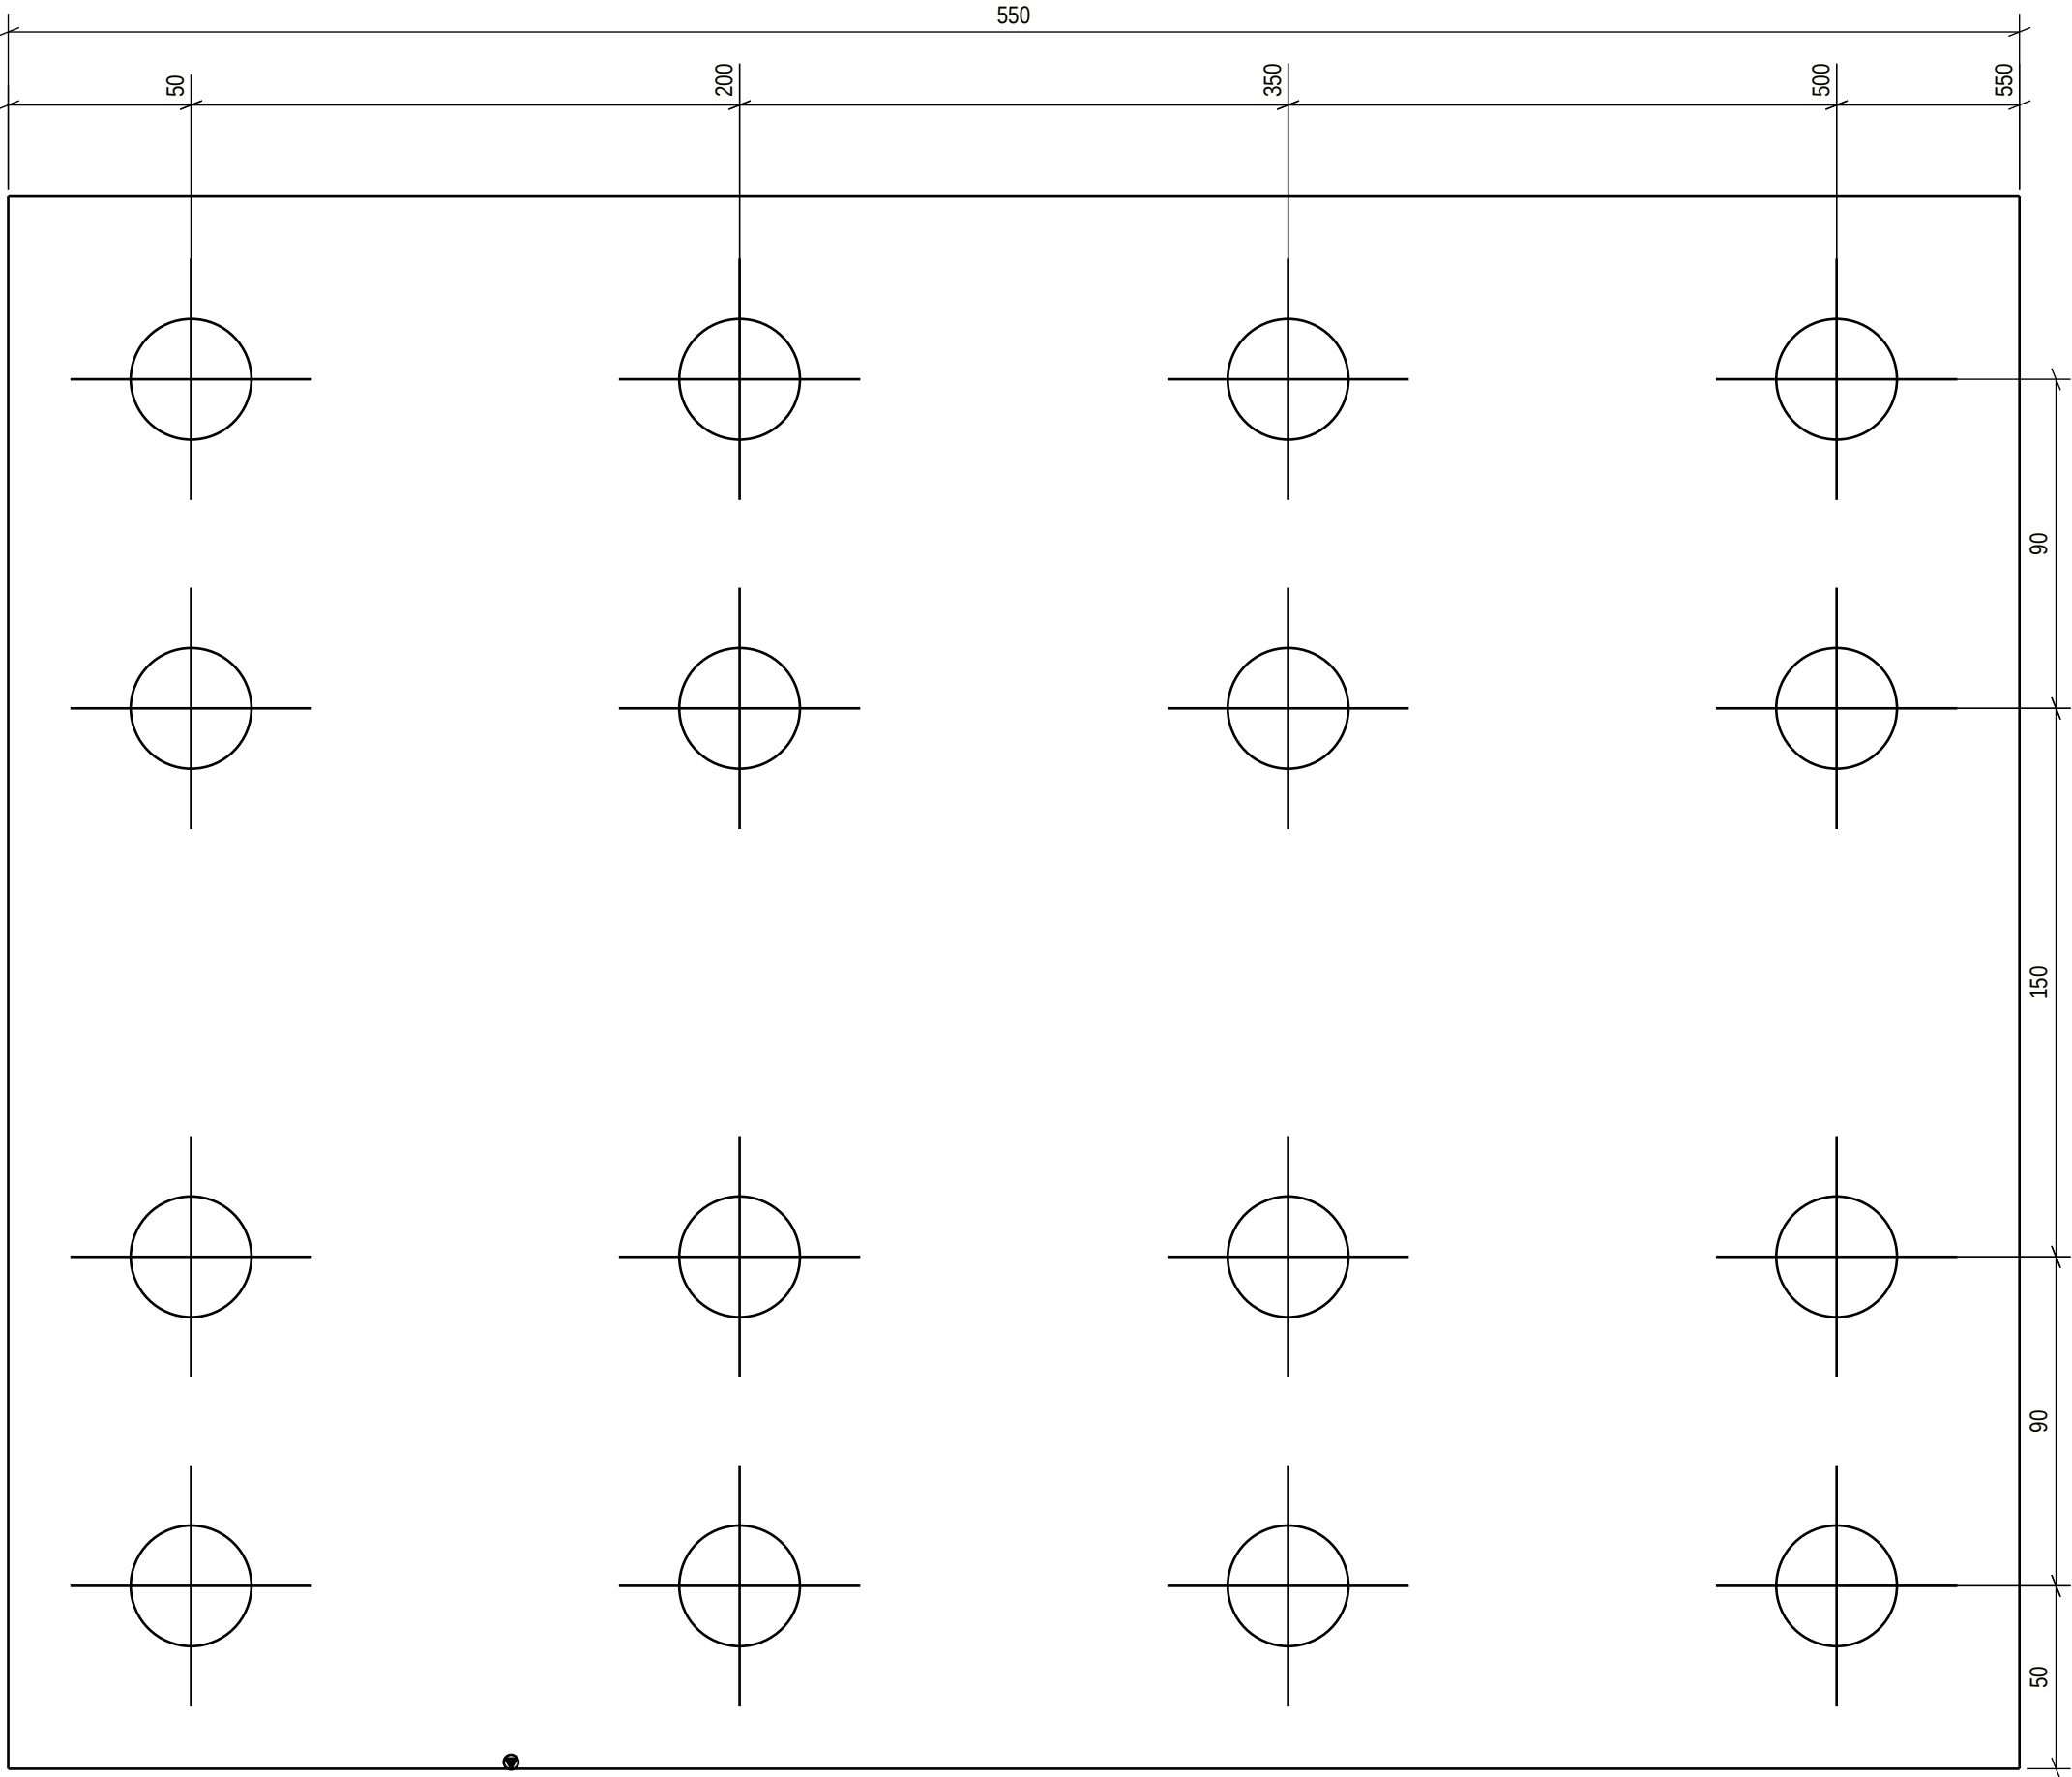


Technical fabrication requirements:		Execution class	
Requirements for fabrication, standard		EN 1090-2, Appendix B	
Execution Specification document nr		Special fabrication tolerances	
25019443-ICC250-0600-0660-000005		Project specification/ shown on drwg.	
Surface preparation grade		Weld inspection, requirements	
ISO8501-3, grade P2		EN 1090-2, Table 24, U>0.5	
Surface treatment		Extent of NDT, fillet welds	
ISO12944-5		MT-EN1290, 20% of welds	
Additional requirements on surface treatment		Extent of NDT, butt welds	
C3.07, EPPUR 240/2		UT, EN-ISO17640, 20% of welds	
Shade		Extent of NDT for splices not shown on drawing	
RAL 7024 (Graphite Gray)		UT, EN-ISO17640, 100% of welds	
Welding of built up steel section		Requirements on holing	
Appendix 1 / Project spec.		EN1090-2 Section 6.6.3	
Welds, if not specified otherwise		Weld class	
EN 9692-1, EN 9692-2		C, EN ISO 5817	
		Additional material inspection	
		Shown on drwg.	

Approved For Construction		PROJECT NAME		DRAWING CONTENT	
		Easpring New Materials Oy		ASSEMBLY DRAWING	
		FAIR Phase 1		PLATE	
				E51EX-1084	
				DATE	DESIGN GROUP
				12.06.2026	STR
				ARCHIVING CODE	PAGE
				DESIGNER	CHECKED
				Alexey Serous	Jere Kallosalmi
				APPROVED	REVISION
				Pertti Koivumaaanaho	
				PROJECT NUMBER	DWG. NO.
				25019443	E51EX-1084


PART LIST FOR ASSEMBLY E51EX-1085, MANUFACTURING AMOUNT 34 PIECES						
PART	PROFILE	MATERIAL	LENGTH [mm]	AREA [m2]	WEIGHT [kg]	PCS
E51EXL-1002	PL2X200	S355J2+N	260	0.09	0.7	1
			TOTAL:	0.09	0.7	

		Execution class	
Technical fabrication requirements:		EXC2	
Requirements for fabrication, standard EN1090-2, table A.3 : EXC2 Execution Specification document nr. 25019443-ICC250-0600-0660-000005 Surface preparation grade ISO8501-3, grade P2 Surface treatment ISO12944-5 Additional requirements on surface treatment C3.07, EPPUR 240/2 Shade RAL 7024 (Graphite Gray) Welding of built up steel section Appendix 1 / Project spec. Welds, if not specified otherwise EN 9692-1, EN 9692-2		Fabrication tolerances EN 1090-2, Appendix B Special fabrication tolerances Project specification/ shown on drwg. Weld inspection, requirements EN 1090-2, Table 24, U>0.5 Extent of NDT, fillet welds MT-EN1290, 20% of welds Extent of NDT, butt welds UT, EN-ISO17640, 20% of welds Extent of NDT for splices not shown on drawing UT-EN-ISO17640, 100% of welds Requirements on healing EN1090-2 Section 6.6.3 Weld class EN ISO 5817	
Additional material inspection Shown on drwg.			

Approved For Construction

 PROJECT NAME Easpring New Materials Oy FAIR Phase 1				DRAWING CONTENT ASSEMBLY DRAWING PLATE E51EX-1085	
		SWECO RAKENNETEKNIIKKA OY ILMALANPORTTI 2 00240 HELSINKI PUH. +358 207 393 000 www.sweco.fi		DATE 12.06.2026	ARCHIVING CODE
		DRAWN Alexey Serous	DESIGNER Alexey Serous	APPROVED Pertti Koivumaaanaho	DESIGN GROUP STR CHECKED Jere Kalliosaalmi
		PROJECT NUMBER 25019443	DWG. NO. E51EX-1085		
		REVISION			


PART LIST FOR ASSEMBLY E51EX-1086, MANUFACTURING AMOUNT 4 PIECES						
PART	PROFILE	MATERIAL	LENGTH [mm]	AREA [m2]	WEIGHT [kg]	PCS
E51EXL-1048	PL2X200	S355J2+N	236	0.08	0.6	1
			TOTAL:	0.08	0.6	

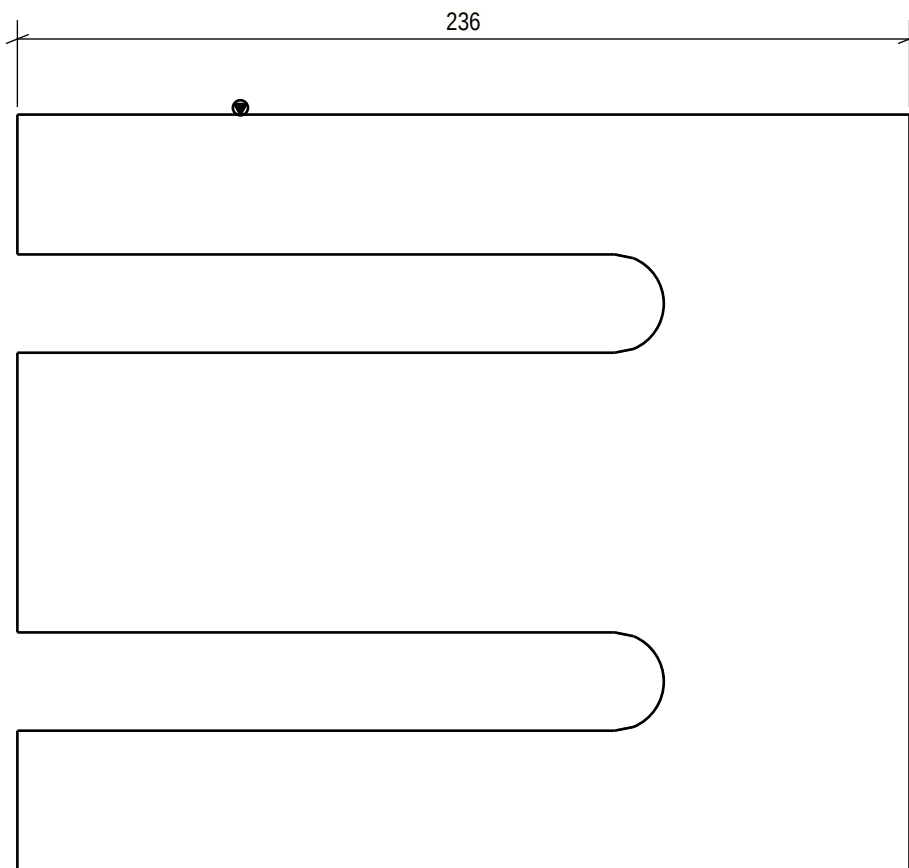

Technical fabrication requirements:		Execution class	
		EXC2	
Approved For Construction			
Requirements for fabrication, standard		Fabrication tolerances	
EN1090-2, table A.3 : EXC2		EN 1090-2, Appendix B	
Execution Specification document nr		Special fabrication tolerances	
25019443-ICC250-0600-0660-000005		Project specification/ shown on drwg.	
Surface preparation grade		Weld inspection, requirements	
ISO8501-3, grade P2		EN 1090-2, Table 24, U>0.5	
Surface treatment		Extent of NDT, fillet welds	
ISO12944-5		MT-EN1290, 20% of welds	
Additional requirements on surface treatment		Extent of NDT, butt welds	
C3.07, EPPUR 240/2		UT, EN-ISO17640, 20% of welds	
Shade		Extent of NDT for splices not shown on drawing	
RAL 7024 (Graphite Gray)		UT, EN-ISO17640, 100% of welds	
Welding of built up steel section		Requirements on holding	
Appendix 1 / Project spec.		EN1090-2 Section 6.6.3	
Welds, if not specified otherwise		Weld class	
EN 9692-1, C, EN 9692-2		C, EN ISO 5817	
a 5 / 5 / a		Additional material inspection	
		Shown on drwg.	
PROJECT NAME		DRAWING CONTENT	
Easpring New Materials Oy		ASSEMBLY DRAWING	
FAIR Phase 1		PLATE	
		E51EX-1086	
DATE		ARCHIVING CODE	
12.06.2026			
DRAWN		DESIGNER	
Alexey Serous		Alexey Serous	
APPROVED		CHECKED	
Pertti Koivumäenaho		Jere Kalliosalmi	
PROJECT NUMBER		DWG. NO.	
25019443		E51EX-1086	
SWECO		SWECO RAKENNETEKNIikka OY	
Sustainable engineering and design		ILMALANPORTTI 2	
		00240 HELSINKI	
		PUH. +358 207 393 000	
		www.sweco.fi	

For special tolerances of bolt hole location
see specification for steel structures

PART LIST FOR ASSEMBLY E51EX-1087, MANUFACTURING AMOUNT 4 PIECES						
PART	PROFILE	MATERIAL	LENGTH [mm]	AREA [m2]	WEIGHT [kg]	PCS
E51EXL-1048	PL2X200	S355J2+N	236	0.08	0.6	1
TOTAL:				0.08	0.6	

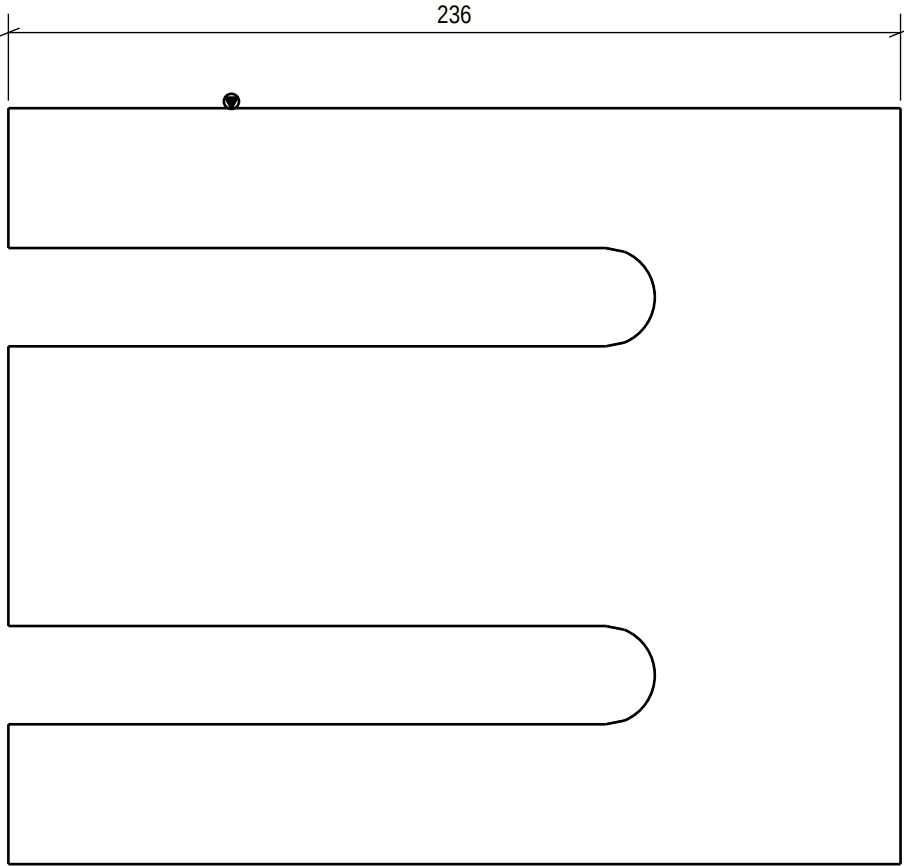


Technical fabrication requirements:		Execution class
Requirements for fabrication, standard EN1090-2, table A.3 : EXC2		EXC2
Execution Specification document nr 25019443-ICC250-0600-0660-000005	Fabrication tolerances EN 1090-2, Appendix B Special fabrication tolerances Project specification/ shown on drwg.	
Surface preparation grade ISO8501-3, grade P2	Weld inspection, requirements EN 1090-2,Table 24, U>0.5	
Surface treatment ISO12944-5	Extent of NDT, fillet welds MT-EN1290,20% of welds	
Additional requirements on surface treatment C3.07, EPPUR 240/2	Extent of NDT, butt welds UT, EN-ISO17640, 20% of welds	
Shade RAL 7024 (Graphite Gray)	Extent of NDT for splices not shown on drawing UT, EN-ISO17640, 100%of welds	
Welding of built up steel section Appendix 1 / Project spec.	Requirements on holing EN1090-2 Section 6.6.3	
Welds, if not specified otherwise EN 9692-1, EN 9692-2	Weld class C, EN ISO 5817	Additional material inspection Shown on drwg.

Approved For Construction

Easpring New Materials Oy
FAIR Phase 1




SWECO RAKENNETEKNIikka OY
ILMALANPORTTI 2
00240 HELSINKI
PUH. +358 207 393 000
www.sweco.fi

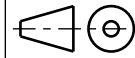

DRAWING CONTENT			
ASSEMBLY DRAWING PLATE E51EX-1087			
DATE 12.06.2026	ARCHIVING CODE	PAGE	DESIGN GROUP STR
DRAWN Alexey Serous	DESIGNER Alexey Serous	APPROVED Pertti Koivumaaanaho	CHECKED Jere Kallosalmi
PROJECT NUMBER 25019443	DWG. NO.	REVISION E51EX-1087	

PART LIST FOR ASSEMBLY E51EX-1088, MANUFACTURING AMOUNT 8 PIECES						
PART	PROFILE	MATERIAL	LENGTH [mm]	AREA [m2]	WEIGHT [kg]	PCS
E51EXL-1001	PL2X180	S355J2+N	240	0.07	0.5	1
TOTAL:				0.07	0.5	

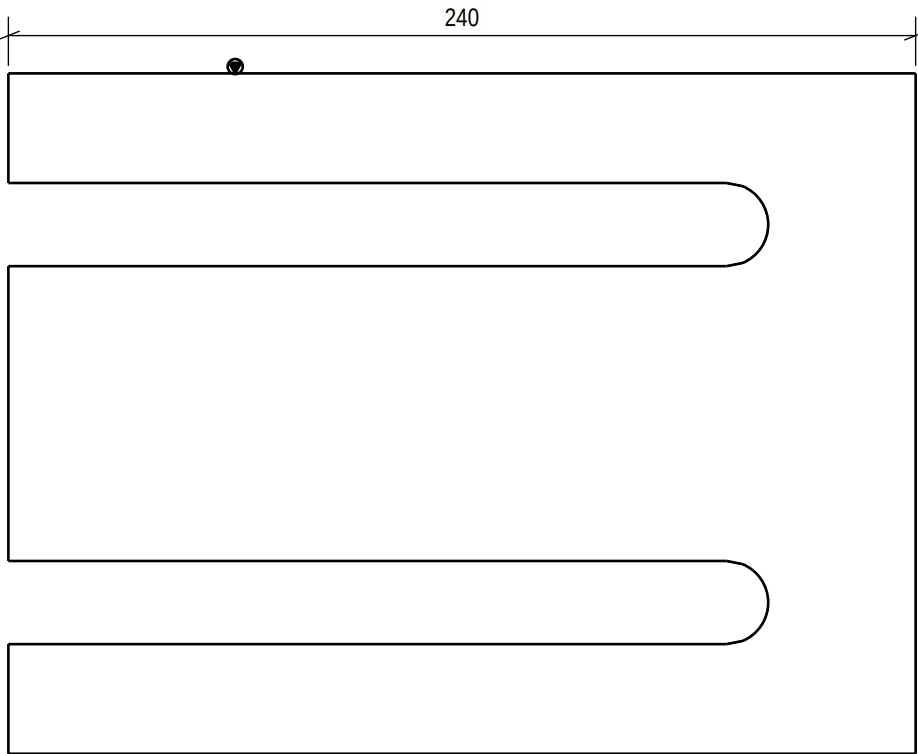

Approved For Construction

Technical fabrication requirements:		Execution class EXC2	
Requirements for fabrication, standard EN1090-2, table A.3 : EXC2		Fabrication tolerances EN 1090-2, Appendix B	
Execution Specification document nr 25019443-ICC250-0600-0660-000005		Special fabrication tolerances Project specification/ shown on drwg.	
Surface preparation grade ISO8501-3, grade P2		Weld inspection, requirements EN 1090-2,Table 24, U>0.5	
Surface treatment ISO12944-5		Extent of NDT, fillet welds MT-EN1290,20% of welds	
Additional requirements on surface treatment C3.07, EPPUR 240/2		Extent of NDT, butt welds UT, EN-ISO17640, 20% of welds	
Shade RAL 7024 (Graphite Gray)		Extent of NDT for splices not shown on drawing UT, EN-ISO17640, 100%of welds	
Welding of built up steel section Appendix 1 / Project spec.		Requirements on holing EN1090-2 Section 6.6.3	
Welds, if not specified otherwise EN 9692-1, EN 9692-2		Weld class C, EN ISO 5817	
		Additional material inspection Shown on drwg.	

01	Quantity decreased	FIALES	18.06.2026	FIKJER
REV.	REVISION	CHANGED BY	DATE	CHECKED BY

PROJECT NAME

Easpring New Materials Oy

FAIR Phase 1



DRAWING CONTENT

ASSEMBLY DRAWING

PLATE

E51EX-1088

 Sustainable engineering and design	SWECO RAKENNETEKNIikka OY ILMALANPORTTI 2 00240 HELSINKI PUH. +358 207 393 000 www.sweco.fi	DATE 12.06.2026	ARCHIVING CODE	PAGE	DESIGN GROUP STR
		DRAWN Alexey Serous	DESIGNER Alexey Serous	APPROVED Pertti Koivumaaanaho	CHECKED Jere Kallosalmi
PROJECT NUMBER 25019443		REVISION E51EX-1088 01			

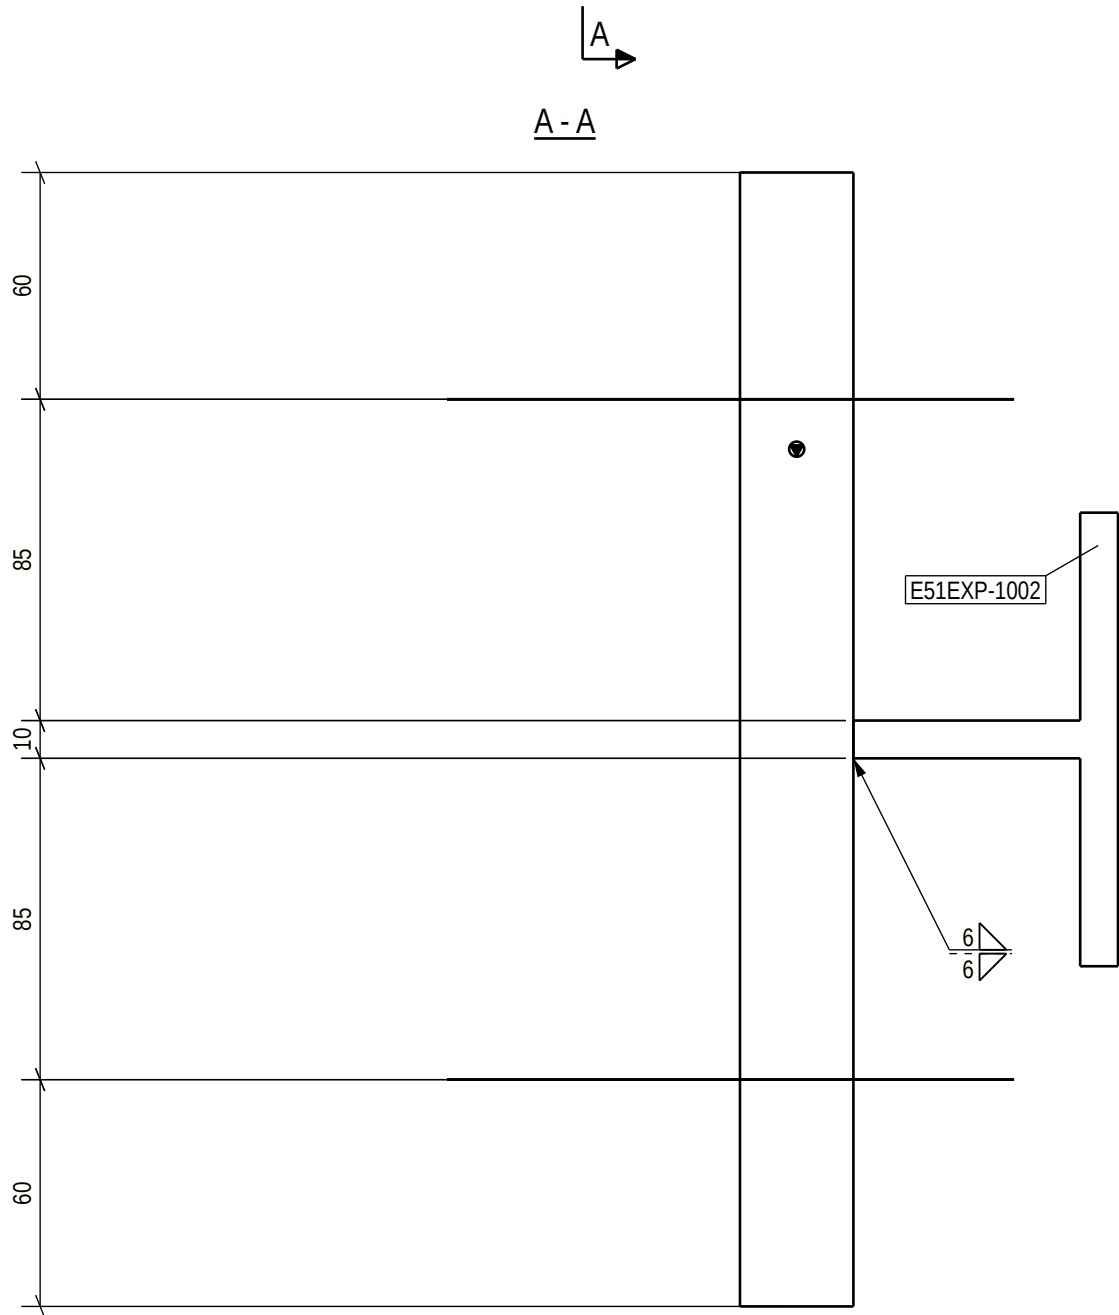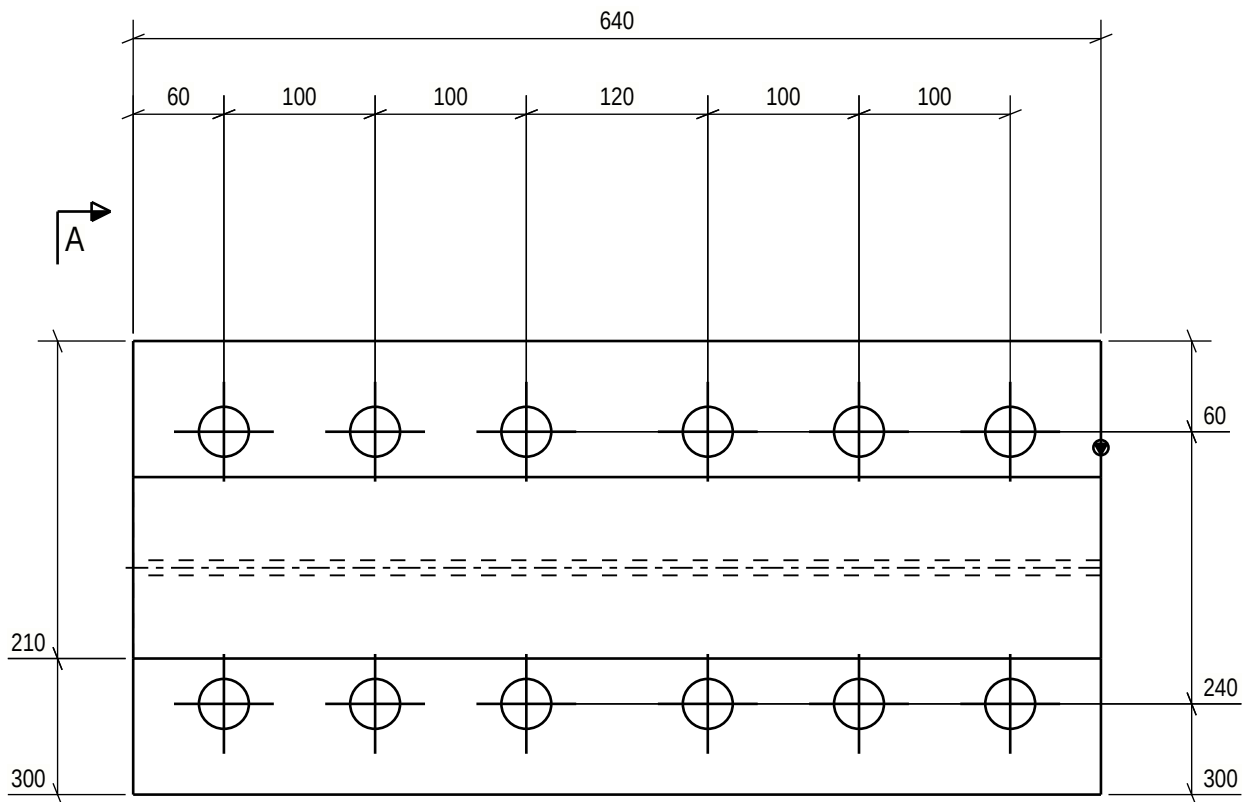


For special tolerances of bolt hole location
see specification for steel structures
Approved For Construction

PART LIST FOR ASSEMBLY E51EX-1089, MANUFACTURING AMOUNT 3 PIECES						
PART	PROFILE	MATERIAL	LENGTH [mm]	AREA [m ²]	WEIGHT [kg]	PCS
E51EXL-1067	PL30X300	S355J2+N	640	0.44	45.2	1
E51EXP-1002	T70-10-10-120	S355J2+N	640	0.25	9.2	1
TOTAL:				0.69	54.4	

Technical fabrication requirements:		Execution class
Requirements for fabrication, standard EN1090-2, table A.3 : EXC2		EXC2
Execution Specification document nr 25019443-ICC250-0600-0660-000005	Fabrication tolerances EN 1090-2, Appendix B Special fabrication tolerances Project specification/ shown on drwg.	
Surface preparation grade ISO8501-3, grade P2	Weld inspection, requirements EN 1090-2, Table 24, U>0.5	
Surface treatment ISO12944-5	Extent of NDT, filled welds MT-EN1290, 20% of welds	
Additional requirements on surface treatment C3.07, EPPUR 240/2	Extent of NDT, butt welds UT, EN-ISO17640, 20% of welds	
Shade RAL 7024 (Graphite Gray)	Extent of NDT for splices not shown on drawing UT, EN-ISO17640, 100% of welds	
Welding of built up steel section Appendix 1 / Project spec.	Requirements on holing EN1090-2 Section 6.6.3	
Welds, if not specified otherwise EN 9692-1, EN 9692-2	Weld class C, EN ISO 5817	Additional material inspection Shown on drwg.

FIRE PROTECTION SAME AS FOR E51WC-1031

PROJECT NAME
Easpring New Materials Oy
FAIR Phase 1

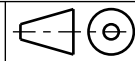


DRAWING CONTENT
ASSEMBLY DRAWING
PLATE
E51EX-1089



SWECO RAKENNTEKNIikka OY
ILMALANPORTTI 2
00240 HELSINKI
PUH. +358 207 393 000
www.sweco.fi

DATE	ARCHIVING CODE	PAGE	DESIGN GROUP
12.06.2026			STR
DRAWN	DESIGNER	APPROVED	CHECKED
Alexey Serous	Alexey Serous	Pertti Koivumaaanaho	Jere Kallosalmi
PROJECT NUMBER	DWG. NO.	REVISION	
25019443		E51EX-1089	


PART LIST FOR ASSEMBLY E51EX-1090, MANUFACTURING AMOUNT 2 PIECES						
PART	PROFILE	MATERIAL	LENGTH [mm]	AREA [m2]	WEIGHT [kg]	PCS
E51EXL-1092	PL2X180	S355J2+N	240	0.07	0.5	1
TOTAL:				0.07	0.5	

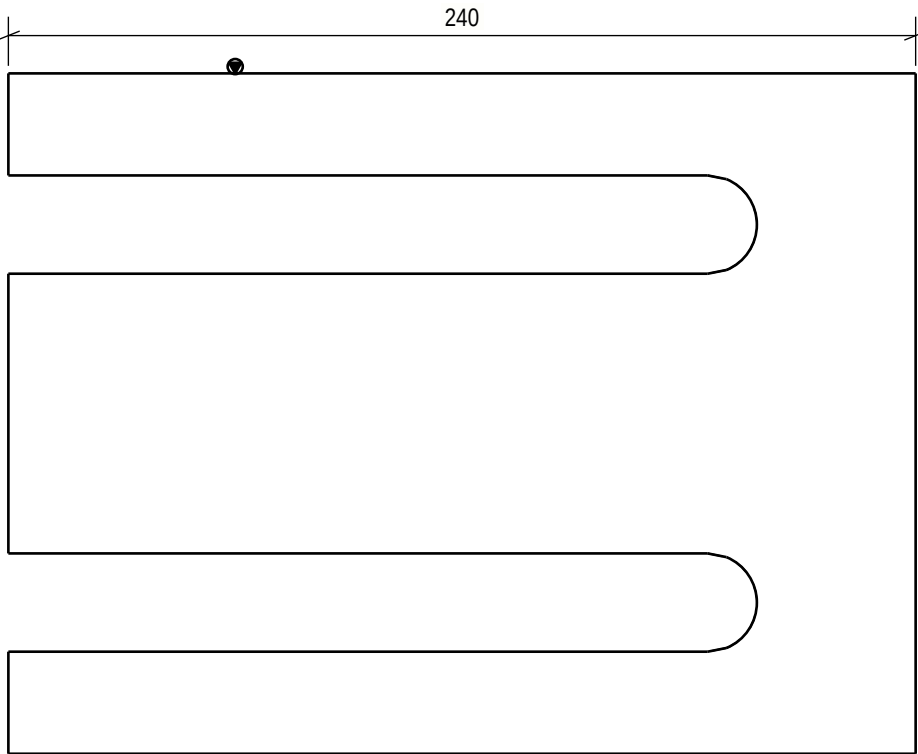

For special tolerances of bolt hole location
see specification for steel structures
Approved For Construction



Technical fabrication requirements:		Execution class EXC2	
Requirements for fabrication, standard EN1090-2, table A.3 : EXC2		Fabrication tolerances EN 1090-2, Appendix B	
Execution Specification document nr 25019443-ICC250-0600-0660-000005		Special fabrication tolerances Project specification/ shown on drwg.	
Surface preparation grade ISO8501-3, grade P2		Weld inspection, requirements EN 1090-2,Table 24, U>0.5	
Surface treatment ISO12944-5		Extent of NDT, fillet welds MT-EN1290,20% of welds	
Additional requirements on surface treatment C3.07, EPPUR 240/2		Extent of NDT, butt welds UT, EN-ISO17640, 20% of welds	
Shade RAL 7024 (Graphite Gray)		Extent of NDT for splices not shown on drawing UT, EN-ISO17640, 100%of welds	
Welding of built up steel section Appendix 1 / Project spec.		Requirements on holing EN1090-2 Section 6.6.3	
Welds, if not specified otherwise EN 9692-1, EN 9692-2		Weld class C, EN ISO 5817	
		Additional material inspection Shown on drwg.	

PROJECT NAME Easpring New Materials Oy FAIR Phase 1			DRAWING CONTENT ASSEMBLY DRAWING PLATE E51EX-1090			
			DATE 18.06.2026	ARCHIVING CODE	PAGE	DESIGN GROUP STR
DRAWN Alexey Serous		DESIGNER Alexey Serous	APPROVED Pertti Koivumaaanaho	CHECKED Jere Kallosalmi	REVISION	
PROJECT NUMBER 25019443		DWG. NO. E51EX-1090				
PUH. +358 207 393 000 www.sweco.fi						

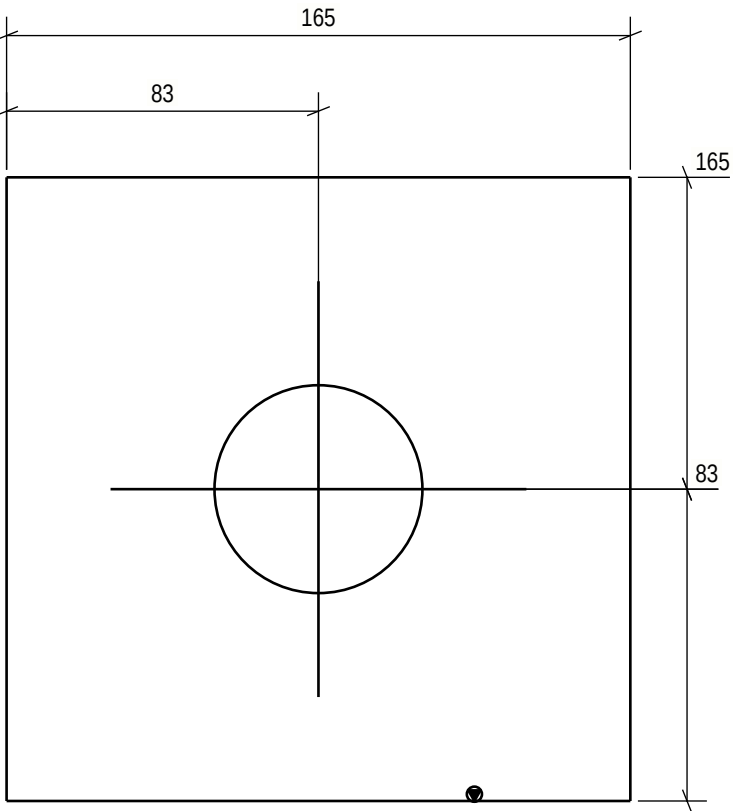

For special tolerances of bolt hole location
see specification for steel structures
Approved For Construction

PART LIST FOR ASSEMBLY E51EX-1091, MANUFACTURING AMOUNT 48 PIECES						
PART	PROFILE	MATERIAL	LENGTH [mm]	AREA [m2]	WEIGHT [kg]	PCS
E51EXL-1031	PL10X165	S355J2+N	165	0.06	2.1	1
TOTAL:				0.06	2.1	

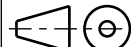 Technical fabrication requirements:		Execution class EXC2		Approved For Construction																	
Requirements for fabrication, standard EN1090-2, table A.3 : EXC2 Execution Specification document nr 25019443-ICC250-0600-0660-000005 Surface preparation grade ISO8501-3, grade P2 Surface treatment ISO12944-5 Additional requirements on surface treatment C4.06 EPPUR 240/3 Shade RAL 7024 (Graphite Gray) Welding of built up steel section Appendix 1 / Project spec. Welds, if not specified otherwise EN 9692-1, EN 9692-2		Fabrication tolerances EN 1090-2, Appendix B Special fabrication tolerances Project specification/ shown on drwg. Weld inspection, requirements EN 1090-2,Table 24, U>0.5 Extent of NDT, fillet welds MT-EN1290,20% of welds Extent of NDT, butt welds UT, EN-ISO17640, 20% of welds Extent of NDT for splices not shown on drawing UT, EN-ISO17640, 100%of welds Requirements on holing EN1090-2 Section 6.6.3 Weld class C, EN ISO 5817 Additional material inspection Shown on drwg.		PROJECT NAME Easpring New Materials Oy FAIR Phase 1 SWECO Sustainable engineering and design  SWECO RAKENNETEKNIikka OY ILMALANPORTTI 2 00240 HELSINKI PUH. +358 207 393 000 www.sweco.fi		 DRAWING CONTENT ASSEMBLY DRAWING PLATE E51EX-1091															
				<table><tr><td>DATE 18.06.2026</td><td>ARCHIVING CODE</td><td>PAGE</td><td>DESIGN GROUP STR</td></tr><tr><td>DRAWN Alexey Serous</td><td>DESIGNER Alexey Serous</td><td>APPROVED Pertti Koivumaaanaho</td><td>CHECKED Jere Kallosalmi</td></tr><tr><td colspan="2">PROJECT NUMBER 25019443</td><td colspan="2">DWG. NO. E51EX-1091</td></tr><tr><td colspan="2"></td><td colspan="2">REVISION</td></tr></table>		DATE 18.06.2026	ARCHIVING CODE	PAGE	DESIGN GROUP STR	DRAWN Alexey Serous	DESIGNER Alexey Serous	APPROVED Pertti Koivumaaanaho	CHECKED Jere Kallosalmi	PROJECT NUMBER 25019443		DWG. NO. E51EX-1091				REVISION	
DATE 18.06.2026	ARCHIVING CODE	PAGE	DESIGN GROUP STR																		
DRAWN Alexey Serous	DESIGNER Alexey Serous	APPROVED Pertti Koivumaaanaho	CHECKED Jere Kallosalmi																		
PROJECT NUMBER 25019443		DWG. NO. E51EX-1091																			
		REVISION																			